

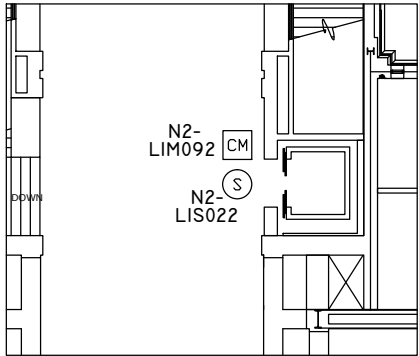


LEVEL 2

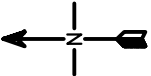

DEVICE LEGEND	
SYMBOL	DESCRIPTION
Ⓢ	SMOKE DETECTOR
Ⓢ	HEAT DETECTOR
CM	CONTROL MODULE
MM	MONITOR MODULE
B _r	BEAM DETECTOR TRANSMITTER
B _r	BEAM DETECTOR REFLECTOR
B _{ts}	BEAM DETECTOR TEST SWITCH
DD	DUCT DETECTOR
F	PULL STATION
RA	REMOTE ANNUNCIATOR
PIV	POST INDICATOR VALVE
FACP	FIRE ALARM CONTROL PANEL
TRAN	TRANSPONDER PANEL

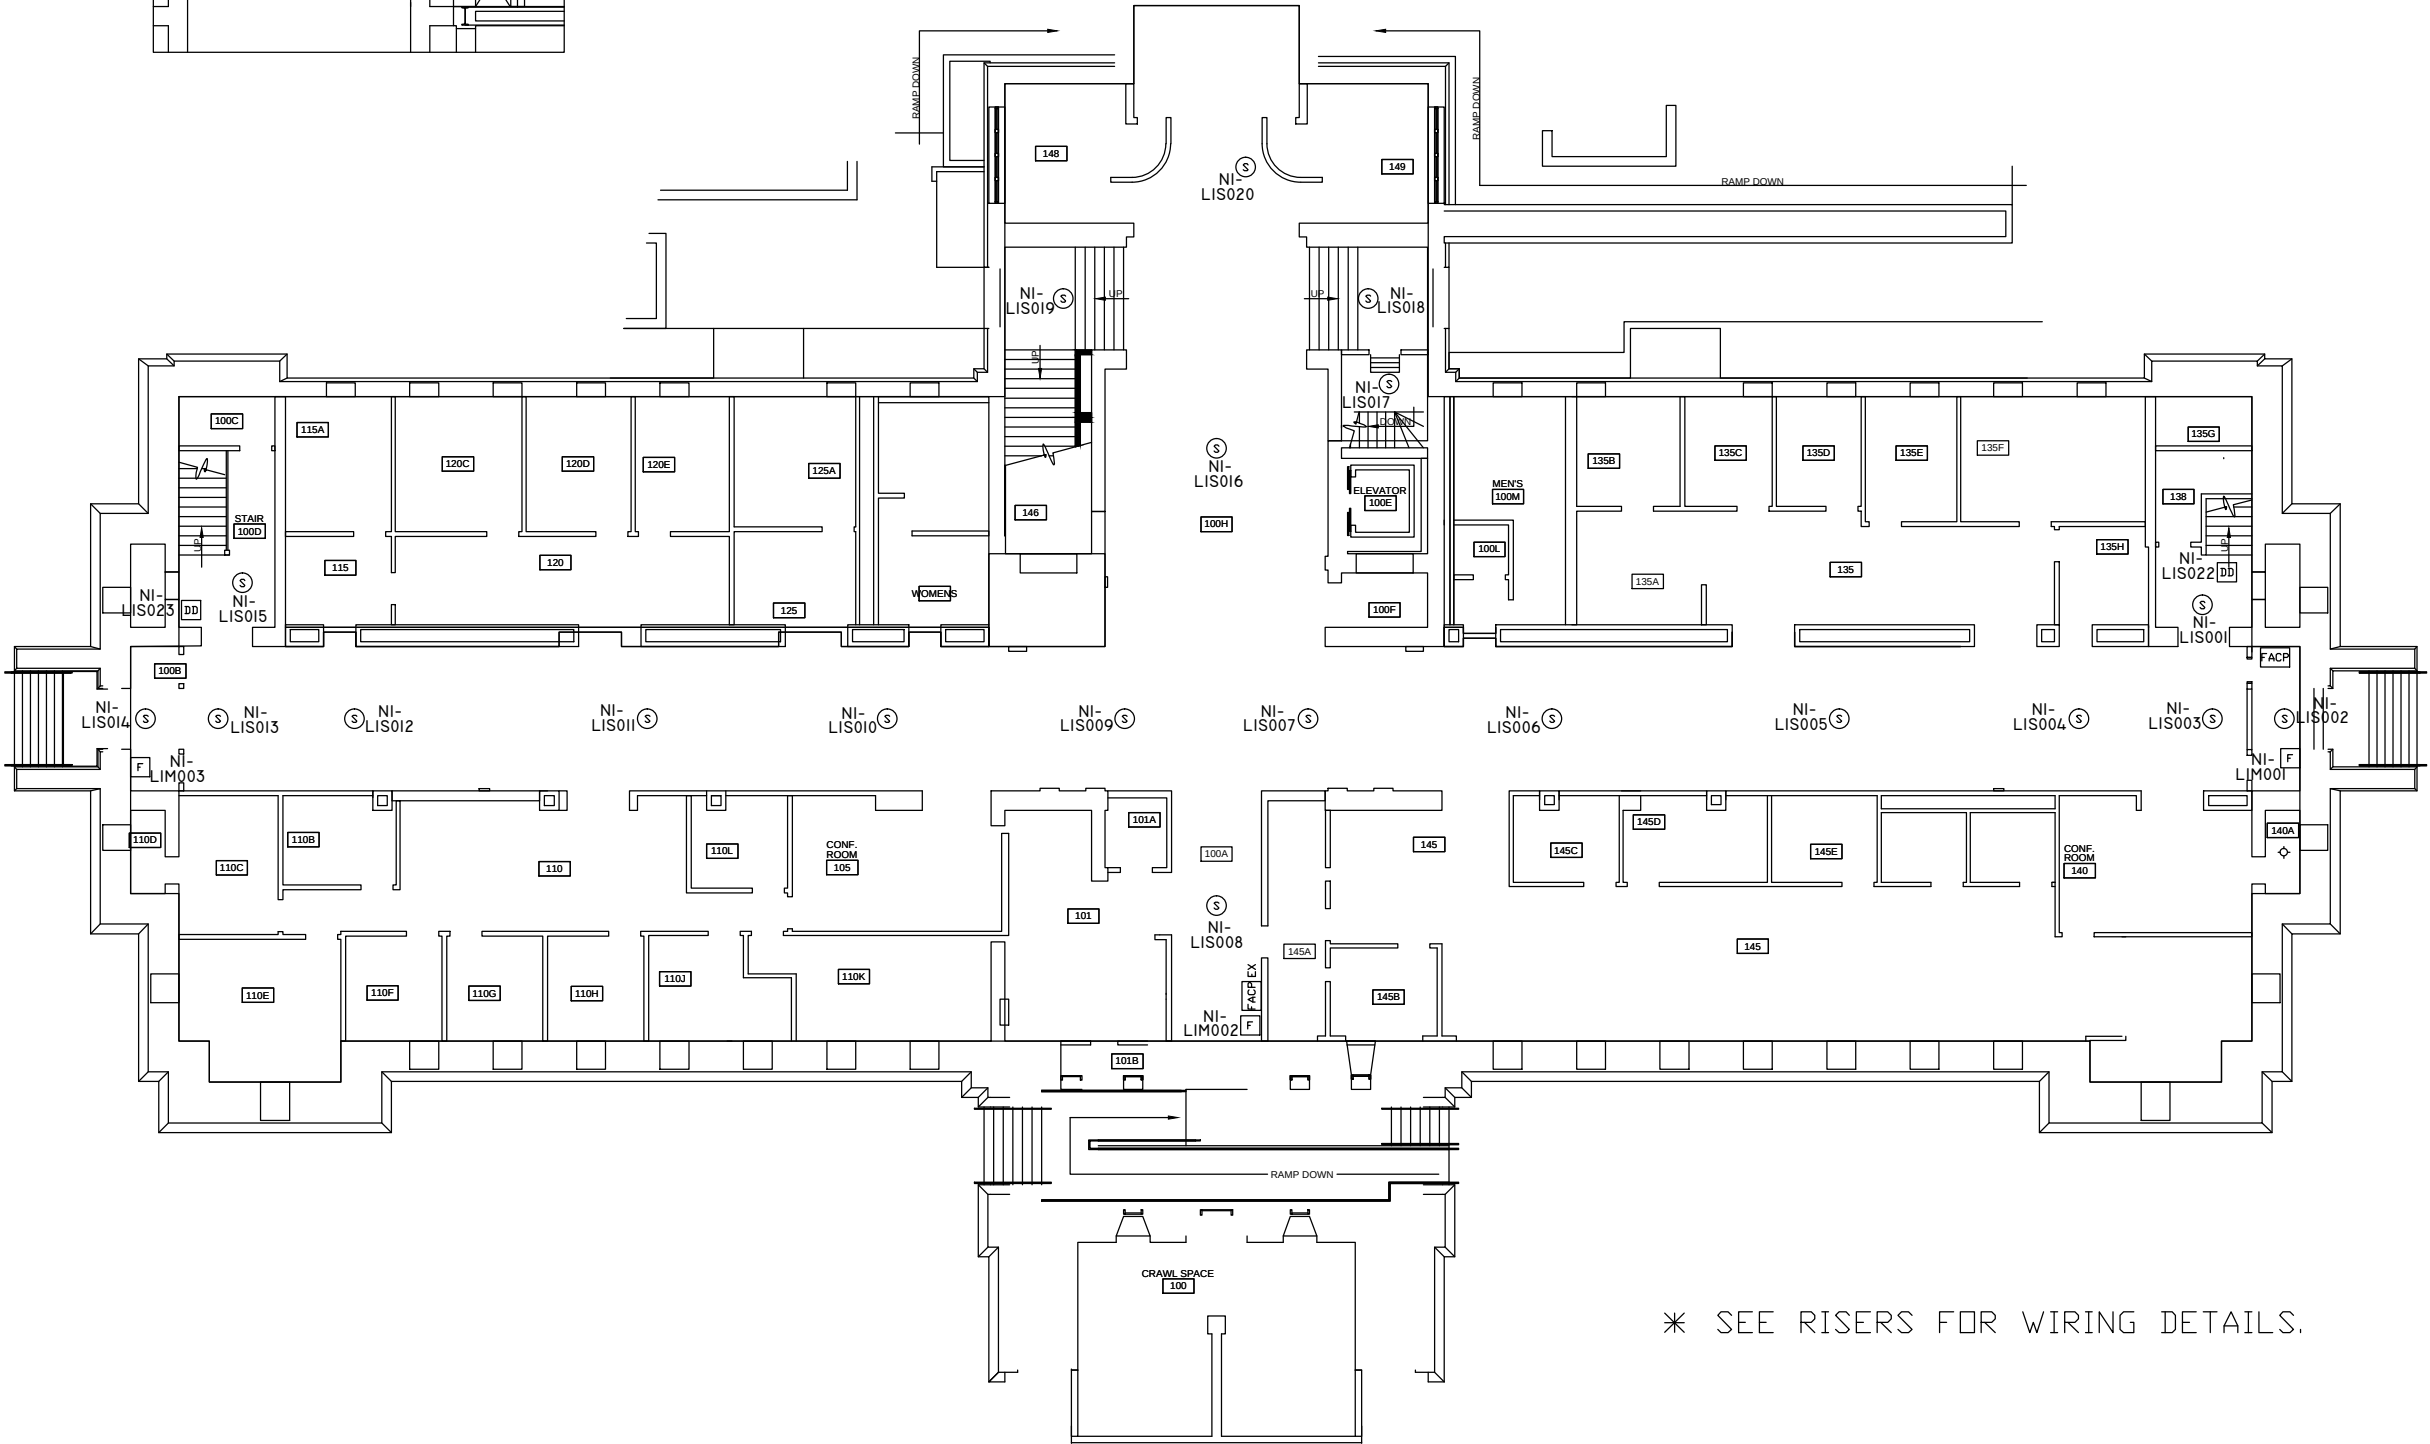

NOTE:
NFS DRAWINGS ARE BASED ON THE PROJECT
ARCHITECT/ENGINEER (A/E) PLANS AND SPECIFICATIONS
FURNISHED TO NFS. A/E IS SOLELY RESPONSIBLE
(NOT NFS) FOR THE TYPE, SIZE, LOCATION, AND
SUITABILITY OF ALL FIRE ALARMS, CONTROL PANELS,
AND OTHER DEVICES SHOWN ON THE A/E PLANS.
NFS DRAWINGS ARE TO SHOW ONLY THE WIRING
DIAGRAMS BETWEEN FIRE ALARM DEVICES AND
CONTROL PANELS. NFS IS NOT RESPONSIBLE FOR
THE INFORMATION SHOWN ON THE A/E PLANS.

PARK BUILDING
FIRST FLOOR
UNIVERSITY OF UTAH
FIRE ALARM SYSTEM

NFS


NELSON FIRE SYSTEMS
801-468-8300

DRAWN BY: DS
DESIGNED BY: XXXX
CHECKED BY: DS
DATE: 1/21/2009
SCALE: N.T.S.
PROJECT NO: 07040
REV NO: XXXX
DRAWING NAME:
IST FLOOR.DWG

FIRE ALARM SYSTEM
NUMBERS


PAGE:

FA-I-03

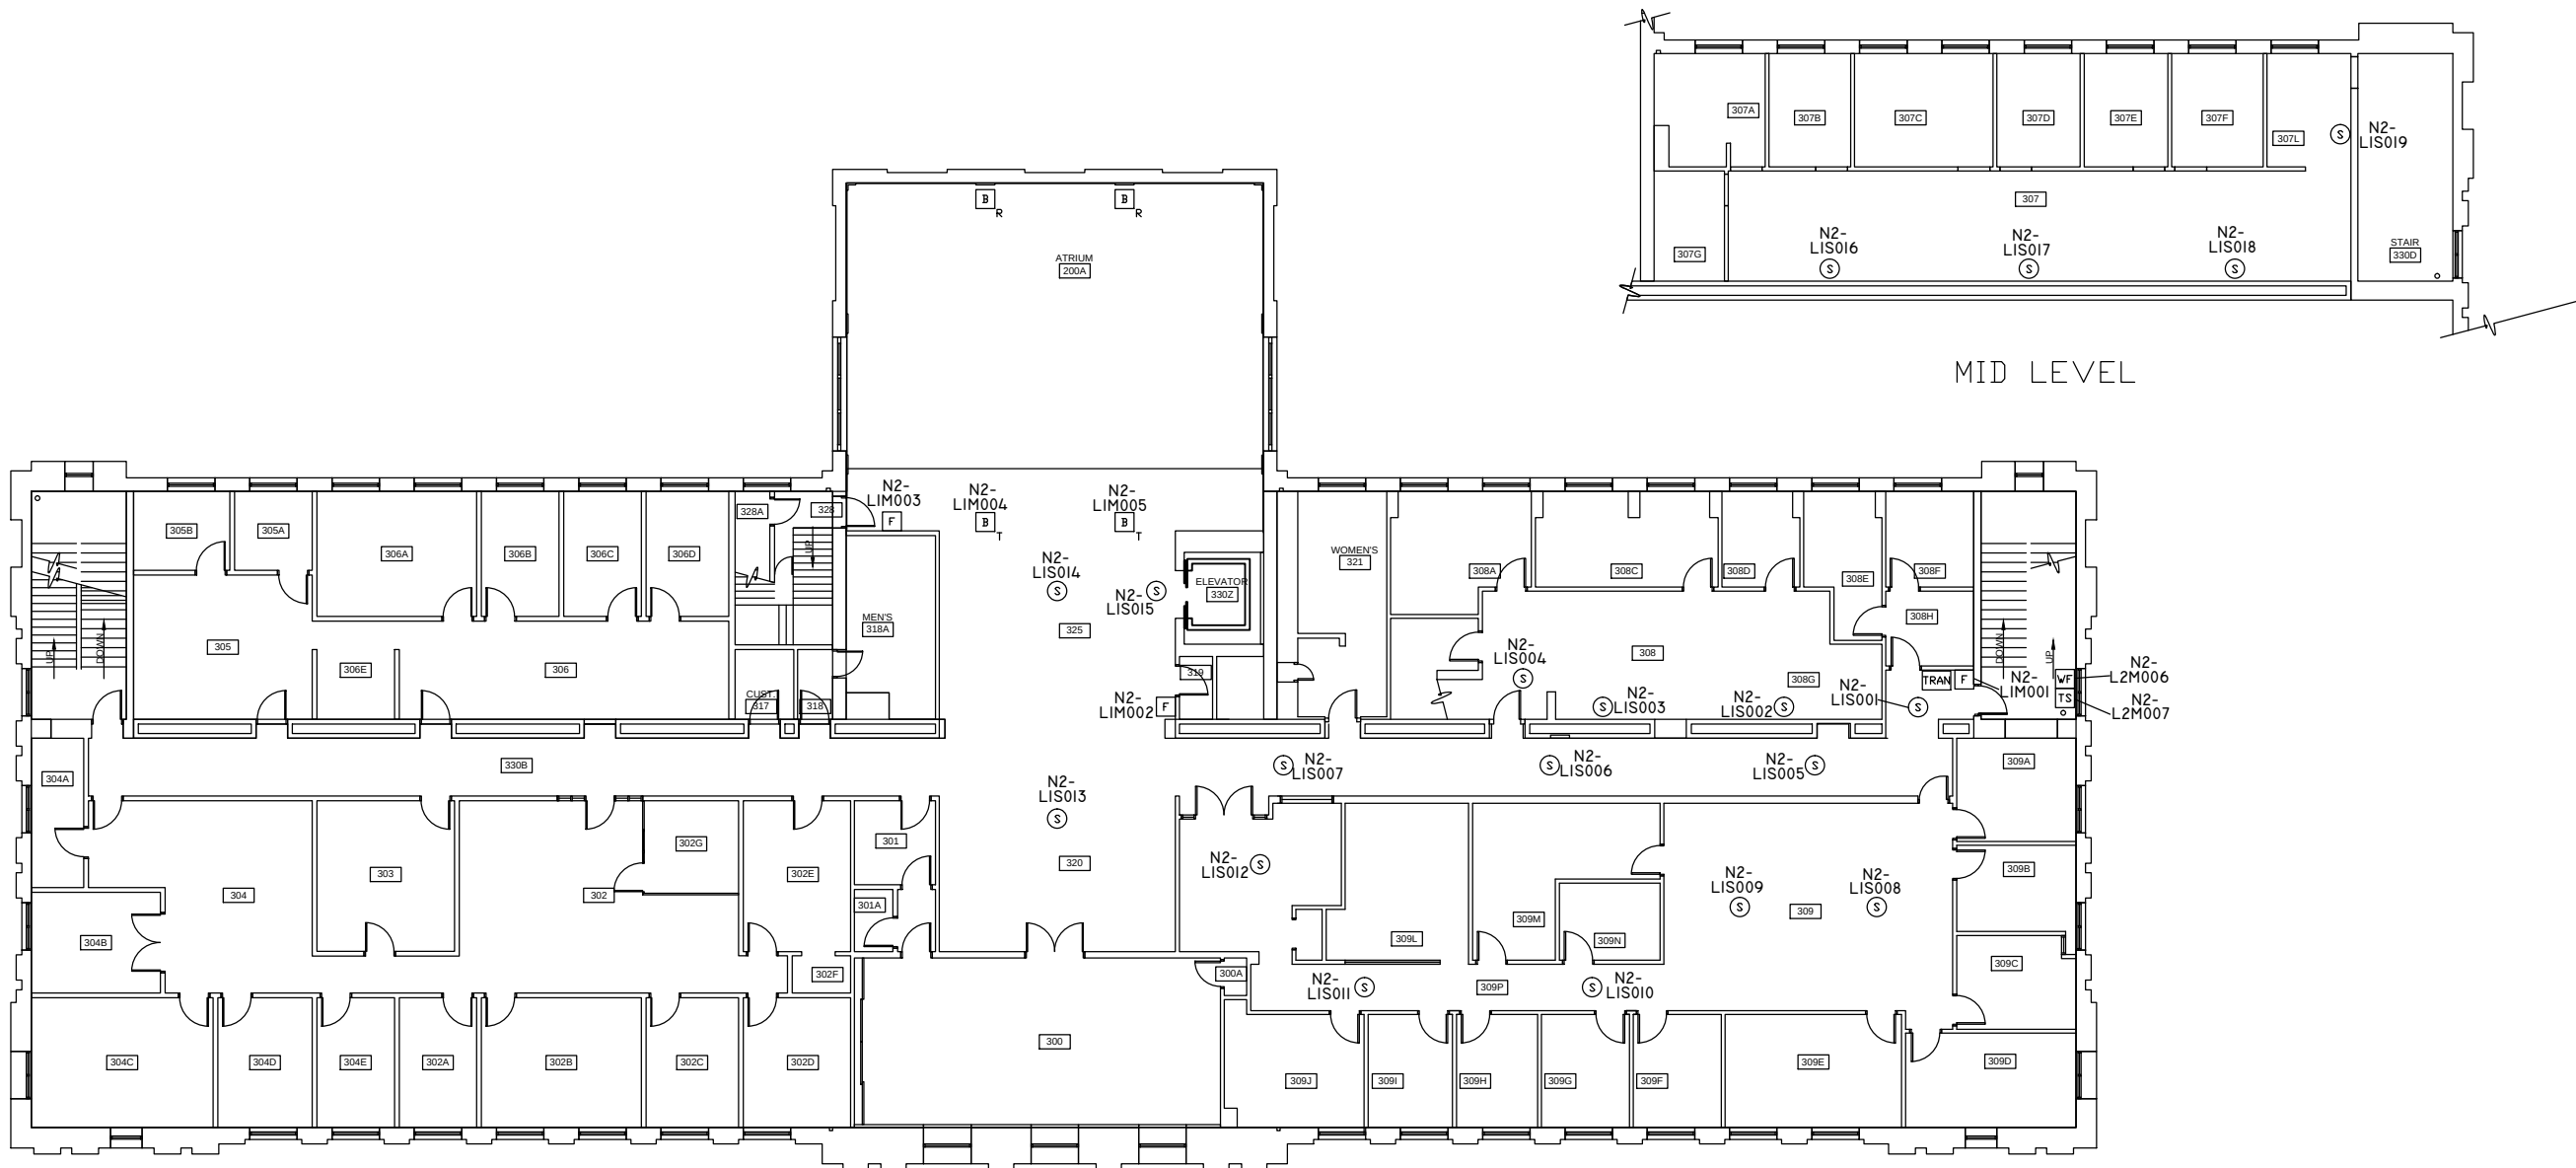

MID LEVEL

DEVICE LEGEND	
SYMBOL	DESCRIPTION
(S)	SMOKE DETECTOR
(T)	HEAT DETECTOR
CM	CONTROL MODULE
M	MONITOR MODULE
B _T	BEAM DETECTOR TRANSMITTER
B _R	BEAM DETECTOR REFLECTOR
B _{TS}	BEAM DETECTOR TEST SWITCH
DD	DUCT DETECTOR
F	PULL STATION
RA	REMOTE ANNUNCIATOR
PIV	POST INDICATOR VALVE
FACP	FIRE ALARM CONTROL PANEL
TRAN	TRANSPONDER PANEL

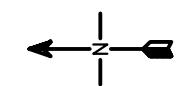


NOTE:
NFS DRAWINGS ARE BASED ON THE PROJECT
ARCHITECT/ENGINEER (A/E) PLANS AND SPECIFICATIONS
FURNISHED TO NFS. A/E IS SOLELY RESPONSIBLE
(NOT NFS) FOR THE TYPE, SIZE, LOCATION, AND
SUITABILITY OF ALL FIRE ALARMS, CONTROL PANELS,
AND OTHER DEVICES SHOWN ON THE A/E PLANS.
NFS DRAWINGS ARE TO SHOW ONLY THE WIRING
DIAGRAMS BETWEEN FIRE ALARM DEVICES AND
CONTROL PANELS. NFS IS NOT RESPONSIBLE FOR
THE INFORMATION SHOWN ON THE A/E PLANS.

PARK BUILDING
THIRD FLOOR
UNIVERSITY OF UTAH
FIRE ALARM SYSTEM


NFS
NELSON FIRE SYSTEMS
801-468-8300

DRAWN BY:	DS
DESIGNED BY:	XXXX
CHECKED BY:	DS
DATE:	1/21/2009
SCALE:	N.T.S.
PROJECT NO:	07040
REV NO:	XXXX
DRAWING NAME:	3RD FLOOR.DWG

FIRE ALARM SYSTEM
NUMBERS

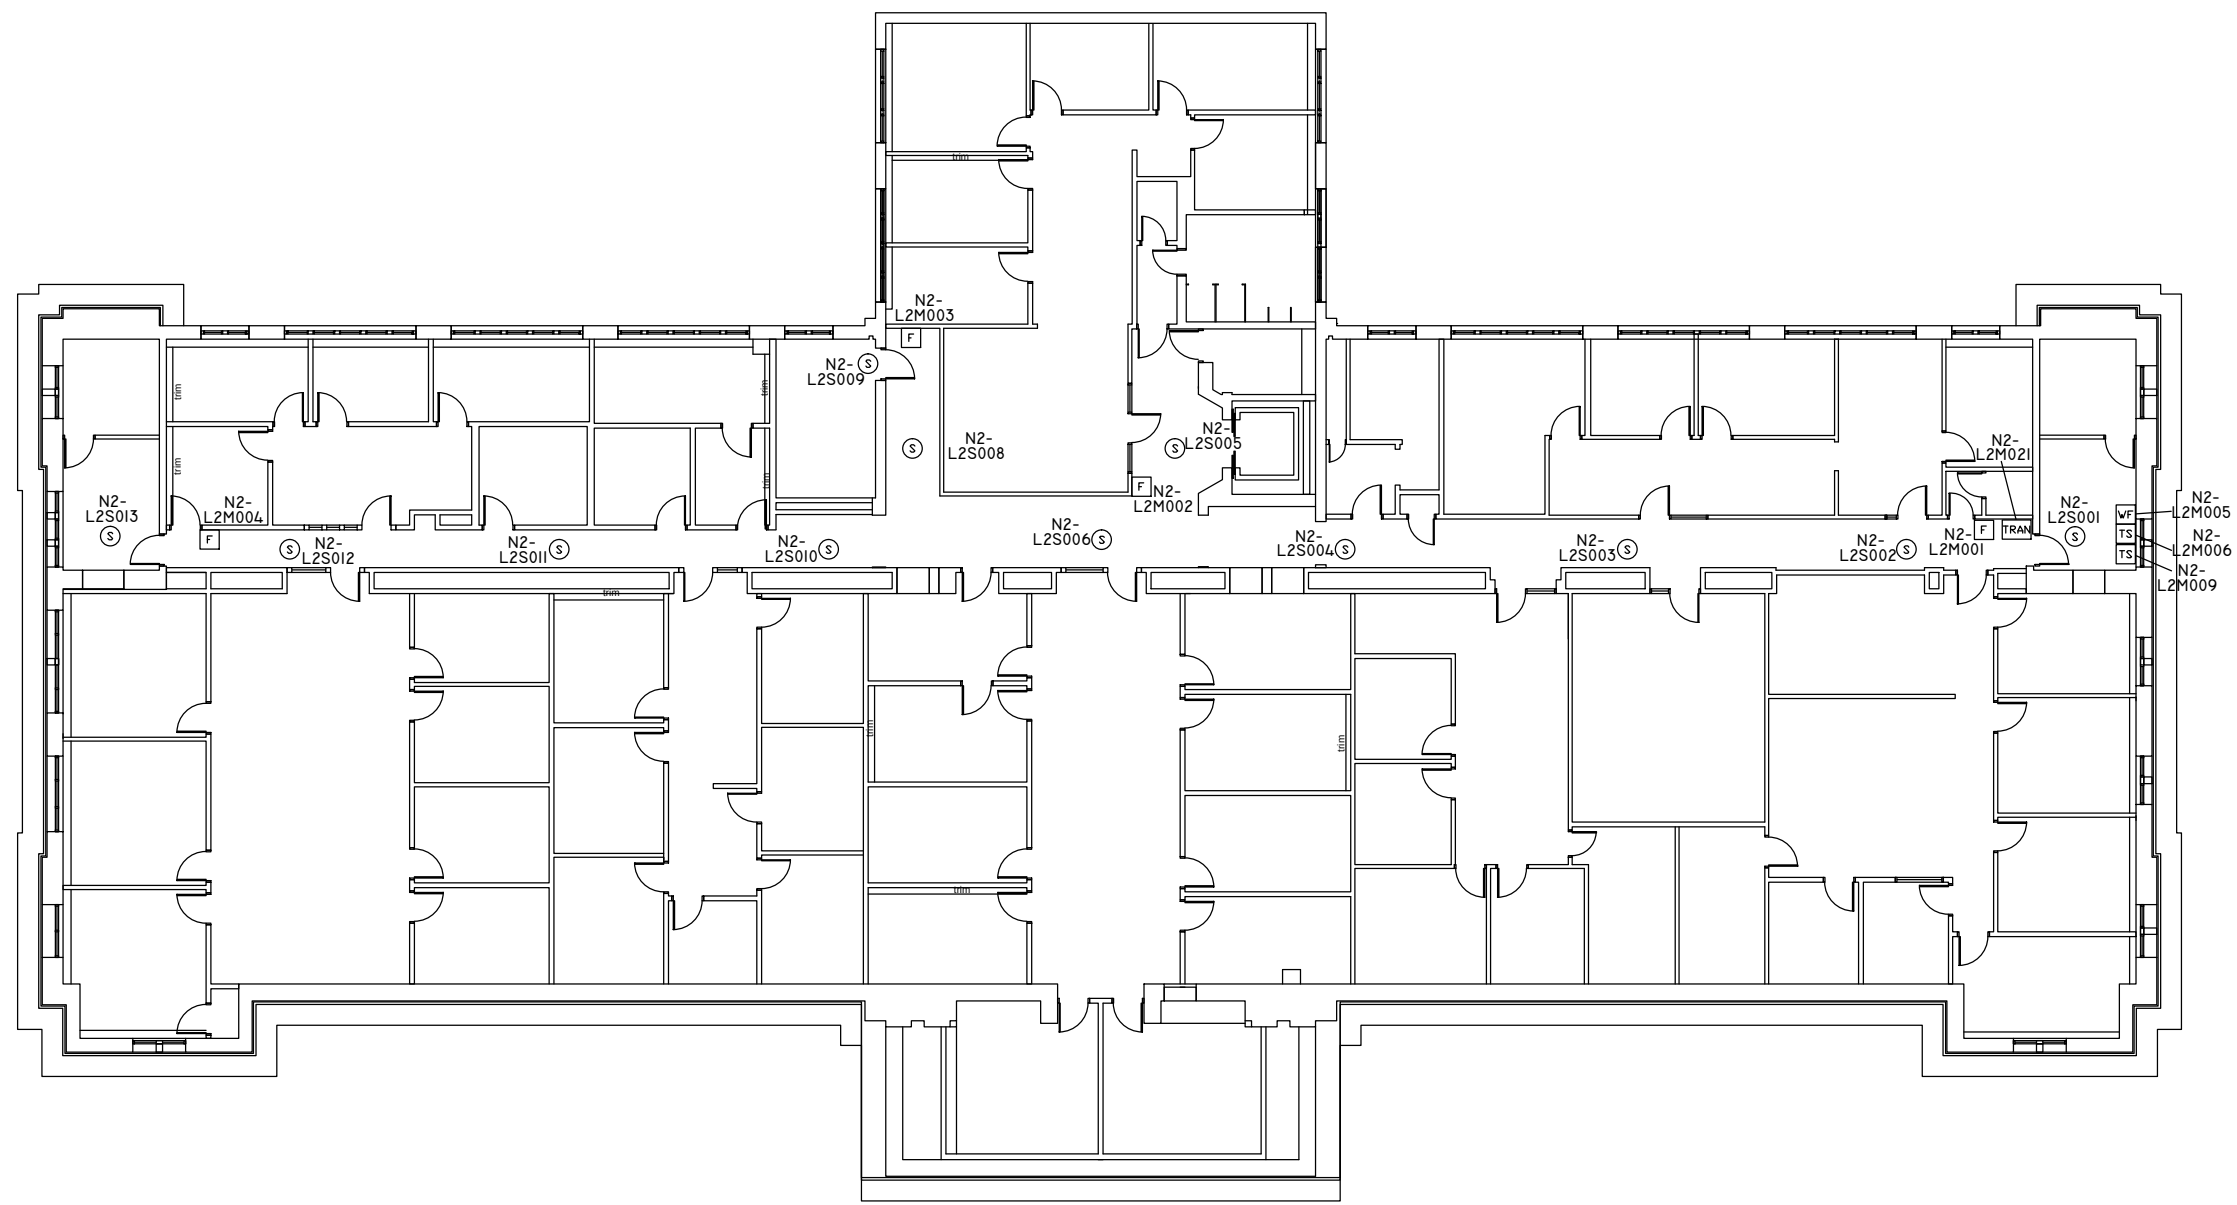

DEVICE LEGEND	
SYMBOL	DESCRIPTION
Ⓢ	SMOKE DETECTOR
Ⓣ	HEAT DETECTOR
CM	CONTROL MODULE
MM	MONITOR MODULE
B _t	BEAM DETECTOR TRANSMITTER
B _r	BEAM DETECTOR REFLECTOR
B _{TS}	BEAM DETECTOR TEST SWITCH
DD	DUCT DETECTOR
F	PULL STATION
RA	REMOTE ANNUNCIATOR
PIV	POST INDICATOR VALVE
FACP	FIRE ALARM CONTROL PANEL
TRAN	TRANSPONDER PANEL

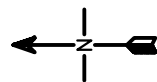

NOTE:
NFS DRAWINGS ARE BASED ON THE PROJECT
ARCHITECT/ENGINEER (A/E) PLANS AND SPECIFICATIONS
FURNISHED TO NFS. A/E IS SOLELY RESPONSIBLE
(NOT NFS) FOR THE TYPE, SIZE, LOCATION, AND
SUITABILITY OF ALL FIRE ALARMS, CONTROL PANELS,
AND OTHER DEVICES SHOWN ON THE A/E PLANS.
NFS DRAWINGS ARE TO SHOW ONLY THE WIRING
DIAGRAMS BETWEEN FIRE ALARM DEVICES AND
CONTROL PANELS. NFS IS NOT RESPONSIBLE FOR
THE INFORMATION SHOWN ON THE A/E PLANS.

PARK BUILDING
FOURTH FLOOR
UNIVERSITY OF UTAH
FIRE ALARM SYSTEM

NFS
NELSON FIRE SYSTEMS
801-468-8300


DRAWN BY:	AK
DESIGNED BY:	XXXX
CHECKED BY:	DS
DATE:	1/21/2009
SCALE:	N.T.S.
PROJECT NO:	07040
REV NO:	XXXX
DRAWING NAME:	4TH FLOOR.DWG

FIRE ALARM SYSTEM
NUMBERS


PAGE:

FA-4-03

* SEE RISERS FOR WIRING DETAILS.

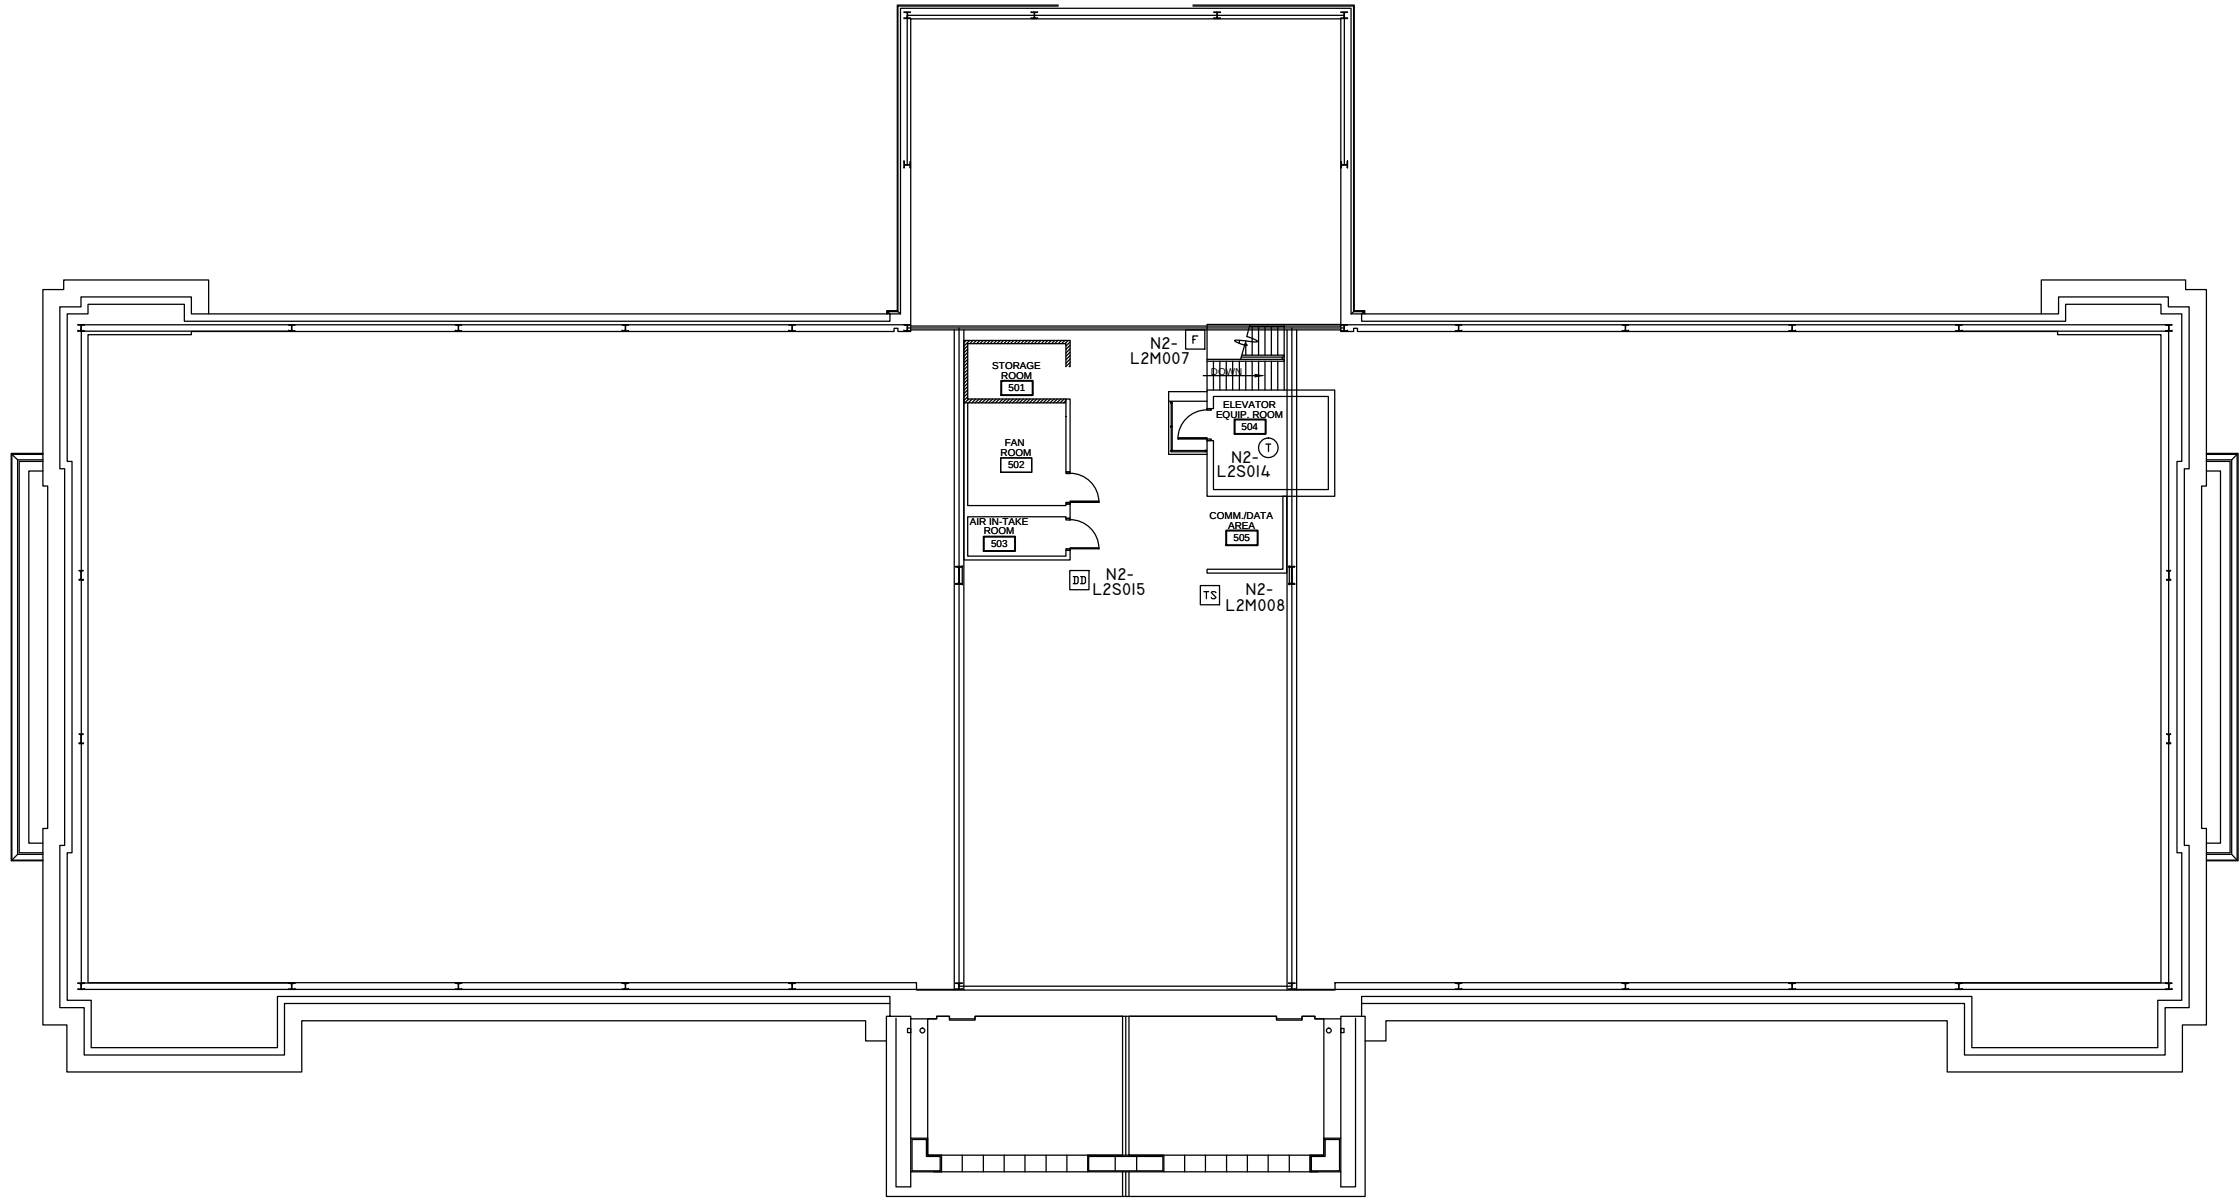

DEVICE LEGEND	
SYMBOL	DESCRIPTION
⊙	SMOKE DETECTOR
⊖	HEAT DETECTOR
CH	CONTROL MODULE
MM	MONITOR MODULE
B _T	BEAM DETECTOR TRANSMITTER
B _R	BEAM DETECTOR REFLECTOR
B _{TS}	BEAM DETECTOR TEST SWITCH
DD	DUCT DETECTOR
F	PULL STATION
RA	REMOTE ANNUNCIATOR
PIV	POST INDICATOR VALVE
FACP	FIRE ALARM CONTROL PANEL
TRAN	TRANSPONDER PANEL

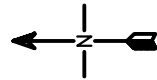

NOTE:
NFS DRAWINGS ARE BASED ON THE PROJECT
ARCHITECT/ENGINEER (A/E) PLANS AND SPECIFICATIONS
FURNISHED TO NFS. A/E IS SOLELY RESPONSIBLE
(NOT NFS) FOR THE TYPE, SIZE, LOCATION, AND
SUITABILITY OF ALL FIRE ALARMS, CONTROL PANELS,
AND OTHER DEVICES SHOWN ON THE A/E PLANS.
NFS DRAWINGS ARE TO SHOW ONLY THE WIRING
DIAGRAMS BETWEEN FIRE ALARM DEVICES AND
CONTROL PANELS. NFS IS NOT RESPONSIBLE FOR
THE INFORMATION SHOWN ON THE A/E PLANS.

PARK BUILDING
ATTIC
UNIVERSITY OF UTAH
FIRE ALARM SYSTEM

NFS


NELSON FIRE SYSTEMS
801-468-8300

DRAWN BY:	DS
DESIGNED BY:	XXXX
CHECKED BY:	DS
DATE:	1/21/2009
SCALE:	N.T.S.
PROJECT NO:	07040
REV NO:	XXXX
DRAWING NAME:	ATTIC.DWG


FIRE ALARM SYSTEM
NUMBERS

PAGE:

FA-A-03

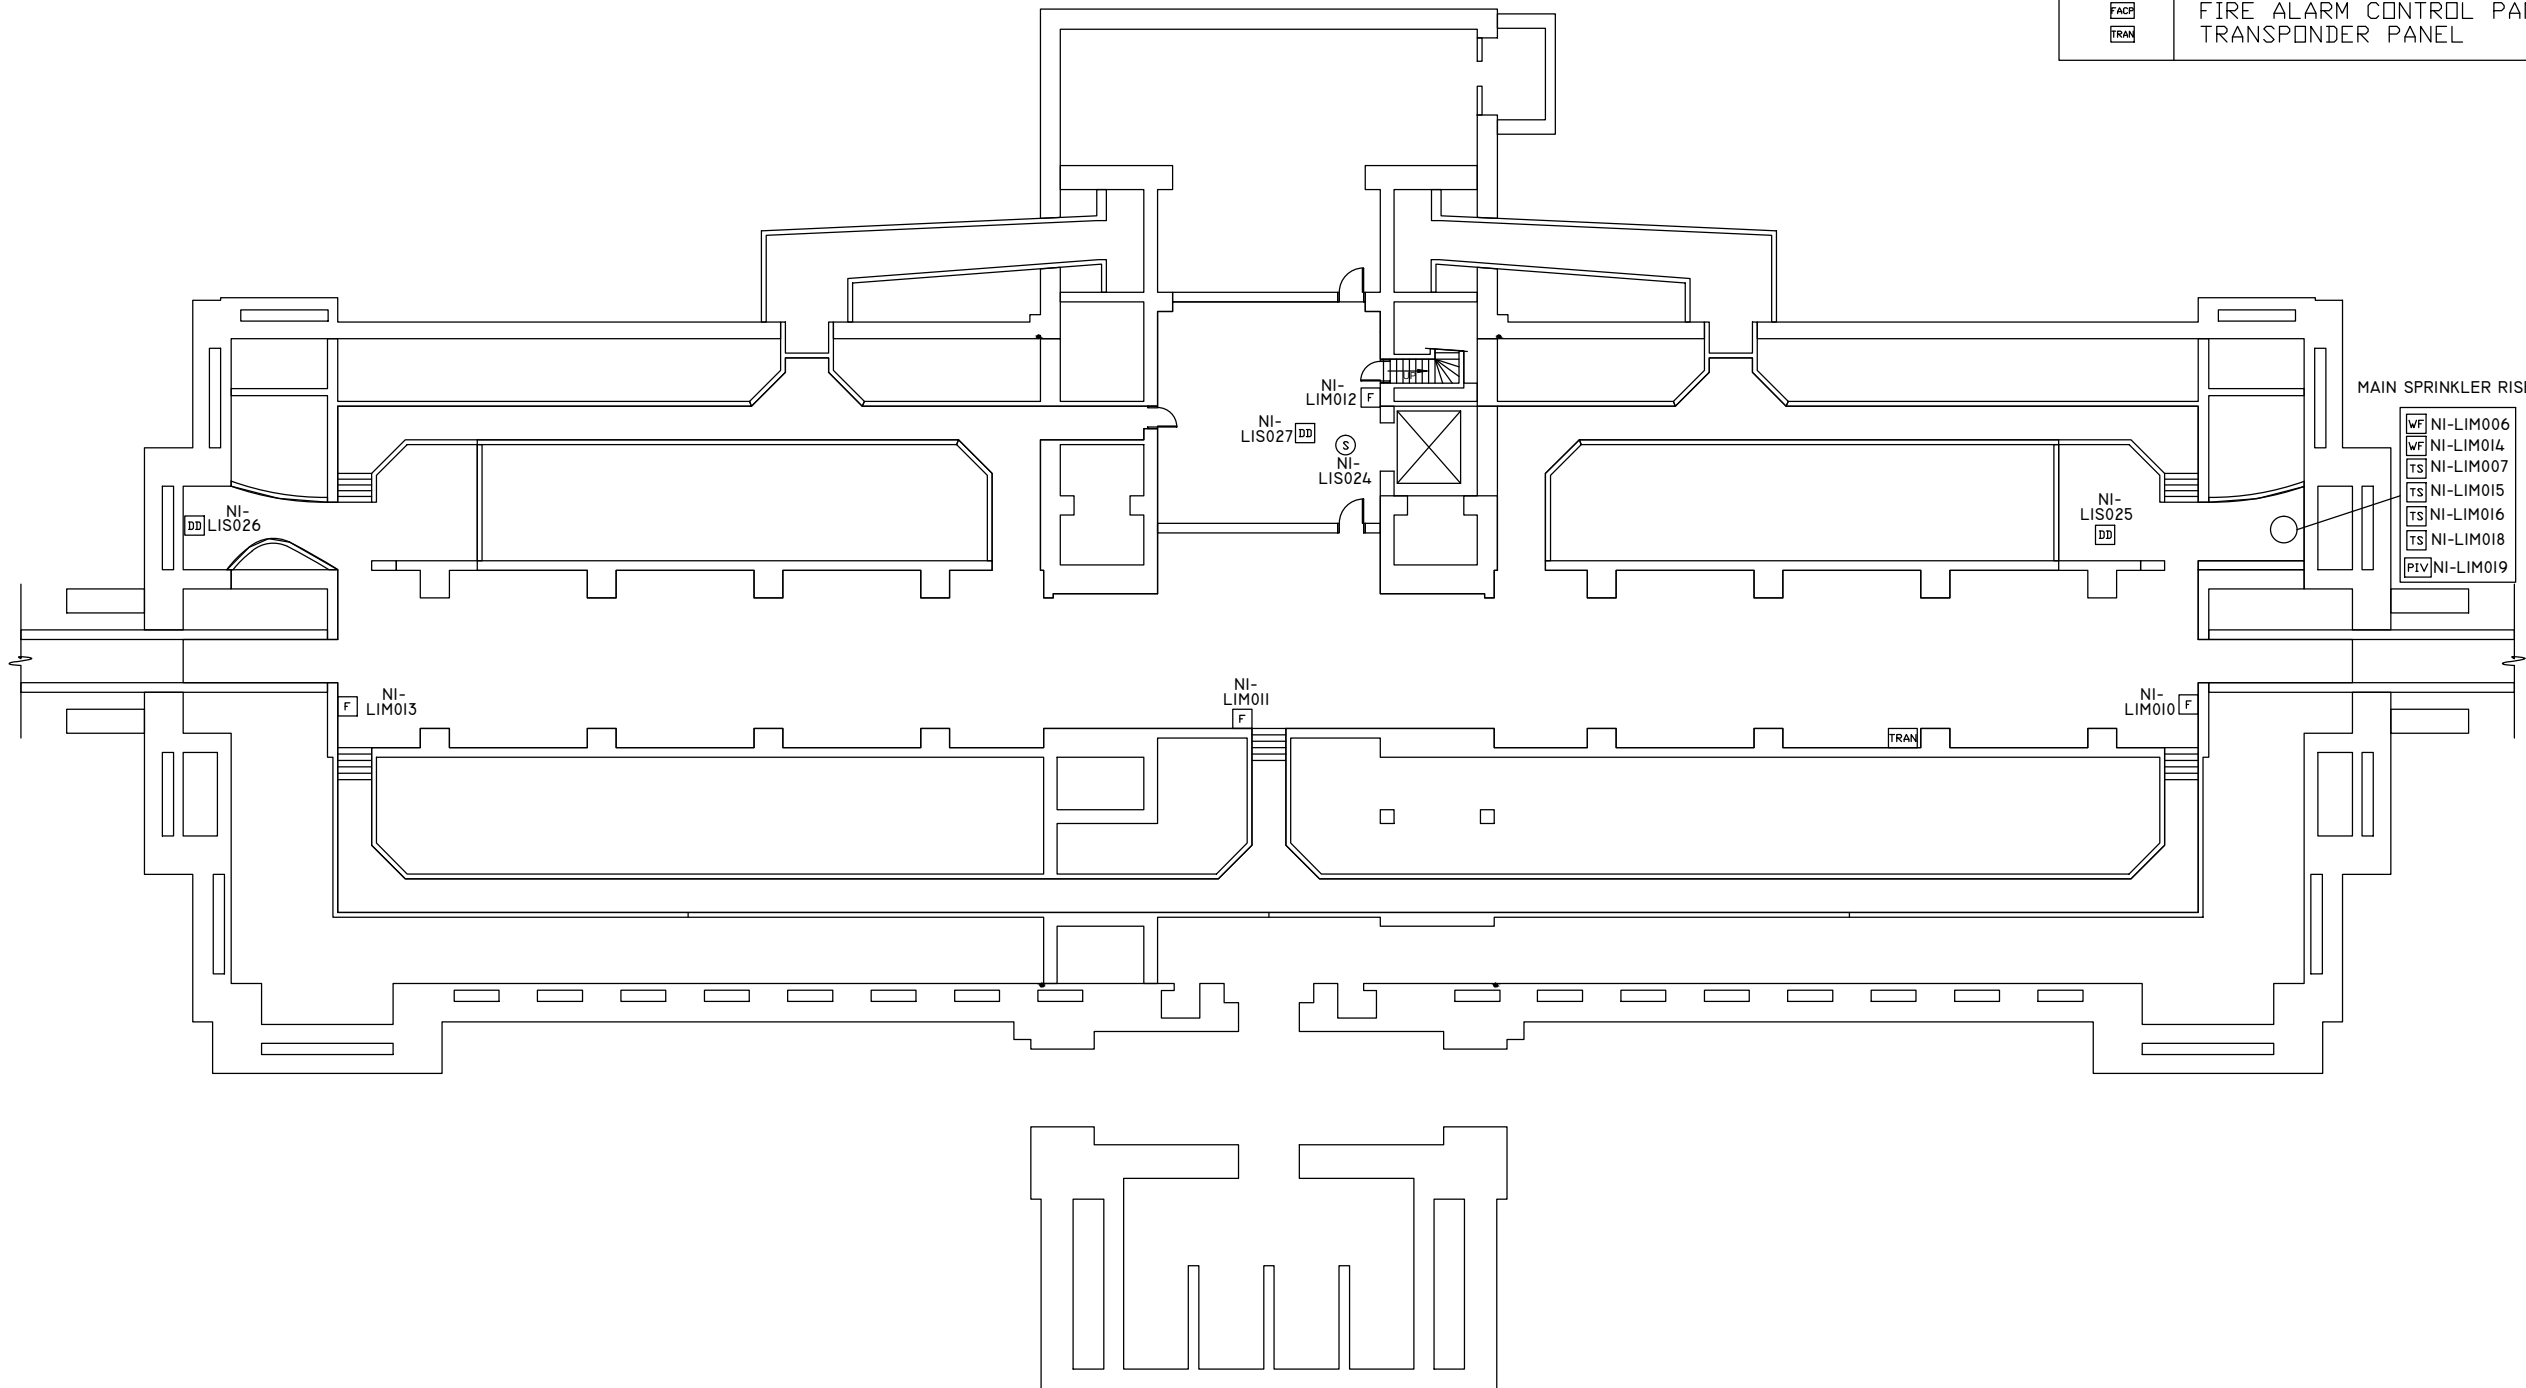

DEVICE LEGEND	
SYMBOL	DESCRIPTION
Ⓢ	SMOKE DETECTOR
Ⓣ	HEAT DETECTOR
CM	CONTROL MODULE
MM	MONITOR MODULE
B _T	BEAM DETECTOR TRANSMITTER
B _R	BEAM DETECTOR REFLECTOR
B _{TS}	BEAM DETECTOR TEST SWITCH
DD	DUCT DETECTOR
F	PULL STATION
RA	REMOTE ANNUNCIATOR
PIV	POST INDICATOR VALVE
FACP	FIRE ALARM CONTROL PANEL
TRAN	TRANSPONDER PANEL

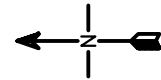

NOTE:
NFS DRAWINGS ARE BASED ON THE PROJECT
ARCHITECT/ENGINEER (A/E) PLANS AND SPECIFICATIONS
FURNISHED TO NFS. A/E IS SOLELY RESPONSIBLE
(NOT NFS) FOR THE TYPE, SIZE, LOCATION, AND
SUITABILITY OF ALL FIRE ALARMS, CONTROL PANELS,
AND OTHER DEVICES SHOWN ON THE A/E PLANS.
NFS DRAWINGS ARE TO SHOW ONLY THE WIRING
DIAGRAMS BETWEEN FIRE ALARM DEVICES AND
CONTROL PANELS. NFS IS NOT RESPONSIBLE FOR
THE INFORMATION SHOWN ON THE A/E PLANS.

PARK BUILDING
BASEMENT
UNIVERSITY OF UTAH
FIRE ALARM SYSTEM

NFS

NELSON FIRE SYSTEMS
801-468-8300

DRAWN BY:	DS
DESIGNED BY:	XXXX
CHECKED BY:	DS
DATE:	1/21/2009
SCALE:	N.T.S.
PROJECT NO:	07040
REV NO:	XXXX
DRAWING NAME:	BASEMENT.DWG

FIRE ALARM SYSTEM
NUMBERS

PAGE:

FA-B-03