


LOWER LEVEL

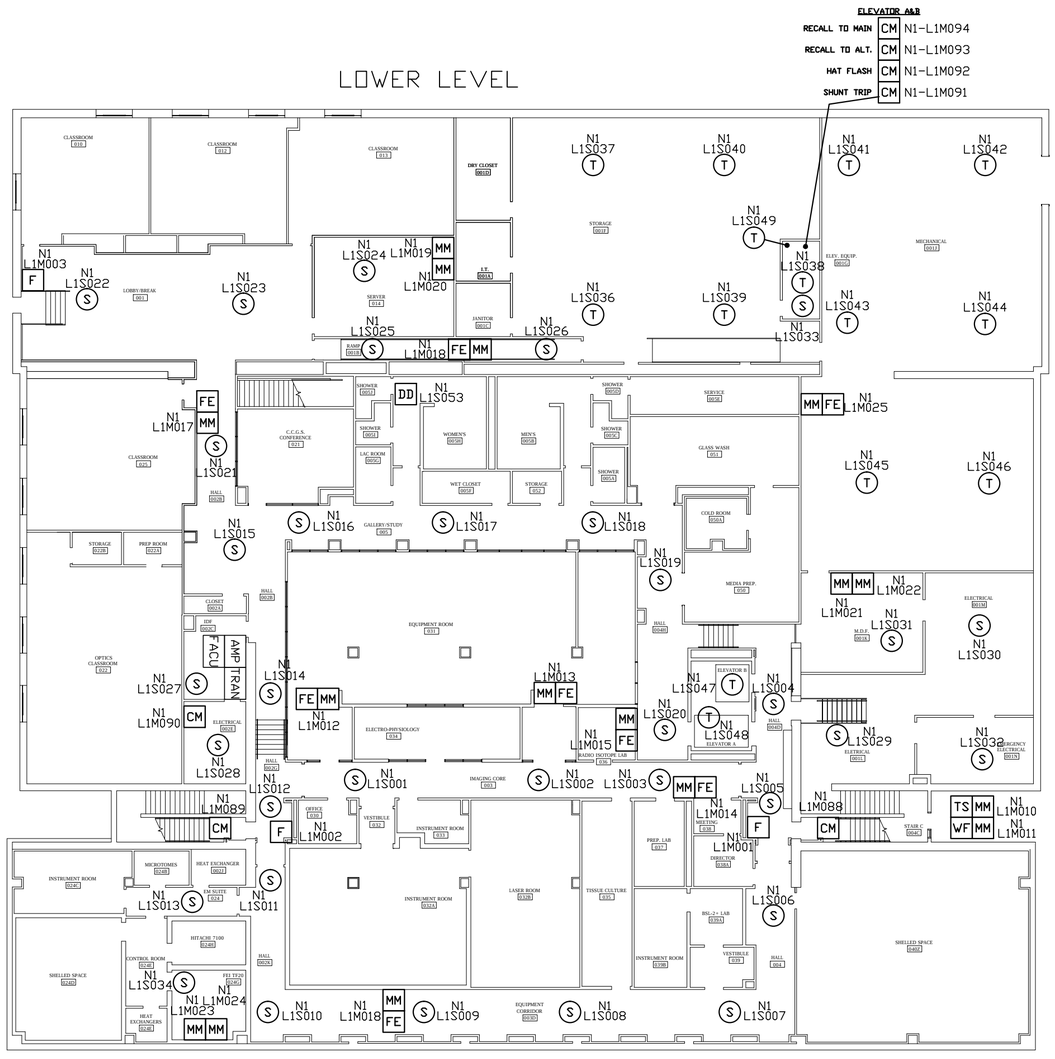


LEVEL 1

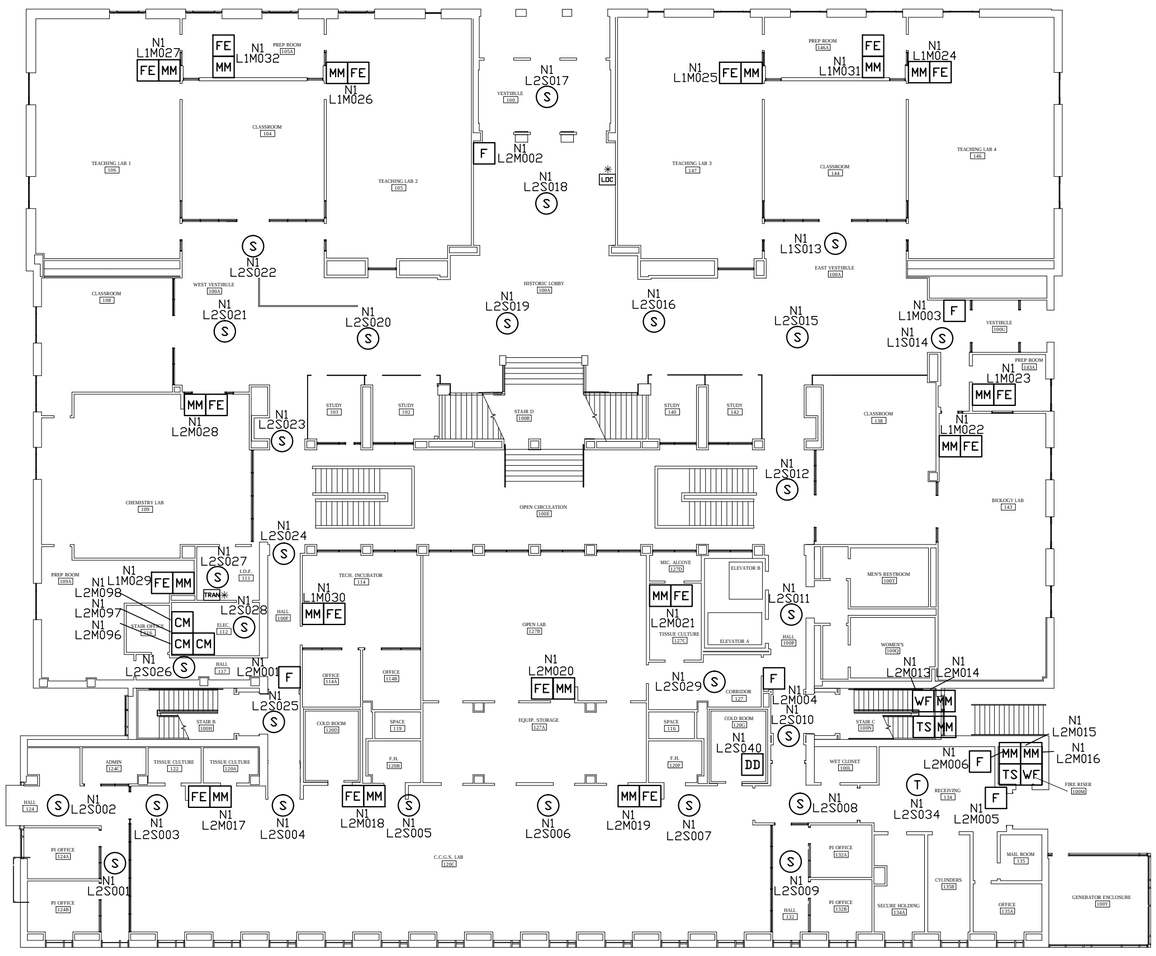


LEVEL 2

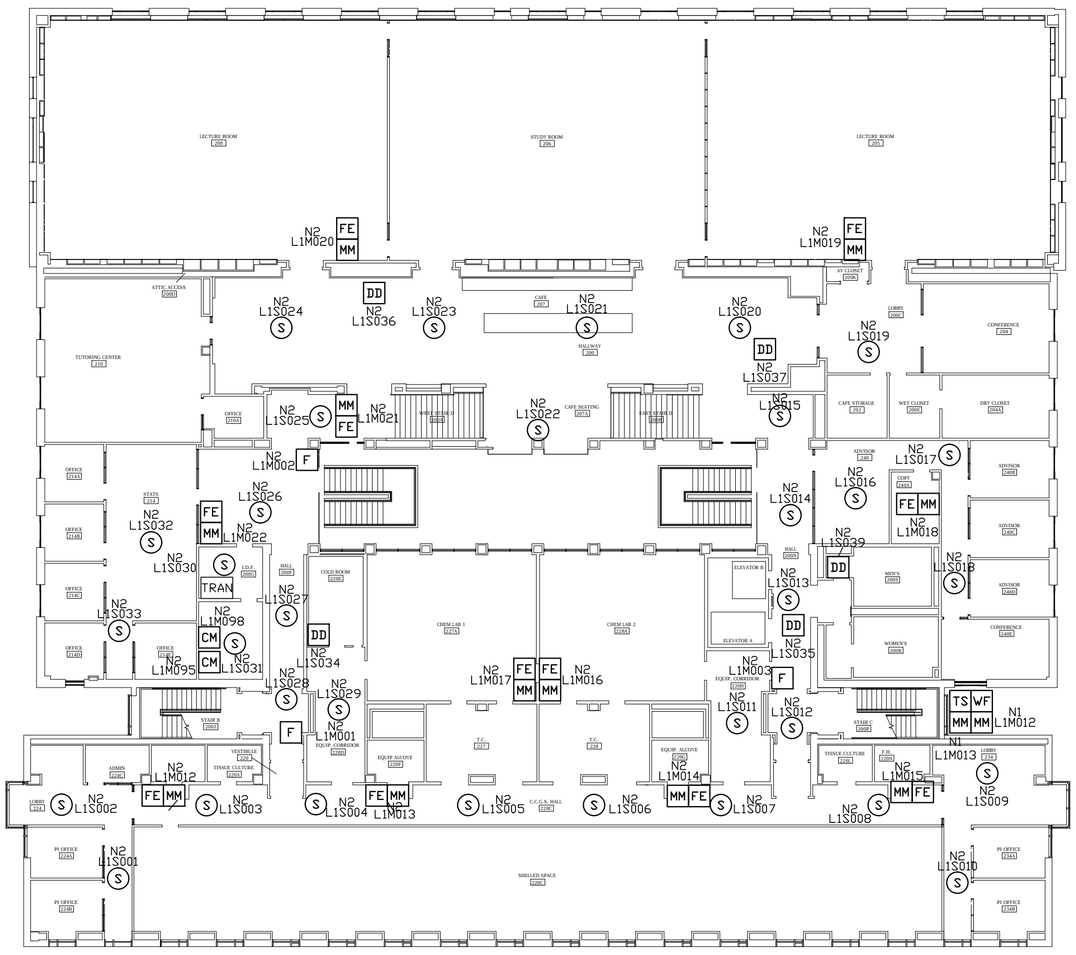

LEVEL 3

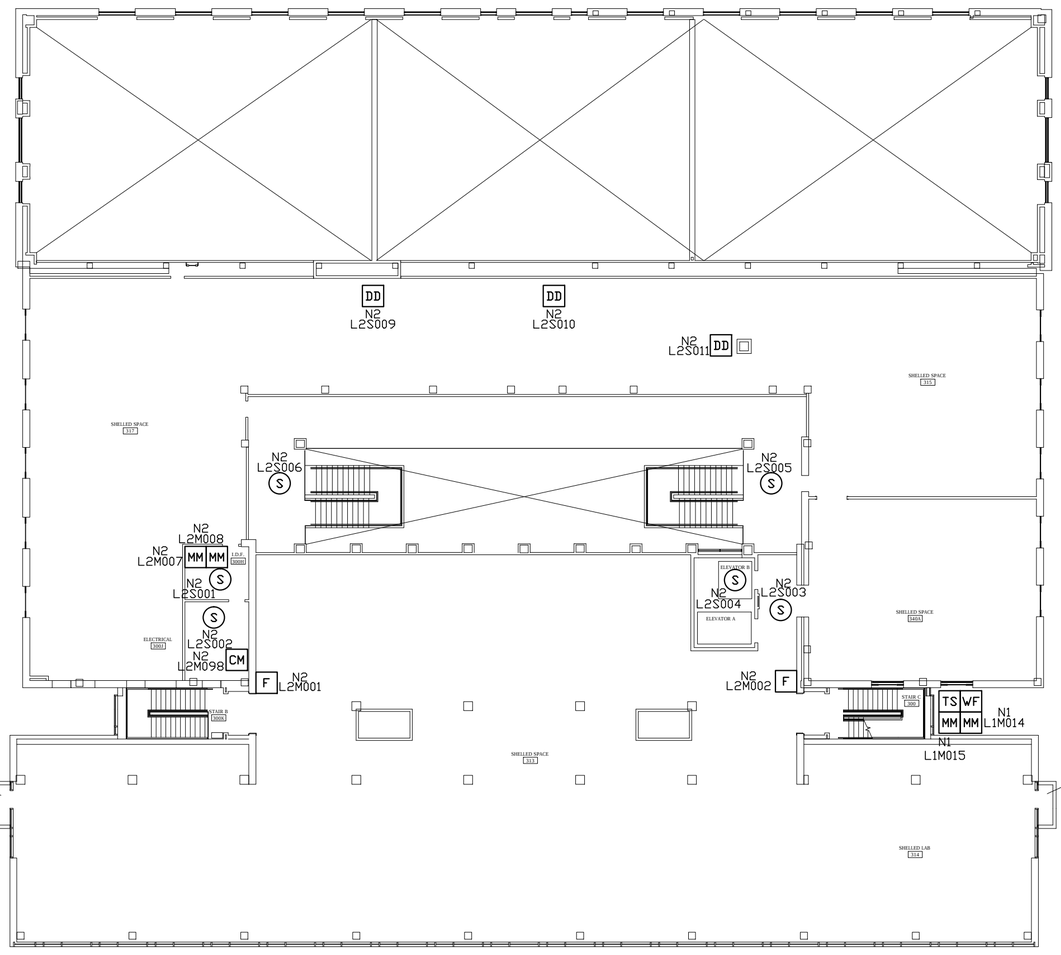

LEVEL 4

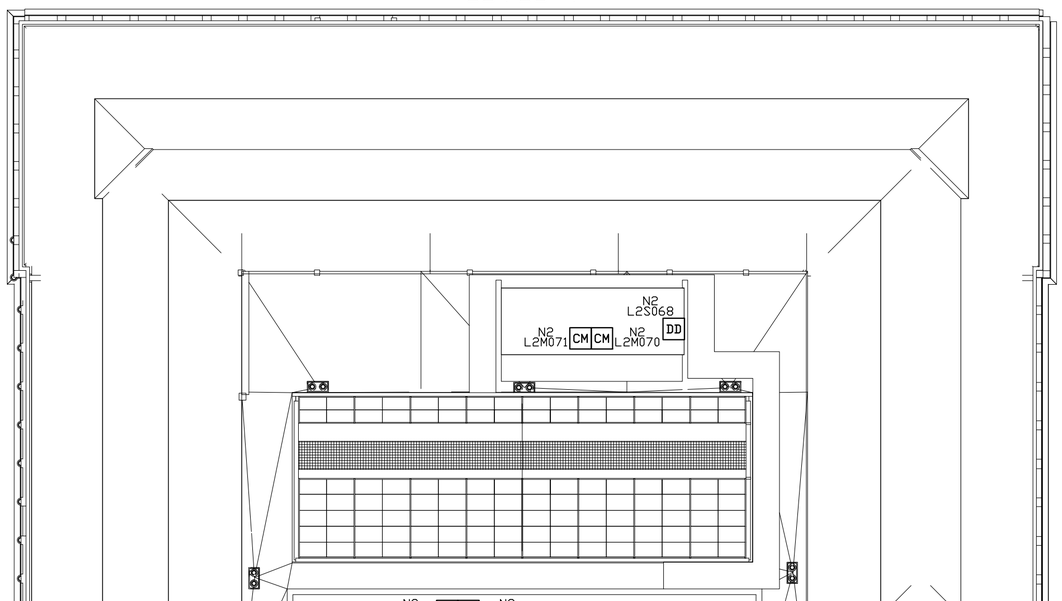

DEVICE LEGEND	
SYMBOL	DESCRIPTION
S	SMOKE DETECTOR
T	HEAT DETECTOR
F	PULL STATION
DD	DUCT DETECTOR
TS	TAMPER SWITCH
WF	WATERFLOW SWITCH
MM	MONITOR MODULE
FE	ENGAUGE FIRE EXTINGUISHER
CM	CONTROL MODULE
RA	REMOTE ANNUNCIATOR
FACU	FIRE ALARM CONTROL UNIT
TRAN	TRANSPONDER PANEL
CMP	CAMPUS MONITORING PANEL
VPS	VESDA POWER SUPPLY
WP	WEATHERPROOF DEVICE
C	CEILING MOUNT DEVICE

N.I.C.E.T.
LEVEL IV
CERTIFICATION
FIRE ALARM SYSTEMS
DONNY SCHULTZ
#104396

PAGE:
FINAL MAP

NELSON FIRE SYSTEMS
ALL LEVELS
NUMBERS

DRAWN BY: AK
DESIGNED BY: XXXX
APPROVED BY: TDT
DATE: 3/1/2017
SCALE: (ARCH C) 1/16" = 1'
PROJECT NO: XXXX
REVISION NO: XXXX
DRAWING NAME:
UofU CROCKER SCIENCE L SS.DWG

NFS
NELSON FIRE SYSTEMS
801-468-8300

UNIVERSITY OF UTAH
CROCKER SCIENCE CENTER
1390 PRESIDENTS CIRCLE
SALT LAKE CITY, UTAH
FIRE ALARM SYSTEM

NOTE:
NFS DRAWINGS ARE BASED ON THE PROJECT ARCHITECTURE/ENGINEER (A/E) PLANS AND SPECIFICATIONS FURNISHED TO NFS. A/E IS SOLELY RESPONSIBLE (NOT NFS) FOR THE TYPE, SIZE, LOCATION, AND SUITABILITY OF ALL FIRE ALARMS, CONTROL PANELS, AND OTHER DEVICES SHOWN ON THE A/E PLANS. NFS DRAWINGS ARE TO SHOW ONLY THE WIRING DIAGRAMS BETWEEN FIRE ALARM DEVICES AND CONTROL PANELS. NFS IS NOT RESPONSIBLE FOR THE INFORMATION SHOWN ON THE A/E PLANS.

N