



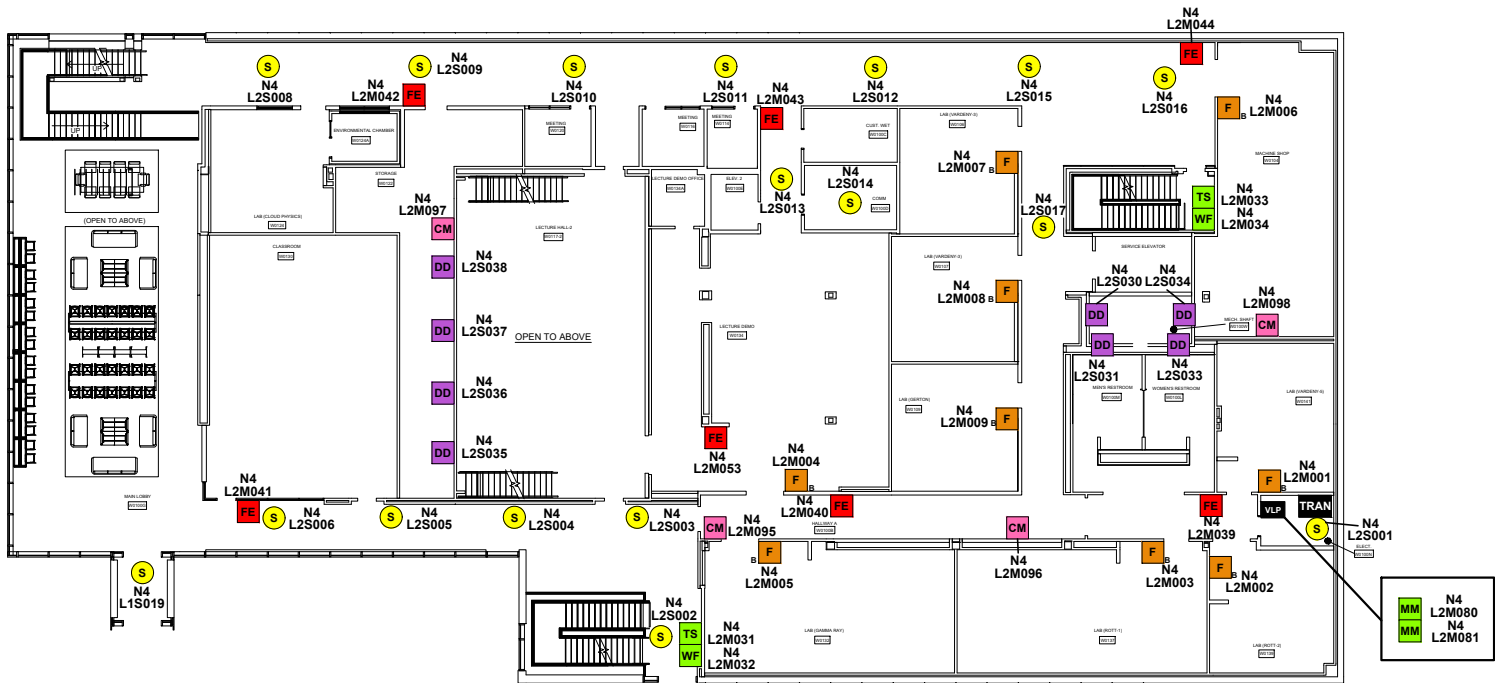

BASEMENT LEVEL 1

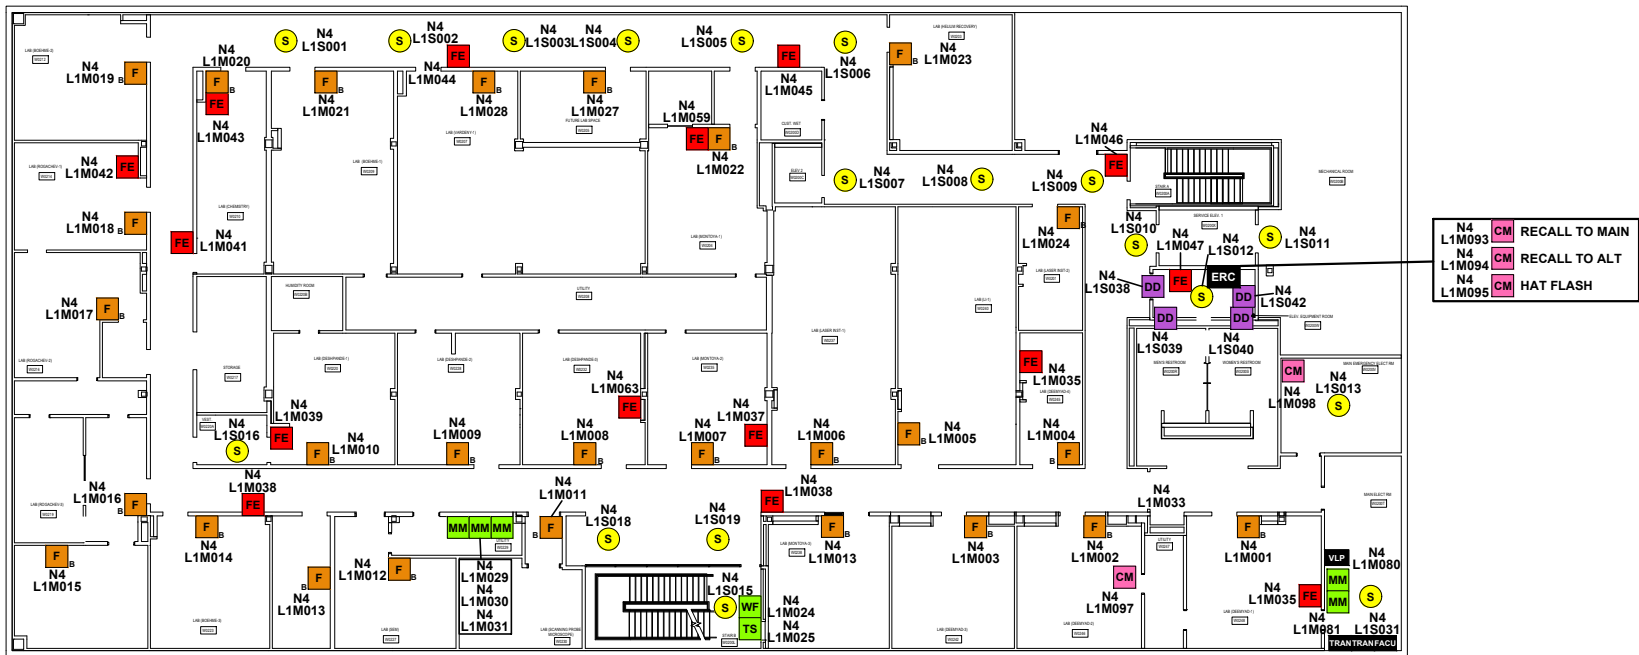

BASEMENT LEVEL 2

DEVICE LEGEND	
SYMBOL	DESCRIPTION
S	SMOKE DETECTOR
F	PULL STATION - BLUE
F	PULL STATION
DD	DUCT DETECTOR
MM	MONITOR MODULE
WF	WATER FLOW SWITCH MODULE
TS	TAMPER SWITCH MODULE
CM	CONTROL MODULE
FE	FIRE EXTINGUISHER
FACU	FIRE ALARM CONTROL UNIT
TRAN	TRANSPONDER PANEL
VLP	VESDA LASER PLUS
TW	TWO-WAY COMM. PANEL
TW	TWO-WAY COMM. STATION



NOTE:
NFS DRAWINGS ARE BASED ON THE PROJECT
ARCHITECTURE/ENGINEER (A/E) PLANS AND
SPECIFICATIONS FURNISHED TO NFS. A/E IS SOLELY
RESPONSIBLE (NOT NFS) FOR THE TYPE, SIZE,
LOCATION, PANEL SCHEDULING, ALARMS,
THE A/E PLANS. NFS DRAWINGS ARE TO SHOW ONLY
THE WIRING DIAGRAMS BETWEEN FIRE ALARM
DEVICES AND CONTROL PANELS. NFS IS NOT
RESPONSIBLE FOR THE INFORMATION SHOWN ON THE
A/E PLANS.

APPLIED SCIENCE BUILDING
UNIVERSITY OF UTAH
201 PRESIDENTS' CIRCLE
SALT LAKE CITY, UT 84112
FIRE ALARM SYSTEM


NFS
NELSON FIRE SYSTEMS
801-468-8300

DRAWN BY: BH
DESIGNED BY: ENVISION
APPROVED BY: KK
DATE: 08/21/2023
SCALE: N.T.S.
PROJECT NO: XXXX
REVISION NO: XXXX
DRAWING NAME:
APPLIED SCIENCE B FM.DWG

NELSON FIRE SYSTEMS
BASEMENTS 1 & 2

PAGE:
FINAL MAP



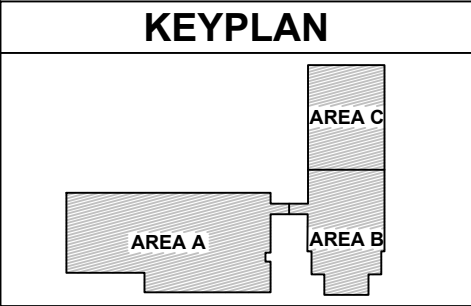

DEVICE LEGEND	
SYMBOL	DESCRIPTION
	SMOKE DETECTOR
	DUCT DETECTOR
	MONITOR MODULE
	WATER FLOW SWITCH MODULE
	TAMPER SWITCH MODULE
	CONTROL MODULE
	FIRE EXTINGUISHER
	LOCAL OPERATING CONSOLE
	FIRE ALARM CONTROL UNIT
	TRANSPONDER PANEL
	VESDA LASER PLUS



NOTE:
NFS DRAWINGS ARE BASED ON THE PROJECT
ARCHITECTURE/ENGINEER (A/E) PLANS AND
SPECIFICATIONS FURNISHED TO NFS. A/E IS SOLELY
RESPONSIBLE (NOT NFS) FOR THE TYPE, SIZE,
LOCATION, PANEL, SUBMITTALS, AND OTHER DETAILS.
THE A/E PLANS, NFS DRAWINGS ARE TO SHOW ONLY
THE WIRING DIAGRAMS BETWEEN FIRE ALARM
DEVICES AND CONTROL PANELS. NFS IS NOT
RESPONSIBLE FOR THE INFORMATION SHOWN ON THE
A/E PLANS.

APPLIED SCIENCE BUILDING
UNIVERSITY OF UTAH
201 PRESIDENTS' CIRCLE
SALT LAKE CITY, UT 84112
FIRE ALARM SYSTEM


NFS
NELSON FIRE SYSTEMS
801-468-8300

DRAWN BY: BH
DESIGNED BY: ENVISION
APPROVED BY: KK
DATE: 08/21/2023
SCALE: N.T.S.
PROJECT NO: XXXX
REVISION NO: XXXX
DRAWING NAME:
APPLIED SCIENCE 1 FM.DWG

NELSON FIRE SYSTEMS
LEVEL 1 & CRAWLSPACE

PAGE:
FINAL MAP



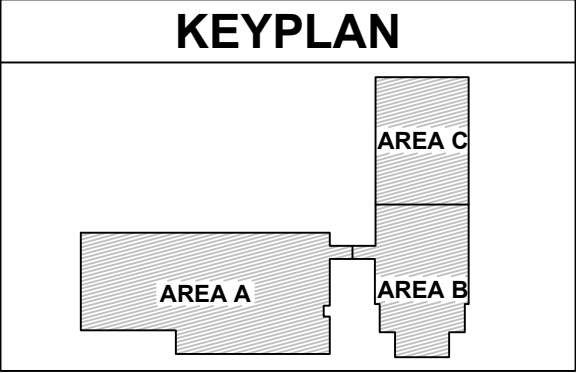

DEVICE LEGEND	
SYMBOL	DESCRIPTION
S	SMOKE DETECTOR
F	PULL STATION
DD	DUCT DETECTOR
MM	MONITOR MODULE
WF	WATER FLOW SWITCH MODULE
TS	TAMPER SWITCH MODULE
CM	CONTROL MODULE
FE	FIRE EXTINGUISHER
TRAN	TRANSPONDER PANEL
VLP	VESDA LASER PLUS



NOTE:
NFS DRAWINGS ARE BASED ON THE PROJECT ARCHITECTURE/ENGINEER (A/E) PLANS AND SPECIFICATIONS FURNISHED TO NFS. A/E IS SOLELY RESPONSIBLE (NOT NFS) FOR THE TYPE, SIZE, LOCATION, AND NUMBER OF ALL OTHER ALARMS, DEVICES, AND CONTROL PANELS SHOWN ON THE A/E PLANS. NFS DRAWINGS ARE TO SHOW ONLY THE WIRING DIAGRAMS BETWEEN FIRE ALARM DEVICES AND CONTROL PANELS. NFS IS NOT RESPONSIBLE FOR THE INFORMATION SHOWN ON THE A/E PLANS.

APPLIED SCIENCE BUILDING
UNIVERSITY OF UTAH
201 PRESIDENTS' CIRCLE
SALT LAKE CITY, UT 84112
FIRE ALARM SYSTEM

NFS
NELSON FIRE SYSTEMS
801-468-8300

DRAWN BY: BH
DESIGNED BY: ENVISION
APPROVED BY: KK
DATE: 08/21/2023
SCALE: N.T.S.
PROJECT NO: XXXX
REVISION NO: XXXX
DRAWING NAME:
APPLIED SCIENCE 2 FM.DWG


NELSON FIRE SYSTEMS
LEVEL 2

PAGE:
FINAL MAP



LEVEL 2

KEYPLAN

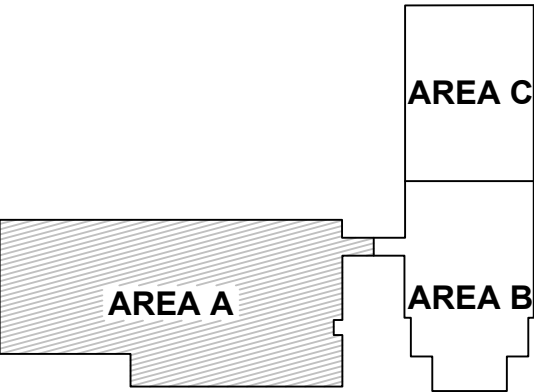

DEVICE LEGEND

SYMBOL	DESCRIPTION
S	SMOKE DETECTOR
F	PULL STATION
DD	DUCT DETECTOR
MM	MONITOR MODULE
WF	WATER FLOW SWITCH MODULE
TS	TAMPER SWITCH MODULE
CM	CONTROL MODULE
FE	FIRE EXTINGUISHER
TRAN	TRANSPONDER PANEL
VEP-1	VESDA LASER PLUS



NOTE:
NFS DRAWINGS ARE BASED ON THE PROJECT
ARCHITECTURE/ENGINEER (A/E) PLANS AND
SPECIFICATIONS FURNISHED TO NFS. A/E IS SOLELY
RESPONSIBLE (NOT NFS) FOR THE TYPE, SIZE,
LOCATION, PANEL SCHEDULE, AND OTHER DETAILS.
THE A/E PLANS, NFS DRAWINGS ARE TO SHOW ONLY
THE WIRING DIAGRAMS BETWEEN FIRE ALARM
DEVICES AND CONTROL PANELS. NFS IS NOT
RESPONSIBLE FOR THE INFORMATION SHOWN ON THE
A/E PLANS.


APPLIED SCIENCE BUILDING
UNIVERSITY OF UTAH
201 PRESIDENTS' CIRCLE
SALT LAKE CITY, UT 84112
FIRE ALARM SYSTEM

NFS
NELSON FIRE SYSTEMS
801-468-8300

DRAWN BY: BH
DESIGNED BY: ENVISION
APPROVED BY: KK
DATE: 08/21/2023
SCALE: N.T.S.
PROJECT NO: XXXX
REVISION NO: XXXX
DRAWING NAME:
APPLIED SCIENCE 3 FM.DWG


NELSON FIRE SYSTEMS
LEVEL 3

PAGE:
FINAL MAP

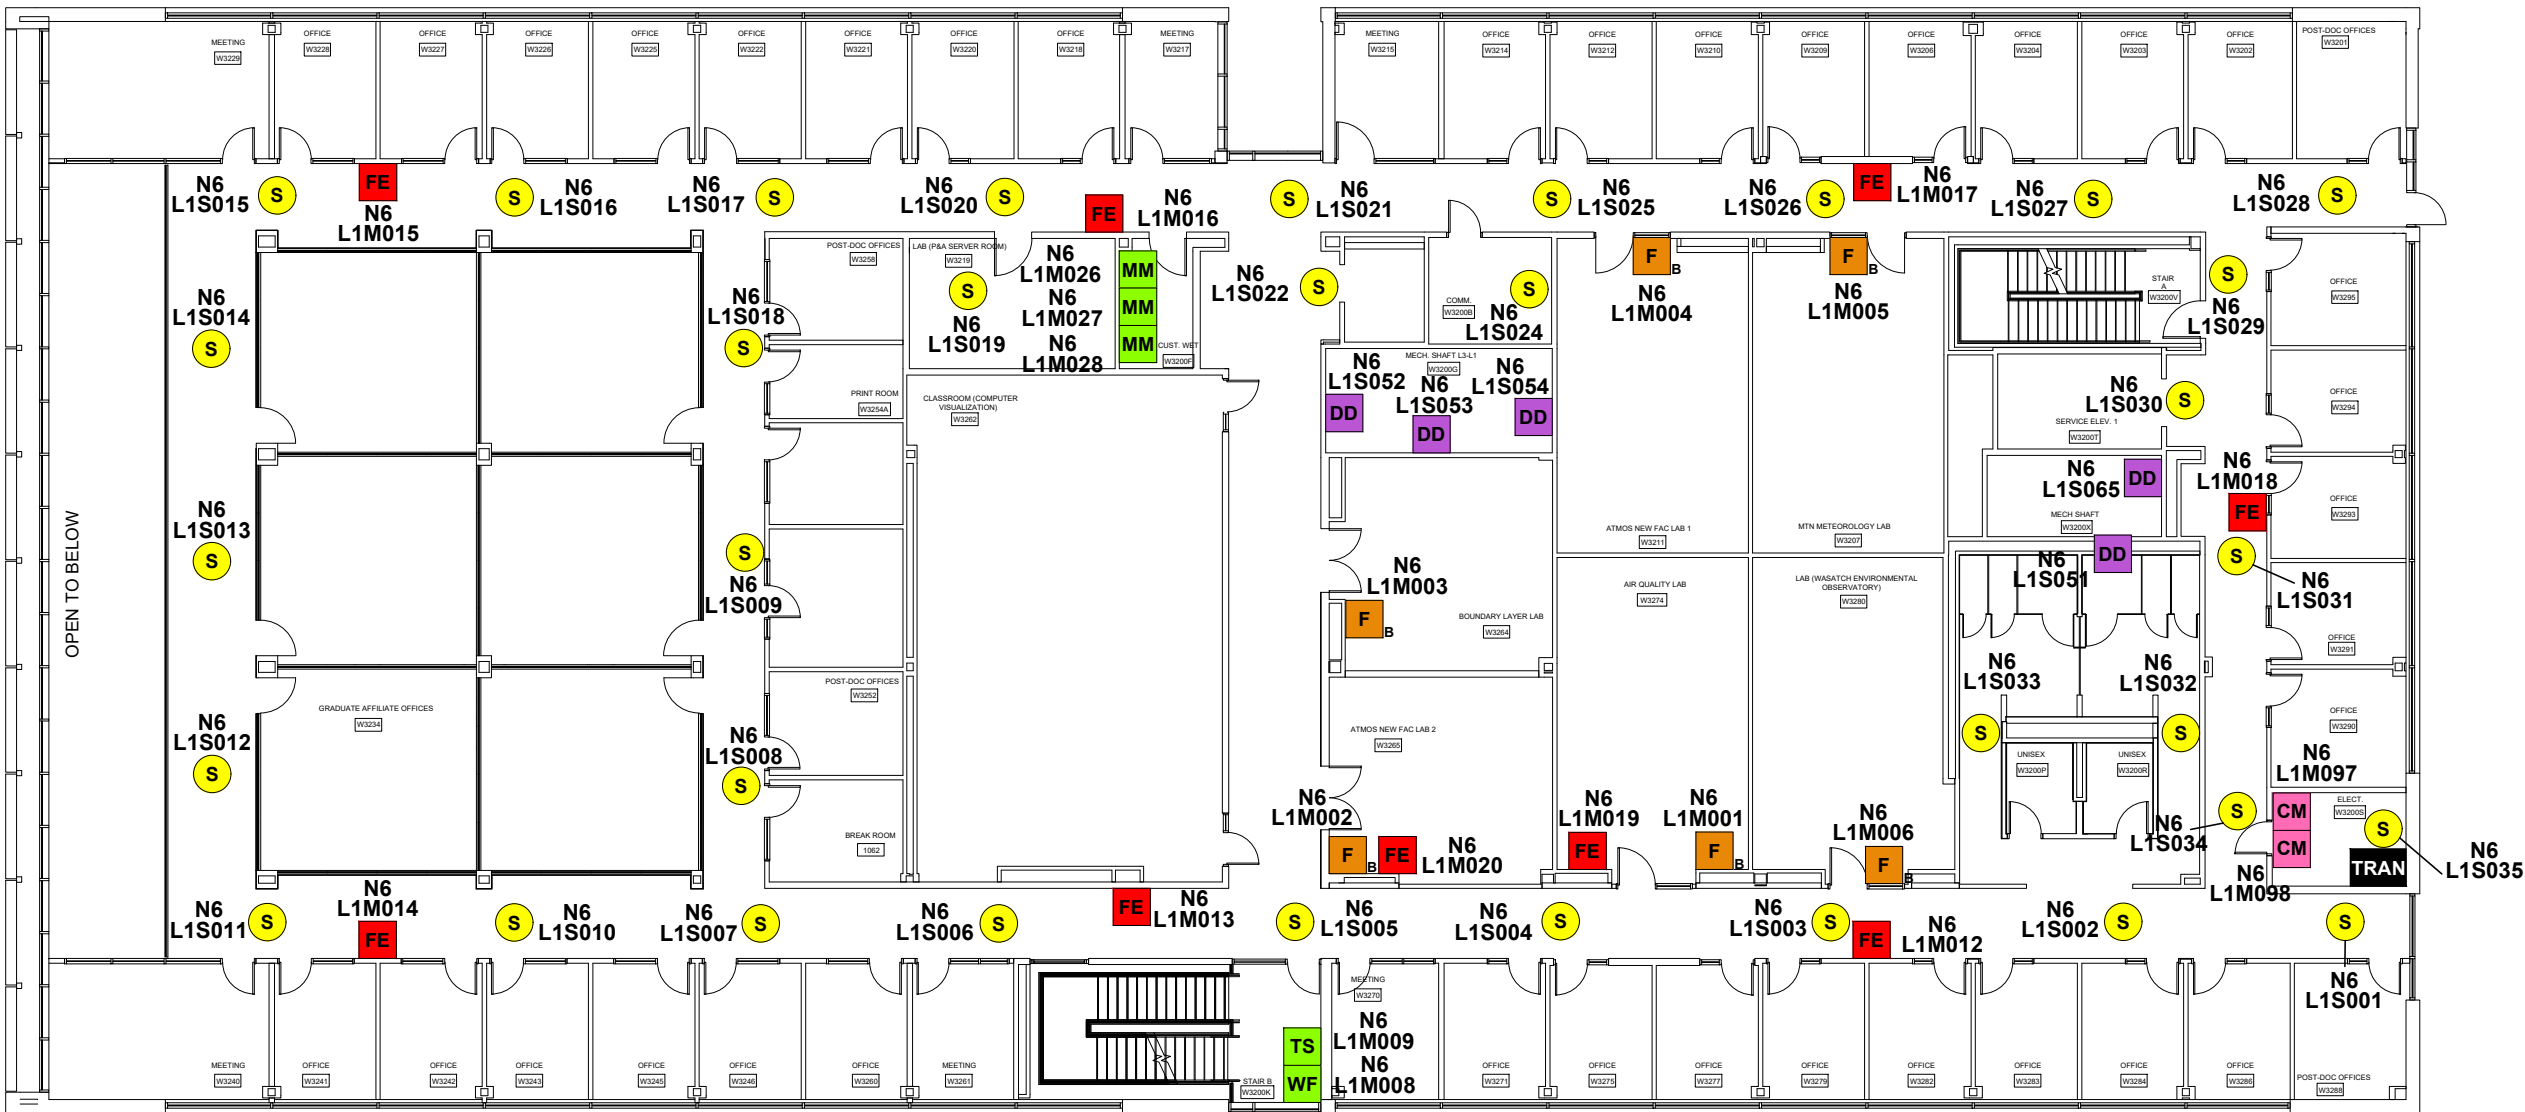

LEVEL 3

KEYPLAN

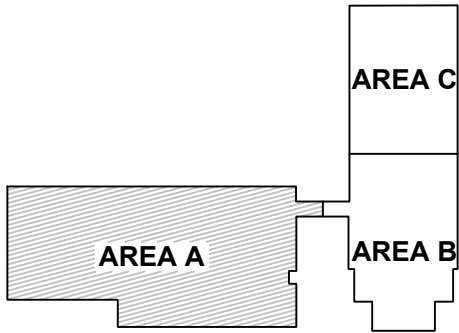

DEVICE LEGEND	
SYMBOL	DESCRIPTION
	SMOKE DETECTOR
	HEAT DETECTOR
	PULL STATION
	DUCT DETECTOR
	MONITOR MODULE
	WATER FLOW SWITCH MODULE
	TAMPER SWITCH MODULE
	CONTROL MODULE
	TRANSPONDER PANEL
	VESDA LASER PLUS



NOTE:
NFS DRAWINGS ARE BASED ON THE PROJECT ARCHITECTURE/ENGINEER (A/E) PLANS AND SPECIFICATIONS FURNISHED TO NFS. A/E IS SOLELY RESPONSIBLE (NOT NFS) FOR THE TYPE, SIZE, LOCATION, AND SUBMITTALS OF ALL ALARMS, PULL STATIONS, AND OTHER DEVICES SHOWN ON THE A/E PLANS. NFS DRAWINGS ARE TO SHOW ONLY THE WIRING DIAGRAMS BETWEEN FIRE ALARM DEVICES AND CONTROL PANELS. NFS IS NOT RESPONSIBLE FOR THE INFORMATION SHOWN ON THE A/E PLANS.

APPLIED SCIENCE BUILDING
UNIVERSITY OF UTAH
201 PRESIDENTS' CIRCLE
SALT LAKE CITY, UT 84112
FIRE ALARM SYSTEM


NFS
NELSON FIRE SYSTEMS
801-468-8300

DRAWN BY:	BH
DESIGNED BY:	ENVISION
APPROVED BY:	KK
DATE:	08/22/2023
SCALE:	N.T.S.
PROJECT NO:	XXXX
REVISION NO:	XXXX
DRAWING NAME:	APPLIED SCIENCE 4 FM.DWG

NELSON FIRE SYSTEMS
LEVEL 4

PAGE:
FINAL MAP

- N6 L2M080  RECALL TO MAIN
- N6 L2M081  RECALL TO ALT
- N6 L2M082  HAT FLASH

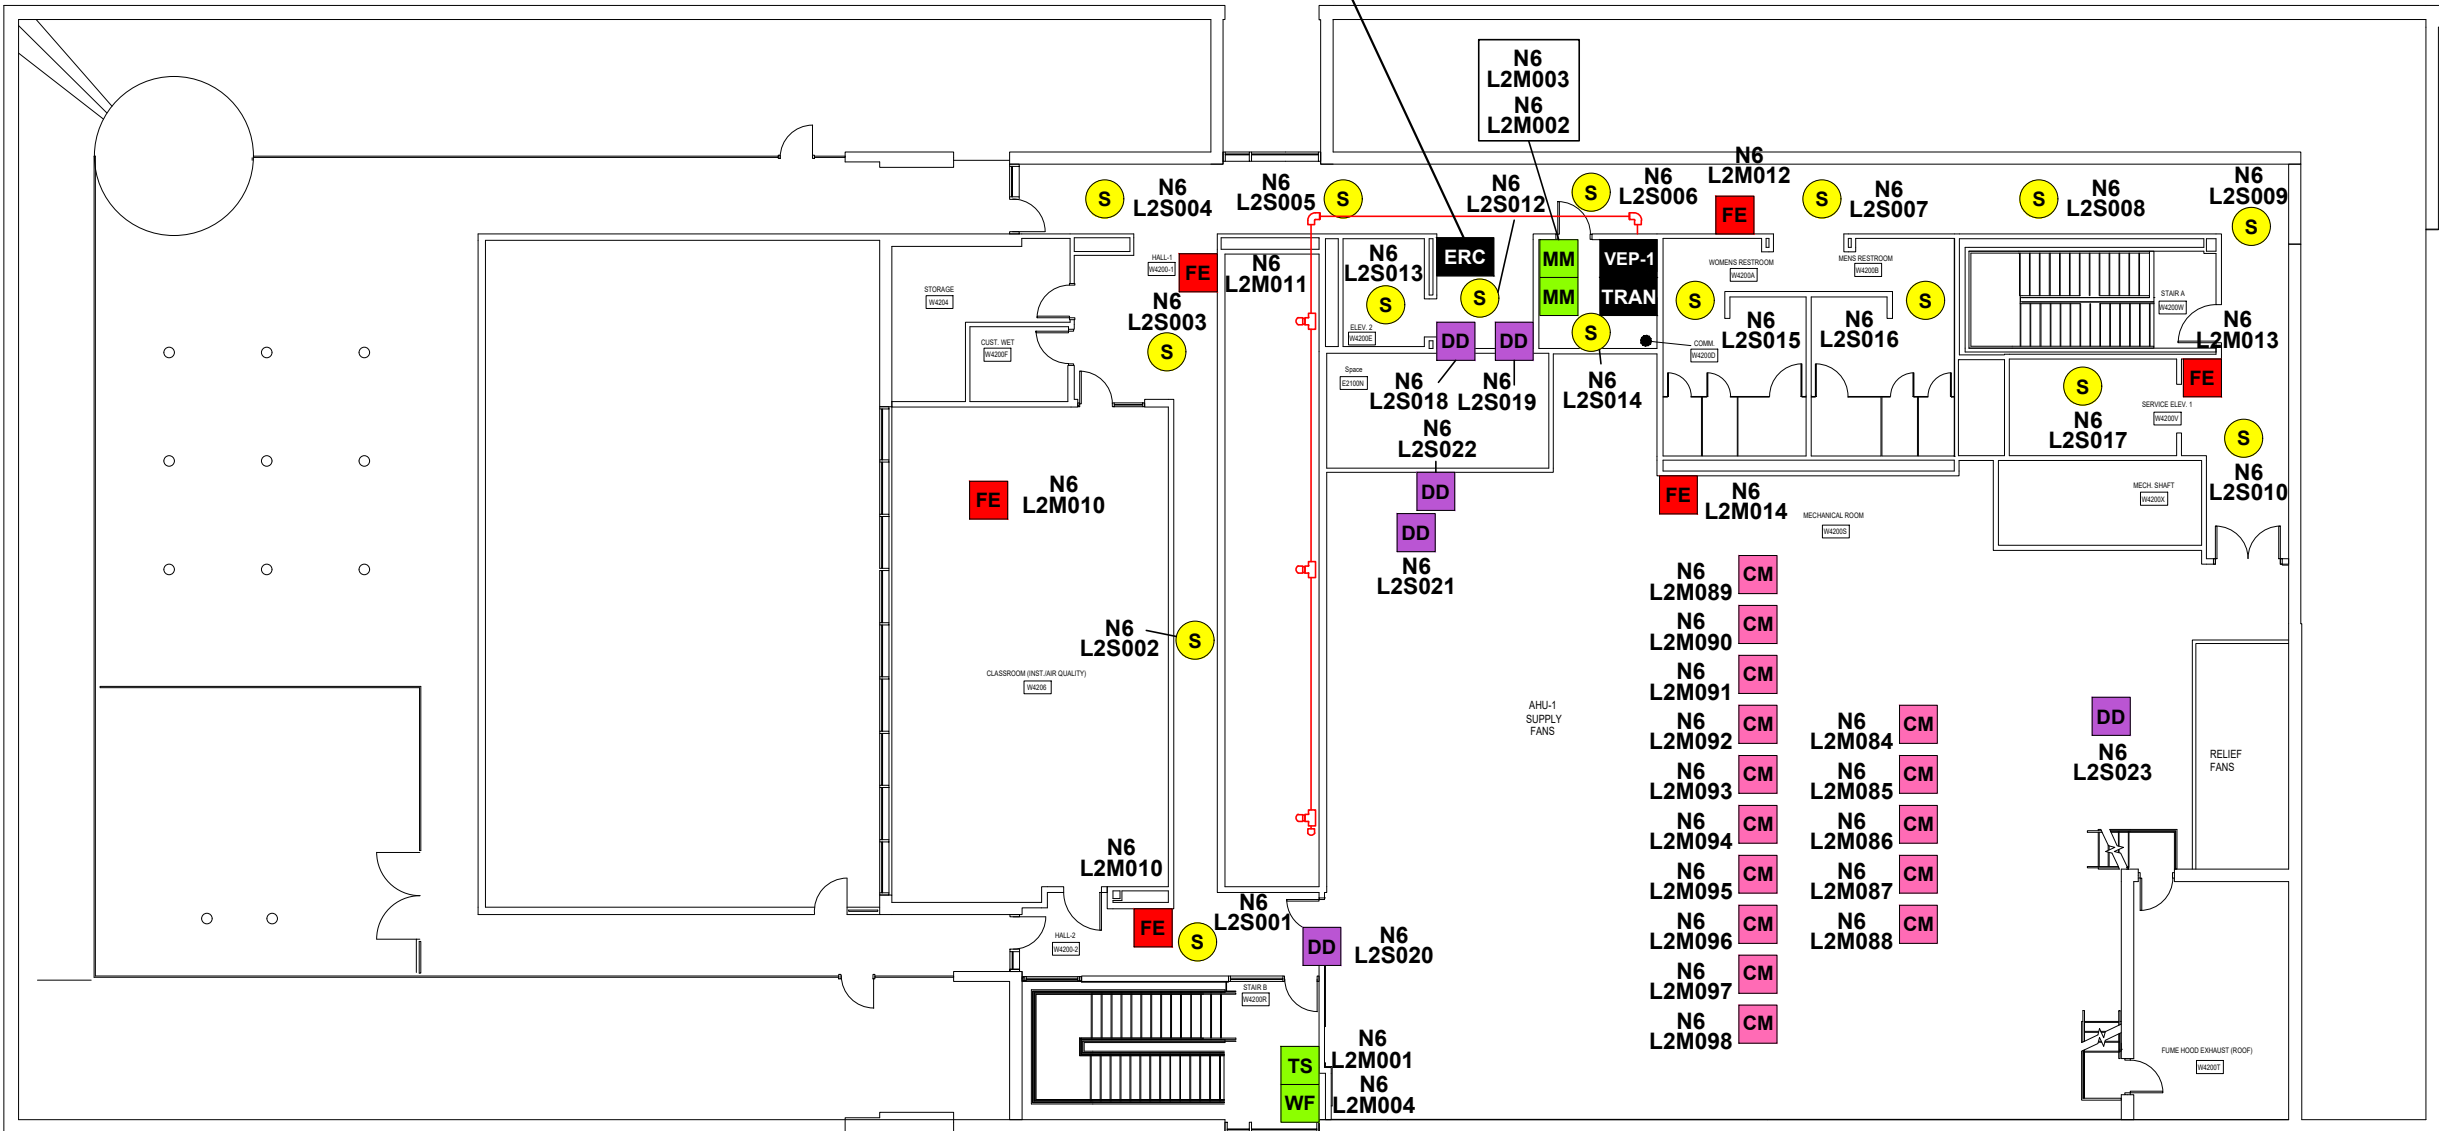

LEVEL 4

