


LEGEND


- SMOKE DETECTOR
- HEAT DETECTOR
- MANUAL PULL STATION
- DUCT DETECTOR
- WATER FLOW SWITCH
- TAMPER SWITCH
- HORN/STROBE
- DOORFOLDER
- MINI HORN

NFS
NELSON FIRE SYSTEMS
801-288-8905


LIFE SCIENCE
BUILDING REMODEL
UNIVERSITY OF UTAH
SALT LAKE CITY, UTAH
MARCH 31, 1993

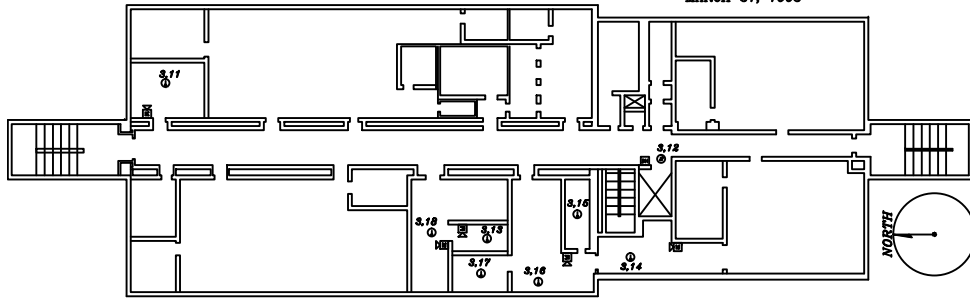


THIRD FLOOR

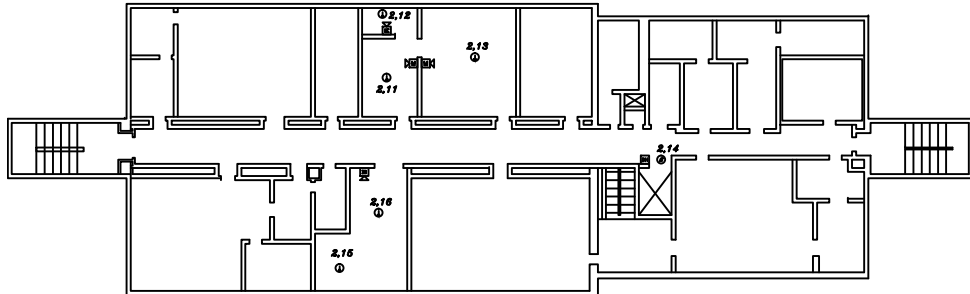


SECOND FLOOR

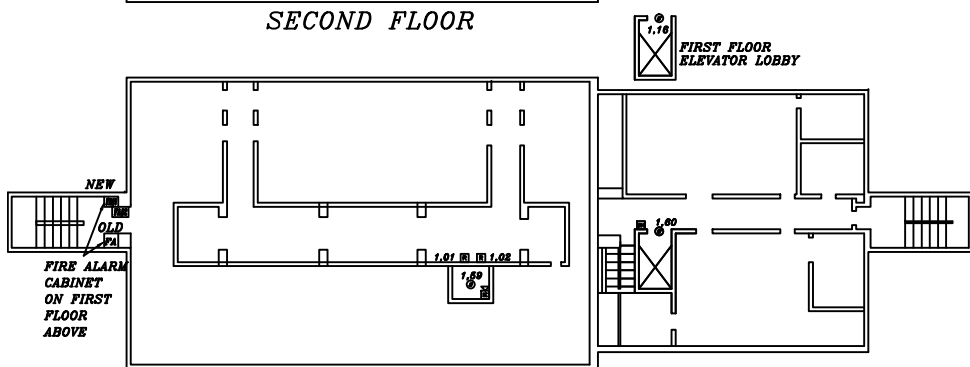


BASEMENT

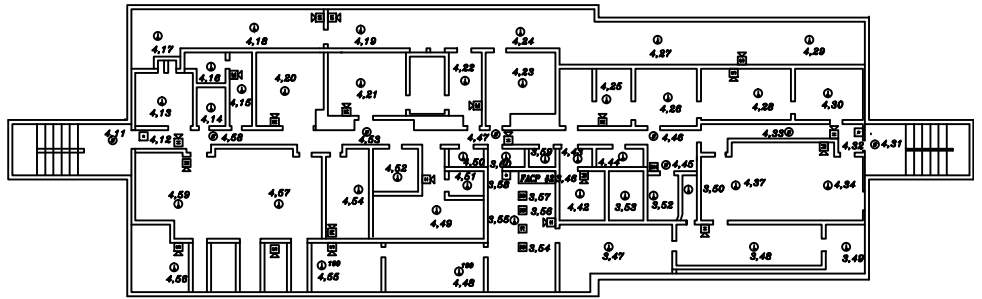

FOURTH FLOOR

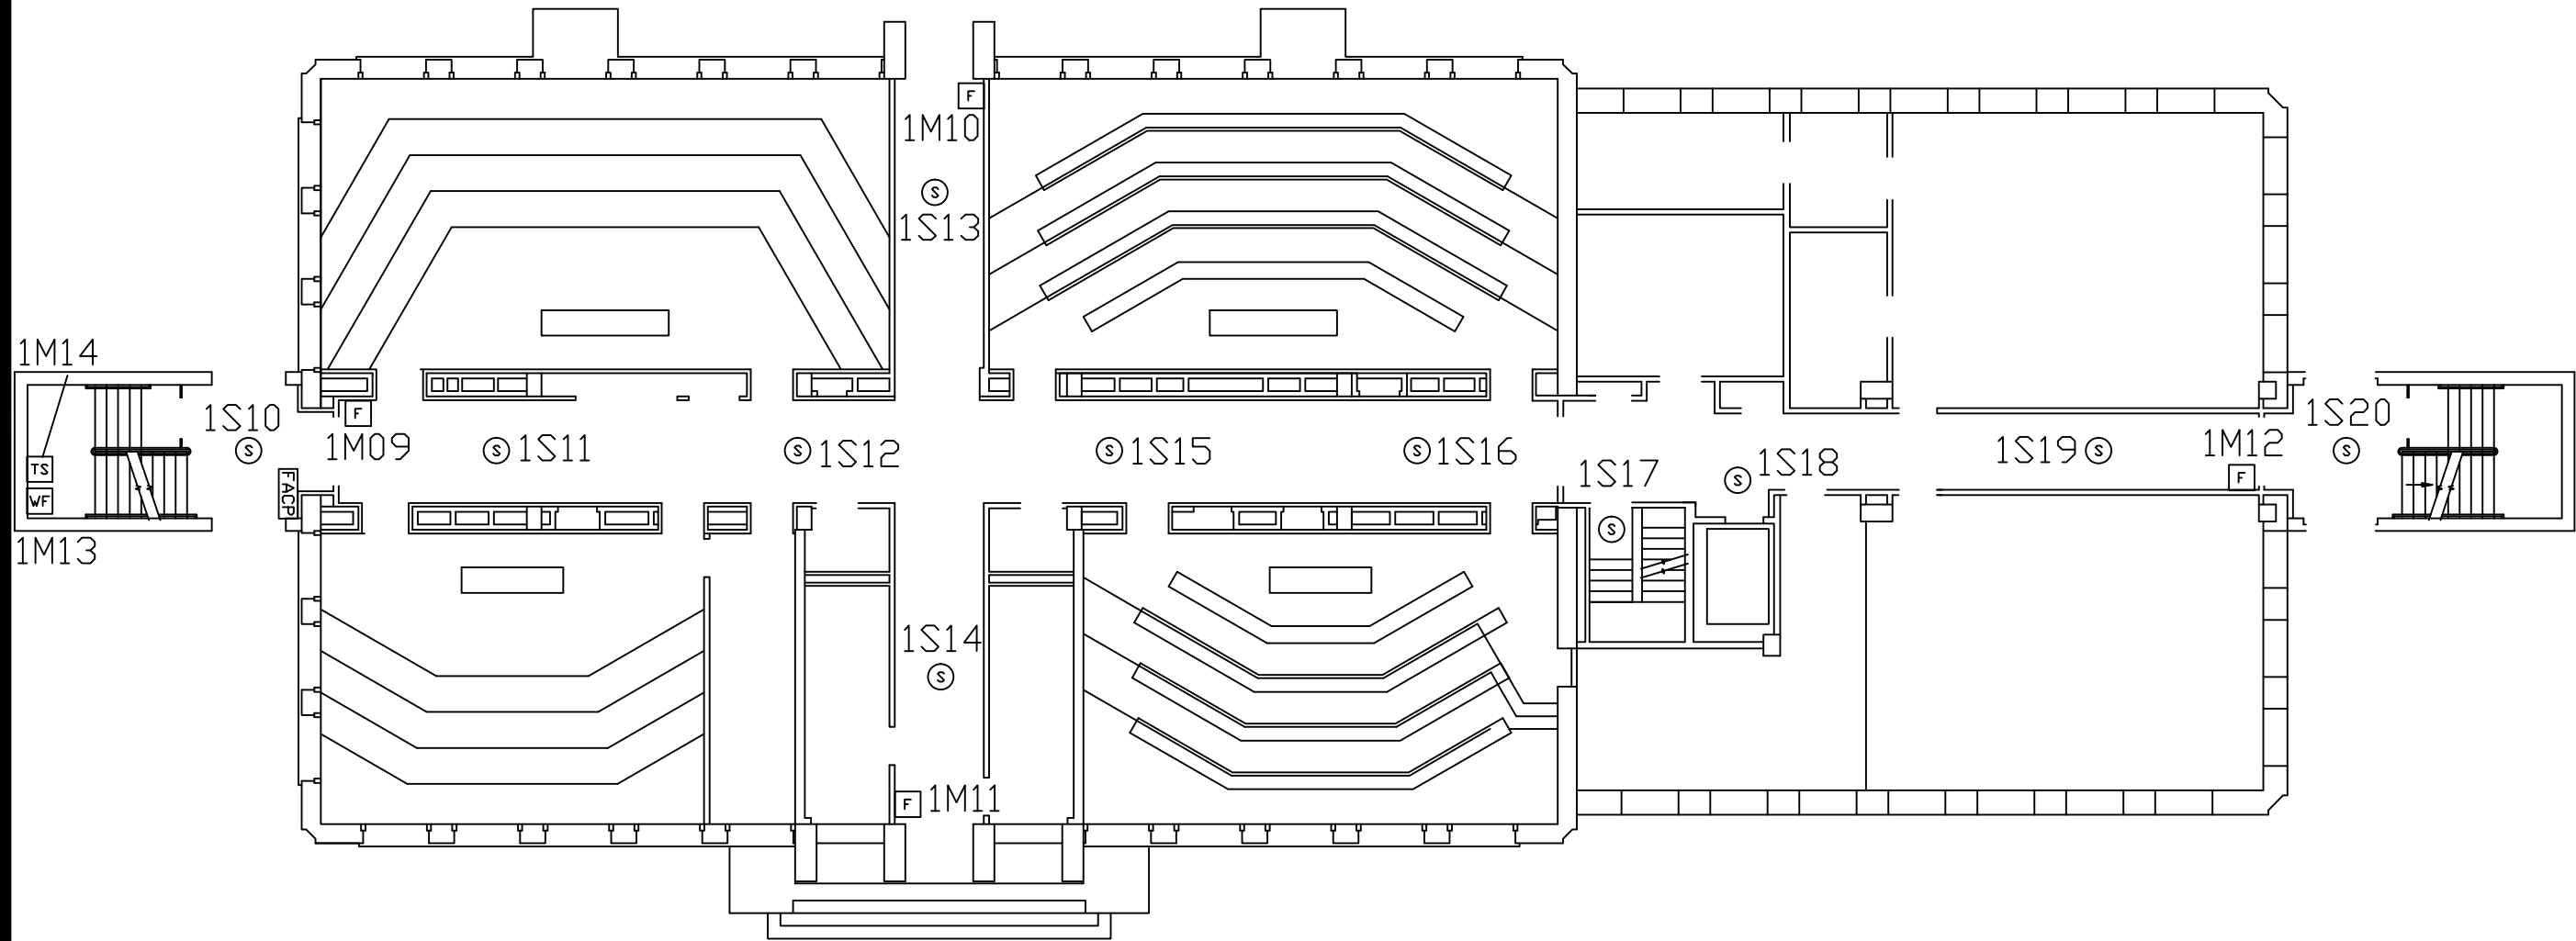

DEVICE LEGEND	
SYMBOL	DESCRIPTION
Ⓢ	SMOKE DETECTOR W/BASE
Ⓣ	THERMAL DETECTOR
F	MANUAL PULL STATION
DD	DUCT SMOKE DETECTOR
WF	WATERFLOW SWITCH MONITOR MODULE
TS	TAMPER SWITCH MONITOR MODULE
FACP	FIRE ALARM CONTROL PANEL
TRAN	TRANSPONDER PANEL
B	WATERFLOW BELL

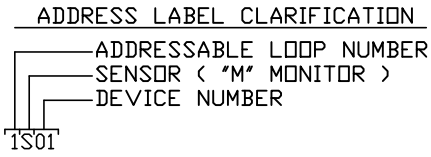

NOTE:
NFS DRAWINGS ARE BASED ON THE PROJECT
ARCHITECT/ENGINEER (A/E) PLANS AND SPECIFICATIONS
FURNISHED TO NFS. A/E IS SOLELY RESPONSIBLE
(NOT NFS) FOR THE TYPE, SIZE, LOCATION, AND
SUITABILITY OF ALL FIRE ALARMS, CONTROL PANELS,
AND OTHER DEVICES SHOWN ON THE A/E PLANS.
NFS DRAWINGS ARE TO SHOW ONLY THE WIRING
DIAGRAMS BETWEEN FIRE ALARM DEVICES AND
CONTROL PANELS. NFS IS NOT RESPONSIBLE FOR
THE INFORMATION SHOWN ON THE A/E PLANS.

LIFE SCIENCES BUILDING
UNIVERSITY OF UTAH
FIRST FLOOR



NFS

NELSON FIRE SYSTEMS
801-468-8300

DRAWN BY:	DS
DESIGNED BY:	JGA
APPROVED BY:	XXXX
DATE:	05/10/04
SCALE:	N.T.S.
PROJECT NO:	XXXX
REV NO:	XXXX
DRAWING NAME:	LSCIENCE1.DWG


FIRE ALARM SYSTEM
FIRST FLOOR
ADDRESSABLE LOOP NUMBERS

NFS
FA-I-04

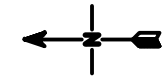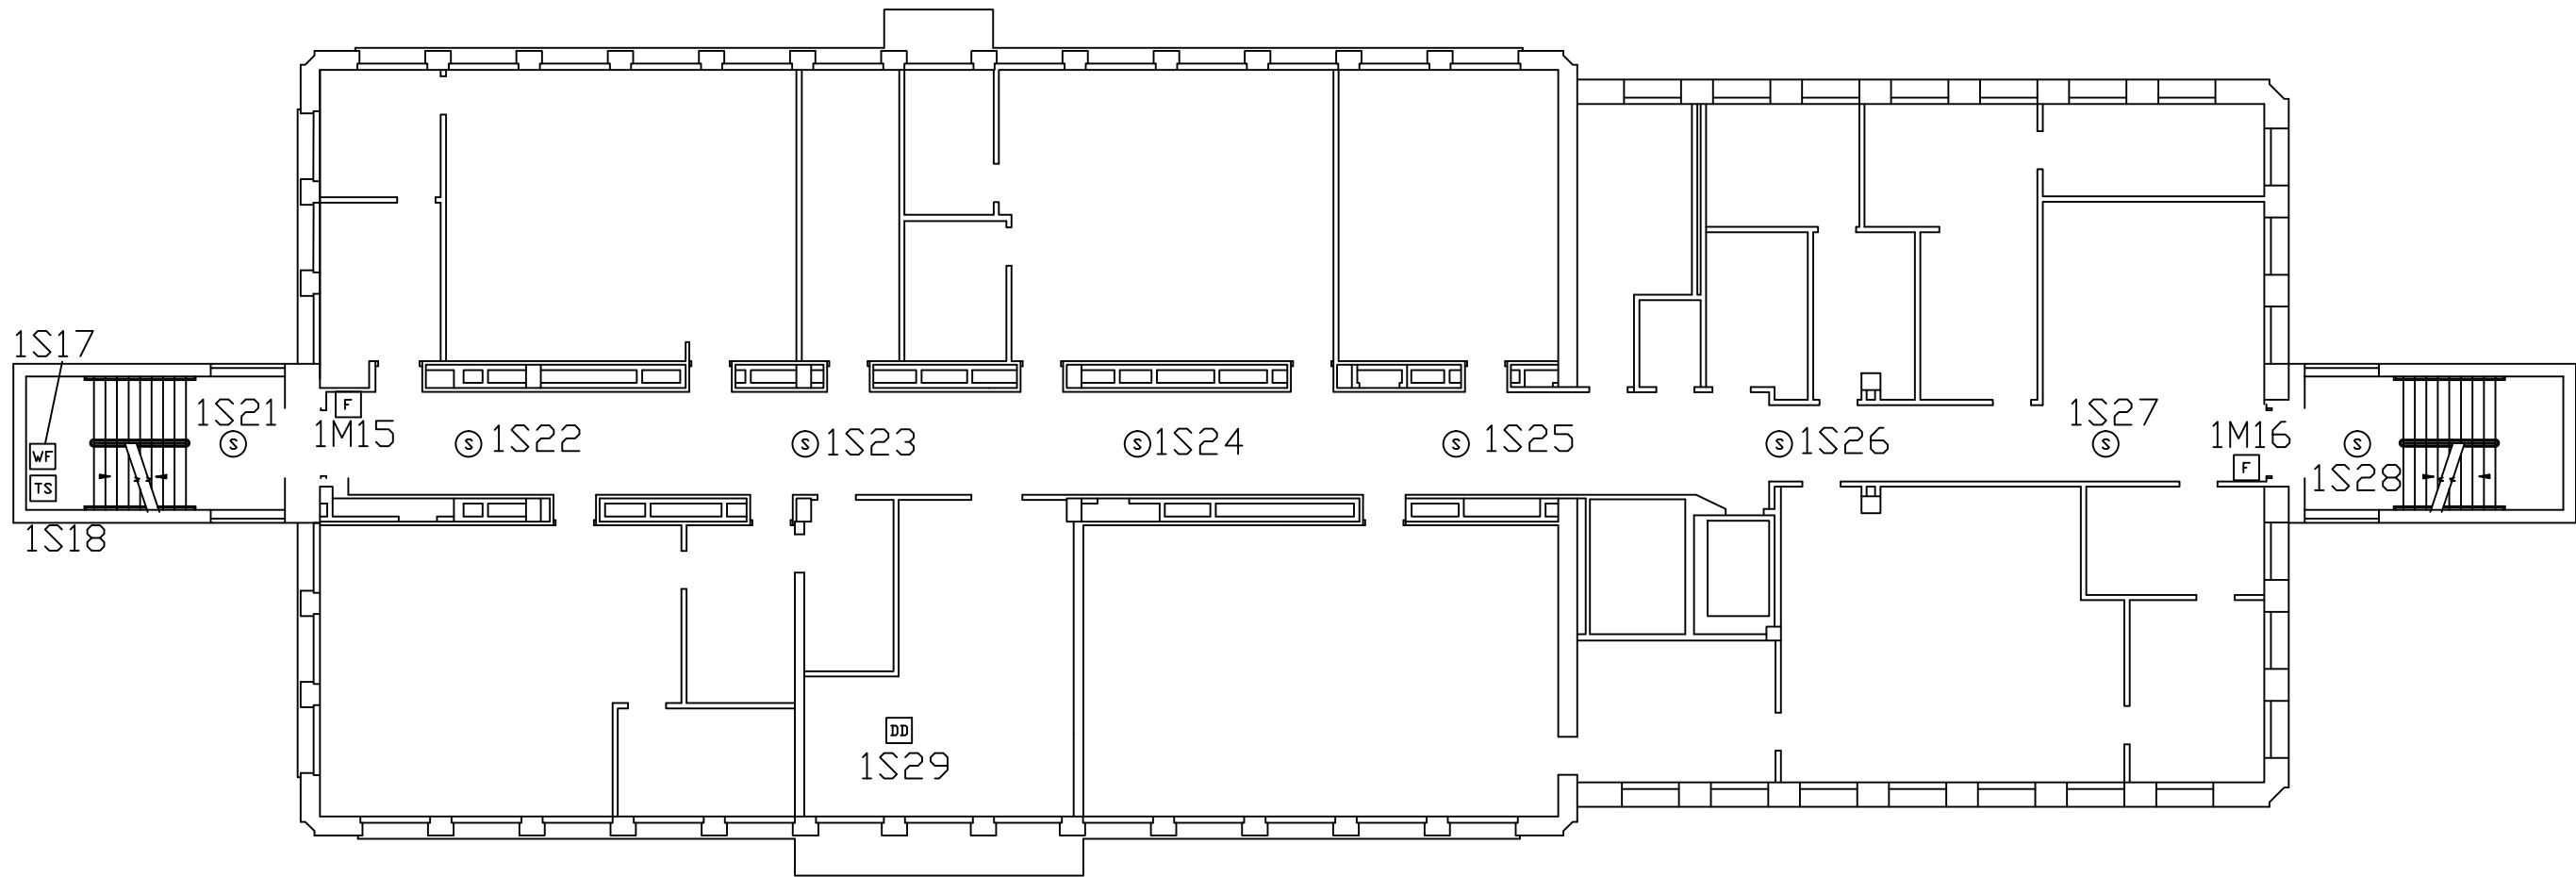

NOTE:
NFS DRAWINGS ARE BASED ON THE PROJECT
ARCHITECT/ENGINEER (A/E) PLANS AND SPECIFICATIONS
FURNISHED TO NFS. A/E IS SOLELY RESPONSIBLE
(NOT NFS) FOR THE TYPE, SIZE, LOCATION, AND
SUITABILITY OF ALL FIRE ALARMS, CONTROL PANELS,
AND OTHER DEVICES SHOWN ON THE A/E PLANS.
NFS DRAWINGS ARE TO SHOW ONLY THE WIRING
DIAGRAMS BETWEEN FIRE ALARM DEVICES AND
CONTROL PANELS. NFS IS NOT RESPONSIBLE FOR
THE INFORMATION SHOWN ON THE A/E PLANS.

LIFE SCIENCES BUILDING
UNIVERSITY OF UTAH
SECOND FLOOR

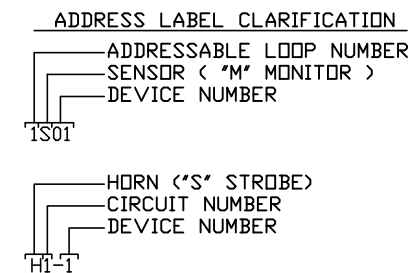

DEVICE LEGEND	
SYMBOL	DESCRIPTION
Ⓢ	SMOKE DETECTOR W/BASE
F	MANUAL PULL STATION
DB	DUCT SMOKE DETECTOR
WF	WATERFLOW SWITCH MONITOR MODULE
TS	TAMPER SWITCH MONITOR MODULE
HS	HORN/STROBE
H	WEATHERPROOF HORN
L	STROBE LIGHT
R	RELAY- ARB-C
DR	DOORHOLDER

WIRE SCHEDULE		
SYMBOL	DESCRIPTION	SIZE
A	ADDRESSABLE LOOP SECOND FLOOR	1 PAIR #14 TWISTED
B	HORN CKT 1 & STROBE CKTS 1,2,3	8 #14'S
C	RELAY CIRCUIT SECOND FLOOR	2 #14'S
D	120 VAC POWER	3 #12'S
E		
F		



- SYSTEM NOTES:
- ① TO THIRD FLOOR TRAN
 - ② TO MAIN FACP
 - ③ TO 120VAC WITH GROUND
 - ④ TO FAN SHUTDOWN
 - ⑤ EXISTING TO REMAIN

NFS
NELSON FIRE SYSTEMS
801-468-8300

DRAWN BY: DS
DESIGNED BY: JGA
APPROVED BY: XXXX
DATE: 12/2/03
SCALE: N.T.S.
PROJECT NO: XXXX
REV NO: XXXX
DRAWING NAME: LSCIENCE2.DWG

FIRE ALARM SYSTEM
SECOND FLOOR
ADDRESSABLE LOOP NUMBERS


NFS
FA-2-04

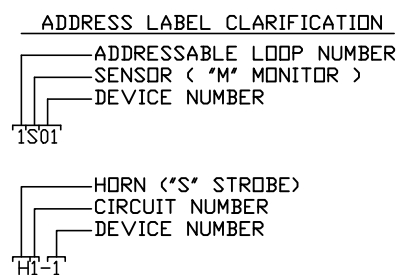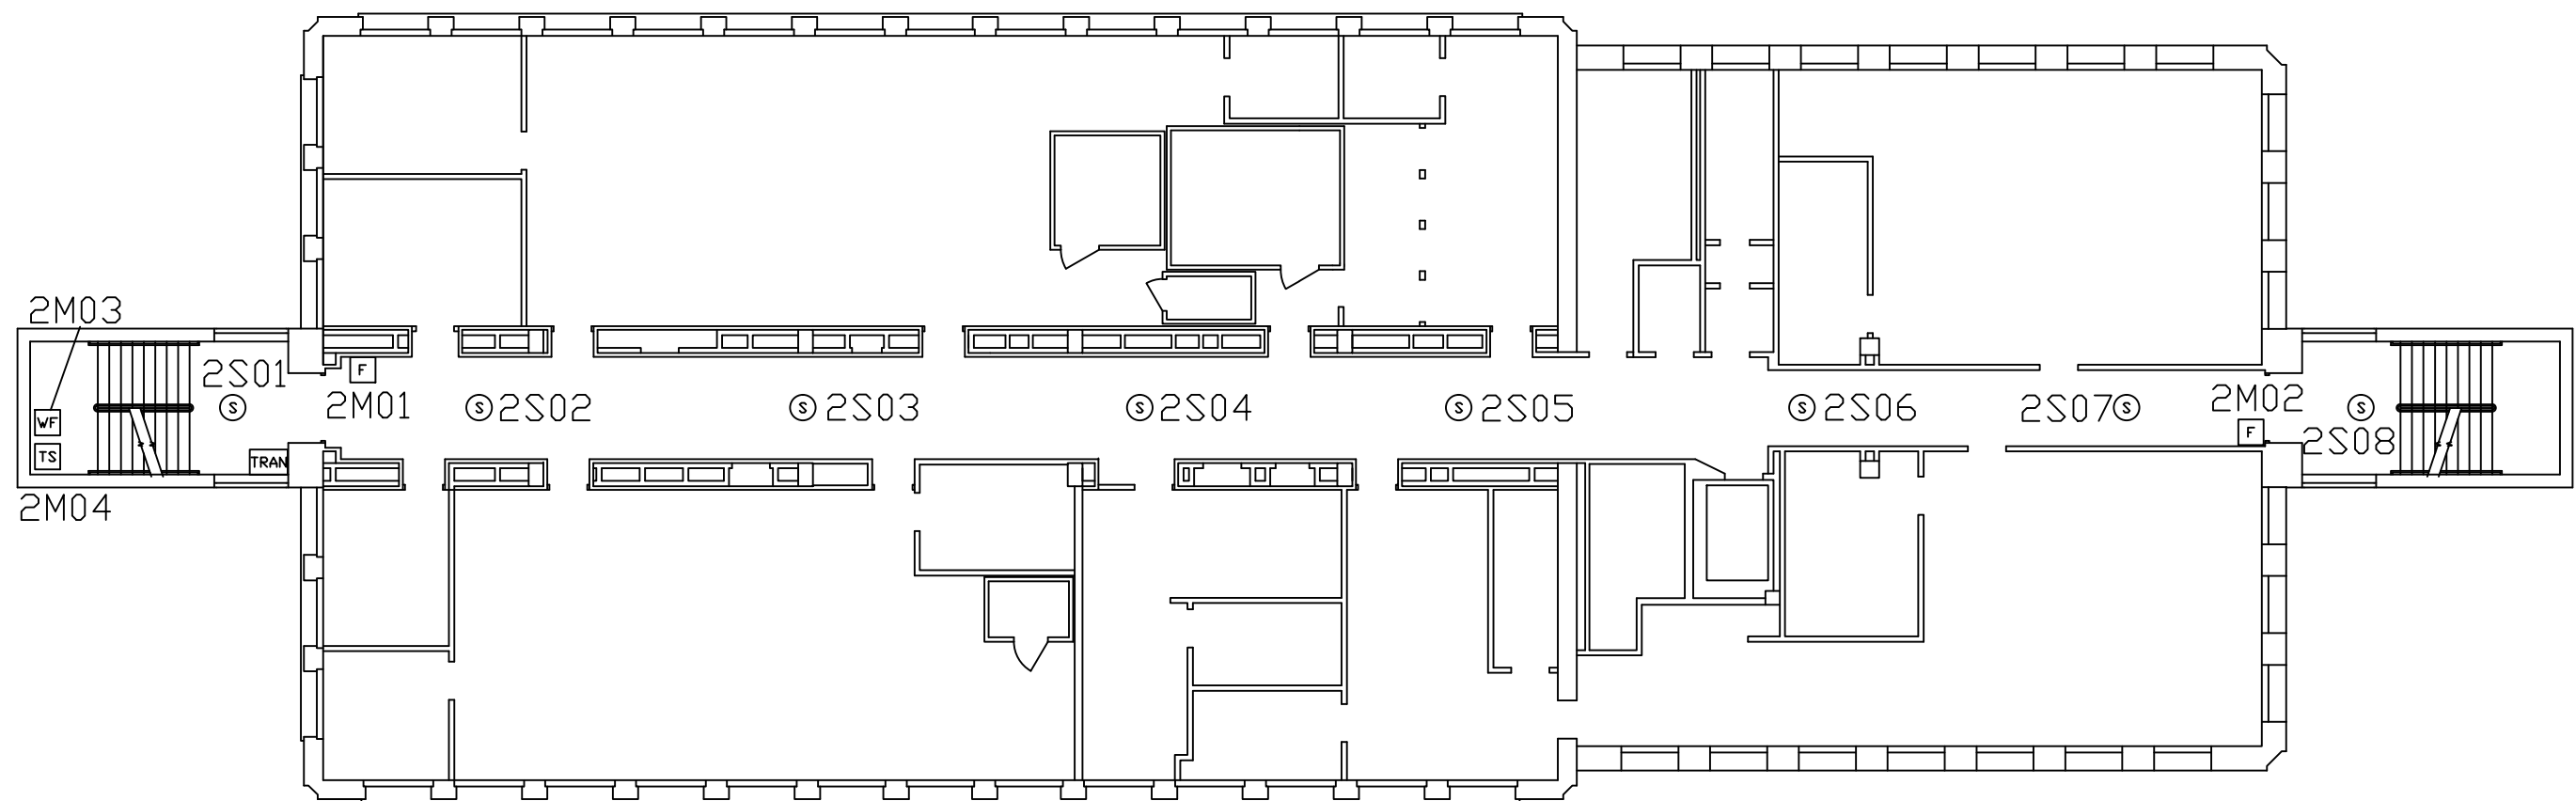

DEVICE LEGEND	
SYMBOL	DESCRIPTION
Ⓢ	SMOKE DETECTOR W/BASE
F	MANUAL PULL STATION
WF	WATERFLOW SWITCH MONITOR MODULE
TS	TAMPER SWITCH MONITOR MODULE
HS	HORN/STROBE
H	WEATHERPROOF HORN
L	STROBE LIGHT
DH	DOORHOLDER
TRAN	TRANSPONDER PANEL

WIRE SCHEDULE		
SYMBOL	DESCRIPTION	SIZE
A	ADDRESSABLE LOOP THIRD FLOOR	1 PAIR #14'S TWISTED
B	HORN CKT 1 & STROBE CKTS 1,2,3	8 #14'S
C	INTERCONNECT WIRING	2 PAIR #14'S TWISTED & 10 #14'S
D	120 VAC POWER	3 #12'S
E		
F		

- SYSTEM NOTES:
- ① TO THIRD FLOOR TRAN
 - ② TO MAIN FACP
 - ③ TO 120VAC WITH GROUND
 - ④ TO FOURTH FLOOR TRAN
 - ⑤ EXISTING TO REMAIN

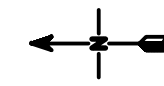

NOTE:
NFS DRAWINGS ARE BASED ON THE PROJECT
ARCHITECT/ENGINEER (A/E) PLANS AND SPECIFICATIONS
FURNISHED TO NFS. A/E IS SOLELY RESPONSIBLE
(NOT NFS) FOR THE TYPE, SIZE, LOCATION, AND
SUITABILITY OF ALL FIRE ALARMS, CONTROL PANELS,
AND OTHER DEVICES SHOWN ON THE A/E PLANS.
NFS DRAWINGS ARE TO SHOW ONLY THE WIRING
DIAGRAMS BETWEEN FIRE ALARM DEVICES AND
CONTROL PANELS. NFS IS NOT RESPONSIBLE FOR
THE INFORMATION SHOWN ON THE A/E PLANS.



LIFE SCIENCES BUILDING
UNIVERSITY OF UTAH
THIRD FLOOR

NFS
NELSON FIRE SYSTEMS
801-468-8300

DRAWN BY:	DS
DESIGNED BY:	JGA
APPROVED BY:	XXXX
DATE:	12/2/03
SCALE:	N.T.S.
PROJECT NO:	XXXX
REV NO:	XXXX
DRAWING NAME:	LSCIENCE3.DWG


FIRE ALARM SYSTEM
THIRD FLOOR
ADDRESSABLE LOOP NUMBERS

NFS
FA-3-04

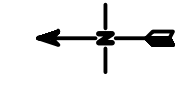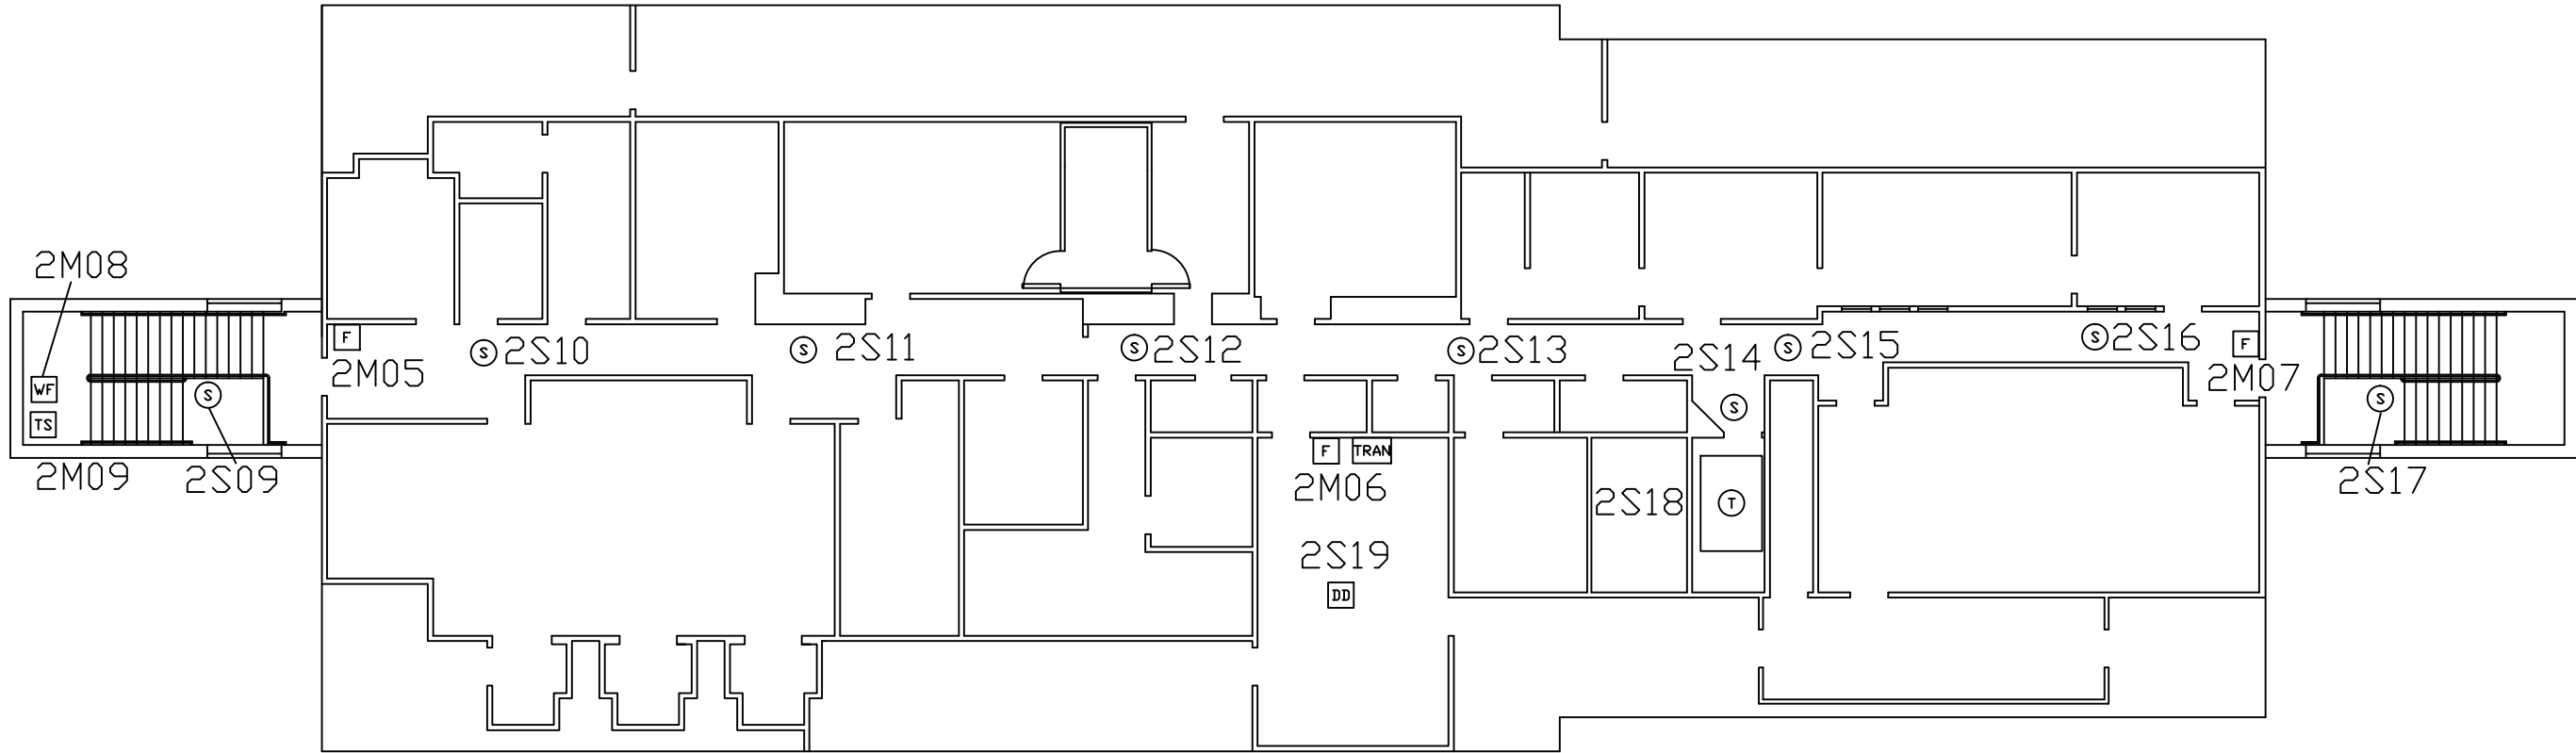

NOTE:
NFS DRAWINGS ARE BASED ON THE PROJECT
ARCHITECT/ENGINEER (A/E) PLANS AND SPECIFICATIONS
FURNISHED TO NFS. A/E IS SOLELY RESPONSIBLE
(NOT NFS) FOR THE TYPE, SIZE, LOCATION, AND
SUITABILITY OF ALL FIRE ALARMS, CONTROL PANELS,
AND OTHER DEVICES SHOWN ON THE A/E PLANS.
NFS DRAWINGS ARE TO SHOW ONLY THE WIRING
DIAGRAMS BETWEEN FIRE ALARM DEVICES AND
CONTROL PANELS. NFS IS NOT RESPONSIBLE FOR
THE INFORMATION SHOWN ON THE A/E PLANS.

LIFE SCIENCES BUILDING
UNIVERSITY OF UTAH
FOURTH FLOOR

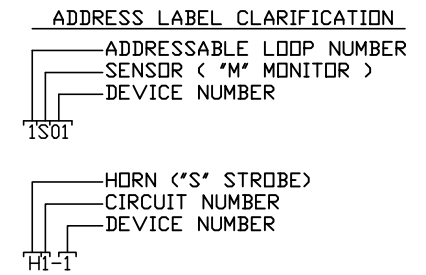

DEVICE LEGEND	
SYMBOL	DESCRIPTION
Ⓢ	SMOKE DETECTOR W/BASE
Ⓣ	THERMAL DETECTOR
ⓕ	MANUAL PULL STATION
ⓓⓓ	DUCT SMOKE DETECTOR
Ⓦⓕ	WATERFLOW SWITCH MONITOR MODULE
ⓉⓈ	TAMPER SWITCH MONITOR MODULE
ⓗⓈ	HORN/STROBE
ⓗ	WEATHERPROOF HORN
ⓛ	STROBE LIGHT
Ⓡ	RELAY- ARB-C
ⓓⓗ	DOORHOLDER
ⓉⓇⓐⓃ	TRANSPONDER PANEL

WIRE SCHEDULE		
SYMBOL	DESCRIPTION	SIZE
A	ADDRESSABLE LOOP FOURTH FLOOR	1 PAIR #14'S TWISTED
B	HORN CKT 1 & STROBE CKTS 1,2	6 #14'S
C	RELAY CIRCUIT FOURTH FLOOR	2 #14'S
D	INTERCONNECT WIRING	2 PAIR #14'S TWISTED & 10 #14'S
E	120 VAC POWER	3 #12'S
F		
G		

- SYSTEM NOTES:
- ① TO FOURTH FLOOR TRAN
 - ② TO MAIN FACP
 - ③ TO 120VAC WITH GROUND
 - ④ TO FAN SHUTDOWN
 - ⑤ TO THIRD FLOOR TRAN
 - ⑥ EXISTING TO REMAIN

NFS
NELSON FIRE SYSTEMS
801-468-8300

DRAWN BY:	DS
DESIGNED BY:	JGA
APPROVED BY:	XXXX
DATE:	12/2/03
SCALE:	N.T.S.
PROJECT NO:	XXXX
REV NO:	XXXX
DRAWING NAME:	LSCIENCE4.DWG

FIRE ALARM SYSTEM
FOURTH FLOOR
ADDRESSABLE LOOP NUMBERS

NFS
FA-4-04

