

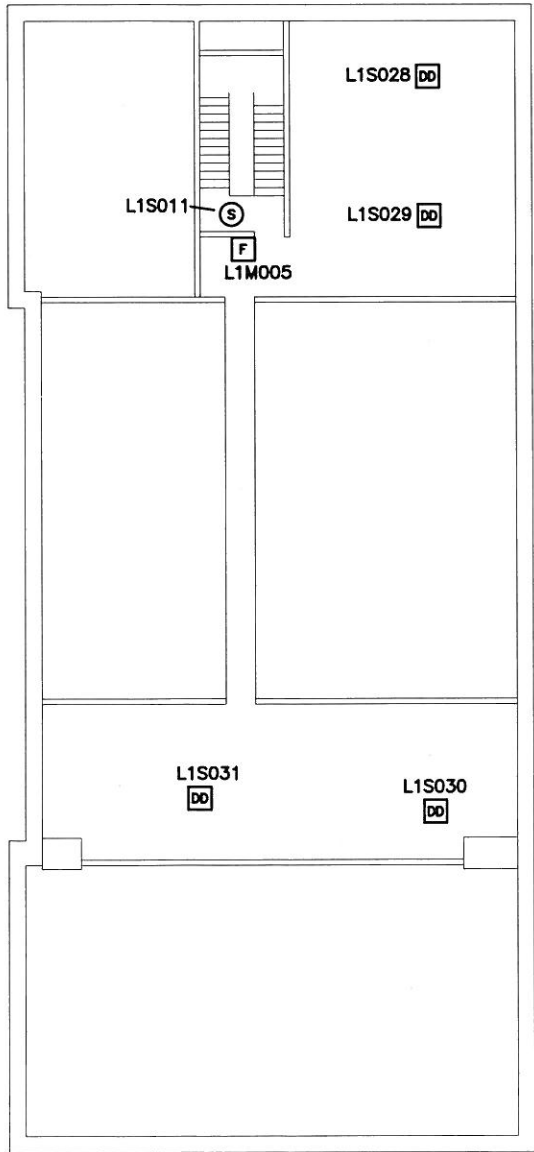


DEVICE LEGEND	
SYMBOL	DESCRIPTION
(S)	SMOKE DETECTOR
(T)	THERMAL DETECTOR
(F)	MANUAL PULL STATION
(DD)	DUCT SMOKE DETECTOR
(WF)	WATERFLOW SWITCH MONITOR MODULE
(TS)	TAMPER SWITCH MONITOR MODULE
(MM)	MONITOR MODULE
(CM)	CONTROL MODULE
(RA)	REMOTE ANNUNCIATOR
(FACP)	FIRE ALARM CONTROL PANEL
(TRAN)	TRANSPONDER PANEL


- THE FOLLOWING DEVICES ARE LOCATED IN THE FIRE ALARM PANEL:
- L1M098 - ELEVATOR RECALL TO ALTERNATE
 - L1M097 - ELEVATOR RECALL TO MAIN
 - L1M095 - BYPASS BUTTON SUPERVISION
 - L1M022 - BYPASS BUTTON SUPERVISION
 - L1M021 - TRANSPONDER SUPERVISION

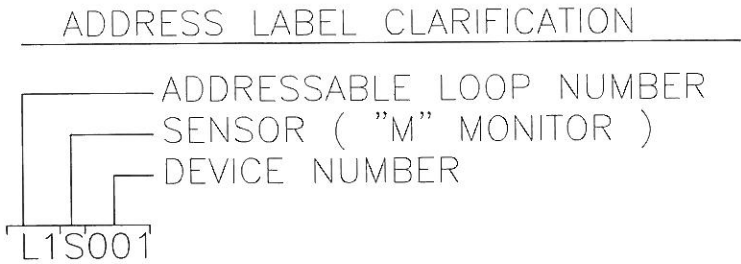


MEZZANINE MECHANICAL ROOM

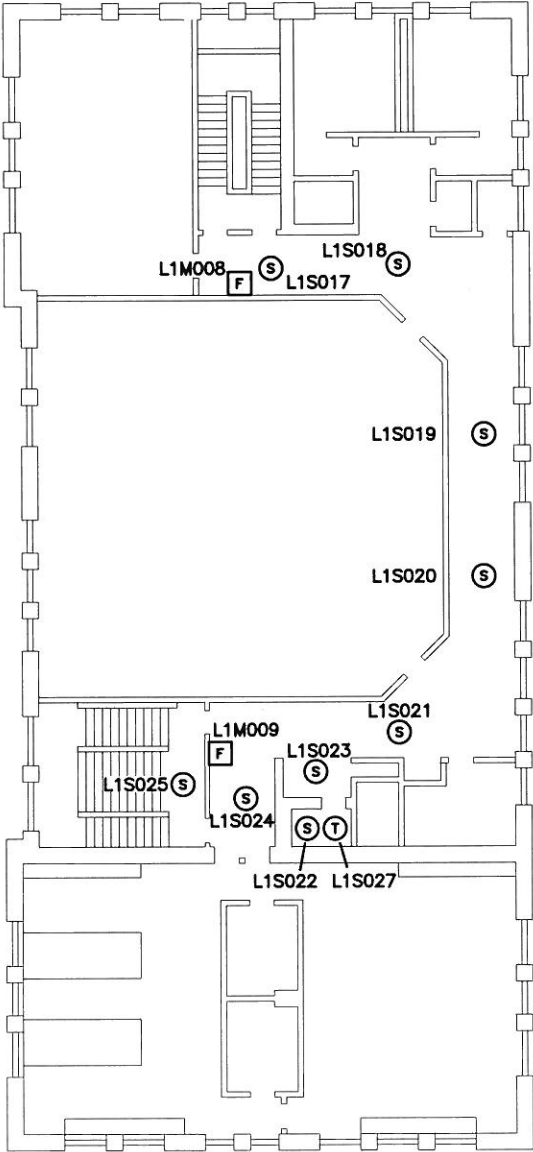


THIRD FLOOR PLAN

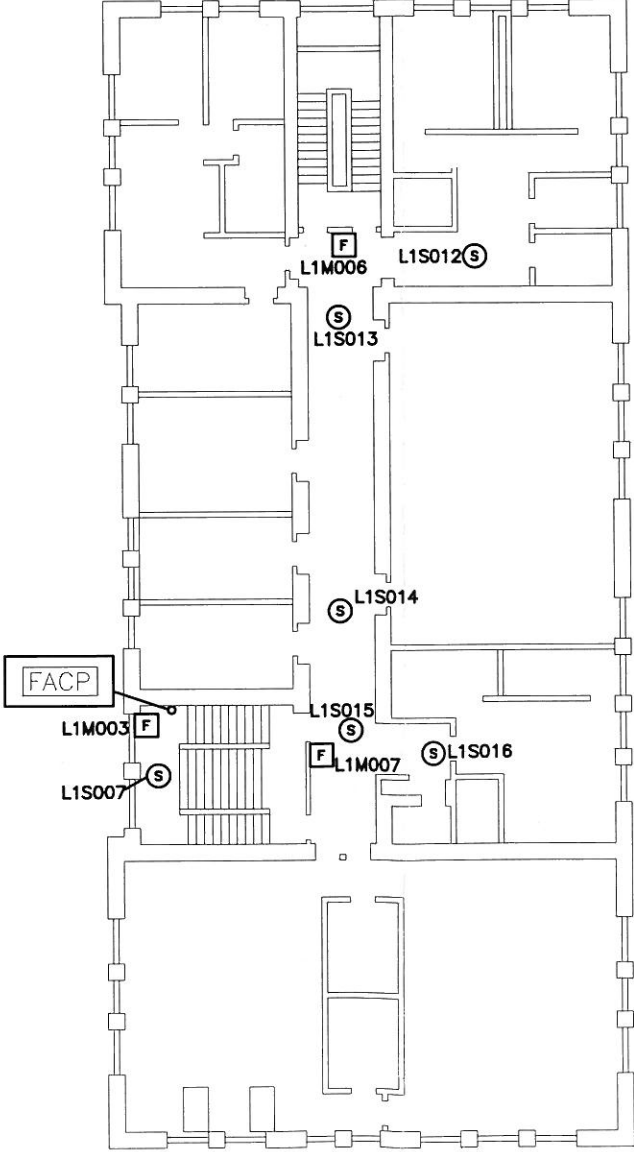

SECOND FLOOR PLAN

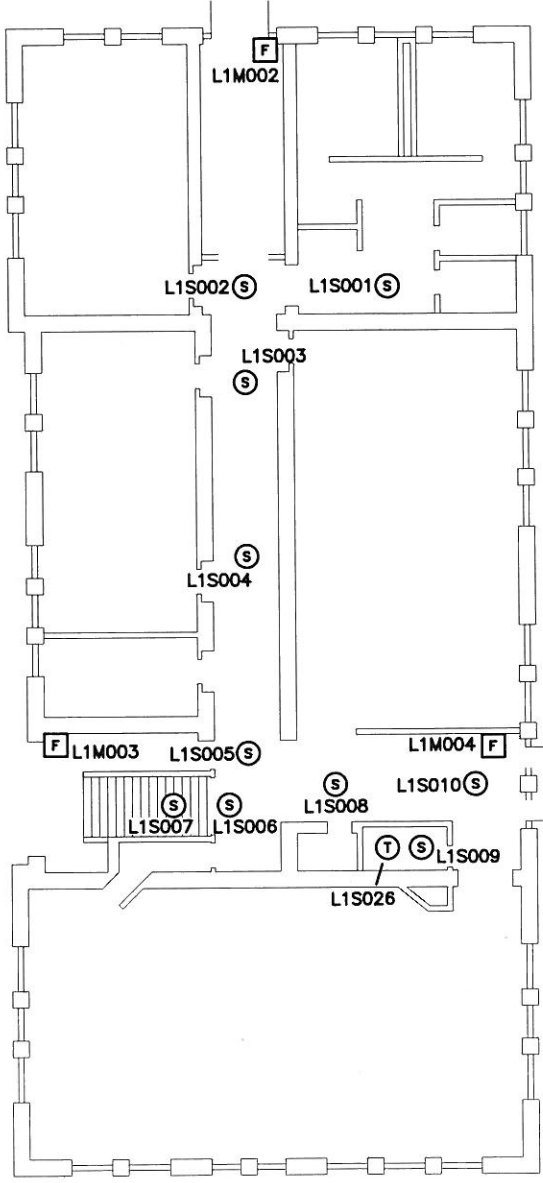

FIRST FLOOR PLAN

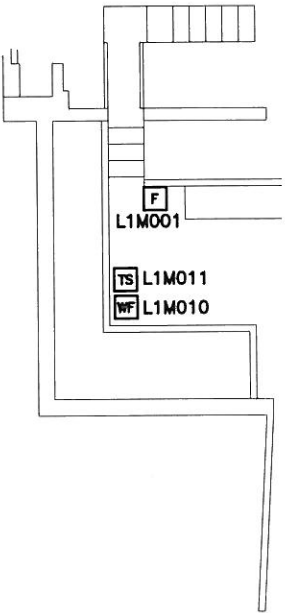

PARTIAL TUNNEL FLOOR PLAN

NOTE:
NFS DRAWINGS ARE BASED ON THE PROJECT ARCHITECT/ENGINEER (A/E) PLANS AND SPECIFICATIONS FURNISHED TO NFS. A/E IS SOLELY RESPONSIBLE (NOT NFS) FOR THE TYPE, SIZE, LOCATION, AND SUITABILITY OF ALL FIRE ALARMS, CONTROL PANELS, AND OTHER DEVICES SHOWN ON THE A/E PLANS. NFS DRAWINGS ARE TO SHOW ONLY THE WIRING DIAGRAMS BETWEEN FIRE ALARM DEVICES AND CONTROL PANELS. NFS IS NOT RESPONSIBLE FOR THE INFORMATION SHOWN ON THE A/E PLANS.

TALMAGE
FLOOR PLAN
FIRE ALARM SYSTEM
UNIVERSITY OF UTAH

NFS
NELSON FIRE SYSTEMS
801-468-8300

DRAWN BY: JG
DESIGNED BY: XXXX
APPROVED BY: DS
DATE: 9/27/07
SCALE: N.T.S.
PROJECT NO: XXXX
REV NO: XXXX
DRAWING NAME: TALMAGE DWG

FIRE ALARM SYSTEM
NUMBERS

PAGE