


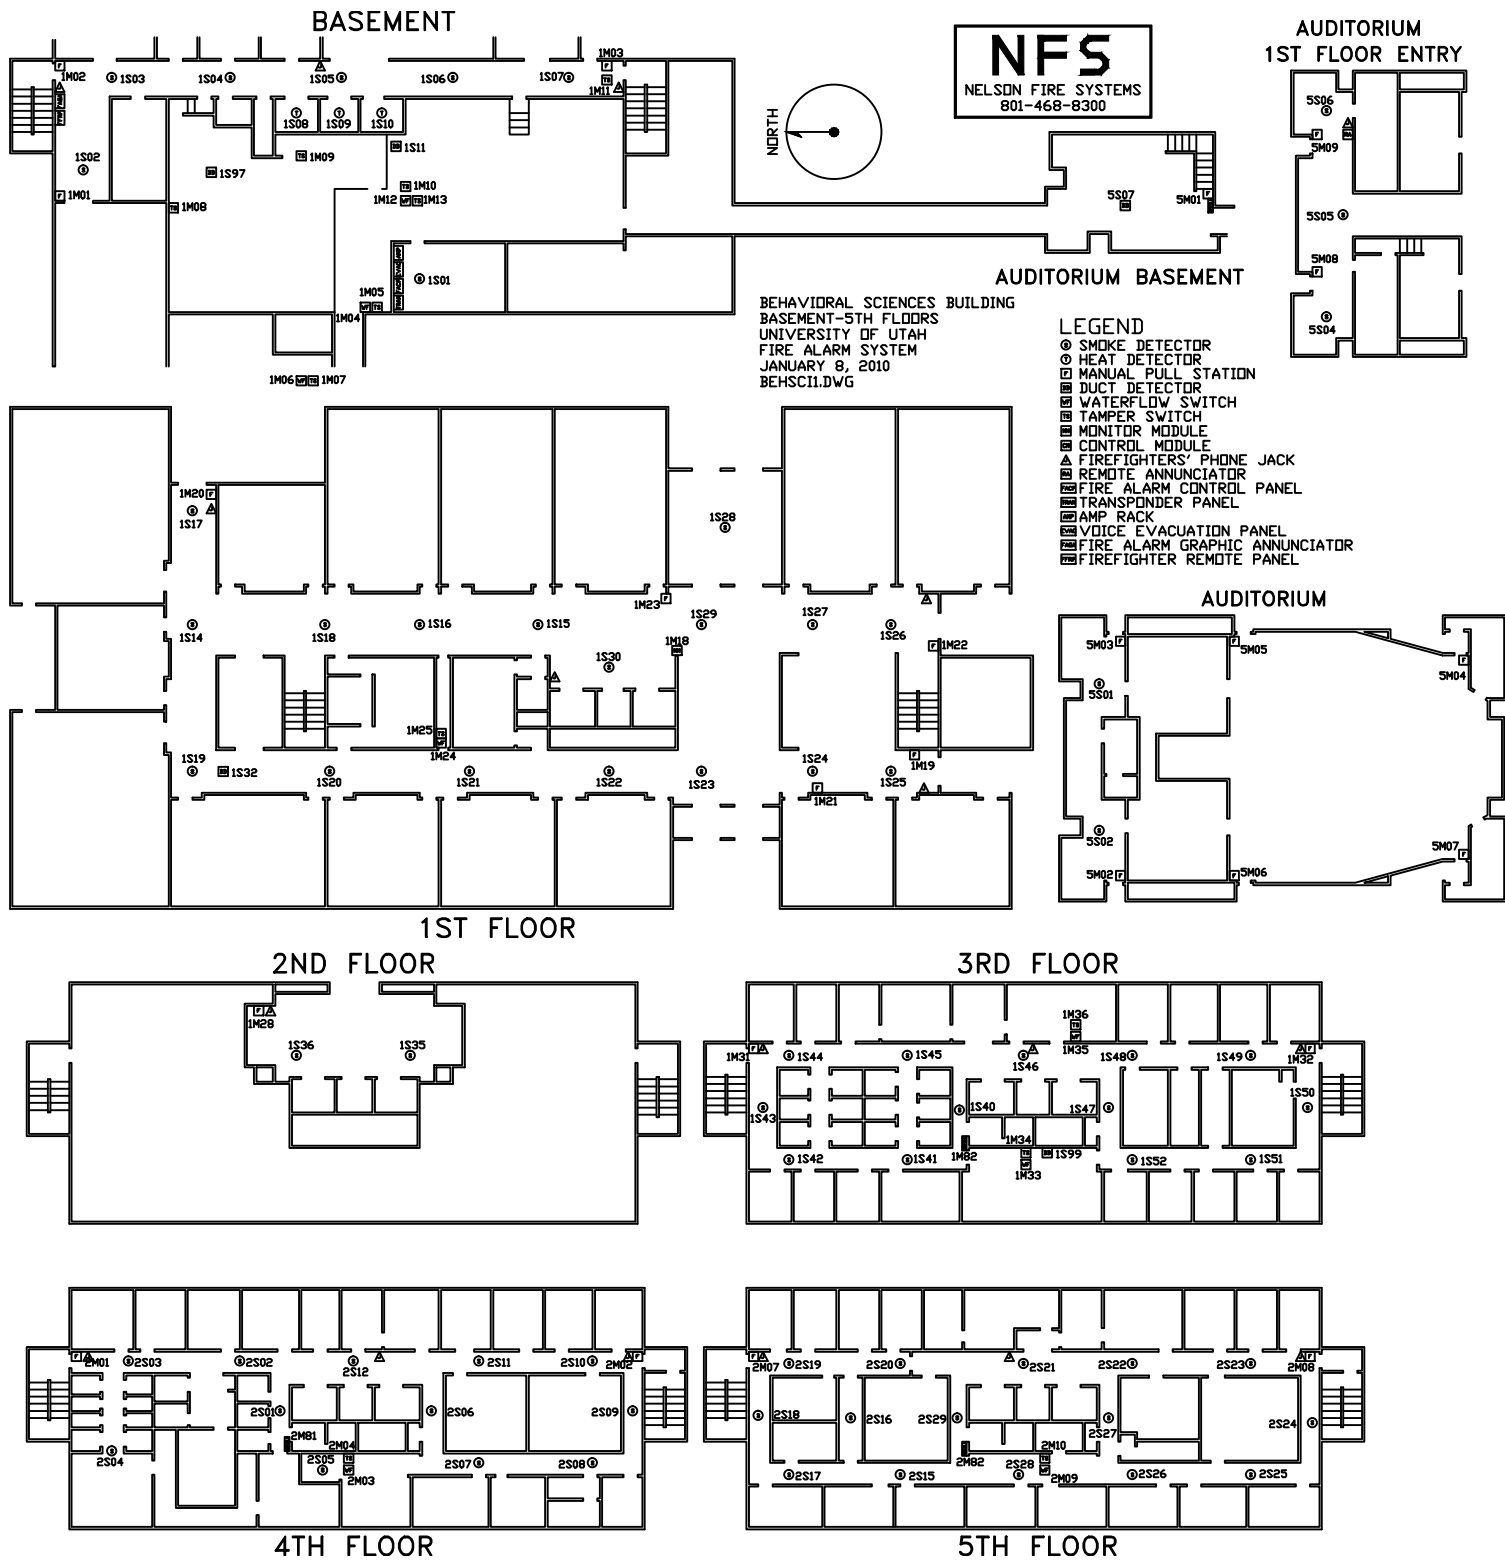

Floor plan of the second floor. The plan shows a central corridor with stairs at both ends. Rooms are labeled with circled numbers and a '3' prefix. The layout includes a large conference room on the right, several offices, and a central area with a staircase and a small room labeled 3M4. The rooms are arranged around a central corridor, with some rooms having multiple entrances or exits. The plan also shows a large room on the left with a staircase and a small room labeled 3M1.

4M26
4M25
4M24
4M31
4S41
4S40
4M21
4S39
4M22
4M23
4M24
4S42
4M25



- ☐ SMOKE DETECTOR
- ☐ HEAT DETECTOR
- ☐ MANUAL PULL STATION
- ☐ DUCT DETECTOR
- ☒ WATERFLOW SWITCH
- ☐ TAMPER SWITCH
- ☐ CONTROL MODULE
- ☒ FIREFIGHTERS' PHONE JACK
- ☐ TRANSPONDER PANEL

4S49 4S50 4S51
4S52
4S53

4M90 ELEV EXHAUST FAN
4M89 ELEV SHAFT DAMPER
4M96 HAT FLASH
4M95 RECALL TO MAIN
4M94 RECALL TO ALT.
4M93 NORTH ELEV SHUNT
4M92 CENTER ELEV SHUNT
4M91 SOUTH ELEV SHUNT