



N.I.C.E.T.
LEVEL III
CERTIFICATION

FIRE ALARM SYSTEMS

DONNY SCHULTZ
#104396

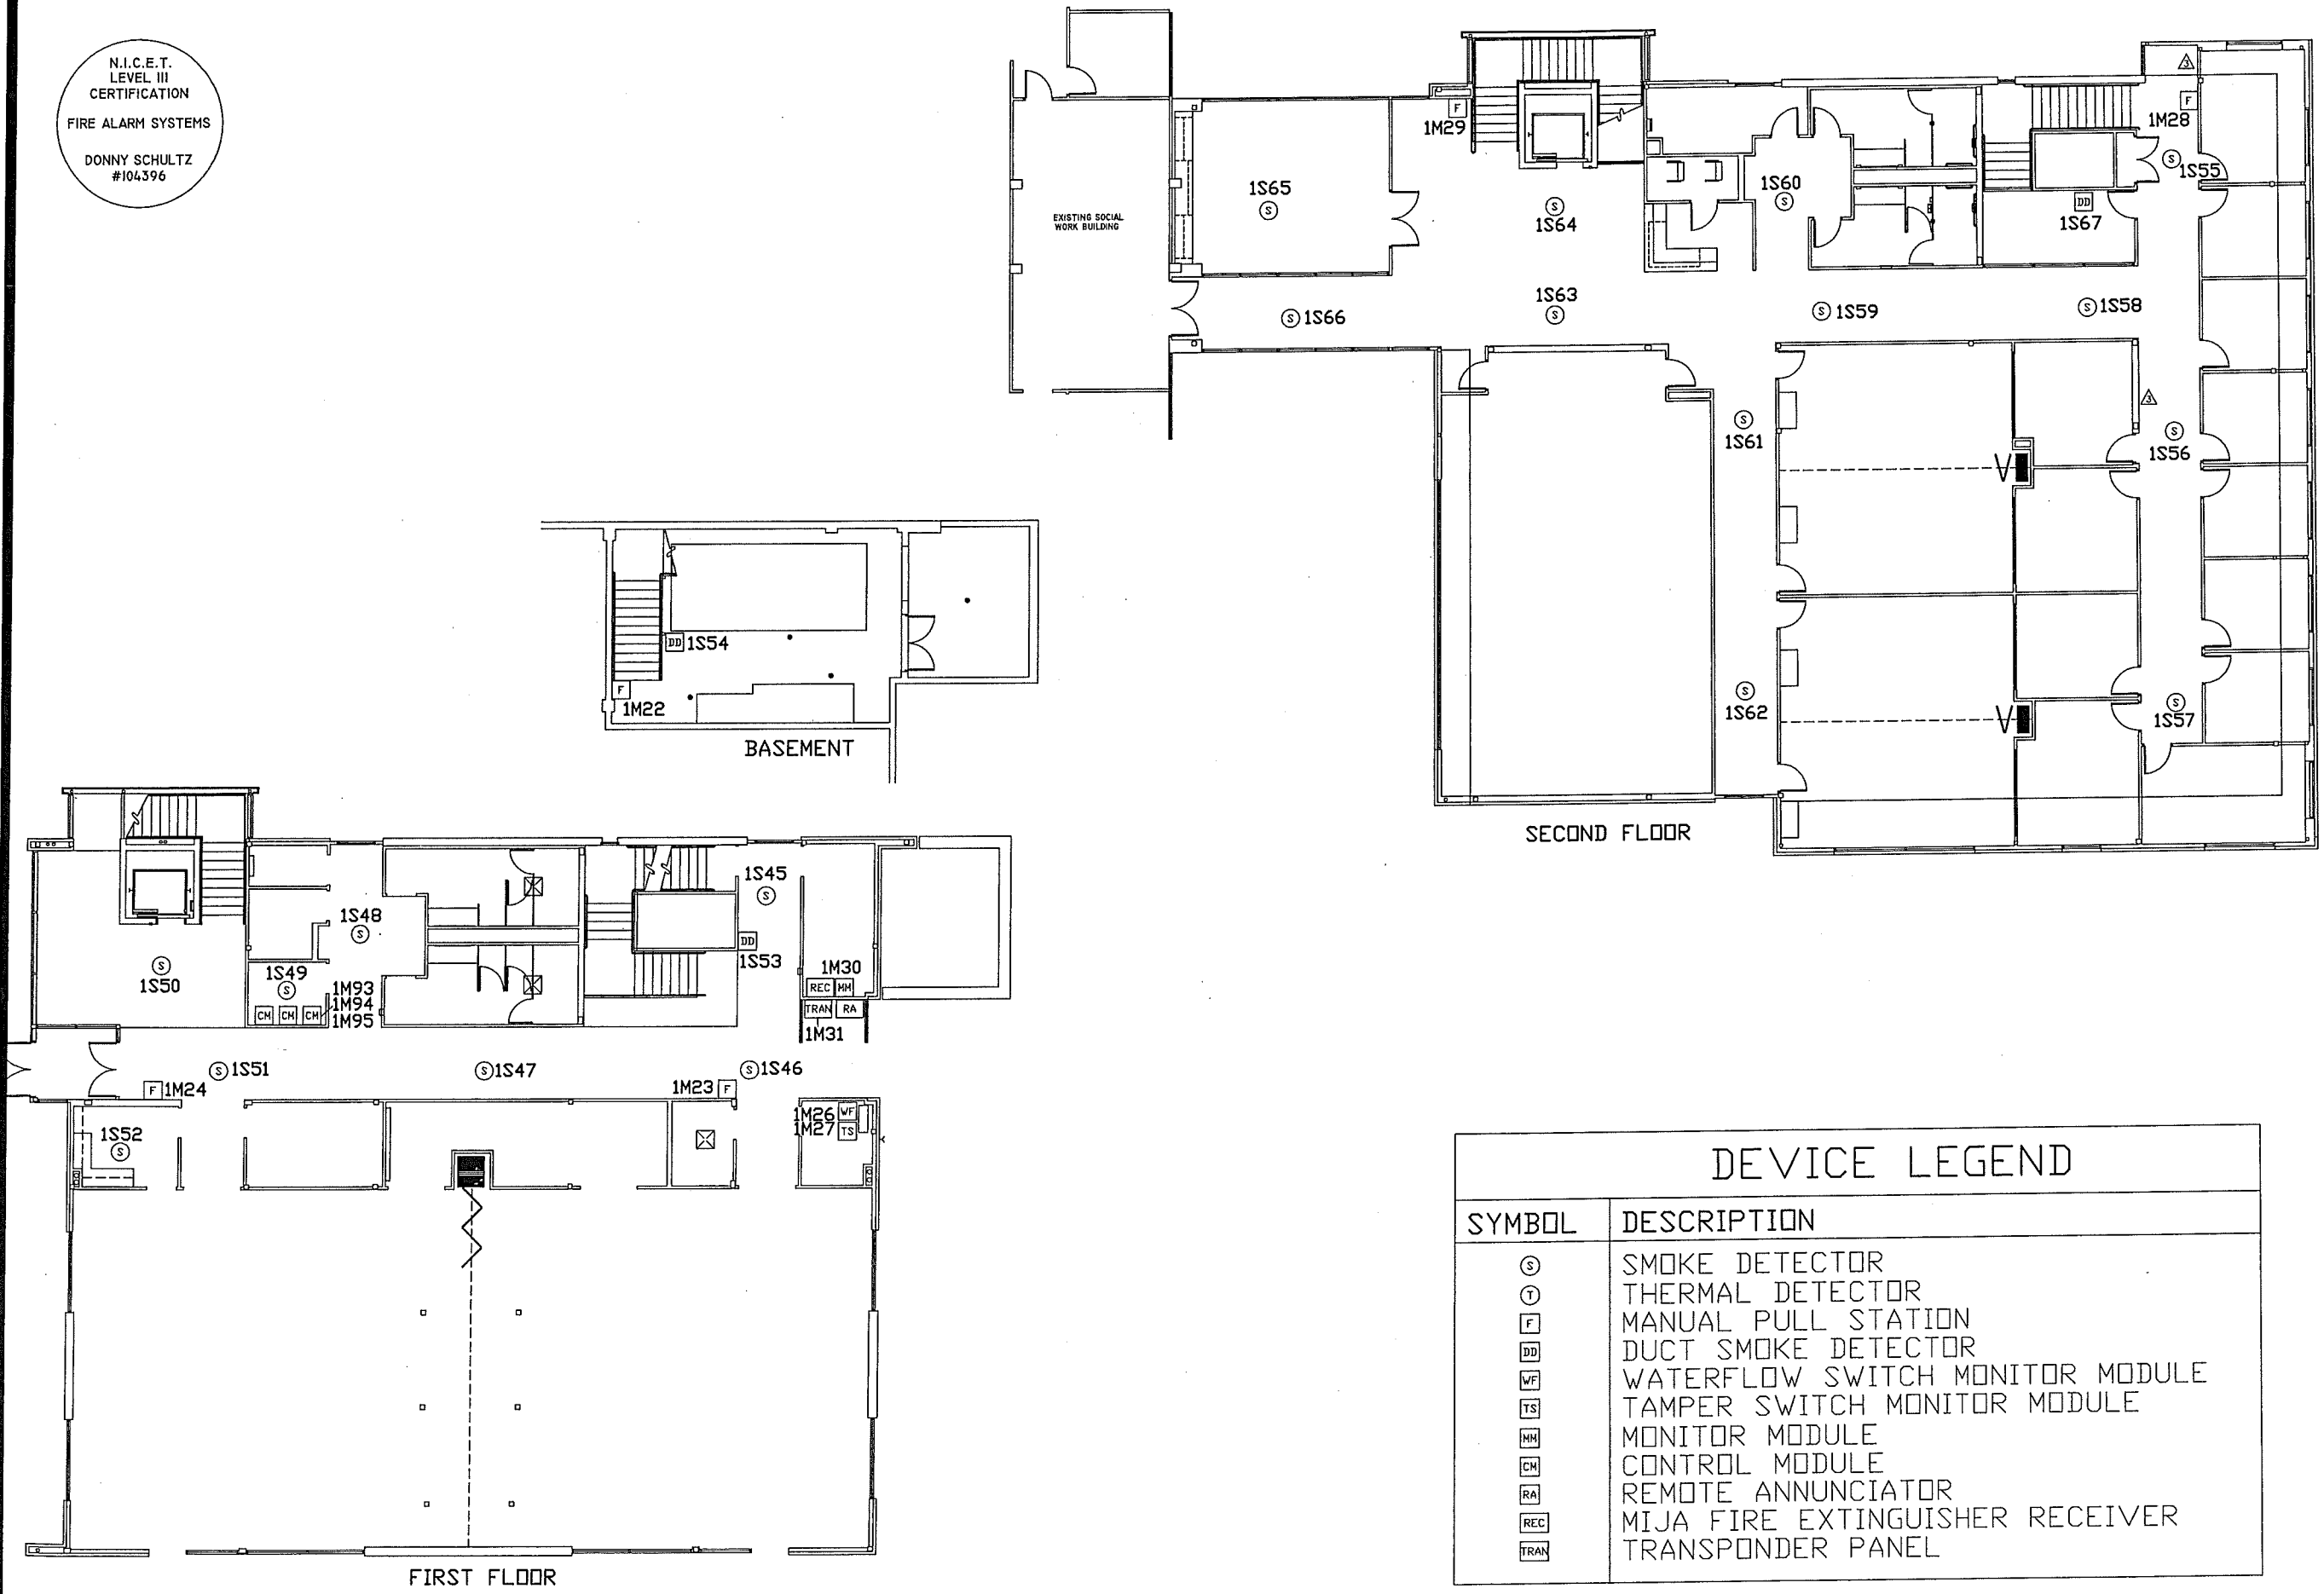

DEVICE LEGEND	
SYMBOL	DESCRIPTION
Ⓢ	SMOKE DETECTOR
Ⓣ	THERMAL DETECTOR
F	MANUAL PULL STATION
DD	DUCT SMOKE DETECTOR
WF	WATERFLOW SWITCH MONITOR MODULE
TS	TAMPER SWITCH MONITOR MODULE
HM	MONITOR MODULE
CM	CONTROL MODULE
RA	REMOTE ANNUNCIATOR
REC	MIJA FIRE EXTINGUISHER RECEIVER
TRAN	TRANSPONDER PANEL

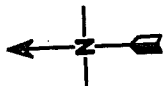

NFS DRAWINGS ARE BASED ON THE PROJECT ARCHITECT/ENGINEER (A/E) PLANS AND SPECIFICATIONS FURNISHED TO NFS. A/E IS SOLELY RESPONSIBLE (NOT NFS) FOR THE TYPE, SIZE, LOCATION, AND SUITABILITY OF ALL FIRE ALARMS, CONTROL PANELS, AND OTHER DEVICES SHOWN ON THE A/E PLANS. NFS DRAWINGS ARE TO SHOW ONLY THE WIRING DIAGRAMS BETWEEN FIRE ALARM DEVICES AND CONTROL PANELS. NFS IS NOT RESPONSIBLE FOR THE INFORMATION SHOWN ON THE A/E PLANS.

COLLEGE OF SOCIAL WORK ADDITION
UNIVERSITY OF UTAH
SOUTH BUILDING
FIRE ALARM SYSTEM

NFS
NELSON FIRE SYSTEMS
801-468-8300

DRAWN BY:	DS
DESIGNED BY:	XXXX
APPROVED BY:	TCT
DATE:	5/6/2008
SCALE:	NONE
PROJECT NO:	0026-III64
REV NO:	I
DRAWING NAME:	SOCIALWORKADDITION IB .DWG

FIRE ALARM SYSTEM

PAGE: