


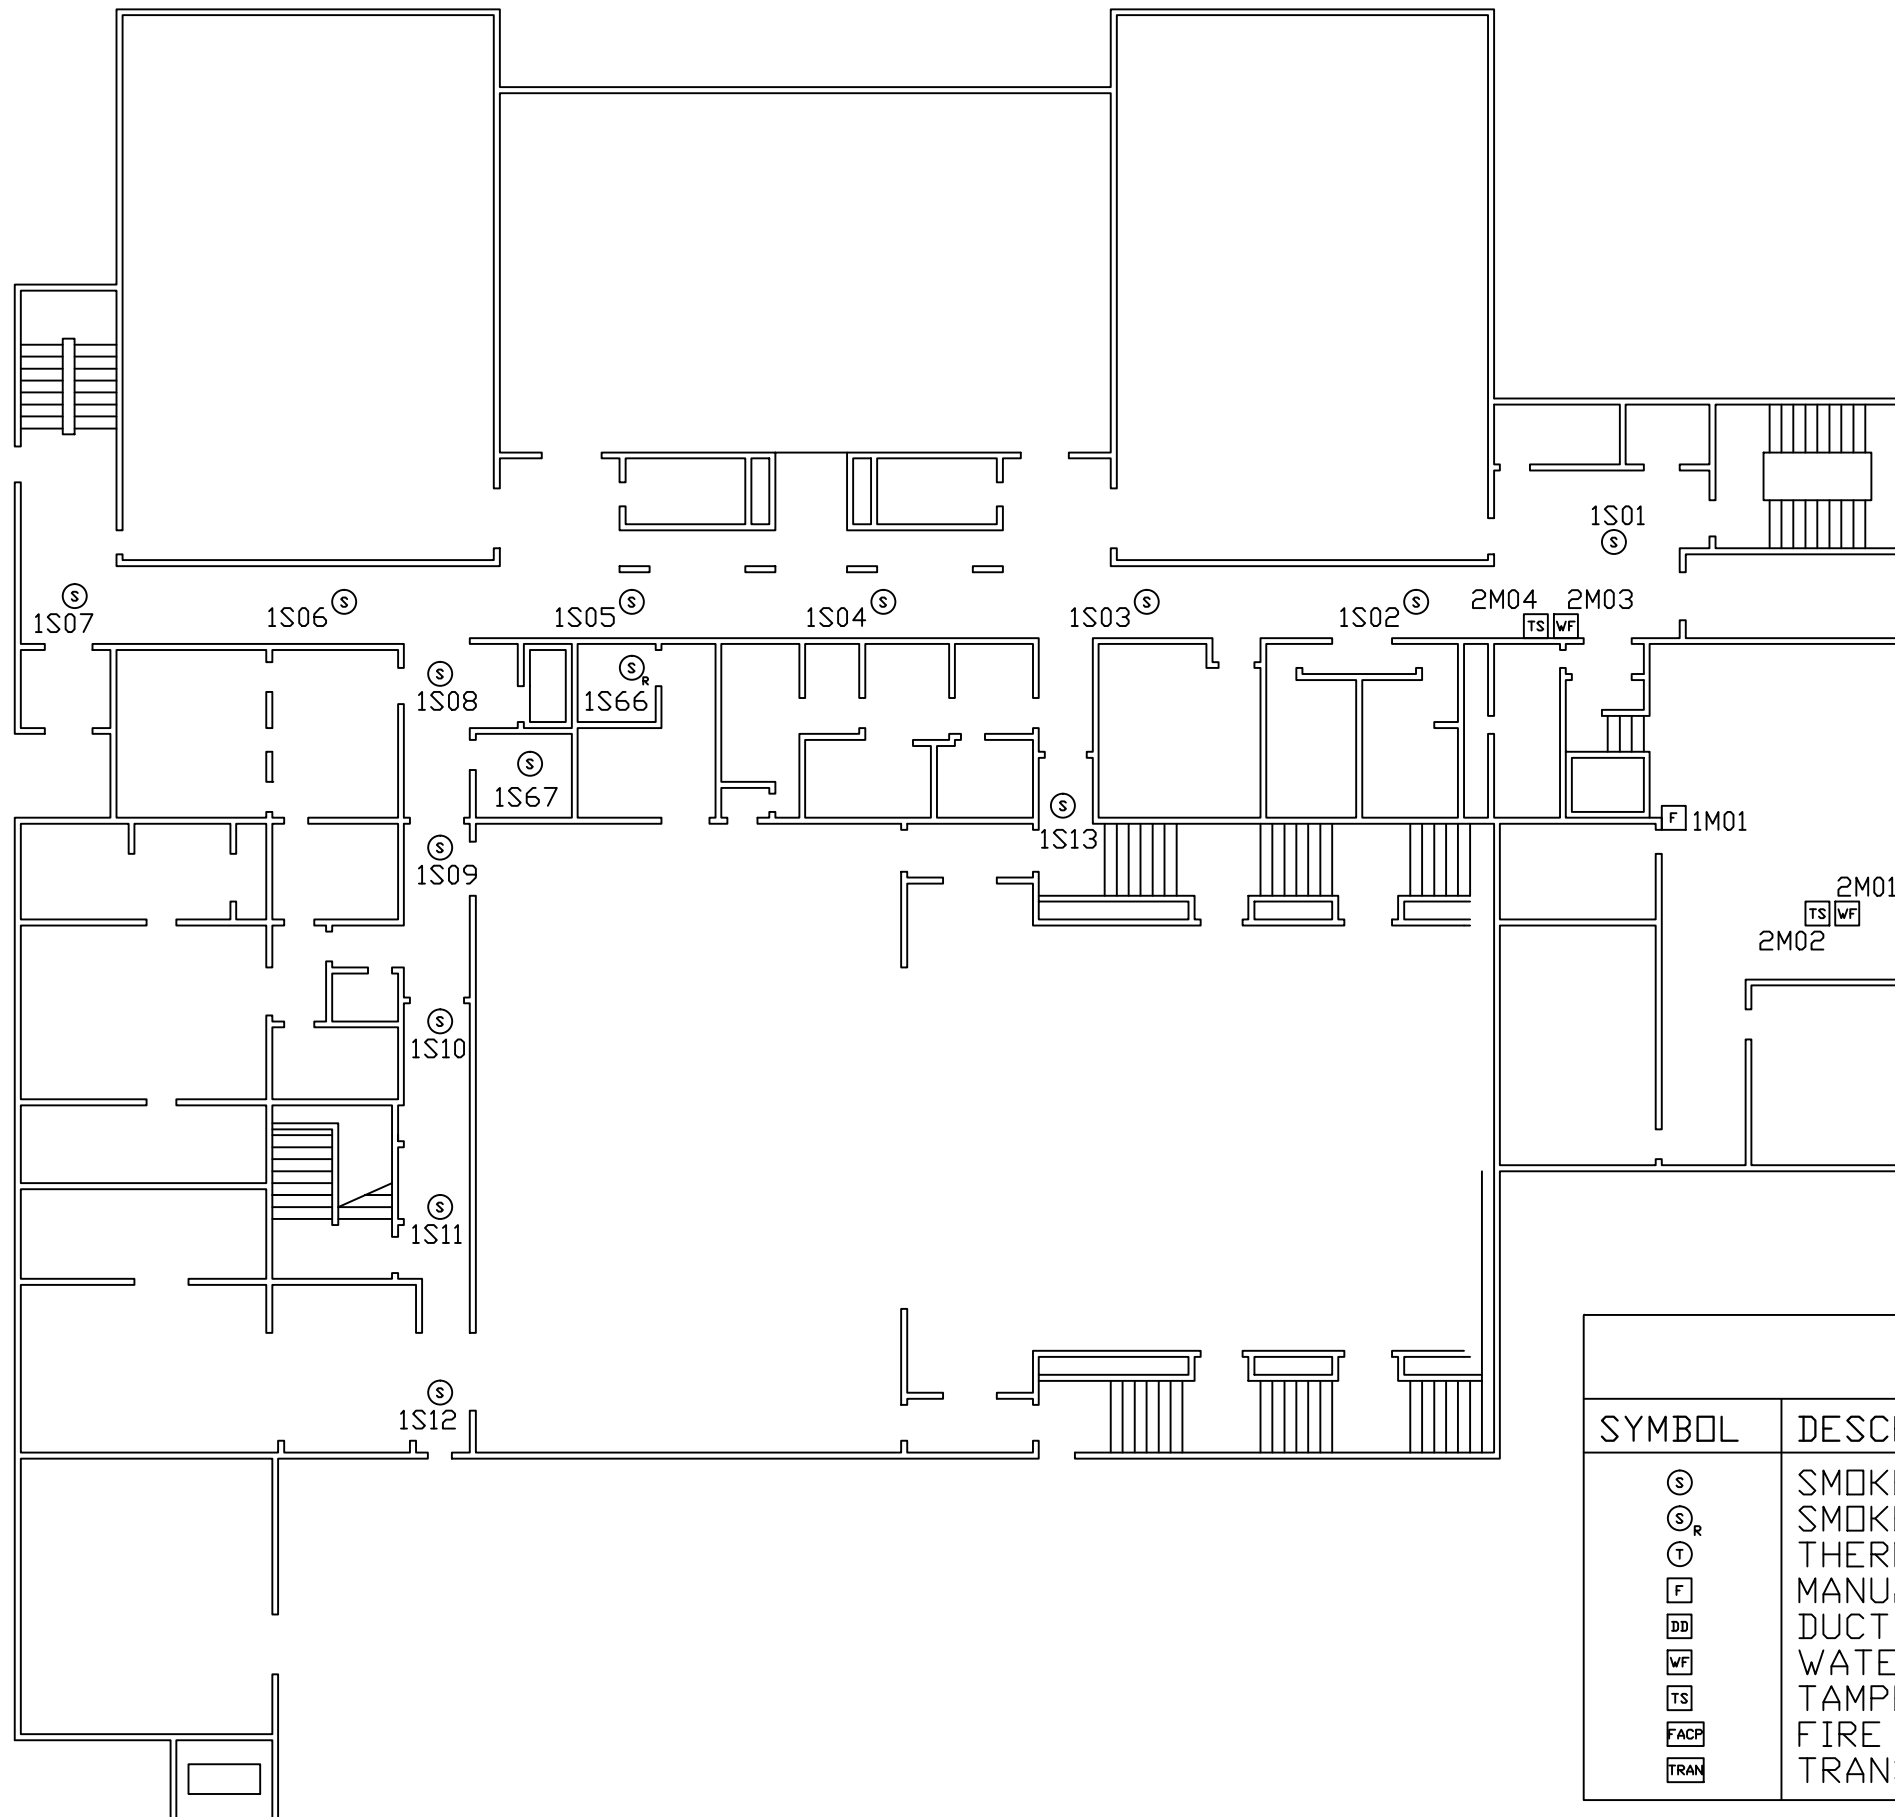

ADDRESS LABEL CLARIFICATION

ADDRESSABLE LOOP NUMBER
SENSOR ("M" MONITOR)
DEVICE NUMBER

1S01

DEVICE LEGEND	
SYMBOL	DESCRIPTION
Ⓢ	SMOKE DETECTOR W/BASE
Ⓢ _R	SMOKE DETECTOR W/RELAY BASE
Ⓣ	THERMAL DETECTOR
F	MANUAL PULL STATION
DD	DUCT SMOKE DETECTOR
WF	WATERFLOW SWITCH MONITOR MODULE
TS	TAMPER SWITCH MONITOR MODULE
FACP	FIRE ALARM CONTROL PANEL
TRAN	TRANSPONDER PANEL



NOTE:
NFS DRAWINGS ARE BASED ON THE PROJECT
ARCHITECT/ENGINEER (A/E) PLANS AND SPECIFICATIONS
FURNISHED TO NFS. A/E IS SOLELY RESPONSIBLE
(NOT NFS) FOR THE TYPE, SIZE, LOCATION, AND
SUITABILITY OF ALL FIRE ALARMS, CONTROL PANELS,
AND OTHER DEVICES SHOWN ON THE A/E PLANS.
NFS DRAWINGS ARE TO SHOW ONLY THE WIRING
DIAGRAMS BETWEEN FIRE ALARM DEVICES AND
CONTROL PANELS. NFS IS NOT RESPONSIBLE FOR
THE INFORMATION SHOWN ON THE A/E PLANS.


UNIVERSITY OF UTAH
MARRIOTT CENTER FOR DANCE
SALT LAKE CITY, UTAH
FIRE ALARM SYSTEM
FIRST FLOOR

NFS
NELSON FIRE SYSTEMS
801-468-8300



DRAWN BY:	ZM
DESIGNED BY:	XXXX
APPROVED BY:	XXXX
DATE:	6/21/05
SCALE:	N.T.S.
PROJECT NO:	XXXX
REV NO:	XXXX
DRAWING NAME:	MARRIOTT DANCE1.DWG

FIRE ALARM SYSTEM
1ST FLOOR DEVICE NUMBERS

PAGE:
FA-01

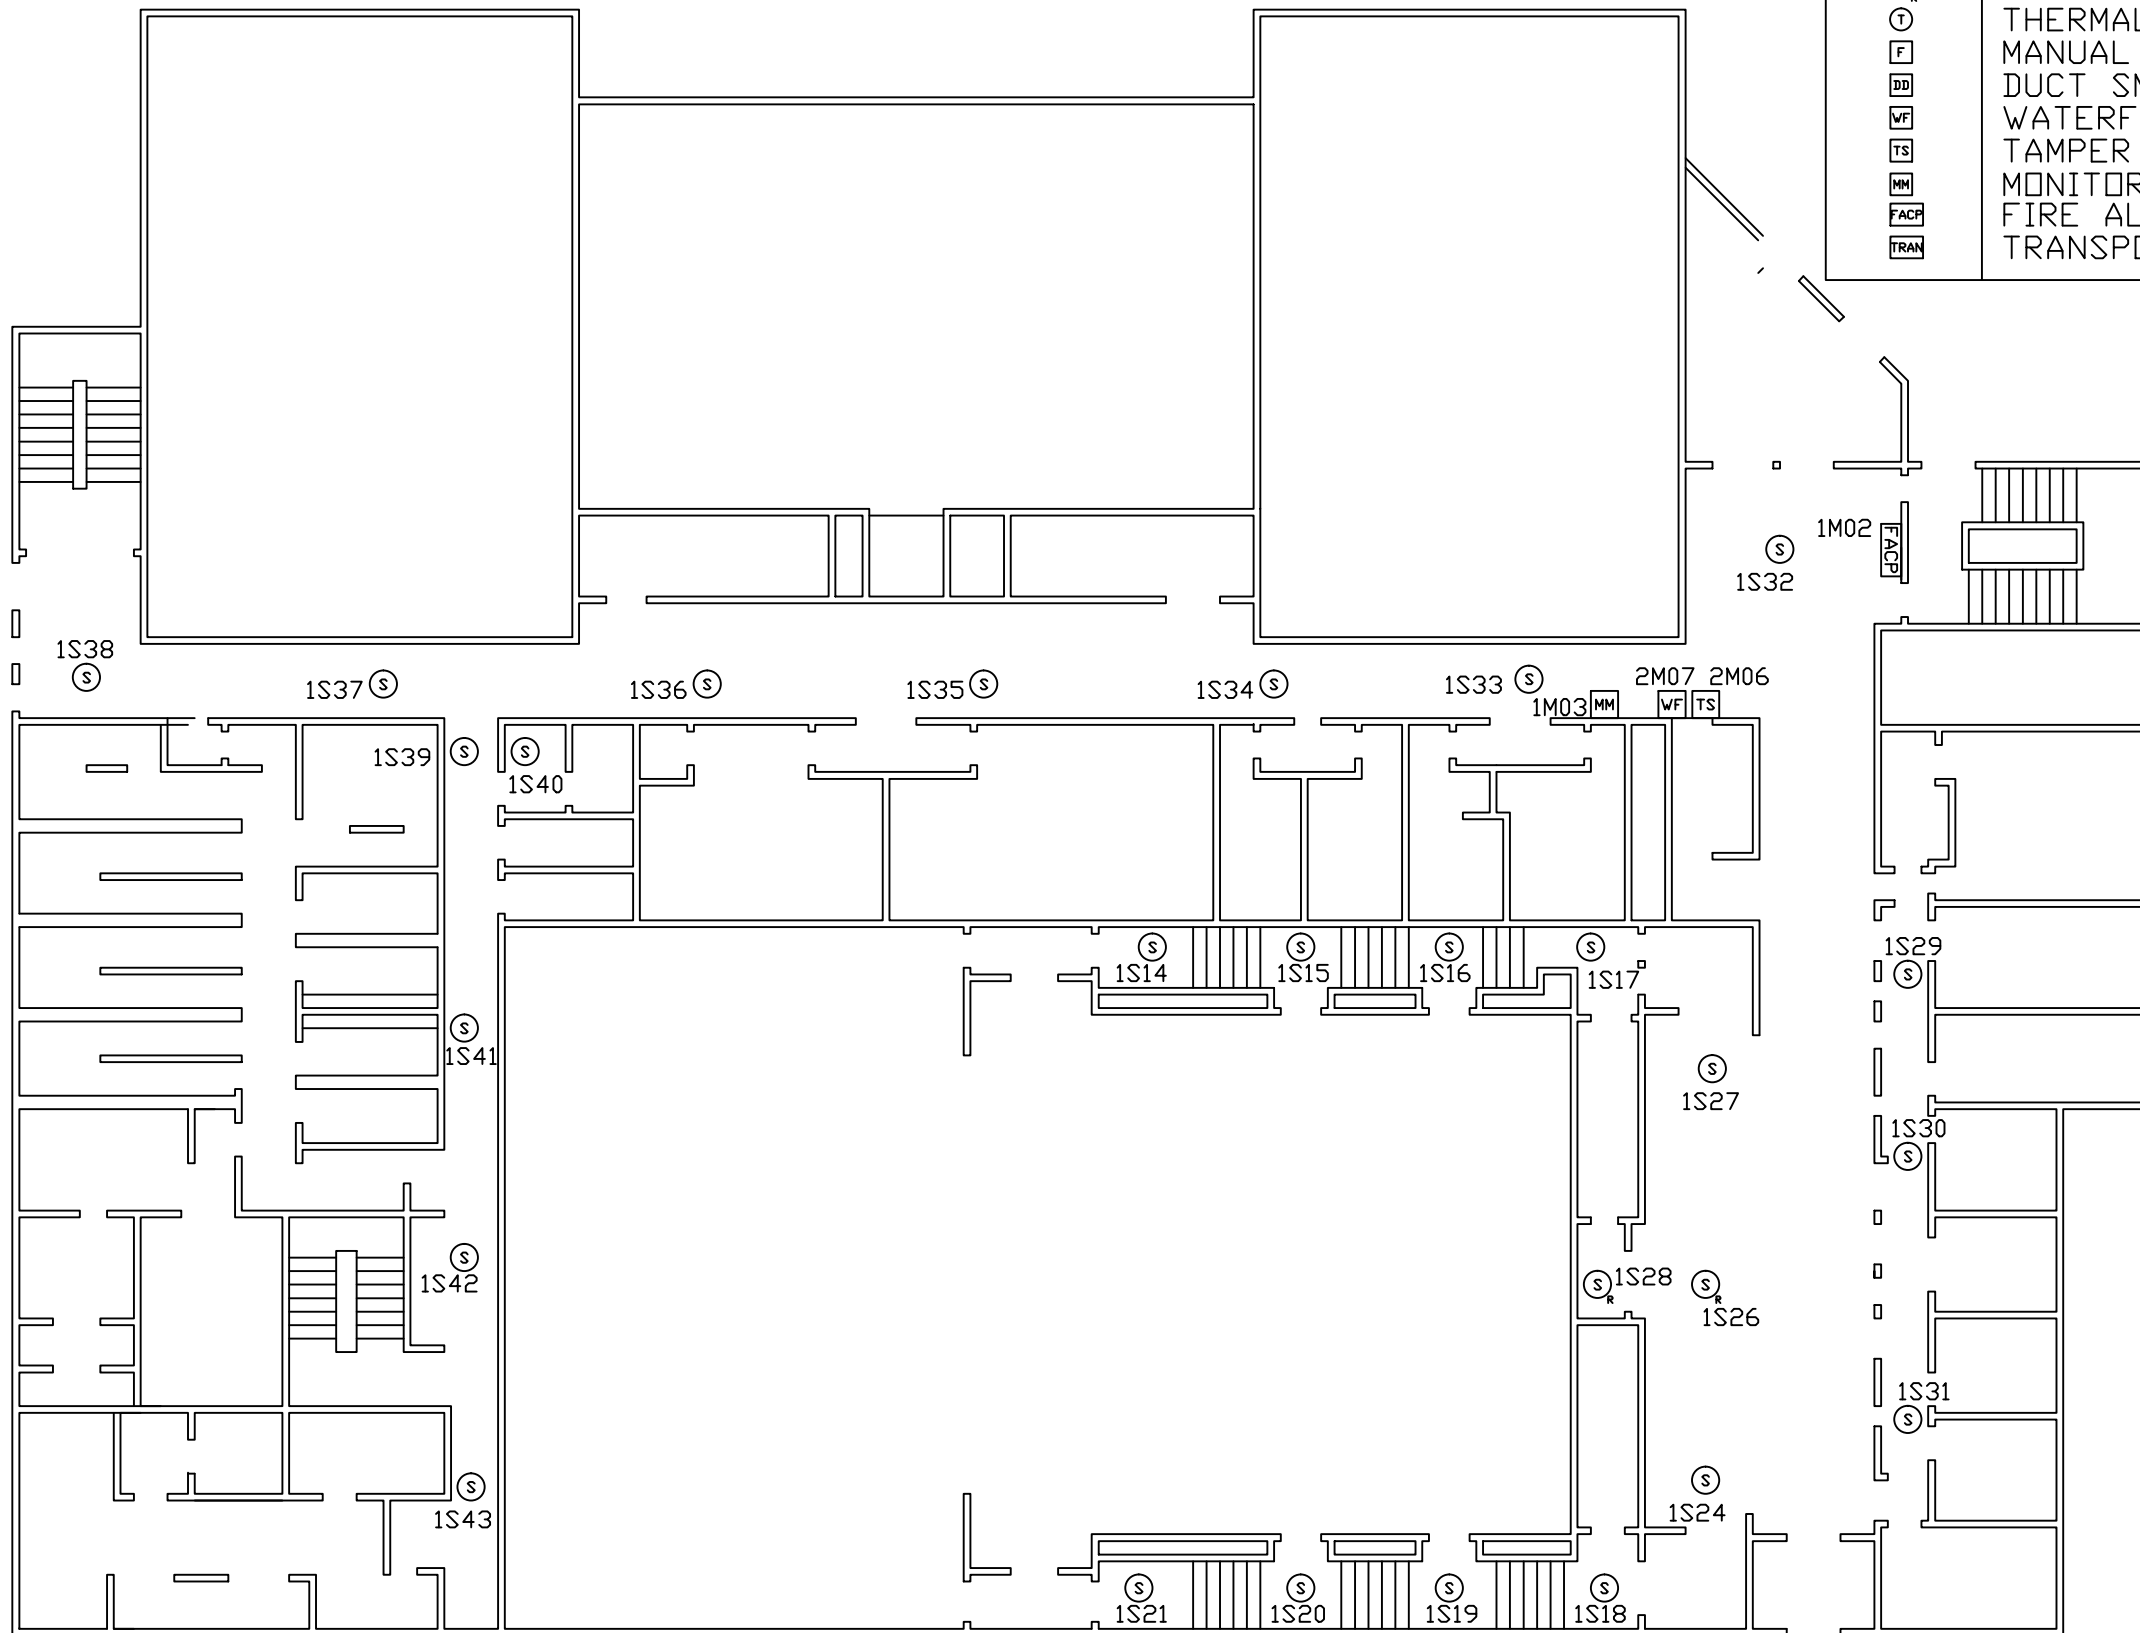

DEVICE LEGEND	
SYMBOL	DESCRIPTION
Ⓢ	SMOKE DETECTOR W/BASE
Ⓢ _R	SMOKE DETECTOR W/RELAY BASE
Ⓣ	THERMAL DETECTOR
ⓕ	MANUAL PULL STATION
ⓓⓓ	DUCT SMOKE DETECTOR
Ⓦⓕ	WATERFLOW SWITCH MONITOR MODULE
ⓉⓈ	TAMPER SWITCH MONITOR MODULE
ⓂⓂ	MONITOR MODULE
ⓕⓐⓔⓅ	FIRE ALARM CONTROL PANEL
ⓉⓇⓐⓃ	TRANSPONDER PANEL

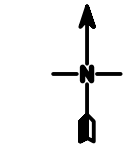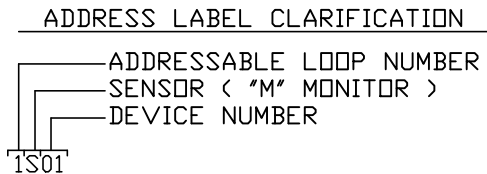

NOTE:
NFS DRAWINGS ARE BASED ON THE PROJECT
ARCHITECT/ENGINEER (A/E) PLANS AND SPECIFICATIONS
FURNISHED TO NFS. A/E IS SOLELY RESPONSIBLE
(NOT NFS) FOR THE TYPE, SIZE, LOCATION, AND
SUITABILITY OF ALL FIRE ALARMS, CONTROL PANELS,
AND OTHER DEVICES SHOWN ON THE A/E PLANS.
NFS DRAWINGS ARE TO SHOW ONLY THE WIRING
DIAGRAMS BETWEEN FIRE ALARM DEVICES AND
CONTROL PANELS. NFS IS NOT RESPONSIBLE FOR
THE INFORMATION SHOWN ON THE A/E PLANS.


UNIVERSITY OF UTAH
MARRIOTT CENTER FOR DANCE
SALT LAKE CITY, UTAH
FIRE ALARM SYSTEM
SECOND FLOOR

NFS
NELSON FIRE SYSTEMS
801-468-8300


DRAWN BY:	ZM
DESIGNED BY:	XXXX
APPROVED BY:	XXXX
DATE:	1/8/2010
SCALE:	N.T.S.
PROJECT NO:	XXXX
REV NO:	XXXX
DRAWING NAME:	MARRIOTT DANCE2.DWG

FIRE ALARM SYSTEM
2ND FLR DEVICE NUMBERS

PAGE:
FA-02

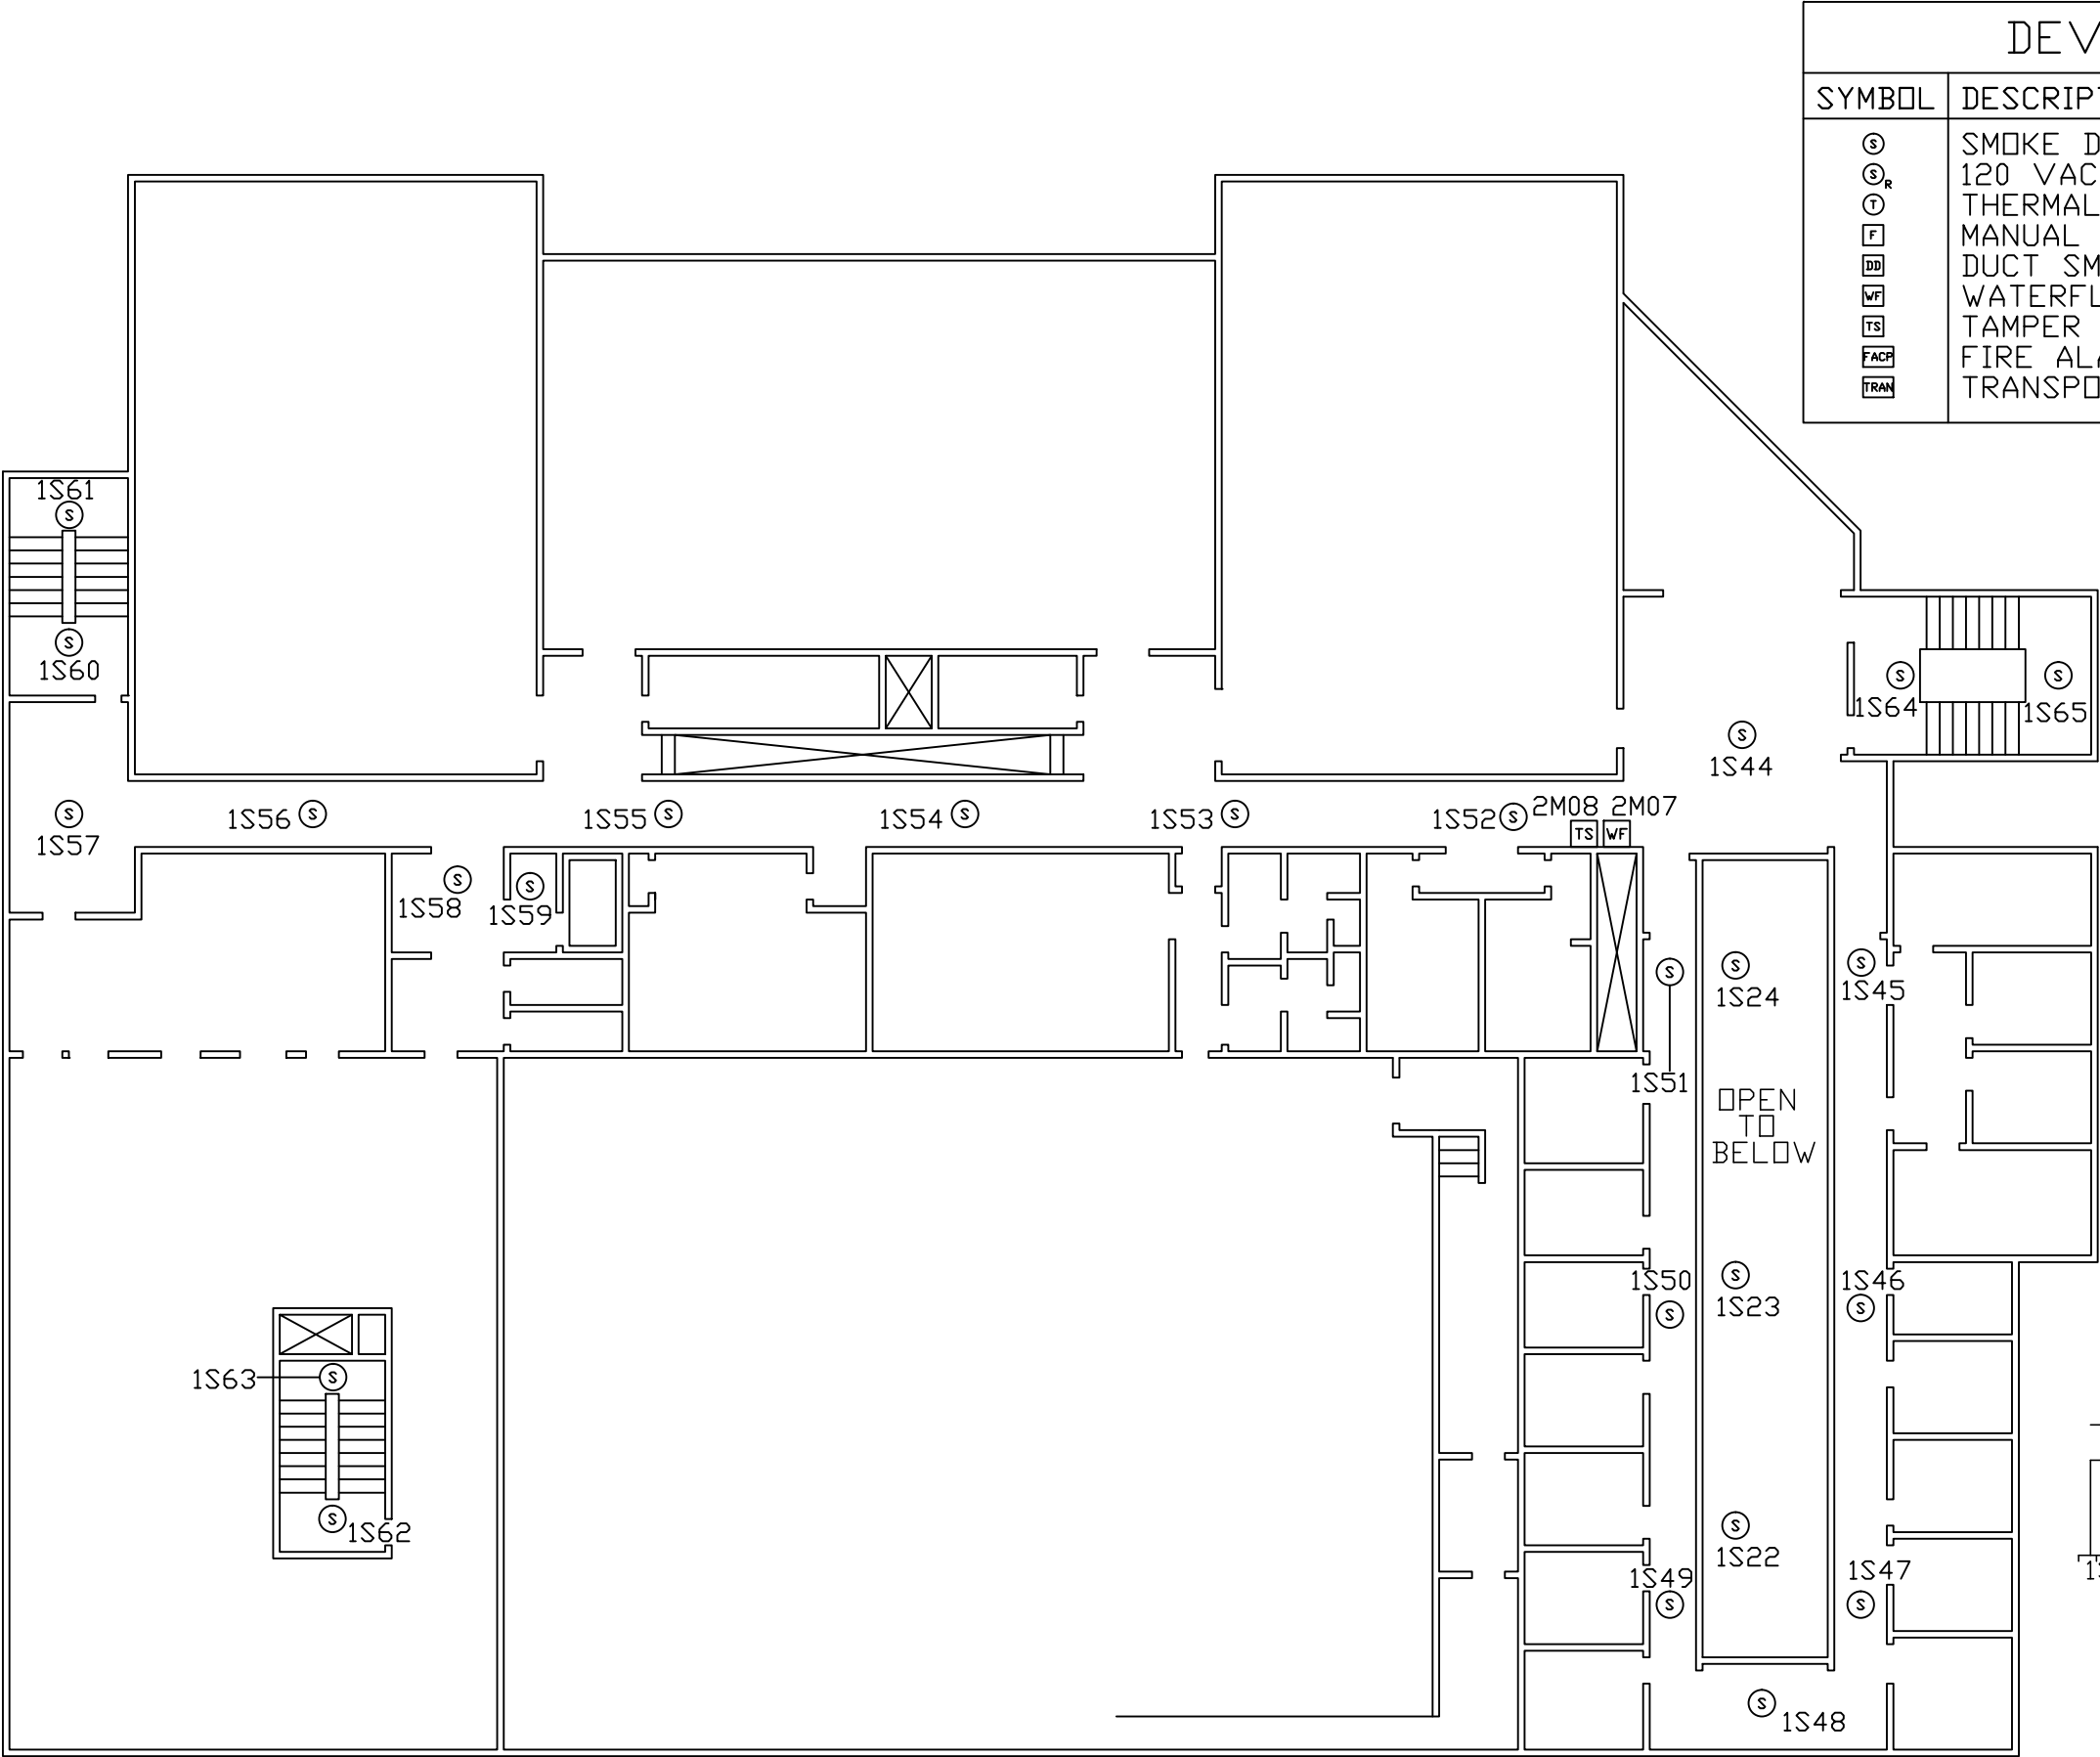

DEVICE LEGEND	
SYMBOL	DESCRIPTION
Ⓢ	SMOKE DETECTOR W/BASE
Ⓢ _R	120 VAC RESIDENTIAL DETECTOR
Ⓢ _T	THERMAL DETECTOR
F	MANUAL PULL STATION
DD	DUCT SMOKE DETECTOR
WF	WATERFLOW SWITCH MONITOR MODULE
TS	TAMPER SWITCH MONITOR MODULE
FACP	FIRE ALARM CONTROL PANEL
TRAN	TRANSPONDER PANEL

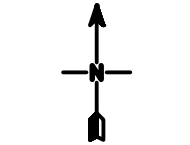

NOTE:
NFS DRAWINGS ARE BASED ON THE PROJECT
ARCHITECT/ENGINEER (A/E) PLANS AND SPECIFICATIONS
FURNISHED TO NFS. A/E IS SOLELY RESPONSIBLE
(NOT NFS) FOR THE TYPE, SIZE, LOCATION, AND
SUITABILITY OF ALL FIRE ALARMS, CONTROL PANELS,
AND OTHER DEVICES SHOWN ON THE A/E PLANS.
NFS DRAWINGS ARE TO SHOW ONLY THE WIRING
DIAGRAMS BETWEEN FIRE ALARM DEVICES AND
CONTROL PANELS. NFS IS NOT RESPONSIBLE FOR
THE INFORMATION SHOWN ON THE A/E PLANS.

UNIVERSITY OF UTAH
MARRIOTT CENTER FOR DANCE
SALT LAKE CITY, UTAH
FIRE ALARM SYSTEM
THIRD FLOOR

NFS
NELSON FIRE SYSTEMS
801-468-8300

ADDRESS LABEL CLARIFICATION

1S01

ADDRESSABLE LOOP NUMBER
SENSOR ("M" MONITOR)
DEVICE NUMBER

DRAWN BY: ZM
DESIGNED BY: XXXX
APPROVED BY: XXXX
DATE: 6/21/05
SCALE: N.T.S.
PROJECT NO: XXXX
REV NO: XXXX
DRAWING NAME:
MARRIOTT DANCE3.DWG

FIRE ALARM SYSTEM
3RD FLR DEVICE NUMBERS

PAGE:
FA-03