
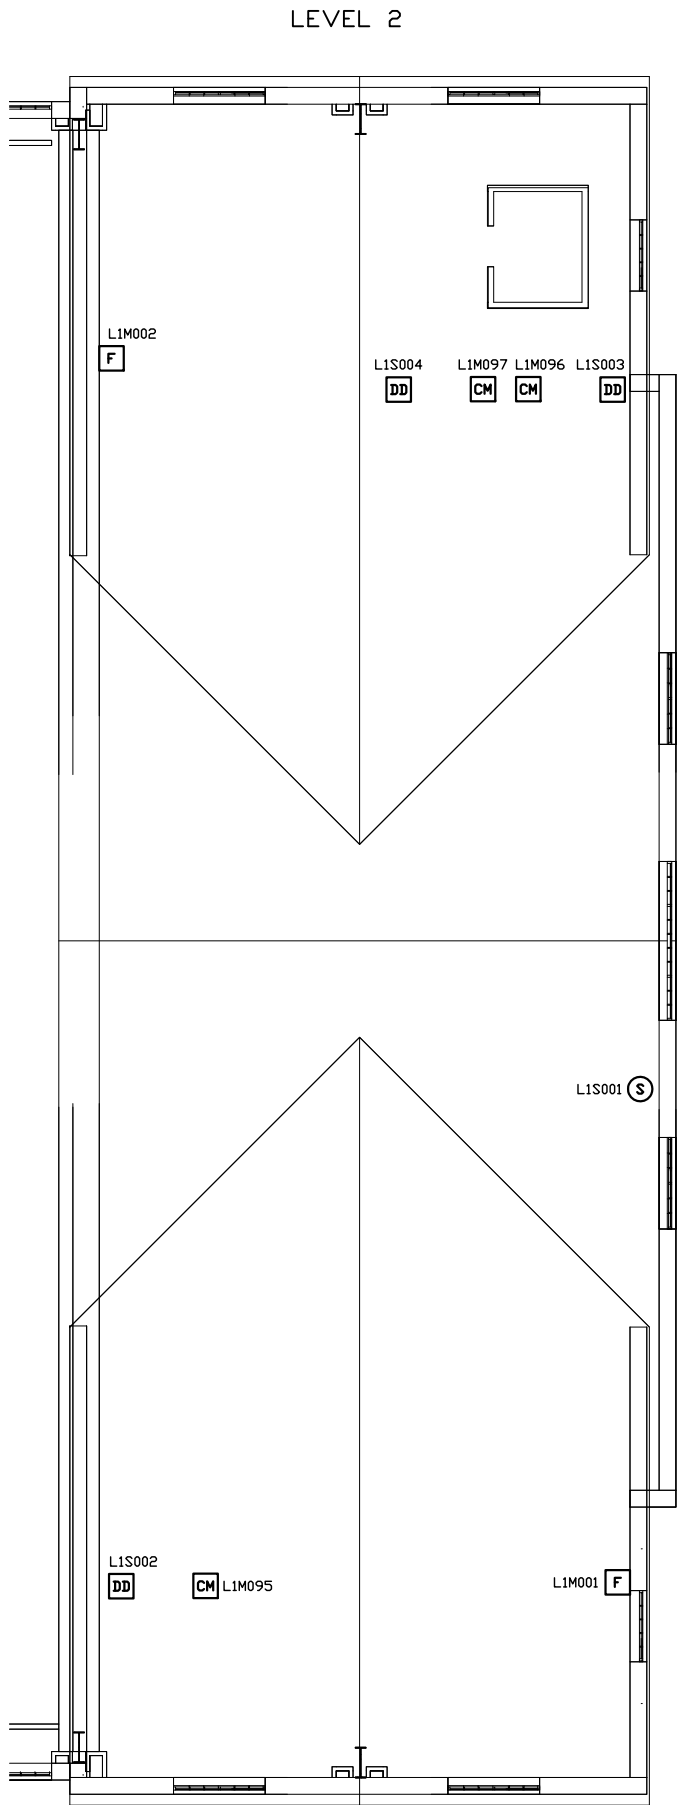


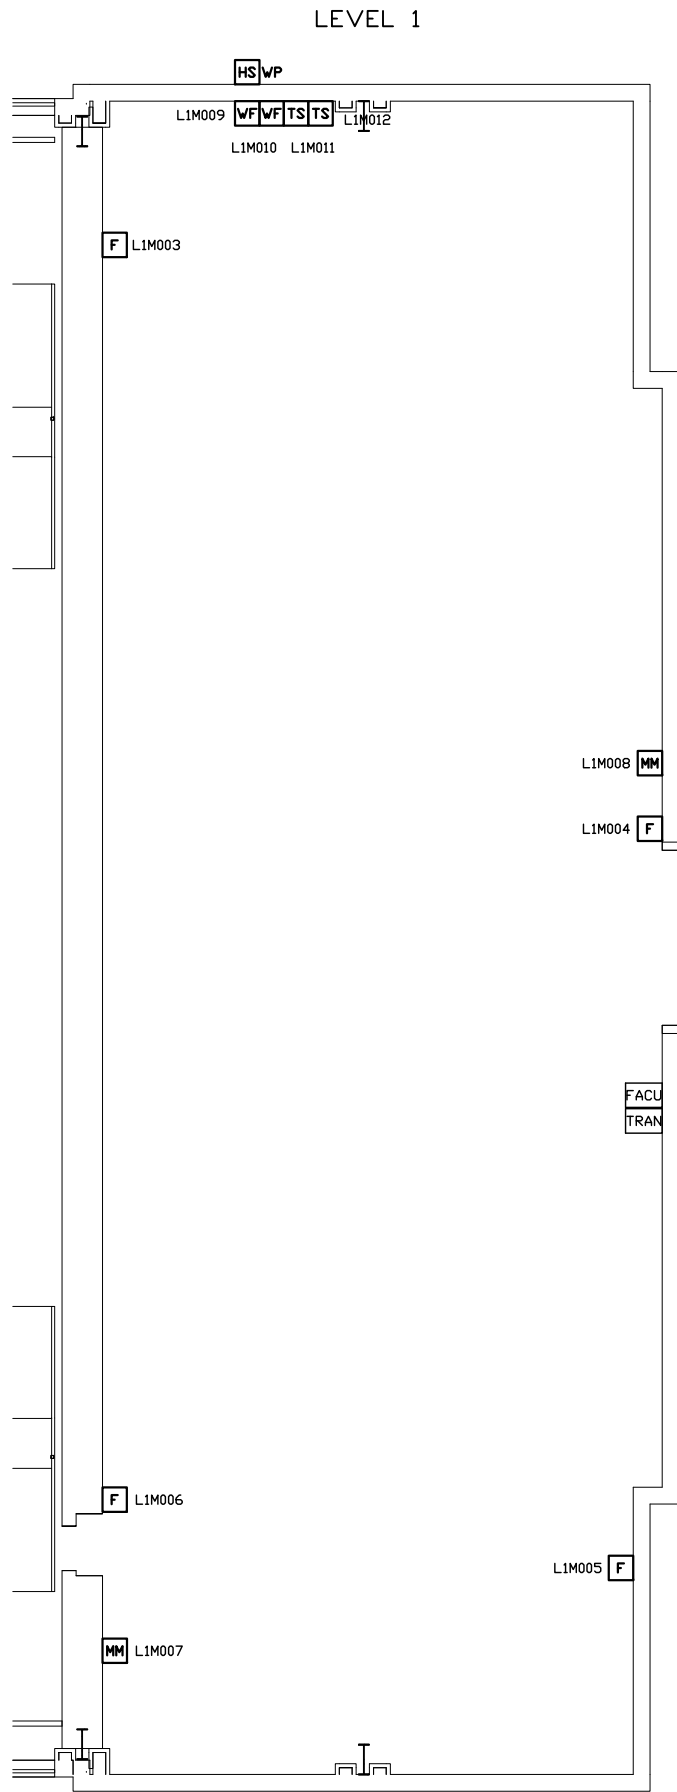

DEVICE LEGEND	
SYMBOL	DESCRIPTION
	HEAT DETECTOR
	PULL STATION
	DUCT DETECTOR
	TAMPER SWITCH
	WATERFLOW SWITCH
	MONITOR MODULE
	CONTROL MODULE
	FIRE ALARM CONTROL UNIT
	TRANSPONDER PANEL

NOTE:
NFS DRAWINGS ARE BASED ON THE PROJECT
ARCHITECTURE/ENGINEER (A/E) PLANS AND
SPECIFICATIONS FURNISHED TO NFS. A/E IS SOLELY
RESPONSIBLE (NOT NFS) FOR THE TYPE, SIZE,
LOCATION, AND SUITABILITY OF ALL FIRE ALARMS,
CONTROL PANELS, AND OTHER DEVICES SHOWN ON
THE A/E PLANS. NFS DRAWINGS ARE TO SHOW ONLY
THE WIRING DIAGRAMS BETWEEN FIRE ALARM
DEVICES AND CONTROL PANELS. NFS IS NOT
RESPONSIBLE FOR THE INFORMATION SHOWN ON THE
A/E PLANS.

UNIVERSITY OF UTAH
FIELDHOUSE CHILLER PLANT
FLOORPLAN LEVELS 1 & 2
375 SOUTH 1400 EAST
SALT LAKE CITY, UT 84112
FIRE ALARM SYSTEM

NFS
NELSON FIRE SYSTEMS
801-468-8300

DRAWN BY:	BDT
DESIGNED BY:	XXXX
APPROVED BY:	DS
DATE:	12/18/2018
SCALE:	N.T.S.
PROJECT NO:	XXXX
REVISION NO:	XXXX
DRAWING NAME:	U OF U FH CHILLER PLANT.DWG

NELSON FIRE SYSTEMS
FLOORPLAN LEVEL 1 & 2
FINAL MAP

PAGE:

FM