



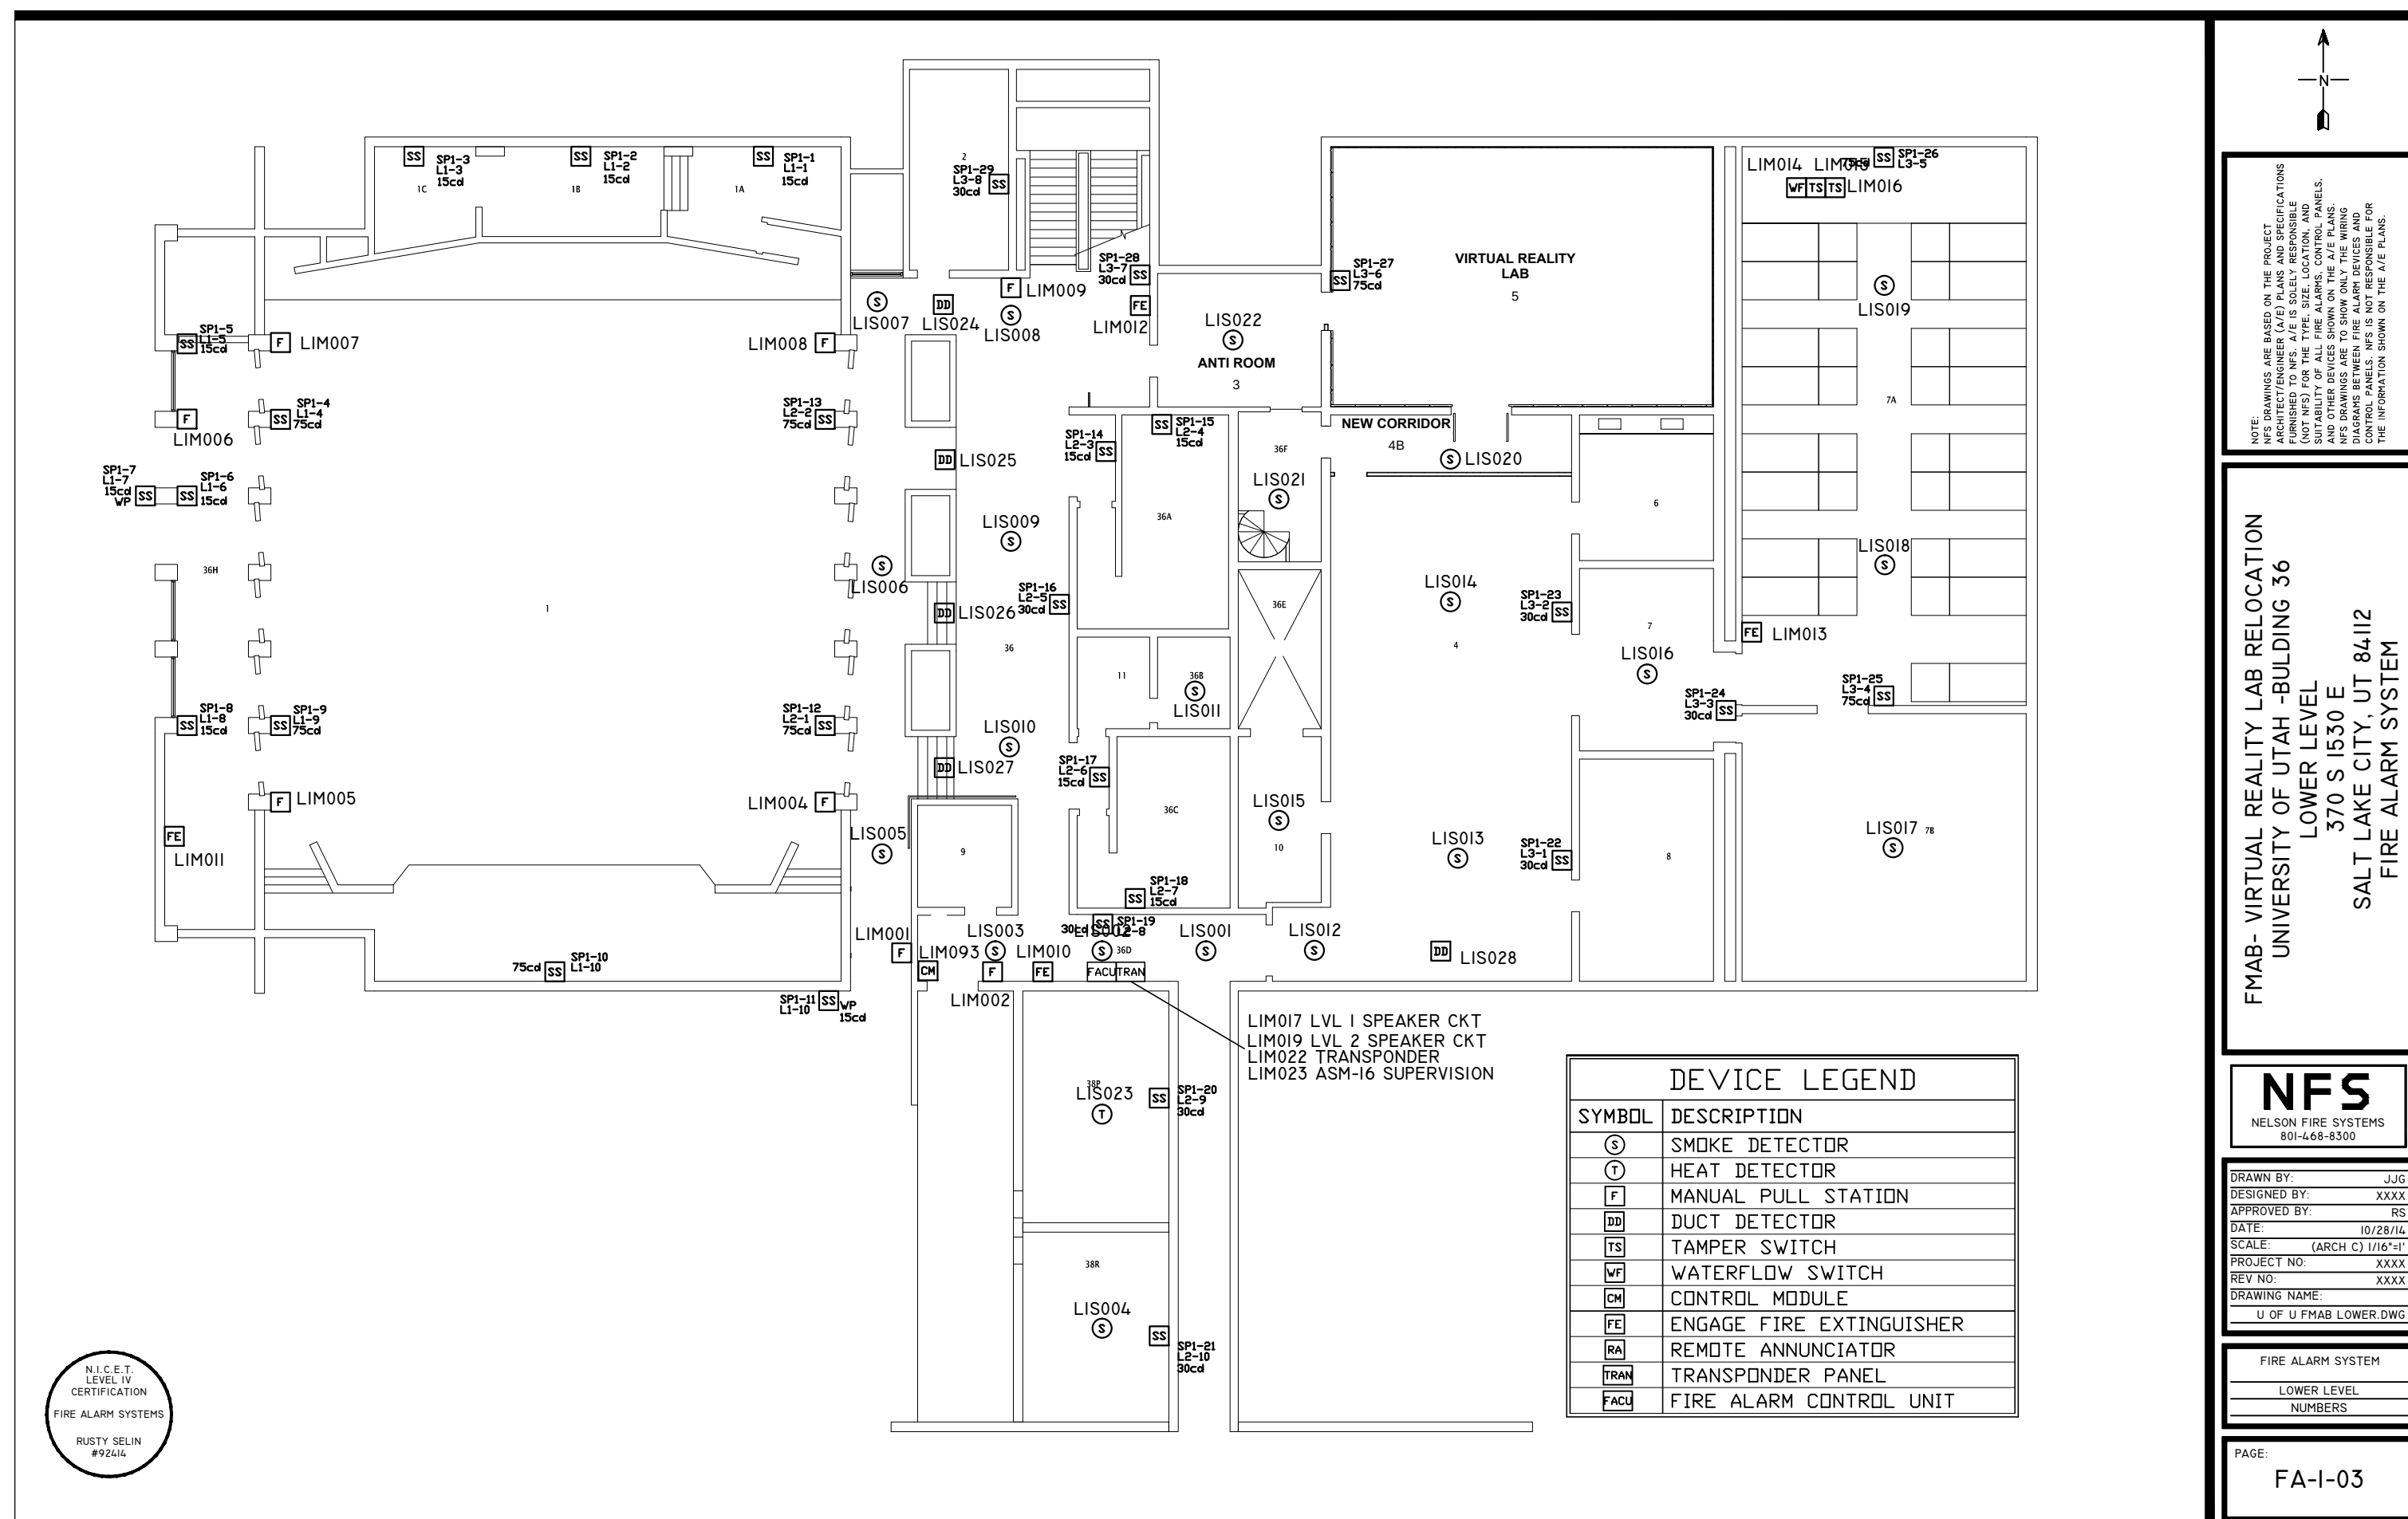

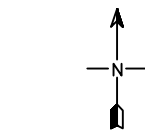

DEVICE LEGEND	
SYMBOL	DESCRIPTION
(S)	SMOKE DETECTOR
(T)	HEAT DETECTOR
(F)	MANUAL PULL STATION
(DD)	DUCT DETECTOR
(TS)	TAMPER SWITCH
(WF)	WATERFLOW SWITCH
(CM)	CONTROL MODULE
(FE)	ENGAGE FIRE EXTINGUISHER
(RA)	REMOTE ANNUNCIATOR
(TRAN)	TRANSPONDER PANEL
(FACU)	FIRE ALARM CONTROL UNIT



NOTES:
NFS DRAWINGS ARE BASED ON THE PROJECT ARCHITECT'S/ENGINEER'S (A/E) PLANS AND SPECIFICATIONS (NOT NFS) FOR THE TYPE, SIZE, LOCATION, AND OTHER INFORMATION. NFS IS NOT RESPONSIBLE FOR THE ACCURACY OF THE INFORMATION SHOWN ON THE A/E PLANS. NFS IS NOT RESPONSIBLE FOR THE INFORMATION SHOWN ON THE A/E PLANS.

FMAB- VIRTUAL REALITY LAB RELOCATION
UNIVERSITY OF UTAH - BUILDING 36
UPPER LEVEL
370 S 1530 E
SALT LAKE CITY, UT 84112
FIRE ALARM SYSTEM

NFS
NELSON FIRE SYSTEMS
801-468-8300

DRAWN BY: JJC
DESIGNED BY: XXXX
APPROVED BY: RS
DATE: 10/28/14
SCALE: (ARCH C) 1/16"=1'
PROJECT NO: XXXX
REV NO: XXXX
DRAWING NAME:
U OF U FMAB UPPER DWG

FIRE ALARM SYSTEM
UPPER LEVEL
NUMBERS

PAGE:
FA-2-03

