



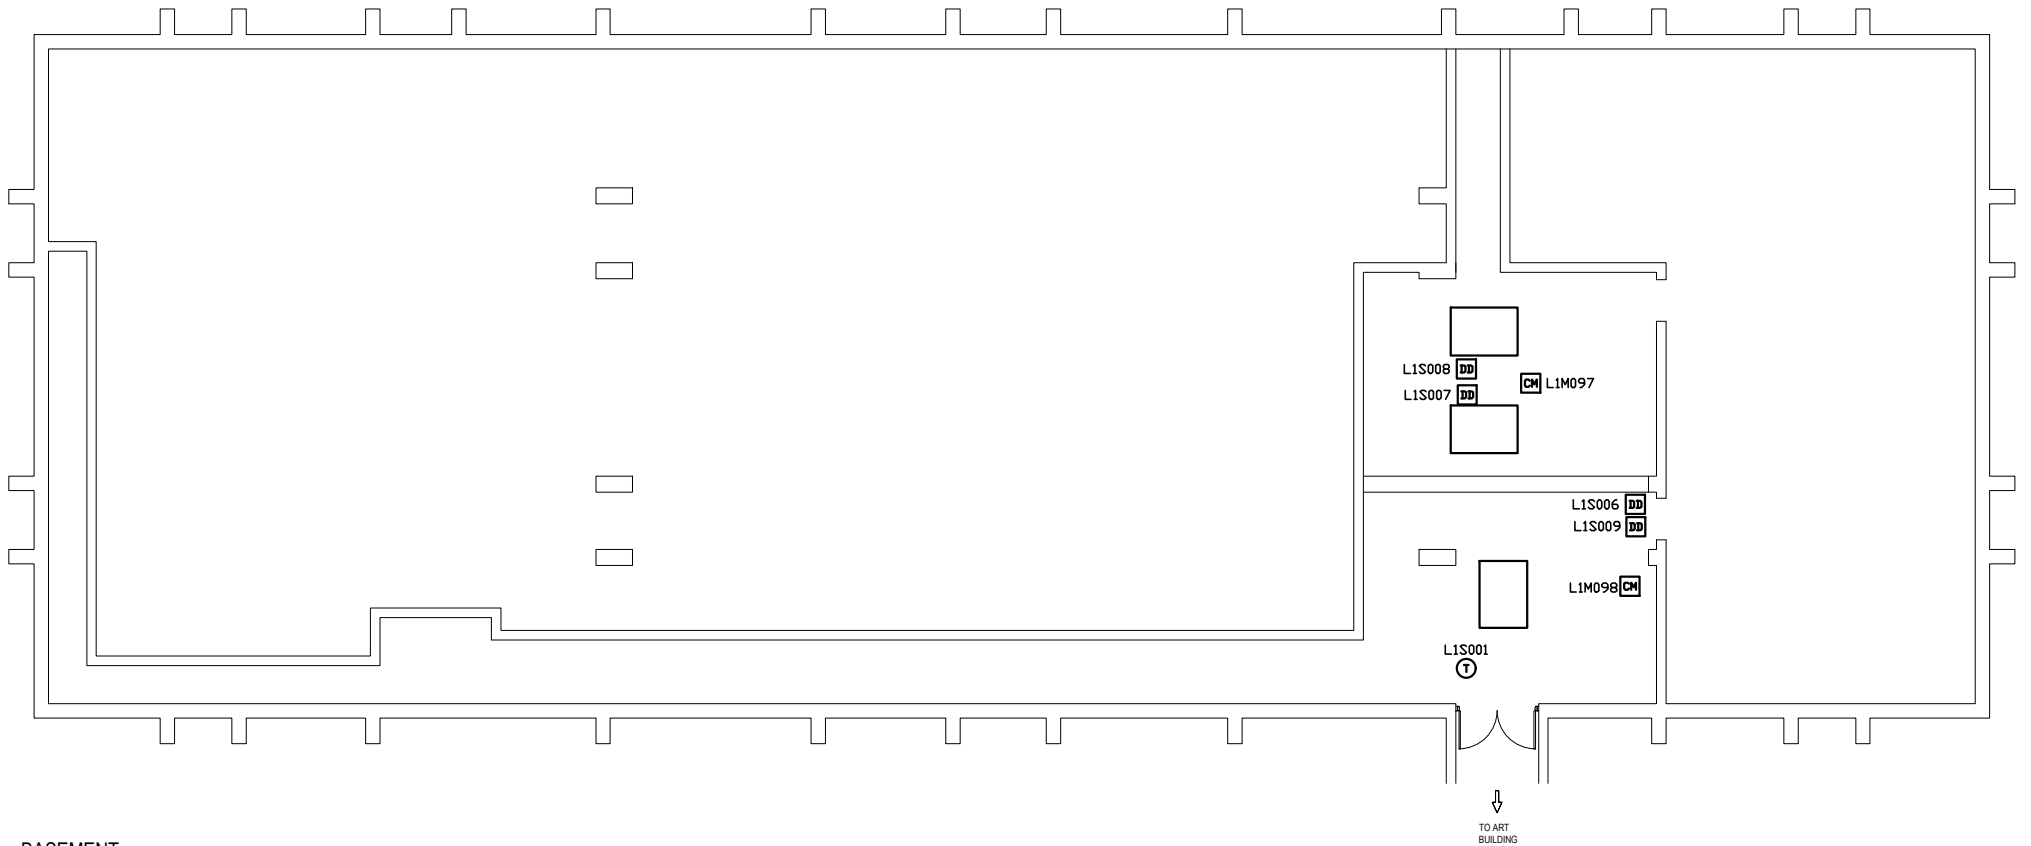


BASEMENT

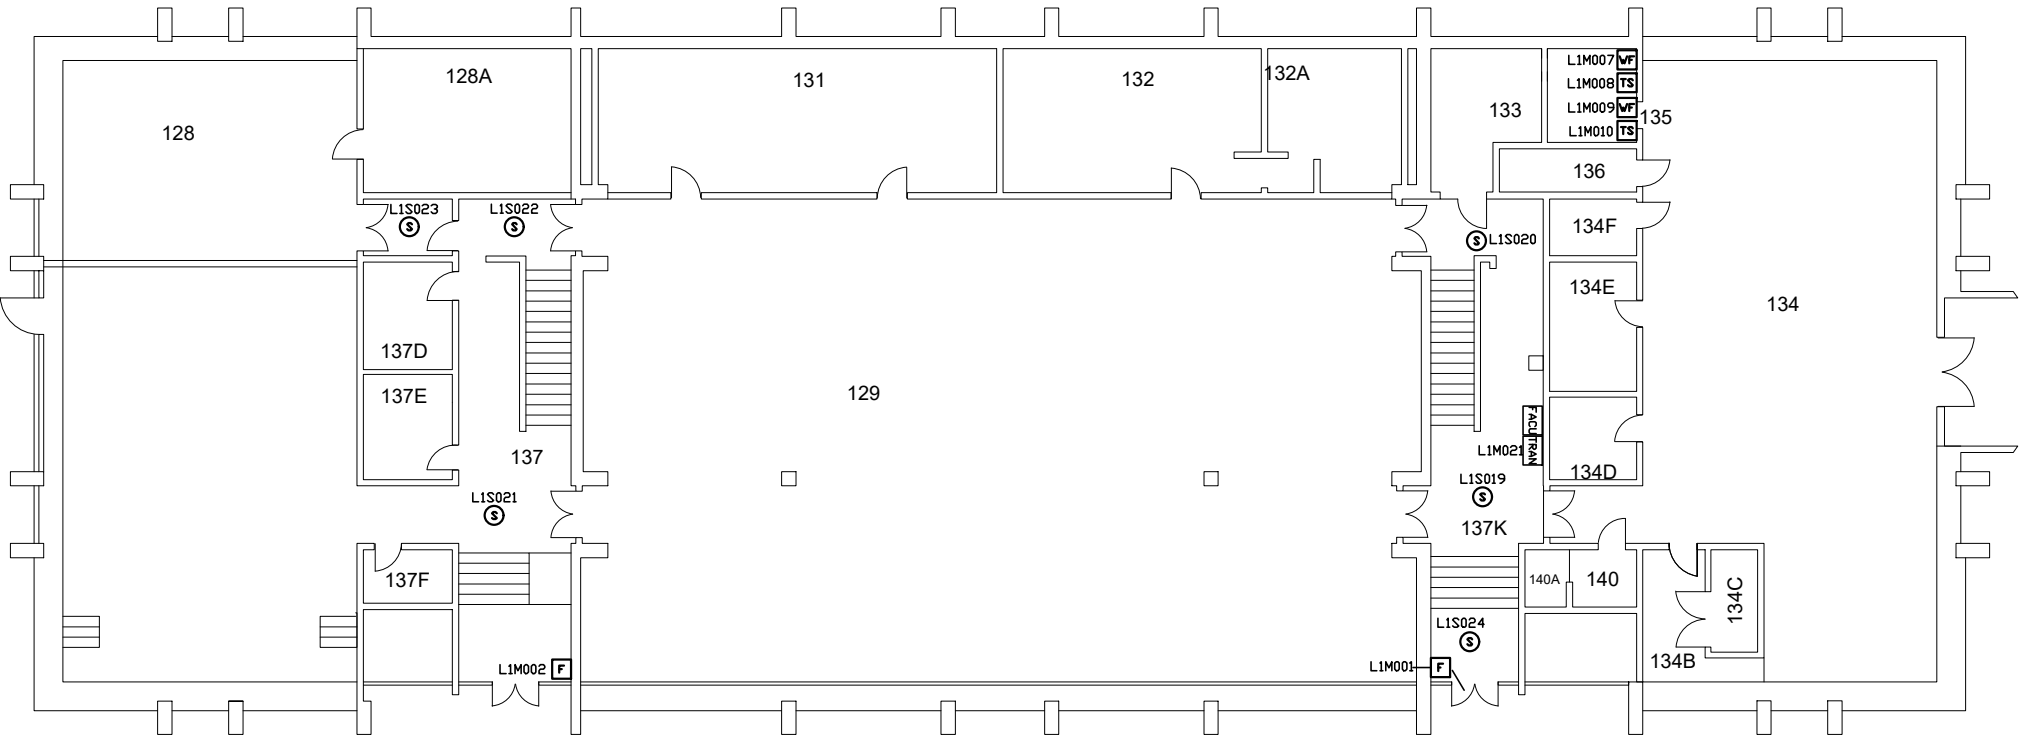

LEVEL 1

DEVICE LEGEND	
SYMBOL	DESCRIPTION
Ⓢ	SMOKE DETECTOR
Ⓣ	HEAT DETECTOR
ⓕ	MANUAL PULL STATION
ⓓⓓ	DUCT DETECTOR
ⓉⓈ	TAMPER SWITCH
Ⓦⓕ	WATERFLOW SWITCH
ⓂⓂ	MONITOR MODULE
ⓐⓂ	CONTROL MODULE
ⓉⓇⓐⓃ	TRANSPONDER PANEL
ⓕⓐⓐⓐ	FIRE ALARM CONTROL UNIT

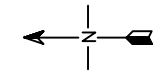

NOTE:
NFS DRAWINGS ARE BASED ON THE PROJECT
ARCHITECT/ENGINEER (A/E) PLANS AND SPECIFICATIONS
FURNISHED TO NFS. A/E IS SOLELY RESPONSIBLE
(NOT NFS) FOR THE TYPE, SIZE, LOCATION, AND
SUITABILITY OF ALL FIRE ALARMS, CONTROL PANELS,
AND OTHER DEVICES SHOWN ON THE A/E PLANS.
NFS DRAWINGS ARE TO SHOW ONLY THE WIRING
DIAGRAMS BETWEEN FIRE ALARM DEVICES AND
CONTROL PANELS. NFS IS NOT RESPONSIBLE FOR
THE INFORMATION SHOWN ON THE A/E PLANS.

UNIVERSITY OF UTAH
ARCHITECTURE BUILDING
BASEMENT & LEVEL 1
SALT LAKE CITY, UTAH
FIRE ALARM SYSTEM


NFS
NELSON FIRE SYSTEMS
801-468-8300

DRAWN BY: AK
DESIGNED BY: XXXX
APPROVED BY: DS
DATE: 1/11/2016
SCALE: (ARCH C) 1/16"=1'
PROJECT NO: XXXX
REV NO: XXXX
DRAWING NAME:
UoFU 1 ARCH BLDG .DWG


FIRE ALARM SYSTEM
BASEMENT & LEVEL 1
FINAL MAP

PAGE:
FA-I



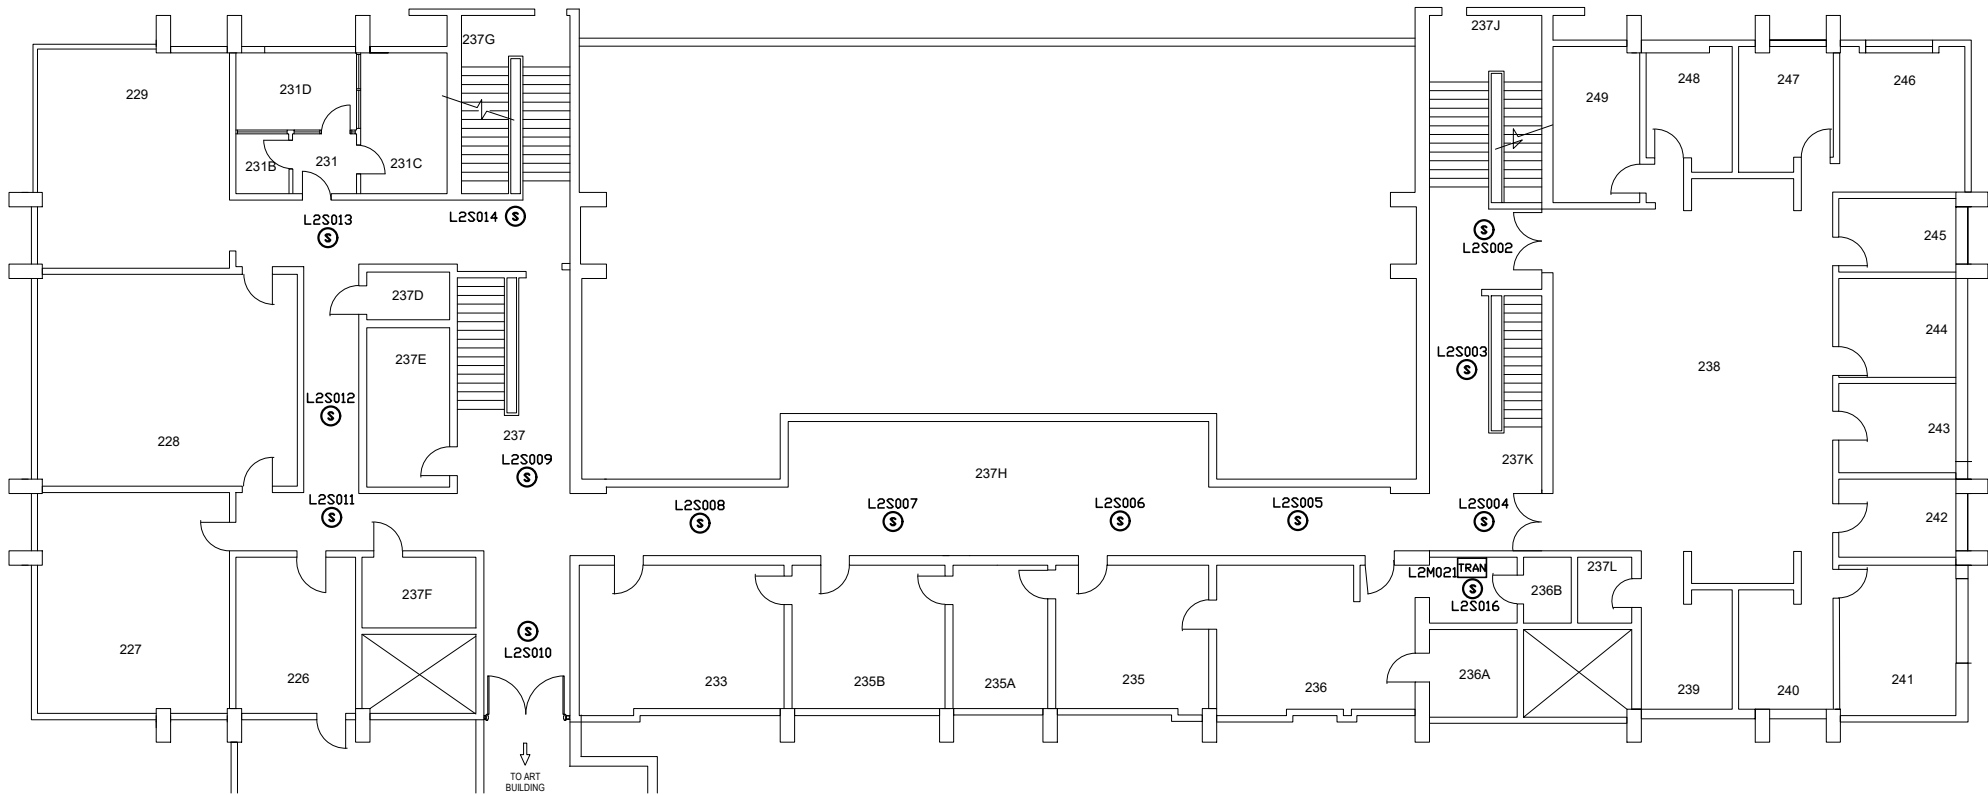


LEVEL 2

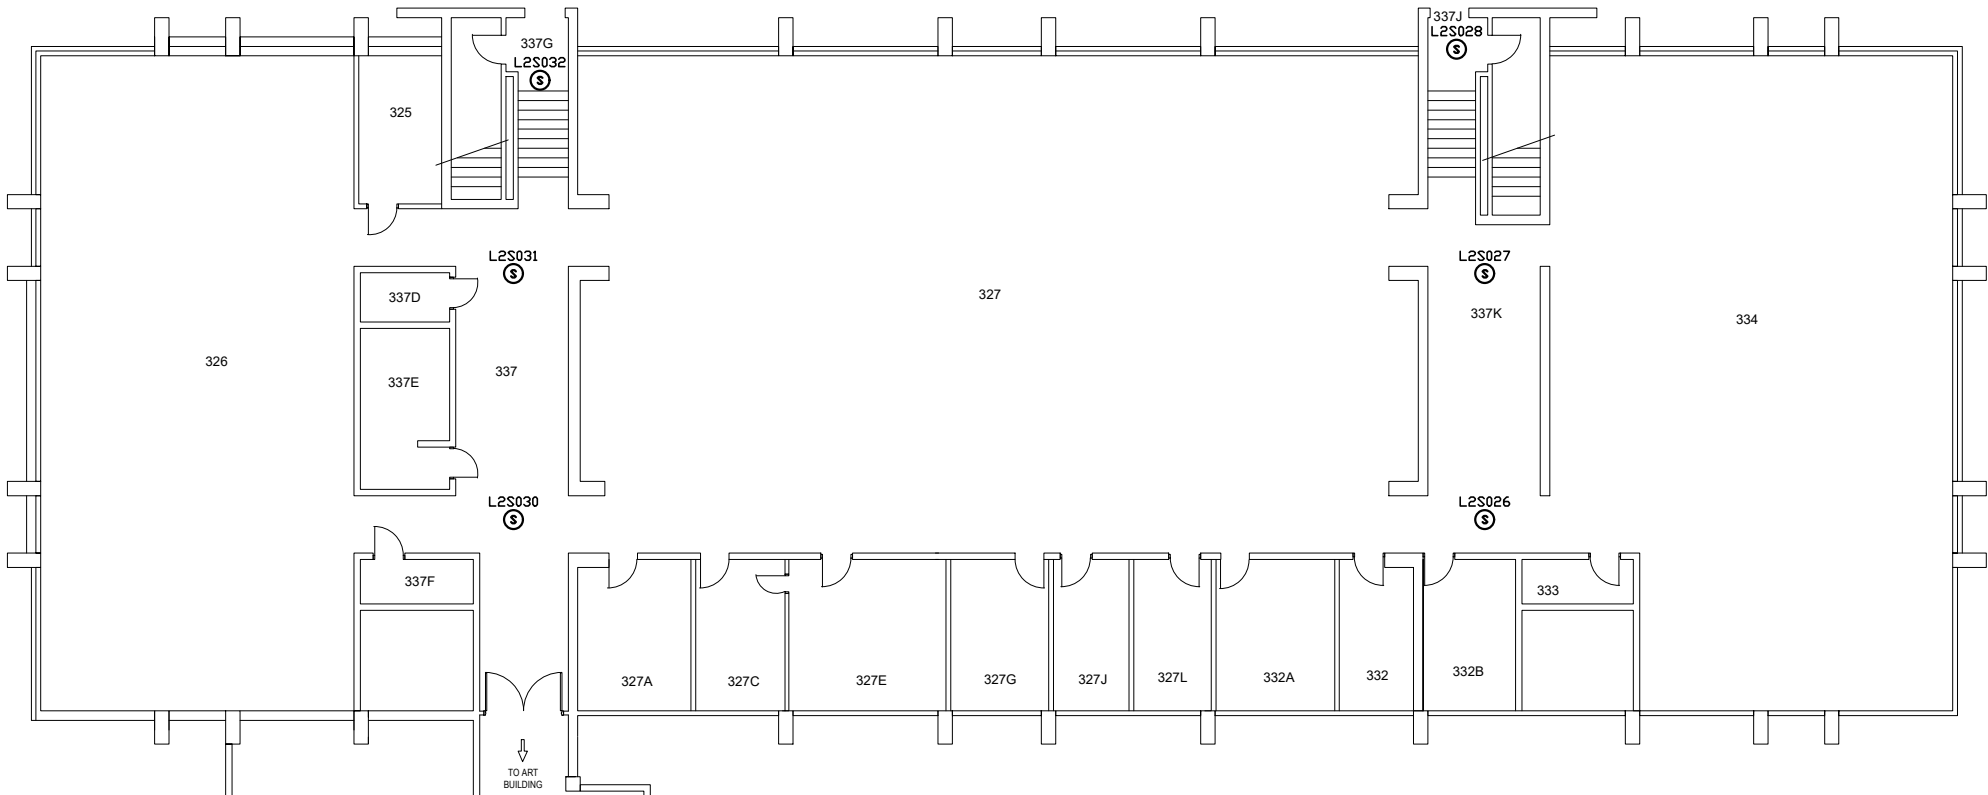

LEVEL 3

DEVICE LEGEND	
SYMBOL	DESCRIPTION
Ⓢ	SMOKE DETECTOR
Ⓣ	HEAT DETECTOR
ⓕ	MANUAL PULL STATION
ⓓⓓ	DUCT DETECTOR
ⓉⓈ	TAMPER SWITCH
Ⓦⓕ	WATERFLOW SWITCH
ⓂⓂ	MONITOR MODULE
ⓐⓂ	CONTROL MODULE
ⓉⓗⓃ	TRANSPONDER PANEL
ⓕⓐⓐ	FIRE ALARM CONTROL UNIT

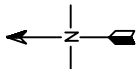

NOTE:
NFS DRAWINGS ARE BASED ON THE PROJECT
ARCHITECT/ENGINEER (A/E) PLANS AND SPECIFICATIONS
FURNISHED TO NFS. A/E IS SOLELY RESPONSIBLE
(NOT NFS) FOR THE TYPE, SIZE, LOCATION, AND
SUITABILITY OF ALL FIRE ALARMS, CONTROL PANELS,
AND OTHER DEVICES SHOWN ON THE A/E PLANS.
NFS DRAWINGS ARE TO SHOW ONLY THE WIRING
DIAGRAMS BETWEEN FIRE ALARM DEVICES AND
CONTROL PANELS. NFS IS NOT RESPONSIBLE FOR
THE INFORMATION SHOWN ON THE A/E PLANS.

UNIVERSITY OF UTAH
ARCHITECTURE BUILDING
LEVELS 2 & 3
SALT LAKE CITY, UTAH
FIRE ALARM SYSTEM

NFS
NELSON FIRE SYSTEMS
801-468-8300

DRAWN BY: AK
DESIGNED BY: XXXX
APPROVED BY: DS
DATE: 8/20/15
SCALE: (ARCH C) 1/16"=1'
PROJECT NO: XXXX
REV NO: XXXX
DRAWING NAME:
UoFU | ARCH BLDG .DWG

FIRE ALARM SYSTEM
LEVELS 2 & 3
FINAL MAP

PAGE:
FA-2

