



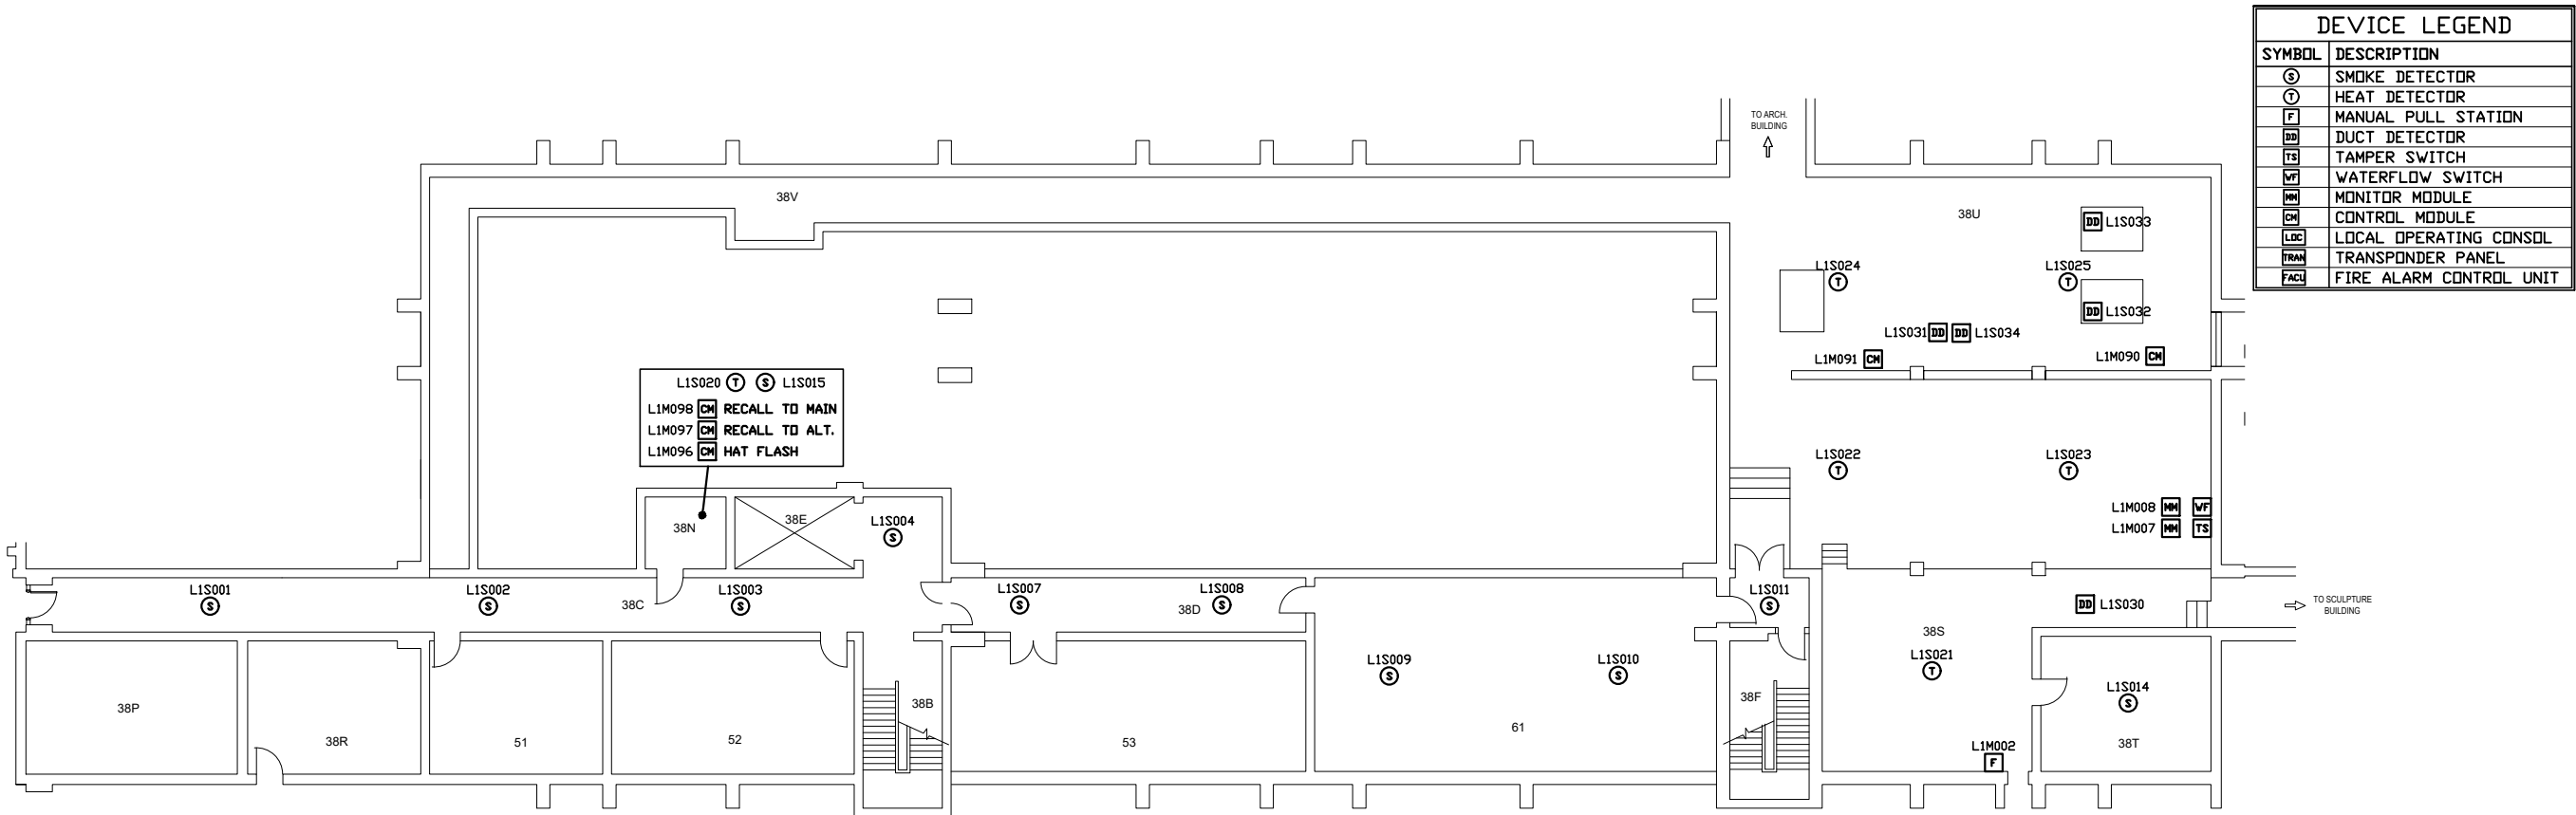

BASEMENT

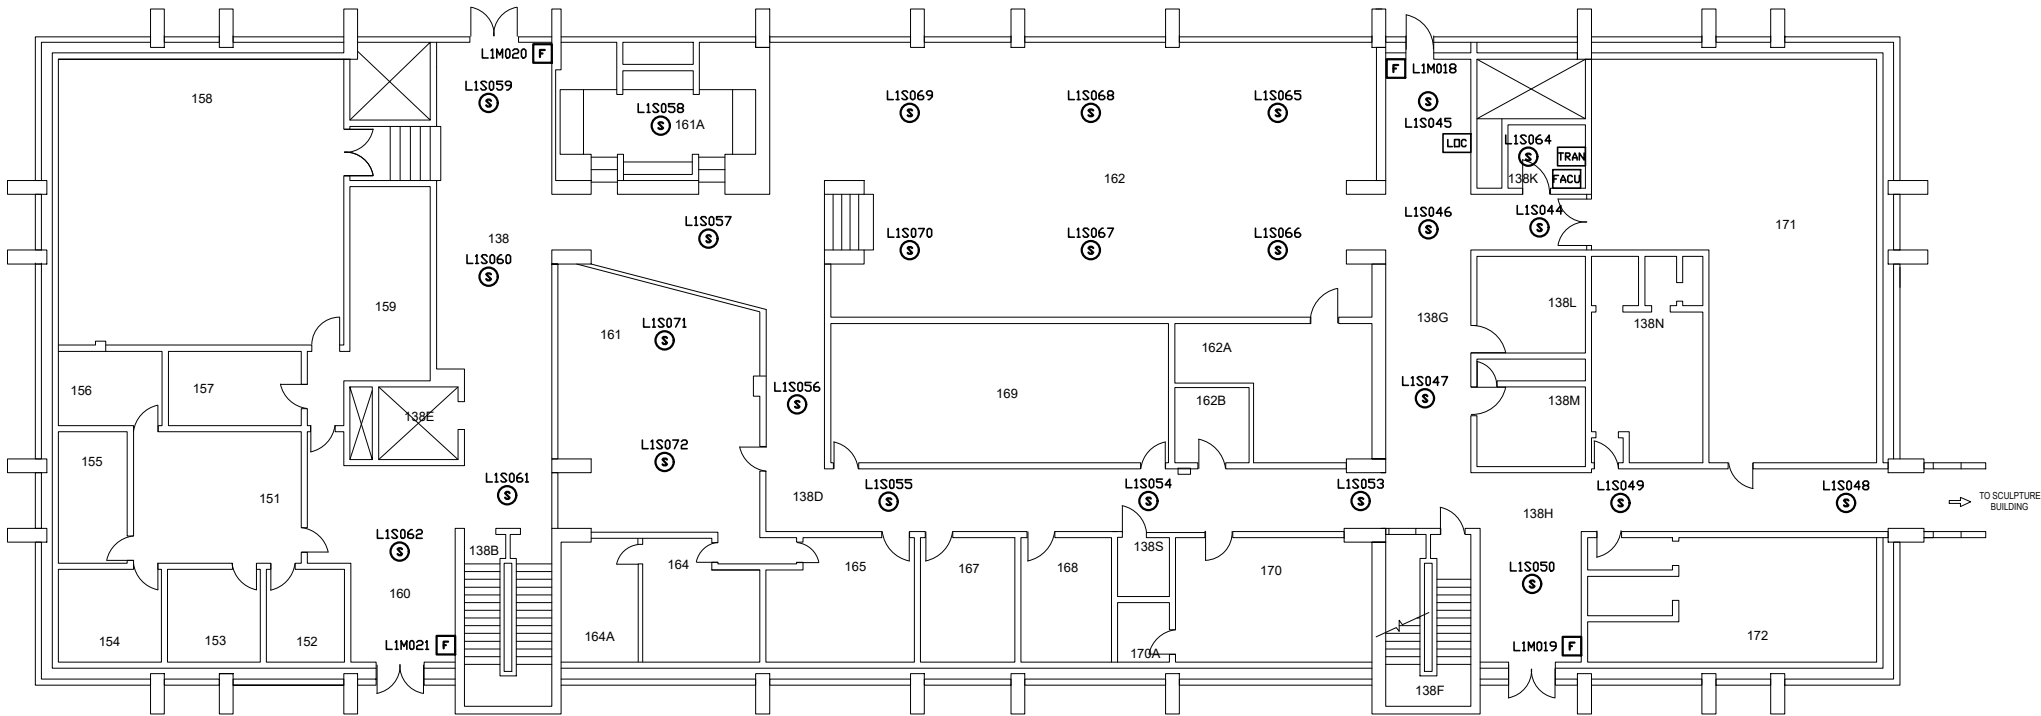

LEVEL 1




UNIVERSITY OF UTAH
ART BUILDING
BASEMENT & LEVEL I
SALT LAKE CITY, UTAH
FIRE ALARM SYSTEM

NFS
NELSON FIRE SYSTEMS
801-468-8300

DRAWN BY: AK
DESIGNED BY: XXXX
APPROVED BY: DS
DATE: 9/8/15
SCALE: (ARCH C) 1/16"=1'
PROJECT NO: XXXX
REV NO: XXXX
DRAWING NAME:
UofU 3 ART BLDG FM.DWG

FIRE ALARM SYSTEM
BASEMENT & LEVEL I
FINAL MAPS

PAGE:
FA-I

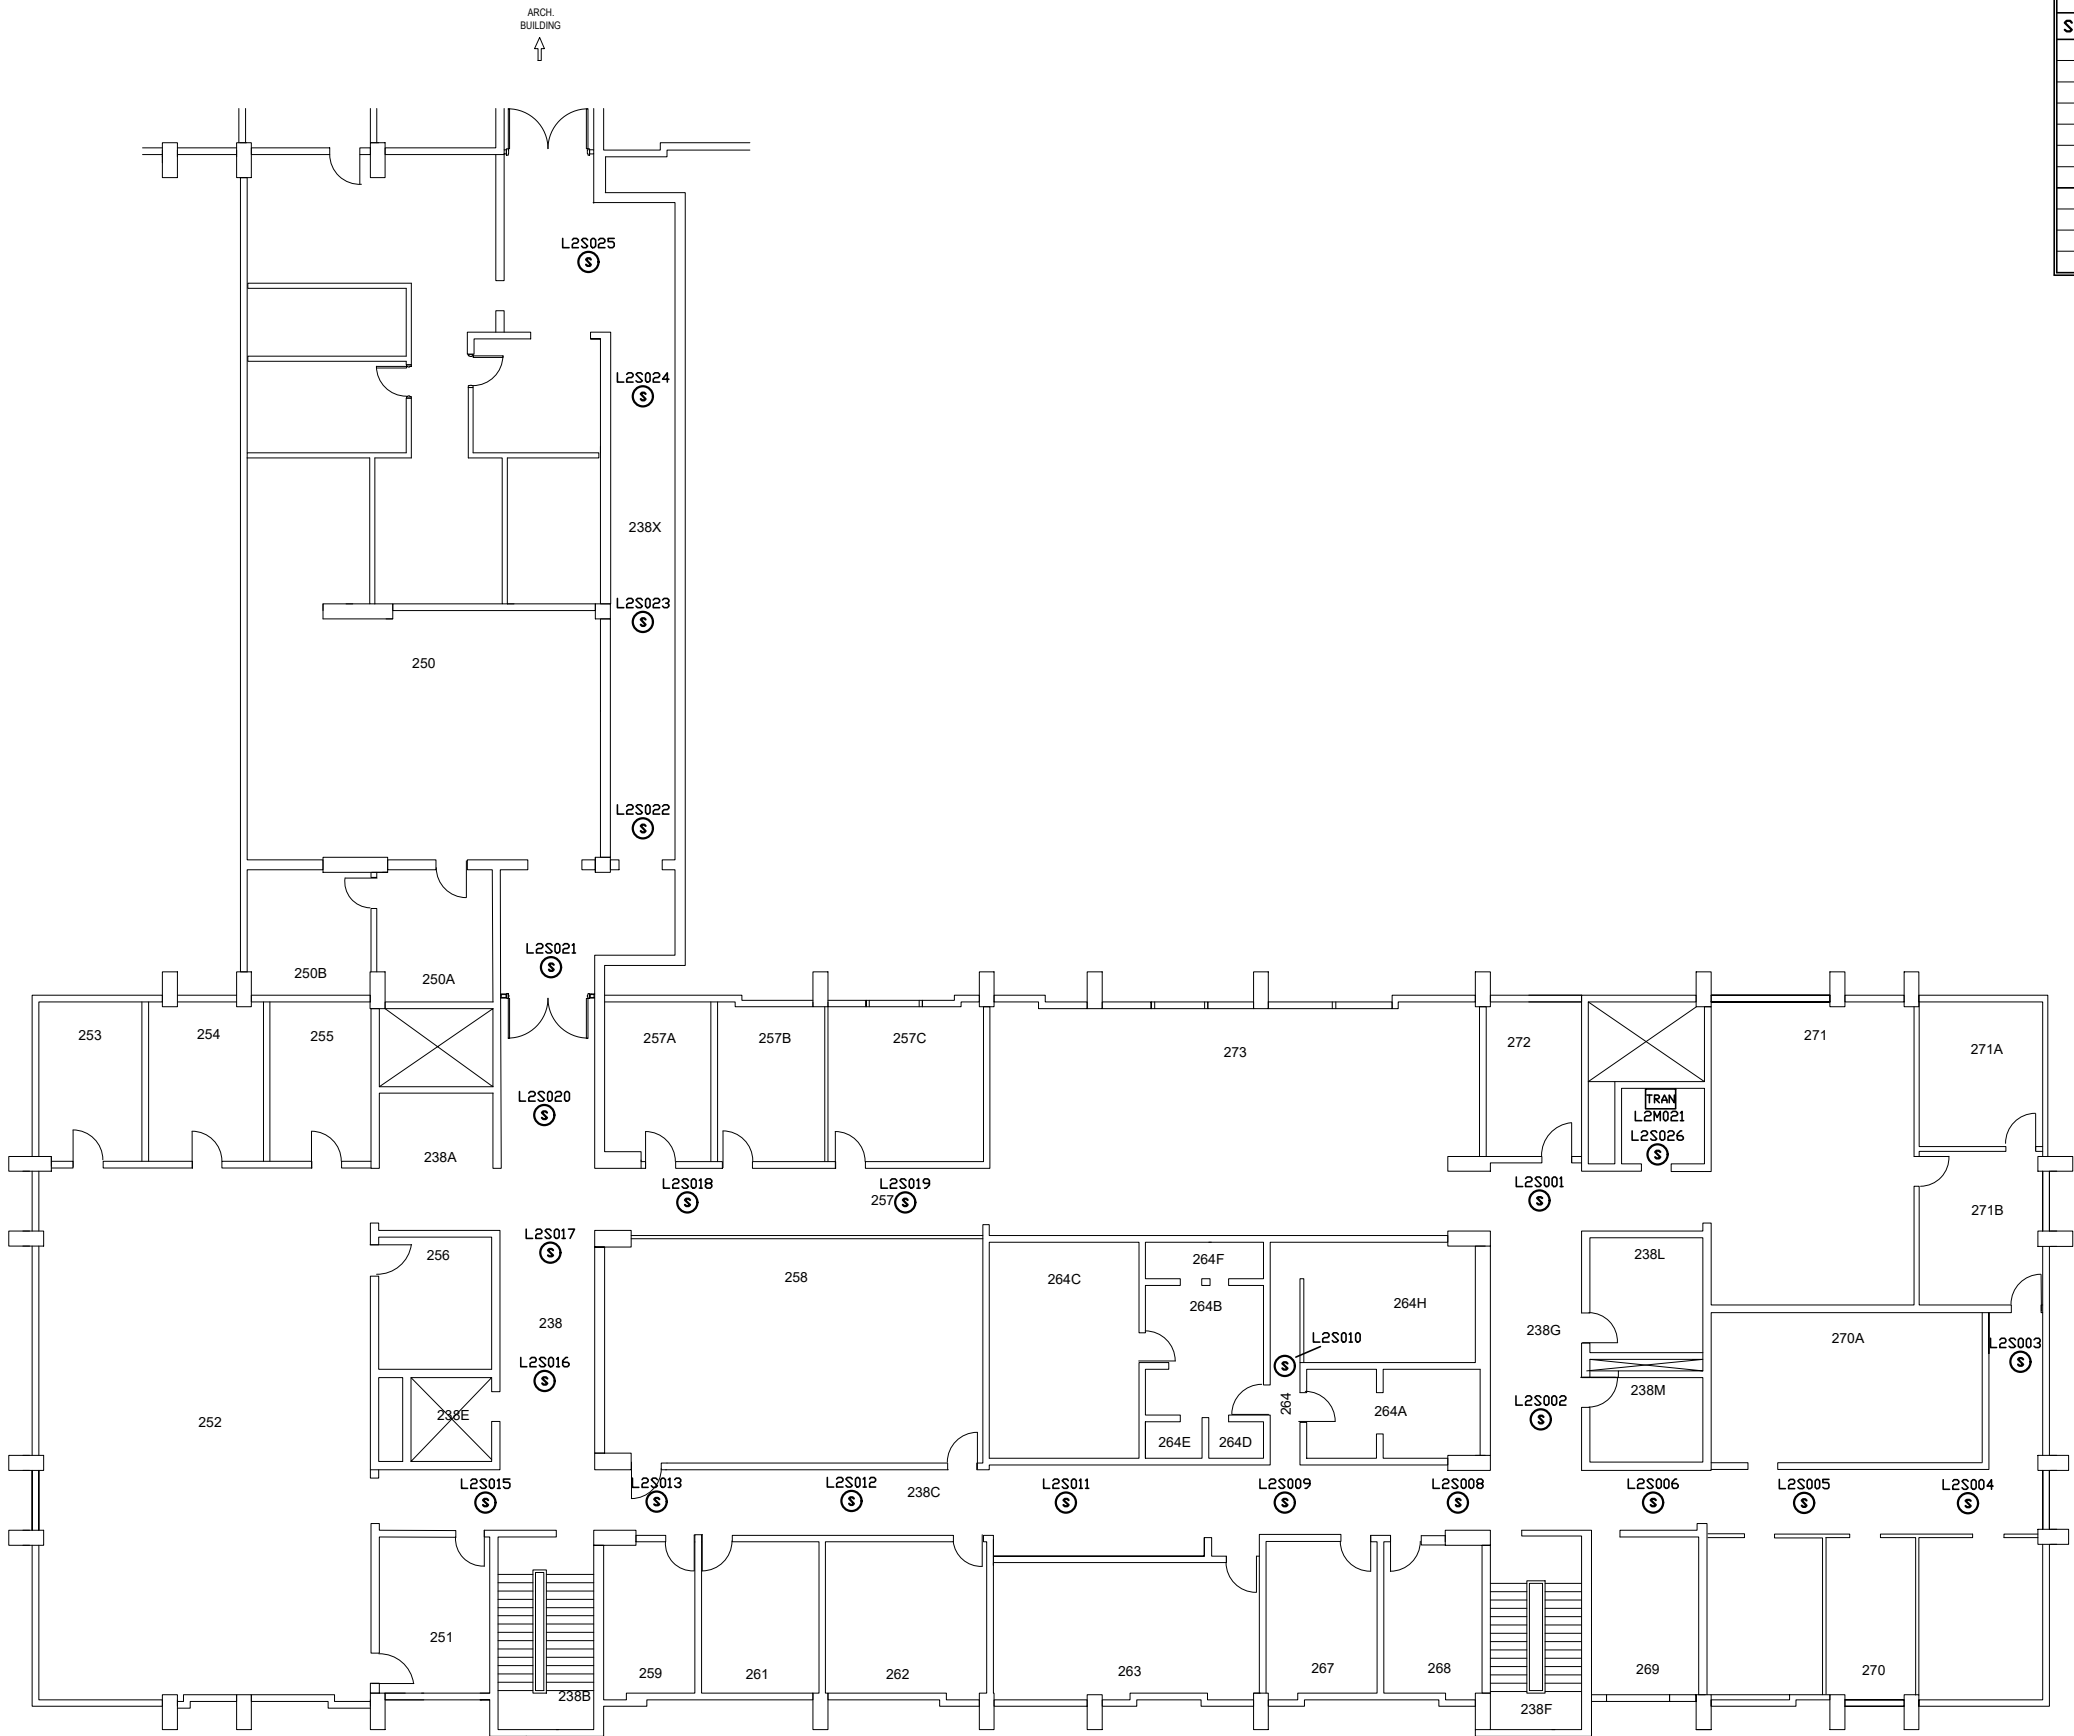

LEVEL 2

DEVICE LEGEND	
SYMBOL	DESCRIPTION
	SMOKE DETECTOR
	HEAT DETECTOR
	MANUAL PULL STATION
	DUCT DETECTOR
	TAMPER SWITCH
	WATERFLOW SWITCH
	MONITOR MODULE
	CONTROL MODULE
	LOCAL OPERATING CONSOL
	TRANSPONDER PANEL
	FIRE ALARM CONTROL UNIT

UNIVERSITY OF UTAH
ART BUILDING
LEVEL 2
SALT LAKE CITY, UTAH
FIRE ALARM SYSTEM


NFS
NELSON FIRE SYSTEMS
801-468-8300

DRAWN BY: AK
DESIGNED BY: XXXX
APPROVED BY: DS
DATE: 9/8/15
SCALE: (ARCH C) 1/16"=1'
PROJECT NO: XXXX
REV NO: XXXX
DRAWING NAME:
UofU 3 ART BLDG FM.DWG

FIRE ALARM SYSTEM
LEVEL 2
FINAL MAPS

PAGE:
FA-2



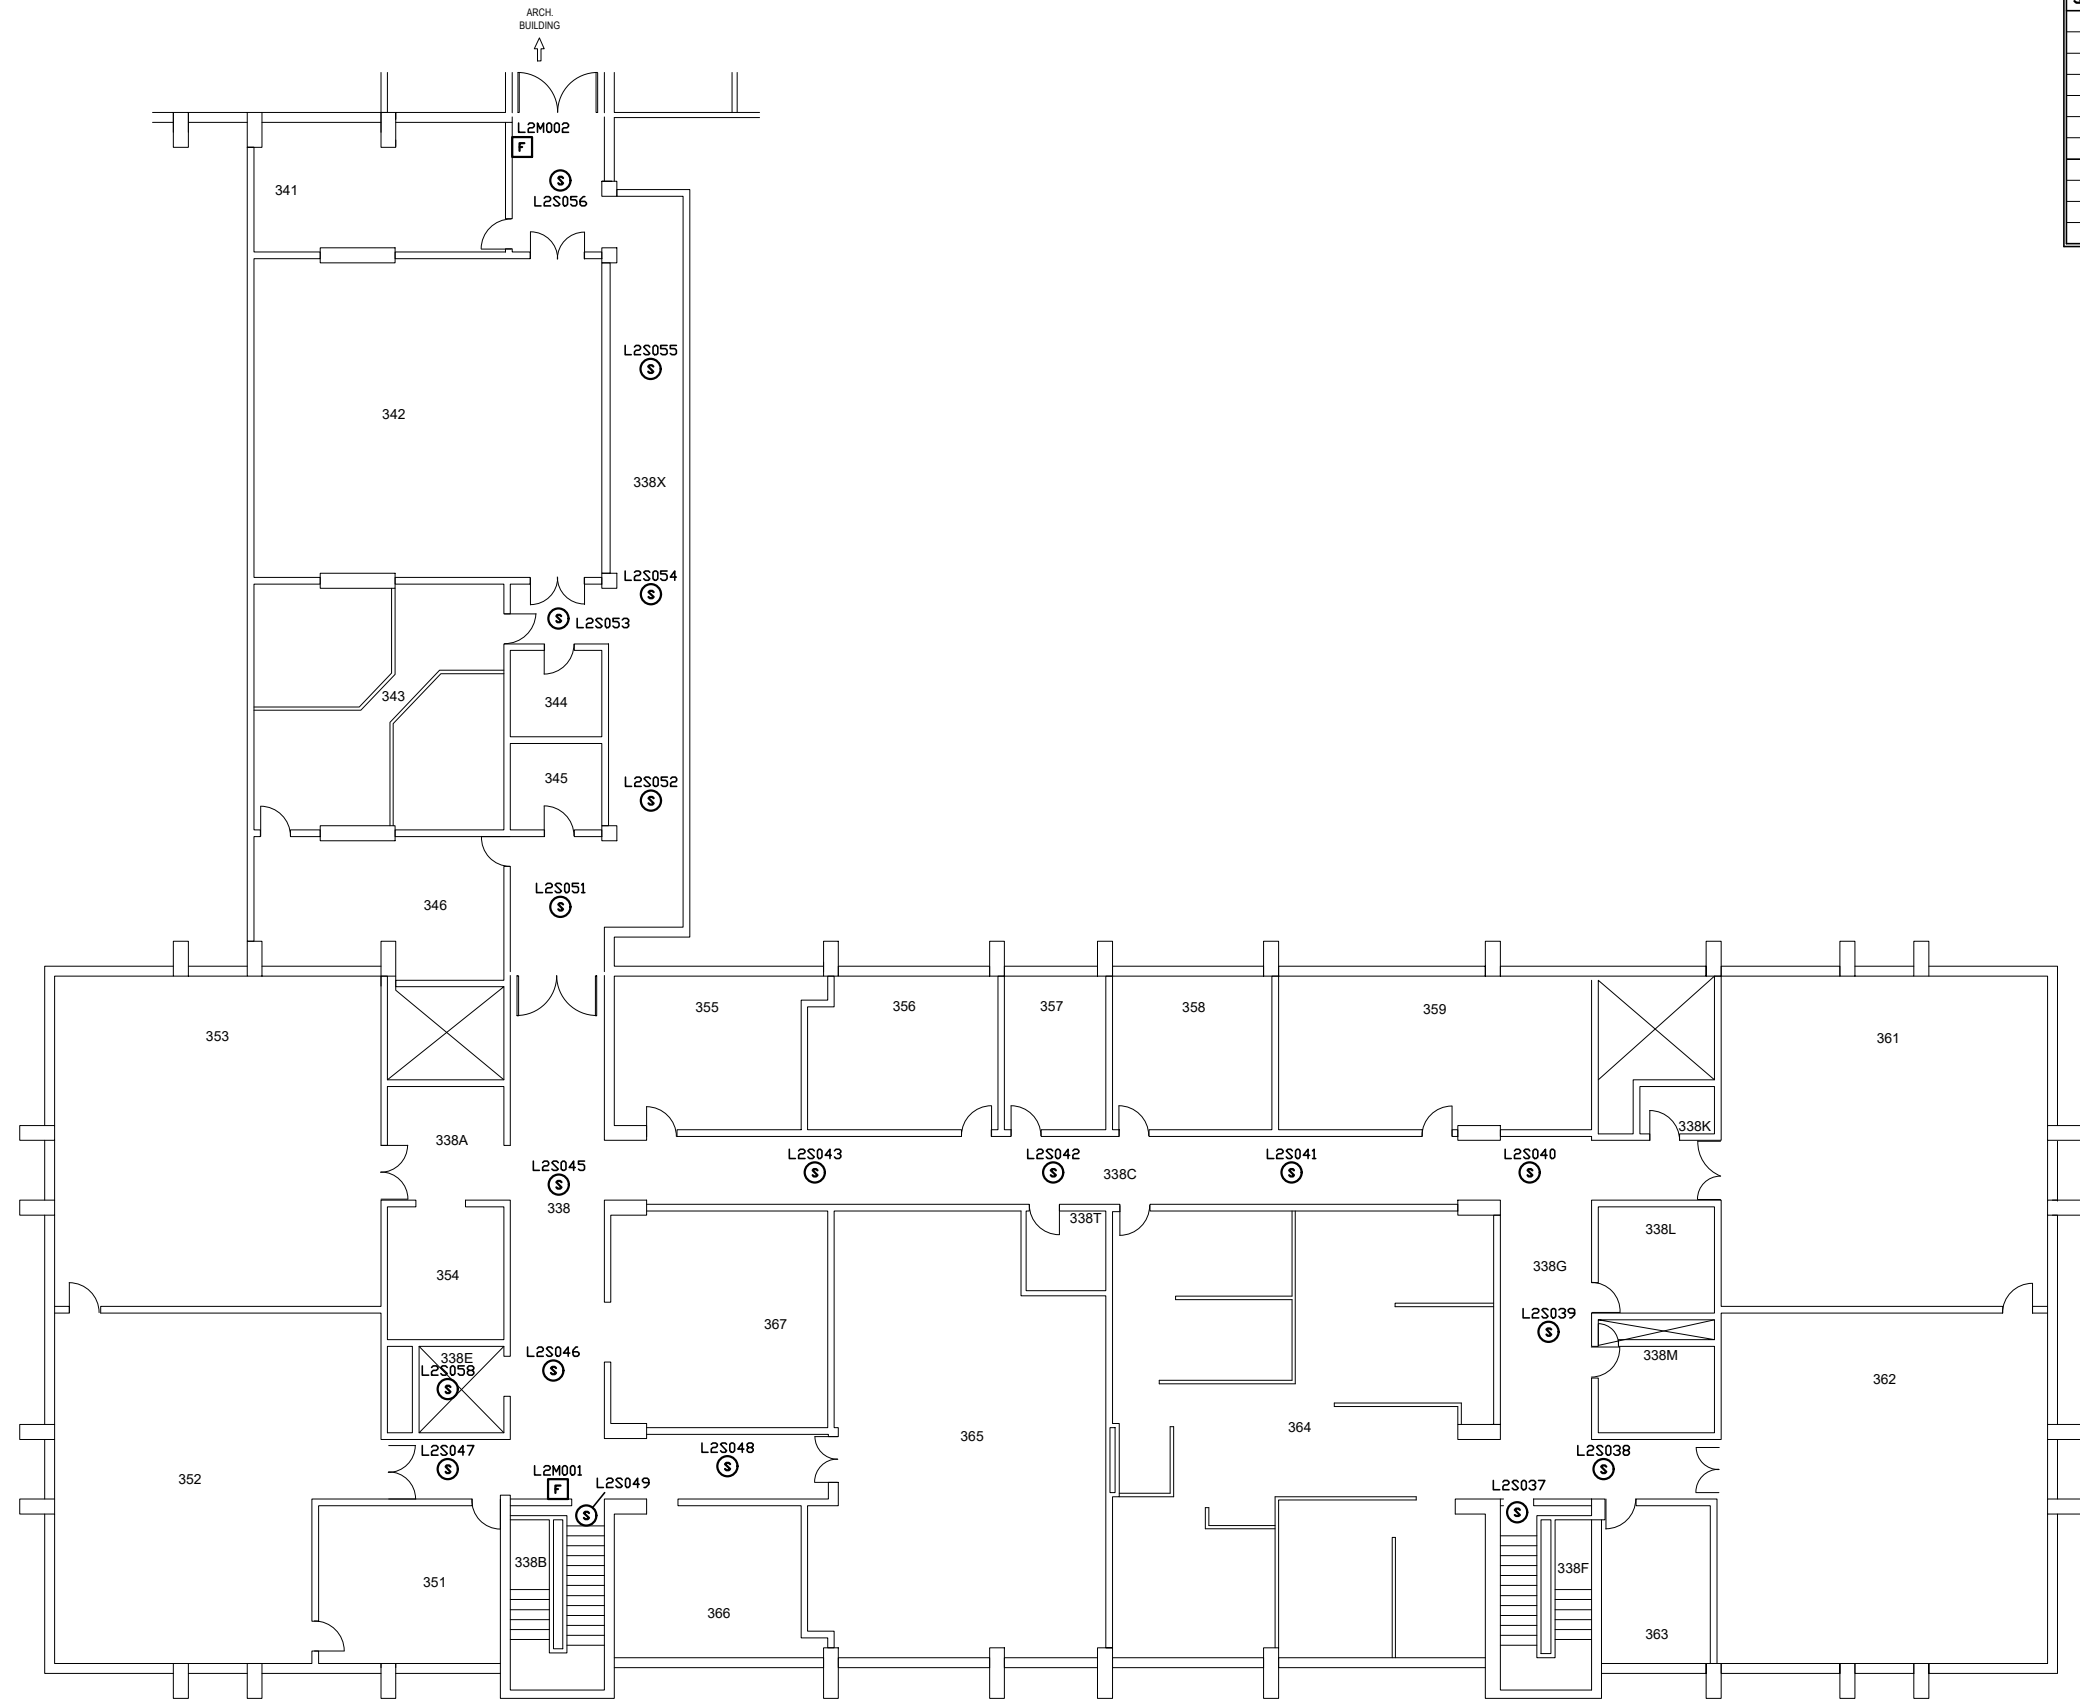

LEVEL 3

DEVICE LEGEND	
SYMBOL	DESCRIPTION
(S)	SMOKE DETECTOR
(T)	HEAT DETECTOR
(F)	MANUAL PULL STATION
(DD)	DUCT DETECTOR
(TS)	TAMPER SWITCH
(WF)	WATERFLOW SWITCH
(MM)	MONITOR MODULE
(CM)	CONTROL MODULE
(LOC)	LOCAL OPERATING CONSOL
(TRAN)	TRANSPONDER PANEL
(FACU)	FIRE ALARM CONTROL UNIT

UNIVERSITY OF UTAH
ART BUILDING
LEVEL 3
SALT LAKE CITY, UTAH
FIRE ALARM SYSTEM

NFS
NELSON FIRE SYSTEMS
801-468-8300

DRAWN BY: AK
DESIGNED BY: XXXX
APPROVED BY: DS
DATE: 9/8/15
SCALE: (ARCH C) 1/16"=1'
PROJECT NO: XXXX
REV NO: XXXX
DRAWING NAME:
UoFU 3 ART BLDG FM.DWG

FIRE ALARM SYSTEM
LEVEL 3
FINAL MAPS

PAGE:
FA-3

