



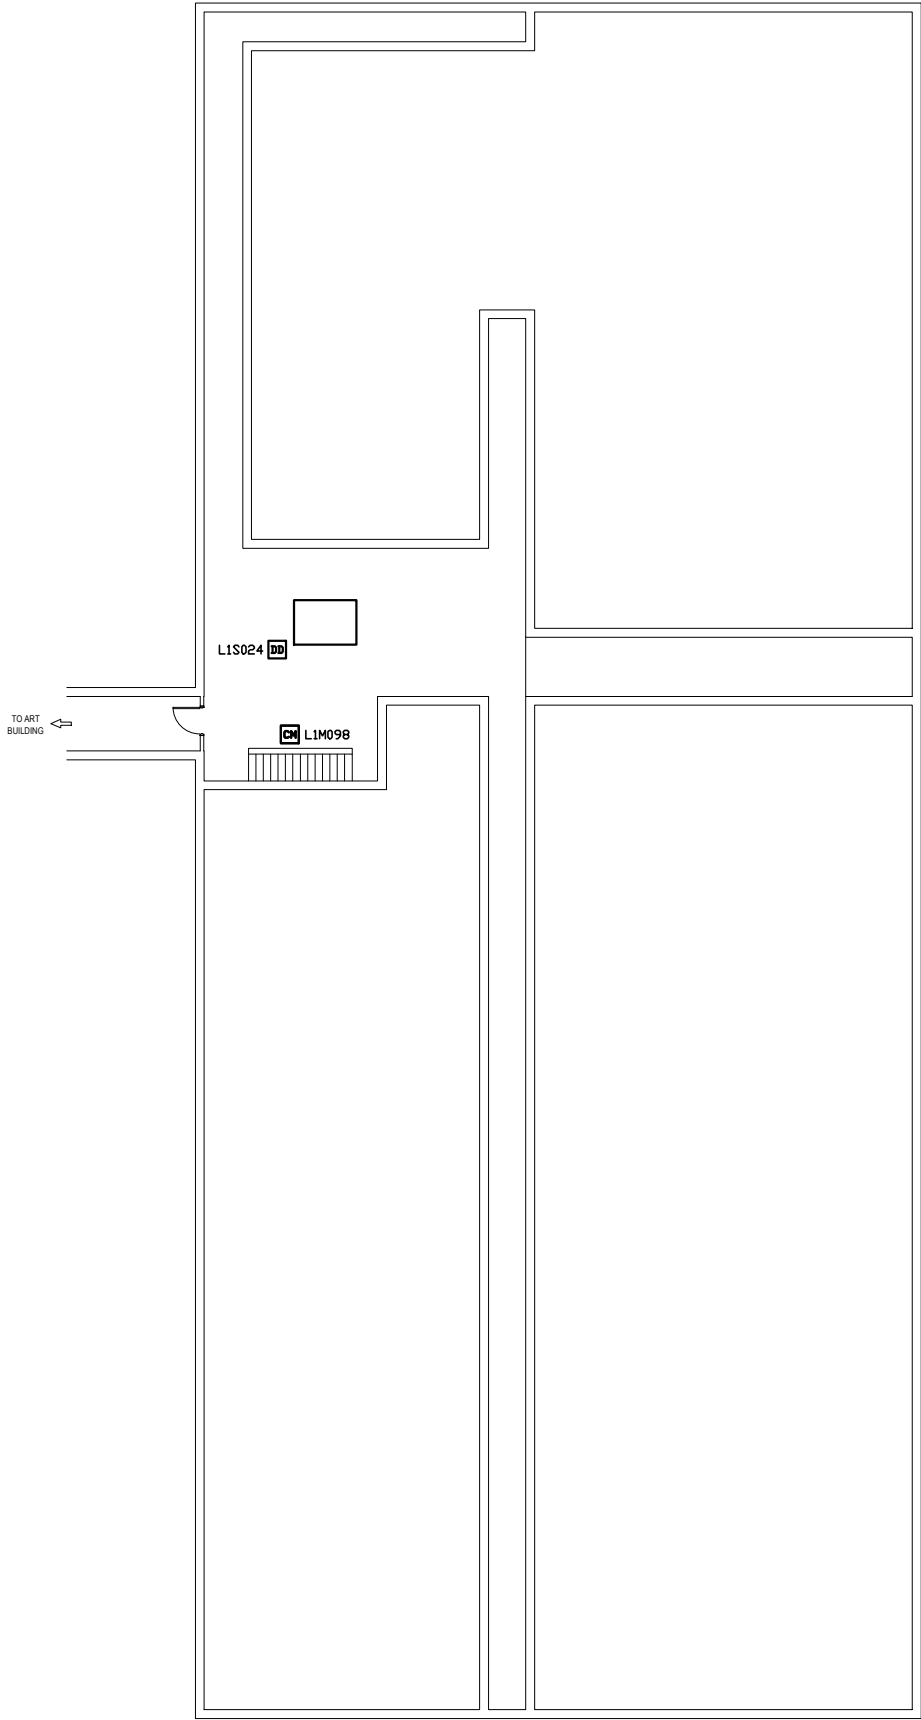


BASEMENT

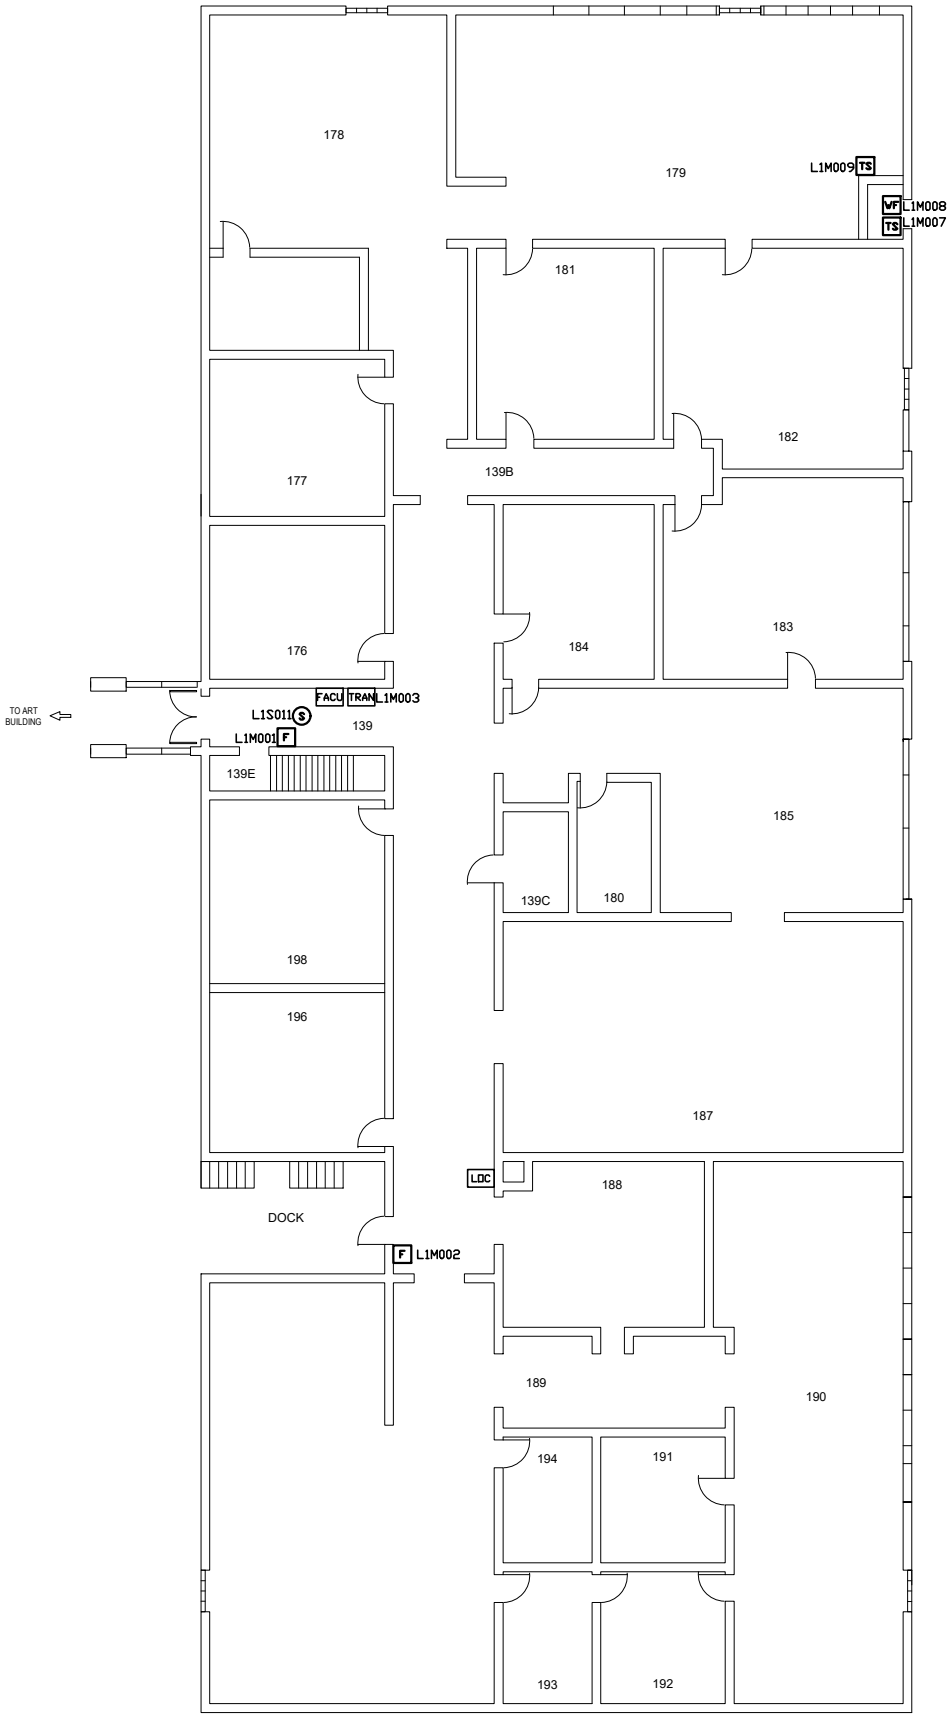

LEVEL 1

DEVICE LEGEND	
SYMBOL	DESCRIPTION
Ⓢ	SMOKE DETECTOR
Ⓣ	HEAT DETECTOR
F	MANUAL PULL STATION
DD	DUCT DETECTOR
TS	TAMPER SWITCH
WF	WATERFLOW SWITCH
MM	MONITOR MODULE
CM	CONTROL MODULE
TRAN	TRANSPONDER PANEL
FACU	FIRE ALARM CONTROL UNIT

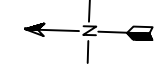

NOTE:
NFS DRAWINGS ARE BASED ON THE PROJECT
ARCHITECT/ENGINEER (A/E) PLANS AND SPECIFICATIONS
FURNISHED TO NFS. A/E IS SOLELY RESPONSIBLE
(NOT NFS) FOR THE TYPE, SIZE, LOCATION, AND
SUITABILITY OF ALL FIRE ALARMS, CONTROL PANELS,
AND OTHER DEVICES SHOWN ON THE A/E PLANS.
NFS DRAWINGS ARE TO SHOW ONLY THE WIRING
DIAGRAMS BETWEEN FIRE ALARM DEVICES AND
CONTROL PANELS. NFS IS NOT RESPONSIBLE FOR
THE INFORMATION SHOWN ON THE A/E PLANS.

UNIVERSITY OF UTAH
SCULPTURE BUILDING BUILDING
BASEMENT & LEVEL I
SALT LAKE CITY, UTAH
FIRE ALARM SYSTEM



DRAWN BY:	AK
DESIGNED BY:	XXXX
APPROVED BY:	DS
DATE:	1/11/2016
SCALE:	(ARCH C) 1/16"=1'
PROJECT NO:	XXXX
REV NO:	XXXX
DRAWING NAME:	UofU 6 ART BLDG .DWG

FIRE ALARM SYSTEM
BASEMENT & LEVEL I
FINAL MAP