


DEVICE LEGEND	
SYMBOL	DESCRIPTION
③	SMOKE DETECTOR
①	THERMAL DETECTOR
F	MANUAL PULL STATION
DD	DUCT SMOKE DETECTOR
WF	WATERFLOW SWITCH MONITOR MODULE
TS	TAMPER SWITCH MONITOR MODULE
MM	MONITOR MODULE
CM	CONTROL MODULE
FACP	FIRE ALARM CONTROL PANEL
TRAN	TRANSPONDER PANEL

ADDRESSABLE LOOP NUMBER
SENSOR ("M" MONITOR)
DEVICE NUMBER

L1S001

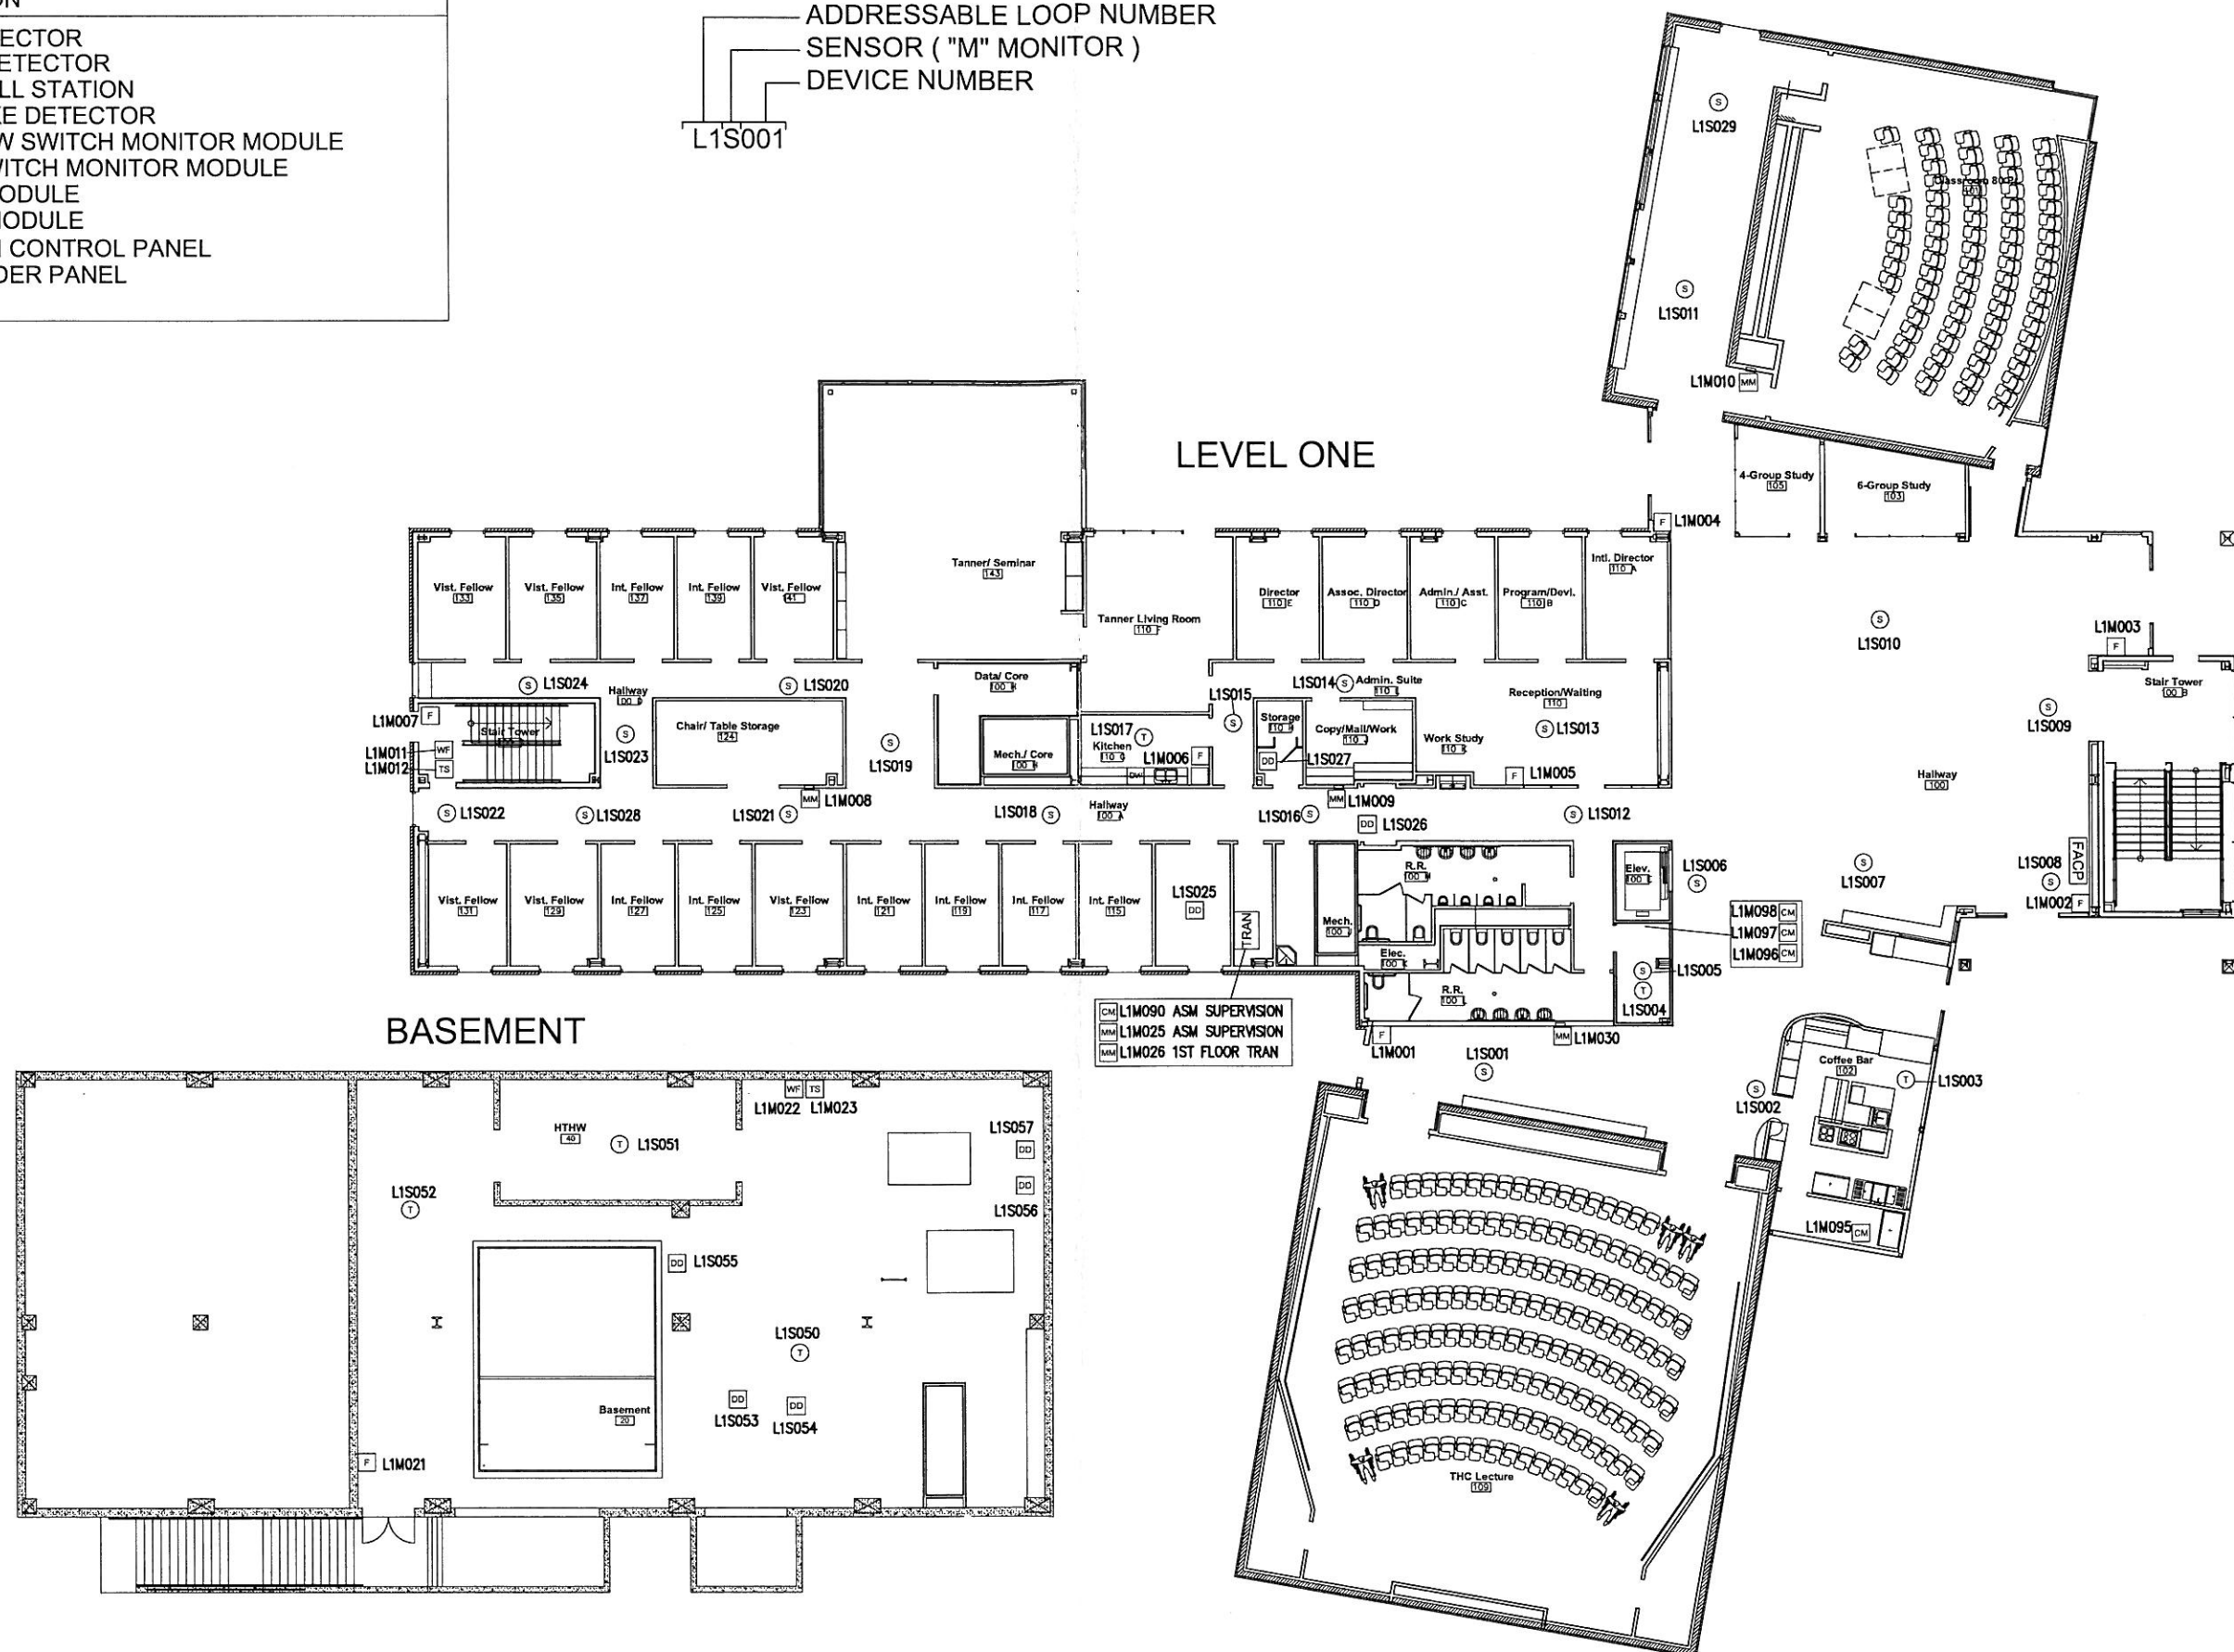

NFS DRAWINGS ARE BASED ON THE PROJECT ARCHITECT/ENGINEER (A/E) PLANS AND SPECIFICATIONS FURNISHED TO NFS. A/E IS SOLELY RESPONSIBLE (NOT NFS) FOR THE TYPE, SIZE, LOCATION, AND SUITABILITY OF ALL FIRE ALARMS, CONTROL PANELS, AND OTHER DEVICES SHOWN ON THE A/E PLANS. NFS DRAWINGS ARE TO SHOW ONLY THE WIRING DIAGRAMS BETWEEN FIRE ALARM DEVICES AND CONTROL PANELS. NFS IS NOT RESPONSIBLE FOR THE INFORMATION SHOWN ON THE A/E PLANS.

CAROLYN TANNER IRISH
HUMANITIES BUILDING
UNIVERSITY OF UTAH
BASEMENT AND LEVEL ONE
FIRE ALARM SYSTEM

NFS

NELSON FIRE SYSTEMS
801-468-8300

DRAWN BY:	DS
DESIGNED BY:	XXXX
APPROVED BY:	TCT
DATE:	8/11/2008
SCALE:	1/16"=1'
PROJECT NO:	05196750
REV NO:	1
DRAWING NAME:	HUMANITIES B AND I.DWG

FIRE ALARM SYSTEM

BASEMENT AND LEVEL 1
DRESSABLE LOOP NUMBERS


GE:

NFS


ADDRESS LABEL CLARIFICATION

ADDRESSABLE LOOP NUMBER
SENSOR ("M" MONITOR)
DEVICE NUMBER


L1S001

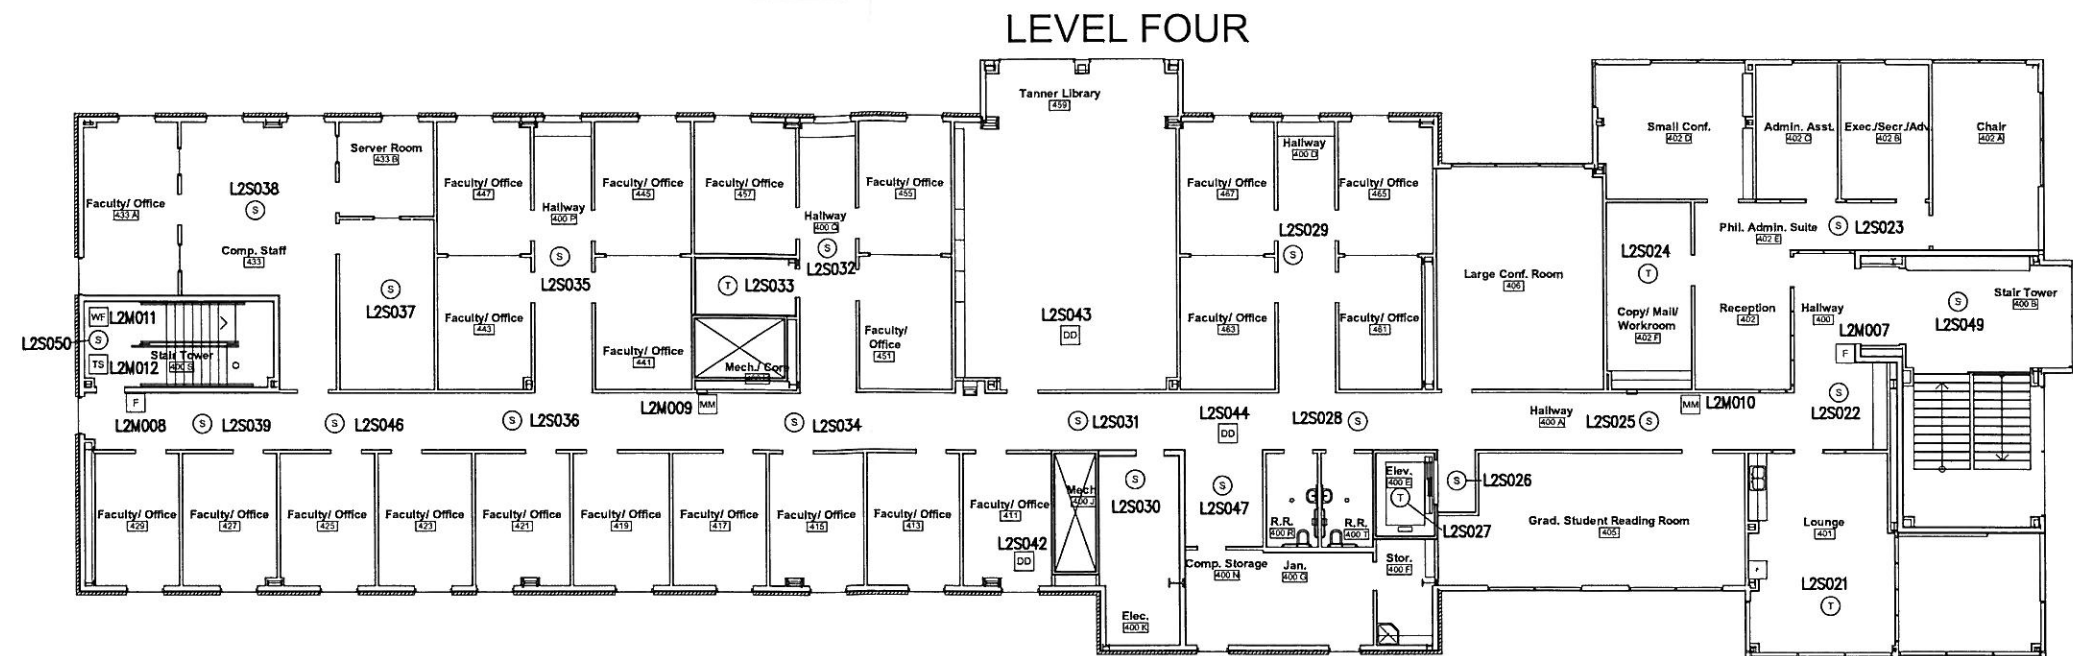

LEVEL THREE

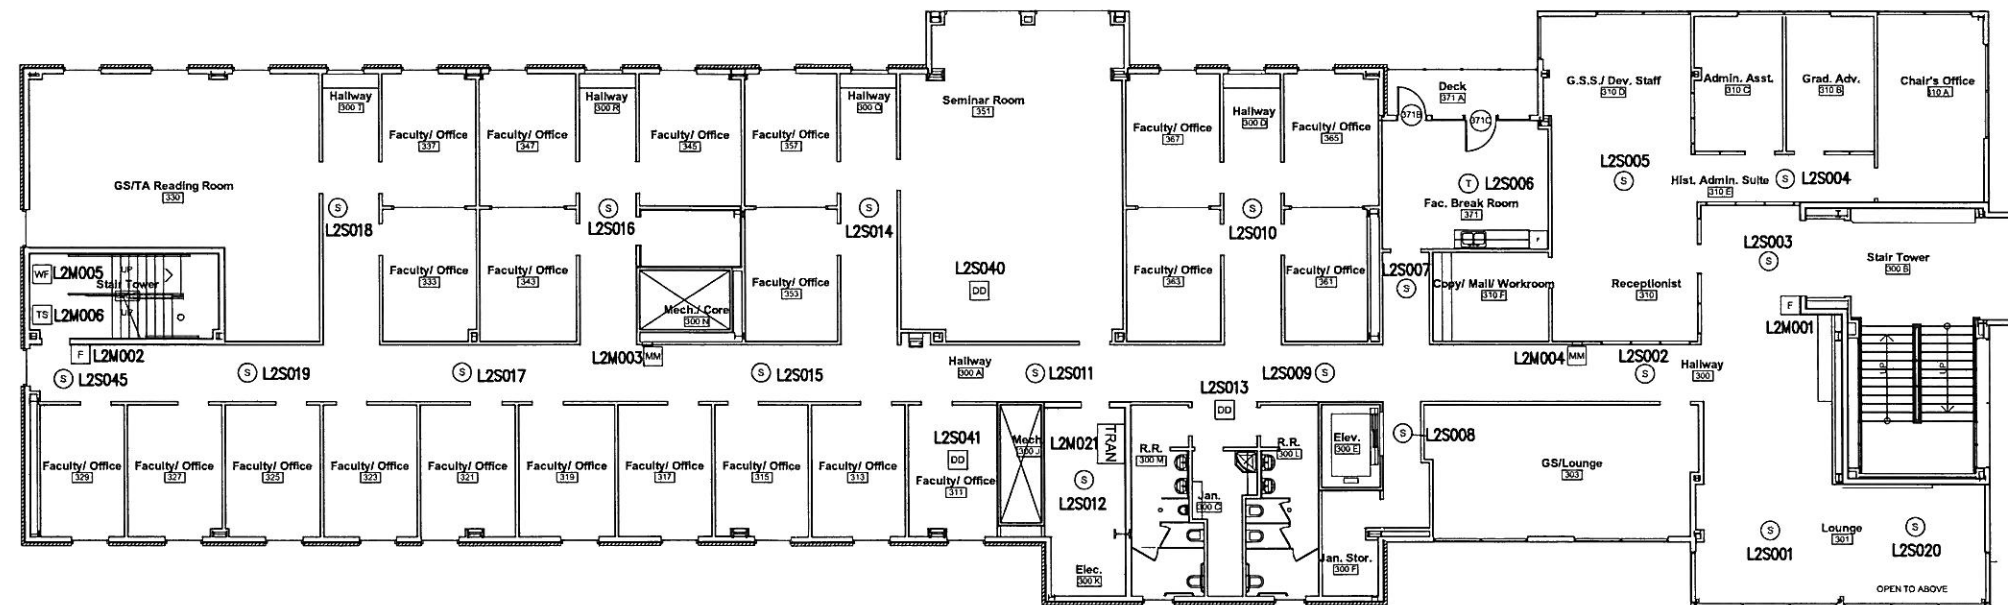


LEVEL TWO

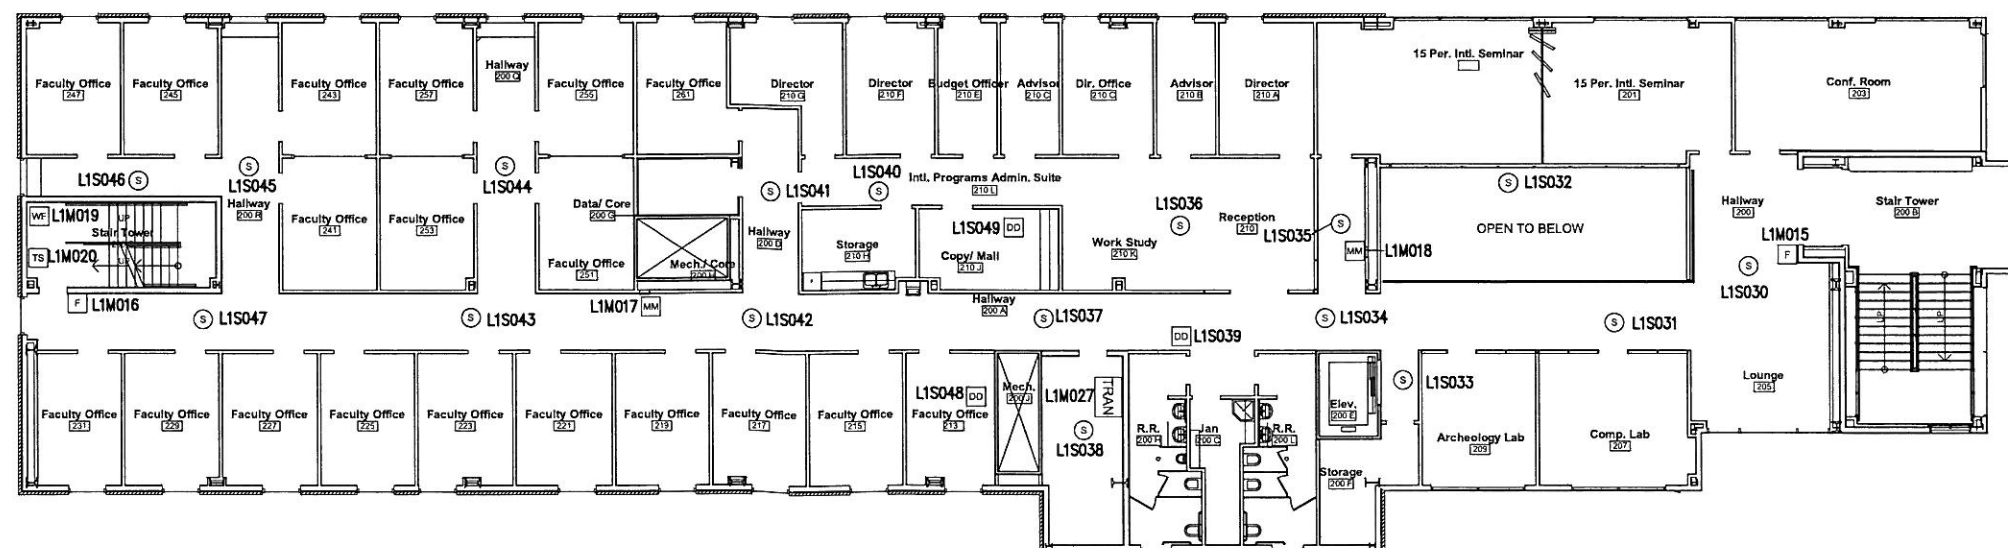

DEVICE LEGEND

SYMBOL	DESCRIPTION
S	SMOKE DETECTOR
T	THERMAL DETECTOR
F	MANUAL PULL STATION
DD	DUCT SMOKE DETECTOR
WF	WATERFLOW SWITCH MONITOR MODULE
TS	TAMPER SWITCH MONITOR MODULE
MM	MONITOR MODULE
CM	CONTROL MODULE
FACP	FIRE ALARM CONTROL PANEL
TRAN	TRANSPONDER PANEL

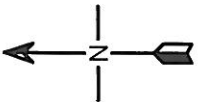

NFS DRAWINGS ARE BASED ON THE PROJECT ARCHITECT/ENGINEER (A/E) PLANS AND SPECIFICATIONS FURNISHED TO NFS. A/E IS SOLELY RESPONSIBLE FOR THE TYPE, SIZE, LOCATION, PANELS, AND OTHER DEVICES SHOWN ON THE PLANS. NFS DRAWINGS ARE TO BE USED ONLY FOR THE WIRING AND CONTROL PANELS. NFS IS NOT RESPONSIBLE FOR THE INFORMATION SHOWN ON THE A/E PLANS.

CAROLYN TANNER IRISH
HUMANITIES BUILDING
UNIVERSITY OF UTAH
LEVELS TWO, THREE, AND FOUR
FIRE ALARM SYSTEM

NFS

NELSON FIRE SYSTEMS
801-468-8300

DRAWN BY: DS
DESIGNED BY: XXXX
APPROVED BY: TCT
DATE: 8/11/2008
SCALE: 1/16"=1'-0"
PROJECT NO: 05196750
REV NO: 1
DRAWING NAME:
HUMANITIES 2,3,4.DWG

FIRE ALARM SYSTEM
LEVELS TWO/THREE/FOUR
ADDRESSABLE LOOP NUMBERS

PAGE:

NFS