


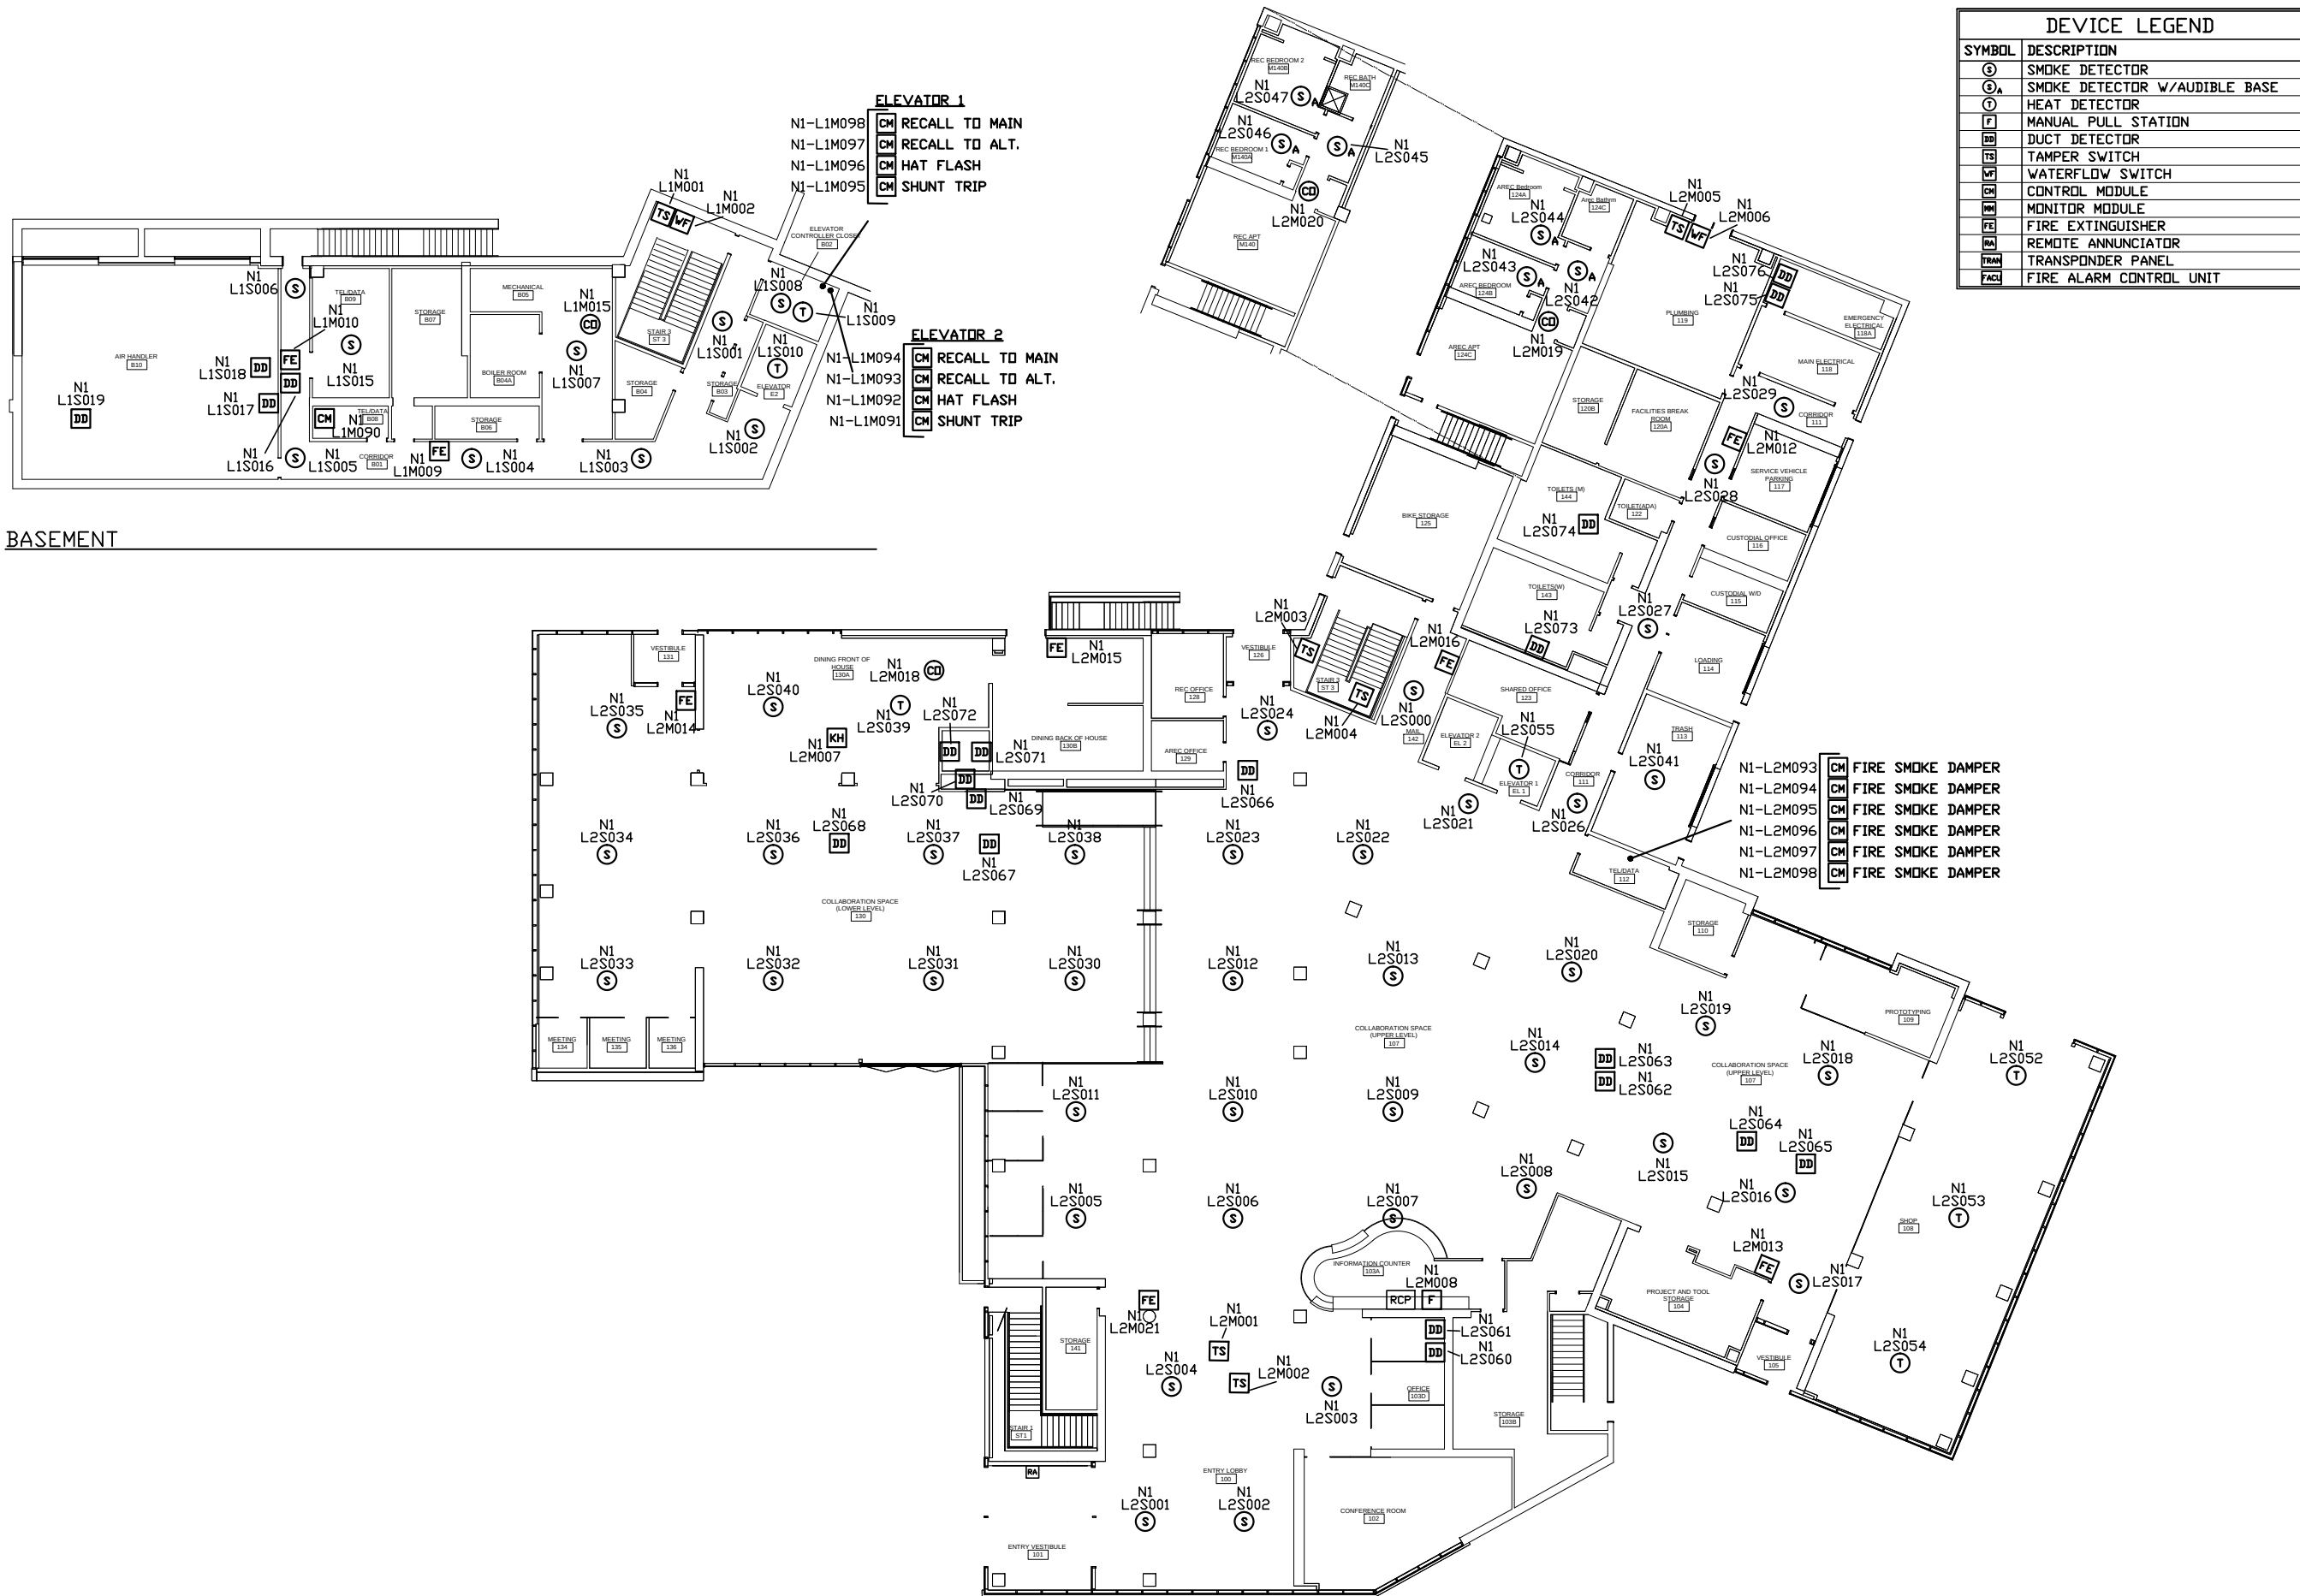

DEVICE LEGEND	
SYMBOL	DESCRIPTION
(S)	SMOKE DETECTOR
(S _A)	SMOKE DETECTOR W/AUDIBLE BASE
(H)	HEAT DETECTOR
(F)	MANUAL PULL STATION
(D)	DUCT DETECTOR
(TS)	TAMPER SWITCH
(CM)	CONTROL MODULE
(M)	MONITOR MODULE
(FE)	FIRE EXTINGUISHER
(RA)	REMOTE ANNUNCIATOR
(TR)	TRANSPONDER PANEL
(FACU)	FIRE ALARM CONTROL UNIT

NOTE:
NFS DRAWINGS ARE BASED ON THE PROJECT
ARCHITECT/ENGINEER (A/E) PLANS AND SPECIFICATIONS
FURNISHED TO NFS. A/E IS SOLELY RESPONSIBLE
(NOT NFS) FOR THE TYPE, SIZE, LOCATION, AND
SUITABILITY OF ALL FIRE ALARMS, CONTROL PANELS,
AND OTHER DEVICES SHOWN ON THE A/E PLANS.
NFS DRAWINGS ARE TO SHOW ONLY THE WIRING
DIAGRAMS BETWEEN FIRE ALARM DEVICES AND
CONTROL PANELS. NFS IS NOT RESPONSIBLE FOR
THE INFORMATION SHOWN ON THE A/E PLANS.


UNIVERSITY OF UTAH
LASSONDE STUDIOS - BASEMENT AND LEVEL 1
1700 STUDENT LIFE WAY
SALT LAKE CITY, UTH 84112
FIRE ALARM SYSTEM

NFS
NELSON FIRE SYSTEMS
801-468-8300

DRAWN BY: AK
DESIGNED BY: XXXX
APPROVED BY: RS
DATE: 8/10/16
SCALE: N.T.S.
PROJECT NO: XXXX
REV NO: XXXX
DRAWING NAME:
UofU LASSONDE STUDIOS FMI.DWG

FIRE ALARM SYSTEM
BASEMENT AND LEVEL 1

PAGE:
FINAL MAP

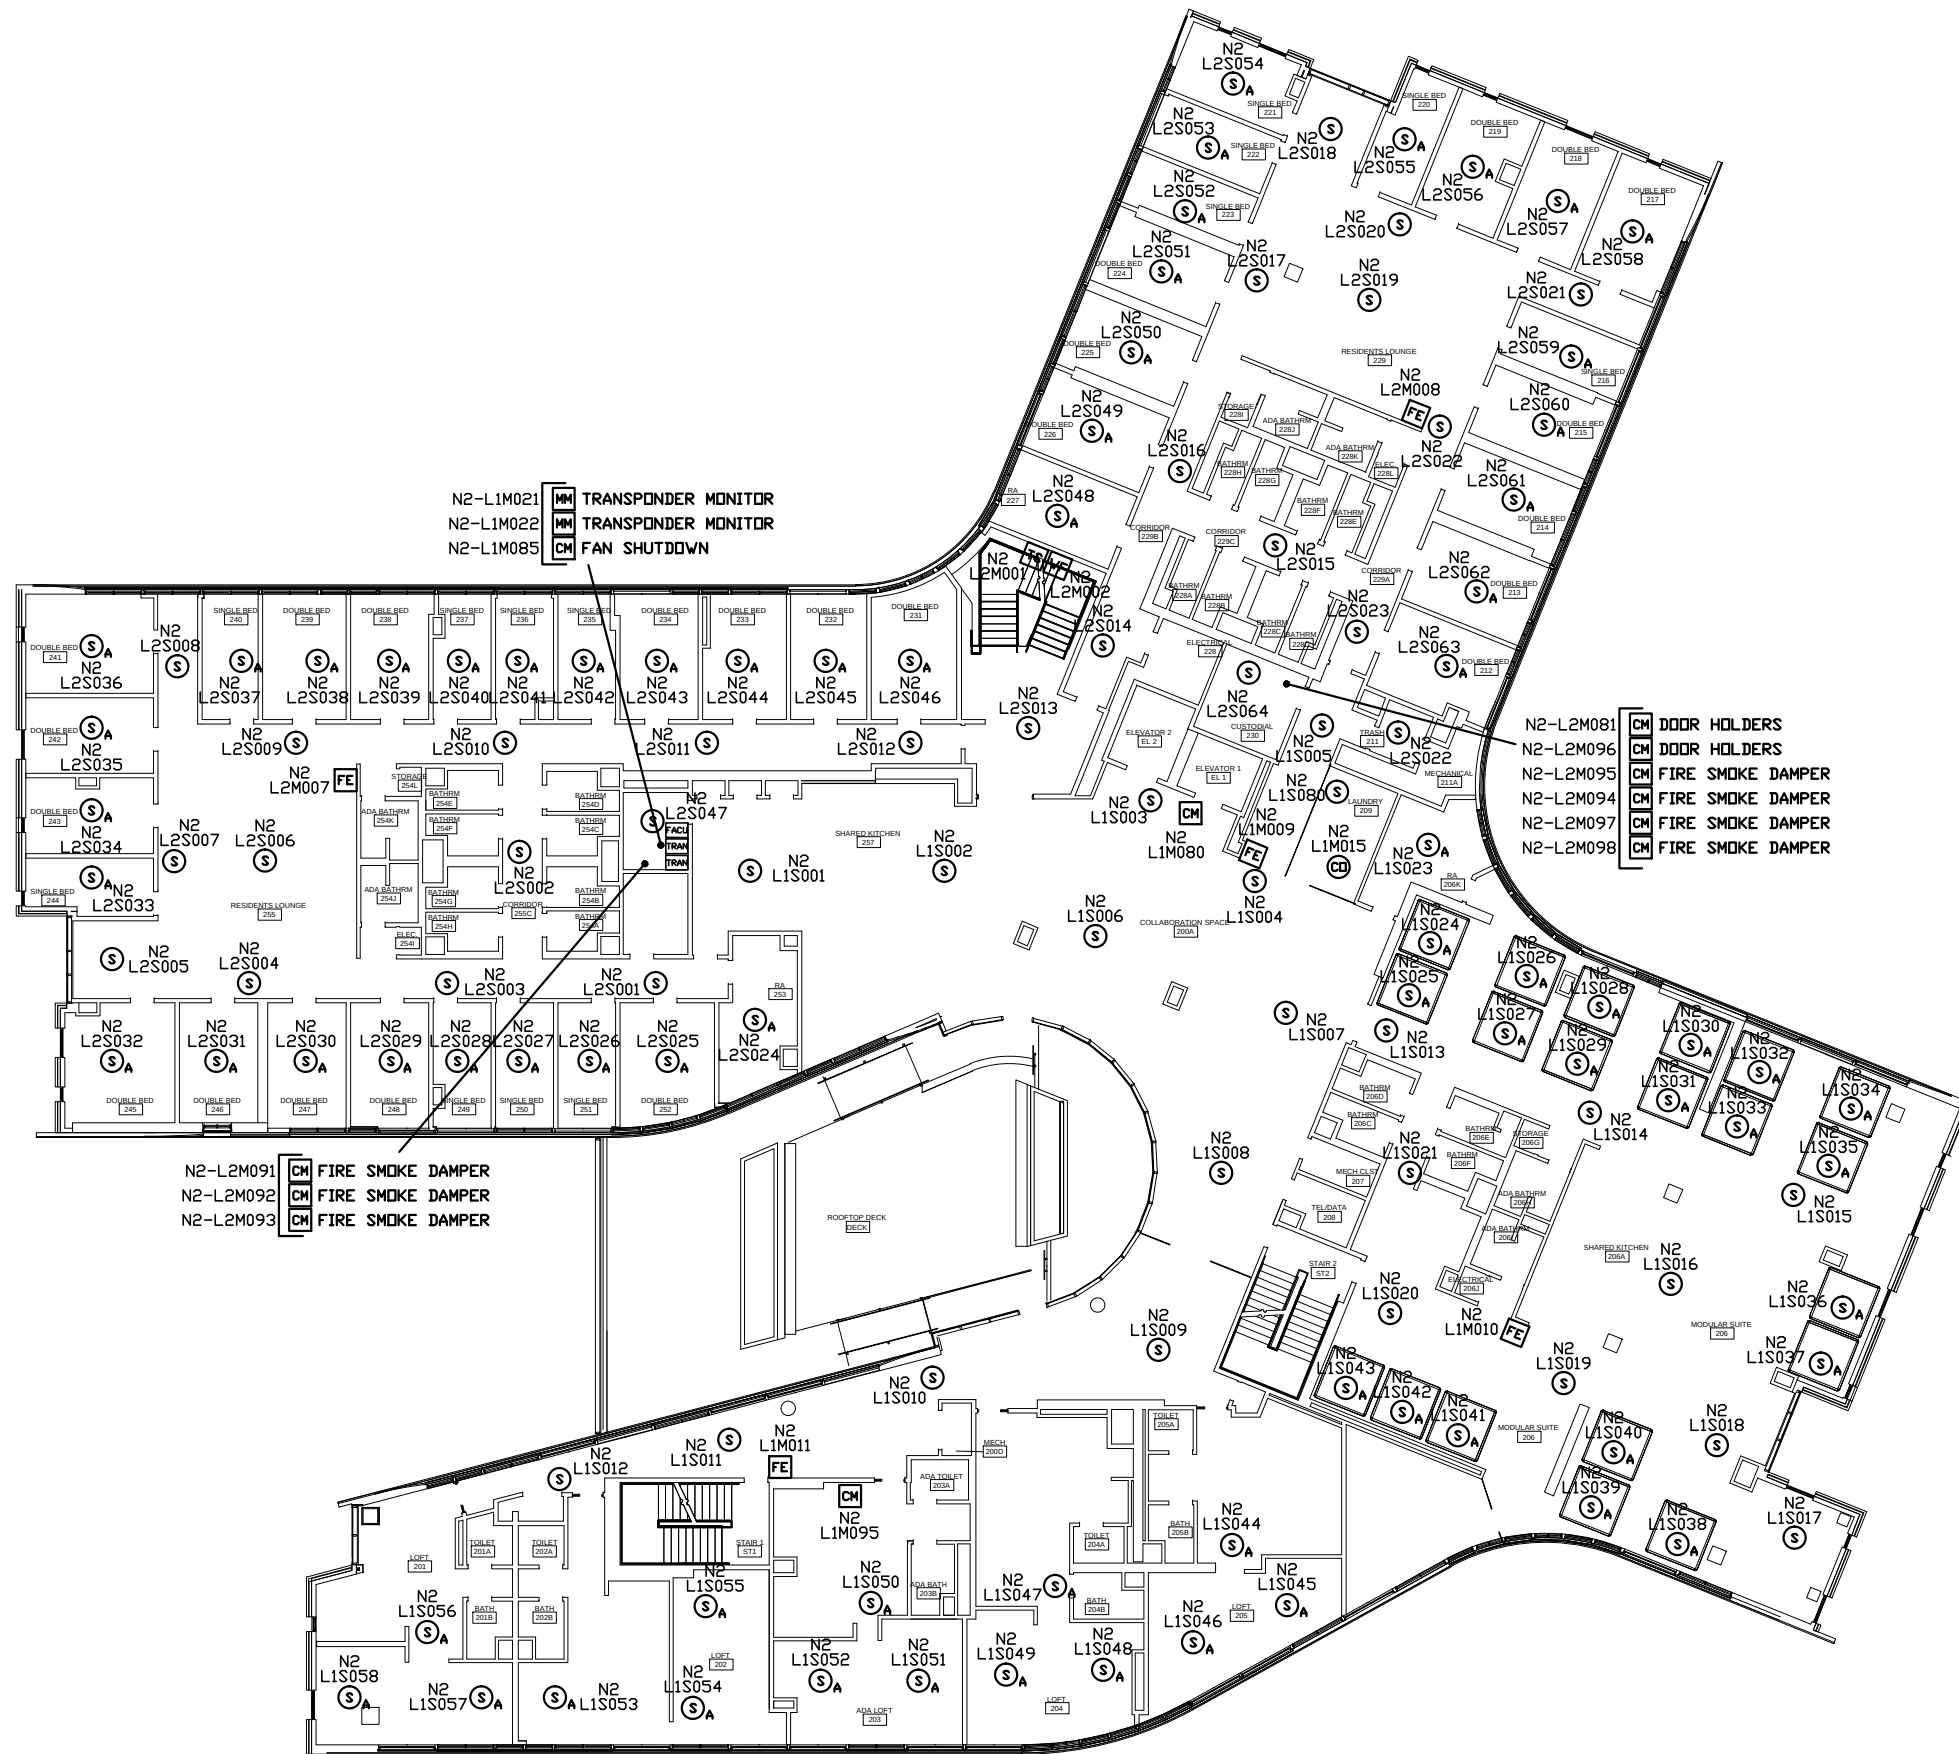

DEVICE LEGEND	
SYMBOL	DESCRIPTION
(S)	SMOKE DETECTOR
(S A)	SMOKE DETECTOR W/AUDIBLE BASE
(H)	HEAT DETECTOR
(F)	MANUAL PULL STATION
(D)	DUCT DETECTOR
(TS)	TAMPER SWITCH
(WS)	WATERFLOW SWITCH
(CM)	CONTROL MODULE
(MM)	MONITOR MODULE
(FE)	FIRE EXTINGUISHER
(RA)	REMOTE ANNUNCIATOR
(TR)	TRANSPONDER PANEL
(FACU)	FIRE ALARM CONTROL UNIT

UNIVERSITY OF UTAH
LASSONDE STUDIOS - LEVEL 2
1700 STUDENT LIFE WAY
SALT LAKE CITY, UTH 84112
FIRE ALARM SYSTEM


NFS
NELSON FIRE SYSTEMS
801-468-8300

DRAWN BY: AK
DESIGNED BY: XXXX
APPROVED BY: RS
DATE: 8/10/16
SCALE: N.T.S.
PROJECT NO: XXXX
REV NO: XXXX
DRAWING NAME:
UofU LASSONDE STUDIOS FM2.DWG

FIRE ALARM SYSTEM
LEVEL 2

PAGE:
FINAL MAP

NOTE:
NFS DRAWINGS ARE BASED ON THE PROJECT
ARCHITECT/ENGINEER (A/E) PLANS AND SPECIFICATIONS
FURNISHED TO NFS. A/E IS SOLELY RESPONSIBLE
(NOT NFS) FOR THE TYPE, SIZE, LOCATION, AND
SUITABILITY OF ALL FIRE ALARMS, CONTROL PANELS,
AND OTHER DEVICES SHOWN ON THE A/E PLANS.
NFS DRAWINGS ARE TO SHOW ONLY THE WIRING
DIAGRAMS BETWEEN FIRE ALARM DEVICES AND
CONTROL PANELS. NFS IS NOT RESPONSIBLE FOR
THE INFORMATION SHOWN ON THE A/E PLANS.

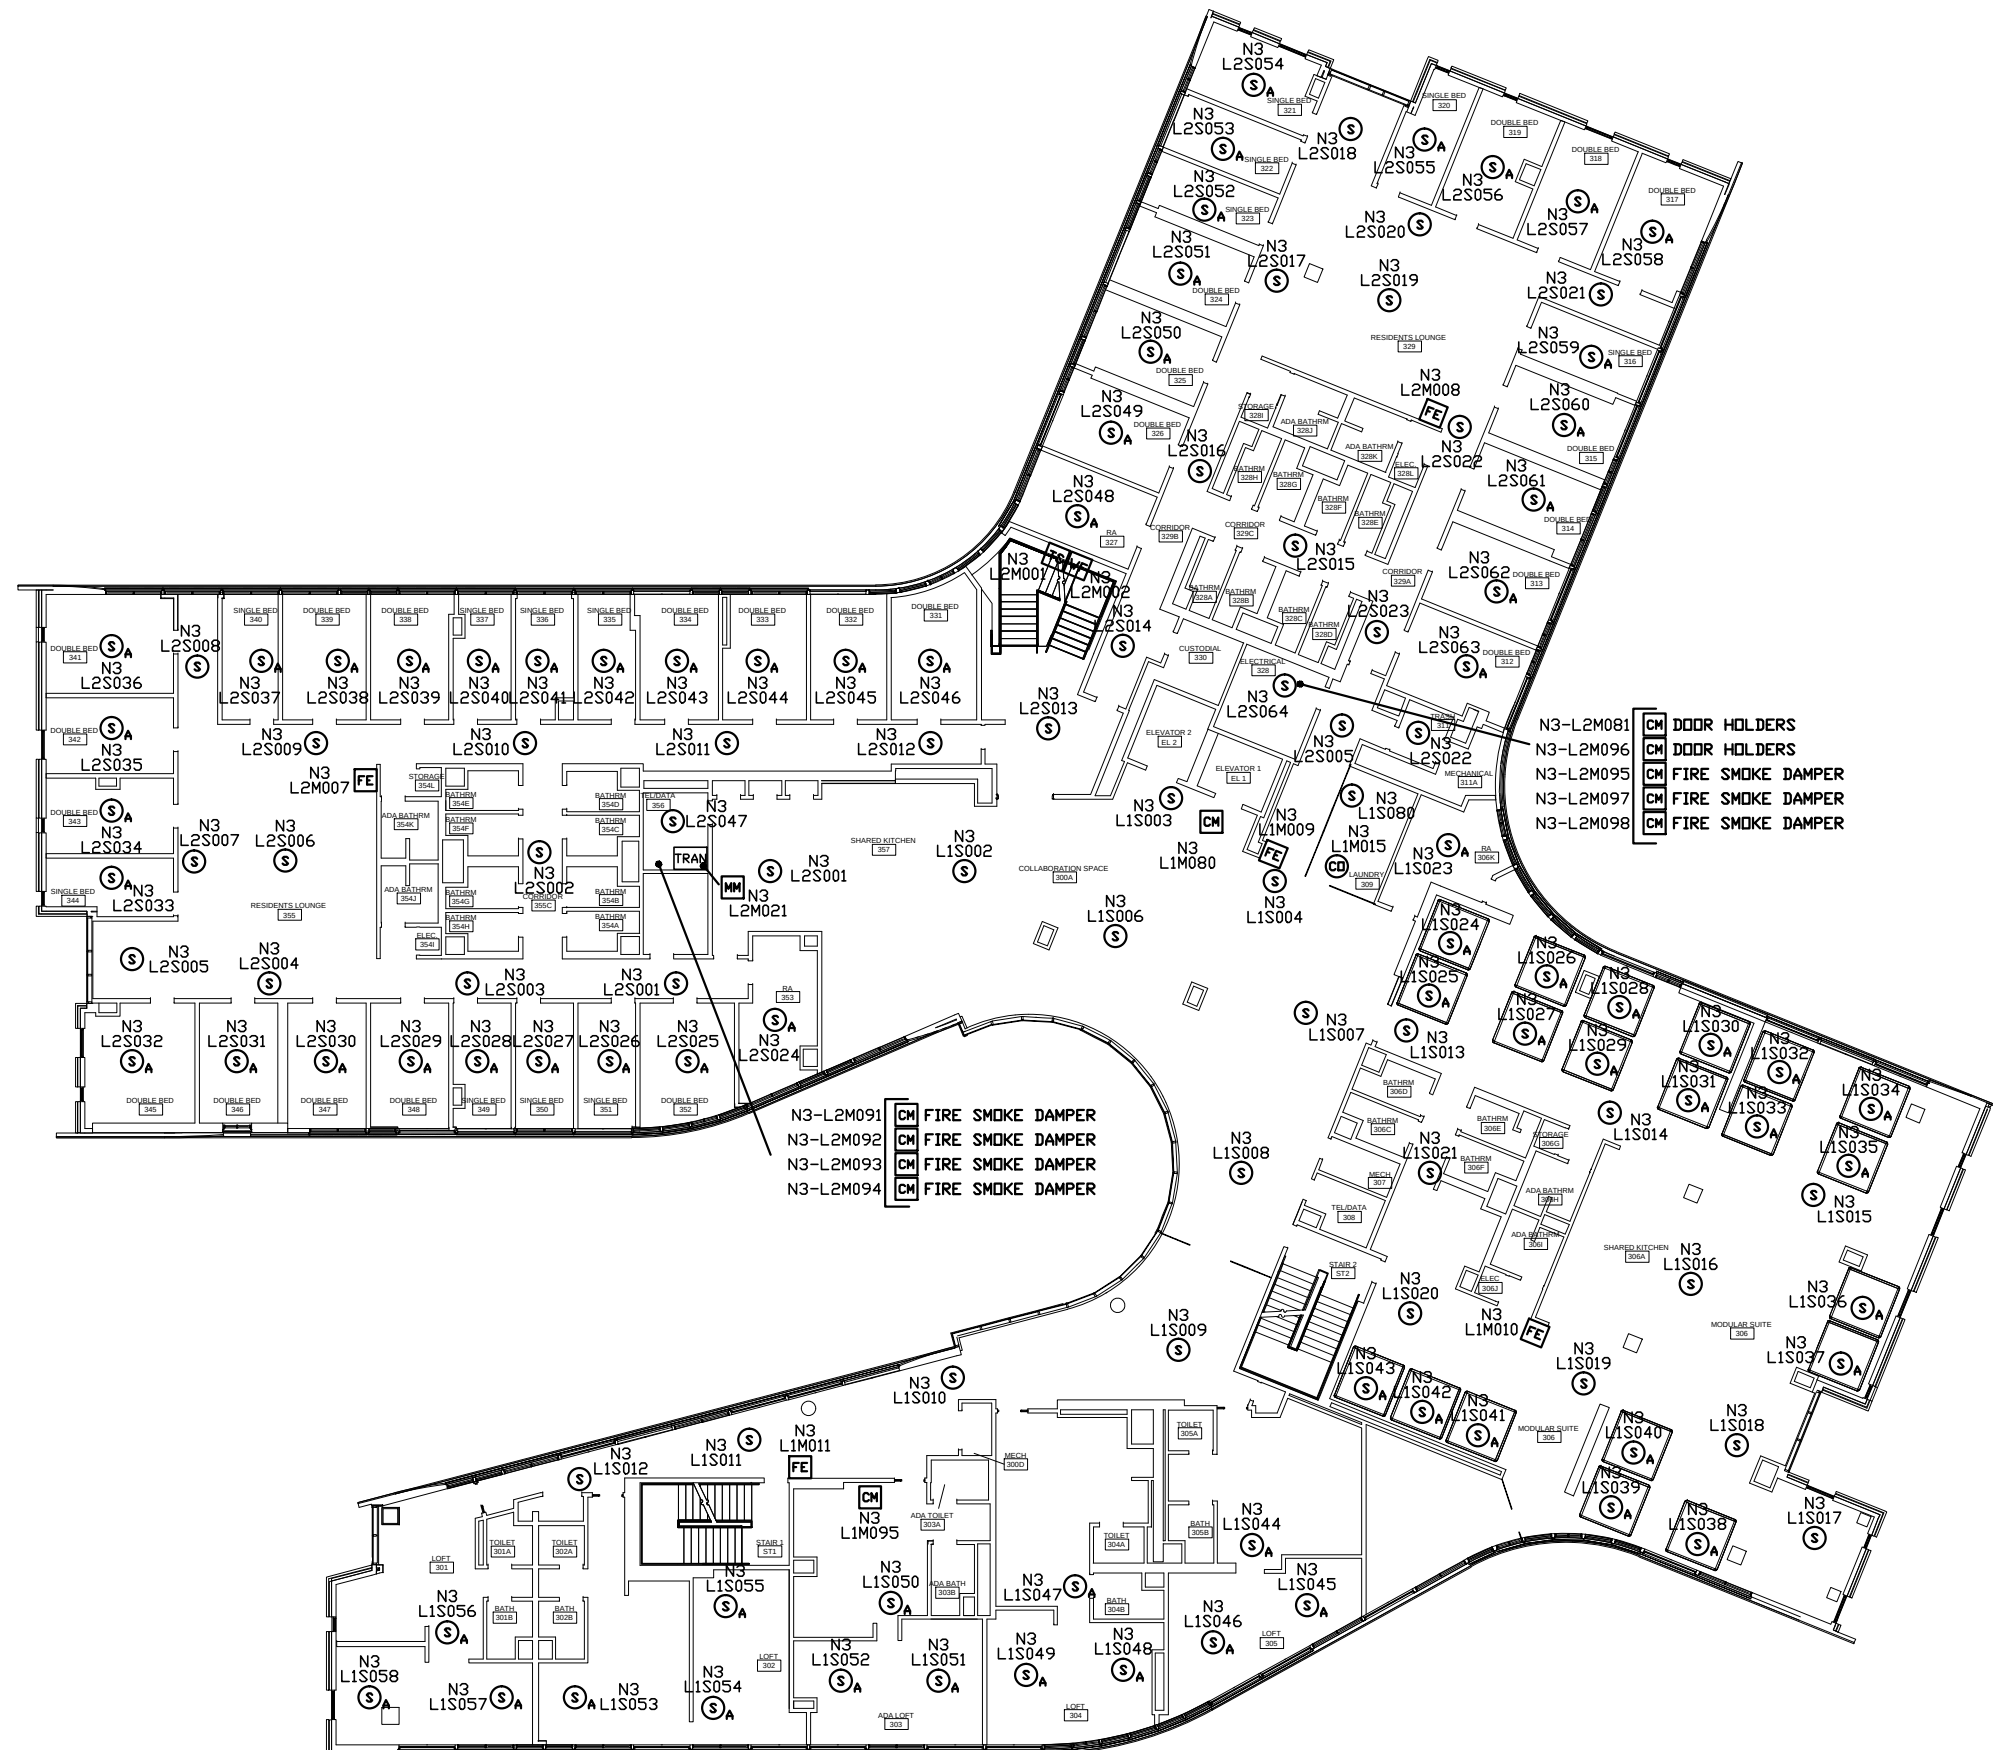

DEVICE LEGEND	
SYMBOL	DESCRIPTION
(S)	SMOKE DETECTOR
(S _A)	SMOKE DETECTOR W/AUDIBLE BASE
(H)	HEAT DETECTOR
(F)	MANUAL PULL STATION
(D)	DUCT DETECTOR
(TS)	TAMPER SWITCH
(WS)	WATERFLOW SWITCH
(CM)	CONTROL MODULE
(M)	MONITOR MODULE
(FE)	FIRE EXTINGUISHER
(RA)	REMOTE ANNUNCIATOR
(TR)	TRANSPONDER PANEL
(FACU)	FIRE ALARM CONTROL UNIT

NOTE:
NFS DRAWINGS ARE BASED ON THE PROJECT
ARCHITECT/ENGINEER (A/E) PLANS AND SPECIFICATIONS
FURNISHED TO NFS. A/E IS SOLELY RESPONSIBLE
(NOT NFS) FOR THE TYPE, SIZE, LOCATION, AND
SUITABILITY OF ALL FIRE ALARMS, CONTROL PANELS,
AND OTHER DEVICES SHOWN ON THE A/E PLANS.
NFS DRAWINGS ARE TO SHOW ONLY THE WIRING
DIAGRAMS BETWEEN FIRE ALARM DEVICES AND
CONTROL PANELS. NFS IS NOT RESPONSIBLE FOR
THE INFORMATION SHOWN ON THE A/E PLANS.


UNIVERSITY OF UTAH
LASSONDE STUDIOS - LEVEL 3
1700 STUDENT LIFE WAY
SALT LAKE CITY, UTH 84112
FIRE ALARM SYSTEM

NFS
NELSON FIRE SYSTEMS
801-468-8300

DRAWN BY: AK
DESIGNED BY: XXXX
APPROVED BY: RS
DATE: 8/10/16
SCALE: N.T.S.
PROJECT NO: XXXX
REV NO: XXXX
DRAWING NAME:
UOFU LASSONDE STUDIOS FM3.DWG

FIRE ALARM SYSTEM
LEVEL 3

PAGE:
FINAL MAP

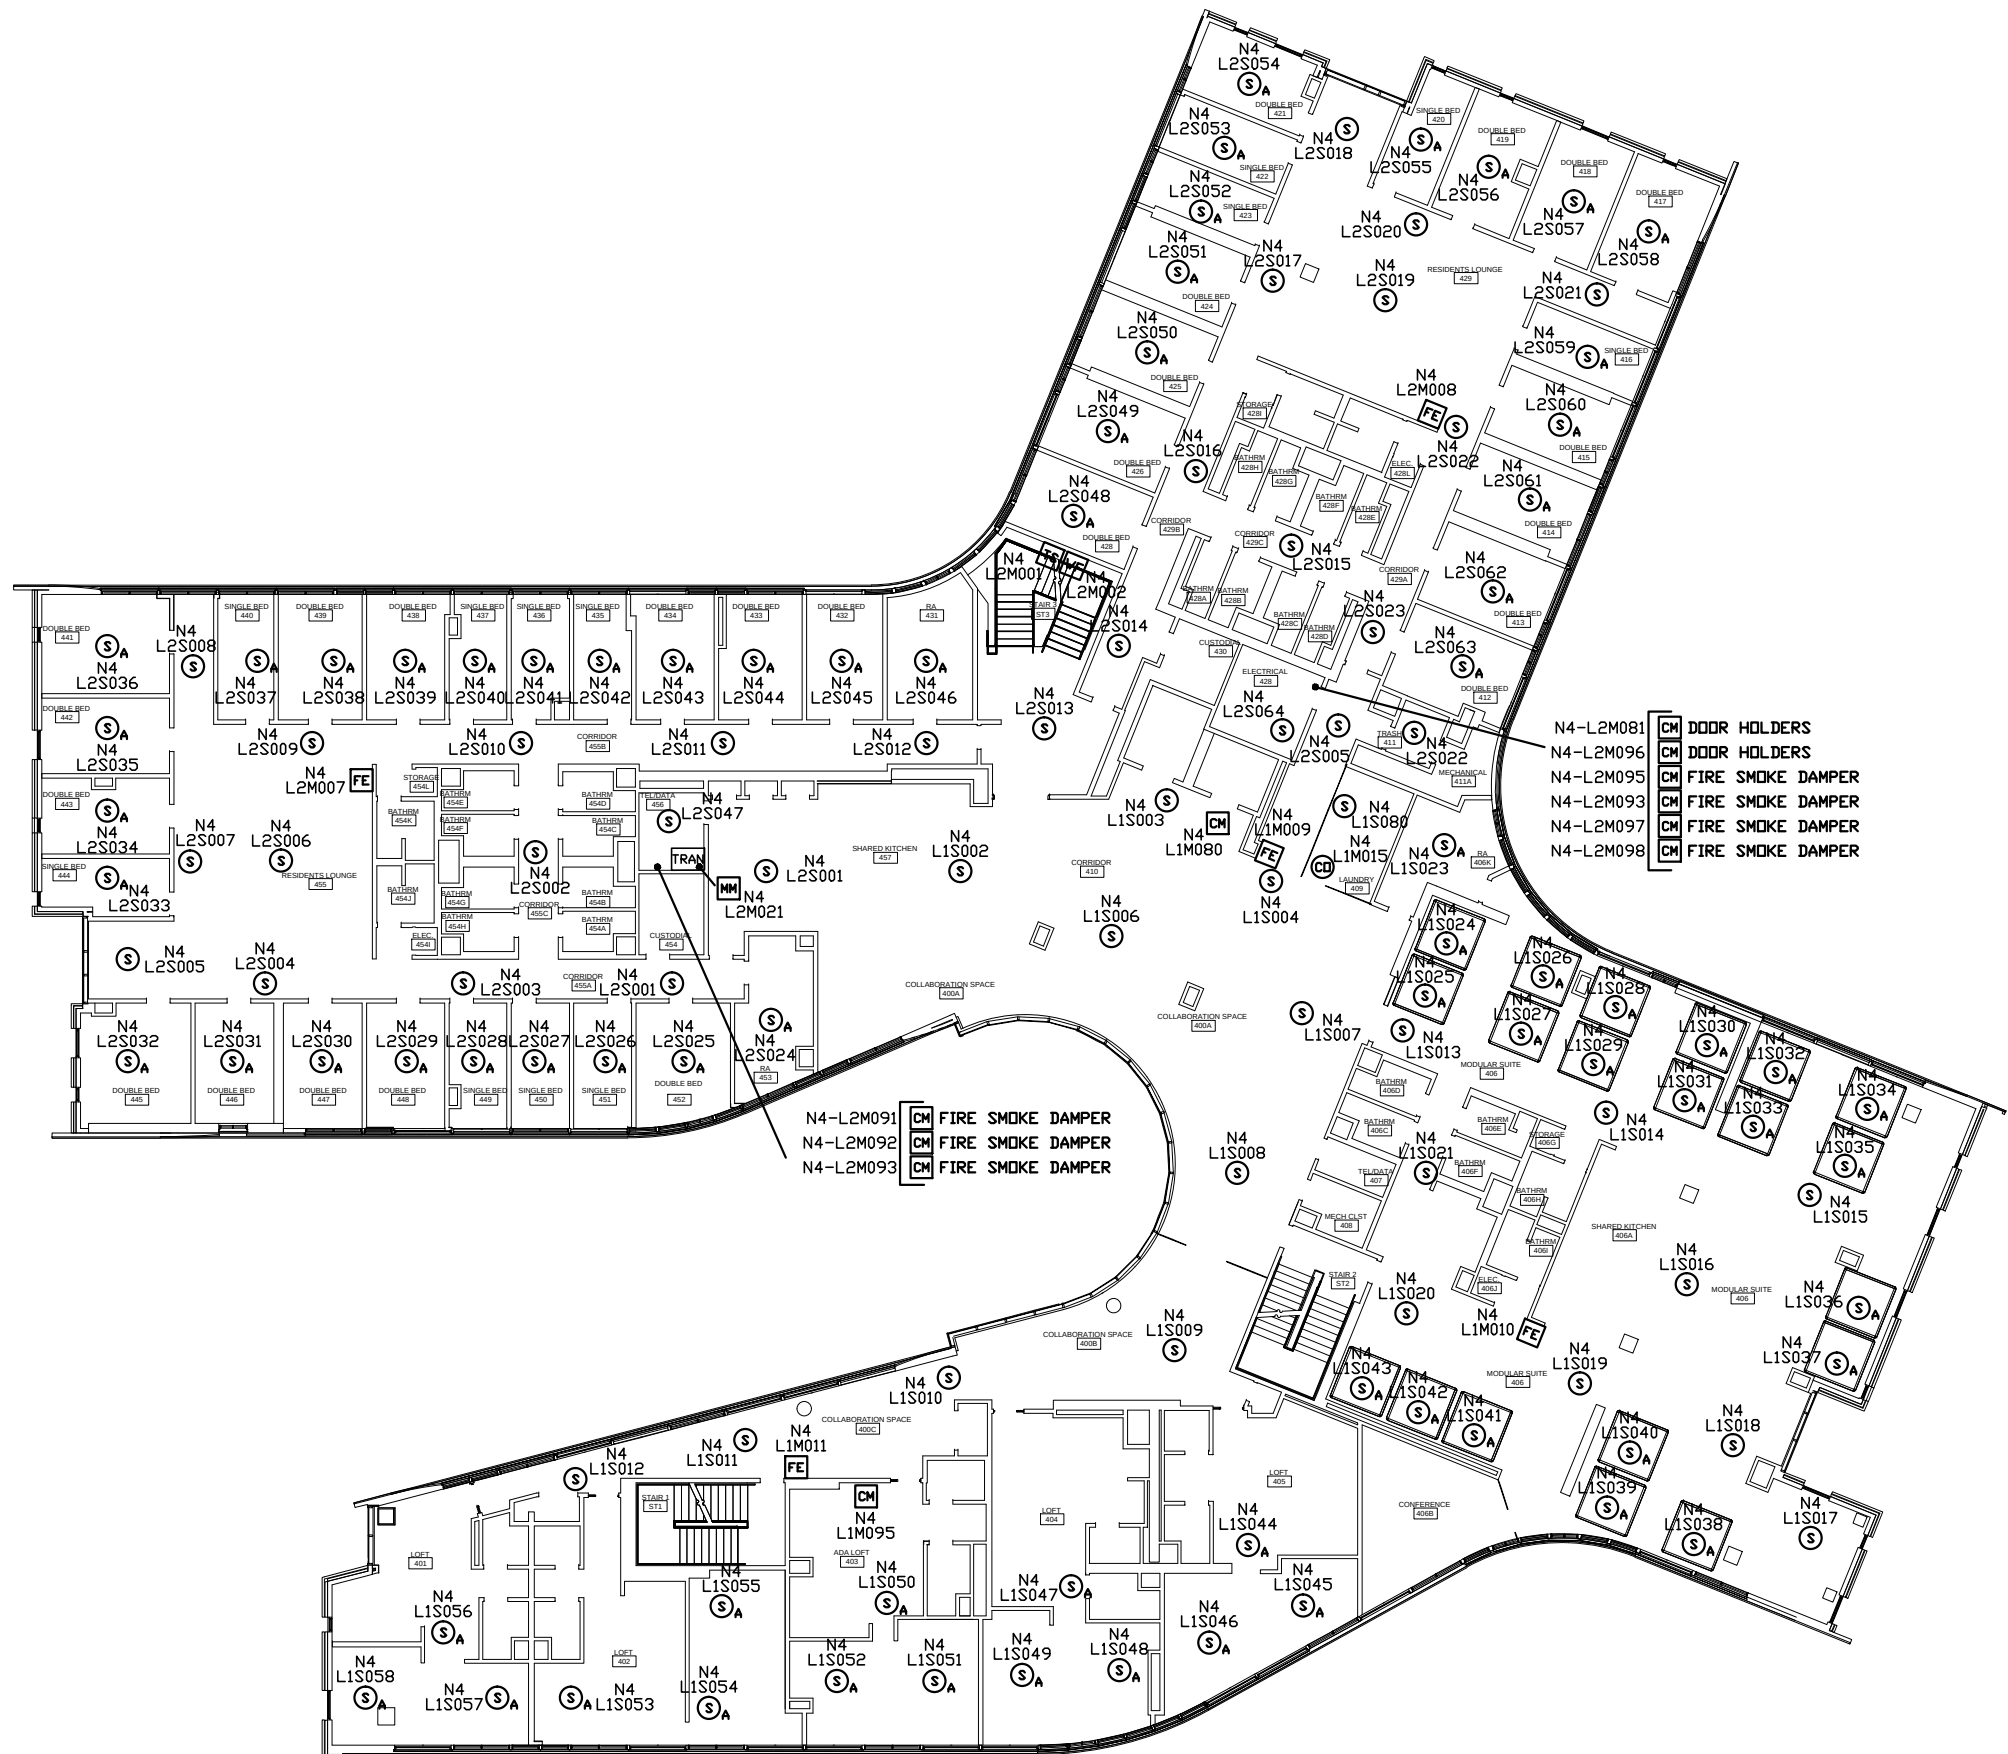

DEVICE LEGEND	
SYMBOL	DESCRIPTION
(S)	SMOKE DETECTOR
(S _A)	SMOKE DETECTOR W/AUDIBLE BASE
(H)	HEAT DETECTOR
(F)	MANUAL PULL STATION
(D)	DUCT DETECTOR
(TS)	TAMPER SWITCH
(WS)	WATERFLOW SWITCH
(CM)	CONTROL MODULE
(MM)	MONITOR MODULE
(FE)	FIRE EXTINGUISHER
(RA)	REMOTE ANNUNCIATOR
(TRAN)	TRANSPONDER PANEL
(FACU)	FIRE ALARM CONTROL UNIT

NOTE:
NFS DRAWINGS ARE BASED ON THE PROJECT
ARCHITECT/ENGINEER (A/E) PLANS AND SPECIFICATIONS
FURNISHED TO NFS. A/E IS SOLELY RESPONSIBLE
(NOT NFS) FOR THE TYPE, SIZE, LOCATION, AND
SUITABILITY OF ALL FIRE ALARMS, CONTROL PANELS,
AND OTHER DEVICES SHOWN ON THE A/E PLANS.
NFS DRAWINGS ARE TO SHOW ONLY THE WIRING
DIAGRAMS BETWEEN FIRE ALARM DEVICES AND
CONTROL PANELS. NFS IS NOT RESPONSIBLE FOR
THE INFORMATION SHOWN ON THE A/E PLANS.


UNIVERSITY OF UTAH
LASSONDE STUDIOS - LEVEL 4
1700 STUDENT LIFE WAY
SALT LAKE CITY, UTH 84112
FIRE ALARM SYSTEM

NFS
NELSON FIRE SYSTEMS
801-468-8300


DRAWN BY: AK
DESIGNED BY: XXXX
APPROVED BY: RS
DATE: 8/10/16
SCALE: N.T.S.
PROJECT NO: XXXX
REV NO: XXXX
DRAWING NAME:
JOFU LASSONDE STUDIOS FM4.DWG

FIRE ALARM SYSTEM
LEVEL 4

PAGE:
FINAL MAP

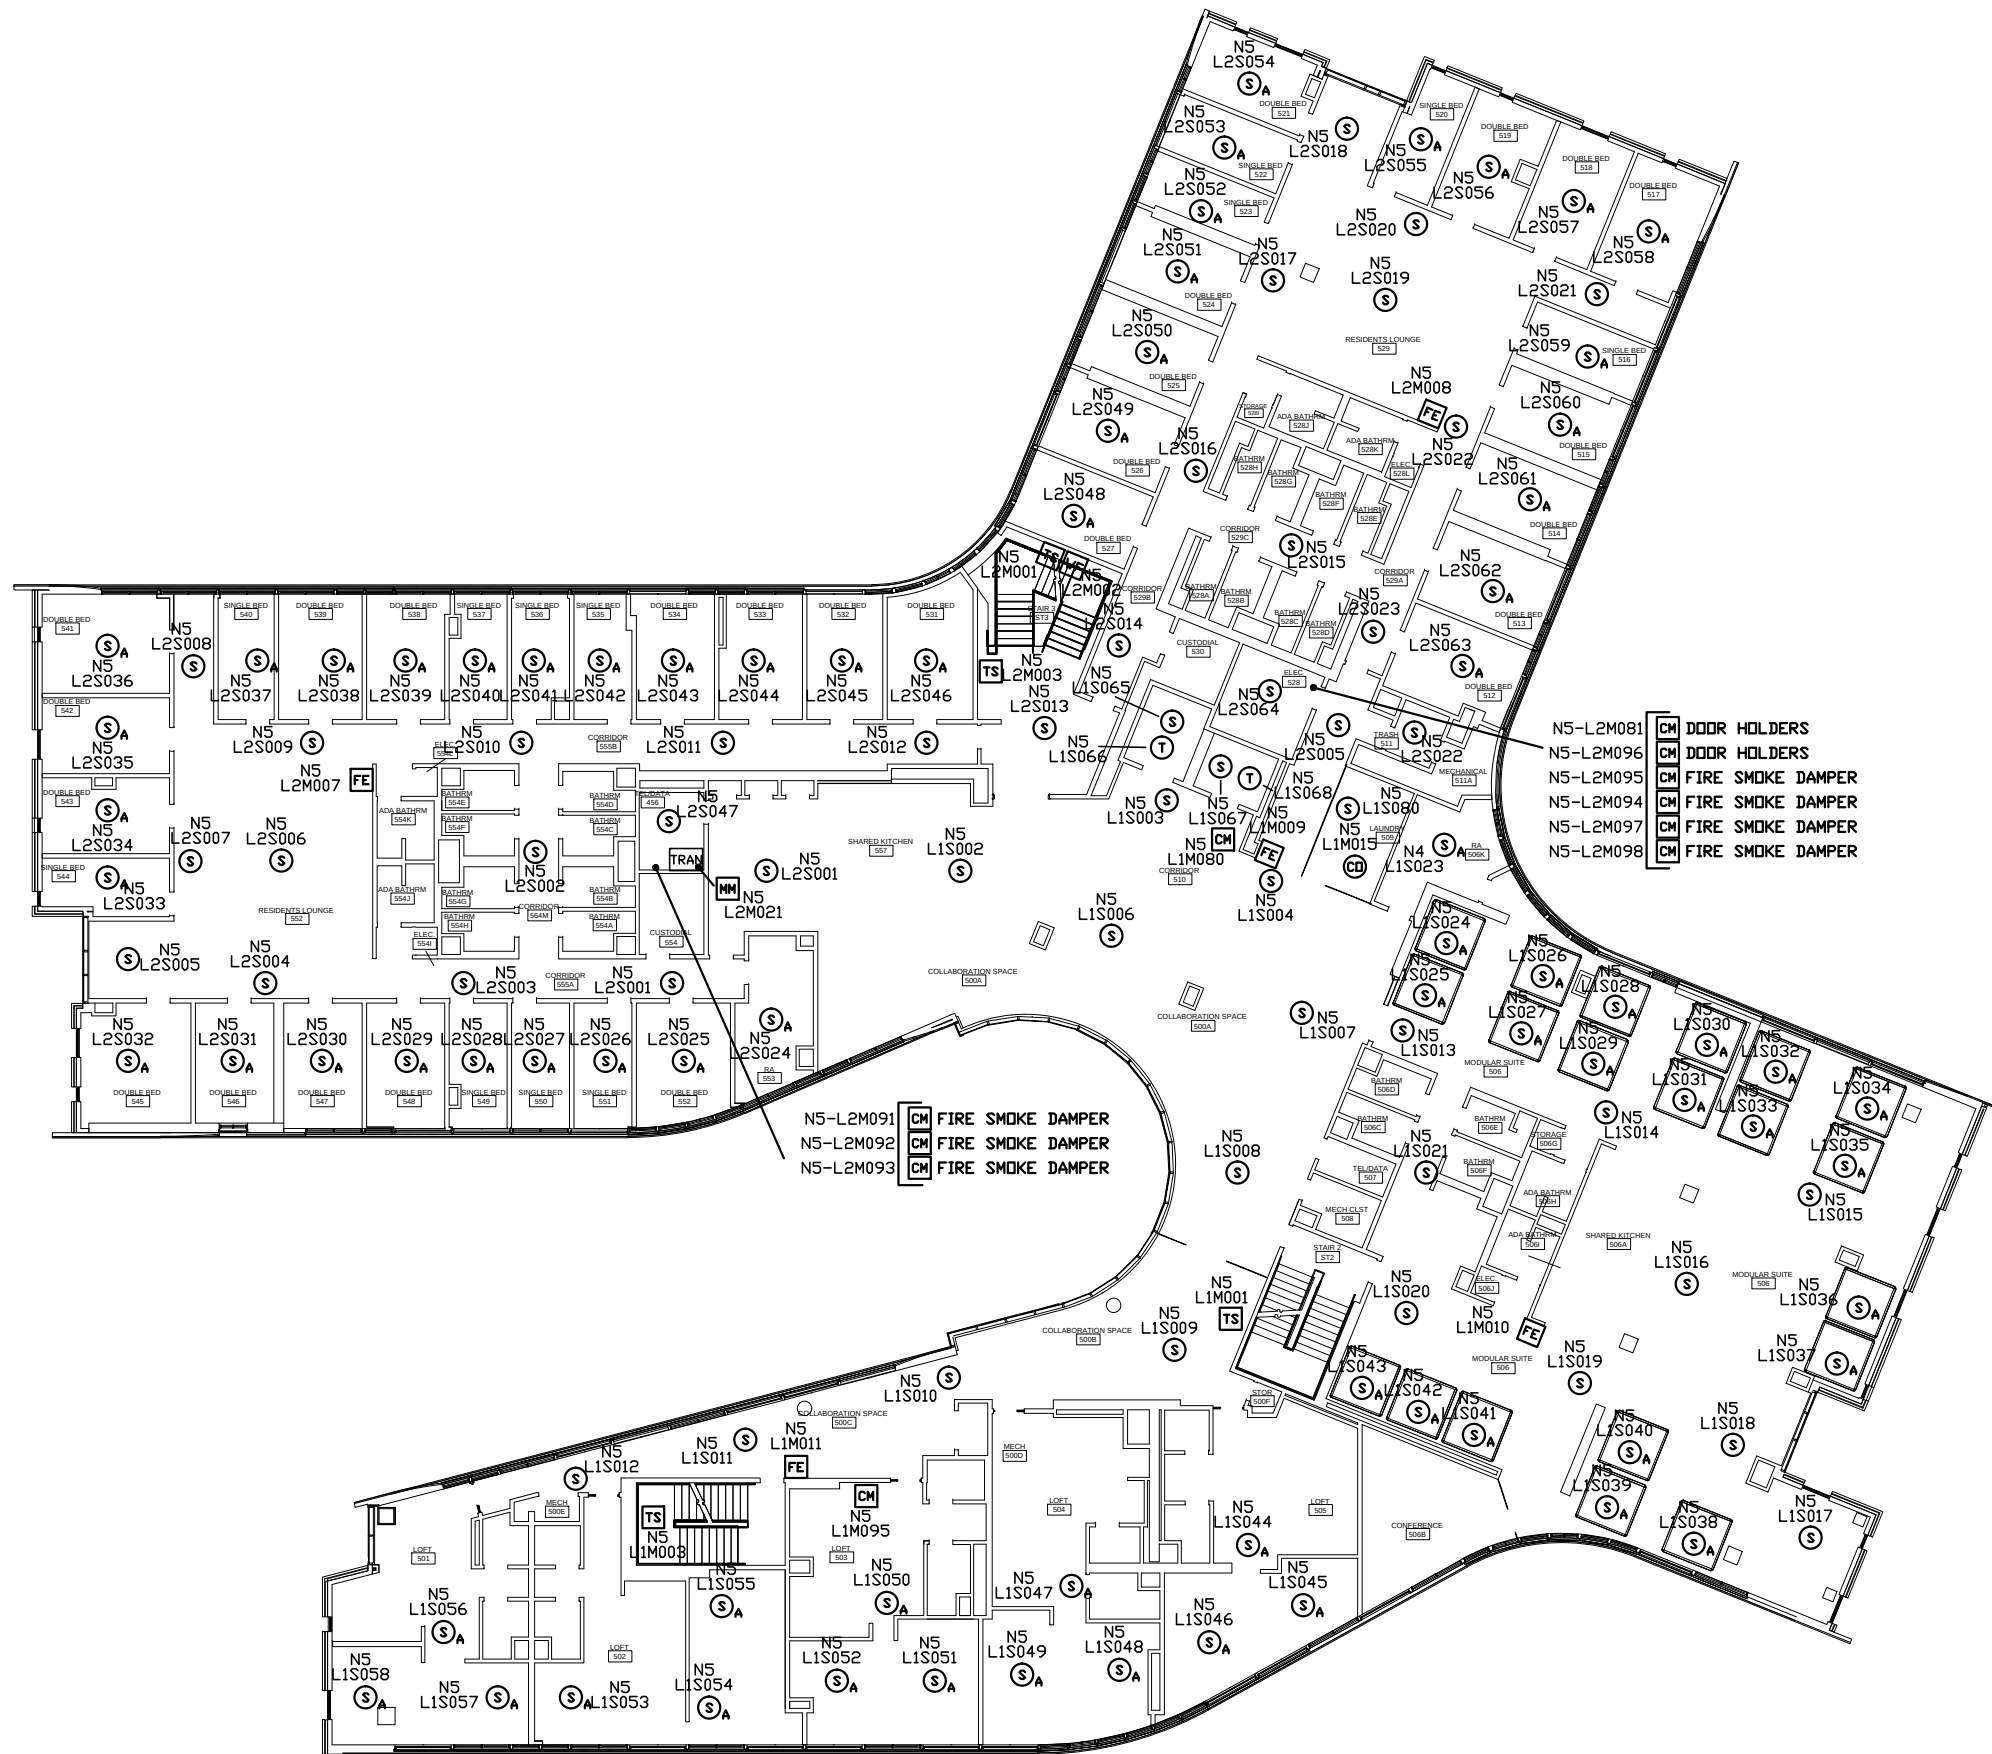

DEVICE LEGEND	
SYMBOL	DESCRIPTION
S	SMOKE DETECTOR
SA	SMOKE DETECTOR W/AUDIBLE BASE
○	HEAT DETECTOR
F	MANUAL PULL STATION
DB	DUCT DETECTOR
TS	TAMPER SWITCH
WS	WATERFLOW SWITCH
CM	CONTROL MODULE
MM	MONITOR MODULE
FE	FIRE EXTINGUISHER
RA	REMOTE ANNUNCIATOR
TRAN	TRANSPONDER PANEL
FACU	FIRE ALARM CONTROL UNIT

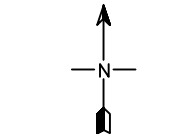

NOTE:
NFS DRAWINGS ARE BASED ON THE PROJECT
ARCHITECT/ENGINEER (A/E) PLANS AND SPECIFICATIONS
FURNISHED TO NFS. A/E IS SOLELY RESPONSIBLE
(NOT NFS) FOR THE TYPE, SIZE, LOCATION, AND
SUITABILITY OF ALL FIRE ALARMS, CONTROL PANELS,
AND OTHER DEVICES SHOWN ON THE A/E PLANS.
NFS DRAWINGS ARE TO SHOW ONLY THE WIRING
DIAGRAMS BETWEEN FIRE ALARM DEVICES AND
CONTROL PANELS. NFS IS NOT RESPONSIBLE FOR
THE INFORMATION SHOWN ON THE A/E PLANS.

UNIVERSITY OF UTAH
LASSONDE STUDIOS - LEVEL 5
1700 STUDENT LIFE WAY
SALT LAKE CITY, UTH 84112
FIRE ALARM SYSTEM

NFS
NELSON FIRE SYSTEMS
801-468-8300

DRAWN BY:	AK
DESIGNED BY:	XXXX
APPROVED BY:	RS
DATE:	8/10/16
SCALE:	N.T.S.
PROJECT NO:	XXXX
REV NO:	XXXX
DRAWING NAME:	JOFU LASSONDE STUDIOS FMS.DWG

FIRE ALARM SYSTEM
LEVEL 5

PAGE:
FINAL MAP