


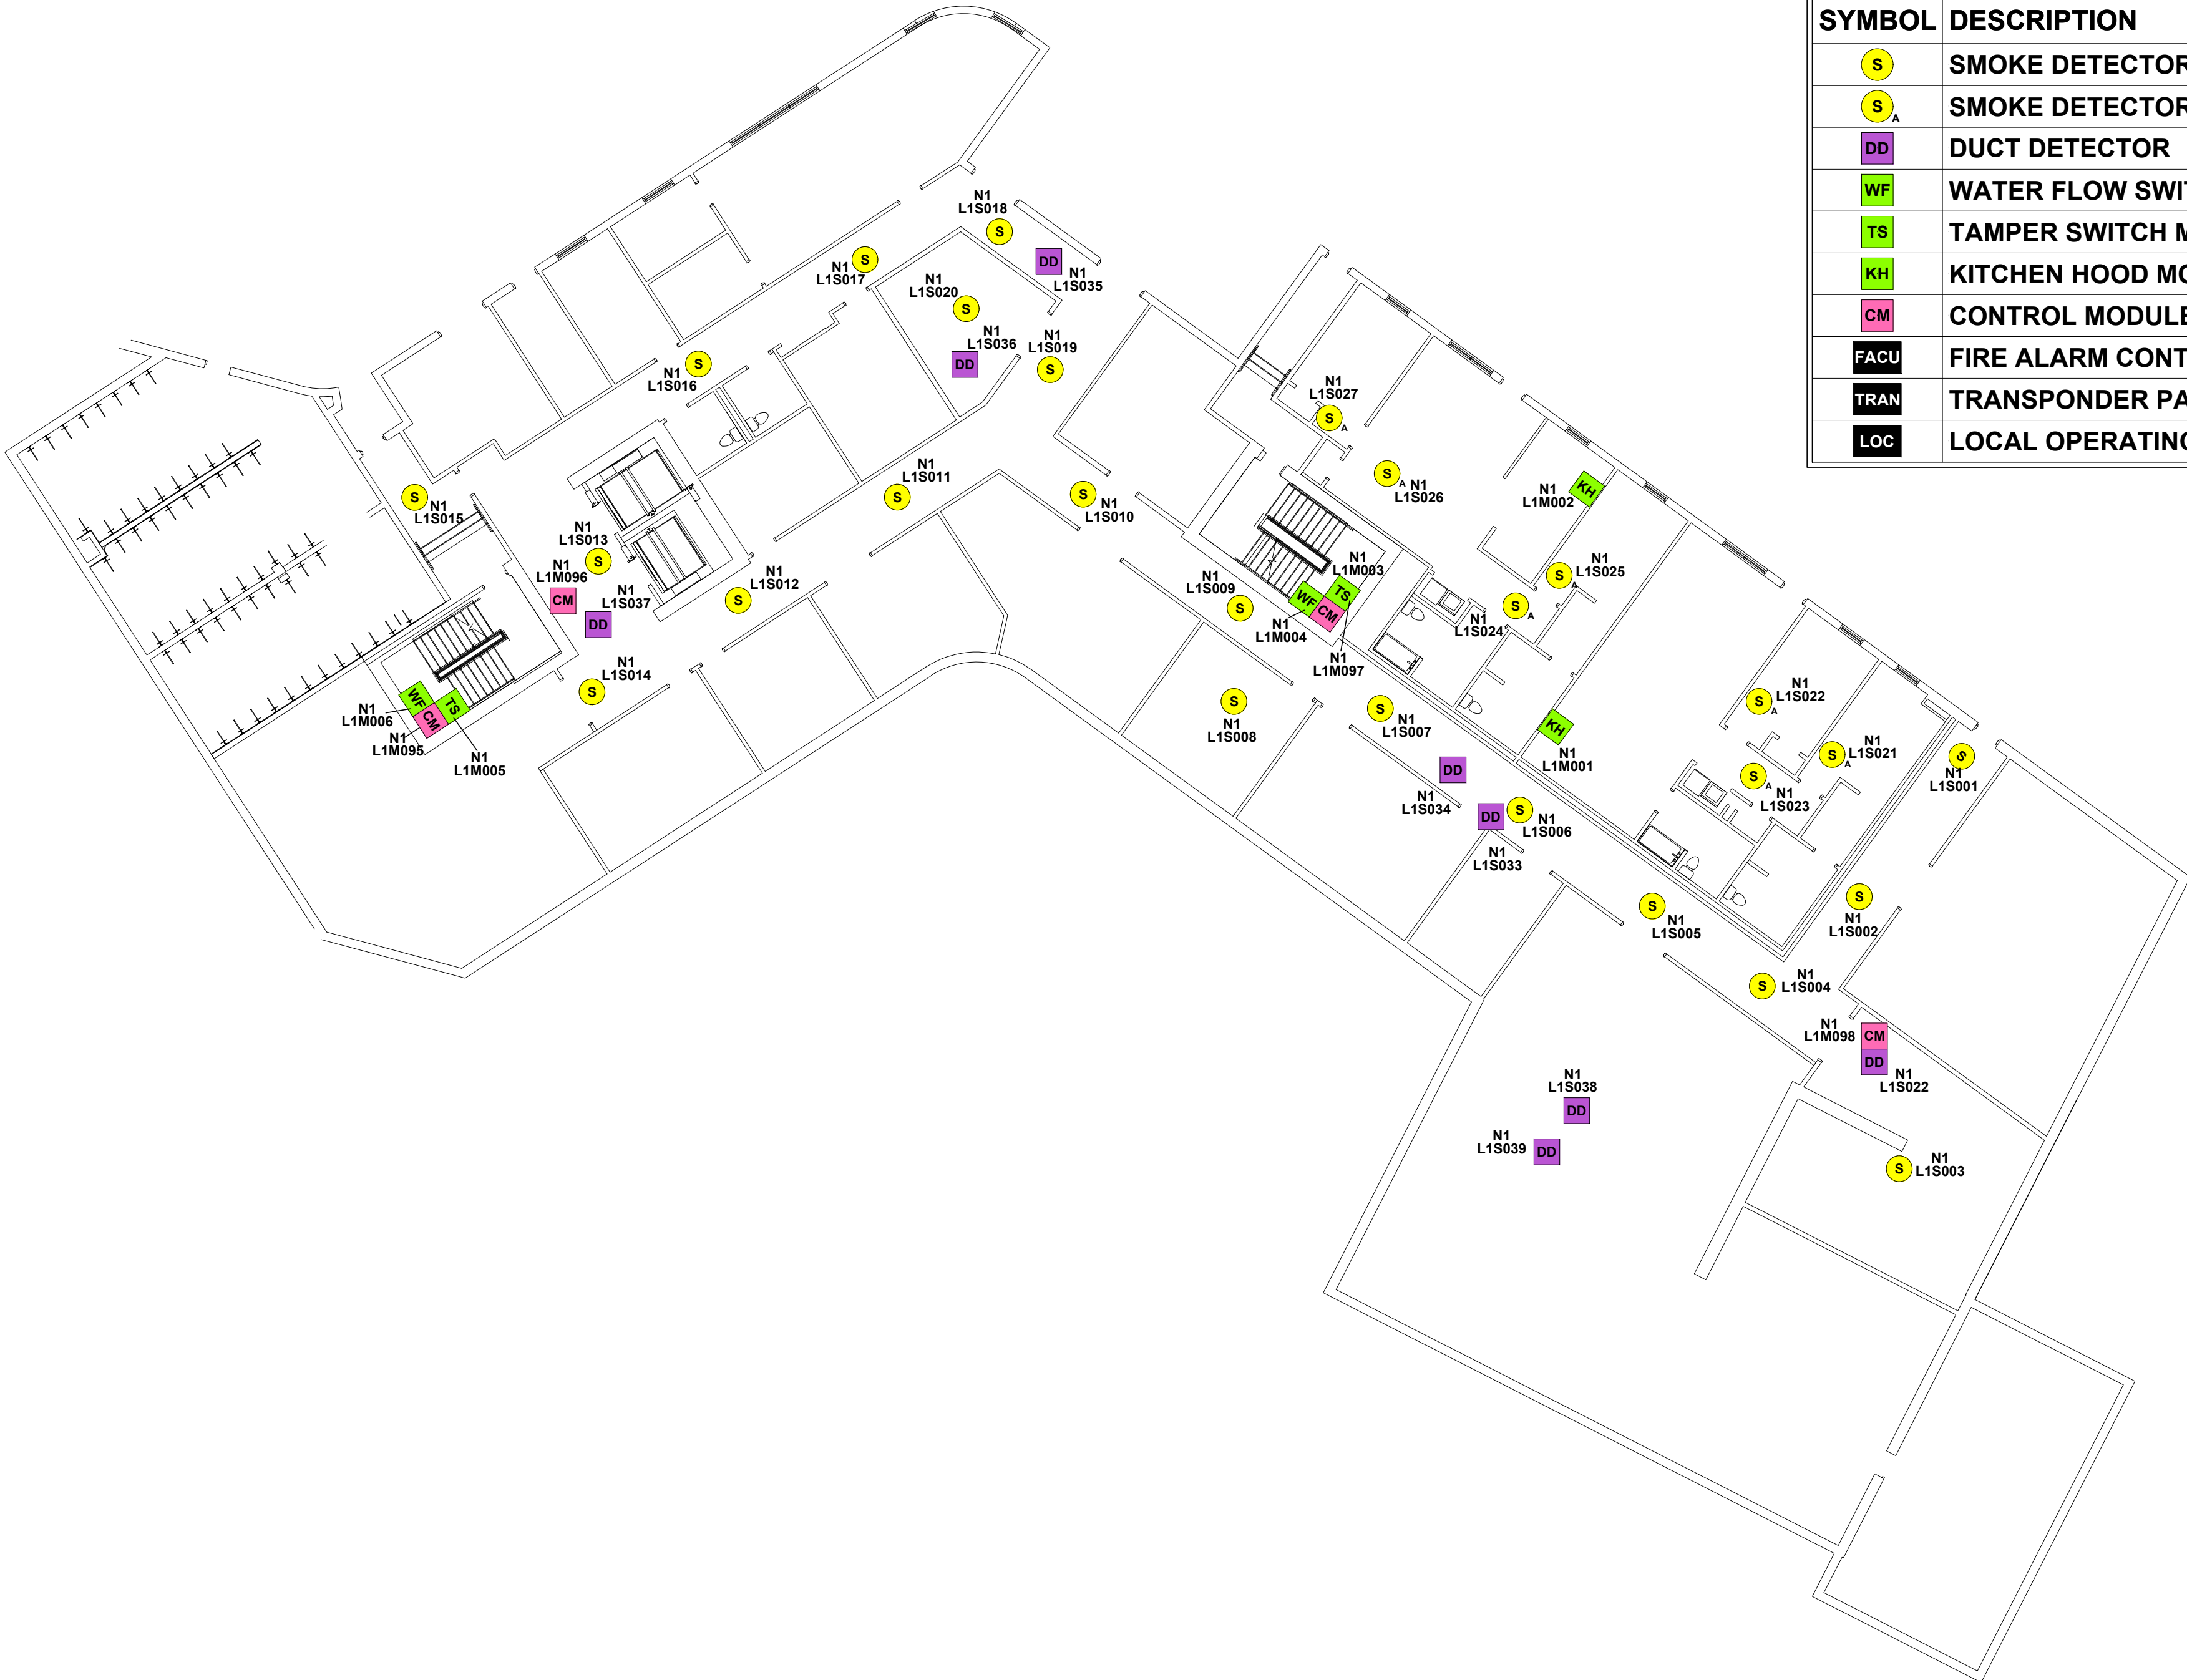

DEVICE LEGEND	
SYMBOL	DESCRIPTION
	SMOKE DETECTOR
	SMOKE DETECTOR- AUDIBLE BASE
	DUCT DETECTOR
	WATER FLOW SWITCH MODULE
	TAMPER SWITCH MODULE
	KITCHEN HOOD MODULE
	CONTROL MODULE
	FIRE ALARM CONTROL UNIT
	TRANSPONDER PANEL
	LOCAL OPERATING CONSOLE

NOTE:
NFS DRAWINGS ARE BASED ON THE PROJECT ARCHITECTURE/ENGINEER (A/E) PLANS AND SPECIFICATIONS FURNISHED TO NFS. A/E IS SOLELY RESPONSIBLE (NOT NFS) FOR THE CORRECT LOCATION (NOT NFS) OF ALL FIRE ALARM DEVICES SHOWN ON THE A/E PLANS. NFS IS NOT RESPONSIBLE FOR THE INFORMATION SHOWN ON THE A/E PLANS.

IMPACT AND PROSPERITY EPICENTER
UNIVERSITY OF UTAH
1755 EAST STUDENT LIFE WAY
SALT LAKE CITY, UTAH 84112
FIRE ALARM SYSTEM


NFS


NELSON FIRE SYSTEMS
801-468-8300

DRAWN BY:	TCT
DESIGNED BY:	XXXX
APPROVED BY:	KK
DATE:	07/29/2023
SCALE:	N.T.S.
PROJECT NO:	XXXX
REVISION NO:	XXXX
DRAWING NAME:	BASEMENT FINAL MAP.DWG

NELSON FIRE SYSTEMS
FLOOR PLAN LEVEL

BASEMENT

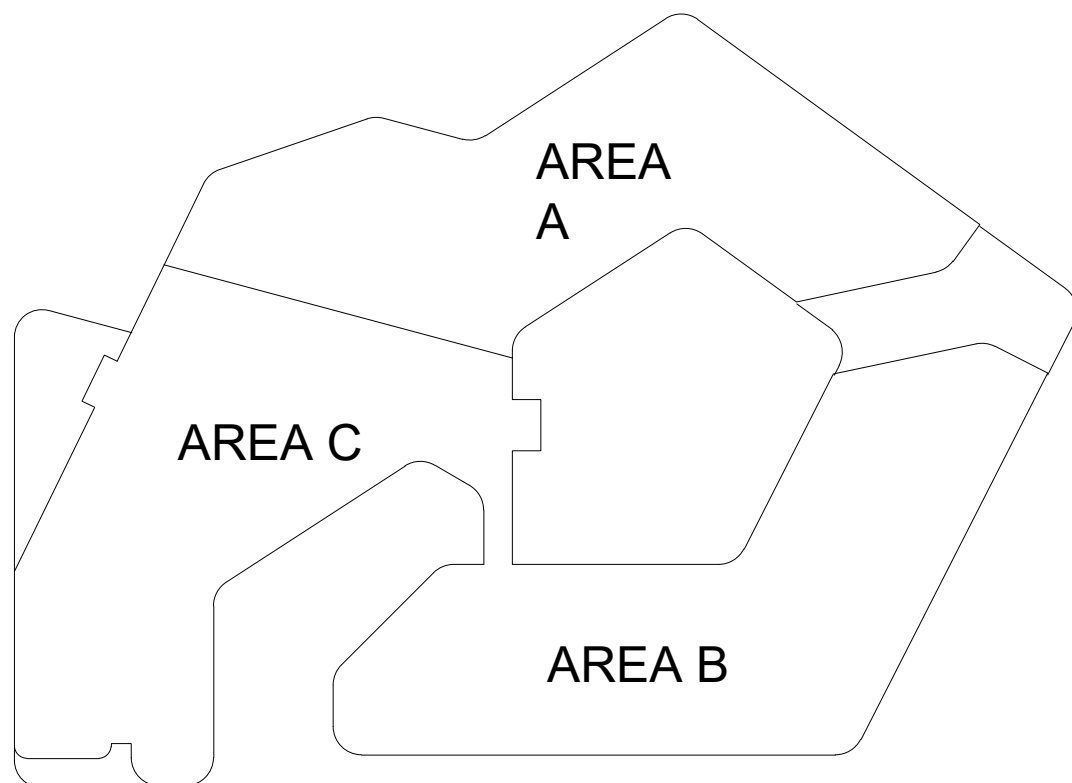

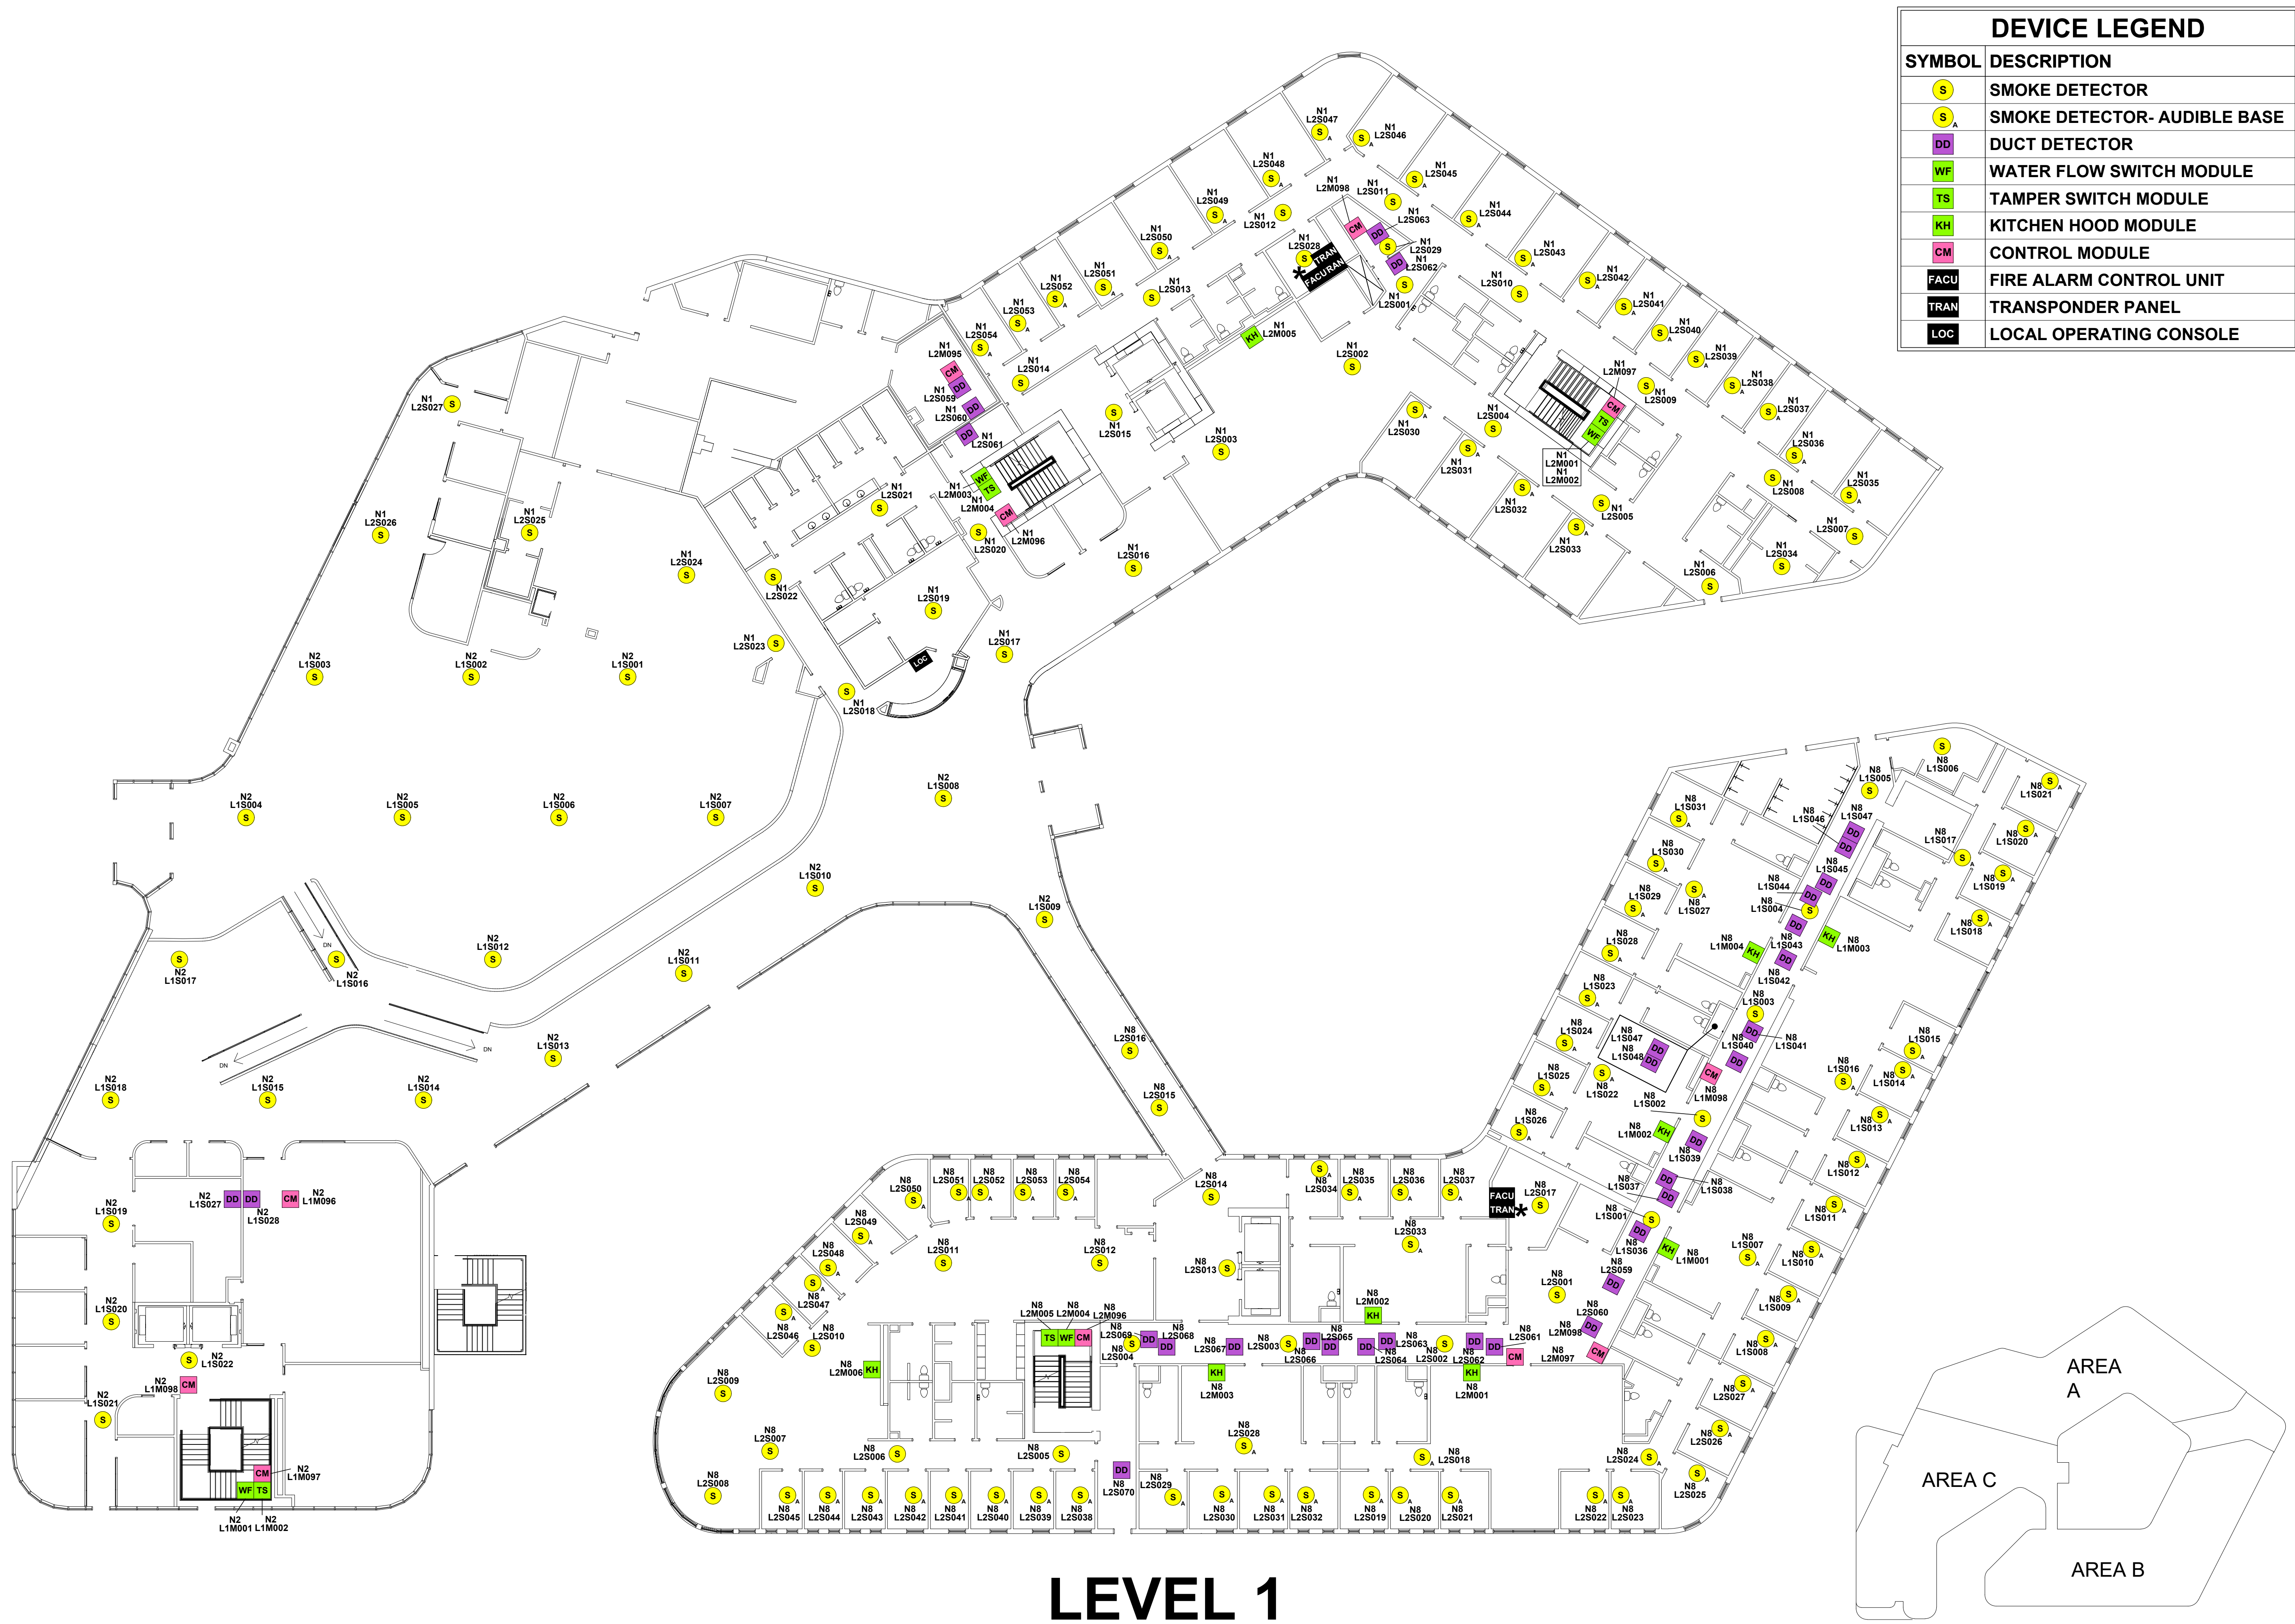

DEVICE LEGEND	
SYMBOL	DESCRIPTION
	SMOKE DETECTOR
	SMOKE DETECTOR- AUDIBLE BASE
	DUCT DETECTOR
	WATER FLOW SWITCH MODULE
	TAMPER SWITCH MODULE
	KITCHEN HOOD MODULE
	CONTROL MODULE
	FIRE ALARM CONTROL UNIT
	TRANSPONDER PANEL
	LOCAL OPERATING CONSOLE

NOTE:
NFS DRAWINGS ARE BASED ON THE PROJECT ARCHITECTURE/ENGINEER (A/E) PLANS AND SPECIFICATIONS FURNISHED TO NFS. A/E IS SOLELY RESPONSIBLE (NOT NFS) FOR THE TYPE, SIZE, LOCATION, AND NUMBER OF ALL FIRE ALARMS, CONTROL PANELS, AND OTHER DEVICES SHOWN ON THE A/E PLANS. NFS DOES NOT GUARANTEE THE ACCURACY OF THE INFORMATION SHOWN ON THE A/E PLANS.



IMPACT AND PROSPERITY EPICENTER
UNIVERSITY OF UTAH
1755 EAST STUDENT LIFE WAY
SALT LAKE CITY, UTAH 84112
FIRE ALARM SYSTEM

NFS
NELSON FIRE SYSTEMS
801-468-8300

DRAWN BY: TCT
DESIGNED BY: XXXX
APPROVED BY: KK
DATE: 07/29/2023
SCALE: N.T.S.
PROJECT NO: XXXX
REVISION NO: XXXX
DRAWING NAME:
LEVEL 1 FINAL MAP.DWG

NELSON FIRE SYSTEMS
FLOOR PLAN LEVEL

PAGE:
FINAL MAP

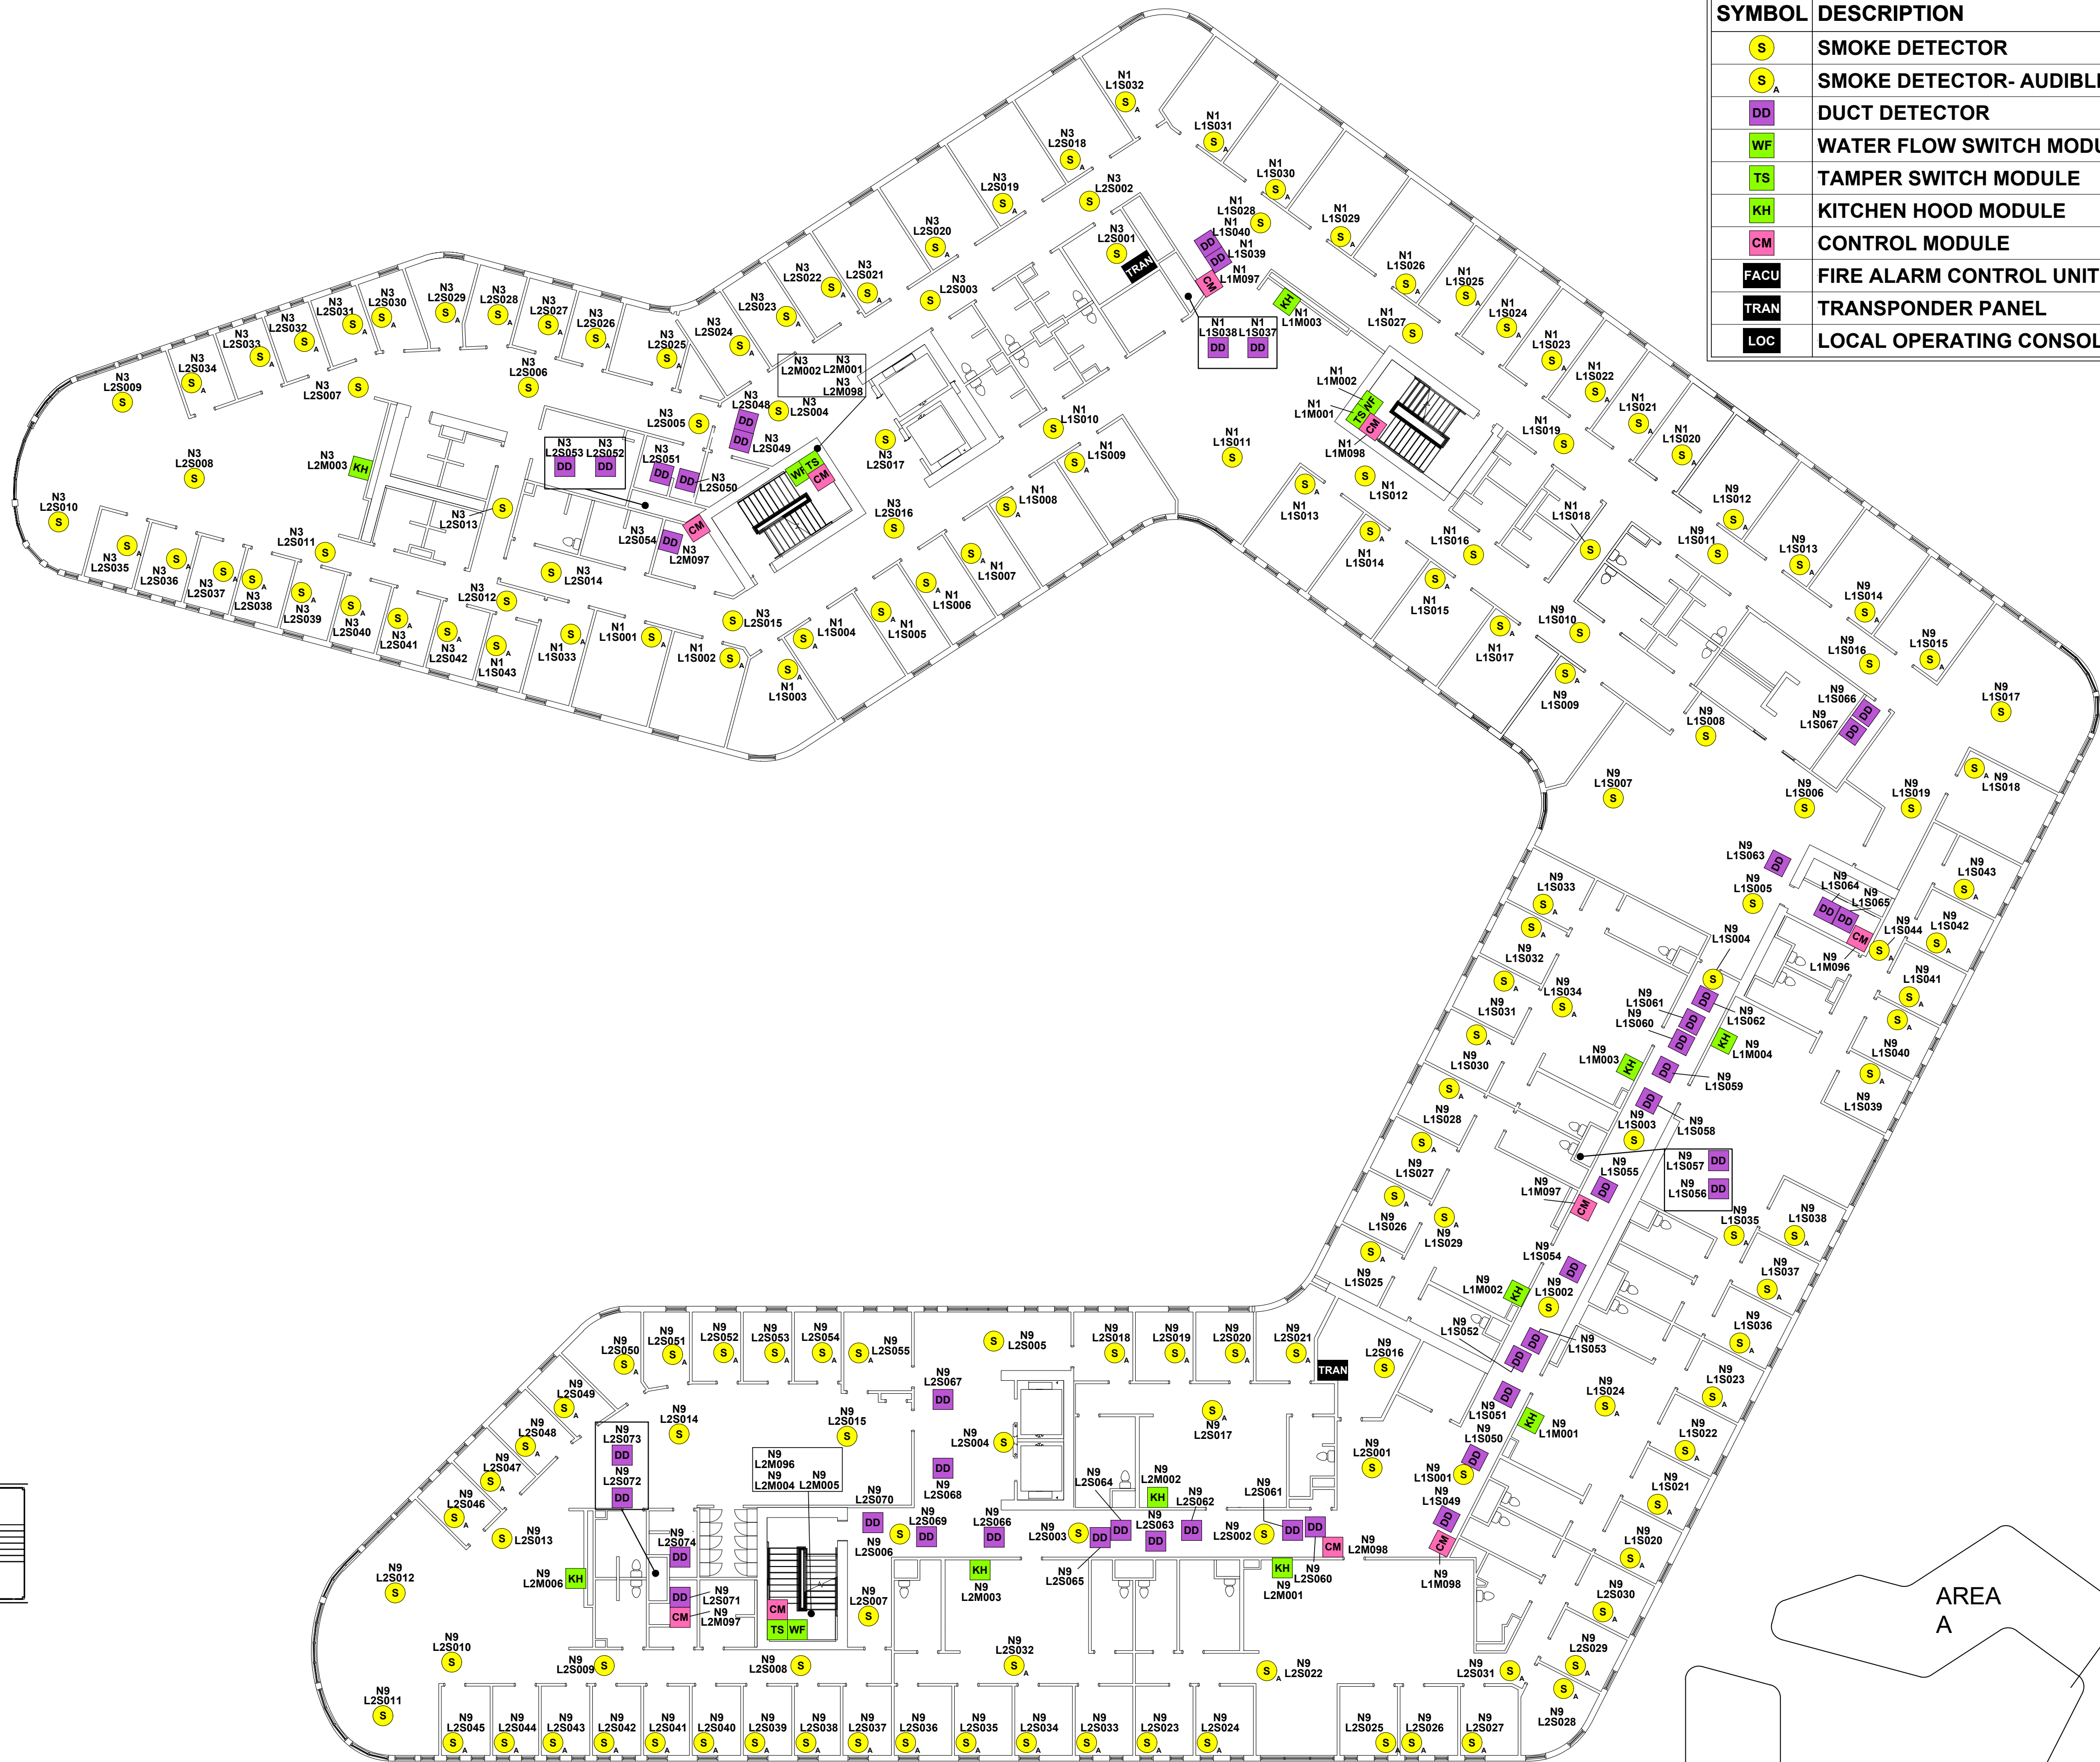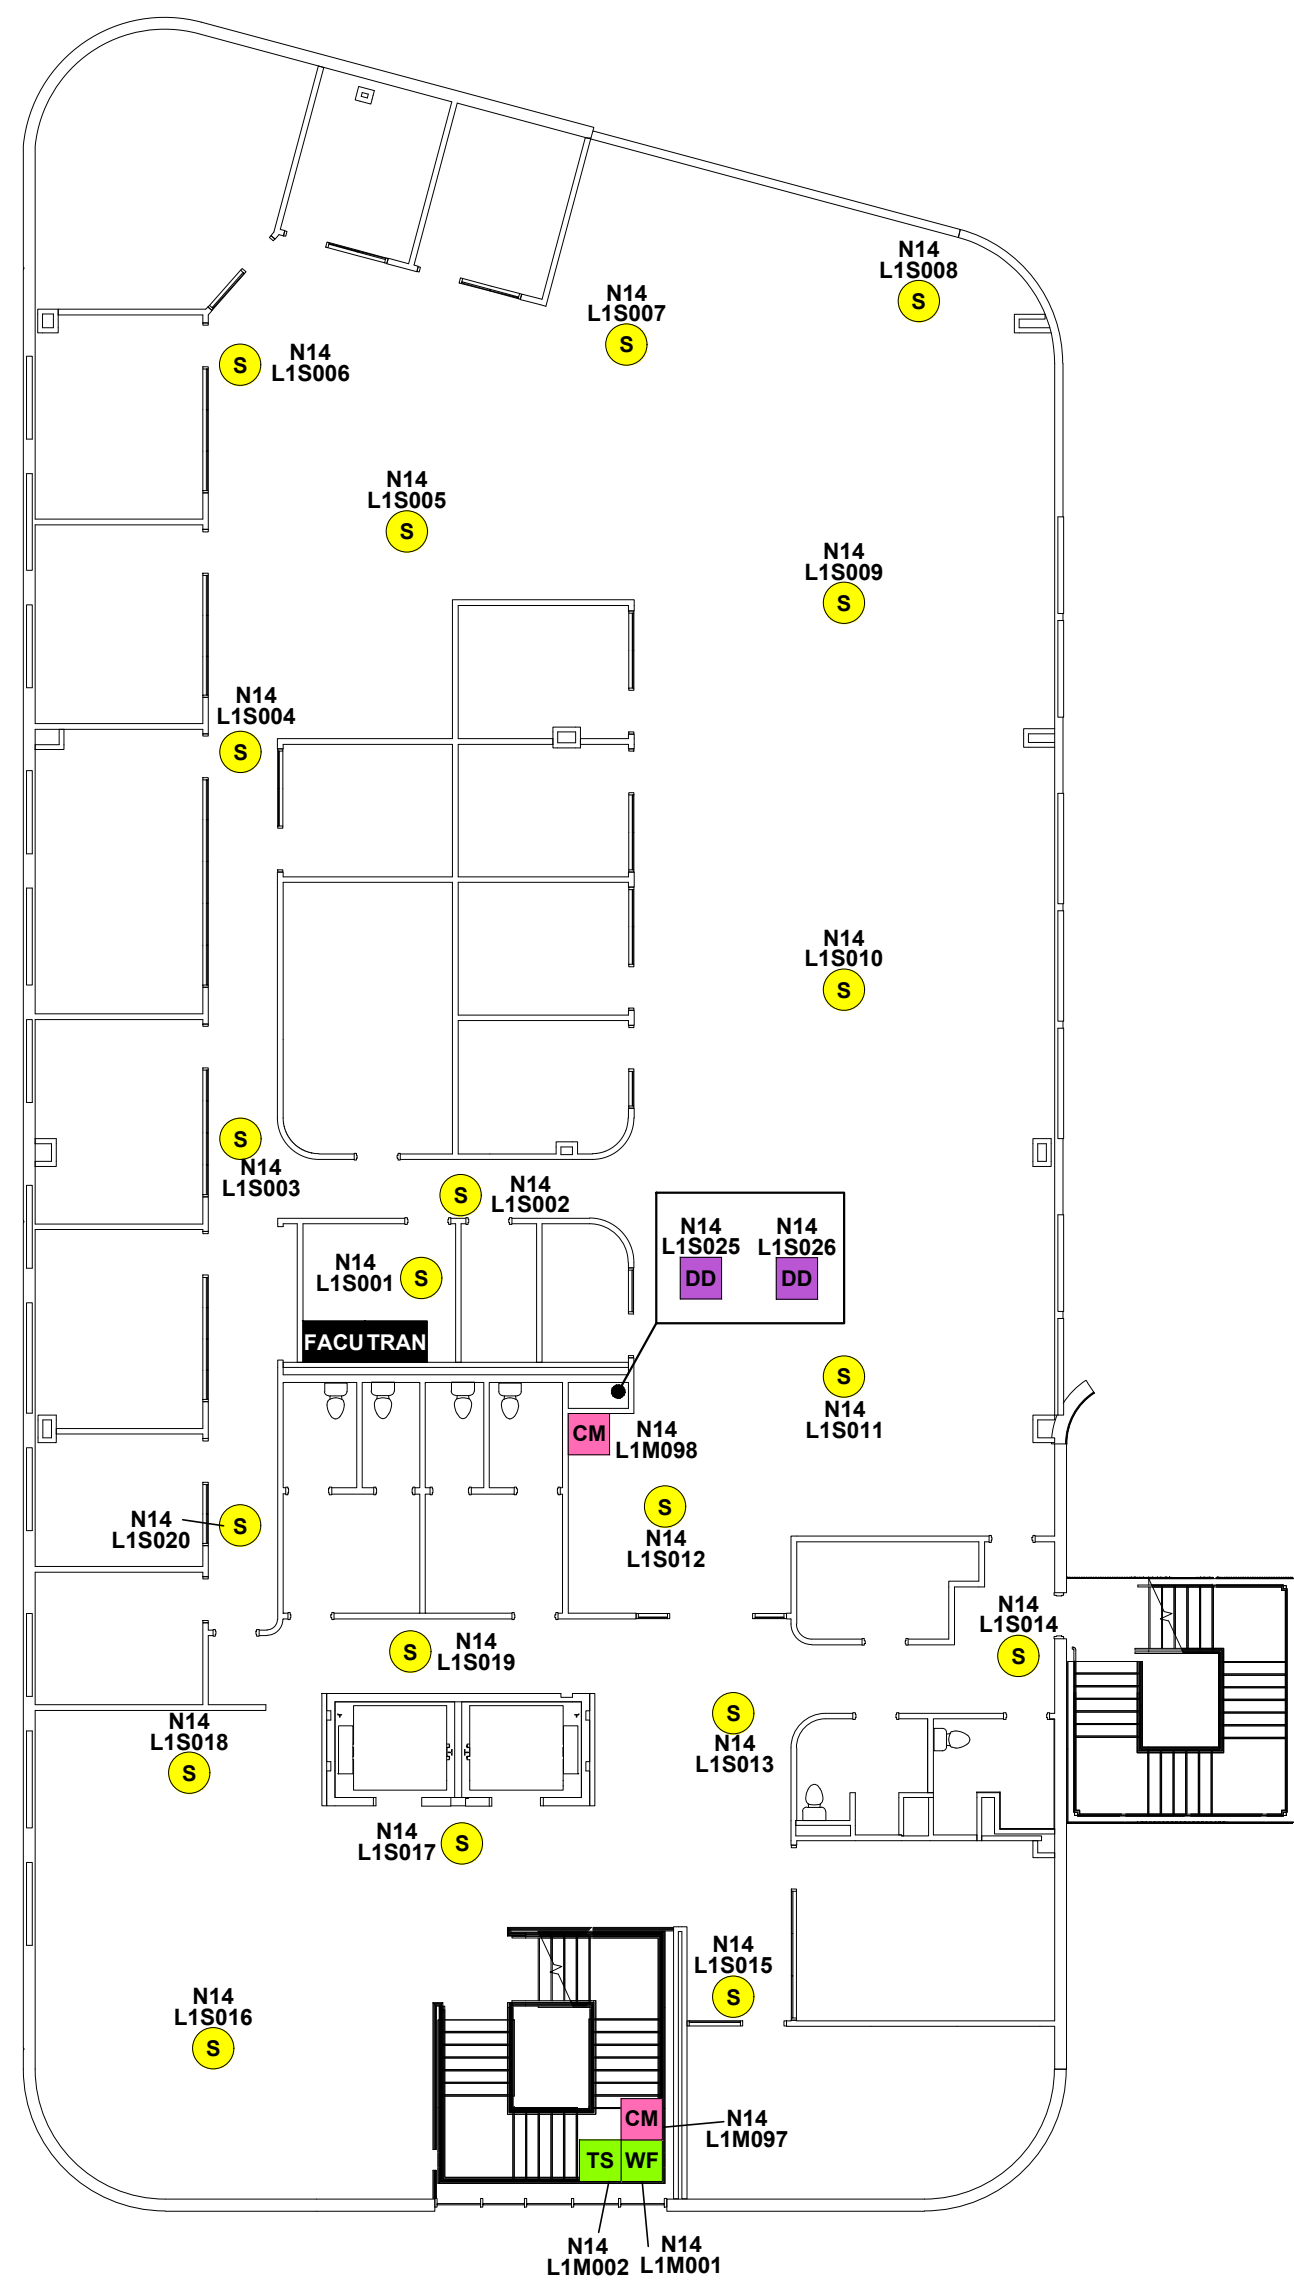

DEVICE LEGEND	
SYMBOL	DESCRIPTION
	SMOKE DETECTOR
	SMOKE DETECTOR- AUDIBLE BASE
	DUCT DETECTOR
	WATER FLOW SWITCH MODULE
	TAMPER SWITCH MODULE
	KITCHEN HOOD MODULE
	CONTROL MODULE
	FIRE ALARM CONTROL UNIT
	TRANSPONDER PANEL
	LOCAL OPERATING CONSOLE

W
N
S
E

NOTE:
NFS DRAWINGS ARE BASED ON THE PROJECT
ARCHITECTURE/ENGINEER (A/E) PLANS AND
SPECIFICATIONS FURNISHED TO NFS. A/E IS
SOLELY RESPONSIBLE (NOT NFS) FOR THE
TYPE, SIZE, LOCATION, SUITABILITY OF
ALL FIRE ALARMS, CONTROL PANELS, AND
OTHER DEVICES SHOWN ON THE A/E PLANS.
NFS DOES NOT GUARANTEE THE
CORRECTNESS OF THE INFORMATION SHOWN
ON THE A/E PLANS.

IMPACT AND PROSPERITY EPICENTER
UNIVERSITY OF UTAH
1755 EAST STUDENT LIFE WAY
SALT LAKE CITY, UTAH 84112
FIRE ALARM SYSTEM


NFS
NELSON FIRE SYSTEMS
801-468-8300


DRAWN BY: TCT
DESIGNED BY: XXXX
APPROVED BY: KK
DATE: 07/29/2023
SCALE: N.T.S.
PROJECT NO: XXXX
REVISION NO: XXXX
DRAWING NAME:
LEVEL 2 FINAL MAP.DWG

NELSON FIRE SYSTEMS
FLOOR PLAN LEVEL

PAGE:
FINAL MAP

LEVEL 2

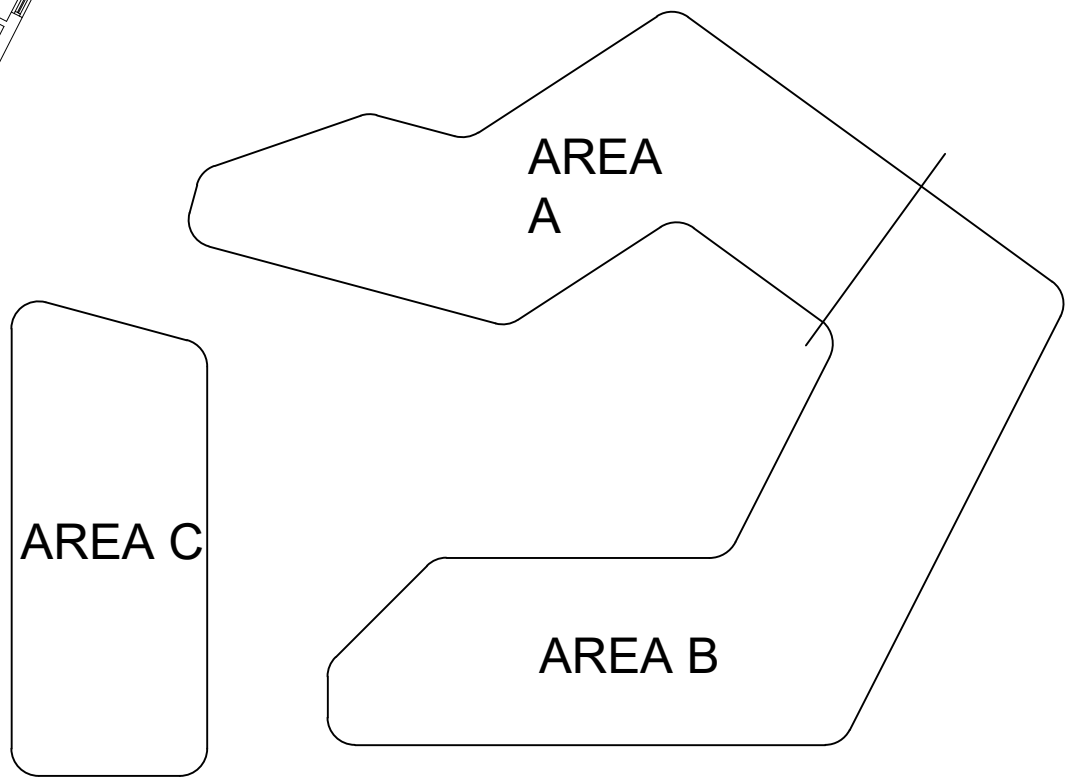

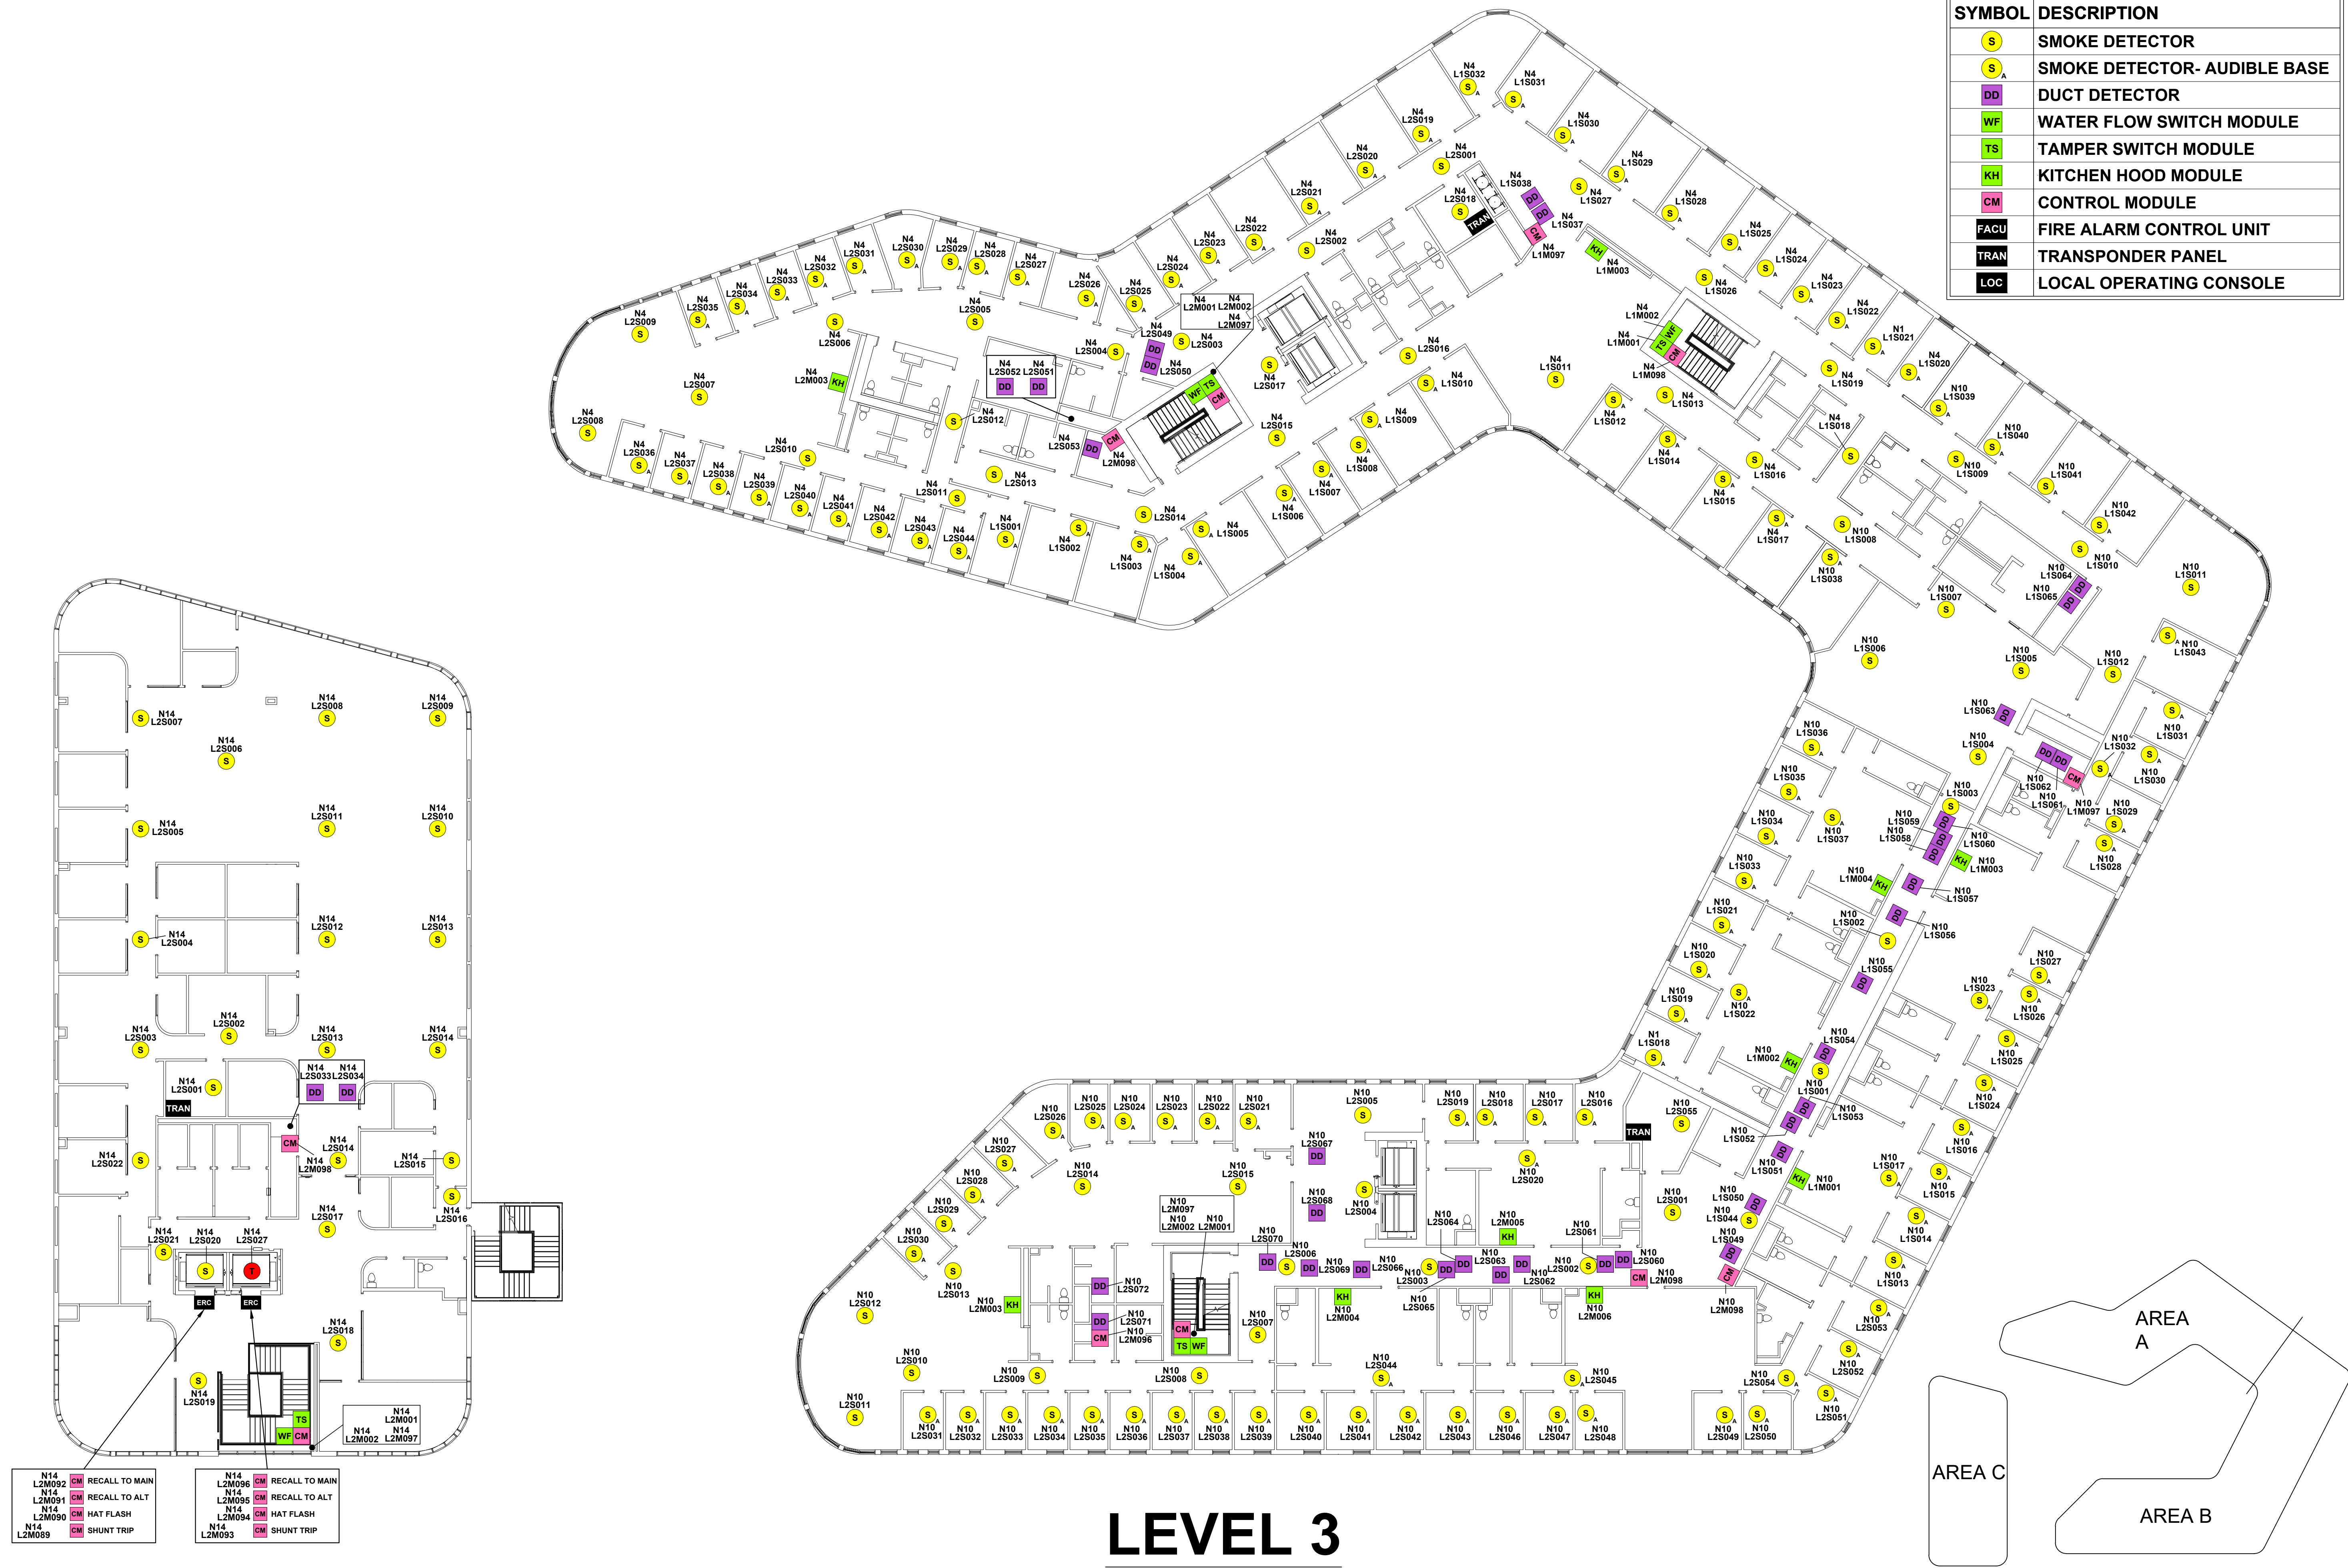

DEVICE LEGEND	
SYMBOL	DESCRIPTION
	SMOKE DETECTOR
	SMOKE DETECTOR- AUDIBLE BASE
	DUCT DETECTOR
	WATER FLOW SWITCH MODULE
	TAMPER SWITCH MODULE
	KITCHEN HOOD MODULE
	CONTROL MODULE
	FIRE ALARM CONTROL UNIT
	TRANSPONDER PANEL
	LOCAL OPERATING CONSOLE

NOTE:
NFS DRAWINGS ARE BASED ON THE PROJECT
ARCHITECTURE/ENGINEER (A/E) PLANS AND
SPECIFICATIONS FURNISHED TO NFS. A/E IS
SOLELY RESPONSIBLE (NOT NFS) FOR THE
TYPE, SIZE, LOCATION, AND NUMBER OF
ALL DEVICES SHOWN ON THE A/E PLANS.
OTHER DEVICES SHOWN ON THE A/E PLANS
WIRING DATA, AND CONTROL PANELS ARE NOT
RESPONSIBLE FOR THE INFORMATION SHOWN
ON THE A/E PLANS.

IMPACT AND PROSPERITY EPICENTER
UNIVERSITY OF UTAH
1755 EAST STUDENT LIFE WAY
SALT LAKE CITY, UTAH 84112
FIRE ALARM SYSTEM

NFS
NELSON FIRE SYSTEMS
801-468-8300

DRAWN BY: TCT
DESIGNED BY: XXXX
APPROVED BY: KK
DATE: 07/29/2023
SCALE: N.T.S.
PROJECT NO: XXXX
REVISION NO: XXXX
DRAWING NAME:
LEVEL 3 FINAL MAP.DWG

NELSON FIRE SYSTEMS
FLOOR PLAN LEVEL

PAGE:
FINAL MAP

AREA C ROOF

LEVEL 4

DEVICE LEGEND	
SYMBOL	DESCRIPTION
	SMOKE DETECTOR
	SMOKE DETECTOR- AUDIBLE BASE
	DUCT DETECTOR
	WATER FLOW SWITCH MODULE
	TAMPER SWITCH MODULE
	KITCHEN HOOD MODULE
	CONTROL MODULE
	FIRE ALARM CONTROL UNIT
	TRANSPONDER PANEL
	LOCAL OPERATING CONSOLE

W
N
S
E

NOTE: NFS DRAWINGS ARE BASED ON THE PROJECT ARCHITECTURE (ENGINEER (A/E) PLANS AND SPECIFICATIONS FURNISHED TO NFS. A/E IS SOLELY RESPONSIBLE (NOT NFS) FOR THE TYPE, SIZE, LOCATION, AND NUMBER OF ALL FIRE ALARMS, CONTROL PANELS, AND OTHER DEVICES SHOWN ON THE A/E PLANS. NFS WILL NOT BE RESPONSIBLE FOR THE TYPE, SIZE, LOCATION, AND NUMBER OF DEVICES AND CONTROL PANELS NOT SHOWN ON THE A/E PLANS.

IMPACT AND PROSPERITY EPICENTER
UNIVERSITY OF UTAH
1755 EAST STUDENT LIFE WAY
SALT LAKE CITY, UTAH 84112
FIRE ALARM SYSTEM

NFS

NELSON FIRE SYSTEMS
801-468-8300

DRAWN BY: TCT

DESIGNED BY: XXXX

APPROVED BY: KK

DATE: 07/29/2023

SCALE: N.T.S.

PROJECT NO: XXXX

REVISION NO: XXXX


DRAWING NAME: LEVEL 4 FINAL MAP.DWG

NELSON FIRE SYSTEMS

FLOOR PLAN LEVEL

PAGE:

FINAL MAP

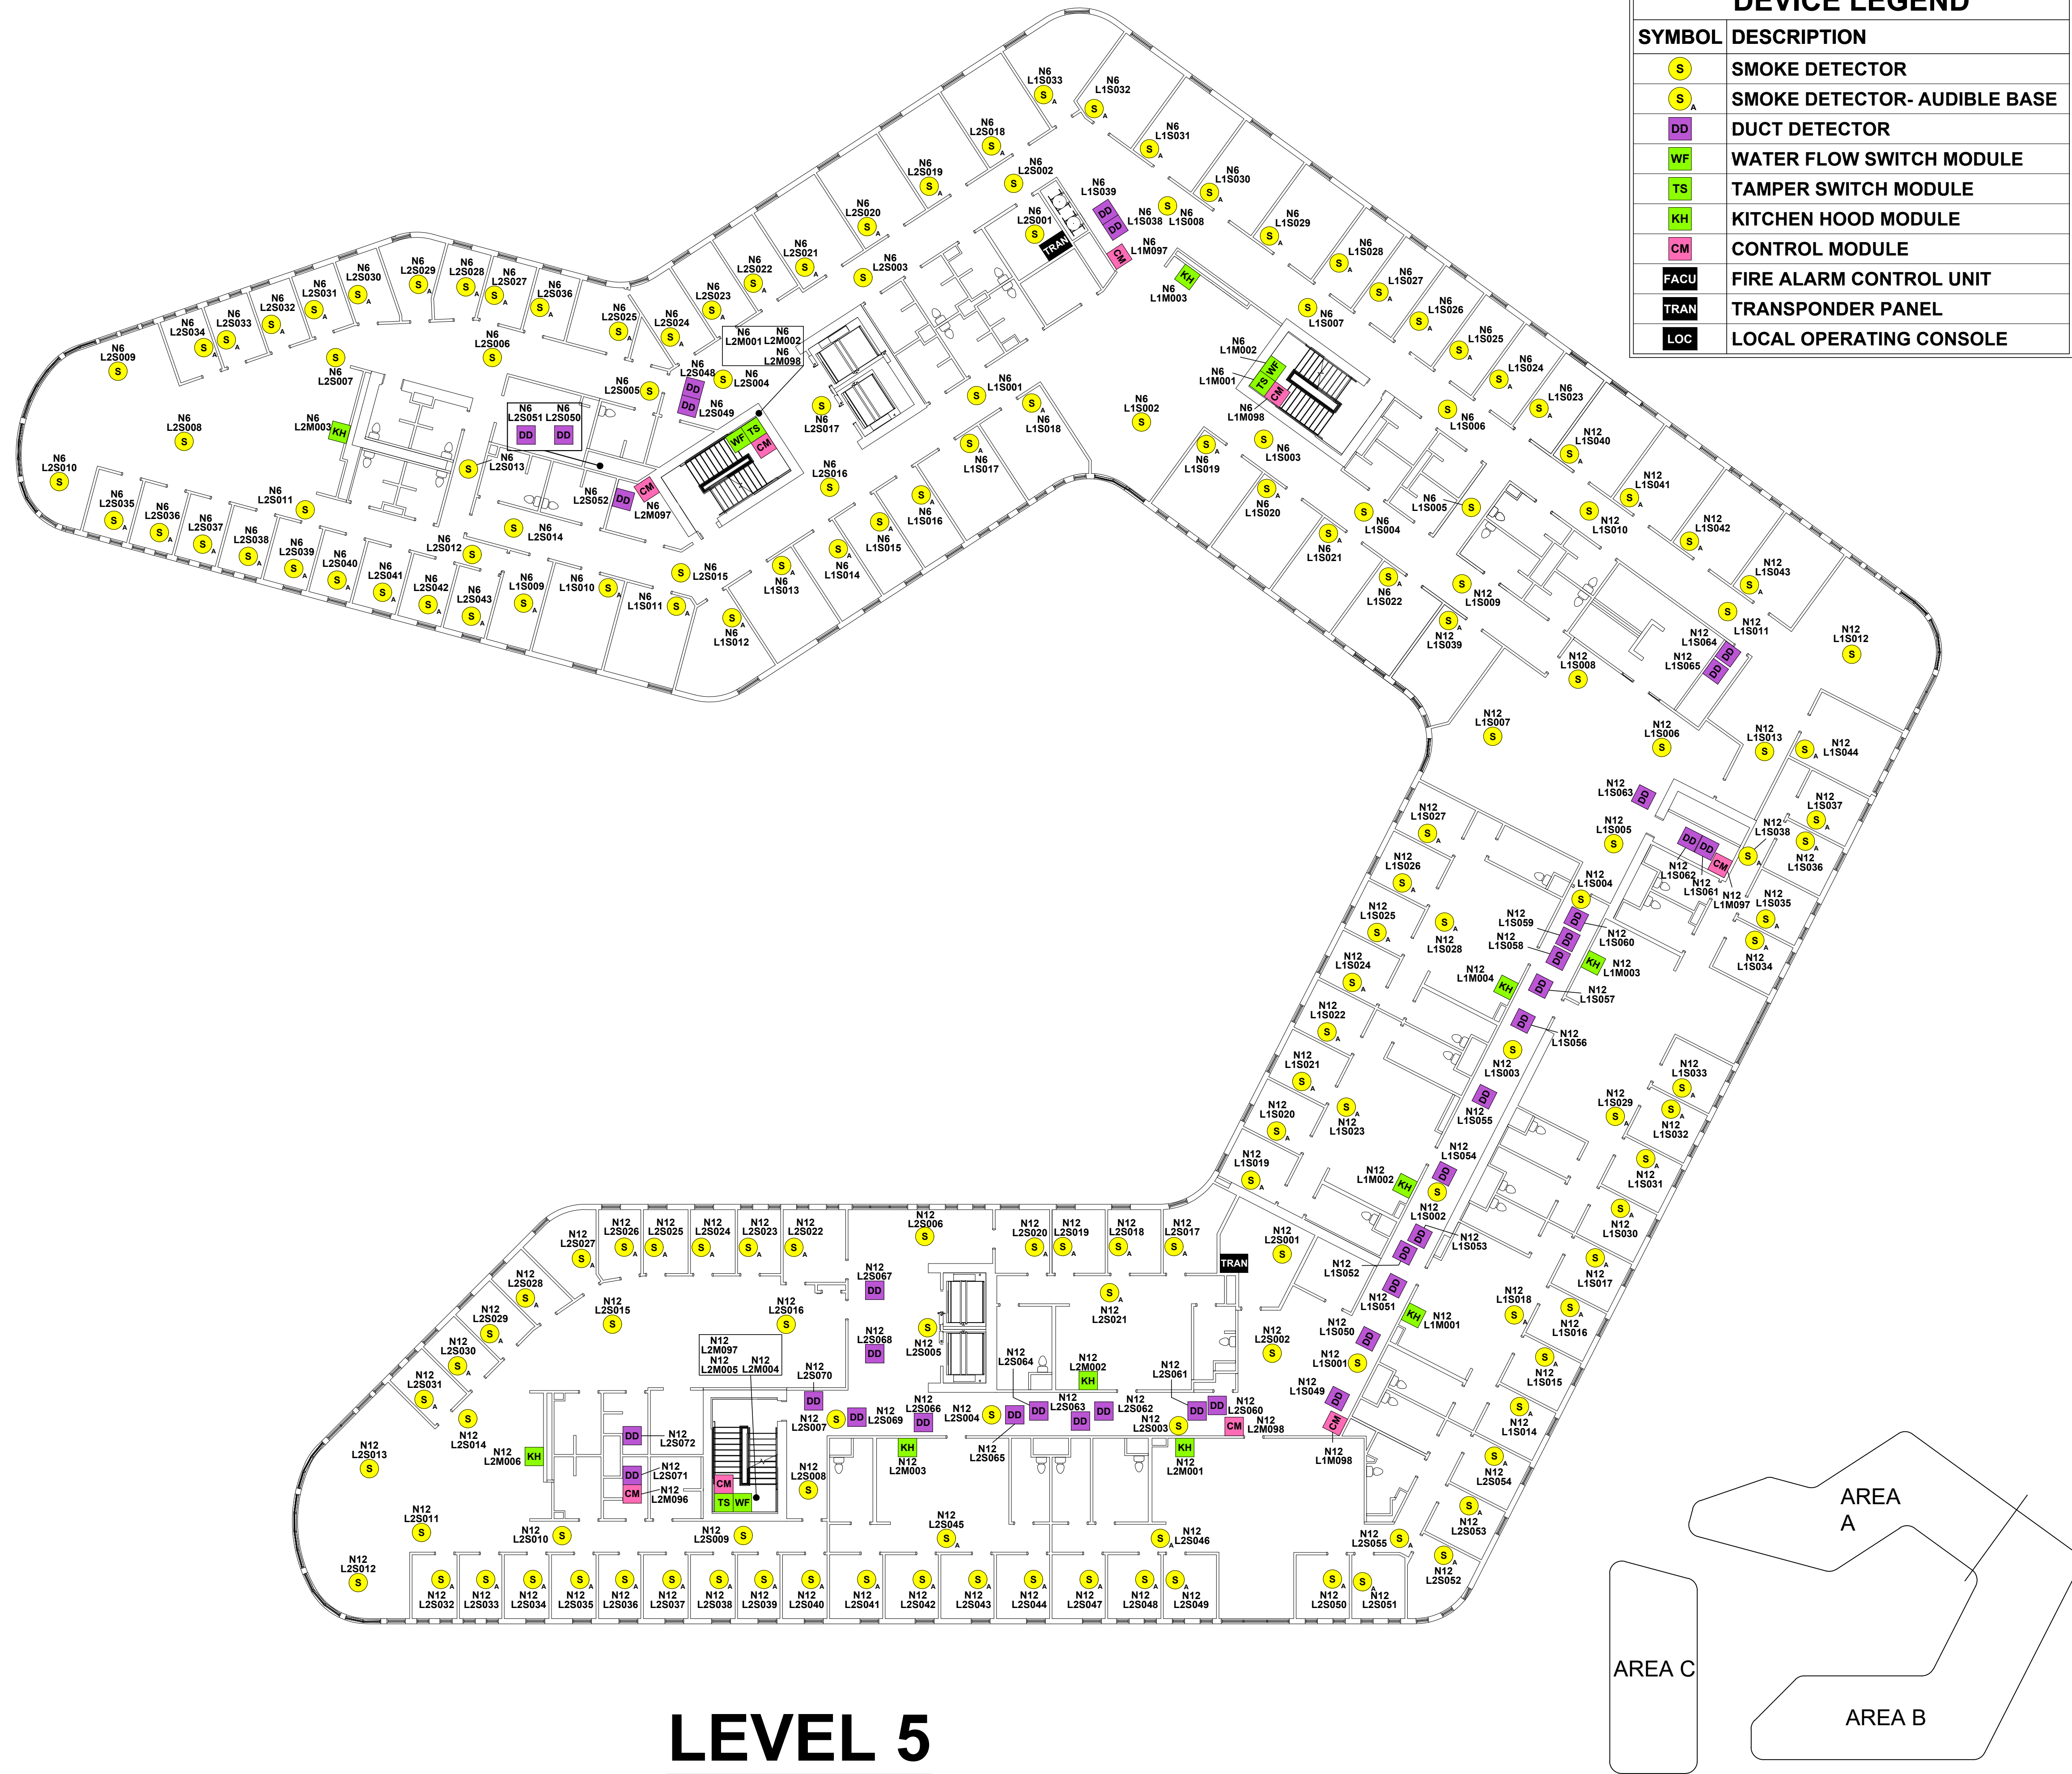

DEVICE LEGEND	
SYMBOL	DESCRIPTION
	SMOKE DETECTOR
	SMOKE DETECTOR- AUDIBLE BASE
	DUCT DETECTOR
	WATER FLOW SWITCH MODULE
	TAMPER SWITCH MODULE
	KITCHEN HOOD MODULE
	CONTROL MODULE
	FIRE ALARM CONTROL UNIT
	TRANSPONDER PANEL
	LOCAL OPERATING CONSOLE

W
N
S
E

NOTE: NFS DRAWINGS ARE BASED ON THE PROJECT ARCHITECTURE (ENGINEER (A/E) PLANS AND SPECIFICATIONS FURNISHED TO NFS. A/E IS SOLELY RESPONSIBLE (NOT NFS) FOR THE TYPE, SIZE, LOCATION, AND AMOUNT OF ALL FIRE ALARM, CONTROL PANELS, AND OTHER DEVICES SHOWN ON THE A/E PLANS. NFS IS NOT RESPONSIBLE FOR THE INFORMATION SHOWN ON THE A/E PLANS.

IMPACT AND PROSPERITY EPICENTER
UNIVERSITY OF UTAH
1755 EAST STUDENT LIFE WAY
SALT LAKE CITY, UTAH 84112
FIRE ALARM SYSTEM

NFS
NELSON FIRE SYSTEMS
801-468-8300

DRAWN BY:	TCT
DESIGNED BY:	XXXX
APPROVED BY:	KK
DATE:	07/29/2023
SCALE:	N.T.S.
PROJECT NO:	XXXX
REVISION NO:	XXXX
DRAWING NAME:	LEVEL 5 FINAL MAP.DWG

ROOF AREA A

ROOF AREA B

LEVEL 6

DEVICE LEGEND	
SYMBOL	DESCRIPTION
S	SMOKE DETECTOR
S _A	SMOKE DETECTOR- AUDIBLE BASE
DD	DUCT DETECTOR
WF	WATER FLOW SWITCH MODULE
TS	TAMPER SWITCH MODULE
KH	KITCHEN HOOD MODULE
CM	CONTROL MODULE
FACU	FIRE ALARM CONTROL UNIT
TRAN	TRANSPONDER PANEL
LOC	LOCAL OPERATING CONSOLE

W
N
S
E

NOTE: NFS DRAWINGS ARE BASED ON THE PROJECT ARCHITECTURE (ENGINEER (A/E) PLANS AND SPECIFICATIONS FURNISHED TO NFS. A/E IS SOLELY RESPONSIBLE (NOT NFS) FOR THE TYPE, SIZE, LOCATION, AND STABILITY OF ALL PRELIMINARY CONTROL PANELS, AND OPERATING DEVICES SHOWN ON THE A/E PLANS. NFS DOES NOT GUARANTEE THE ACCURACY OF THE INFORMATION SHOWN ON THE A/E PLANS.

IMPACT AND PROSPERITY EPICENTER
UNIVERSITY OF UTAH
1755 EAST STUDENT LIFE WAY
SALT LAKE CITY, UTAH 84112
FIRE ALARM SYSTEM

NFS
NELSON FIRE SYSTEMS
801-468-8300

DRAWN BY: TCT
DESIGNED BY: XXXX
APPROVED BY: KK
DATE: 07/29/2023
SCALE: N.T.S.
PROJECT NO: XXXX
REVISION NO: XXXX
DRAWING NAME:
LEVEL 6 FINAL MAP.DWG

NELSON FIRE SYSTEMS
FLOOR PLAN LEVEL

PAGE:
FINAL MAP