



NFS
NELSON FIRE SYSTEMS
801-484-9992

LEGEND

- ⊙ SMOKE DETECTOR
- ⊙ HEAT DETECTOR
- MANUAL PULL STATION
- ▣ DUCT DETECTOR
- ▣ WATER FLOW SWITCH
- ▣ TAMPER SWITCH

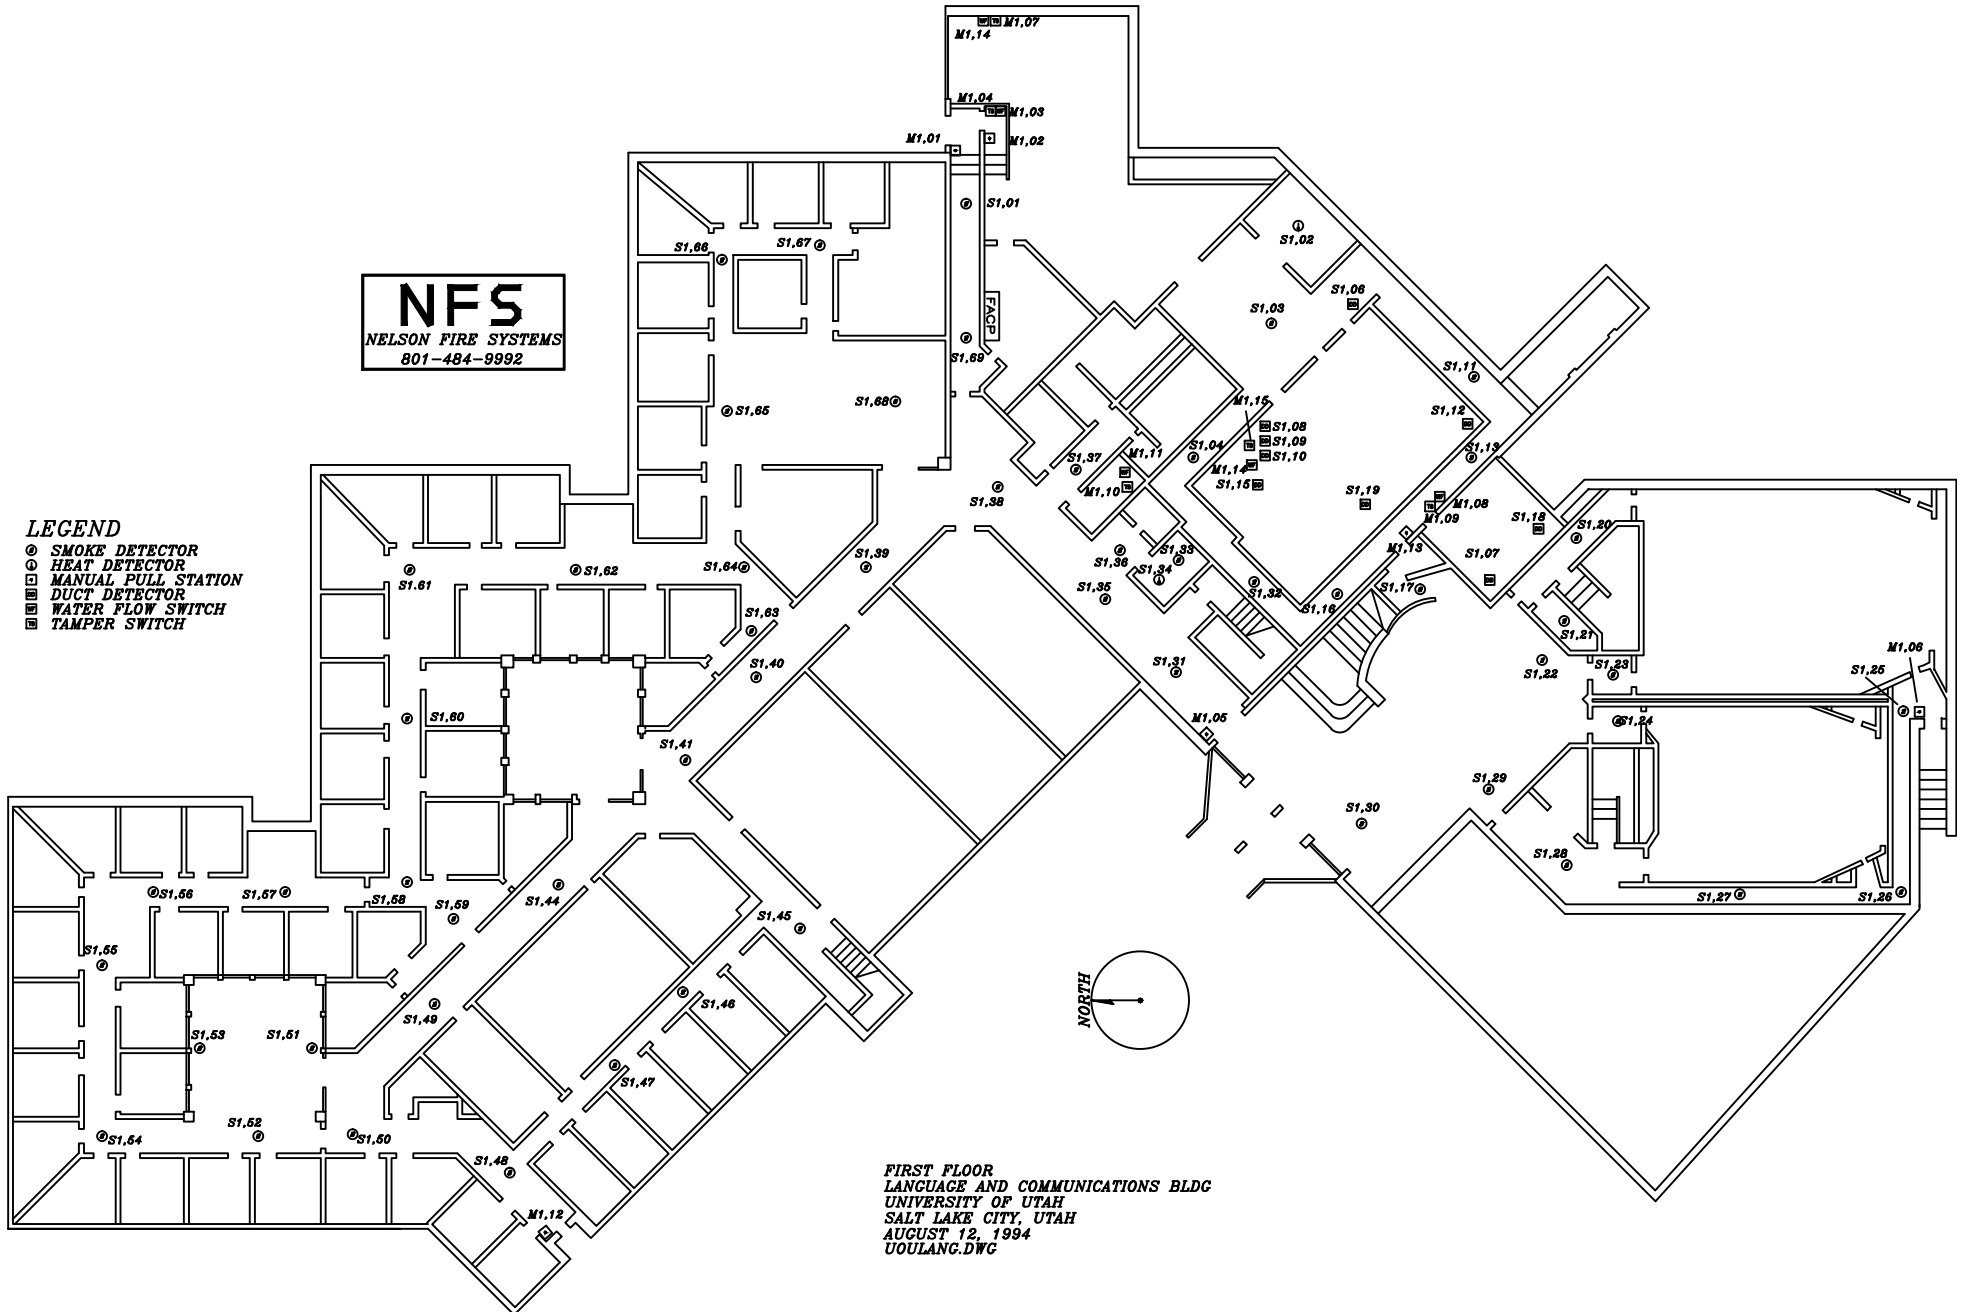


FIRST FLOOR
LANGUAGE AND COMMUNICATIONS BLDG
UNIVERSITY OF UTAH
SALT LAKE CITY, UTAH
AUGUST 12, 1994
UOULANG.DWG

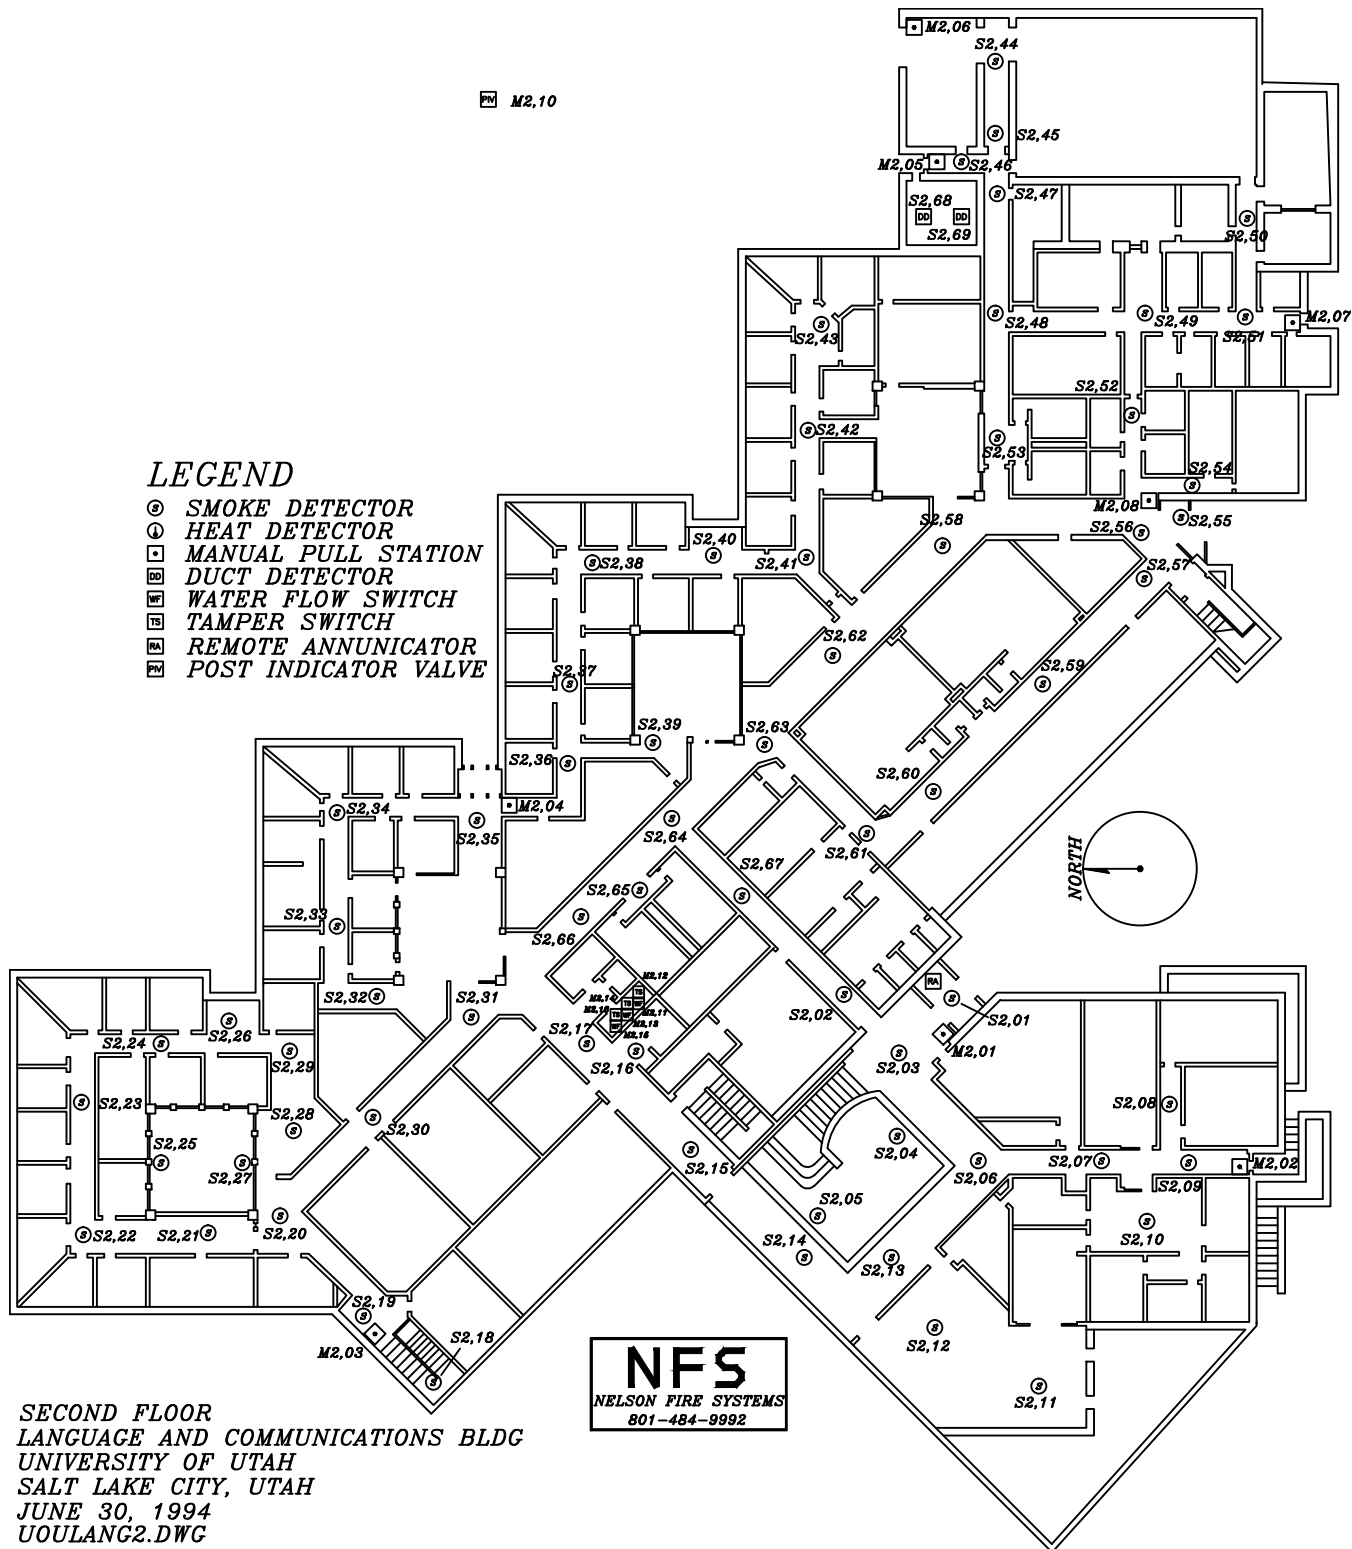

LEGEND

- Ⓢ SMOKE DETECTOR
- Ⓛ HEAT DETECTOR
- MANUAL PULL STATION
- WF WATER FLOW SWITCH
- TS TAMPER SWITCH

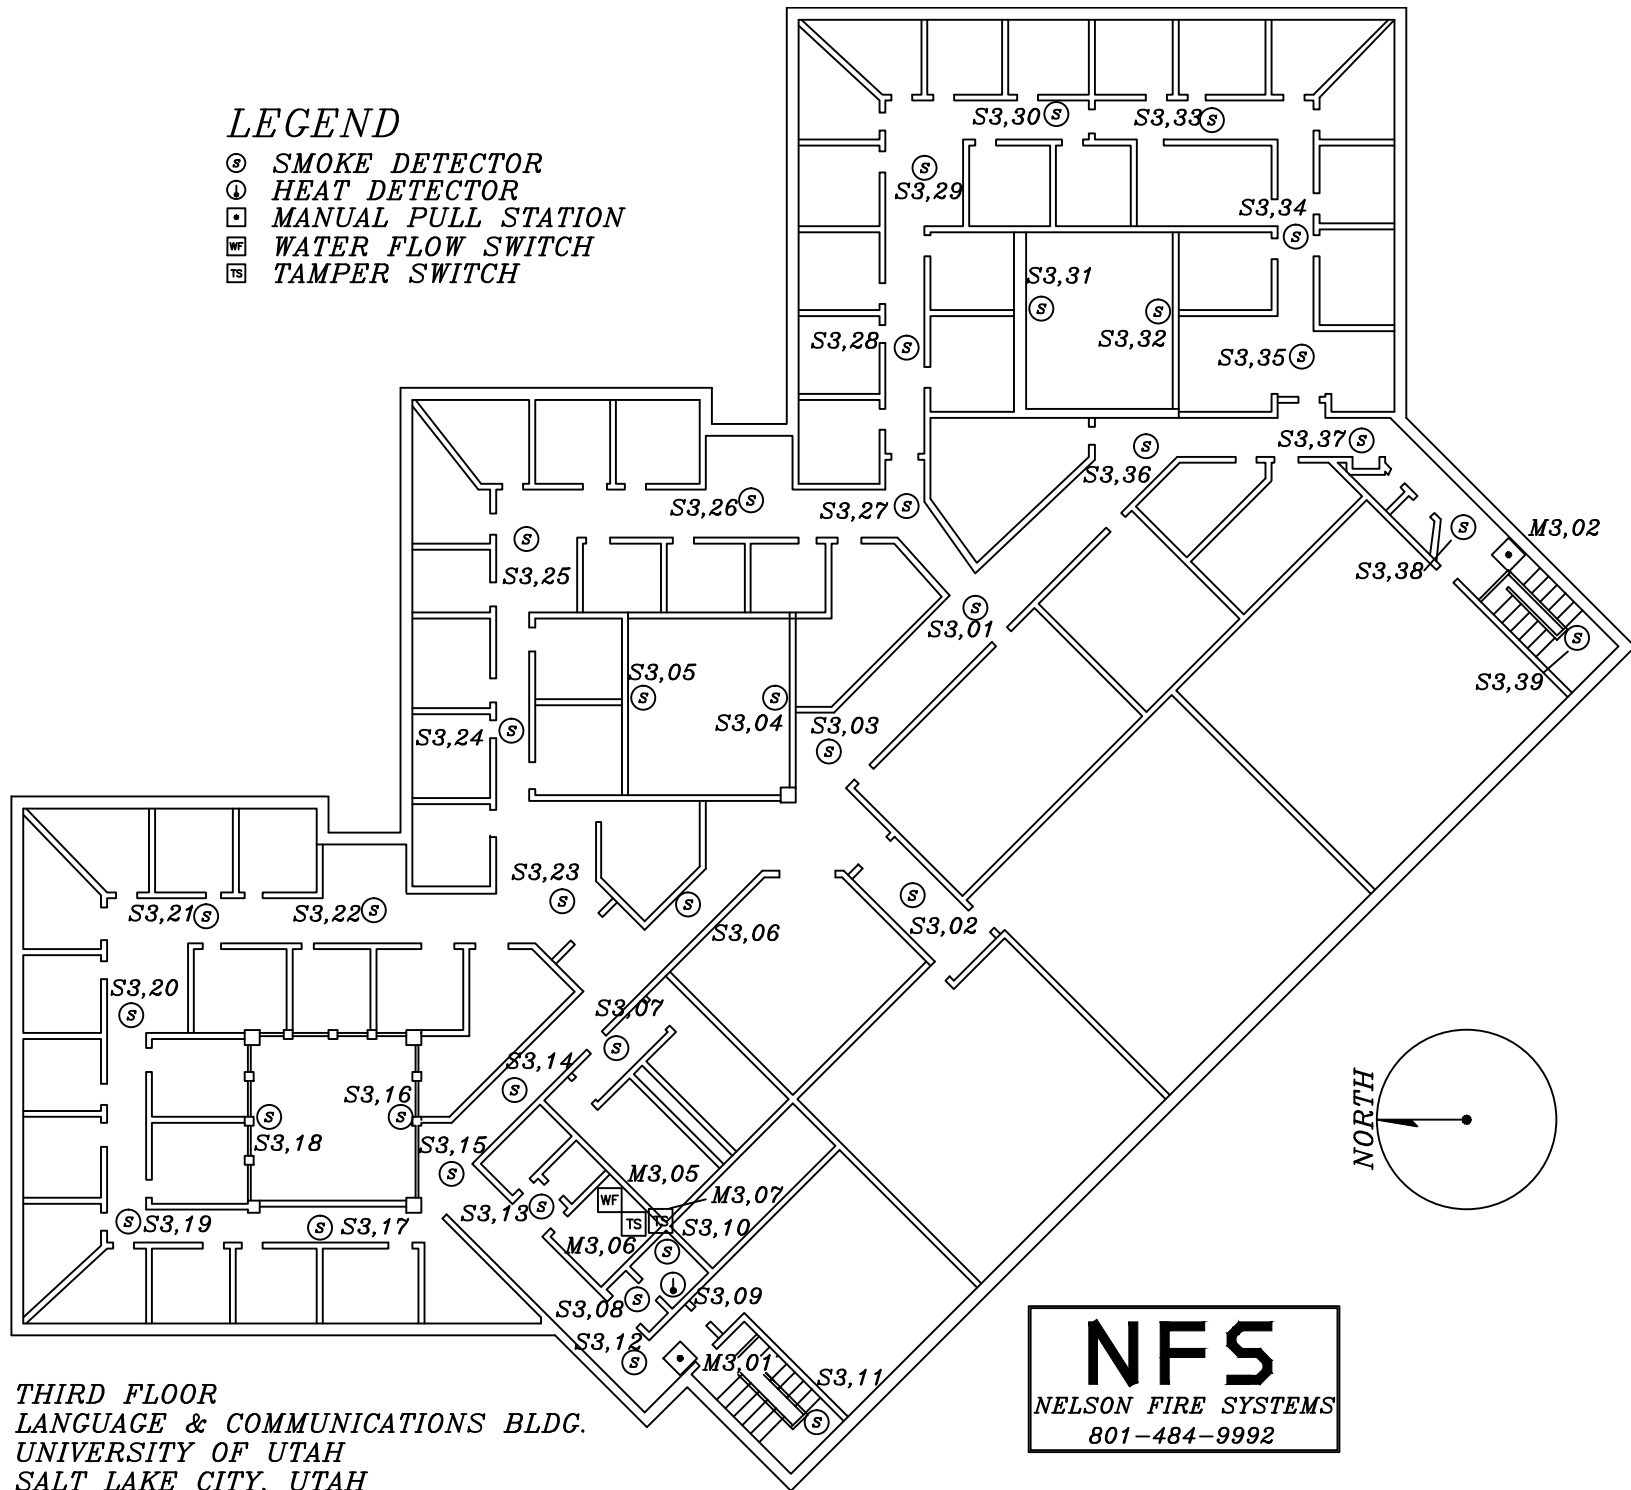

THIRD FLOOR
 LANGUAGE & COMMUNICATIONS BLDG.
 UNIVERSITY OF UTAH
 SALT LAKE CITY, UTAH
 AUGUST 12, 1994
 UOULANG3.DWG

NFS
 NELSON FIRE SYSTEMS
 801-484-9992