


DEVICE LEGEND	
SYMBOL	DESCRIPTION
Ⓢ	SMOKE DETECTOR
Ⓣ	HEAT DETECTOR
ⓕ	MANUAL PULL STATION
ⓓⓓ	DUCT DETECTOR
ⓂⓂ	MONITOR MODULE
ⒸⓂ	CONTROL MODULE
Ⓛ _c	STROBE ONLY-CEILING
ⓗⓈ	HORN/STROBE
Ⓓⓗ	DOORHOLDER
ⓕⓔ	ENGAGE FIRE EXTINGUISHER
ⓉⓗⓇⓗ	TRANSPONDER PANEL
ⓕⓐⒸⓊ	FIRE ALARM CONTROL UNIT

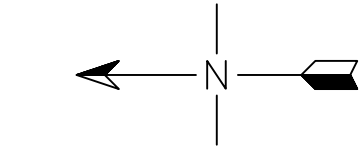

NOTE:
NFS DRAWINGS ARE BASED ON THE PROJECT
ARCHITECT/ENGINEER (A/E) PLANS AND SPECIFICATIONS
FURNISHED TO NFS. A/E IS SOLELY RESPONSIBLE
(NOT NFS) FOR THE TYPE, SIZE, LOCATION, AND
SUITABILITY OF ALL FIRE ALARMS, CONTROL PANELS,
AND OTHER DEVICES SHOWN ON THE A/E PLANS.
NFS DRAWINGS ARE TO SHOW ONLY THE WIRING
DIAGRAMS BETWEEN FIRE ALARM DEVICES AND
CONTROL PANELS. NFS IS NOT RESPONSIBLE FOR
THE INFORMATION SHOWN ON THE A/E PLANS.


UNIVERSITY OF UTAH
SILL CENTER RENOVATION
BASEMENT
SALT LAKE CITY, UT
FIRE ALARM SYSTEM


NFS
NELSON FIRE SYSTEMS
801-468-8300

DRAWN BY:	AK
DESIGNED BY:	XXXX
APPROVED BY:	RS
DATE:	3/17/15
SCALE:	(ANSI B) 1/16"=1'
PROJECT NO:	XXXX
REV NO:	XXXX
DRAWING NAME:	SILL RENOVATION B.DWG


FIRE ALARM SYSTEM
BASEMENT
NUMBERS

PAGE:
FA-B-03

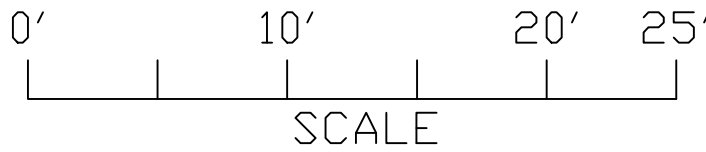

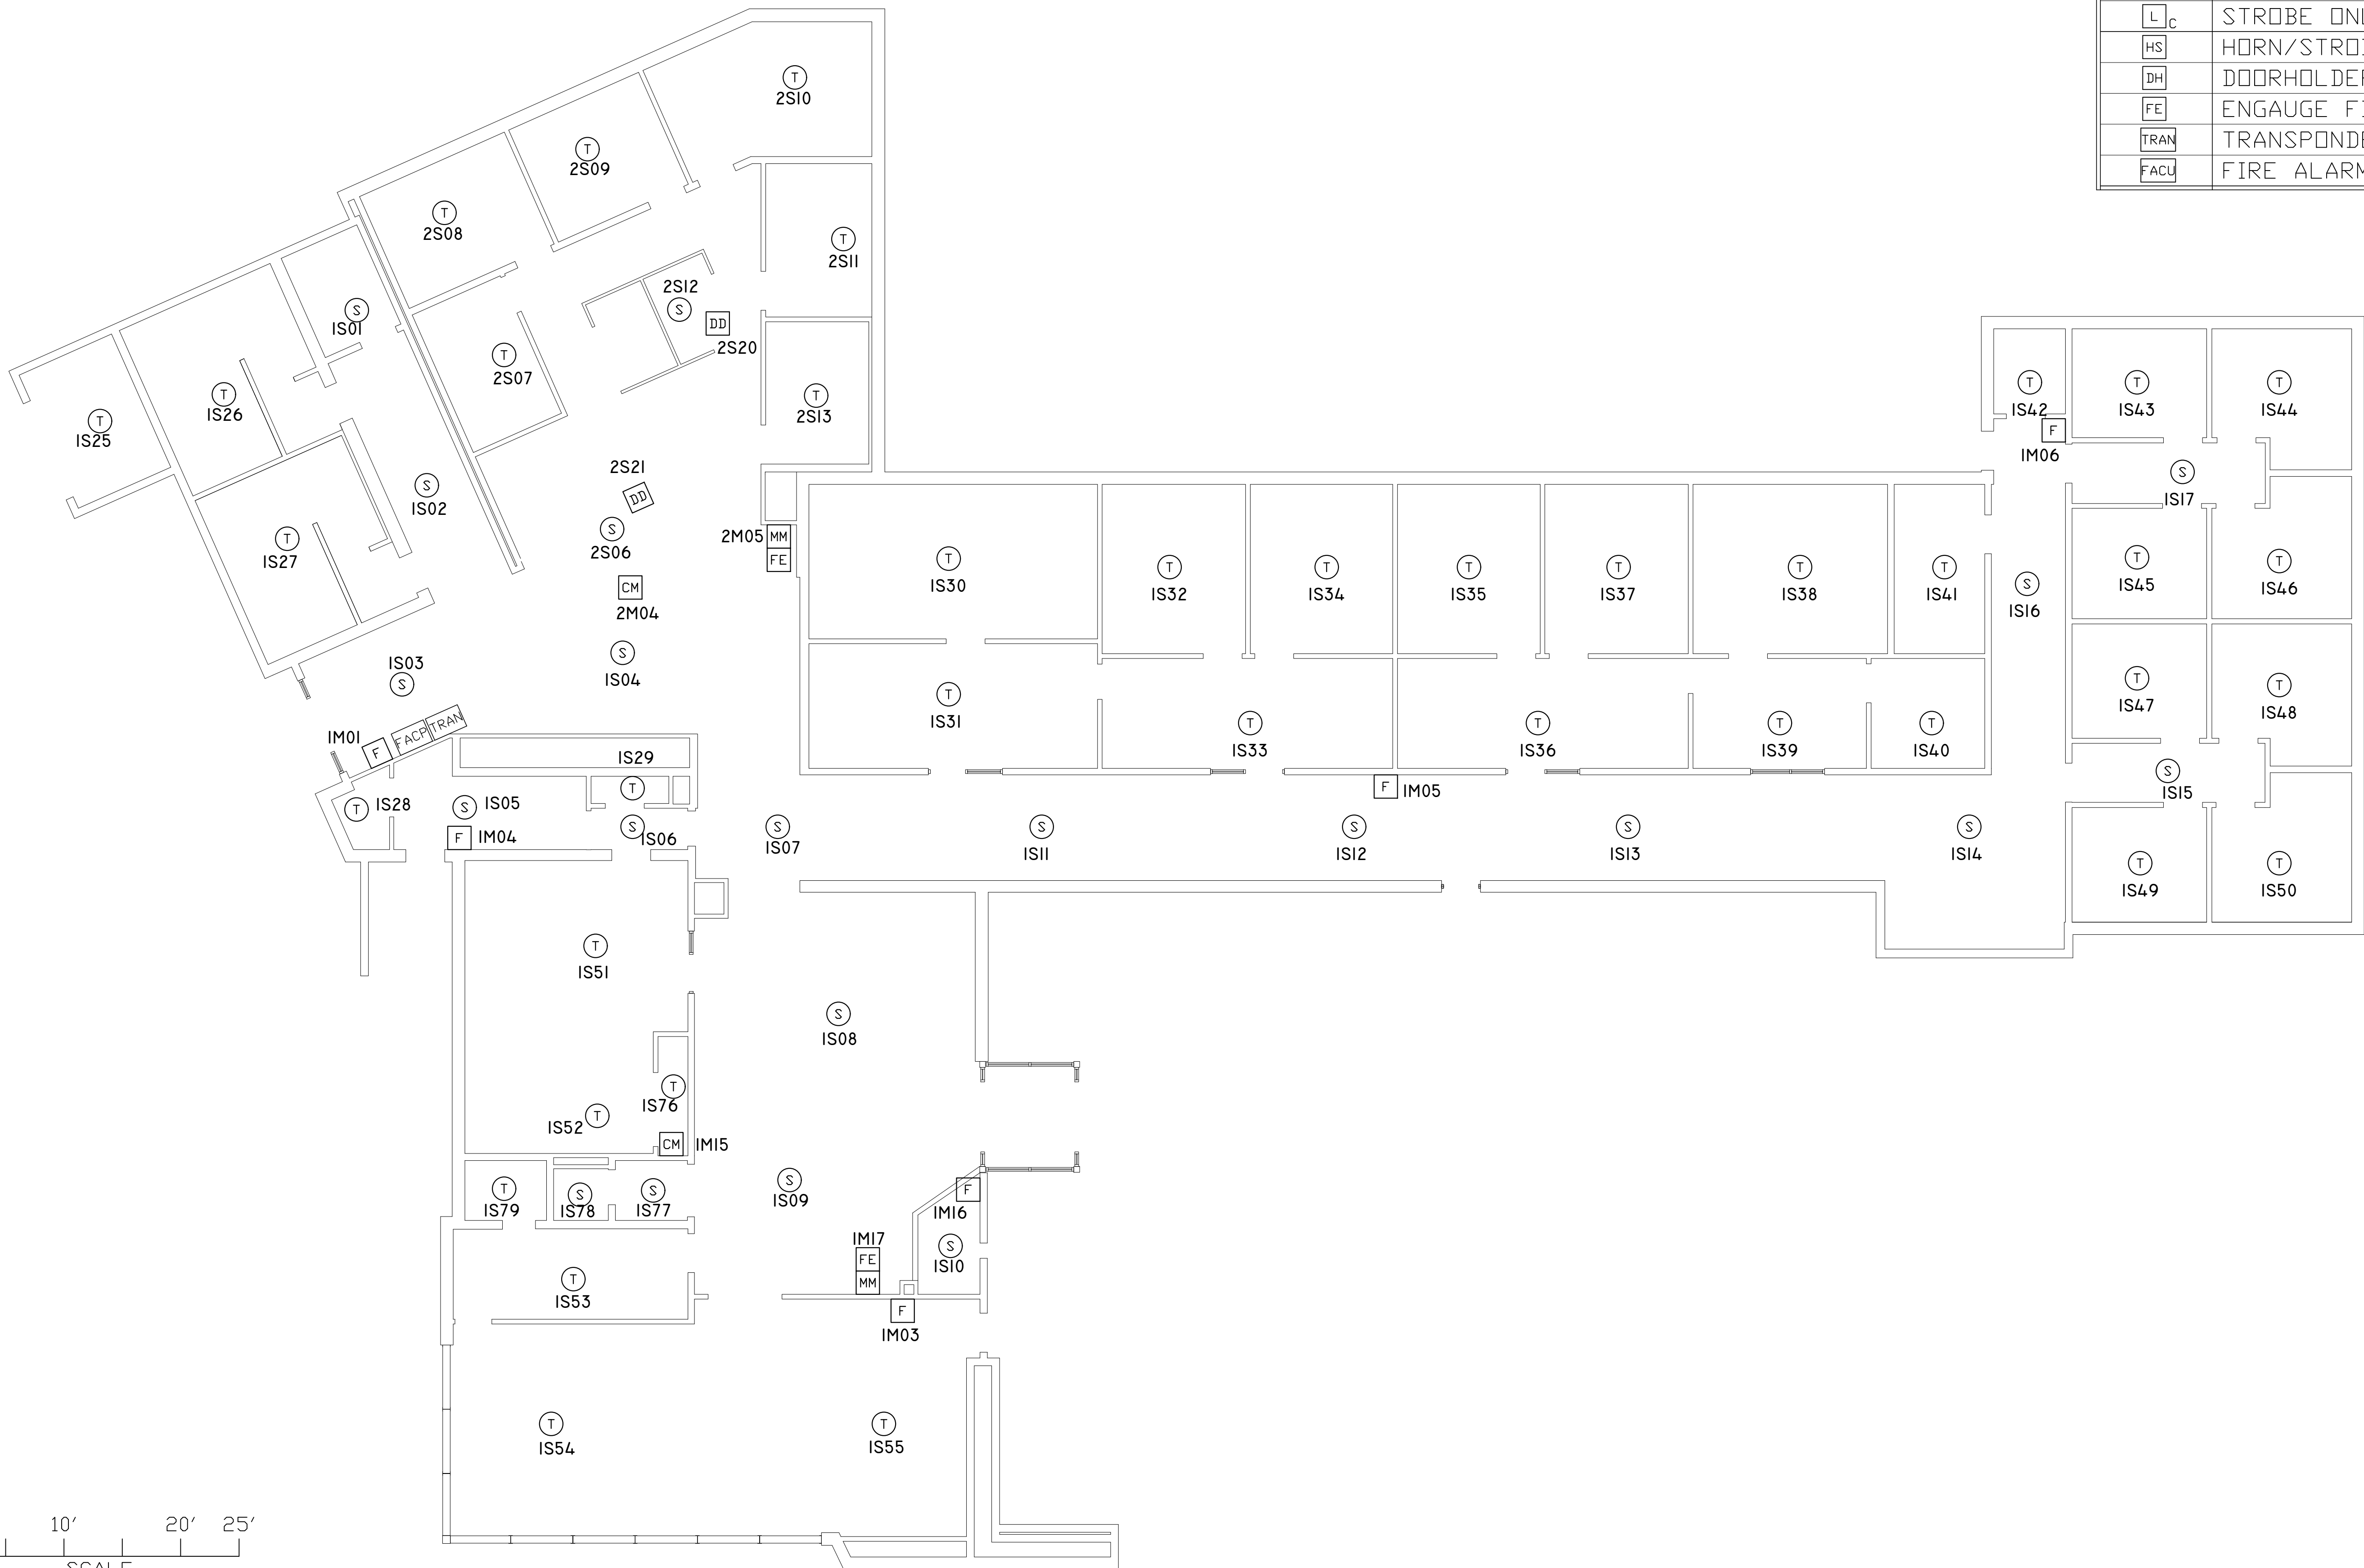

DEVICE LEGEND	
SYMBOL	DESCRIPTION
(S)	SMOKE DETECTOR
(T)	HEAT DETECTOR
[F]	MANUAL PULL STATION
[DD]	DUCT DETECTOR
[MM]	MONITOR MODULE
[CM]	CONTROL MODULE
[L] _c	STROBE ONLY-CEILING
[HS]	HORN/STROBE
[DH]	DOORHOLDER
[FE]	ENGAGE FIRE EXTINGUISHER
[TRAN]	TRANSPONDER PANEL
[FACU]	FIRE ALARM CONTROL UNIT

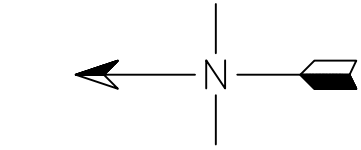

NOTE:
NFS DRAWINGS ARE BASED ON THE PROJECT
ARCHITECT/ENGINEER (A/E) PLANS AND SPECIFICATIONS
FURNISHED TO NFS. A/E IS SOLELY RESPONSIBLE
(NOT NFS) FOR THE TYPE, SIZE, LOCATION, AND
SUITABILITY OF ALL FIRE ALARMS, CONTROL PANELS,
AND OTHER DEVICES SHOWN ON THE A/E PLANS.
NFS DRAWINGS ARE TO SHOW ONLY THE WIRING
DIAGRAMS BETWEEN FIRE ALARM DEVICES AND
CONTROL PANELS. NFS IS NOT RESPONSIBLE FOR
THE INFORMATION SHOWN ON THE A/E PLANS.

UNIVERSITY OF UTAH
SILL CENTER RENOVATION
LEVEL I
SALT LAKE CITY, UT
FIRE ALARM SYSTEM

NFS
NELSON FIRE SYSTEMS
801-468-8300

DRAWN BY: AK
DESIGNED BY: XXXX
APPROVED BY: RS
DATE: 3/17/15
SCALE: (ANSI B) 1/16"=1'
PROJECT NO: XXXX
REV NO: XXXX
DRAWING NAME:
SILL RENOVATION I.DWG

FIRE ALARM SYSTEM
LEVEL I
NUMBERS

PAGE:
FA-I-03

0' 10' 20' 25'
SCALE

