DEVICE LEGEND

SYMBOL	DESCRIPTION
(S)	SMOKE DETECTOR
F	MANUAL PULL STATION
TS	TAMPER SWITCH
WF	WATERFLOW SWITCH
TRAN	TRANSPONDER PANEL
FACU	FIRE ALARM CONTROL UNIT

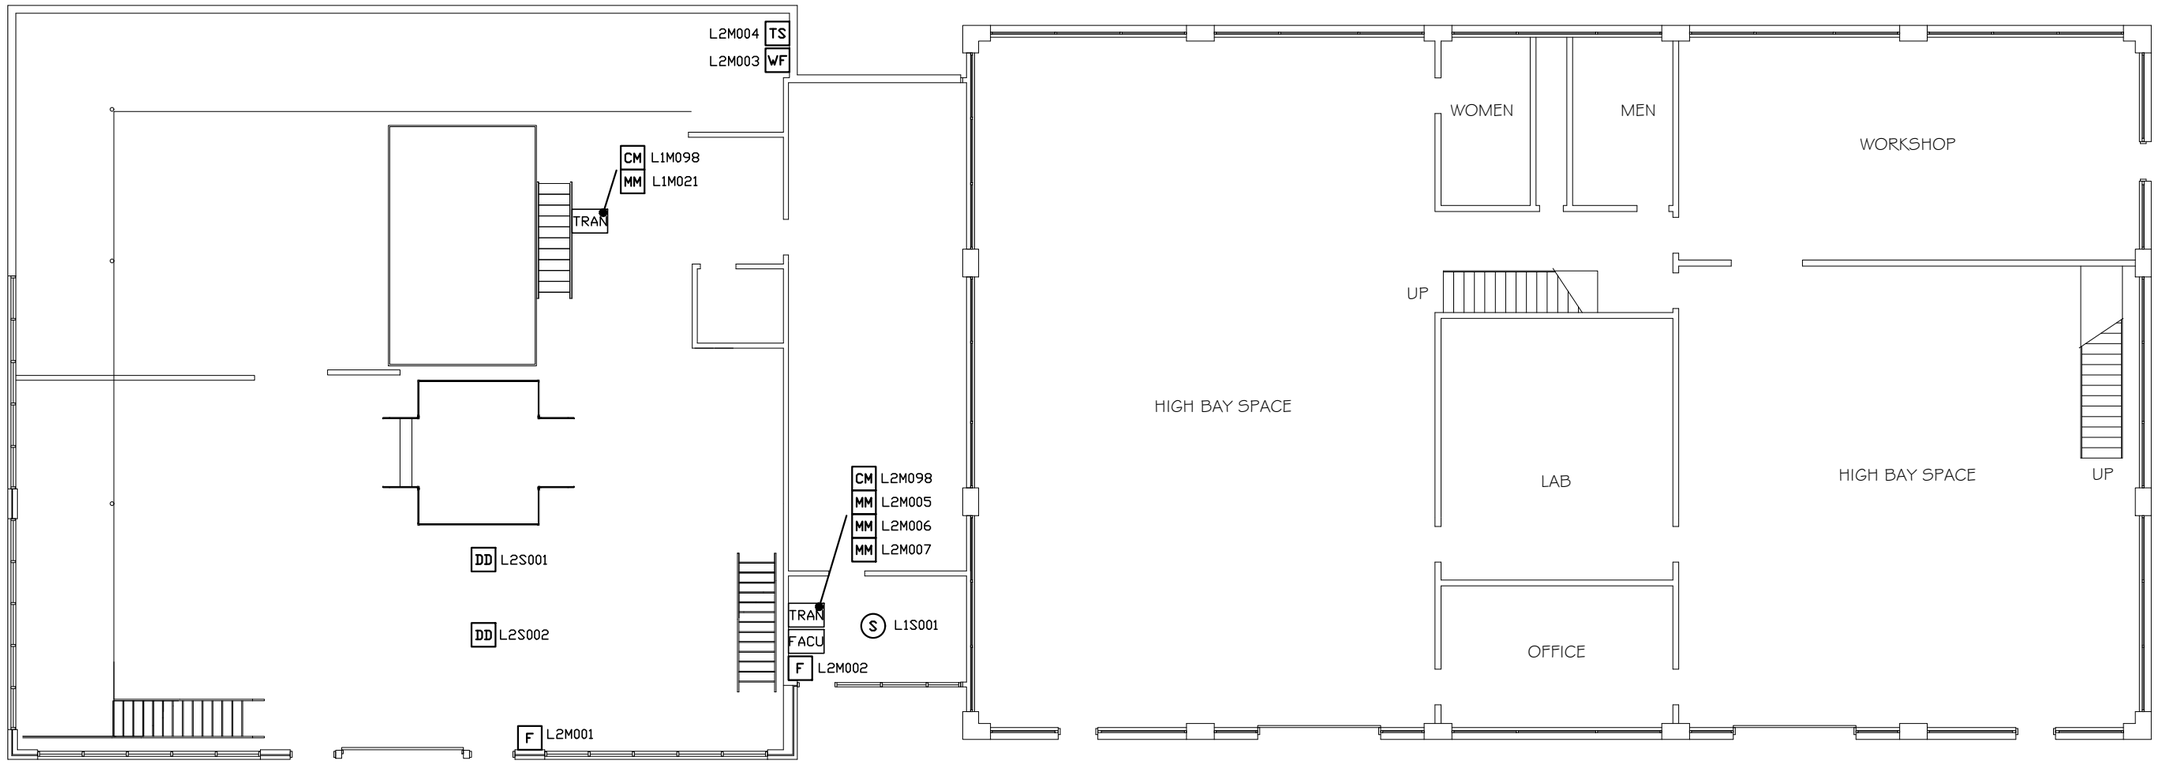

NOTE:
NFS DRAWINGS ARE BASED ON THE PROJECT ARCHITECT/ENGINEER (A/E) PLANS AND SPECIFICATIONS FURNISHED TO NFS. A/E IS SOLELY RESPONSIBLE FOR WHETHER THE SIZE, LOCATION AND SUITABILITY OF ALL FIRE ALARMS, CONTROL PANELS, AND OTHER DEVICES SHOWN ON THE A/E PLANS. NFS DRAWINGS ARE TO SHOW ONLY THE WIRING DIAGRAMS BETWEEN FIRE ALARM DEVICES AND CONTROL PANELS. NFS IS NOT RESPONSIBLE FOR THE INFORMATION SHOWN ON THE A/E PLANS.

UNIVERSITY OF UTAH
BERRY METAL COMPANY
MAIN LEVEL
FIRE ALARM SYSTEM

NFS
NELSON FIRE SYSTEMS
801-468-8300

DRAWN BY:	AK
DESIGNED BY:	XXXX
APPROVED BY:	BN
DATE:	12/30/15
SCALE:	(ANSI B) 1/16"=1'
PROJECT NO:	XXXX
REV NO:	XXXX
DRAWING NAME:	DRAWING NAME.DWG

FIRE ALARM SYSTEM
LEVEL 1
INITIATION & NOTIFICATION

PAGE:
FA-1-01