

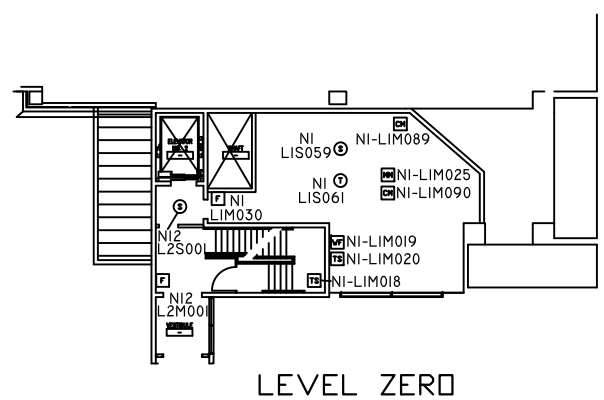


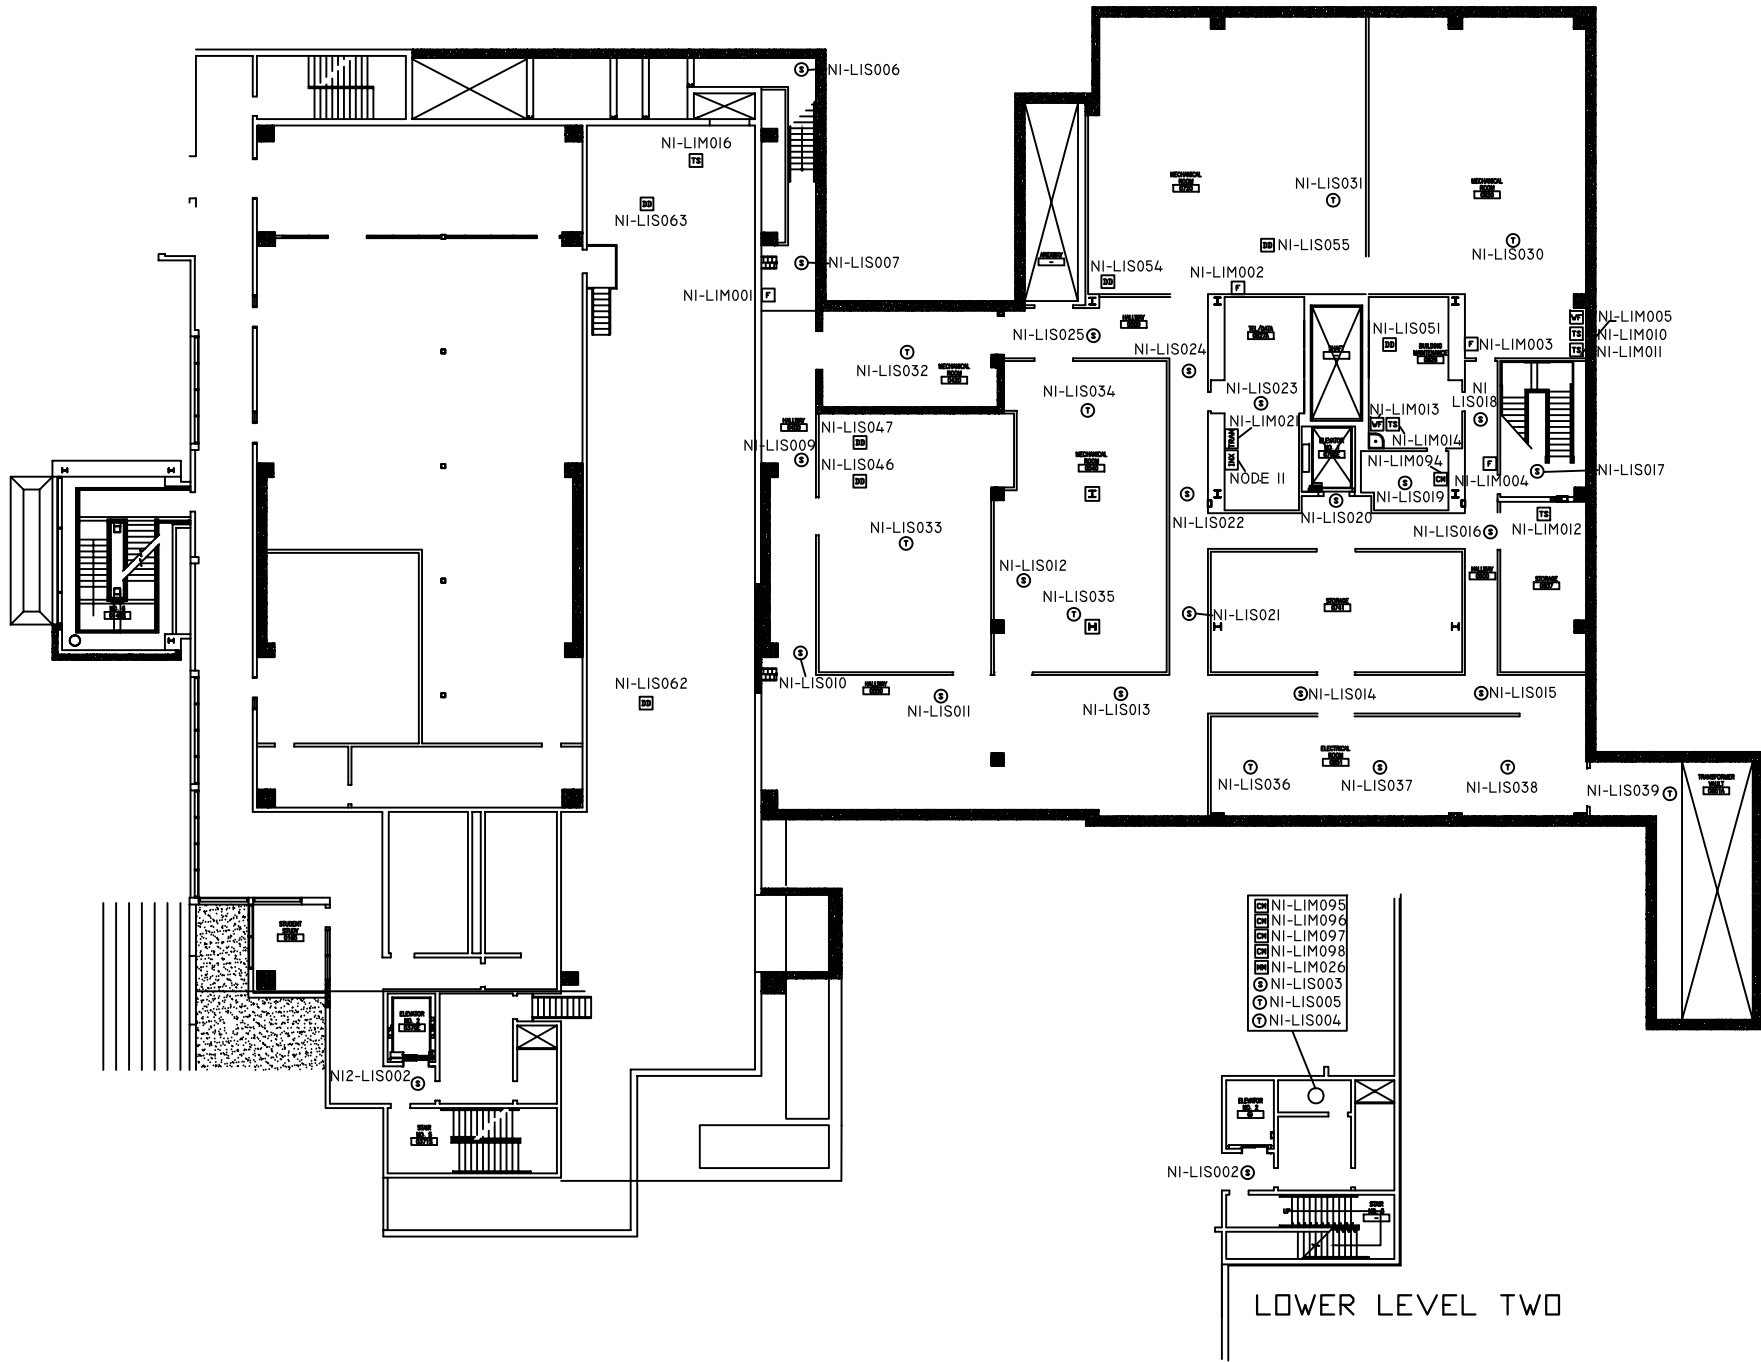

ADDRESS LABEL CLARIFICATION

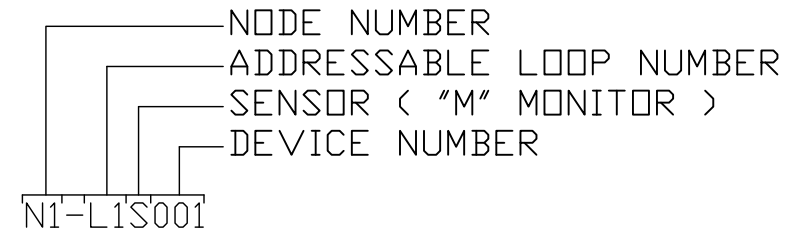

NOTE:
NFS DRAWINGS ARE BASED ON THE PROJECT
ARCHITECT/ENGINEER (A/E) PLANS AND SPECIFICATIONS
FURNISHED TO NFS. A/E IS SOLELY RESPONSIBLE
(NOT NFS) FOR THE TYPE, SIZE, LOCATION, AND
SUITABILITY OF ALL FIRE ALARMS, CONTROL PANELS,
AND OTHER DEVICES SHOWN ON THE A/E PLANS.
NFS DRAWINGS ARE TO SHOW ONLY THE WIRING
DIAGRAMS BETWEEN FIRE ALARM DEVICES AND
CONTROL PANELS. NFS IS NOT RESPONSIBLE FOR
THE INFORMATION SHOWN ON THE A/E PLANS.

UNIVERSITY OF UTAH
WARNOCK ENGINEERING BUILDING
LOWER LEVEL ONE AND TWO
AND LEVEL ZERO
FIRE ALARM SYSTEM

NFS


NELSON FIRE SYSTEMS
801-468-8300

DRAWN BY: DS
DESIGNED BY: SEE
APPROVED BY: TCT
DATE: 1/26/2007
SCALE: 1/16" = 1'
PROJECT NO: 0062-11258
REV NO: 1
DRAWING NAME:
U OF U WARNOCK LLI.DWG

FIRE ALARM SYSTEM
LLI - LL2 - AND LVL ZERO
ADDRESSABLE LOOP NUMBERS

DEVICE LEGEND

SYMBOL	DESCRIPTION
Ⓢ	SMOKE DETECTOR
Ⓣ	THERMAL DETECTOR
F	MANUAL PULL STATION
DB	DUCT SMOKE DETECTOR
WF	WATERFLOW SWITCH MONITOR MODULE
TS	TAMPER SWITCH MONITOR MODULE
MM	MONITOR MODULE
CM	CONTROL MODULE
RA	REMOTE ANNUNCIATOR
FACP	FIRE ALARM CONTROL PANEL
TRAN	TRANSPONDER PANEL

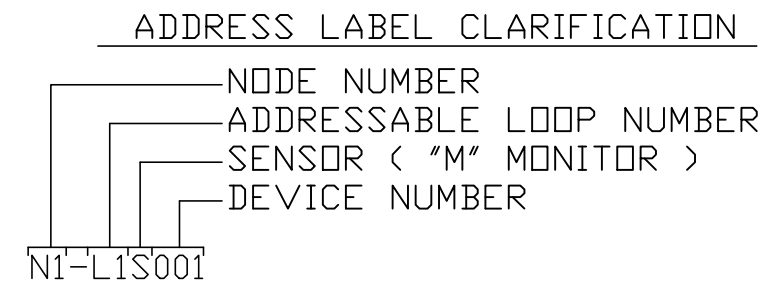

DEVICE LEGEND	
SYMBOL	DESCRIPTION
Ⓢ	SMOKE DETECTOR
Ⓣ	THERMAL DETECTOR
F	MANUAL PULL STATION
DD	DUCT SMOKE DETECTOR
WF	WATERFLOW SWITCH MONITOR MODULE
TS	TAMPER SWITCH MONITOR MODULE
MM	MONITOR MODULE
CM	CONTROL MODULE
RA	REMOTE ANNUNCIATOR
FACP	FIRE ALARM CONTROL PANEL
TRAN	TRANSPONDER PANEL


NOTE:
NFS DRAWINGS ARE BASED ON THE PROJECT
ARCHITECT/ENGINEER (E) PLANS AND SPECIFICATIONS
FURNISHED. NFS IS SOLELY RESPONSIBLE
(NOT NFS) FOR THE TYPE, SIZE, LOCATION AND
SUITABILITY OF ALL FIRE ALARMS, CONTROL PANELS,
AND OTHER DEVICES SHOWN ON THE A/E PLANS.
NFS DRAWINGS ARE TO SHOW ONLY THE WIRING
DIAGRAMS BETWEEN FIRE ALARM DEVICES AND
CONTROL PANELS. NFS IS NOT RESPONSIBLE FOR
THE INFORMATION SHOWN ON THE A/E PLANS.

UNIVERSITY OF UTAH
WARNOCK ENGINEERING BUILDING
LEVEL ONE
FIRE ALARM SYSTEM


NFS
NELSON FIRE SYSTEMS
801-468-8300

DRAWN BY:	DS
DESIGNED BY:	SEE
APPROVED BY:	TCT
DATE:	1/26/2007
SCALE:	1/16" = 1'
PROJECT NO:	0062-II258
REV NO:	I
DRAWING NAME:	
U OF U WARNOCK I.DWG	

FIRE ALARM SYSTEM
LEVEL ONE
ADDRESSABLE LOOP NUMBERS

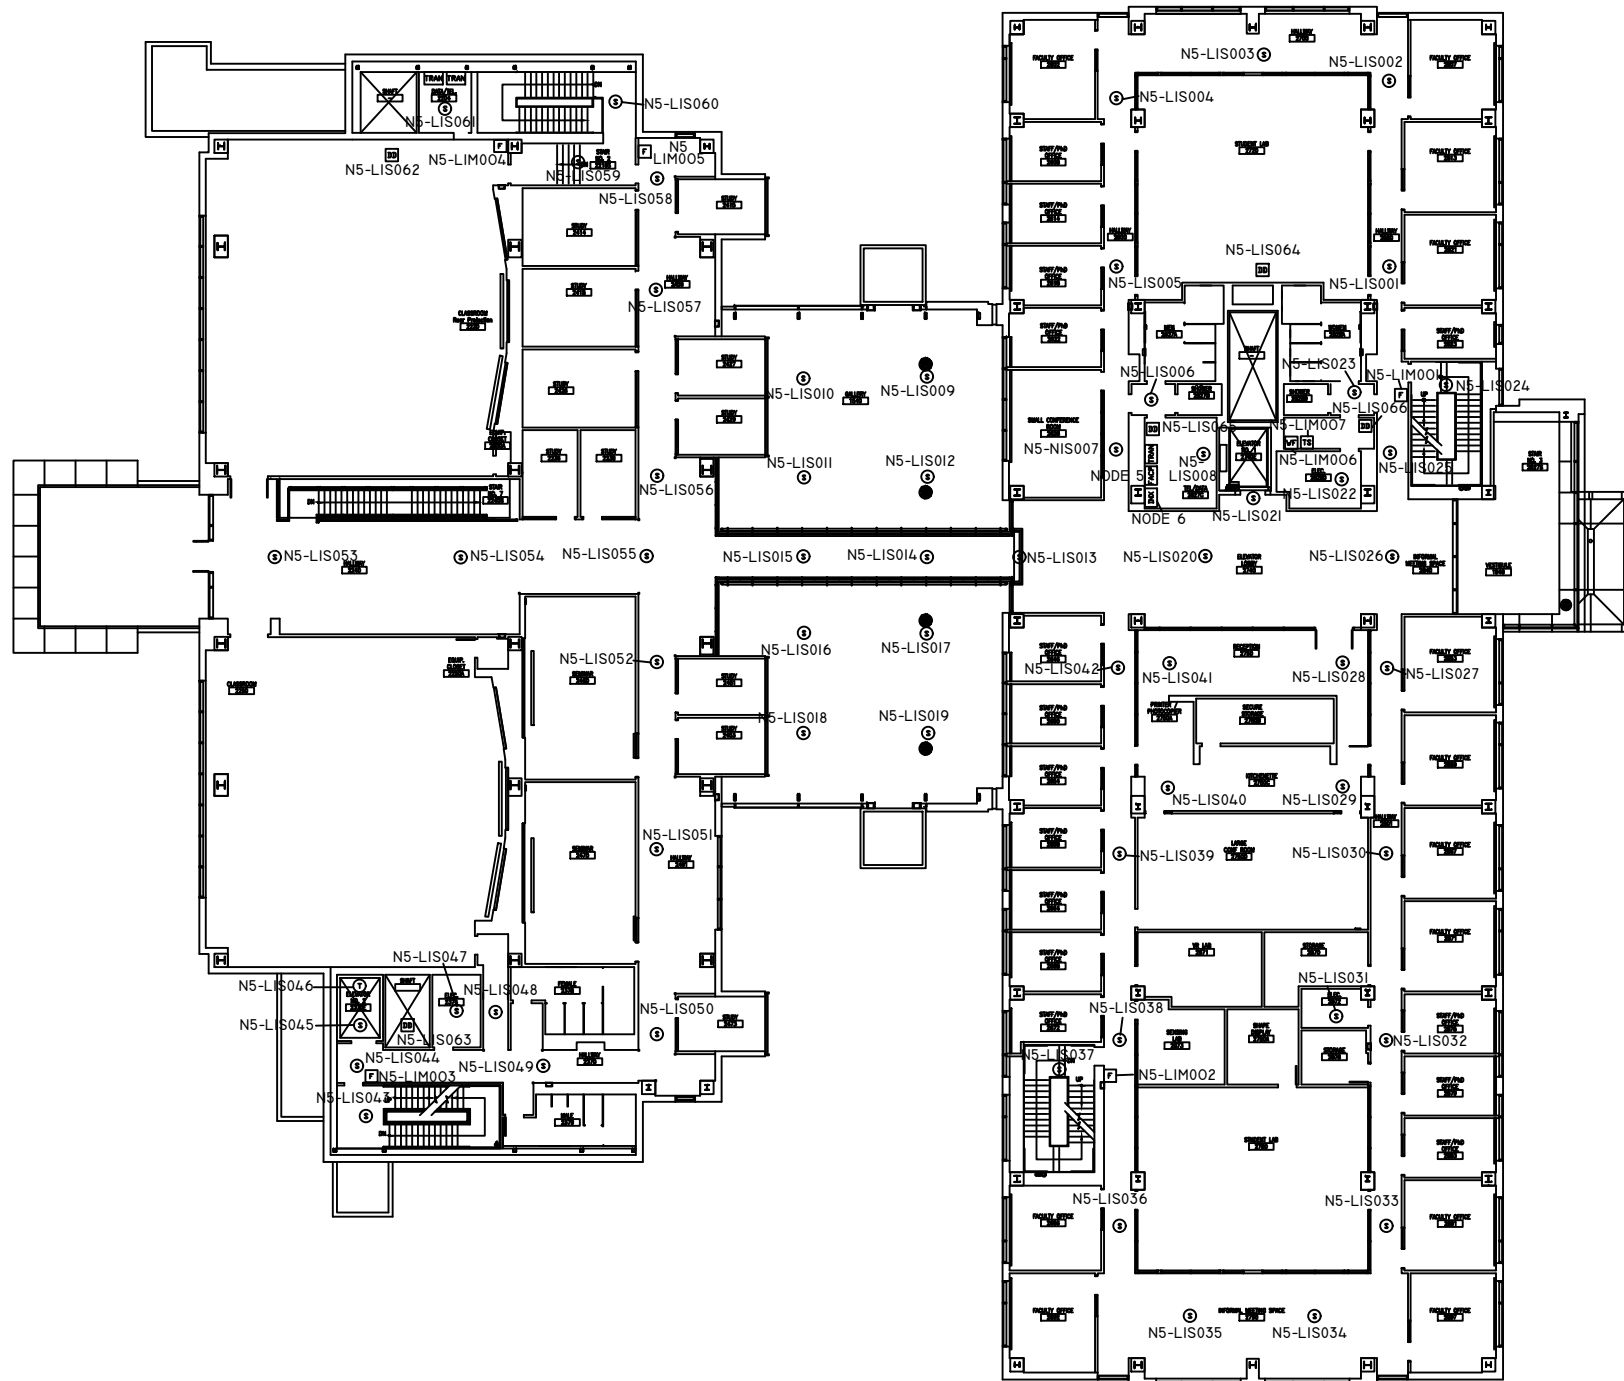

ADDRESS LABEL CLARIFICATION

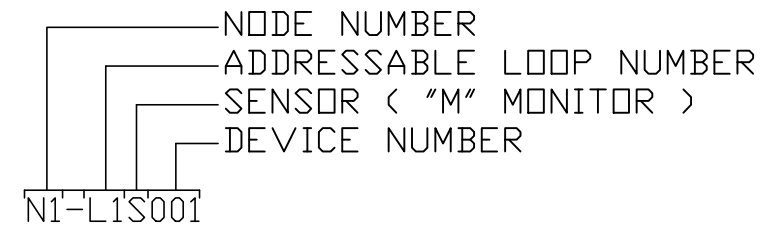


DEVICE LEGEND	
SYMBOL	DESCRIPTION
Ⓢ	SMOKE DETECTOR
Ⓣ	THERMAL DETECTOR
F	MANUAL PULL STATION
DS	DUCT SMOKE DETECTOR
WF	WATERFLOW SWITCH MONITOR MODULE
TS	TAMPER SWITCH MONITOR MODULE
MM	MONITOR MODULE
CM	CONTROL MODULE
RA	REMOTE ANNUNCIATOR
FACP	FIRE ALARM CONTROL PANEL
TRAN	TRANSPONDER PANEL

UNIVERSITY OF UTAH
WARNOCK ENGINEERING BUILDING
LEVEL TWO
FIRE ALARM SYSTEM


NFS
NELSON FIRE SYSTEMS
801-468-8300

DRAWN BY: DS
DESIGNED BY: SEE
APPROVED BY: TCT
DATE: 1/26/2007
SCALE: 1/16" = 1'
PROJECT NO: 0062-II258
REV NO: I
DRAWING NAME:
U OF U WARNOCK 2.DWG


FIRE ALARM SYSTEM
LEVEL TWO
ADDRESSABLE LOOP NUMBERS

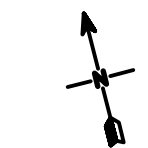

NOTE:
NFS DRAWINGS ARE BASED ON THE PROJECT
ARCHITECT/ENGINEER (A/E) PLANS AND SPECIFICATIONS
FURNISHED TO NFS. A/E IS SOLELY RESPONSIBLE
(NOT NFS) FOR THE TYPE, SIZE, LOCATION, AND
SUITABILITY OF ALL FIRE ALARMS, CONTROL PANELS,
AND OTHER DEVICES SHOWN ON THE A/E PLANS.
NFS DRAWINGS ARE TO SHOW ONLY THE WIRING
DIAGRAMS BETWEEN FIRE ALARM DEVICES AND
CONTROL PANELS. NFS IS NOT RESPONSIBLE FOR
THE INFORMATION SHOWN ON THE A/E PLANS.

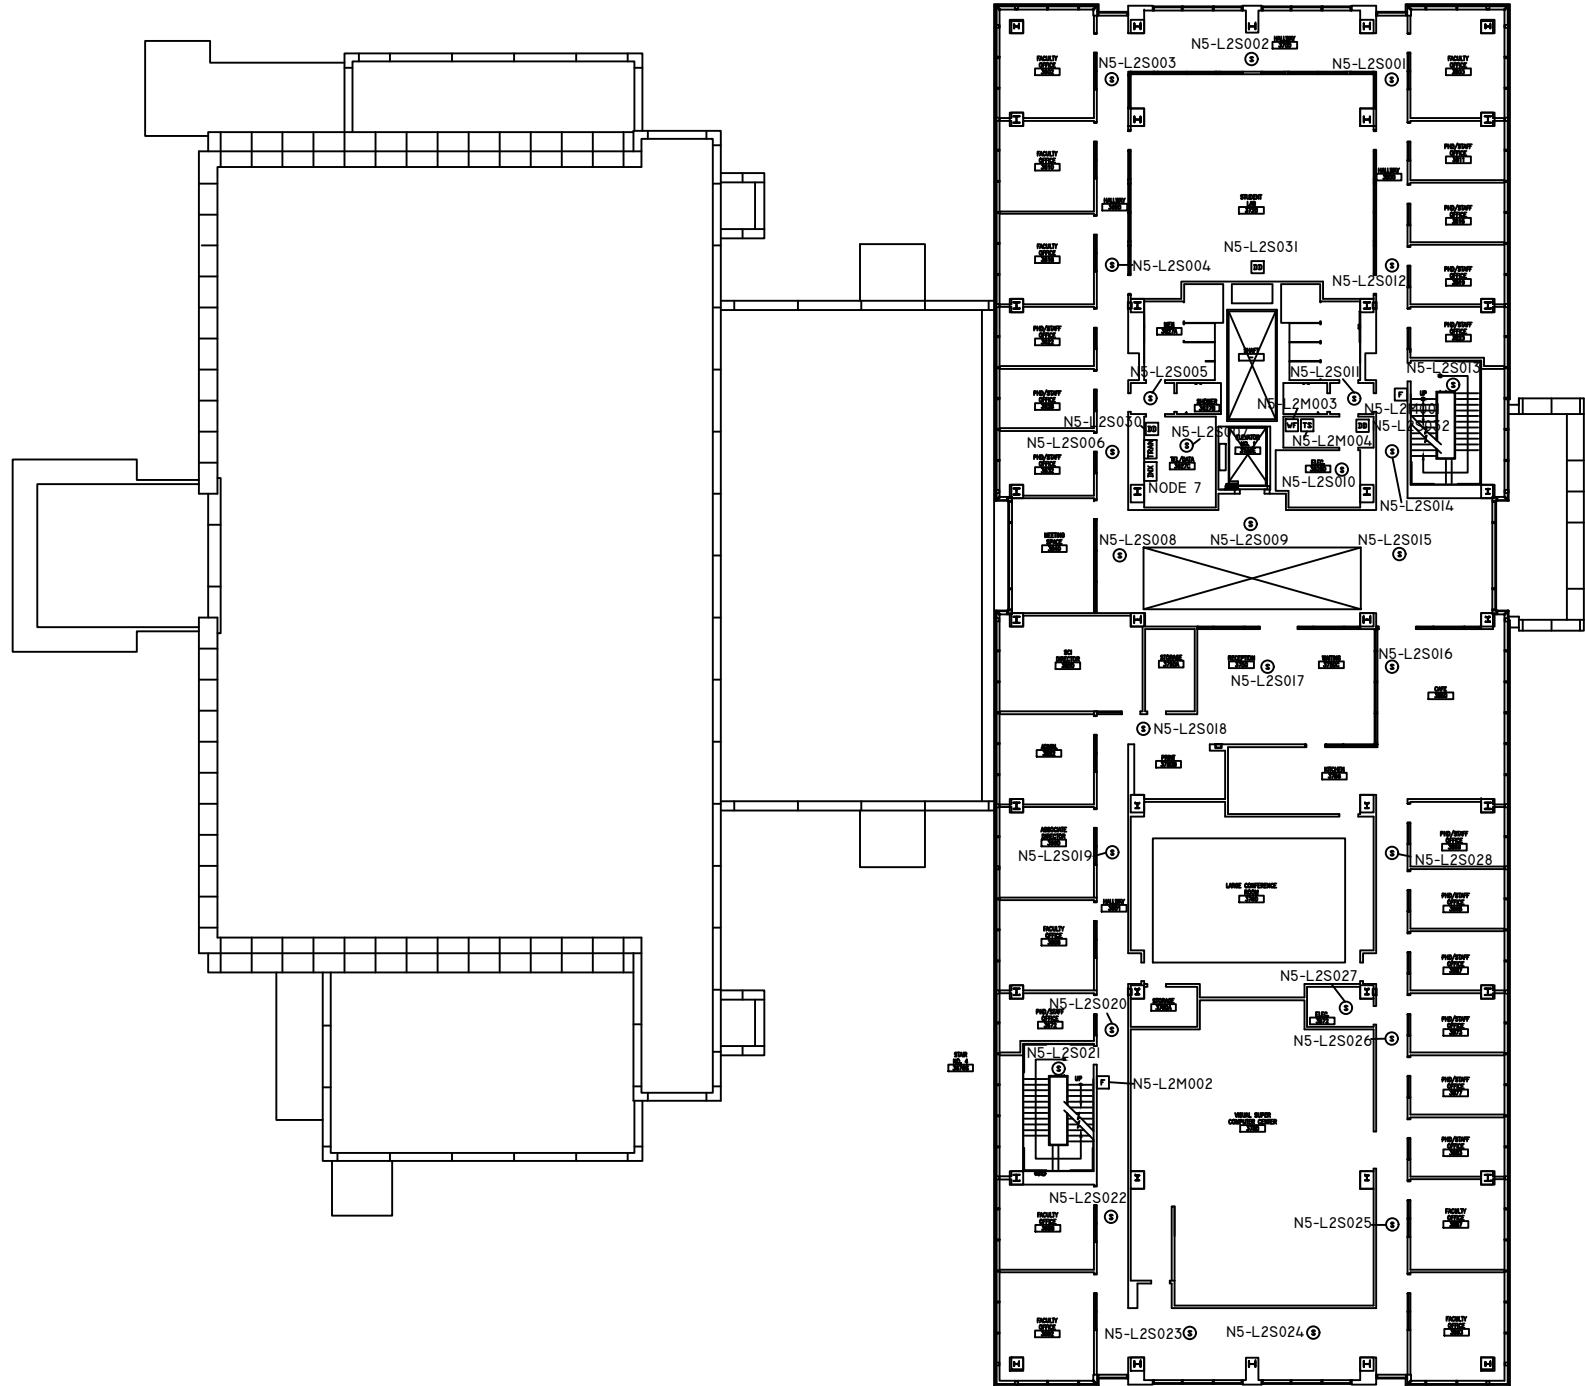

ADDRESS LABEL CLARIFICATION

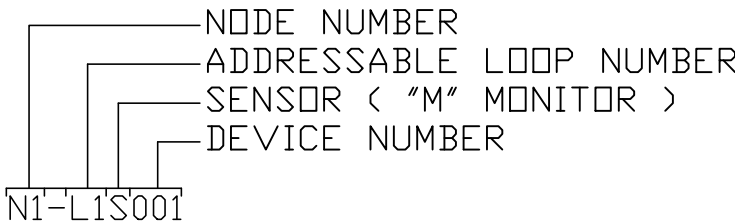

DEVICE LEGEND	
SYMBOL	DESCRIPTION
Ⓢ	SMOKE DETECTOR
Ⓣ	THERMAL DETECTOR
F	MANUAL PULL STATION
DB	DUCT SMOKE DETECTOR
WF	WATERFLOW SWITCH MONITOR MODULE
TS	TAMPER SWITCH MONITOR MODULE
MM	MONITOR MODULE
CM	CONTROL MODULE
RA	REMOTE ANNUNCIATOR
FACP	FIRE ALARM CONTROL PANEL
TRAN	TRANSPONDER PANEL

NOTE:
NFS DRAWINGS ARE BASED ON THE PROJECT
ARCHITECT/ENGINEER (A/E) PLANS AND SPECIFICATIONS
FURNISHED TO NFS. A/E IS SOLELY RESPONSIBLE
(NOT NFS) FOR THE TYPE, SIZE, LOCATION, AND
SUITABILITY OF ALL FIRE ALARMS, CONTROL PANELS,
AND OTHER DEVICES SHOWN ON THE A/E PLANS.
NFS DRAWINGS ARE TO SHOW ONLY THE WIRING
DIAGRAMS BETWEEN FIRE ALARM DEVICES AND
CONTROL PANELS. NFS IS NOT RESPONSIBLE FOR
THE INFORMATION SHOWN ON THE A/E PLANS.

UNIVERSITY OF UTAH
WARNOCK ENGINEERING BUILDING
LEVEL THREE
FIRE ALARM SYSTEM

NFS
NELSON FIRE SYSTEMS
801-468-8300

DRAWN BY: DS

DESIGNED BY: SEE

APPROVED BY: TCT

DATE: 1/26/2007

SCALE: 1/16" = 1'

PROJECT NO: 0062-II258

REV NO: I

DRAWING NAME: U OF U WARNOCK 3.DWG

FIRE ALARM SYSTEM
LEVEL THREE
ADDRESSABLE LOOP NUMBERS


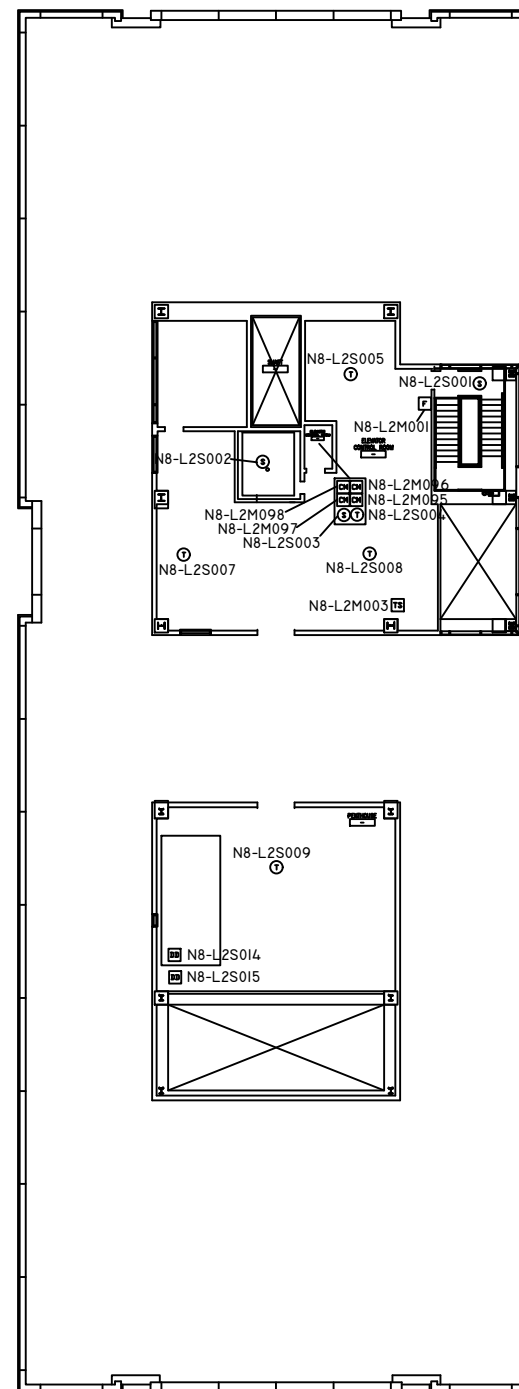


Diagram illustrating the bit fields of the address N1-L1S001:

- N1 - NODE NUMBER
- L1 - ADDRESSABLE LOOP NUMBER
- S - SENSOR ("M" MONITOR)
- 001 - DEVICE NUMBER

DEVICE LEGEND	
SYMBOL	DESCRIPTION
③	SMOKE DETECTOR
Ⓣ	THERMAL DETECTOR
ⓕ	MANUAL PULL STATION
DD	DUCT SMOKE DETECTOR
WT	WATERFLOW SWITCH MONITOR MODULE
TS	TAMPER SWITCH MONITOR MODULE
MM	MONITOR MODULE
CM	CONTROL MODULE
RA	REMOTE ANNUNCIATOR
FACP	FIRE ALARM CONTROL PANEL
TRAN	TRANSPONDER PANEL

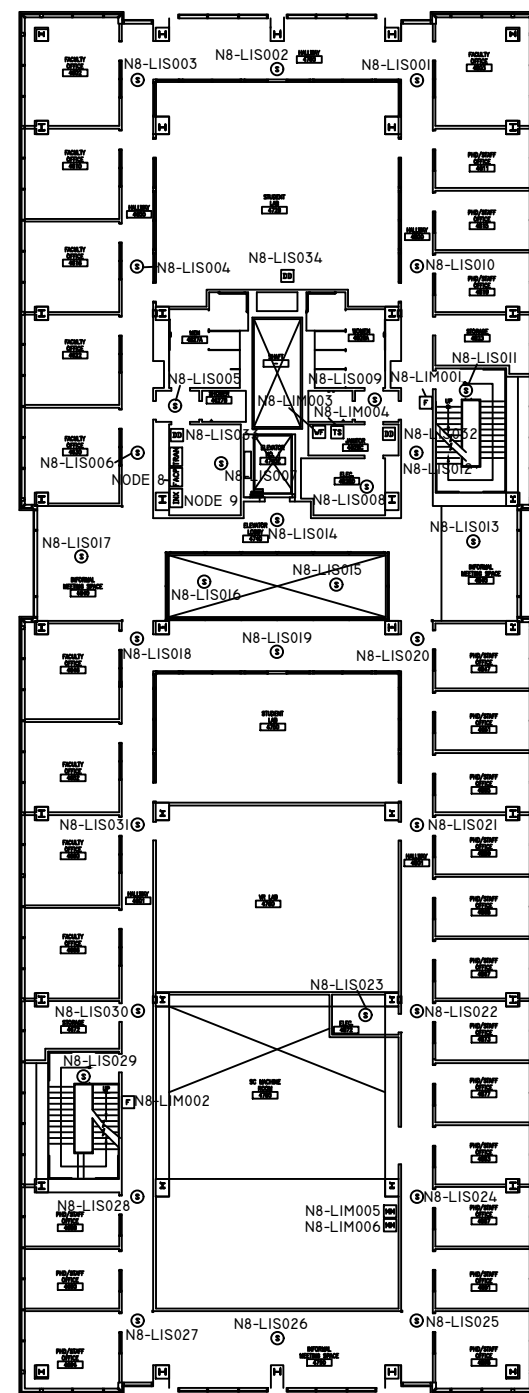

NOTE:
NFS DRAWINGS ARE BASED ON THE PROJECT
ARCHITECT/ENGINEER (A/E) PLANS AND SPECIFICATIONS
FURNISHED TO NFS. A/E IS SOLELY RESPONSIBLE
(NOT NFS) FOR THE TYPE, SIZE, LOCATION, AND
SUITABILITY OF ALL FIRE ALARMS, CONTROL PANELS,
AND OTHER DEVICES SHOWN ON THE A/E PLANS.
NFS DRAWINGS ARE TO SHOW ONLY THE WIRING
DIAGRAMS BETWEEN FIRE ALARM DEVICES AND
CONTROL PANELS. NFS IS NOT RESPONSIBLE FOR
THE INFORMATION SHOWN ON THE A/E PLANS.


UNIVERSITY OF UTAH
WARNOCK ENGINEERING BUILDING
LEVEL FOUR AND PENTHOUSE
FIRE ALARM SYSTEM


NFS

NELSON FIRE SYSTEMS
801-468-8300


DRAWN BY:	DS
DESIGNED BY:	SEE
APPROVED BY:	TCT
DATE:	1/26/2007
SCALE:	1/16" = 1'
PROJECT NO:	0062-II258
REV NO:	I
DRAWING NAME:	
U OF U WARNOCK 4.DWG	

FIRE ALARM SYSTEM
LEVEL FOUR- PENTHOUSE
ADDRESSABLE LOOP NUMBERS

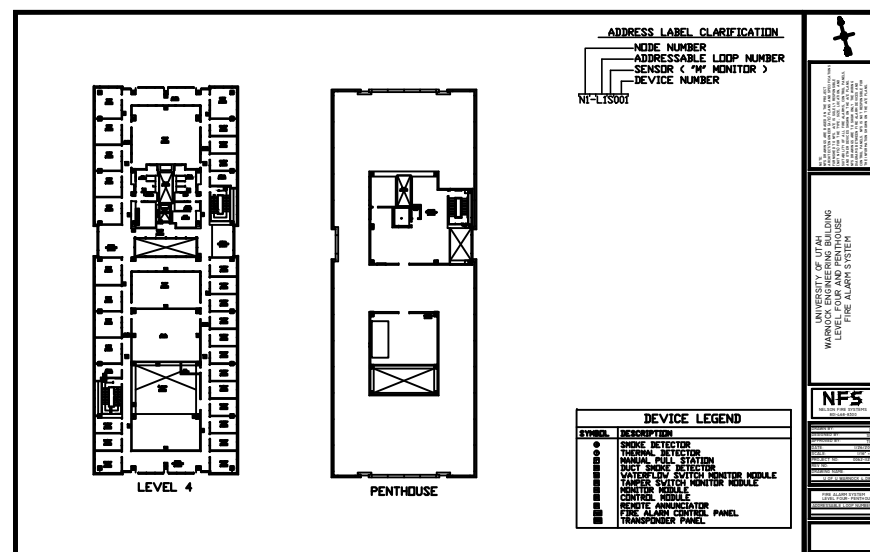


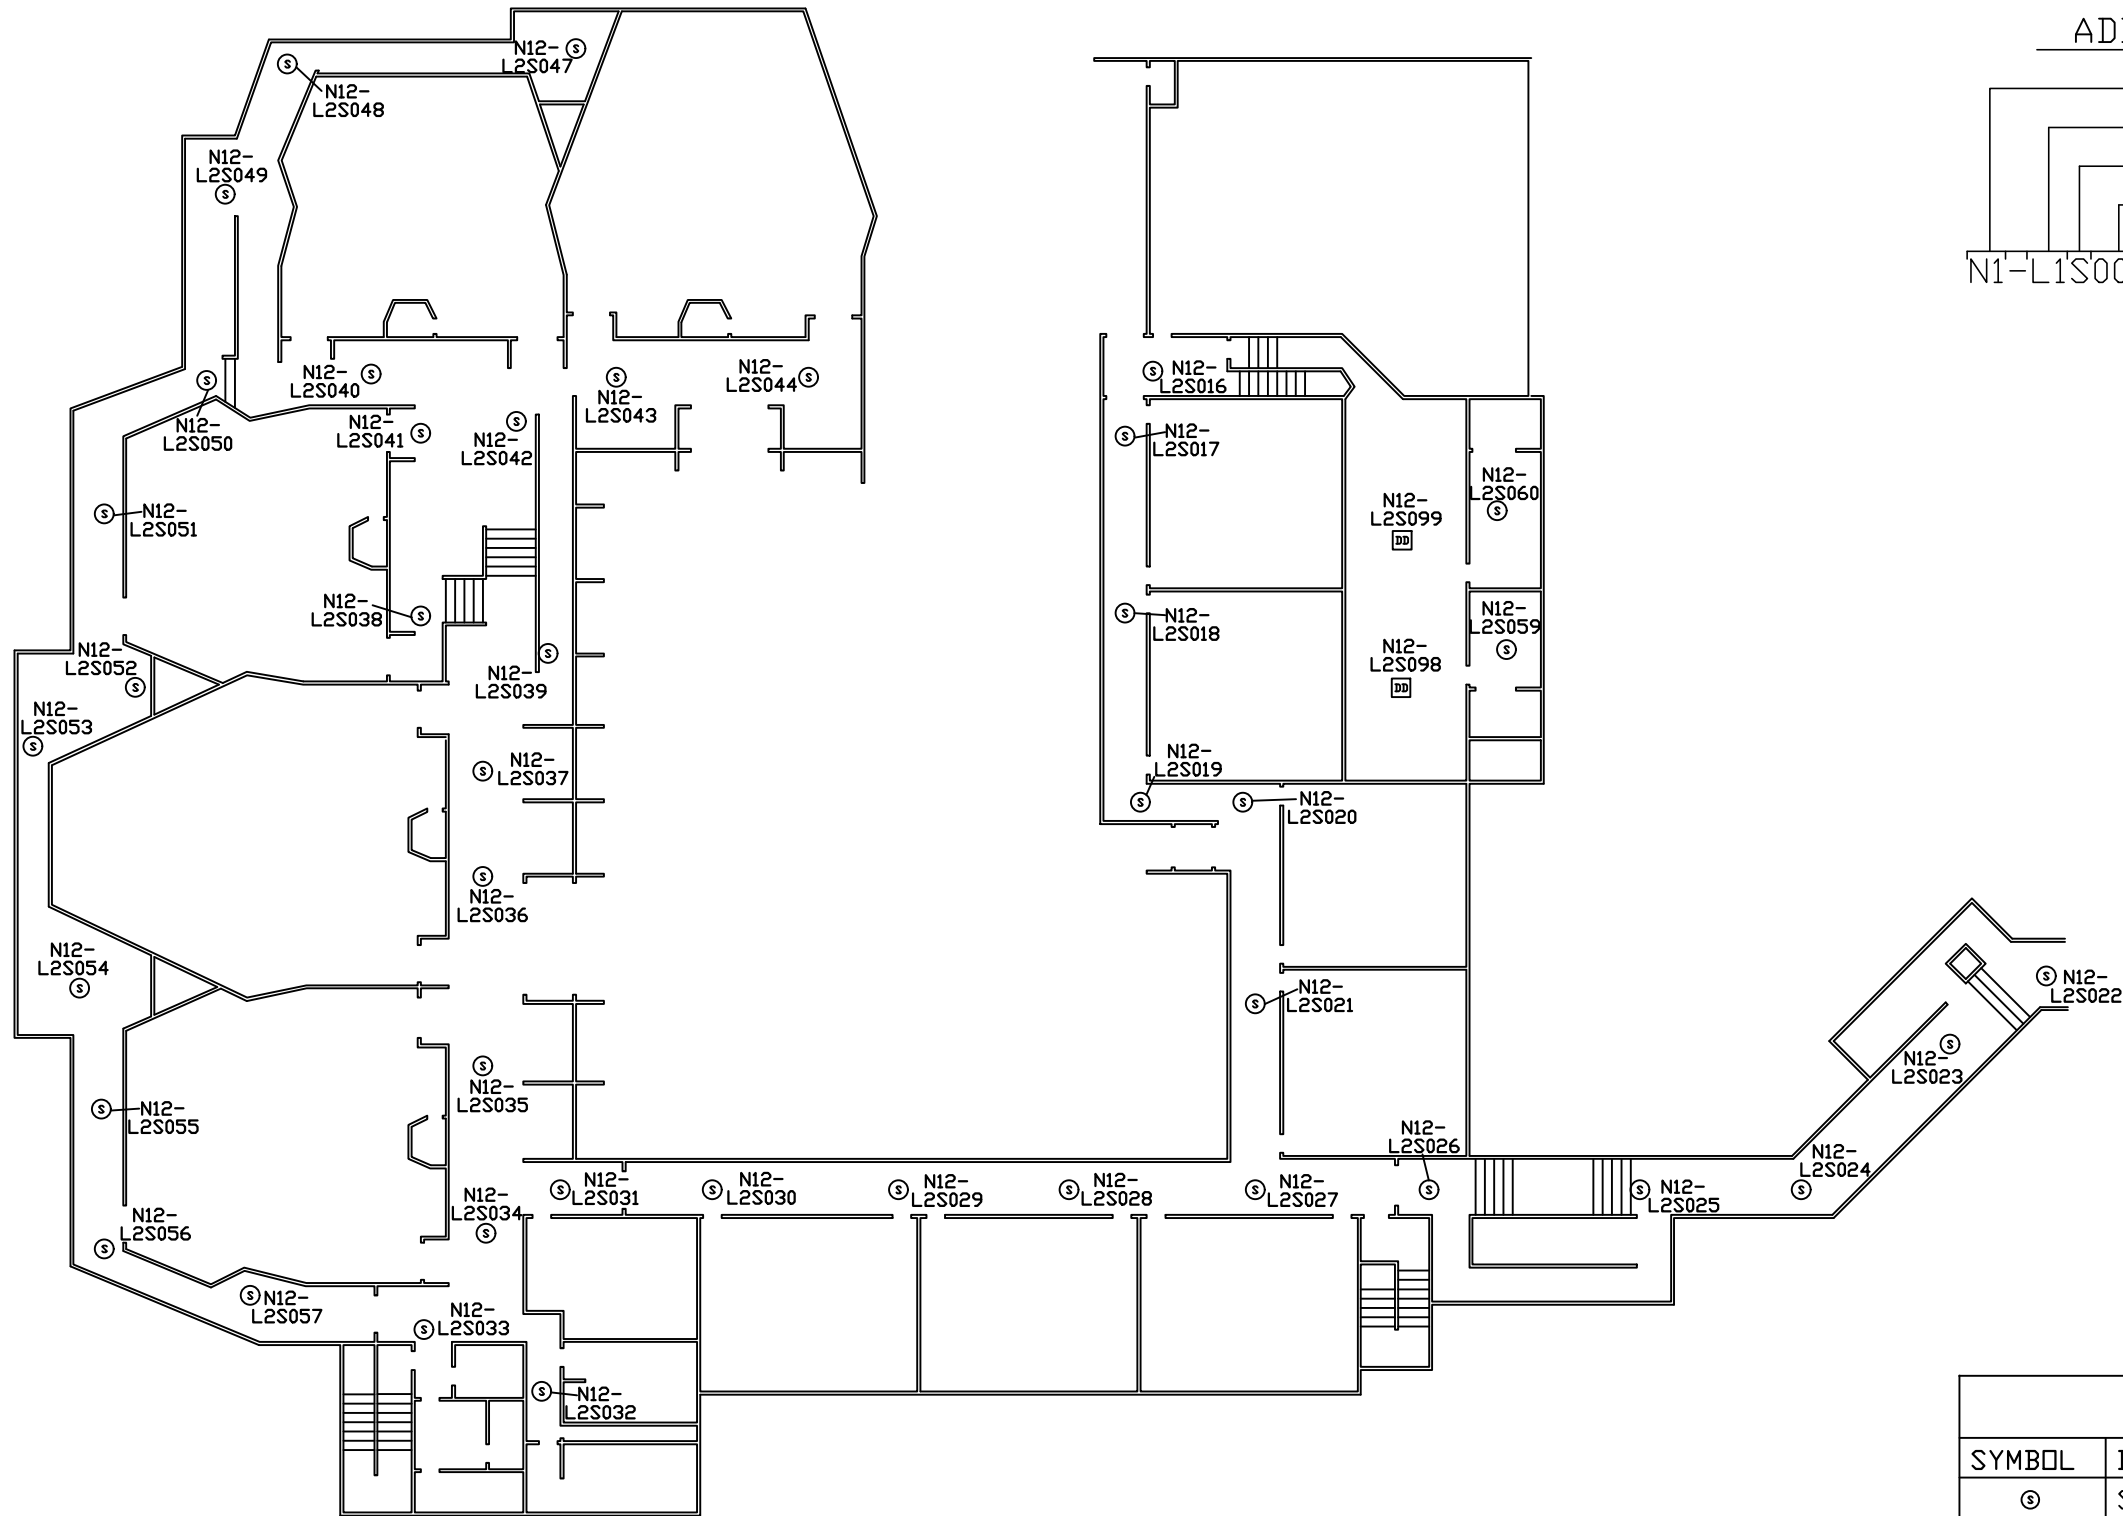

ADDRESS LABEL CLARIFICATION

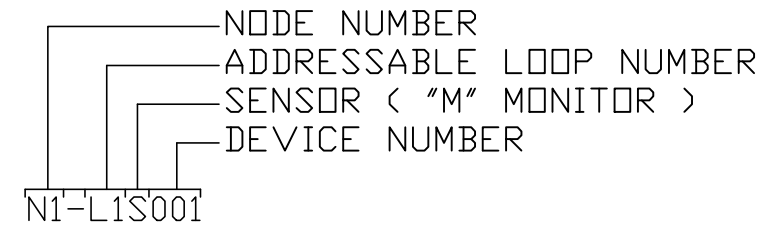

DEVICE LEGEND	
SYMBOL	DESCRIPTION
Ⓢ	SMOKE DETECTOR
Ⓣ	THERMAL DETECTOR
F	MANUAL PULL STATION
DD	DUCT SMOKE DETECTOR
WF	WATERFLOW SWITCH MONITOR MODULE
TS	TAMPER SWITCH MONITOR MODULE
MM	MONITOR MODULE
CM	CONTROL MODULE
RA	REMOTE ANNUNCIATOR
FACP	FIRE ALARM CONTROL PANEL
TRAN	TRANSPONDER PANEL

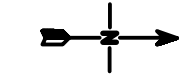




NOTE:
NFS DRAWINGS ARE BASED ON THE PROJECT
ARCHITECT/ENGINEER (A/E) PLANS AND SPECIFICATIONS
FURNISHED TO NFS. A/E IS SOLELY RESPONSIBLE
(NOT NFS) FOR THE TYPE, SIZE, LOCATION, AND
SUITABILITY OF ALL FIRE ALARMS, CONTROL PANELS,
AND OTHER DEVICES SHOWN ON THE A/E PLANS.
NFS DRAWINGS ARE TO SHOW ONLY THE WIRING
DIAGRAMS BETWEEN FIRE ALARM DEVICES AND
CONTROL PANELS. NFS IS NOT RESPONSIBLE FOR
THE INFORMATION SHOWN ON THE A/E PLANS.

UNIVERSITY OF UTAH
ENGINEERING MINES CLASSROOM BUILDING
LEVEL ONE
FIRE ALARM SYSTEM

NFS
NELSON FIRE SYSTEMS
801-468-8300

DRAWN BY: DS
DESIGNED BY: SEE
APPROVED BY: TCT
DATE: 1/26/2007
SCALE: 1/16" = 1'
PROJECT NO: 0062-II258
REV NO: I
DRAWING NAME:
U OF U WARNOCK-EMCB I.DWG.


FIRE ALARM SYSTEM
LEVEL ONE
ADDRESSABLE LOOP NUMBERS

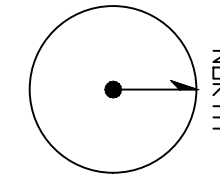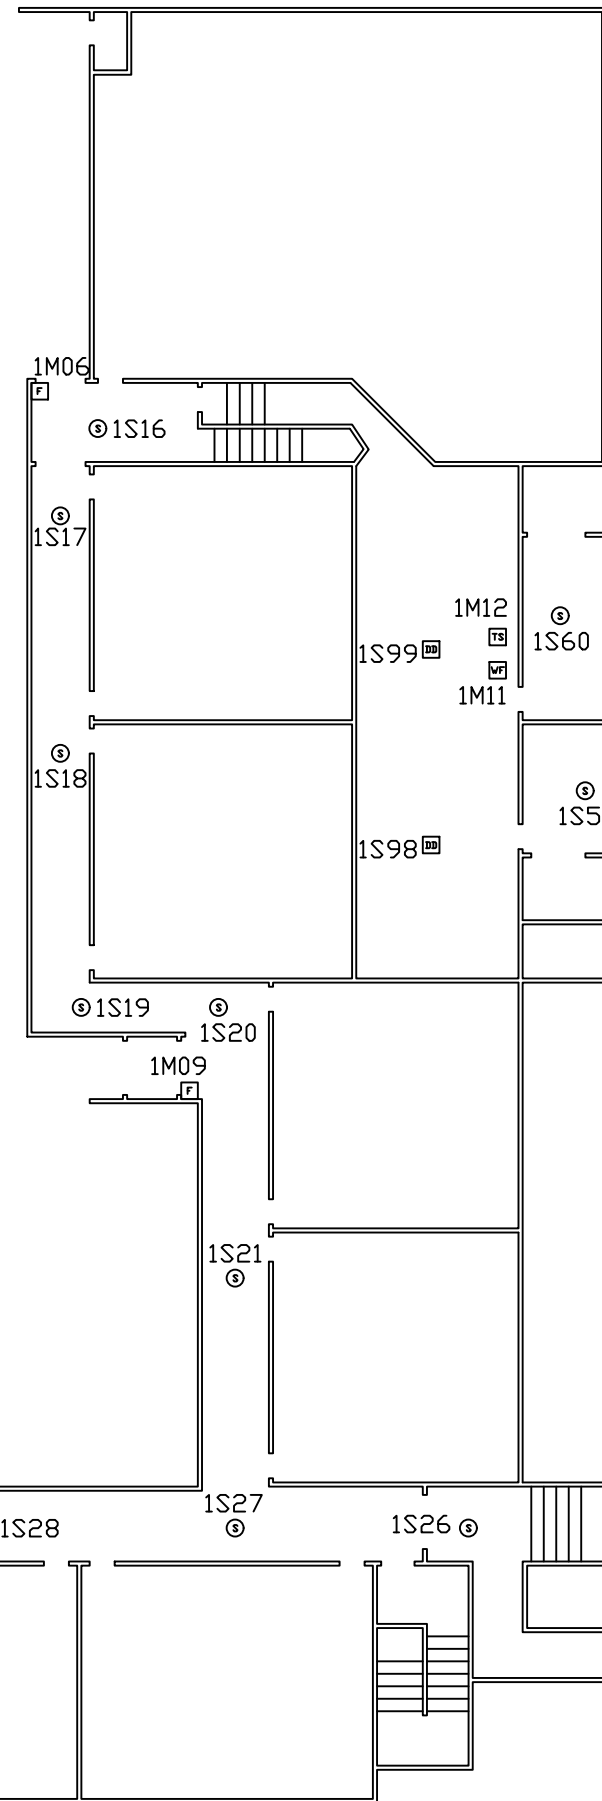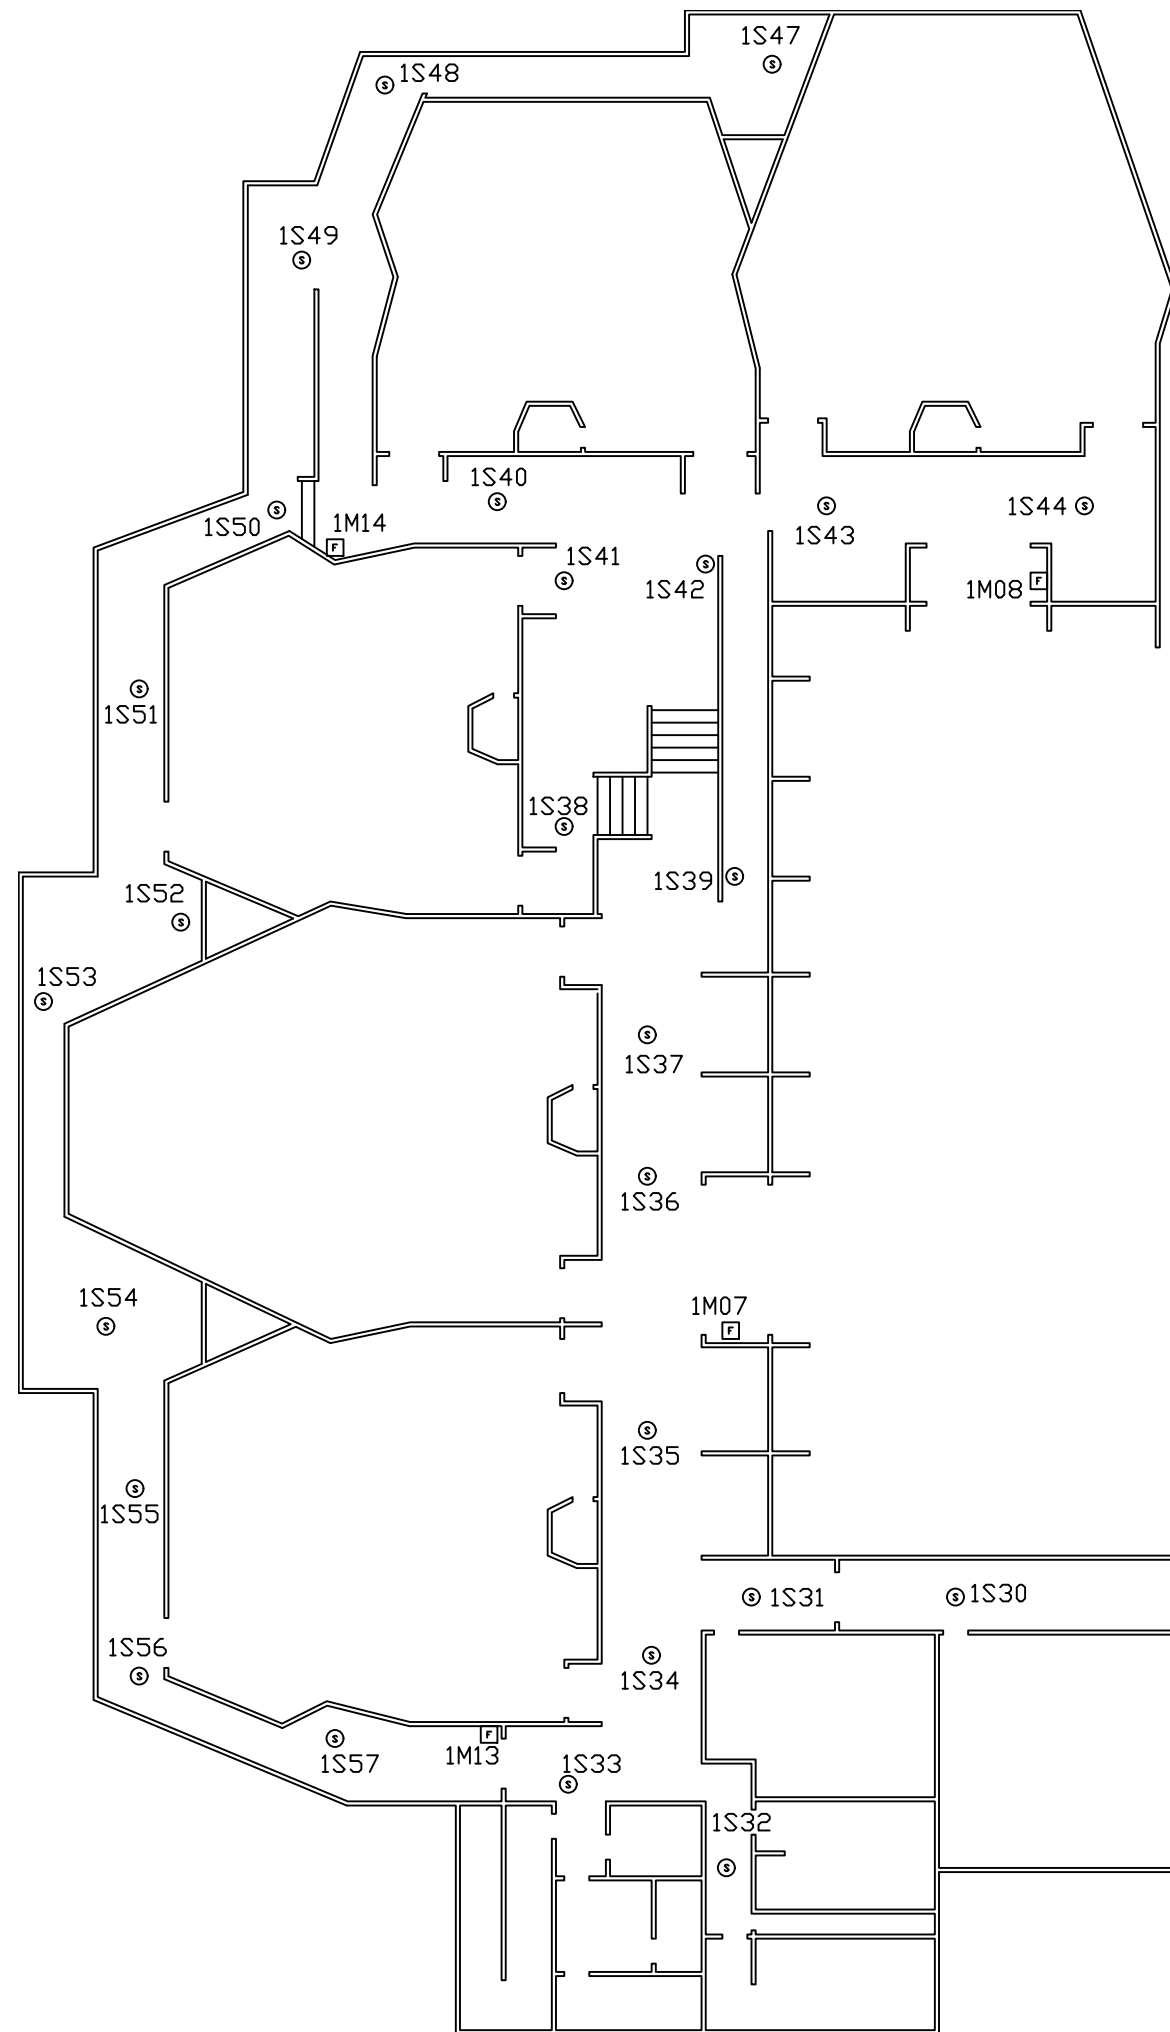

- LEGEND
- ⊙ SMOKE DETECTOR
 - ⌡ MANUAL PULL STATION
 - ▢ DUCT DETECTOR
 - ⌡ WATERFLOW SWITCH
 - ⌡ TAMPER SWITCH

NFS
NELSON FIRE SYSTEMS
801-468-8300

ENGINEERING, MINES CLASSROOM BLDG
LEVEL 1
UNIVERSITY OF UTAH
FIRE ALARM SYSTEM
APRIL 10, 2001
ENCLASS1.DWG

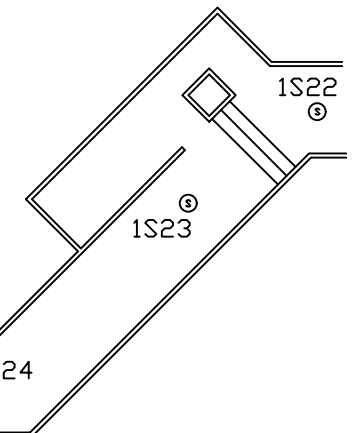

- LEGEND
- ⊙ SMOKE DETECTOR
 - MANUAL PULL STATION
 - ▣ DUCT DETECTOR
 - ▤ WATERFLOW SWITCH
 - ▥ TAMPER SWITCH
 - ▦ PRE-ACTION SYSTEM
 - ▧ REMOTE ANNUNCIATOR
 - ▨ FIRE ALARM CONTROL PANEL
 - ▩ TRANSPONDER PANEL

NFS
NELSON FIRE SYSTEMS
801-468-8300

ENGINEERING, MINES CLASSROOM BLDG
LEVELS 2 & 3
UNIVERSITY OF UTAH
FIRE ALARM SYSTEM
APRIL 10, 2001
ENCLASS2.DWG

