


DEVICE LEGEND	
SYMBOL	DESCRIPTION
⊙	SMOKE DETECTOR W/BASE
⊙	THERMAL DETECTOR
□	MANUAL PULL STATION
□	DUCT SMOKE DETECTOR
□	WATERFLOW SWITCH MONITOR MODULE
□	TAMPER SWITCH MONITOR MODULE
□	STROBE LIGHT
□	SPEAKER/STROBE
□	WEATHERPROOF SPEAKER
□	MONITOR MODULE
□	CONTROL MODULE
□	RELAY- ARB-C
□	DOORHOLDER
□	FIRE ALARM CONTROL PANEL
□	TRANSPONDER PANEL

ADDRESS LABEL CLARIFICATION



— ADDRESSABLE LOOP NUMBER
— SENSOR ("M" MONITOR)
— DEVICE NUMBER

— HORN ("S" STROBE)
— CIRCUIT NUMBER
— DEVICE NUMBER

BALCONY LEVEL

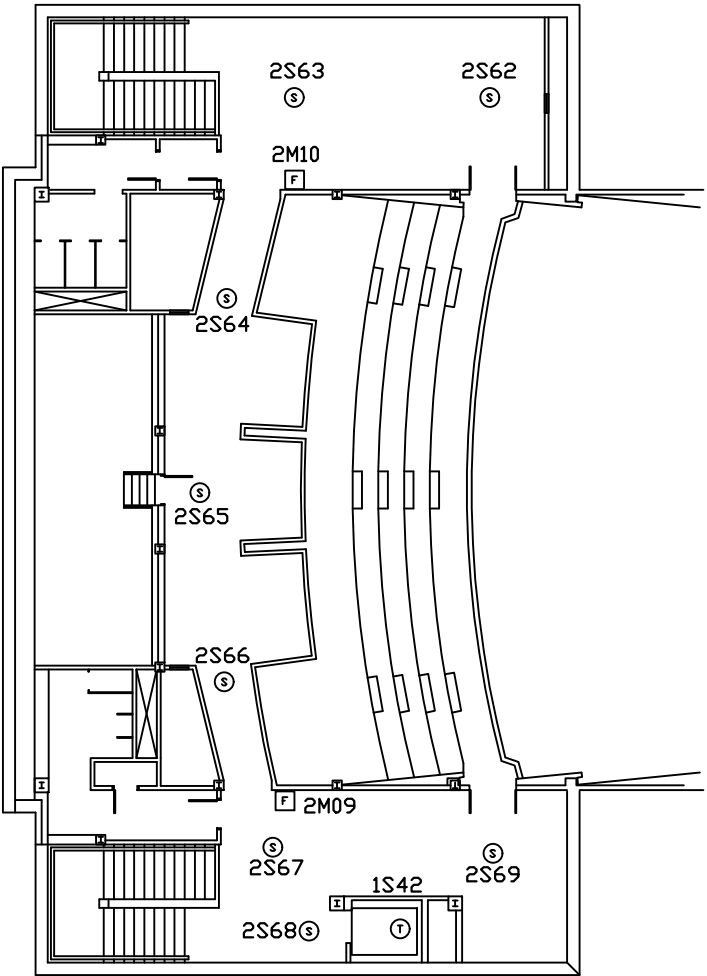

BALCONY LEVEL
LIGHT/SOUND BOOTH

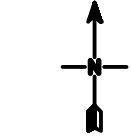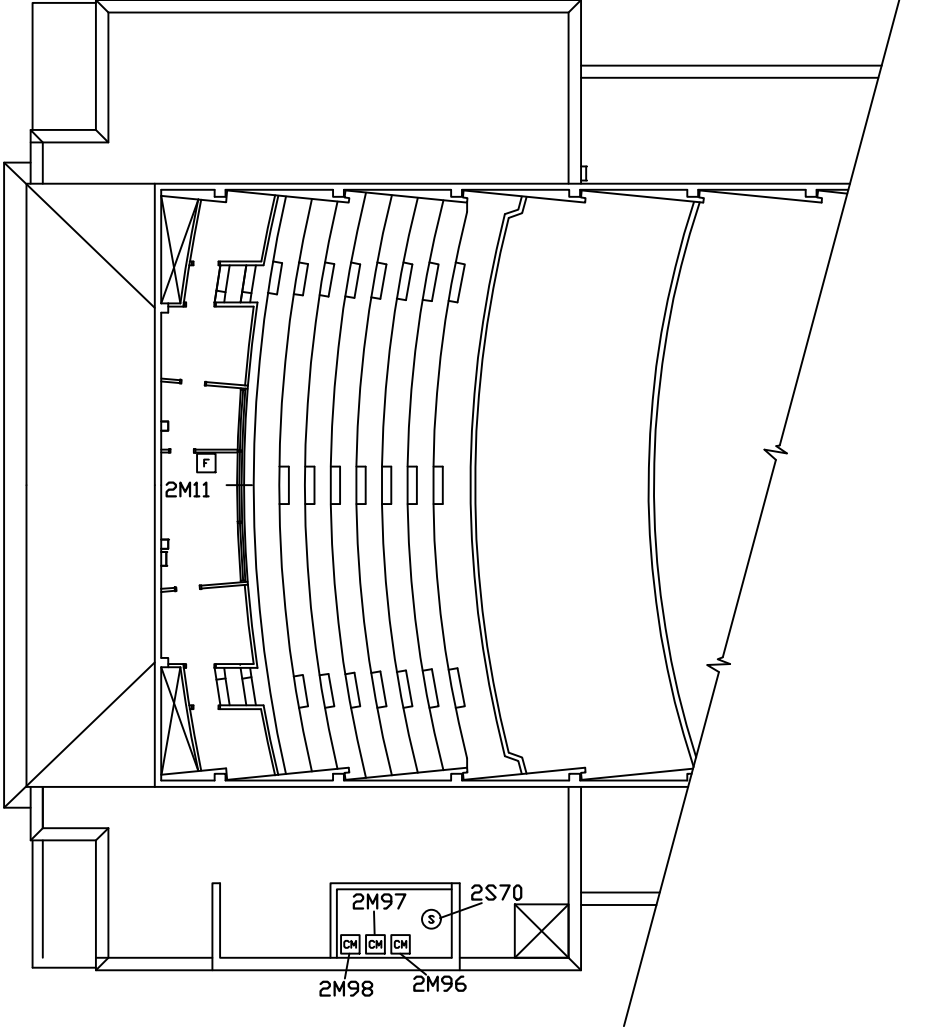

NOTE:
NFS DRAWINGS ARE BASED ON THE PROJECT
ARCHITECT/ENGINEER (A/E) PLANS AND SPECIFICATIONS
FURNISHED TO NFS. A/E IS SOLELY RESPONSIBLE
(NOT NFS) FOR THE TYPE, SIZE, LOCATION, AND
SUITABILITY OF ALL FIRE ALARMS, CONTROL PANELS,
AND OTHER DEVICES SHOWN ON THE A/E PLANS.
NFS DRAWINGS ARE TO SHOW ONLY THE WIRING
AND CONNECTIONS BETWEEN DEVICES AND
CONTROL PANELS. NFS IS NOT RESPONSIBLE FOR
THE INFORMATION SHOWN ON THE A/E PLANS.

UNIVERSITY OF UTAH
BALCONY LEVEL
FIRE ALARM SYSTEM

NFS
NELSON FIRE SYSTEMS
801-468-8300

DRAWN BY: DPS
DESIGNED BY: JGA
APPROVED BY: TCT
DATE: 9/30/2004
SCALE: N.T.S.
PROJECT NO: 066-12126
REV NO: XXXX
DRAWING NAME:
PMTBALCONY.DWG

FIRE ALARM SYSTEM
BALCONY LEVEL
ADDRESSABLE NUMBERS

NFS
FA-B-04

DEVICE LEGEND	
SYMBOL	DESCRIPTION
⊙	SMOKE DETECTOR W/BASE
⊙	THERMAL DETECTOR
⊙	MANUAL PULL STATION
⊙	DUCT SMOKE DETECTOR
⊙	WATERFLOW SWITCH MONITOR MODULE
⊙	TAMPER SWITCH MONITOR MODULE
⊙	STROBE LIGHT
⊙	SPEAKER/STROBE
⊙	WEATHERPROOF SPEAKER
⊙	MONITOR MODULE
⊙	CONTROL MODULE
⊙	RELAY- ARB-C
⊙	DOORHOLDER
⊙	REMOTE ANNUNCIATOR ENCLOSURE
⊙	FIRE ALARM CONTROL PANEL
⊙	TRANSPONDER PANEL


ADDRESS LABEL CLARIFICATION

ADDRESSABLE LOOP NUMBER

SENSOR ("M" MONITOR)

DEVICE NUMBER

1S01

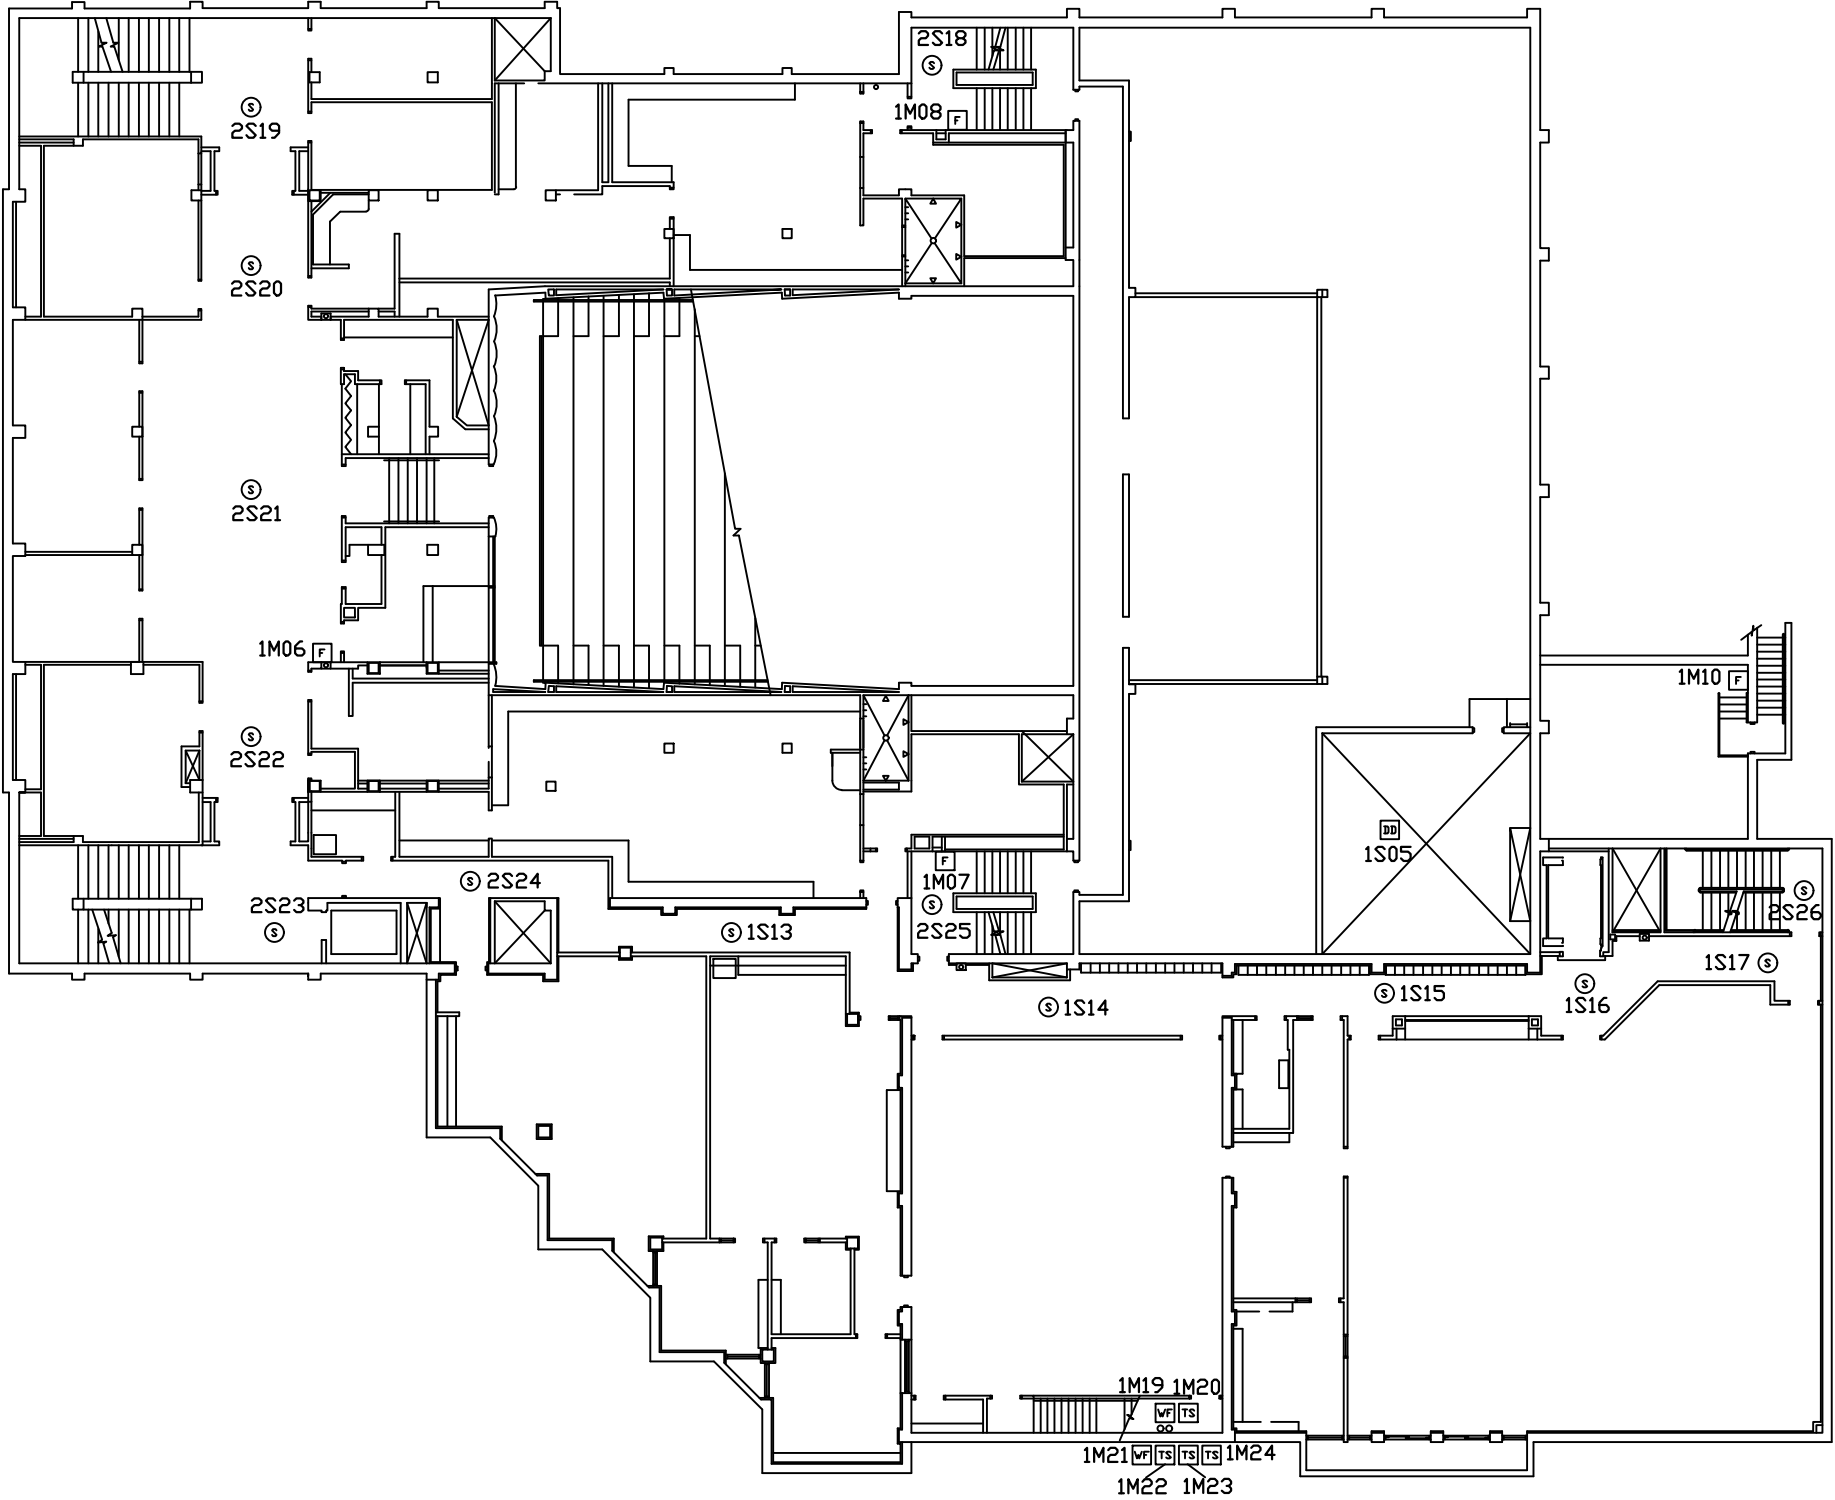

NOTE:
NFS DRAWINGS ARE BASED ON THE PROJECT
ARCHITECT/ENGINEER (A/E) PLANS AND SPECIFICATIONS
FURNISHED TO NFS. A/E IS SOLELY RESPONSIBLE,
(NOT NFS) FOR THE TYPE, SIZE, LOCATION, AND
SUITABILITY OF ALL FIRE ALARMS, CONTROL PANELS,
AND OTHER DEVICES SHOWN ON THE A/E PLANS.
NFS DRAWINGS ARE FOR INFORMATION ONLY. NFS
DRAWS ARE NOT RESPONSIBLE FOR THE TYPE, SIZE,
LOCATION, OR SUITABILITY OF DEVICES SHOWN ON
CONTROL PANELS. NFS IS NOT RESPONSIBLE FOR
THE INFORMATION SHOWN ON THE A/E PLANS.

PIONEER MEMORIAL THEATRE
UNIVERSITY OF UTAH
ADMINISTRATION LEVEL
FIRE ALARM SYSTEM




NFS
NELSON FIRE SYSTEMS
801-468-8300

DRAWN BY: DPS
DESIGNED BY: JGA
APPROVED BY: TCT
DATE: 9/30/2004
SCALE: N.T.S.
PROJECT NO: 066-12126
REV NO: XXXX
DRAWING NAME:
PMTADMIN.DWG

FIRE ALARM SYSTEM
ADMINISTRATION LEVEL
ADDRESSABLE NUMBERS

NFS
FA-A-04

DEVICE LEGEND	
SYMBOL	DESCRIPTION
Ⓢ	SMOKE DETECTOR W/BASE
Ⓢ	THERMAL DETECTOR
Ⓢ	MANUAL PULL STATION
Ⓢ	DUCT SMOKE DETECTOR
Ⓢ	WATERFLOW SWITCH MONITOR MODULE
Ⓢ	TAMPER SWITCH MONITOR MODULE
Ⓢ	STROBE LIGHT
Ⓢ	SPEAKER/STROBE
Ⓢ	WEATHERPROOF SPEAKER
Ⓢ	MONITOR MODULE
Ⓢ	CONTROL MODULE
Ⓢ	RELAY- ARB-C
Ⓢ	DOORHOLDER
Ⓢ	REMOTE ANNUNCIATOR ENCLOSURE
Ⓢ	FIRE ALARM CONTROL PANEL
Ⓢ	TRANSPONDER PANEL

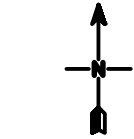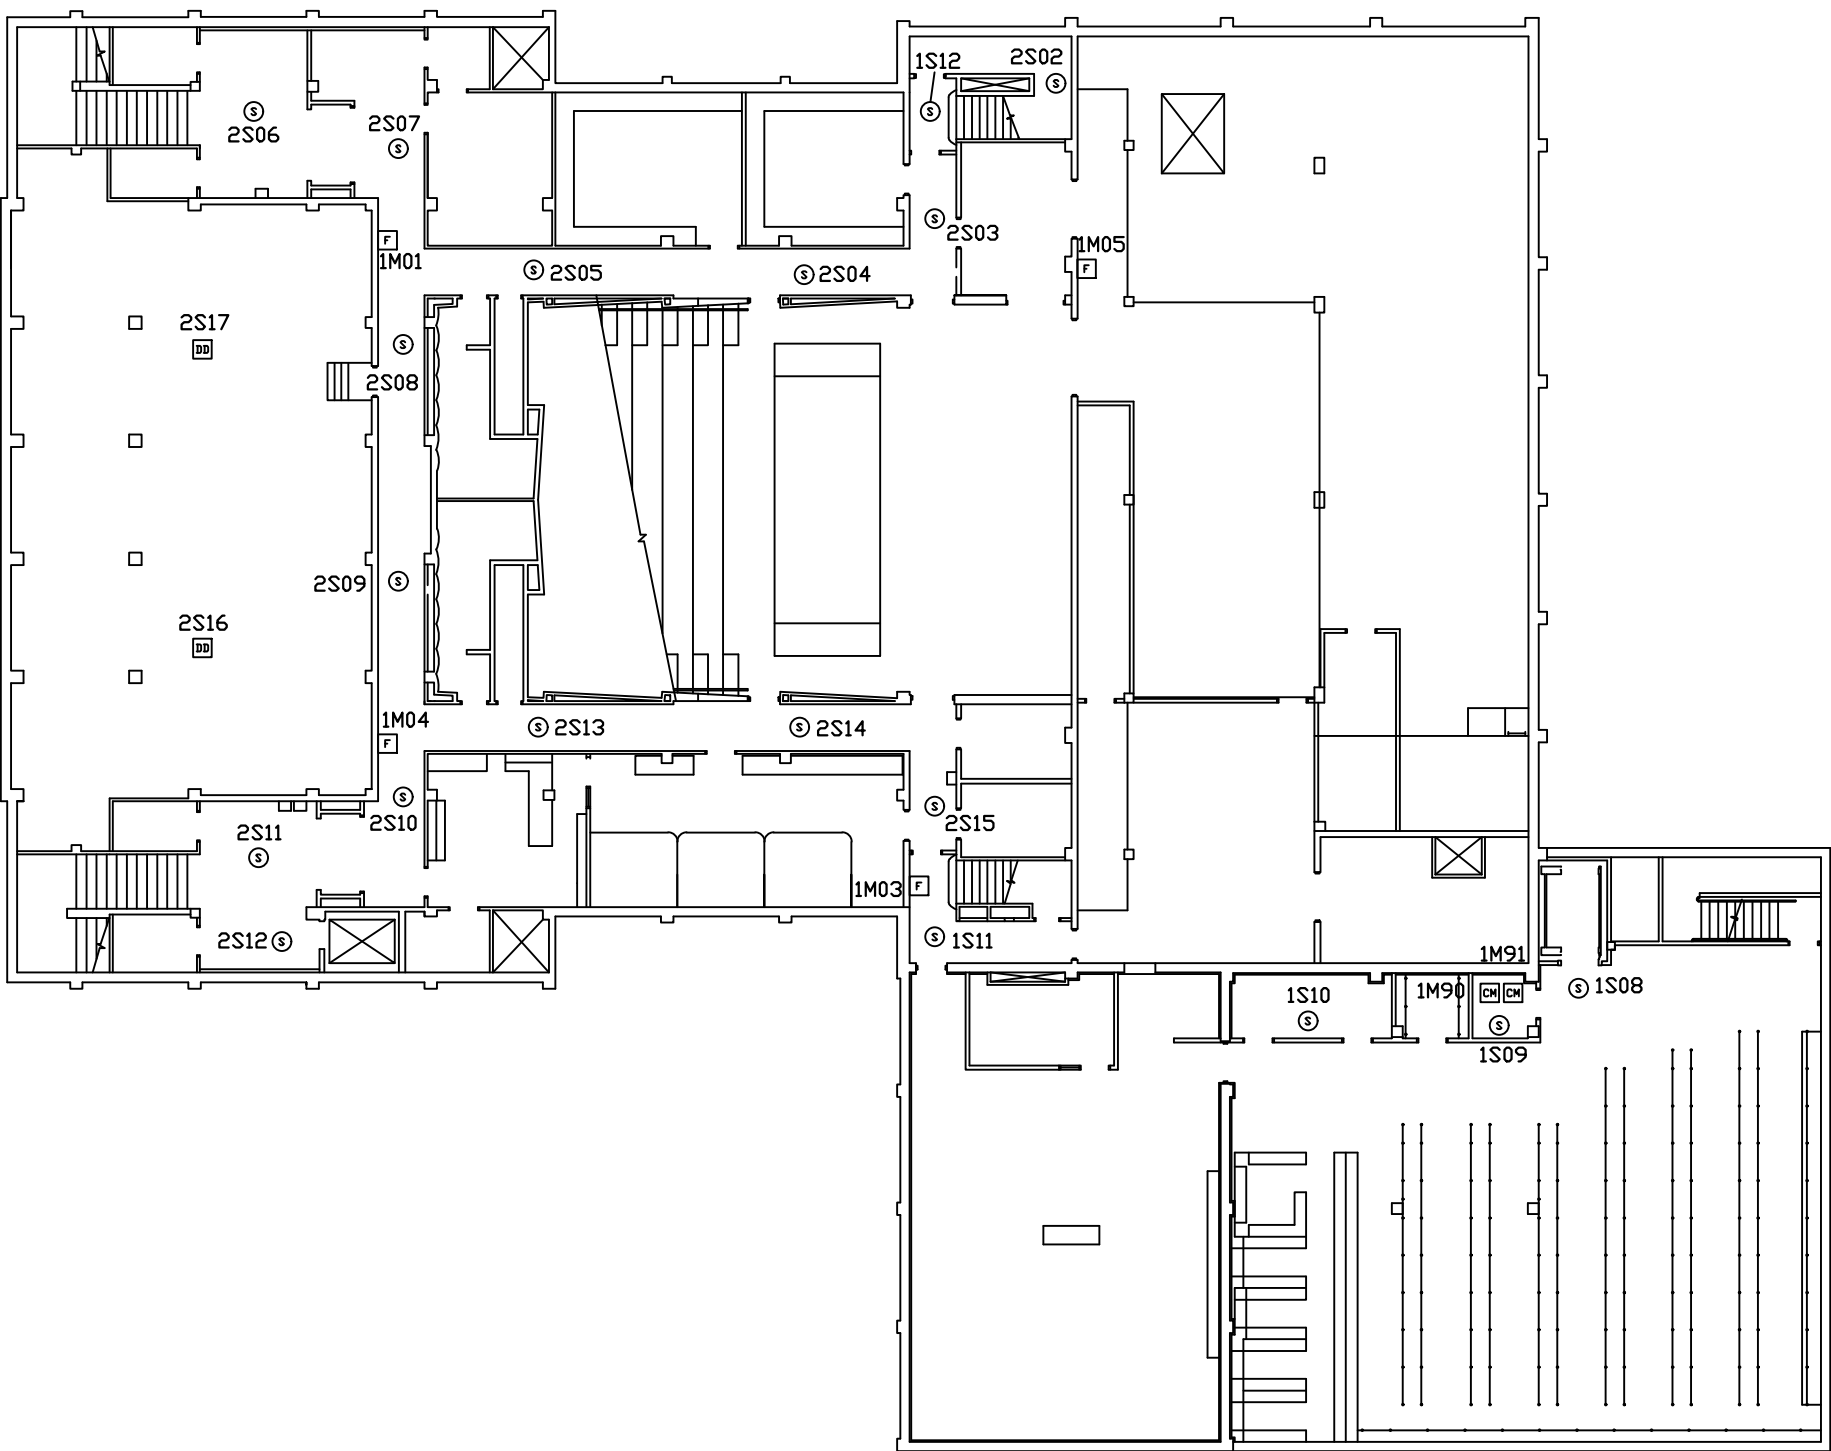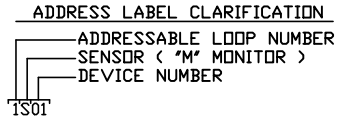

NOTE:
NFS DRAWINGS ARE BASED ON THE PROJECT
ARCHITECT/ENGINEER (A/E) PLANS AND SPECIFICATIONS
FURNISHED TO NFS. A/E IS SOLELY RESPONSIBLE,
(NOT NFS) FOR THE TYPE, SIZE, LOCATION, AND
SUITABILITY OF ALL FIRE ALARMS, CONTROL PANELS,
AND OTHER DEVICES SHOWN ON THE A/E PLANS.
NFS DRAWINGS ARE FOR INFORMATION ONLY. NFS
DRAFTER, ENGINEER, AND PROJECT MANAGER
CONTROL PANELS. NFS IS NOT RESPONSIBLE FOR
THE INFORMATION SHOWN ON THE A/E PLANS.

PIONEER MEMORIAL THEATRE
UNIVERSITY OF UTAH
COSTUME LEVEL
FIRE ALARM SYSTEM



NFS
NELSON FIRE SYSTEMS
801-468-8300

DRAWN BY:	DPS
DESIGNED BY:	JGA
APPROVED BY:	TCT
DATE:	9/30/2004
SCALE:	N.T.S.
PROJECT NO:	066-12126
REV NO:	XXXX
DRAWING NAME:	PMTCOSTUME.DWG

FIRE ALARM SYSTEM
COSTUME LEVEL
ADDRESSABLE NUMBERS

NFS
FA-C-04

DEVICE LEGEND	
SYMBOL	DESCRIPTION
⊙	SMOKE DETECTOR W/BASE
⊙	THERMAL DETECTOR
⊙	MANUAL PULL STATION
⊙	DUCT SMOKE DETECTOR
⊙	WATERFLOW SWITCH MONITOR MODULE
⊙	TAMPER SWITCH MONITOR MODULE
⊙	STROBE LIGHT
⊙	SPEAKER/STROBE
⊙	WEATHERPROOF SPEAKER
⊙	MONITOR MODULE
⊙	CONTROL MODULE
⊙	RELAY- ARB-C
⊙	DOORHOLDER
⊙	REMOTE ANNUNCIATOR ENCLOSURE
⊙	FIRE ALARM CONTROL PANEL
⊙	TRANSPONDER PANEL

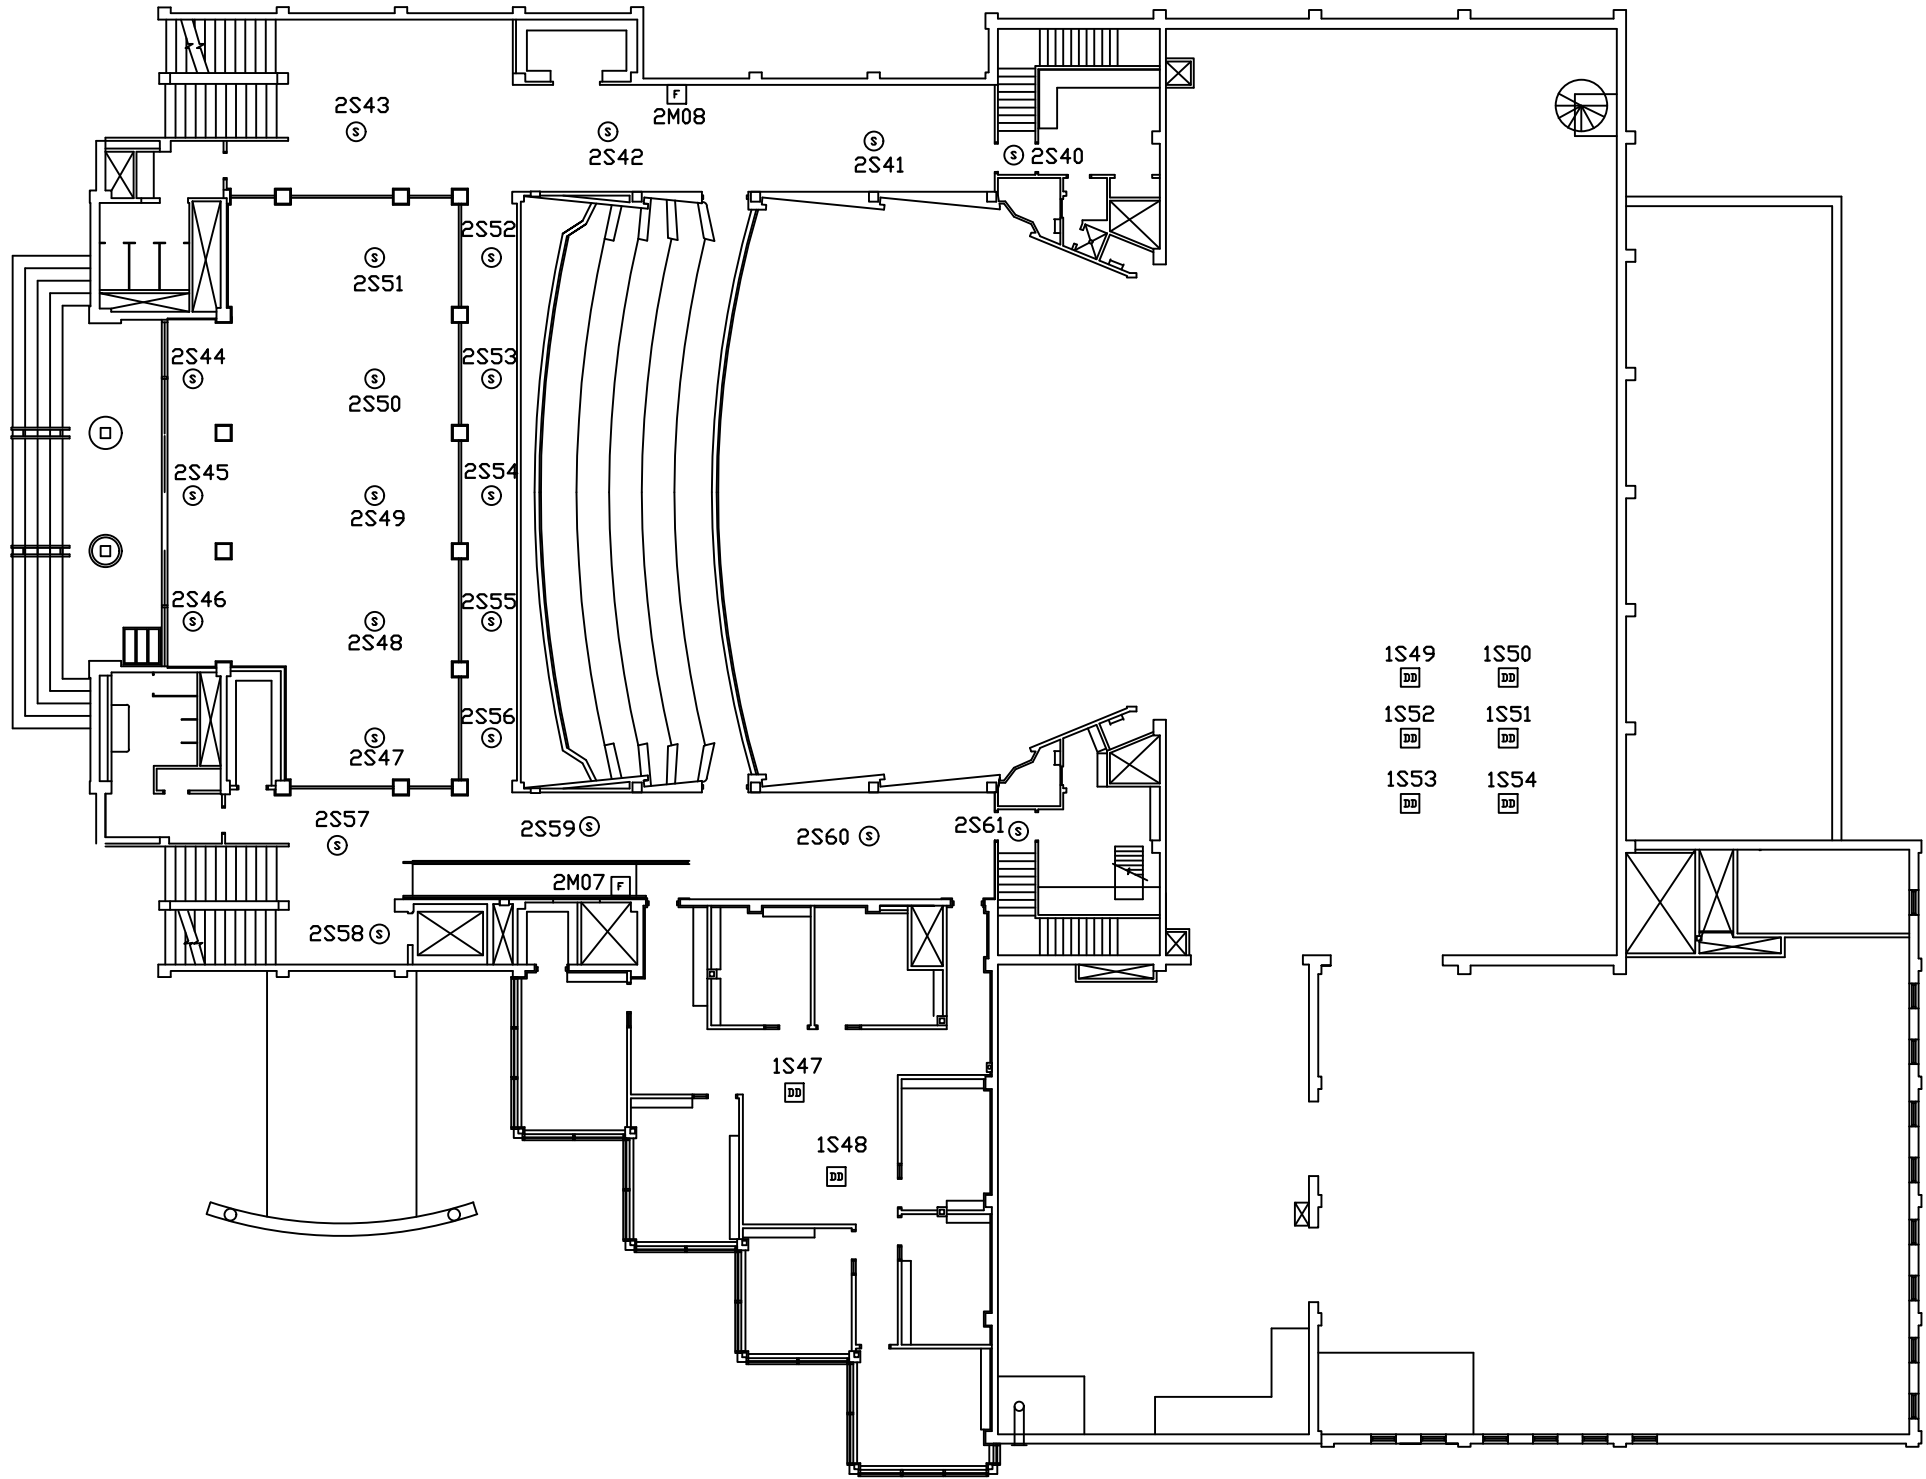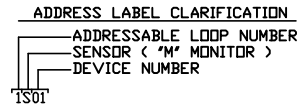

NOTE:
NFS DRAWINGS ARE BASED ON THE PROJECT
ARCHITECT/ENGINEER (A/E) PLANS AND SPECIFICATIONS
FURNISHED TO NFS. A/E IS SOLELY RESPONSIBLE
(NOT NFS) FOR THE TYPE, SIZE, LOCATION, AND
SUITABILITY OF ALL FIRE ALARMS, CONTROL PANELS,
AND OTHER DEVICES SHOWN ON THE A/E PLANS.
NFS DRAWINGS ARE TO SHOW ONLY THE WIRING
AND ARE NOT TO BE USED FOR CONSTRUCTION OF
CONTROL PANELS. NFS IS NOT RESPONSIBLE FOR
THE INFORMATION SHOWN ON THE A/E PLANS.

PIONEER MEMORIAL THEATRE
UNIVERSITY OF UTAH
LOGE LEVEL
FIRE ALARM SYSTEM

NFS
NELSON FIRE SYSTEMS
801-468-8300

DRAWN BY:	DPS
DESIGNED BY:	JGA
APPROVED BY:	TCT
DATE:	9/30/2004
SCALE:	N.T.S.
PROJECT NO:	066-12126
REV NO:	XXXX
DRAWING NAME:	PMTLOGE.DWG


FIRE ALARM SYSTEM
LOGE LEVEL
ADDRESSABLE NUMBERS

NFS

FA-L-04

DEVICE LEGEND	
SYMBOL	DESCRIPTION
⊙	SMOKE DETECTOR W/BASE
⊙	THERMAL DETECTOR
⊙	MANUAL PULL STATION
⊙	DUCT SMOKE DETECTOR
⊙	WATERFLOW SWITCH MONITOR MODULE
⊙	TAMPER SWITCH MONITOR MODULE
⊙	STROBE LIGHT
⊙	SPEAKER/STROBE
⊙	WEATHERPROOF SPEAKER
⊙	MONITOR MODULE
⊙	CONTROL MODULE
⊙	RELAY- ARB-C
⊙	DOORHOLDER
⊙	REMOTE ANNUNCIATOR ENCLOSURE
⊙	FIRE ALARM CONTROL PANEL
⊙	TRANSPONDER PANEL

ADDRESS LABEL CLARIFICATION
ADDRESSABLE LOOP NUMBER
SENSOR ("M" MONITOR)
DEVICE NUMBER

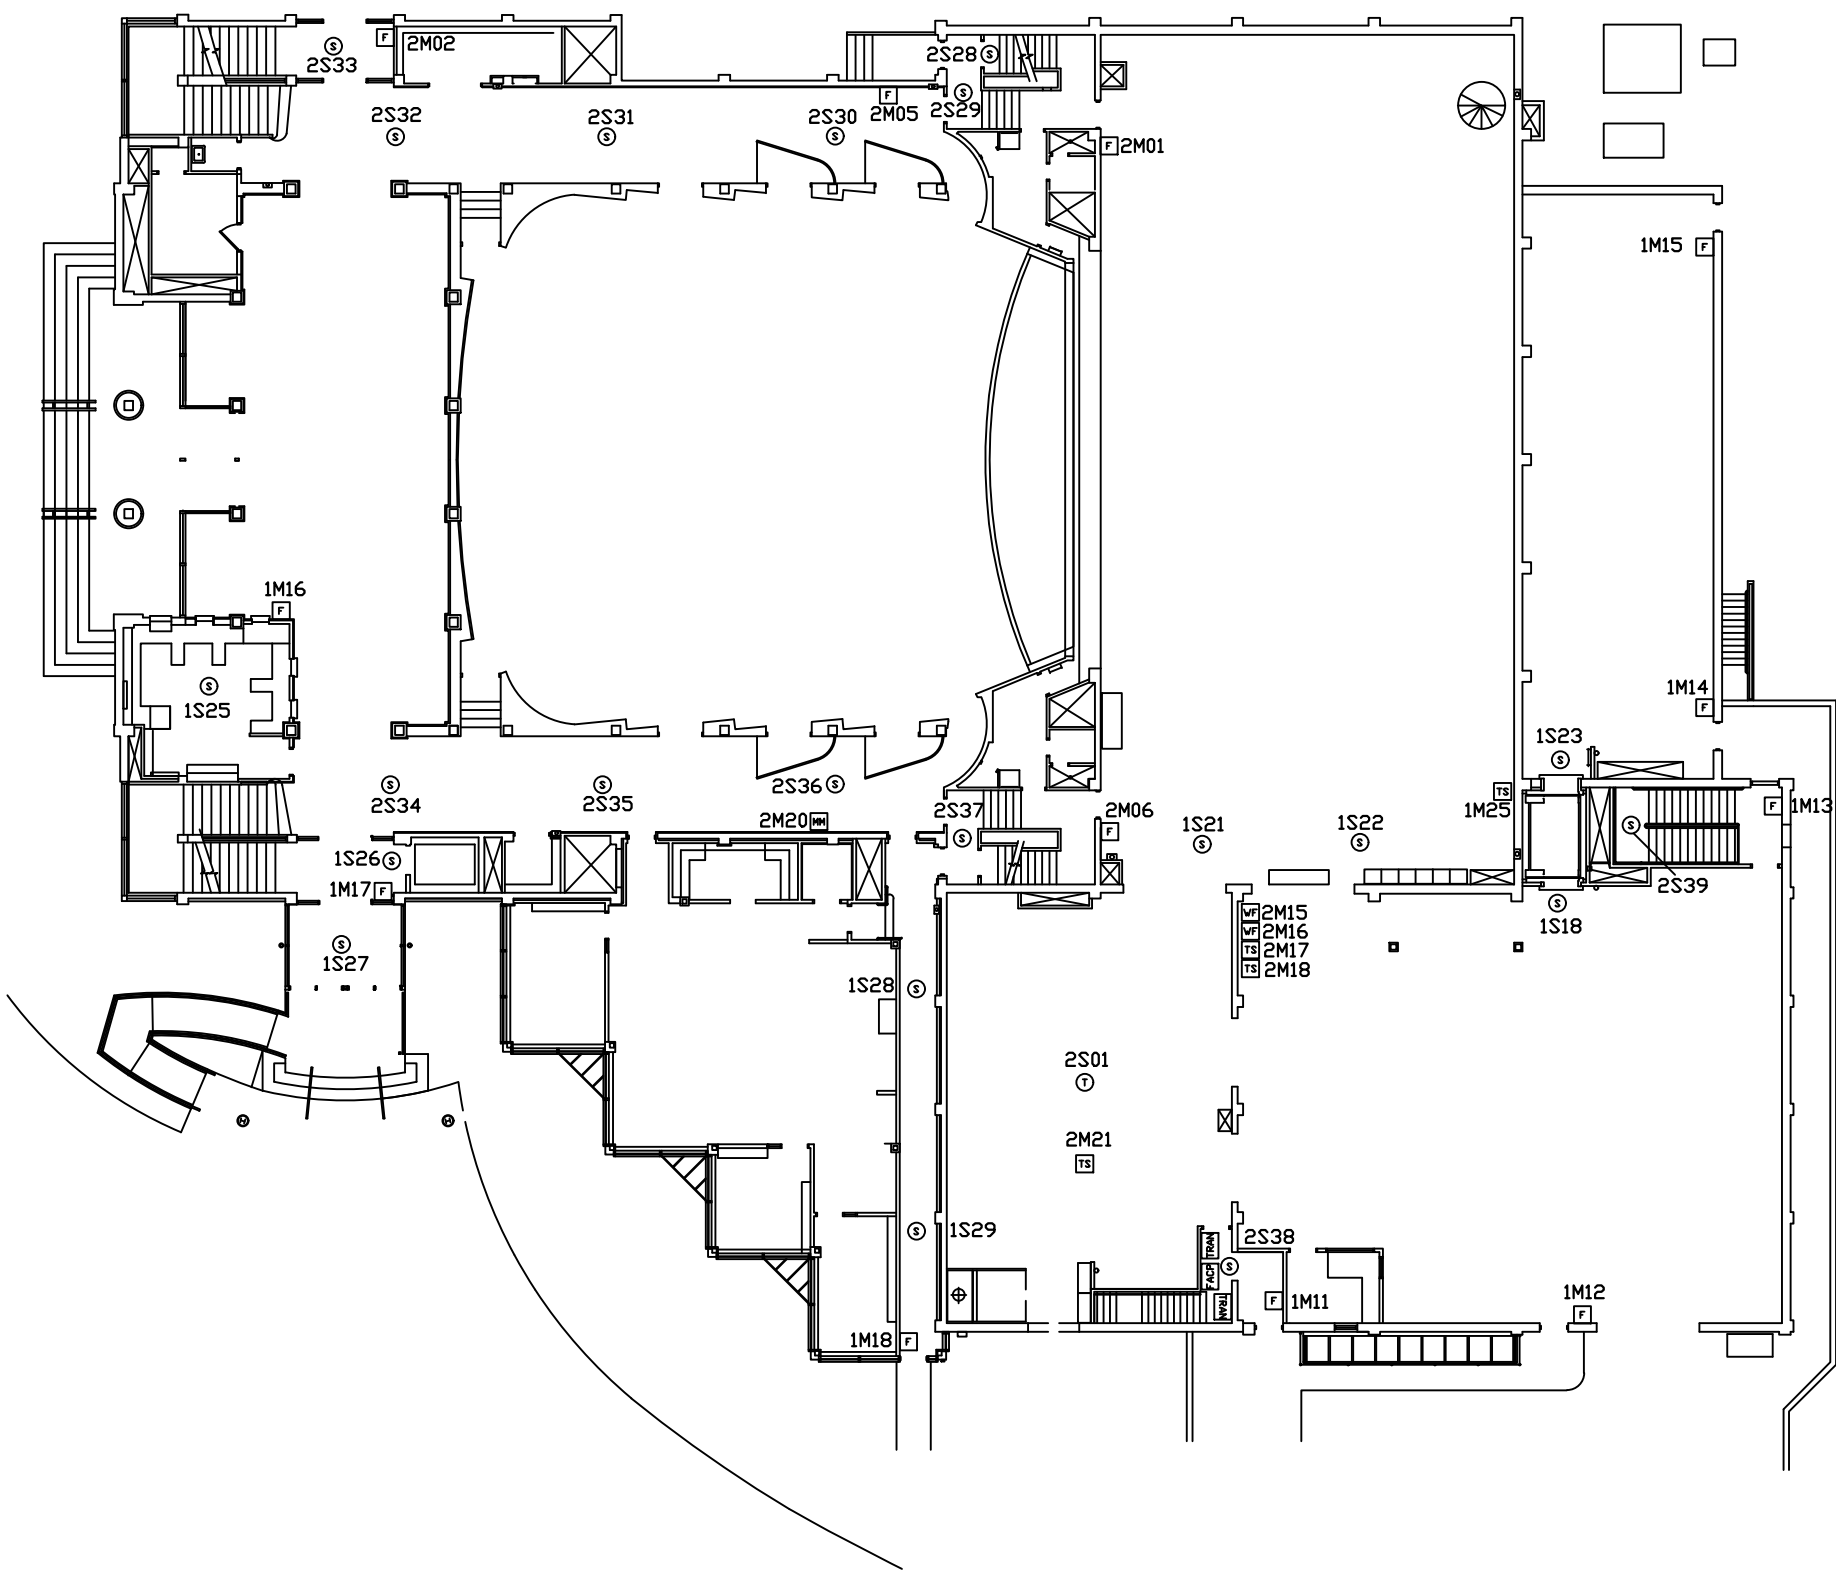

NOTE:
NFS DRAWINGS ARE BASED ON THE PROJECT
ARCHITECT/ENGINEER (A/E) PLANS AND SPECIFICATIONS
FURNISHED TO NFS. A/E IS SOLELY RESPONSIBLE
(NOT NFS) FOR THE TYPE, SIZE, LOCATION, AND
SUITABILITY OF ALL FIRE ALARMS, CONTROL PANELS,
AND OTHER DEVICES SHOWN ON THE A/E PLANS.
NFS DRAWINGS ARE TO SHOW ONLY THE WIRING
DIAGRAM BETWEEN THE A/E PLANS AND THE
CONTROL PANELS. NFS IS NOT RESPONSIBLE FOR
THE INFORMATION SHOWN ON THE A/E PLANS.

PIONEER MEMORIAL THEATRE
UNIVERSITY OF UTAH
MAIN LEVEL
FIRE ALARM SYSTEM

NFS
NELSON FIRE SYSTEMS
801-468-8300

DRAWN BY:	DPS
DESIGNED BY:	JGA
APPROVED BY:	TCT
DATE:	1/8/2010
SCALE:	N.T.S.
PROJECT NO:	066-12126
REV NO:	XXXX
DRAWING NAME:	FMTMAIN.DWG

FIRE ALARM SYSTEM
MAIN LEVEL
ADDRESSABLE NUMBERS

NFS
FA-M-04