


DEVICE LEGEND	
SYMBOL	DESCRIPTION
(S)	SMOKE DETECTOR
(T)	HEAT DETECTOR
(F)	MANUAL PULL STATION
(DD)	DUCT DETECTOR
(TS)	TAMPER SWITCH
(WF)	WATERFLOW SWITCH
(MM)	MONITOR MODULE
(FE)	EVM EXTINGUISHER MONITORING
(CM)	CONTROL MODULE
(RA)	REMOTE ANNUNCIATOR
(LOC)	LOCAL OPERATING CONSOLE
(TRAN)	TRANSPONDER PANEL
(FACU)	FIRE ALARM CONTROL UNIT
(VLC)	VESDA LASER COMPACT
(VPS)	VESDA POWER SUPPLY

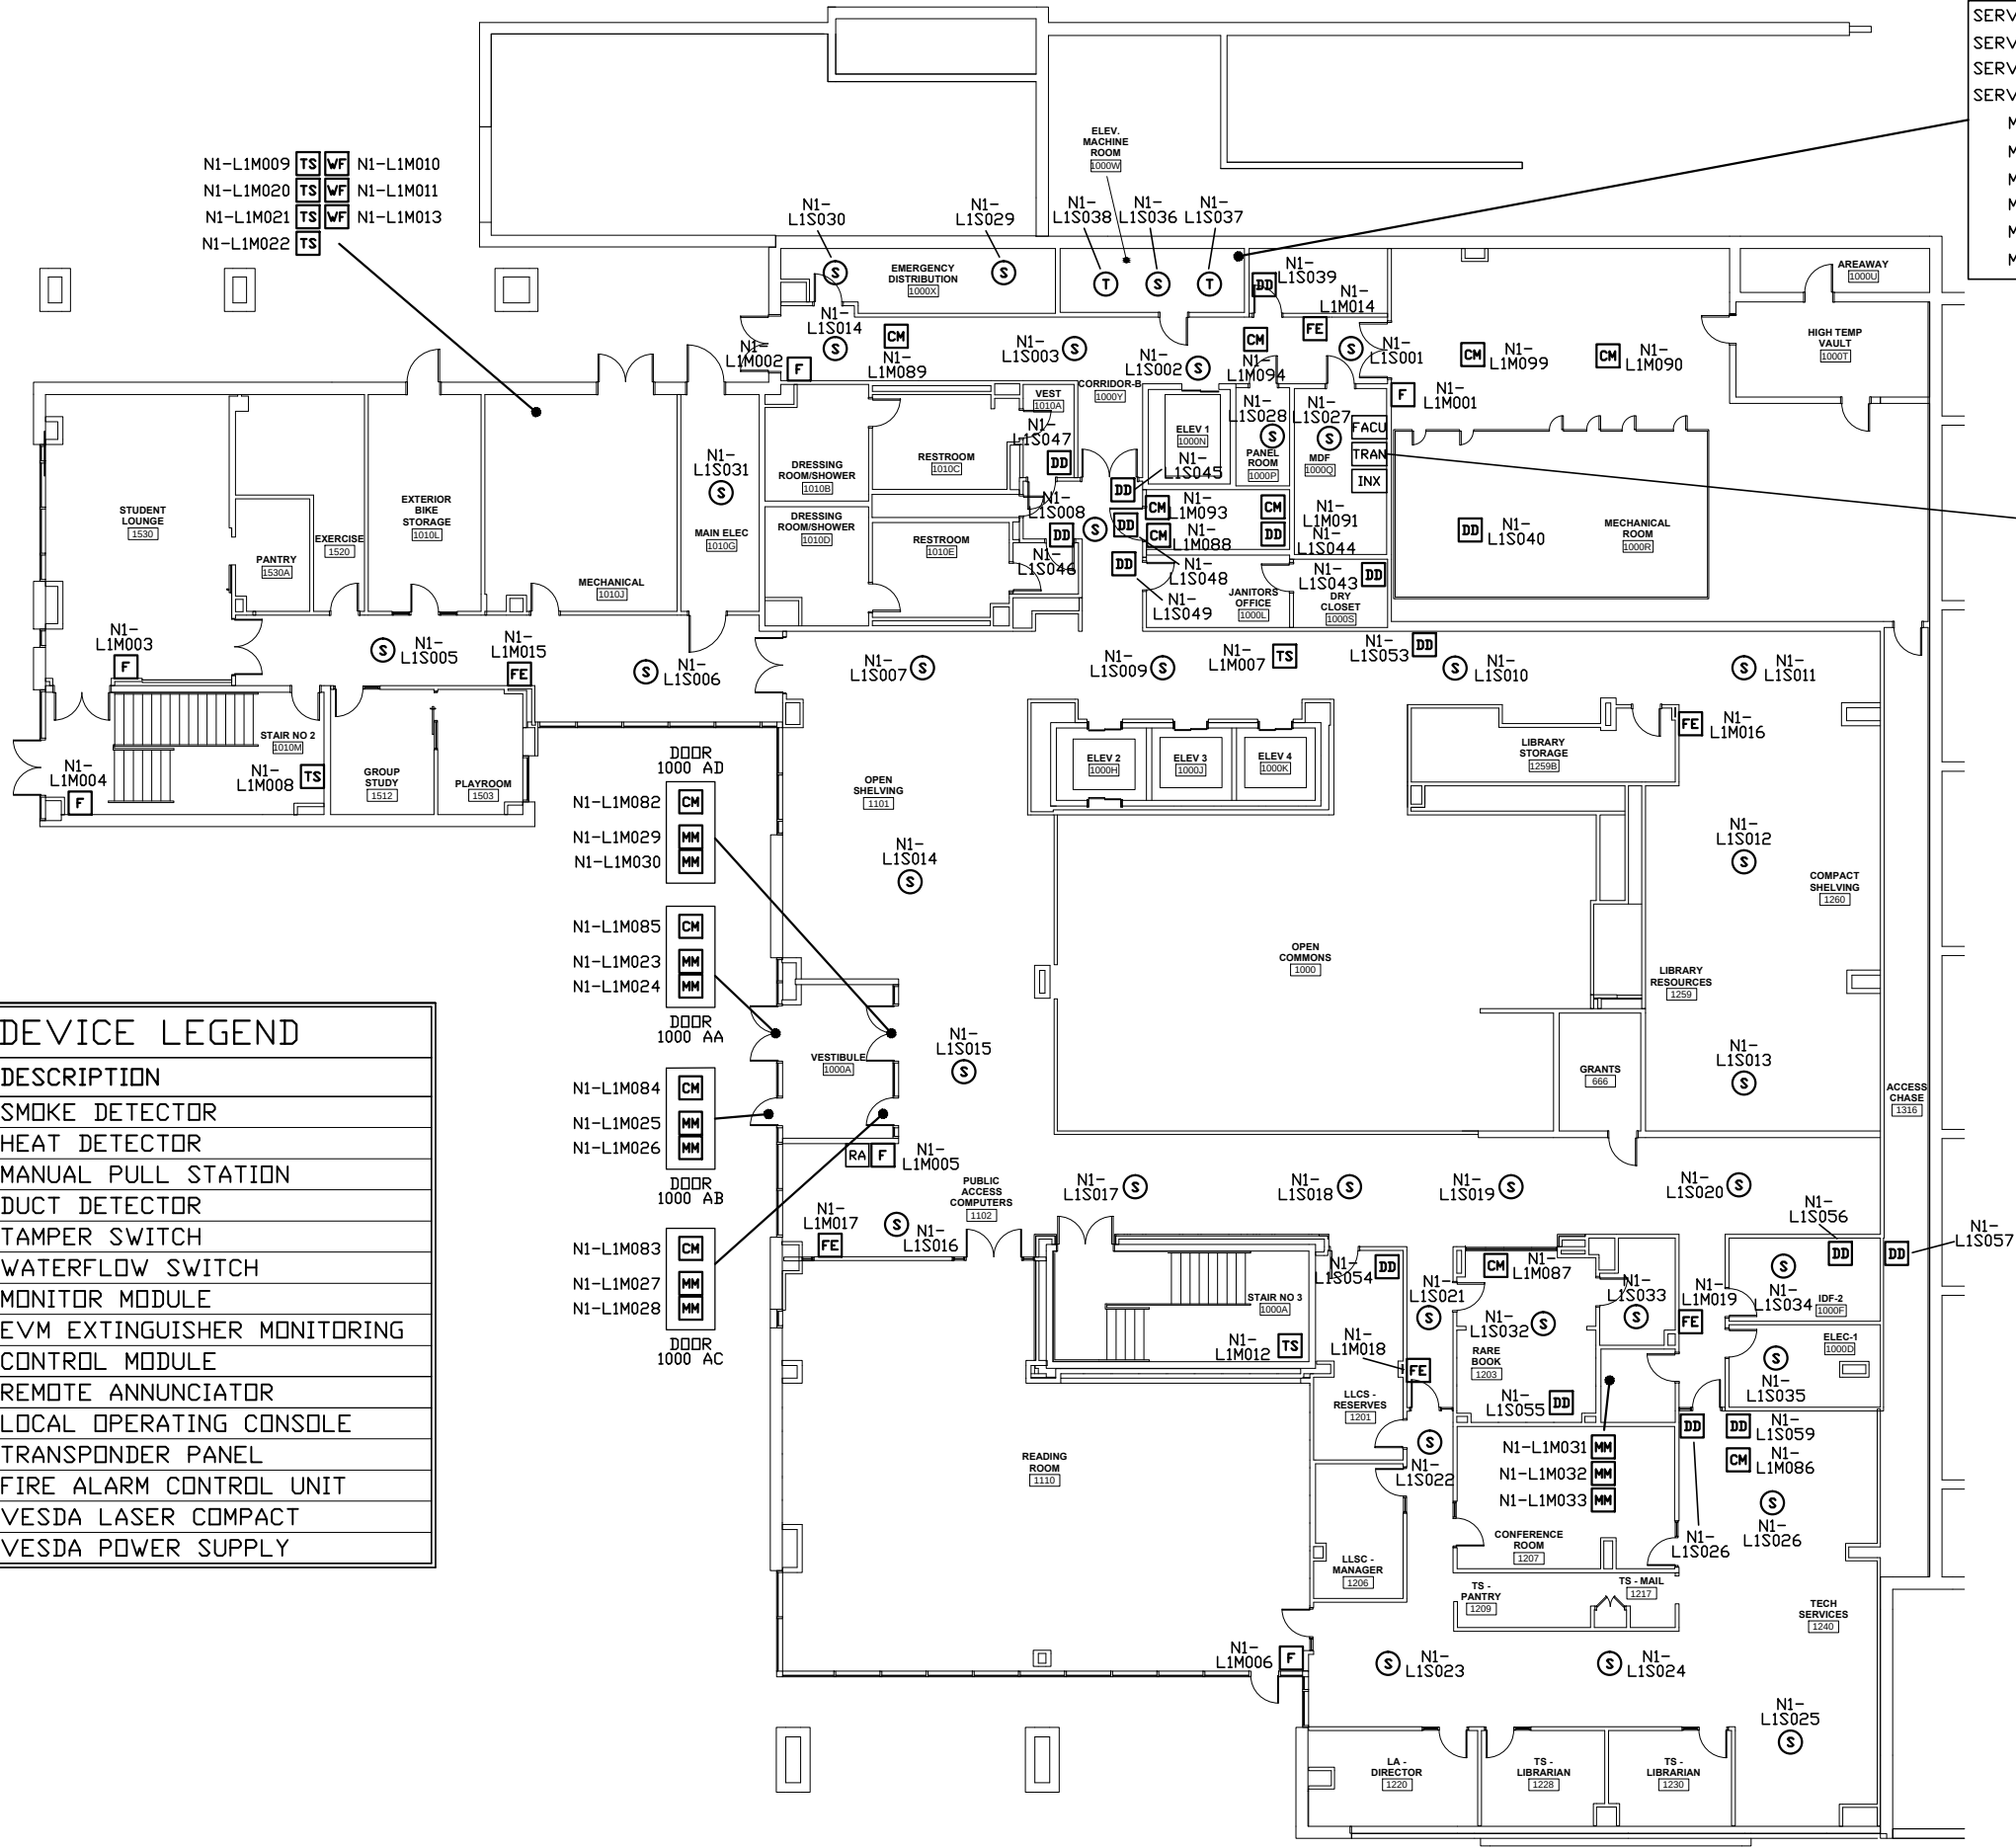

- SERVICE ELEV. CM N1-L1M098 RECALL TO MAIN
- SERVICE ELEV. CM N1-L1M097 RECALL TO ALT.
- SERVICE ELEV. CM N1-L1M096 HAT FLASH
- SERVICE ELEV. CM N1-L1M095 SHUNT TRIP
- MAIN ELEV. CM N1-L1M076 RECALL TO MAIN
- MAIN ELEV. CM N1-L1M077 RECALL TO ALT.
- MAIN ELEV. CM N1-L1M078 HAT FLASH
- MAIN ELEV. CM N1-L1M079 SHUNT TRIP
- MAIN ELEV. CM N1-L1M080 SHUNT TRIP
- MAIN ELEV. CM N1-L1M081 SHUNT TRIP

- CM N1-L1M060 1ST FLR SPEAKER CIRCUIT
- CM N1-L1M061 2ND FLR SPEAKER CIRCUIT
- CM N1-L1M062 1ST FLR SPEAKER CIRCUIT
- CM N1-L1M063 3RD FLR SPEAKER CIRCUIT
- CM N1-L1M064 2ND FLR SPEAKER CIRCUIT
- CM N1-L1M065 3RD FLR SPEAKER CIRCUIT
- CM N1-L1M066 4TH FLR SPEAKER CIRCUIT
- CM N1-L1M067 5TH FLR SPEAKER CIRCUIT
- CM N1-L1M068 4TH FLR SPEAKER CIRCUIT
- CM N1-L1M069 6TH FLR SPEAKER CIRCUIT
- CM N1-L1M070 5TH FLR SPEAKER CIRCUIT
- CM N1-L1M071 SPARE SPEAKER CIRCUIT
- CM N1-L1M092 SECURITY INTERFACE
- MM N1-L1M035 LEVEL 1 TRANSPONDER PANEL
- MM N1-L1M036 AMP FAULT SUPERVISION
- MM N1-L1M037 ASM SUPERVISION

UNIVERSITY OF UTAH
QUINNEY SCHOOL OF LAW
LEVEL I
SOUTH CAMPUS DRIVE
SALT LAKE CITY, UTAH
FIRE ALARM SYSTEM


NFS
NELSON FIRE SYSTEMS
801-468-8300

DRAWN BY:	AK
DESIGNED BY:	XXXX
APPROVED BY:	DPS
DATE:	6/22/15
SCALE:	N.T.S.
PROJECT NO:	XXXX
REV NO:	XXXX
DRAWING NAME:	QUINNEY LAW FM I.DWG

FIRE ALARM SYSTEM
FINAL MAP
LEVEL I

PAGE:
FA-I



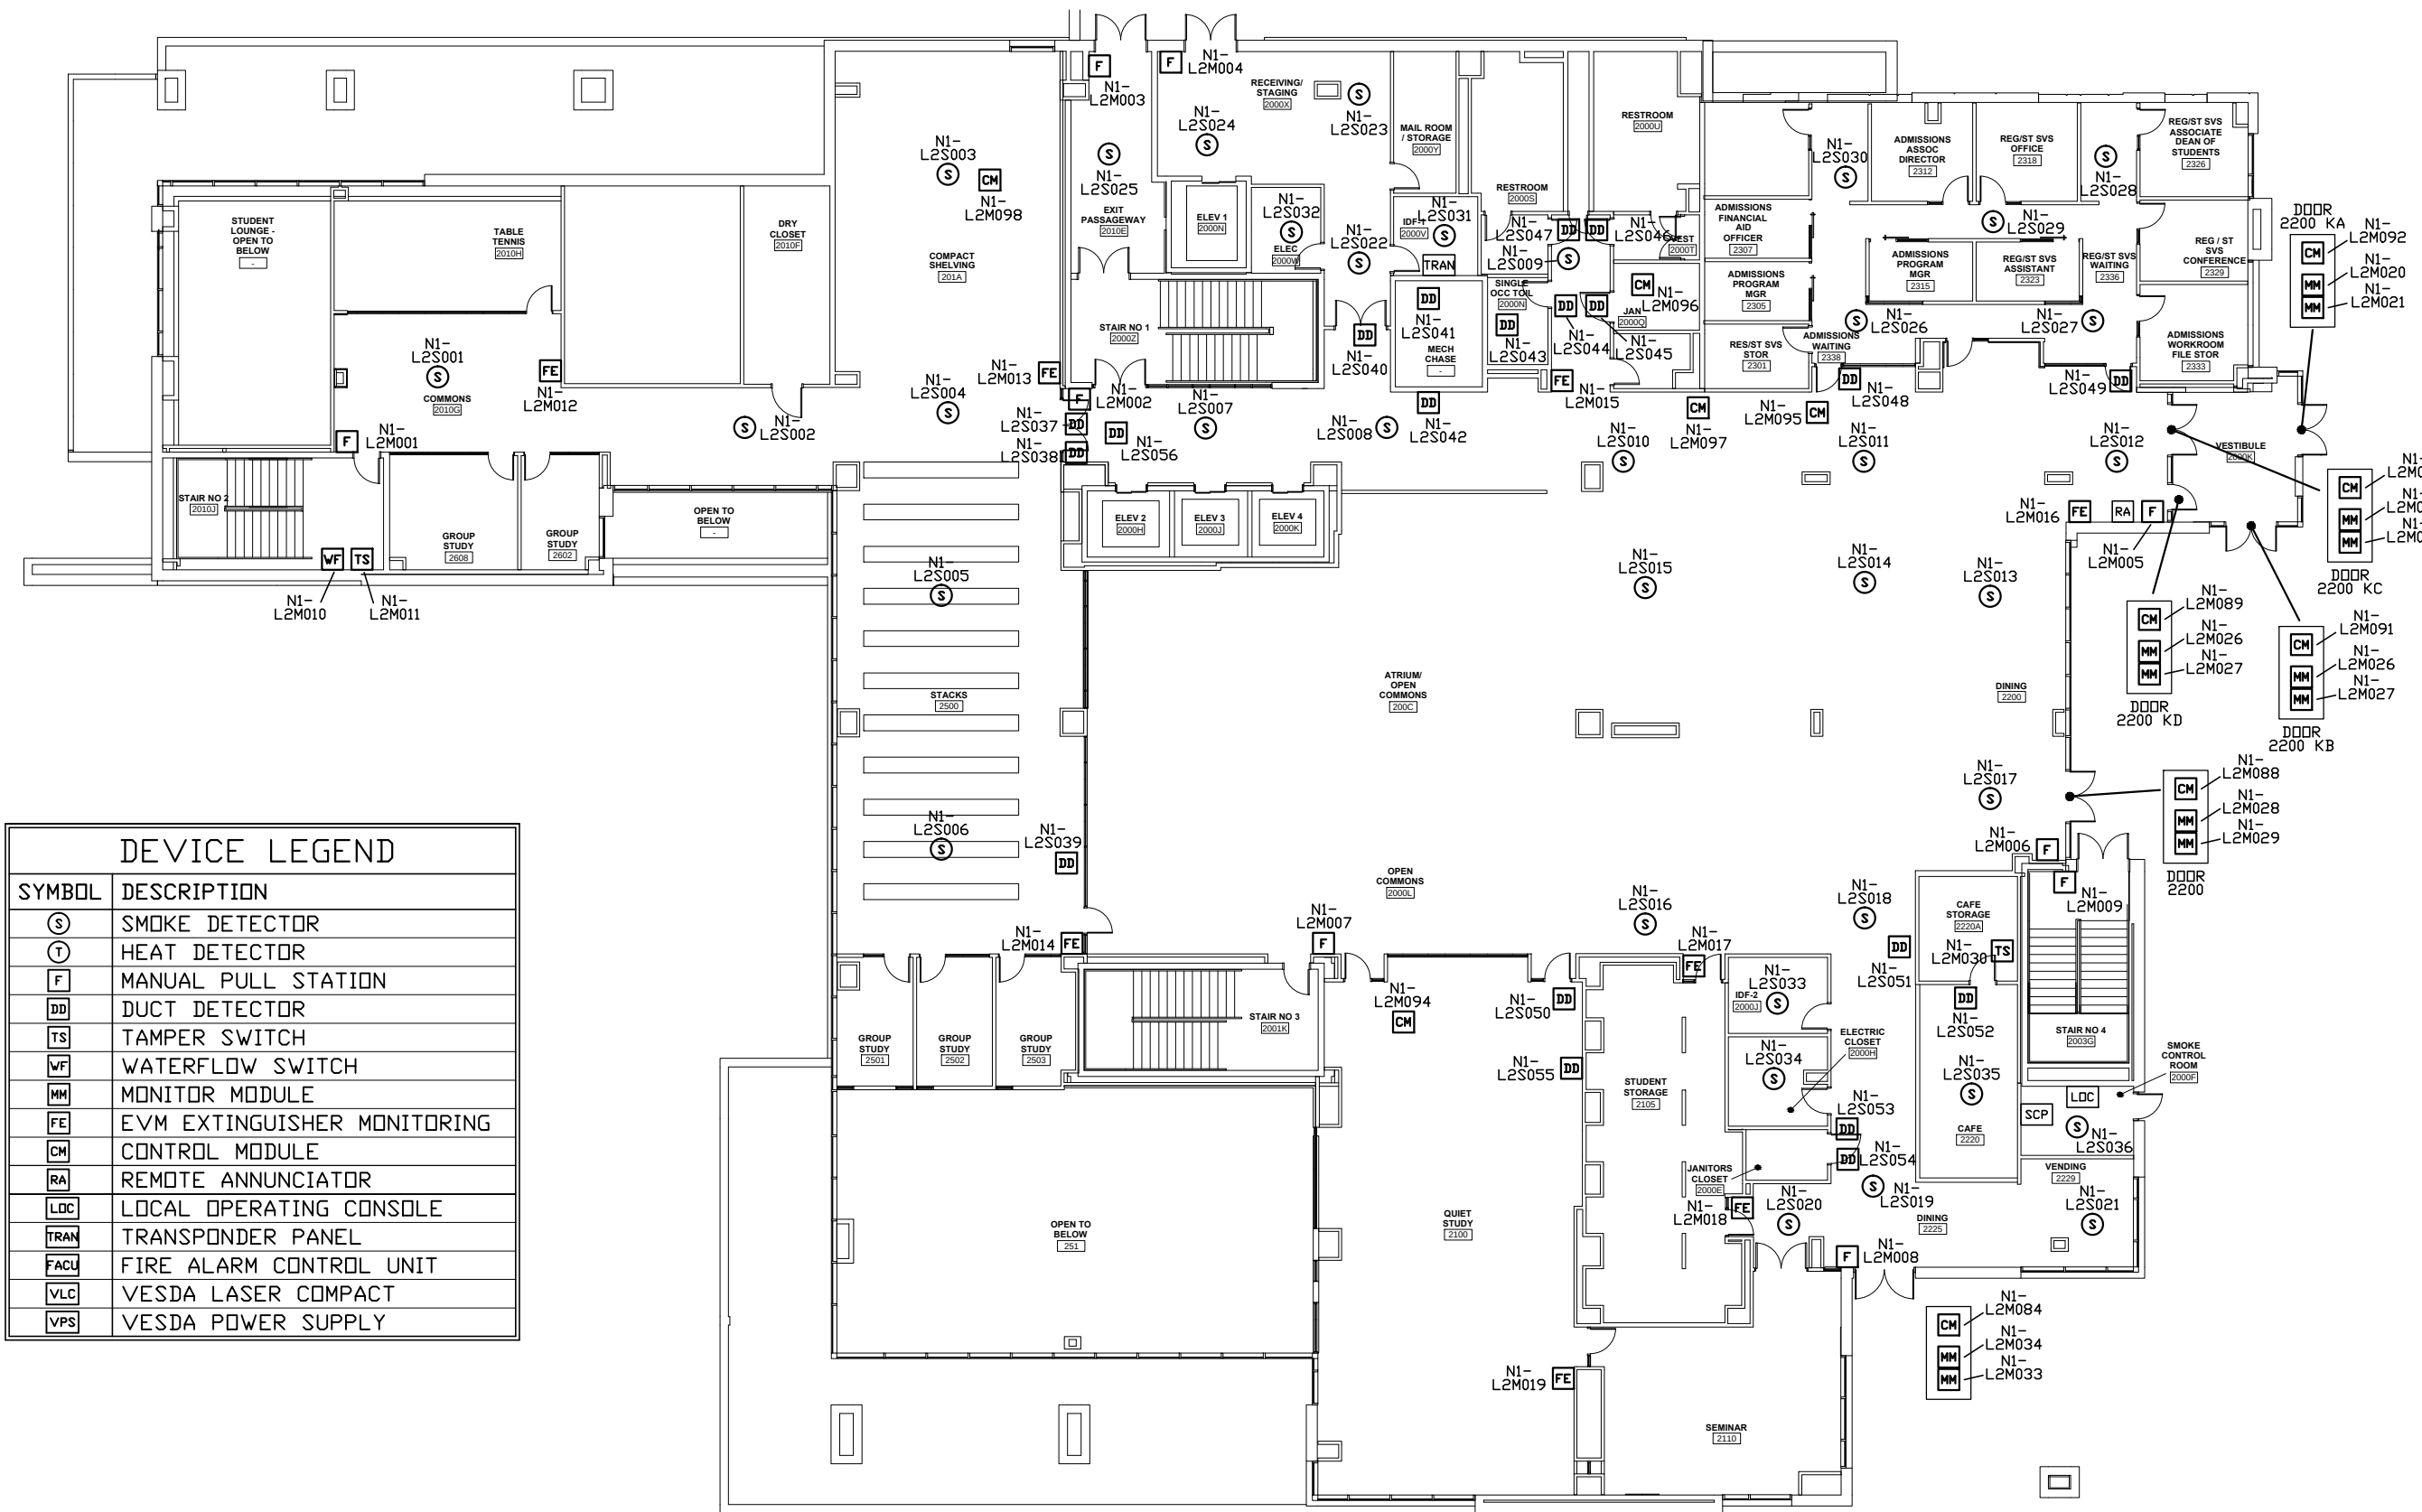

DEVICE LEGEND	
SYMBOL	DESCRIPTION
(S)	SMOKE DETECTOR
(T)	HEAT DETECTOR
(F)	MANUAL PULL STATION
(DD)	DUCT DETECTOR
(TS)	TAMPER SWITCH
(WF)	WATERFLOW SWITCH
(MM)	MONITOR MODULE
(FE)	EVM EXTINGUISHER MONITORING
(CM)	CONTROL MODULE
(RA)	REMOTE ANNUNCIATOR
(LOC)	LOCAL OPERATING CONSOLE
(TRAN)	TRANSPONDER PANEL
(FACU)	FIRE ALARM CONTROL UNIT
(VLC)	VESDA LASER COMPACT
(VPS)	VESDA POWER SUPPLY

NOTE:
NFS DRAWINGS ARE BASED ON THE PROJECT
ARCHITECT/ENGINEER (A/E) PLANS AND SPECIFICATIONS
FURNISHED TO NFS. A/E IS SOLELY RESPONSIBLE
(NOT NFS) FOR THE TYPE, SIZE, LOCATION, AND
SUITABILITY OF ALL FIRE ALARMS, CONTROL PANELS,
AND OTHER DEVICES SHOWN ON THE A/E PLANS.
NFS DRAWINGS ARE TO SHOW ONLY THE WIRING
DIAGRAMS BETWEEN FIRE ALARM DEVICES AND
CONTROL PANELS. NFS IS NOT RESPONSIBLE FOR
THE INFORMATION SHOWN ON THE A/E PLANS.

UNIVERSITY OF UTAH
QUINNEY SCHOOL OF LAW
LEVEL 2
SOUTH CAMPUS DRIVE
SALT LAKE CITY, UTAH
FIRE ALARM SYSTEM


NFS
NELSON FIRE SYSTEMS
801-468-8300

DRAWN BY: AK
DESIGNED BY: XXXX
APPROVED BY: DPS
DATE: 6/22/15
SCALE: N.T.S.
PROJECT NO: XXXX
REV NO: XXXX
DRAWING NAME:
QUINNEY LAW FM 2.DWG

FIRE ALARM SYSTEM
FINAL MAP
LEVEL 2

PAGE:
FA-2



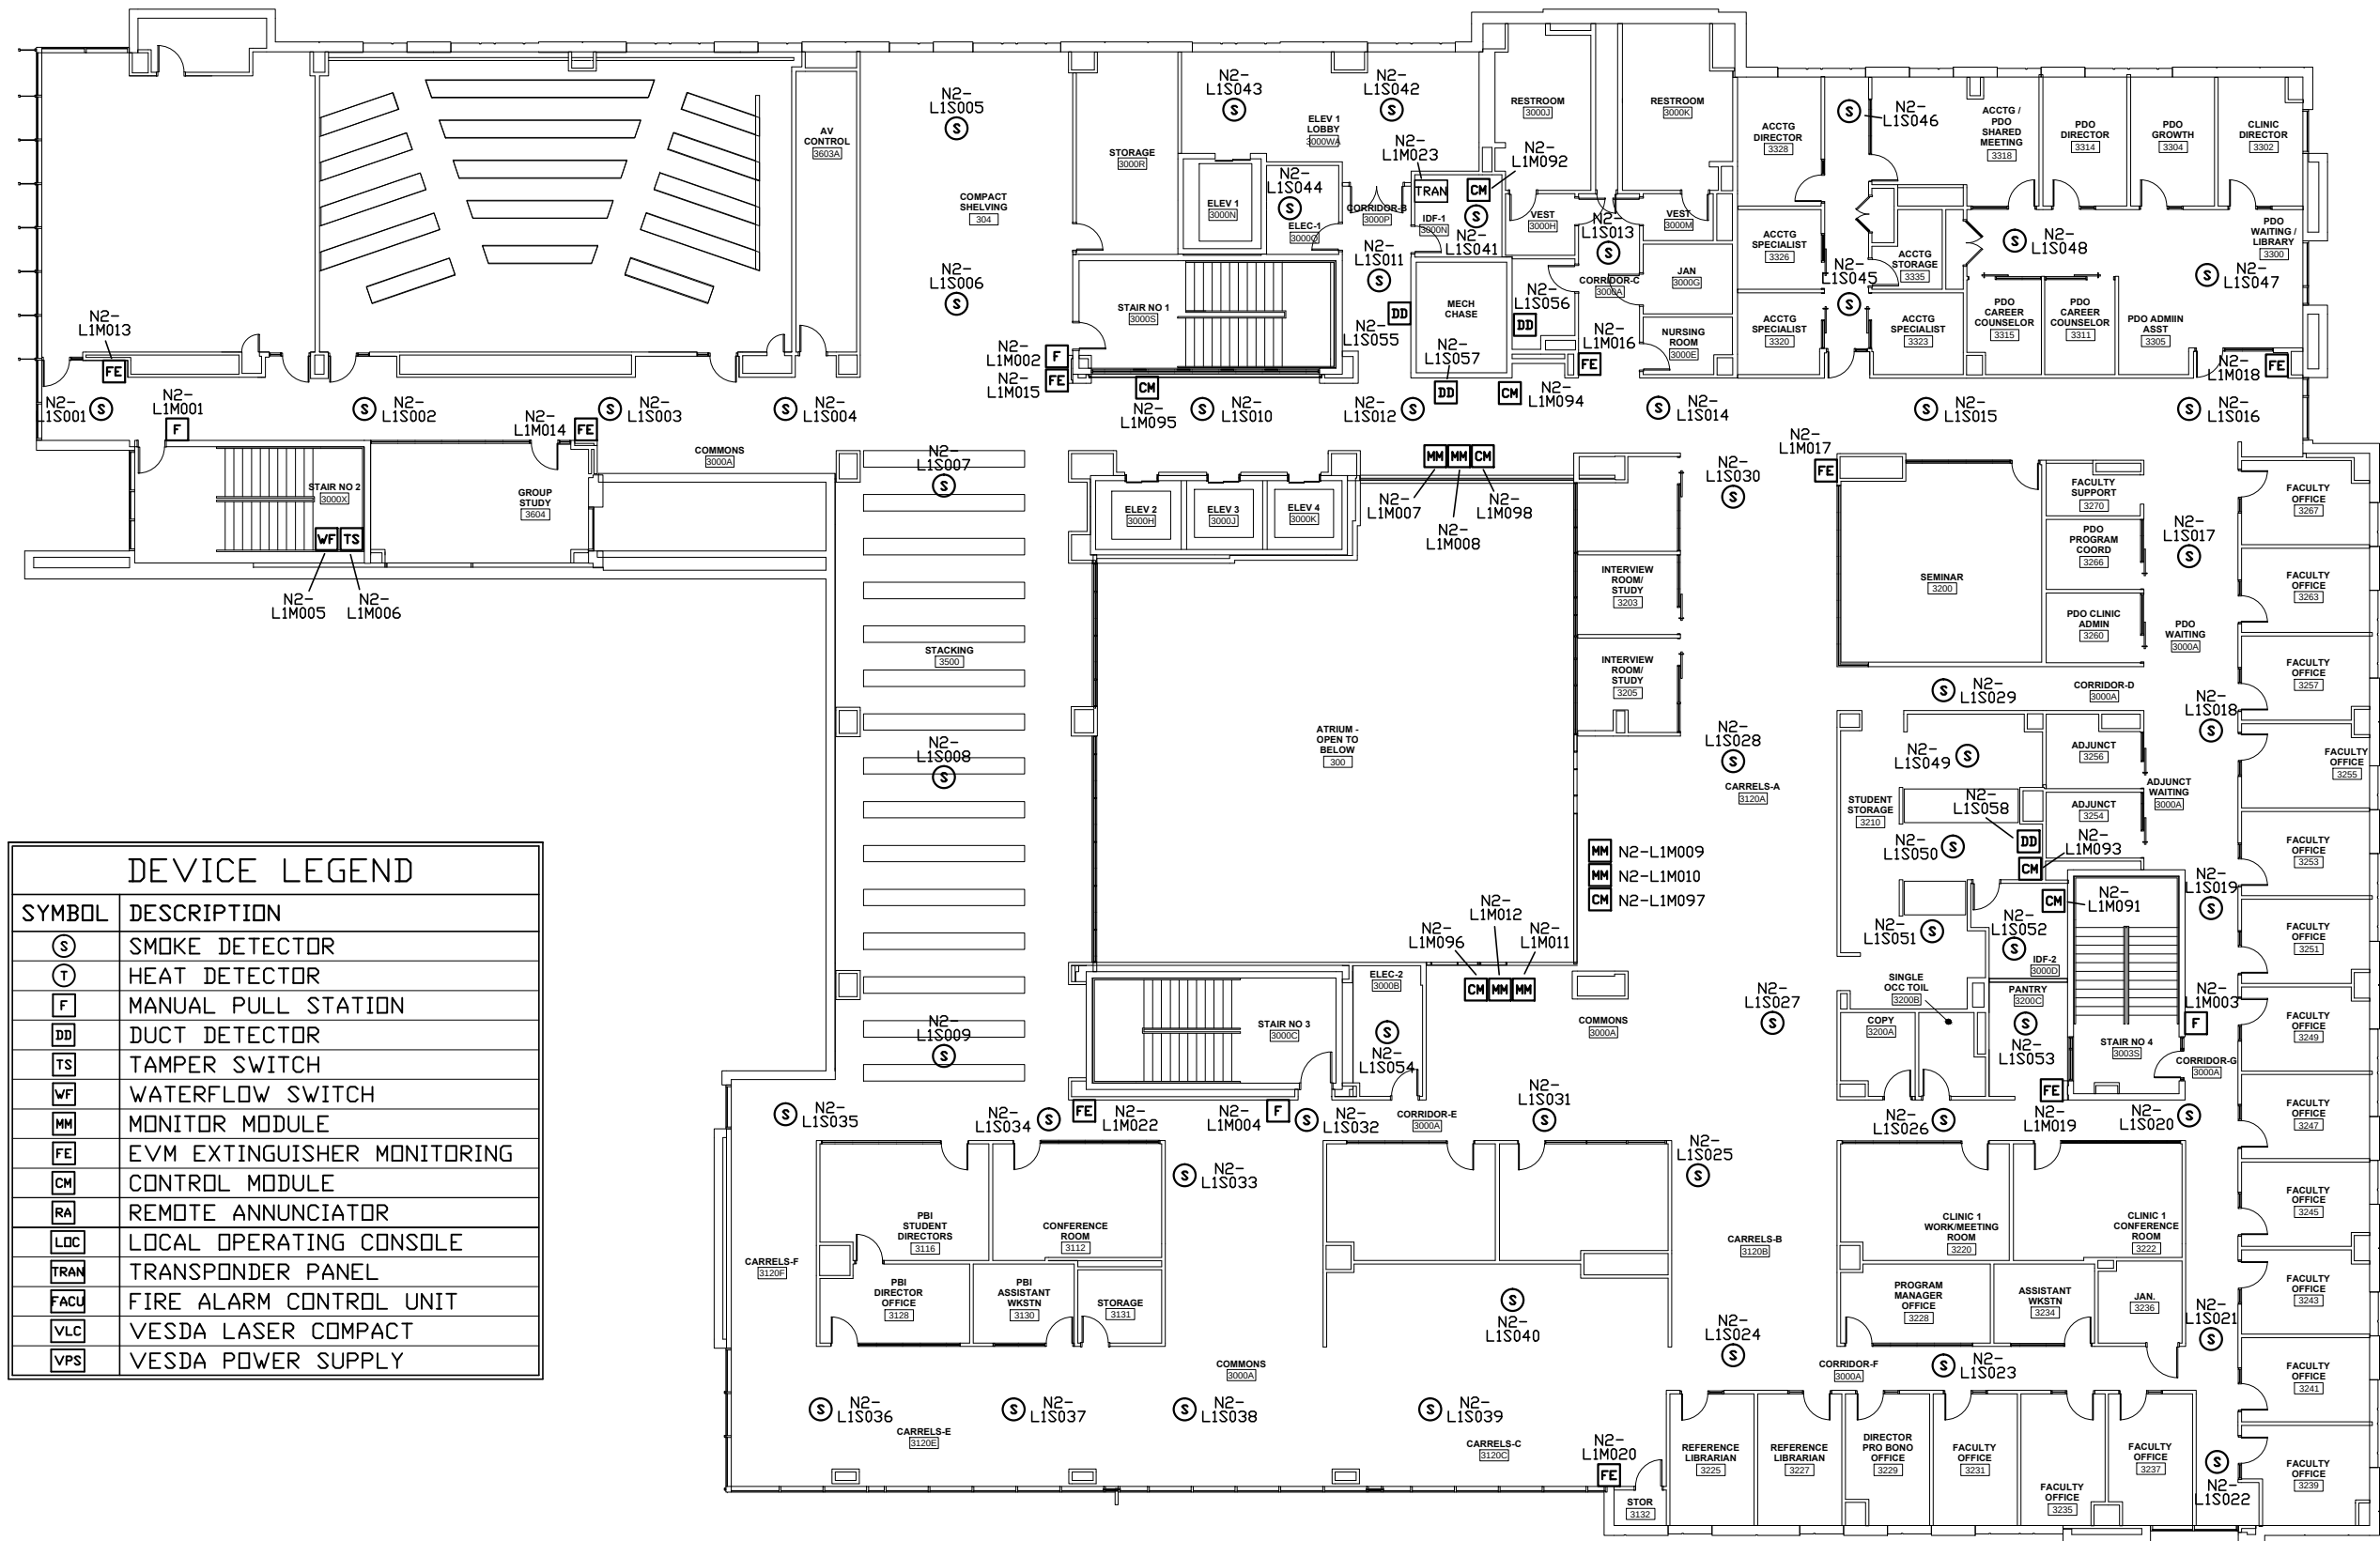

DEVICE LEGEND	
SYMBOL	DESCRIPTION
(S)	SMOKE DETECTOR
(T)	HEAT DETECTOR
(F)	MANUAL PULL STATION
(DD)	DUCT DETECTOR
(TS)	TAMPER SWITCH
(WF)	WATERFLOW SWITCH
(MM)	MONITOR MODULE
(FE)	EVM EXTINGUISHER MONITORING
(CM)	CONTROL MODULE
(RA)	REMOTE ANNUNCIATOR
(LOC)	LOCAL OPERATING CONSOLE
(TRAN)	TRANSPONDER PANEL
(FACU)	FIRE ALARM CONTROL UNIT
(VLC)	VESDA LASER COMPACT
(VPS)	VESDA POWER SUPPLY

NOTE:
NFS DRAWINGS ARE BASED ON THE PROJECT
ARCHITECT/ENGINEER (A/E) PLANS AND SPECIFICATIONS
FURNISHED TO NFS. A/E IS SOLELY RESPONSIBLE
(NOT NFS) FOR THE TYPE, SIZE, LOCATION, AND
SUITABILITY OF ALL FIRE ALARMS, CONTROL PANELS,
AND OTHER DEVICES SHOWN ON THE A/E PLANS.
NFS DRAWINGS ARE TO SHOW ONLY THE WIRING
DIAGRAMS BETWEEN FIRE ALARM DEVICES AND
CONTROL PANELS. NFS IS NOT RESPONSIBLE FOR
THE INFORMATION SHOWN ON THE A/E PLANS.

UNIVERSITY OF UTAH
QUINNEY SCHOOL OF LAW
LEVEL 3
SOUTH CAMPUS DRIVE
SALT LAKE CITY, UTAH
FIRE ALARM SYSTEM

NFS
NELSON FIRE SYSTEMS
801-468-8300

DRAWN BY: AK
DESIGNED BY: XXXX
APPROVED BY: DPS
DATE: 6/22/15
SCALE: N.T.S.
PROJECT NO: XXXX
REV NO: XXXX
DRAWING NAME:
QUINNEY LAW FM 3.DWG

FIRE ALARM SYSTEM
FINAL MAP
LEVEL 3

PAGE:
FA-3





DEVICE LEGEND	
SYMBOL	DESCRIPTION
(S)	SMOKE DETECTOR
(T)	HEAT DETECTOR
[F]	MANUAL PULL STATION
[DD]	DUCT DETECTOR
[TS]	TAMPER SWITCH
[WF]	WATERFLOW SWITCH
[MM]	MONITOR MODULE
[FE]	EVM EXTINGUISHER MONITORING
[CM]	CONTROL MODULE
[RA]	REMOTE ANNUNCIATOR
[LOC]	LOCAL OPERATING CONSOLE
[TRAN]	TRANSPONDER PANEL
[FACU]	FIRE ALARM CONTROL UNIT
[VLC]	VESDA LASER COMPACT
[VPS]	VESDA POWER SUPPLY

NOTE:
NFS DRAWINGS ARE BASED ON THE PROJECT
ARCHITECT/ENGINEER (A/E) PLANS AND SPECIFICATIONS
(NFS) FOR THE FIRE SMOKE RESPONSIVE
SUITABILITY OF THE FIRE SIZE, CONTROL PANELS,
AND OTHER DEVICES SHOWN ON THE A/E PLANS.
NFS DRAWINGS ARE TO SHOW ONLY THE WIRING
DIAGRAMS BETWEEN FIRE ALARM DEVICES AND
CONTROL PANELS. NFS IS NOT RESPONSIBLE FOR
THE INFORMATION SHOWN ON THE A/E PLANS.

UNIVERSITY OF UTAH
QUINNEY SCHOOL OF LAW
LEVEL 4
SOUTH CAMPUS DRIVE
SALT LAKE CITY, UTAH
FIRE ALARM SYSTEM

NFS
NELSON FIRE SYSTEMS
801-468-8300


DRAWN BY:	AK
DESIGNED BY:	XXXX
APPROVED BY:	DPS
DATE:	6/22/15
SCALE:	N.T.S.
PROJECT NO:	XXXX
REV NO:	XXXX
DRAWING NAME:	QUINNEY LAW FM 4.DWG

FIRE ALARM SYSTEM


FINAL MAP

LEVEL 4

PAGE:
FA-4

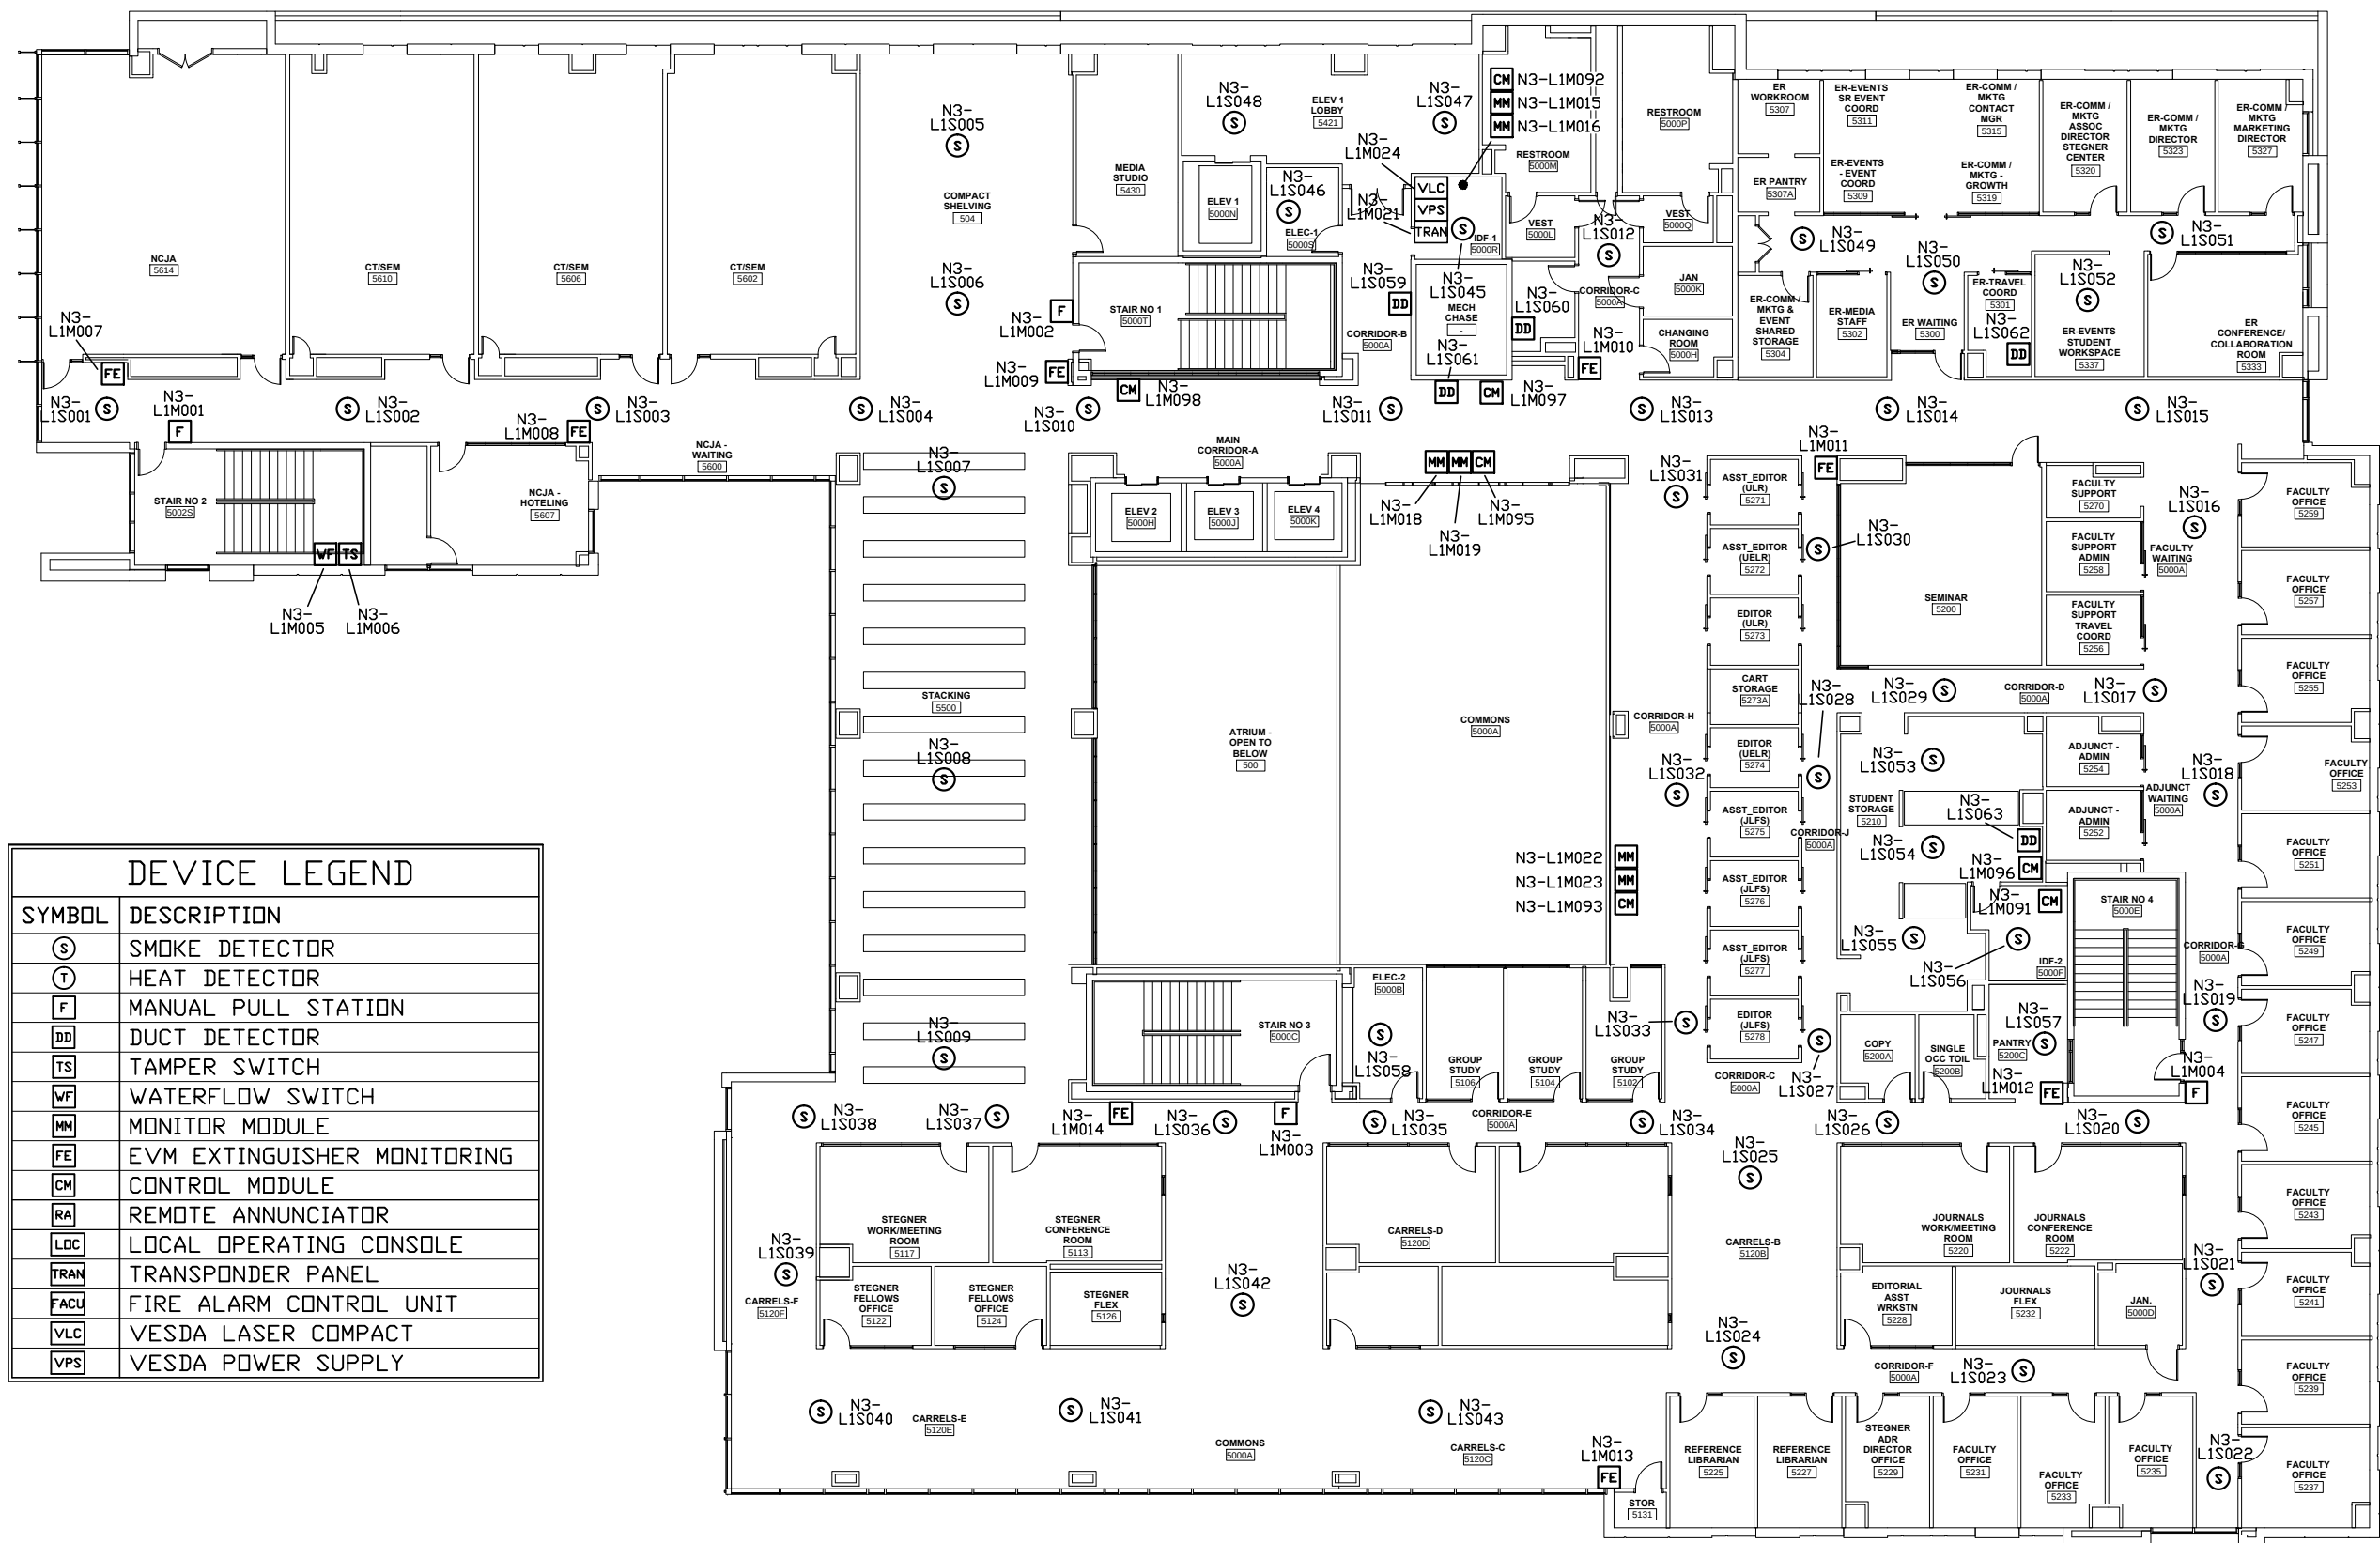

DEVICE LEGEND	
SYMBOL	DESCRIPTION
(S)	SMOKE DETECTOR
(T)	HEAT DETECTOR
(F)	MANUAL PULL STATION
(DD)	DUCT DETECTOR
(TS)	TAMPER SWITCH
(WF)	WATERFLOW SWITCH
(MM)	MONITOR MODULE
(FE)	EVM EXTINGUISHER MONITORING
(CM)	CONTROL MODULE
(RA)	REMOTE ANNUNCIATOR
(LOC)	LOCAL OPERATING CONSOLE
(TRAN)	TRANSPONDER PANEL
(FACU)	FIRE ALARM CONTROL UNIT
(VLC)	VESDA LASER COMPACT
(VPS)	VESDA POWER SUPPLY

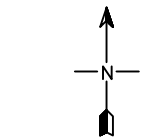

NOTE:
NFS DRAWINGS ARE BASED ON THE PROJECT
ARCHITECT/ENGINEER (A/E) PLANS AND SPECIFICATIONS
FURNISHED TO NFS. A/E IS SOLELY RESPONSIBLE
(NOT NFS) FOR THE TYPE, SIZE, LOCATION, AND
SUITABILITY OF ALL FIRE ALARMS, CONTROL PANELS,
AND OTHER DEVICES SHOWN ON THE A/E PLANS.
NFS DRAWINGS ARE TO SHOW ONLY THE WIRING
DIAGRAMS BETWEEN FIRE ALARM DEVICES AND
CONTROL PANELS. NFS IS NOT RESPONSIBLE FOR
THE INFORMATION SHOWN ON THE A/E PLANS.

UNIVERSITY OF UTAH
QUINNEY SCHOOL OF LAW
LEVEL 5
SOUTH CAMPUS DRIVE
SALT LAKE CITY, UTAH
FIRE ALARM SYSTEM


NFS
NELSON FIRE SYSTEMS
801-468-8300

DRAWN BY: AK
DESIGNED BY: XXXX
APPROVED BY: DPS
DATE: 6/22/15
SCALE: N.T.S.
PROJECT NO: XXXX
REV NO: XXXX
DRAWING NAME:
QUINNEY LAW FM 5.DWG


FIRE ALARM SYSTEM
FINAL MAP
LEVEL 5

PAGE:
FA-5



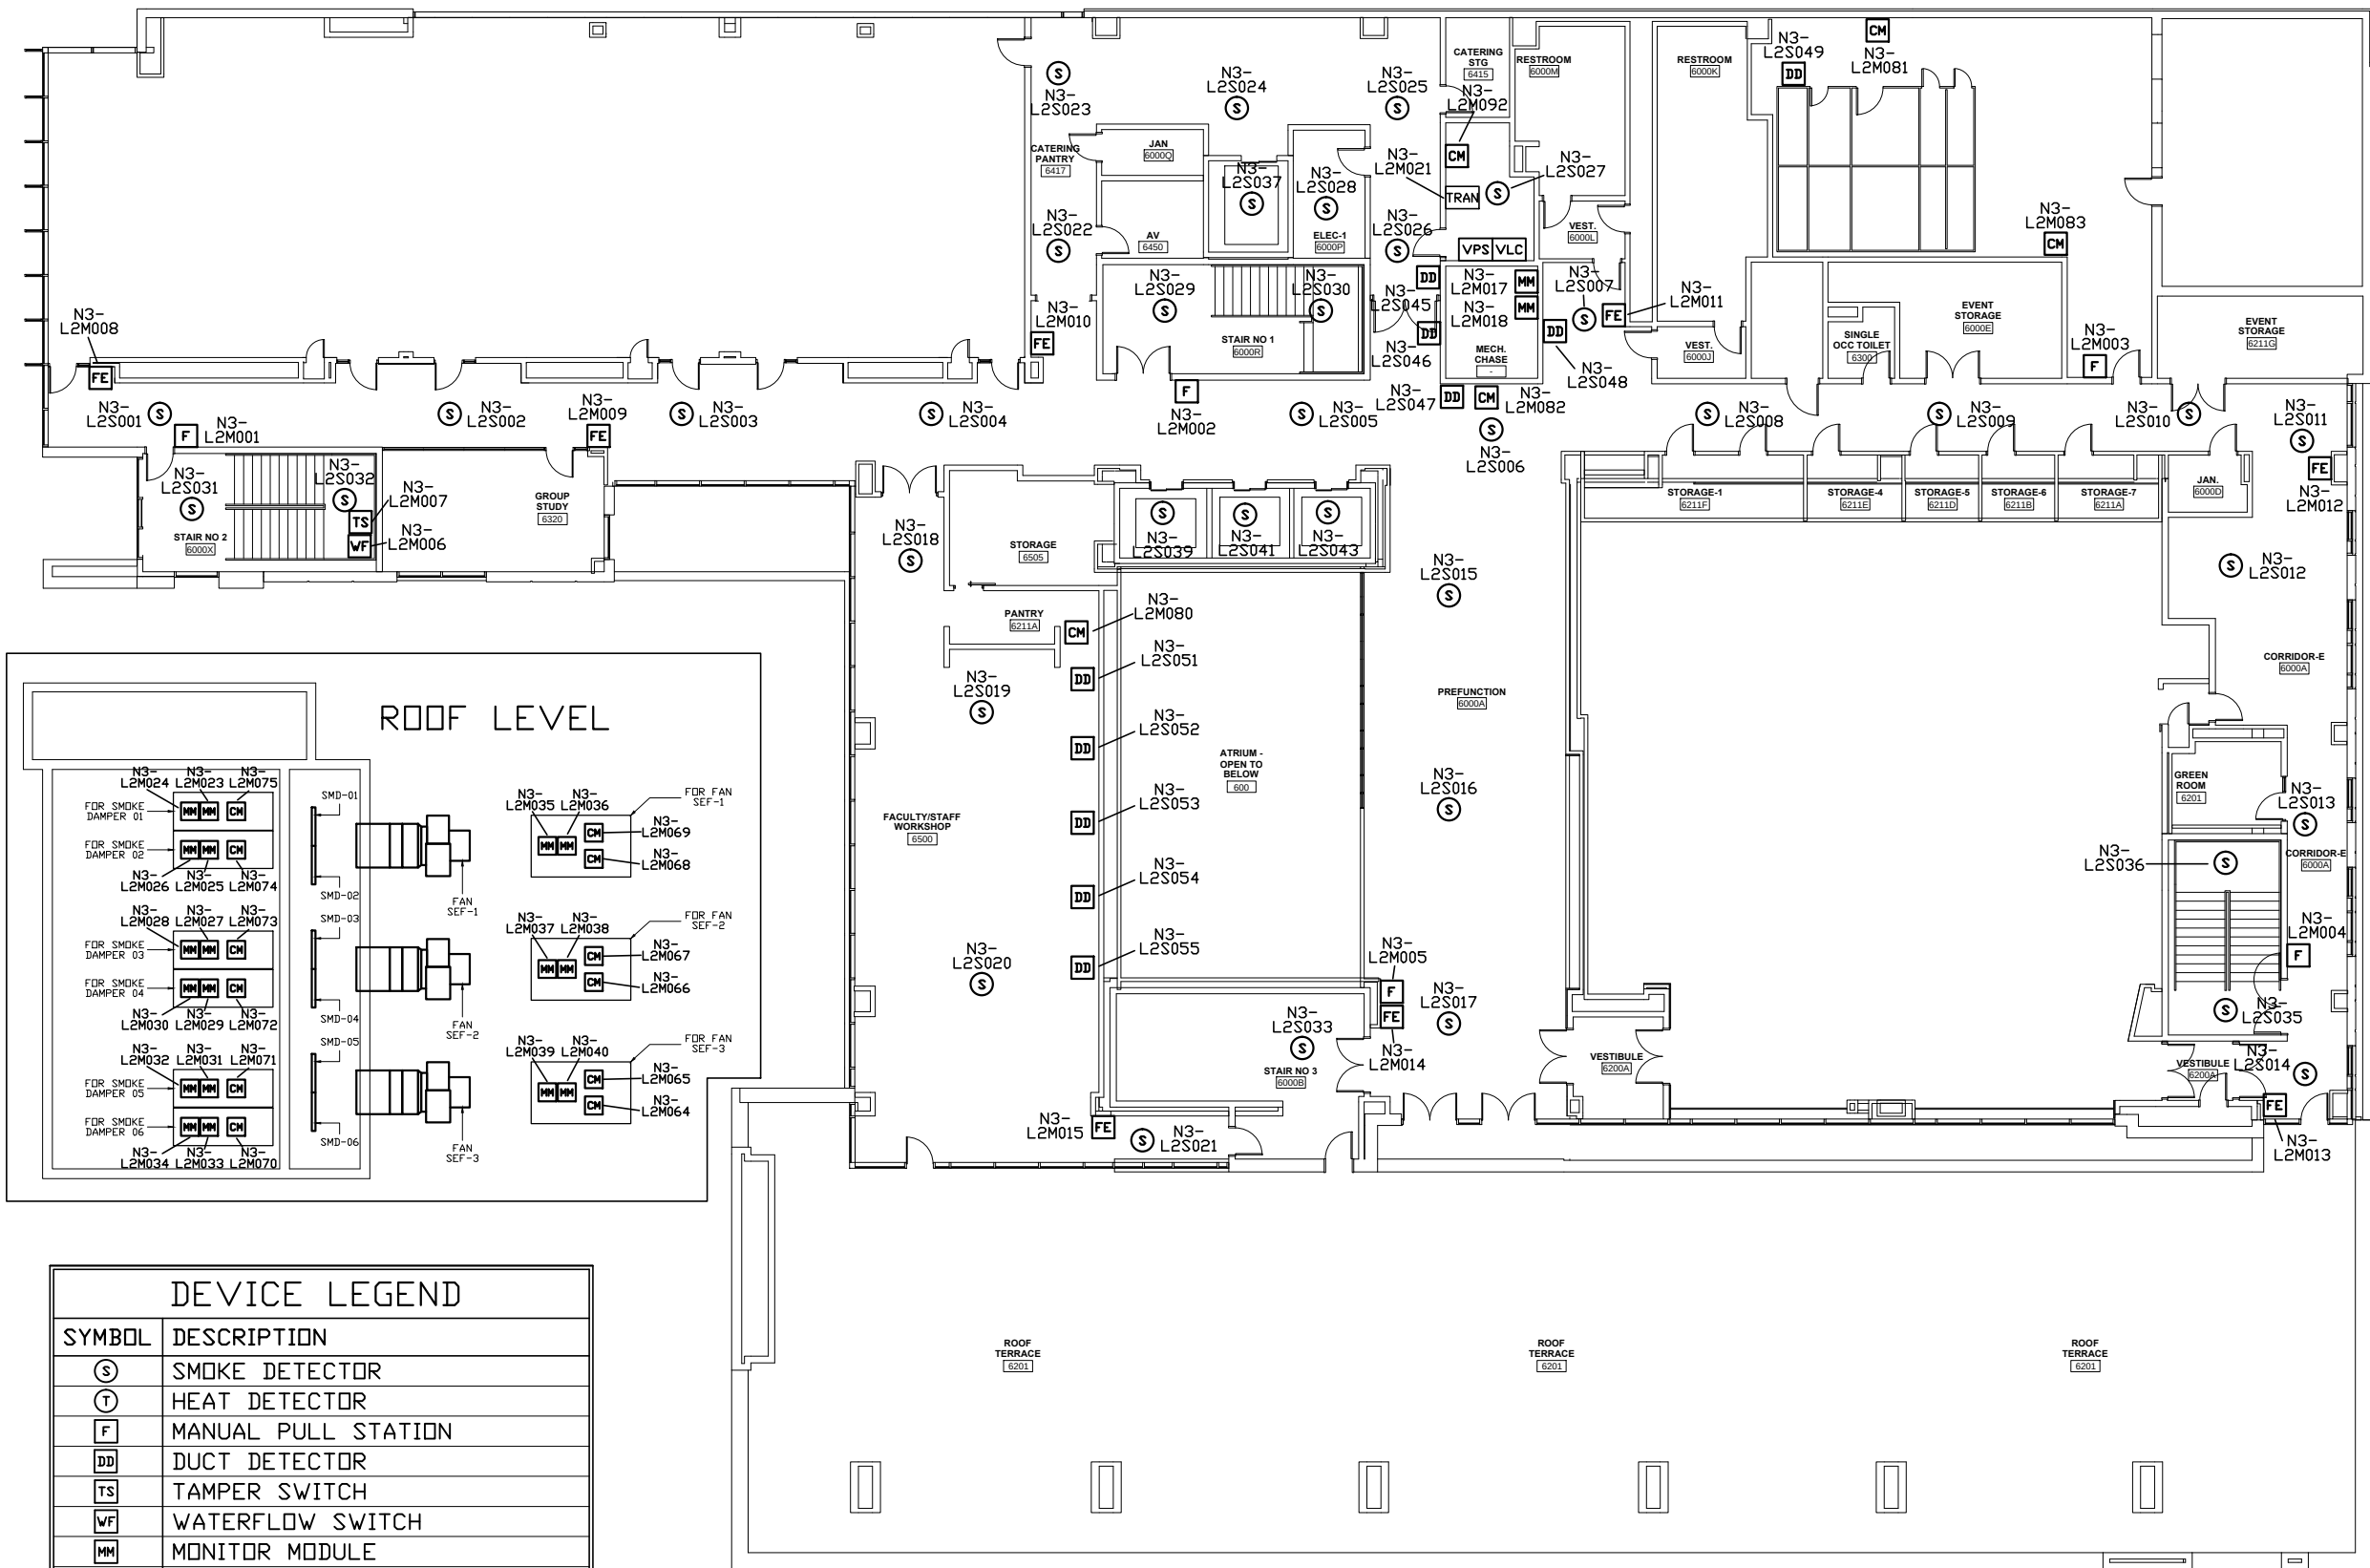

ROOF LEVEL

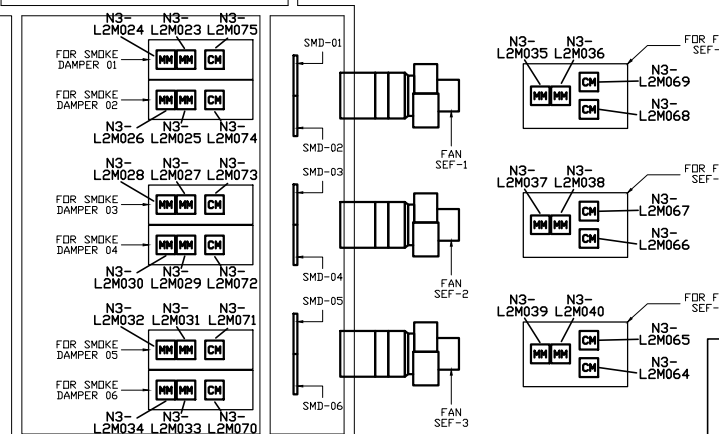

DEVICE LEGEND	
SYMBOL	DESCRIPTION
(S)	SMOKE DETECTOR
(T)	HEAT DETECTOR
(F)	MANUAL PULL STATION
(DD)	DUCT DETECTOR
(TS)	TAMPER SWITCH
(WF)	WATERFLOW SWITCH
(MM)	MONITOR MODULE
(FE)	EVM EXTINGUISHER MONITORING CONTROL MODULE
(RA)	REMOTE ANNUNCIATOR
(LOC)	LOCAL OPERATING CONSOLE
(TRAN)	TRANSPONDER PANEL
(FACU)	FIRE ALARM CONTROL UNIT
(VLC)	VESDA LASER COMPACT
(VPS)	VESDA POWER SUPPLY

UNIVERSITY OF UTAH
QUINNEY SCHOOL OF LAW
LEVEL 6
SOUTH CAMPUS DRIVE
SALT LAKE CITY, UTAH
FIRE ALARM SYSTEM

NFS
NELSON FIRE SYSTEMS
801-468-8300

DRAWN BY: AK
DESIGNED BY: XXXX
APPROVED BY: DPS
DATE: 6/22/15
SCALE: N.T.S.
PROJECT NO: XXXX
REV NO: XXXX
DRAWING NAME: QUINNEY LAW FM 6.DWG

FIRE ALARM SYSTEM
FINAL MAP
LEVEL 6

PAGE:
FA-6

