



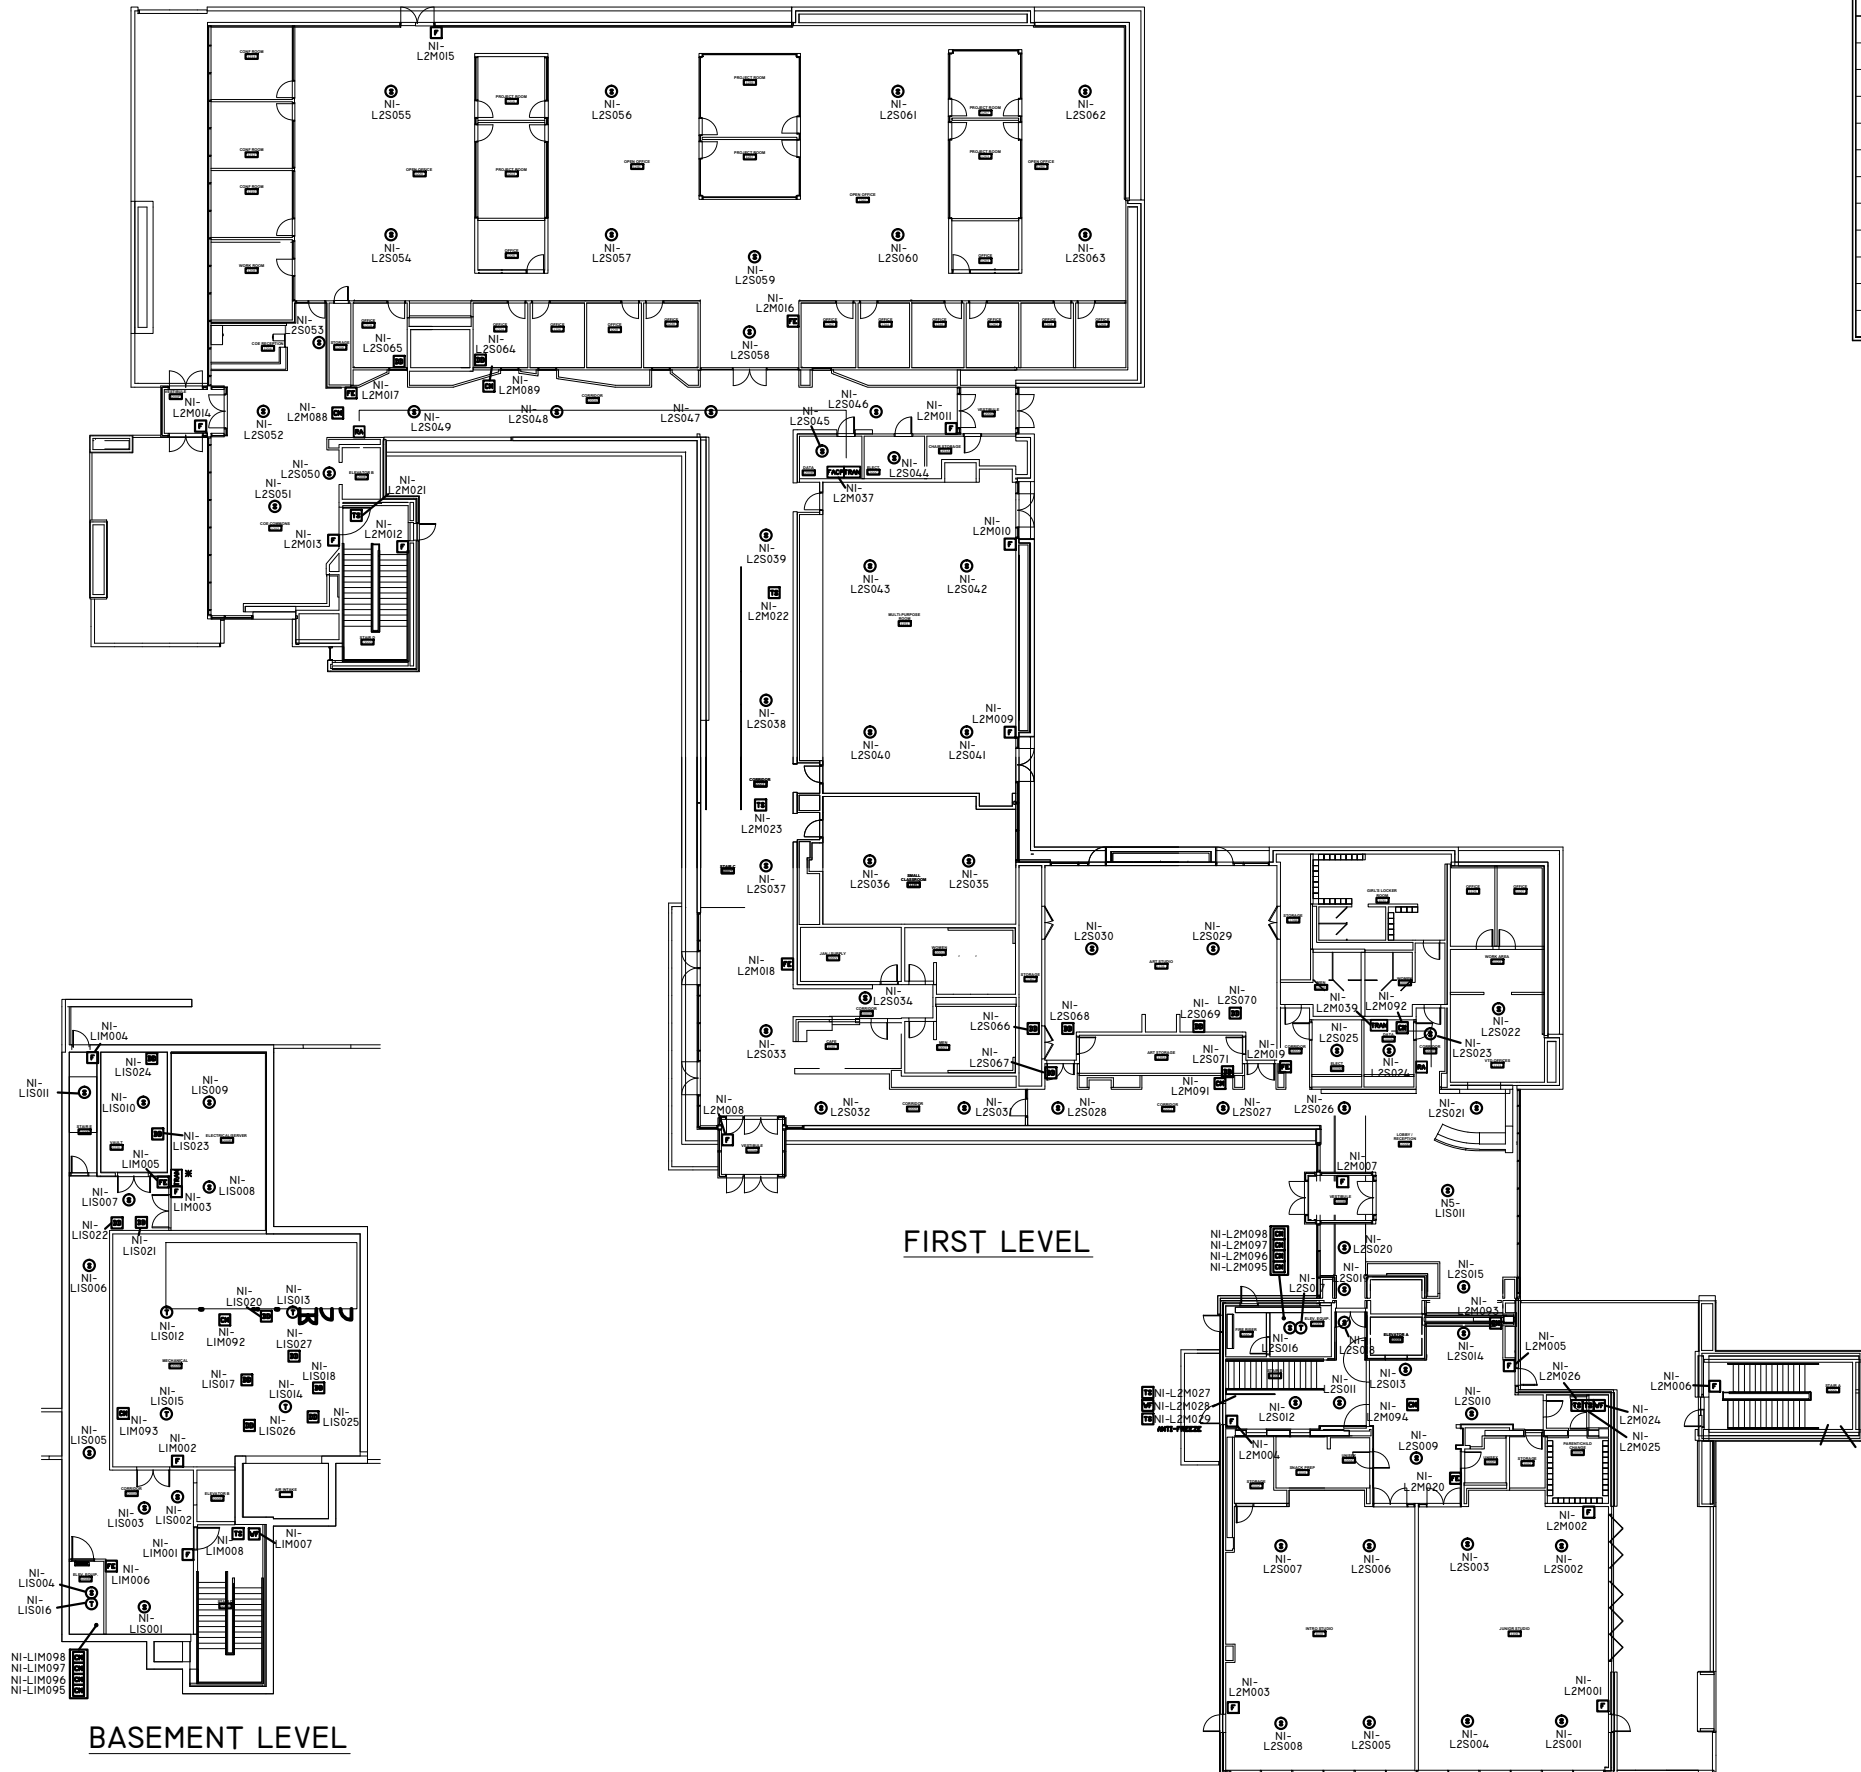

DEVICE LEGEND	
SYMBOL	DESCRIPTION
S	SMOKE DETECTOR
H	HEAT DETECTOR
F	MANUAL PULL STATION
DD	DUCT DETECTOR
WF	WATERFLOW SWITCH
TS	TAMPER SWITCH
FE	ENGAGE FIRE EXTINGUISHER
MM	MONITOR MODULE
CM	CONTROL MODULE
RA	REMOTE ANNUNCIATOR
FACP	FIRE ALARM CONTROL PANEL
TRAN	TRANSPONDER PANEL

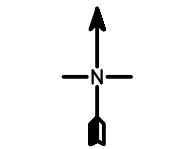

NOTE:
NFS DRAWINGS ARE BASED ON THE PROJECT
ARCHITECT/ENGINEER (A/E) PLANS AND SPECIFICATIONS
FURNISHED TO NFS. A/E IS SOLELY RESPONSIBLE
(NOT NFS) FOR THE TYPE, SIZE, LOCATION, AND
SUITABILITY OF ALL FIRE ALARMS, CONTROL PANELS,
AND OTHER DEVICES SHOWN ON THE A/E PLANS.
NFS DRAWINGS ARE TO SHOW ONLY THE WIRING
DIAGRAMS BETWEEN FIRE ALARM DEVICES AND
CONTROL PANELS. NFS IS NOT RESPONSIBLE FOR
THE INFORMATION SHOWN ON THE A/E PLANS.

ARTS AND EDUCATION COMPLEX
UNIVERSITY OF UTAH
CAMPUS CENTER DRIVE
SALT LAKE CITY, UTAH 84112
FIRE ALARM SYSTEM


NFS
NELSON FIRE SYSTEMS
801-468-8300

DRAWN BY: JJC
DESIGNED BY: XXXX
APPROVED BY: DPS
DATE: 12/26/2013
SCALE: N.T.S.
PROJECT NO: XXXX
REV NO: XXXX
DRAWING NAME:
BTSAC FIRST FM.DWG


FIRE ALARM SYSTEM
LEVEL I
NUMBERS

PAGE:
FA-I-03



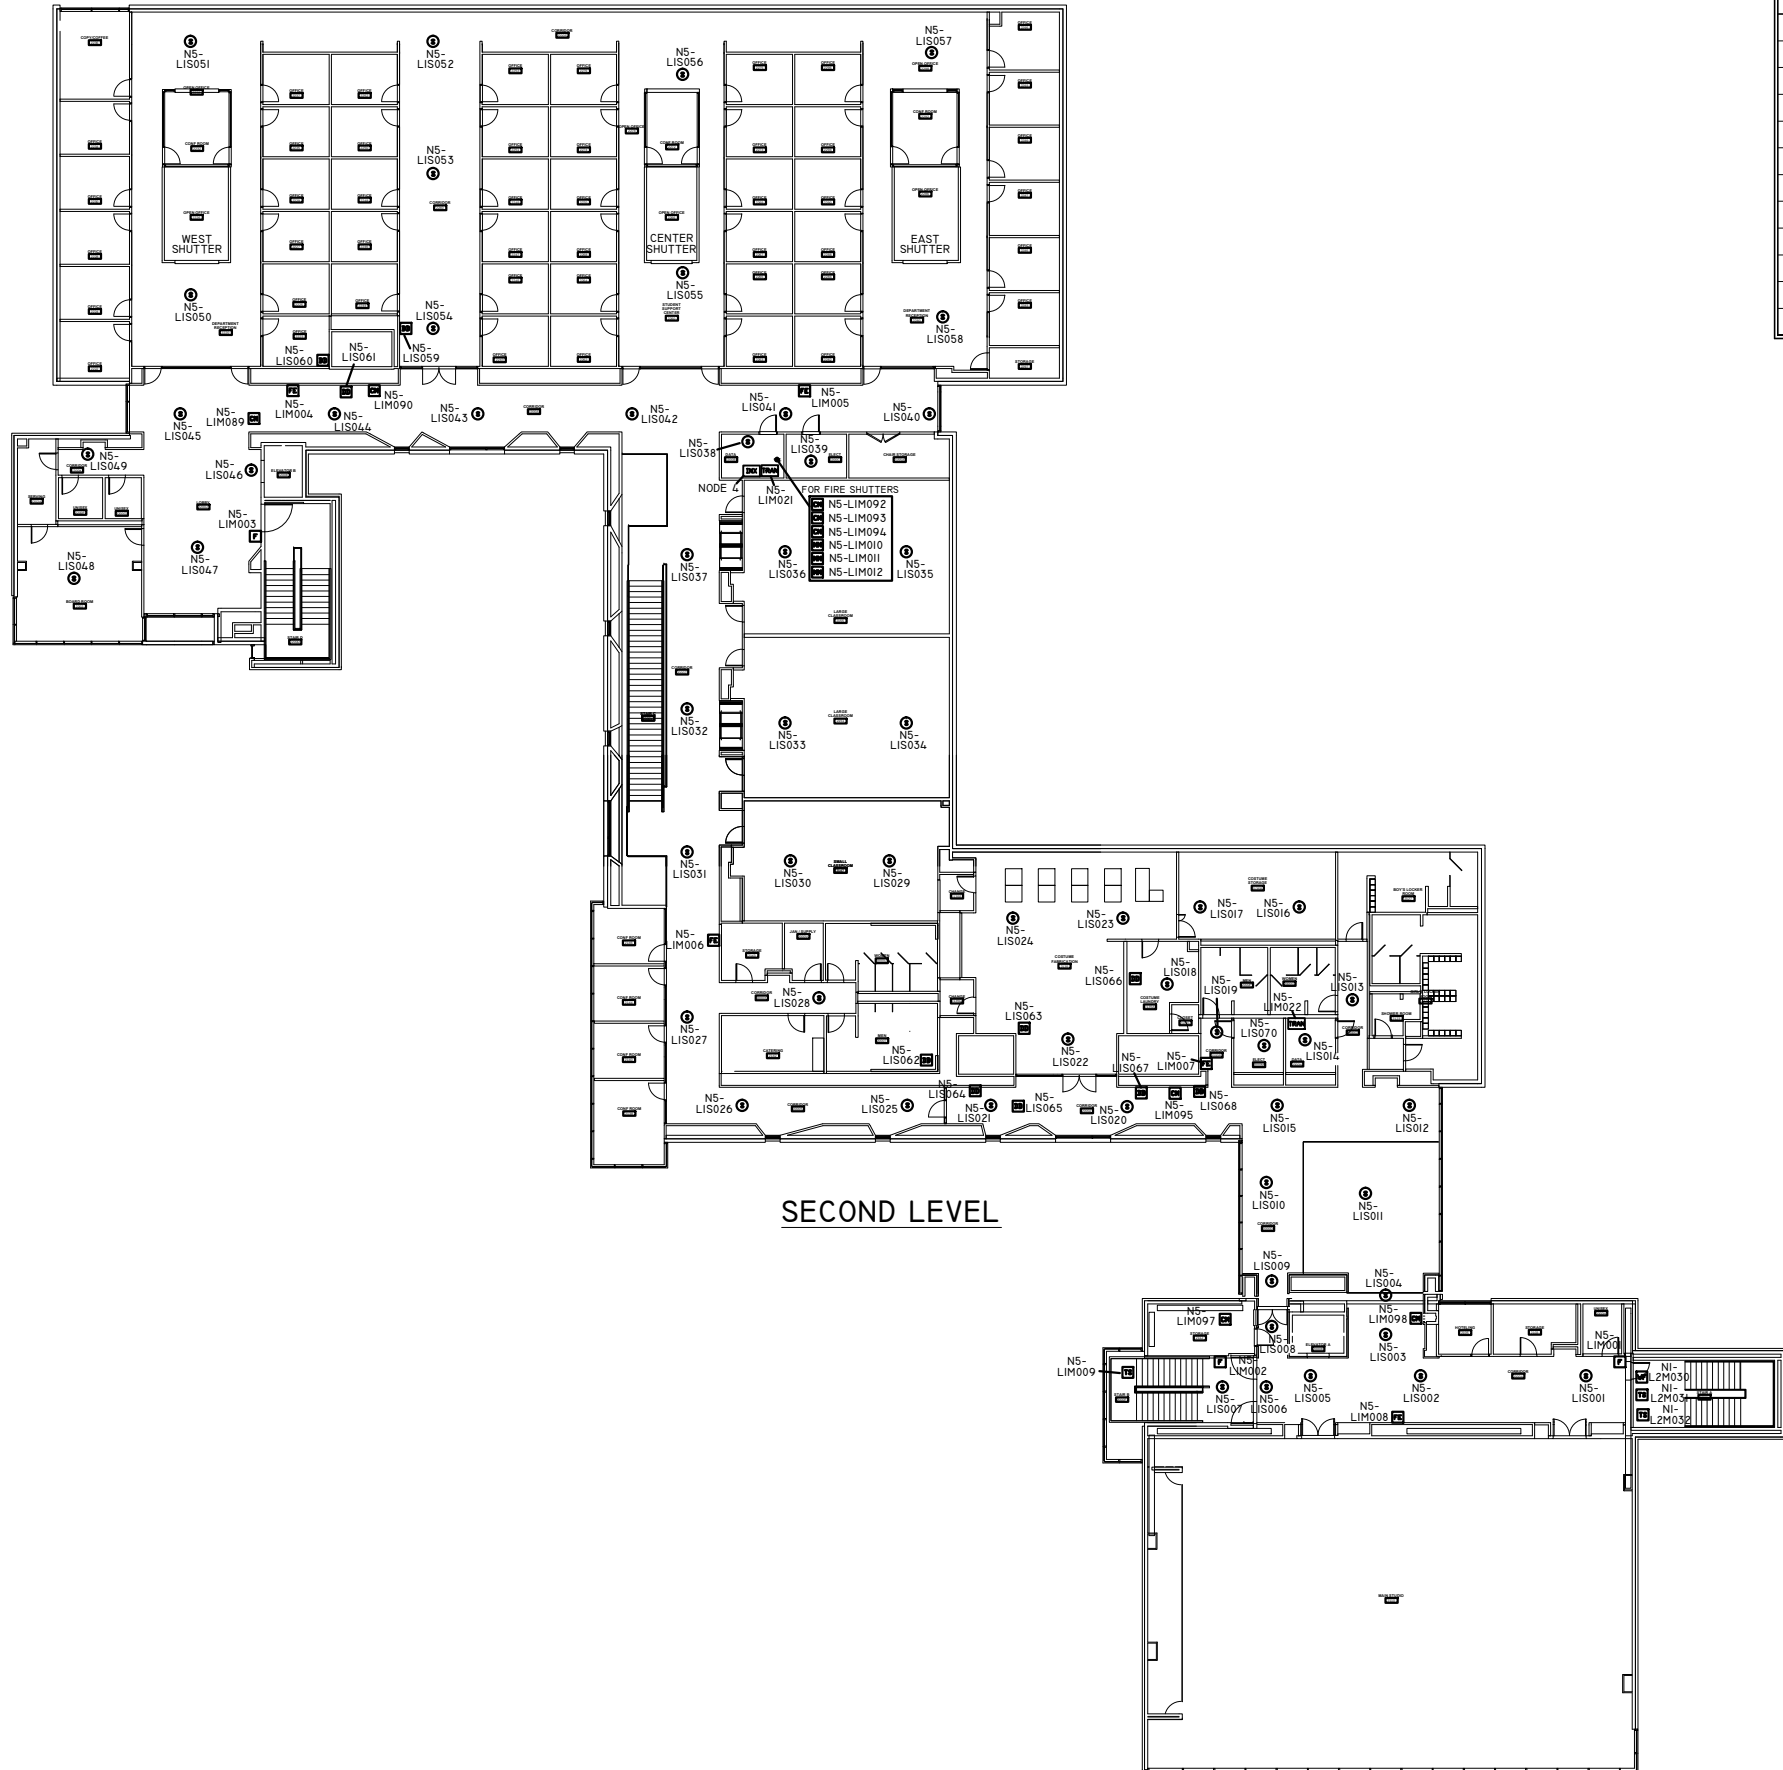

DEVICE LEGEND	
SYMBOL	DESCRIPTION
③	SMOKE DETECTOR
①	HEAT DETECTOR
F	MANUAL PULL STATION
DB	DUCT DETECTOR
WF	WATERFLOW SWITCH
TS	TAMPER SWITCH
FE	ENGAGE FIRE EXTINGUISHER
MM	MONITOR MODULE
CM	CONTROL MODULE
RA	REMOTE ANNUNCIATOR
FACP	FIRE ALARM CONTROL PANEL
TRAN	TRANSPONDER PANEL

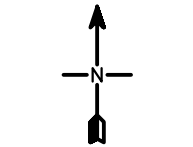

NOTE:
NFS DRAWINGS ARE BASED ON THE PROJECT
ARCHITECT/ENGINEER (A/E) PLANS AND SPECIFICATIONS
FURNISHED TO NFS. A/E IS SOLELY RESPONSIBLE
(NOT NFS) FOR THE TYPE, SIZE, LOCATION, AND
SUITABILITY OF ALL FIRE ALARMS, CONTROL PANELS,
AND OTHER DEVICES SHOWN ON THE A/E PLANS.
NFS DRAWINGS ARE TO SHOW ONLY THE WIRING
DIAGRAMS BETWEEN FIRE ALARM DEVICES AND
CONTROL PANELS. NFS IS NOT RESPONSIBLE FOR
THE INFORMATION SHOWN ON THE A/E PLANS.

ARTS AND EDUCATION COMPLEX
UNIVERSITY OF UTAH
CAMPUS CENTER DRIVE
SALT LAKE CITY, UTAH 84112
FIRE ALARM SYSTEM


NFS
NELSON FIRE SYSTEMS
801-468-8300

DRAWN BY: JJC
DESIGNED BY: XXXX
APPROVED BY: DPS
DATE: 12/26/2013
SCALE: N.T.S.
PROJECT NO: XXXX
REV NO: XXXX
DRAWING NAME:
BTSAC SECOND FM.DWG


FIRE ALARM SYSTEM
LEVEL 2
NUMBERS

PAGE:
FA-2-03




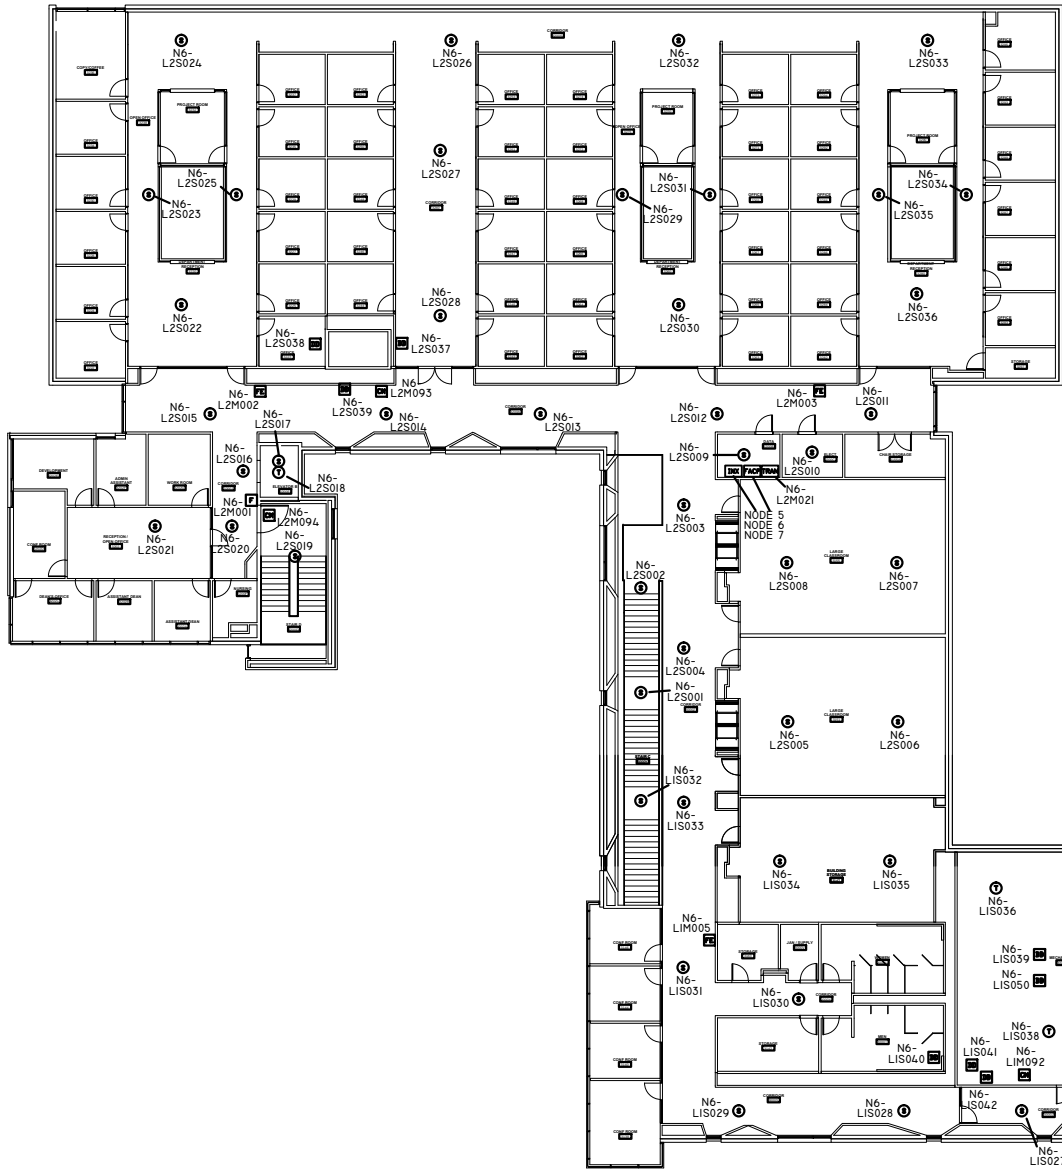

THIRD LEVEL

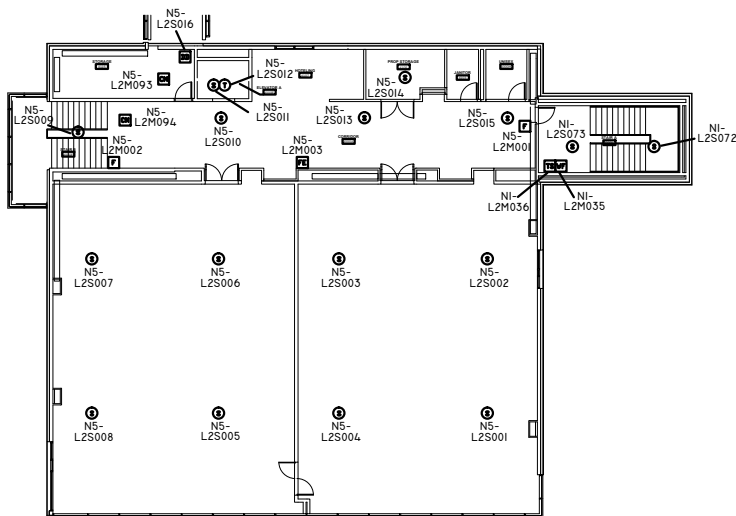

FOURTH LEVEL

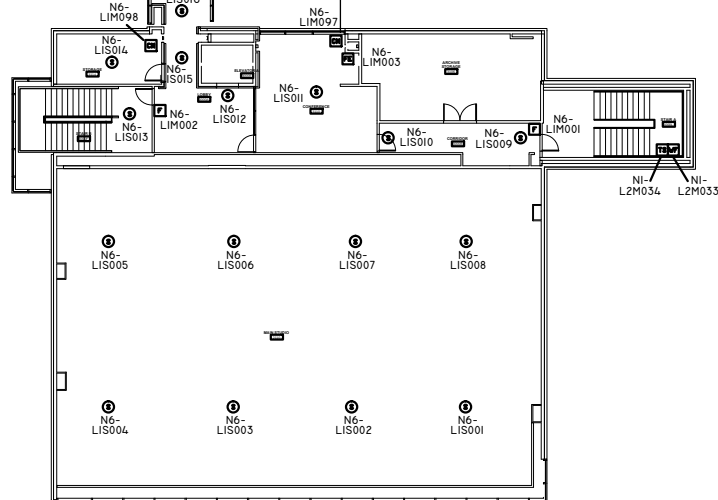

FIFTH LEVEL

DEVICE LEGEND	
SYMBOL	DESCRIPTION
S	SMOKE DETECTOR
H	HEAT DETECTOR
F	MANUAL PULL STATION
DD	DUCT DETECTOR
WF	WATERFLOW SWITCH
TS	TAMPER SWITCH
FE	ENGAGE FIRE EXTINGUISHER
MM	MONITOR MODULE
CM	CONTROL MODULE
RA	REMOTE ANNUNCIATOR
FACP	FIRE ALARM CONTROL PANEL
TRAN	TRANSPONDER PANEL

NOTE:
NFS DRAWINGS ARE BASED ON THE PROJECT
ARCHITECT/ENGINEER (A/E) PLANS AND SPECIFICATIONS
FURNISHED TO NFS. A/E IS SOLELY RESPONSIBLE
(NOT NFS) FOR THE TYPE, SIZE, LOCATION, AND
SUITABILITY OF ALL FIRE ALARMS, CONTROL PANELS,
AND OTHER DEVICES SHOWN ON THE A/E PLANS.
NFS DRAWINGS ARE TO SHOW ONLY THE WIRING
DIAGRAMS BETWEEN FIRE ALARM DEVICES AND
CONTROL PANELS. NFS IS NOT RESPONSIBLE FOR
THE INFORMATION SHOWN ON THE A/E PLANS.

ARTS AND EDUCATION COMPLEX
UNIVERSITY OF UTAH
CAMPUS CENTER DRIVE
SALT LAKE CITY, UTAH 84112
FIRE ALARM SYSTEM

NFS
NELSON FIRE SYSTEMS
801-468-8300

DRAWN BY:	JJG
DESIGNED BY:	XXXX
APPROVED BY:	DPS
DATE:	12/16/2013
SCALE:	N.T.S.
PROJECT NO:	XXXX
REV NO:	XXXX
DRAWING NAME:	BTSAEC THIRD FM.DWG

FIRE ALARM SYSTEM
LEVEL 3
NUMBERS

PAGE:
FA-3-03

