



BASEMENT

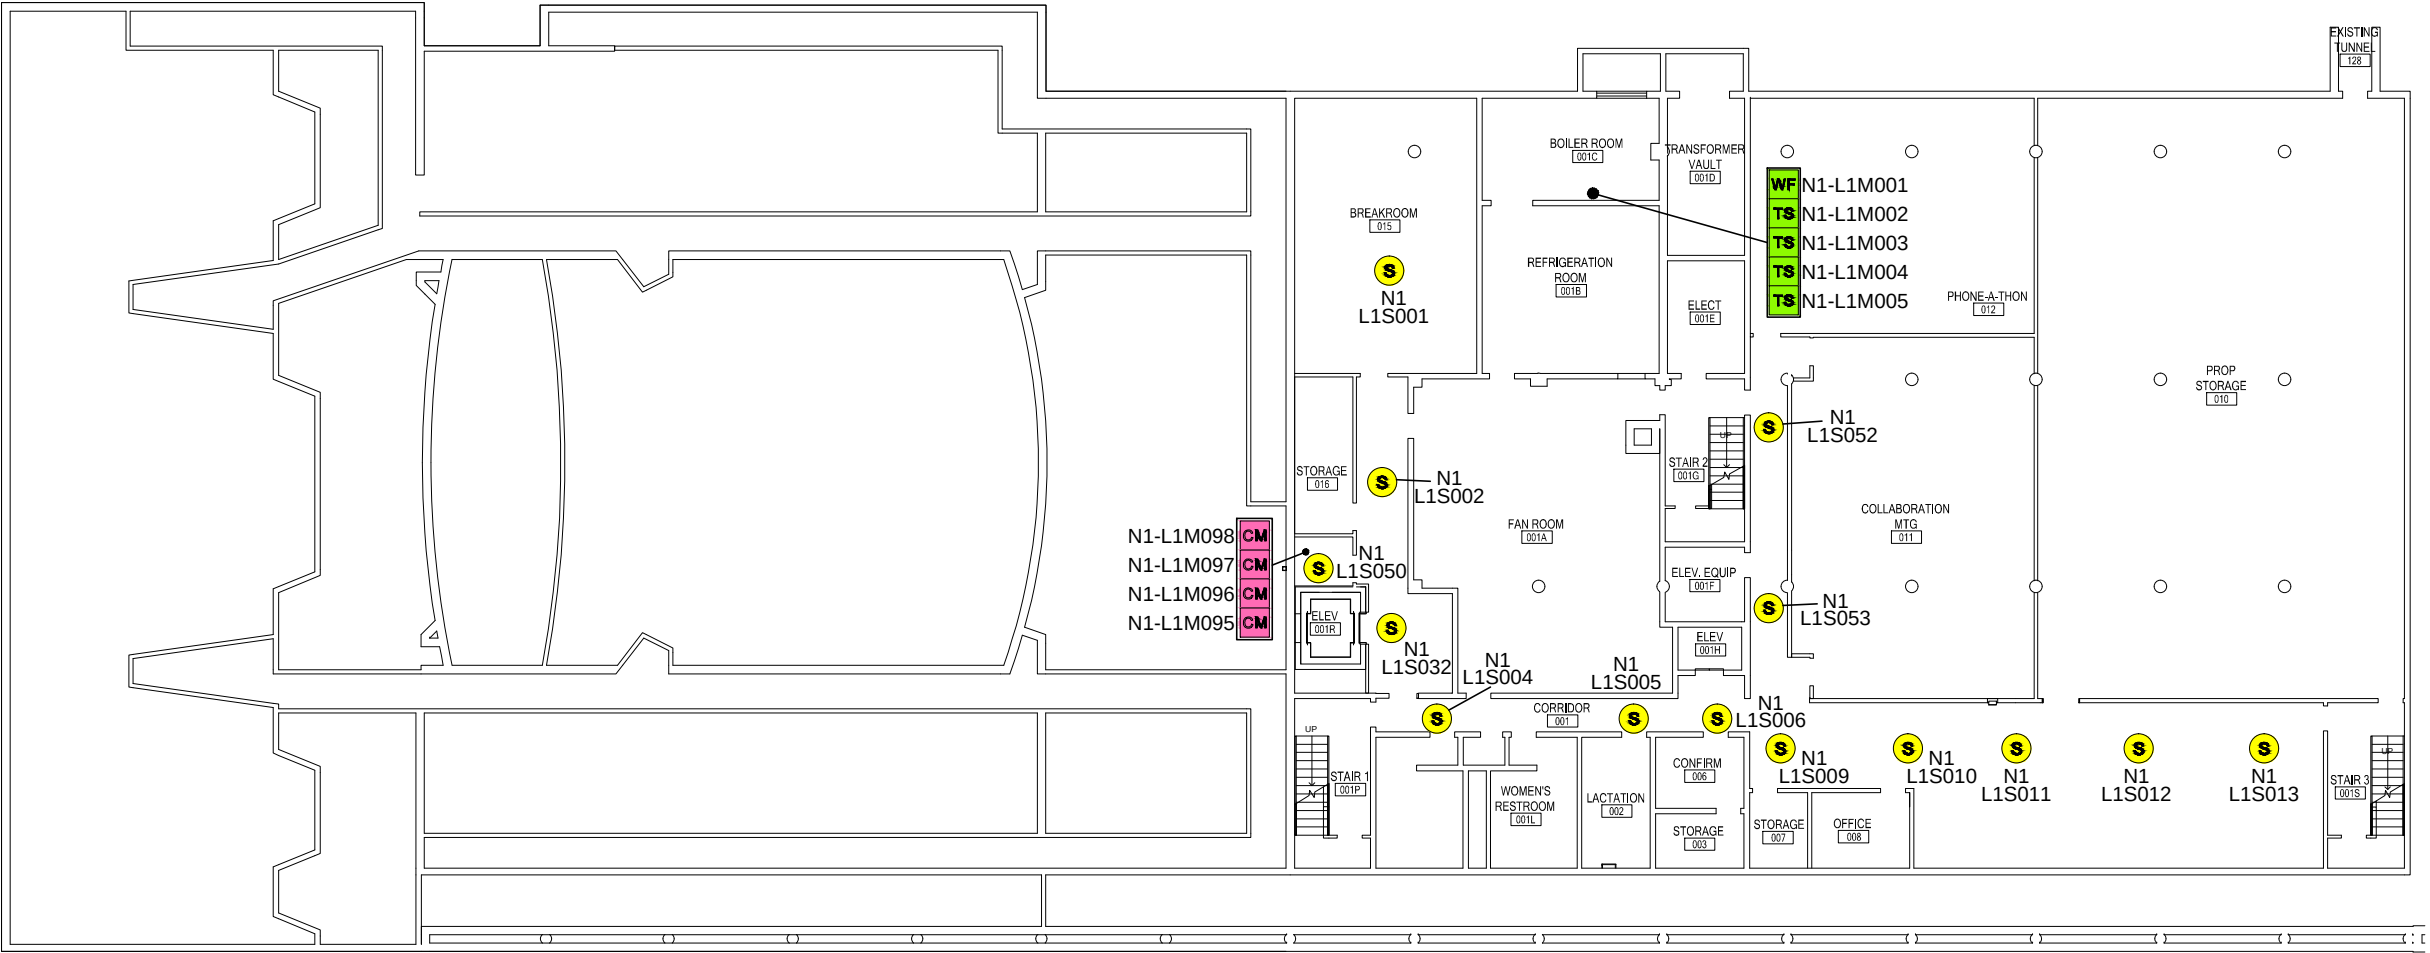

DEVICE LEGEND	
SYMBOL	DESCRIPTION
	SMOKE DETECTOR
	WATER FLOW SWITCH MODULE
	TAMPER SWITCH MODULE
	CONTROL MODULE
	RELAY
	FIRE ALARM CONTROL UNIT
	TRANSPONDER PANEL

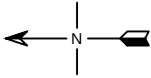

NOTE:
NFS DRAWINGS ARE BASED ON THE PROJECT ARCHITECT/ENGINEER (A/E) PLANS AND SPECIFICATIONS FURNISHED TO NFS. A/E IS SOLELY RESPONSIBLE (NOT NFS) FOR THE TYPE, SIZE, LOCATION, AND SUITABILITY OF ALL FIRE ALARMS, CONTROL PANELS, AND OTHER DEVICES SHOWN ON THE A/E PLANS. NFS DRAWINGS ARE TO SHOW ONLY THE WIRING DIAGRAMS BETWEEN FIRE ALARM DEVICES AND CONTROL PANELS. NFS IS NOT RESPONSIBLE FOR THE INFORMATION SHOWN ON THE A/E PLANS.

UNIVERSITY OF UTAH
THEATRE & DEVELOPMENT REMODEL BLDG 73
332 SOUTH 1400 EAST
SALT LAKE CITY, UTAH 84112
FIRE ALARM SYSTEM

NFS
NELSON FIRE SYSTEMS

DRAWN BY:	JPK
DESIGNED BY:	XXXX
APPROVED BY:	TDT
DATE:	1/17/20
SCALE:	N.T.S
PROJECT NO:	XXXX
REVISION NO:	XXXX
DRAWING NAME:	
UofU OLD LAW BLDG 73 B FM.DWG	


NELSON FIRE SYSTEMS

BASEMENT


PAGE:




PENTHOUSE

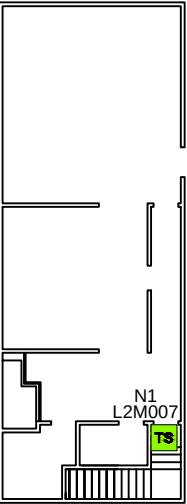


LEVEL 2

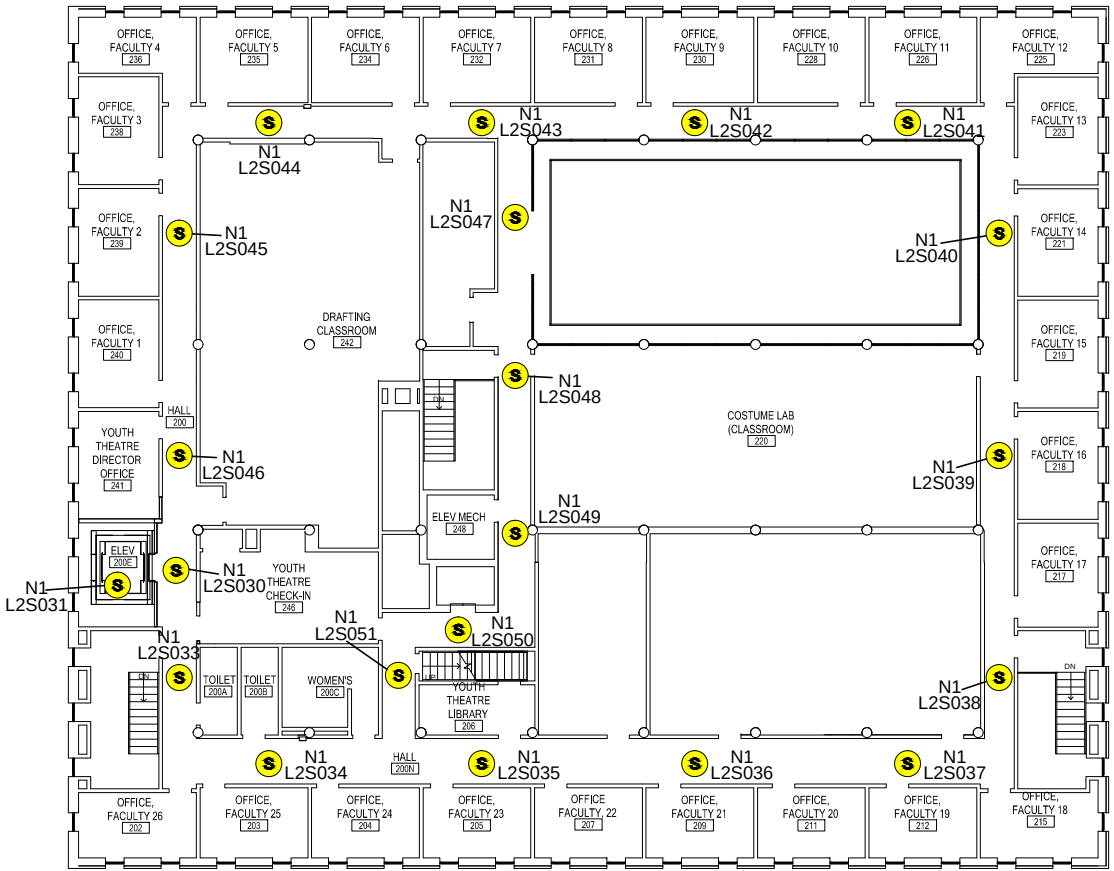

LEVEL 1

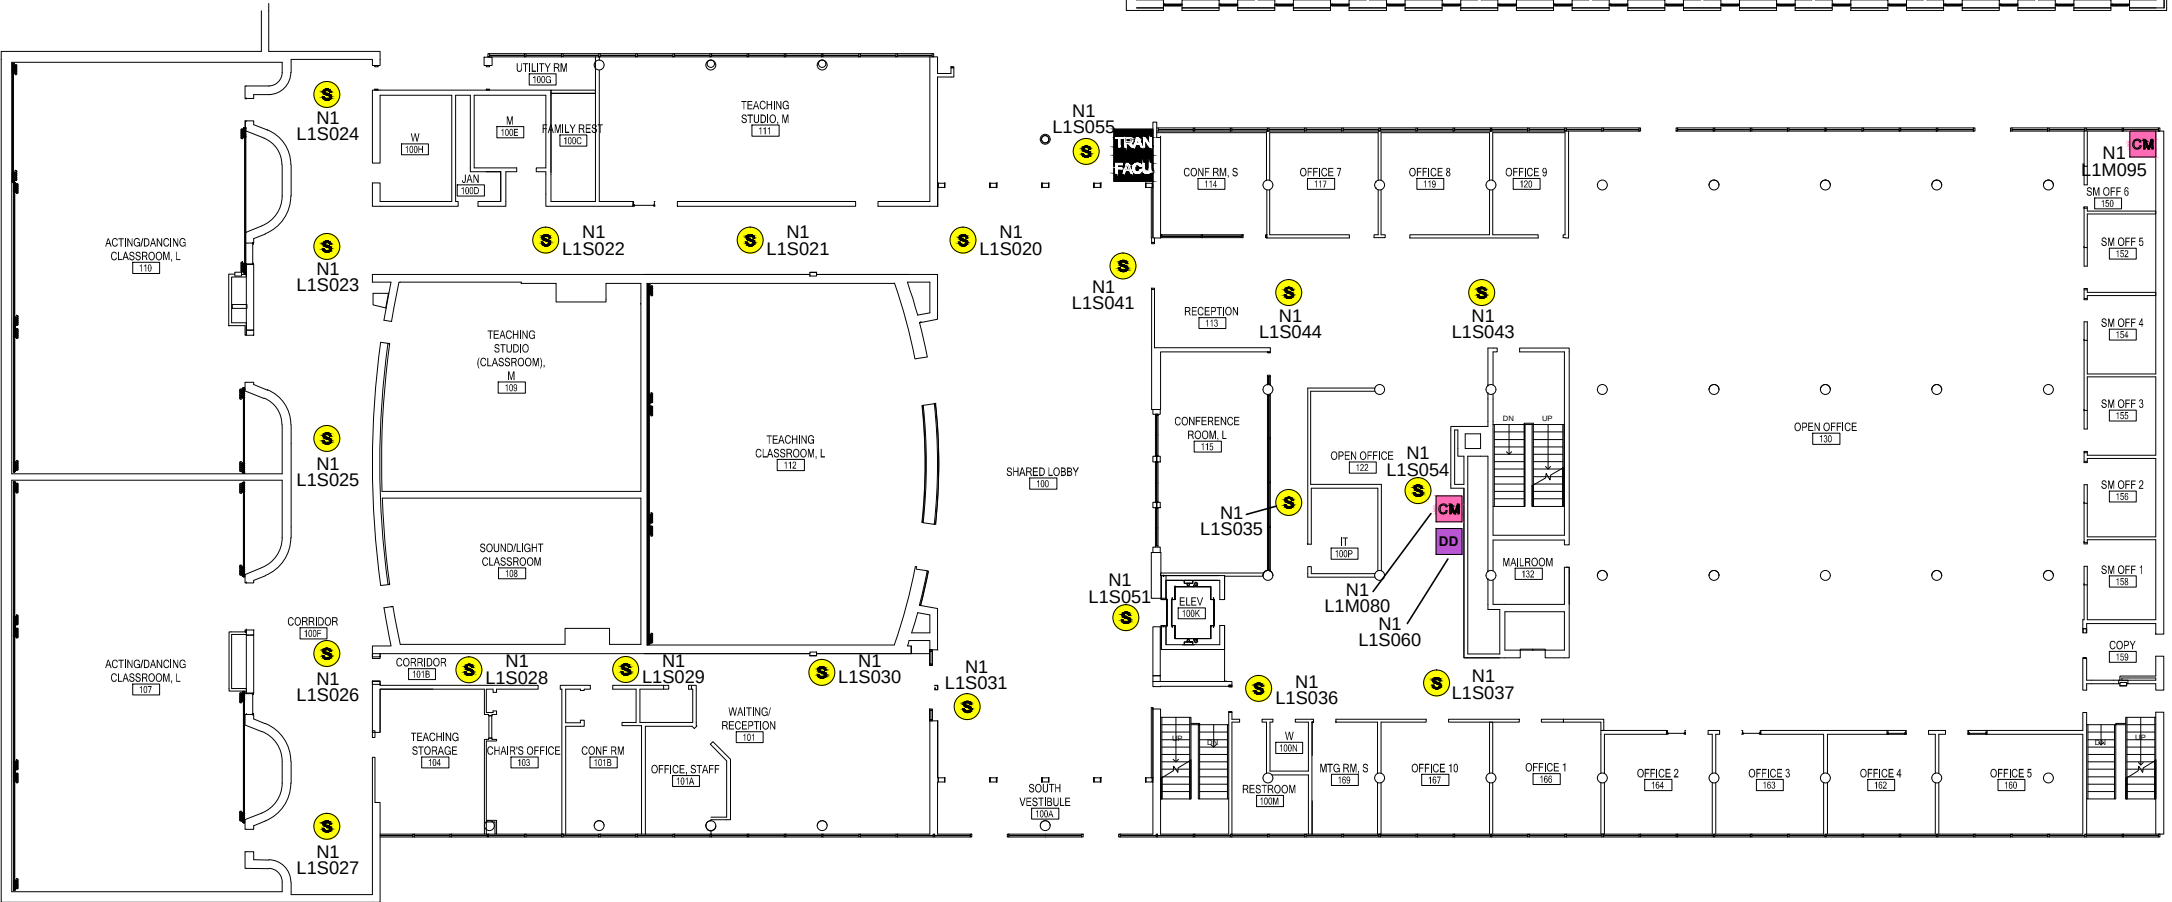

DEVICE LEGEND	
SYMBOL	DESCRIPTION
	SMOKE DETECTOR
	DUCT DETECTOR
	WATER FLOW SWITCH MODULE
	TAMPER SWITCH MODULE
	CONTROL MODULE
	FIRE ALARM CONTROL UNIT
	TRANSPONDER PANEL

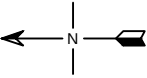

NOTE:
NFS DRAWINGS ARE BASED ON THE PROJECT
ARCHITECTURE/ENGINEER (A/E) PLANS AND
SPECIFICATIONS FURNISHED TO NFS. A/E IS SOLELY
RESPONSIBLE (NOT NFS) FOR THE TYPE, SIZE,
LOCATION, AND SUITABILITY OF ALL FIRE ALARMS,
CONTROL PANELS, AND OTHER DEVICES SHOWN ON
THE A/E PLANS. NFS DRAWINGS ARE TO SHOW ONLY
THE WIRING DIAGRAMS BETWEEN FIRE ALARM
DEVICES AND CONTROL PANELS. NFS IS NOT
RESPONSIBLE FOR THE INFORMATION SHOWN ON THE
A/E PLANS.

UNIVERSITY OF UTAH
THEATRE & DEVELOPMENT REMODEL BLDG 73
332 SOUTH 1400 EAST
SALT LAKE CITY, UTAH 84112
FIRE ALARM SYSTEM

NFS
NELSON FIRE SYSTEMS

DRAWN BY: JPK
DESIGNED BY: XXXX
APPROVED BY: XXXX
DATE: 1/17/20
SCALE: N.T.S.
PROJECT NO: XXXX
REVISION NO: XXXX
DRAWING NAME:
UOFLD OLD LAW BLDG 73 FM.DWG

NELSON FIRE SYSTEMS
LEVEL 1, 2 AND PENTHOUSE

PAGE:
FINAL MAP

