

NOTE:
NFS DRAWINGS ARE BASED ON THE PROJECT
ARCHITECTURE/ENGINEER (A/E) PLANS AND
SPECIFICATIONS FURNISHED TO NFS. A/E IS SOLELY
RESPONSIBLE (NOT NFS) FOR THE TYPE, SIZE,
LOCATION, AND SUITABILITY OF ALL FIRE ALARMS,
CONTROL PANELS, AND OTHER DEVICES SHOWN ON
THE A/E PLANS. NFS DRAWINGS ARE TO SHOW ONLY
THE WIRING DIAGRAMS BETWEEN FIRE ALARM
DEVICES AND CONTROL PANELS. NFS IS NOT
RESPONSIBLE FOR THE INFORMATION SHOWN ON THE
A/E PLANS.

GARFF EXECUTIVE EDUCATION BUILDING - LVL I
UNIVERSITY OF UTAH
1705 EAST CAMPUS CENTER DRIVE
SALT LAKE CITY, UTAH 84112
FIRE ALARM SYSTEM

NFS
NELSON FIRE SYSTEMS
801-468-8300

DRAWN BY: KLM
DESIGNED BY: DPS
APPROVED BY: DPS
DATE: 7/16/18
SCALE: N.T.S.
PROJECT NO.: XXXX
REVISION NO.: XXXX
DRAWING NAME:
GARFF EXECUTIVE ED IFM DWG


NELSON FIRE SYSTEMS


LEVEL I

PAGE:

FINAL MAP

DEVICE LEGEND	
SYMBOL	DESCRIPTION
①	SMOKE DETECTOR
②	HEAT DETECTOR
③	PULL STATION
④	DUCT DETECTOR
⑤	TAMPER SWITCH
⑥	WATERFLOW SWITCH
⑦	KITCHENHOOD MONITOR MODULE
⑧	MONITOR MODULE
⑨	CONTROL MODULE
⑩	LOCAL OPERATING CONSOLE
⑪	FIRE ALARM CONTROL UNIT
⑫	TRANSPONDER PANEL
⑬	PRE-ACTION PANEL

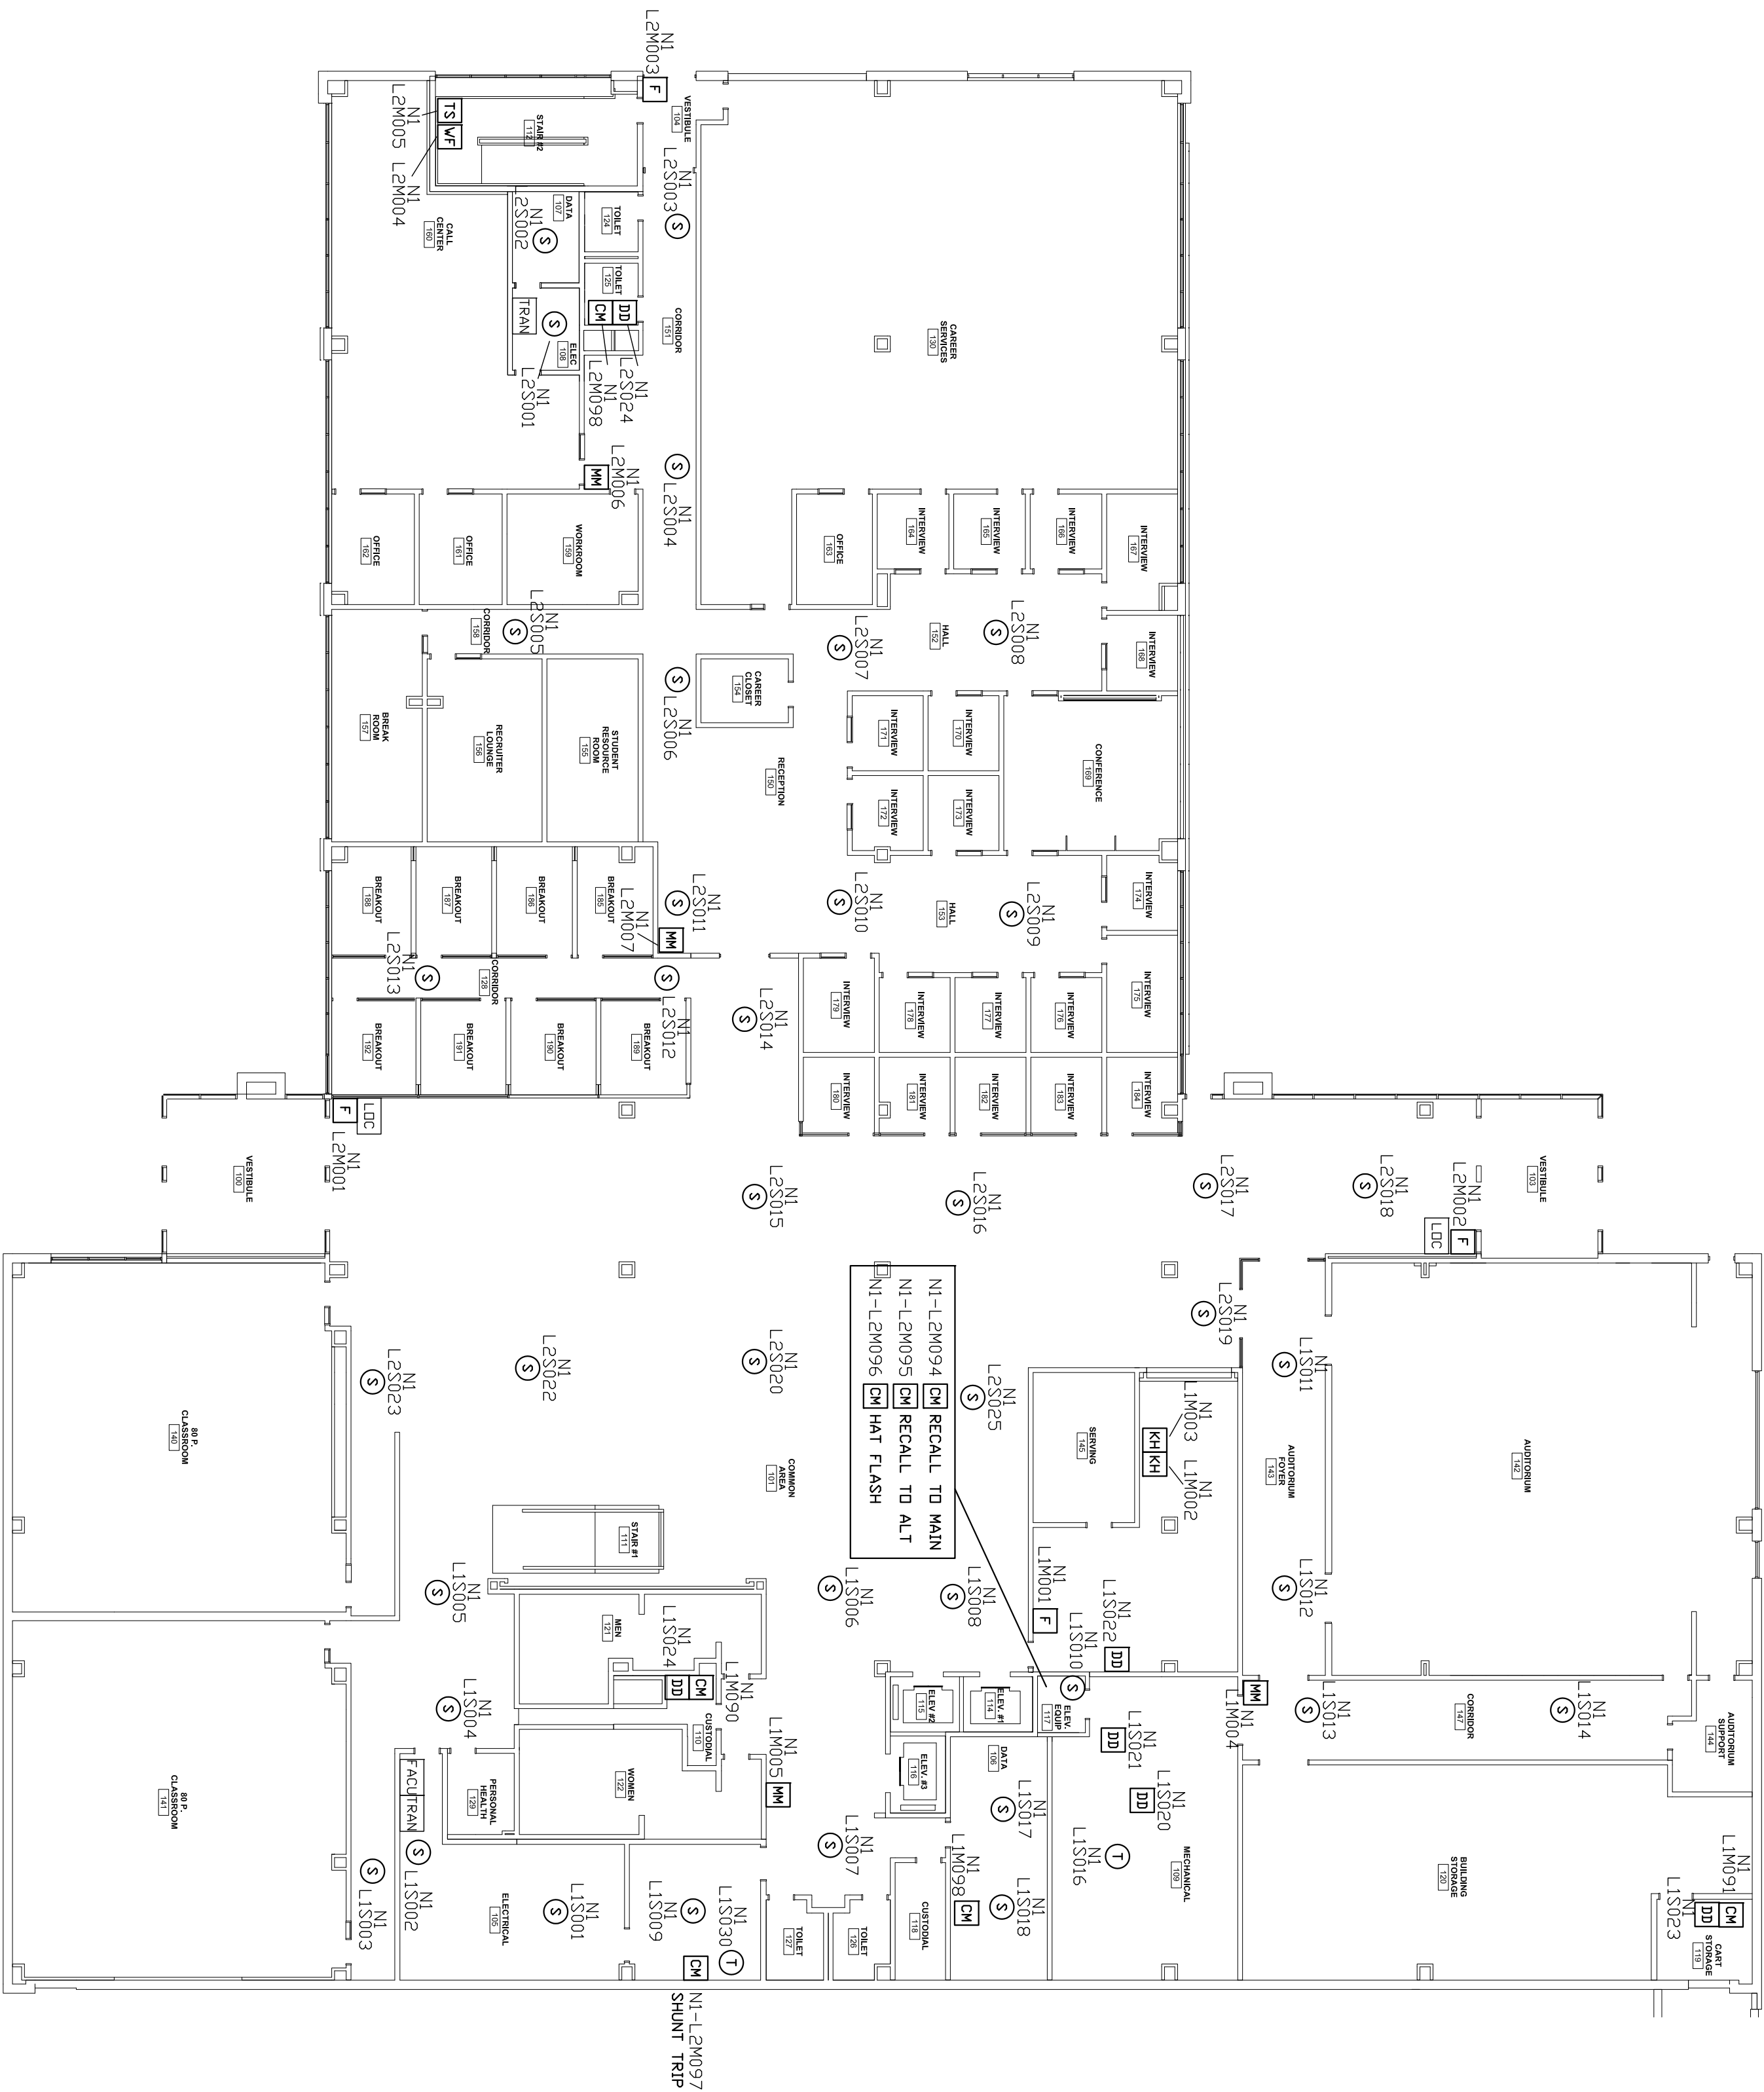

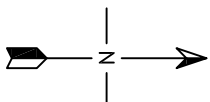

NOTE:
NFS DRAWINGS ARE BASED ON THE PROJECT
ARCHITECTURE/ENGINEER (A/E) PLANS AND
SPECIFICATIONS FURNISHED TO NFS. A/E IS SOLELY
RESPONSIBLE (NOT NFS) FOR THE TYPE, SIZE,
LOCATION, AND SUITABILITY OF ALL FIRE ALARMS,
CONTROL PANELS, AND OTHER DEVICES SHOWN ON
THE A/E PLANS. NFS DRAWINGS ARE TO SHOW ONLY
THE WIRING DIAGRAMS BETWEEN FIRE ALARM
DEVICES AND CONTROL PANELS. NFS IS NOT
RESPONSIBLE FOR THE INFORMATION SHOWN ON THE
A/E PLANS.

GARFF EXECUTIVE EDUCATION BUILDING - LVL 2
UNIVERSITY OF UTAH
1705 EAST CAMPUS CENTER DRIVE
SALT LAKE CITY, UTAH 84112
FIRE ALARM SYSTEM


NFS
NELSON FIRE SYSTEMS
801-468-8300



DRAWN BY: KLM
DESIGNED BY: DPS
APPROVED BY: N.T.S.
DATE: 7/16/18
SCALE: N.T.S.
PROJECT NO.: XXXX
REVISION NO.: XXXX
DRAWING NAME:
GARFF EXECUTIVE ED 2FM DWG

NELSON FIRE SYSTEMS
LEVEL 2

PAGE:
FINAL MAP

DEVICE LEGEND	
SYMBOL	DESCRIPTION
①	SMOKE DETECTOR
②	HEAT DETECTOR
③	PULL STATION
④	DUCT DETECTOR
⑤	TAMPER SWITCH
⑥	WATERFLOW SWITCH
⑦	MONITOR MODULE
⑧	CONTROL MODULE
⑨	LOCAL OPERATING CONSOLE
⑩	FIRE ALARM CONTROL UNIT
⑪	TRANSPOUNDER PANEL
⑫	PRE-ACTION PANEL

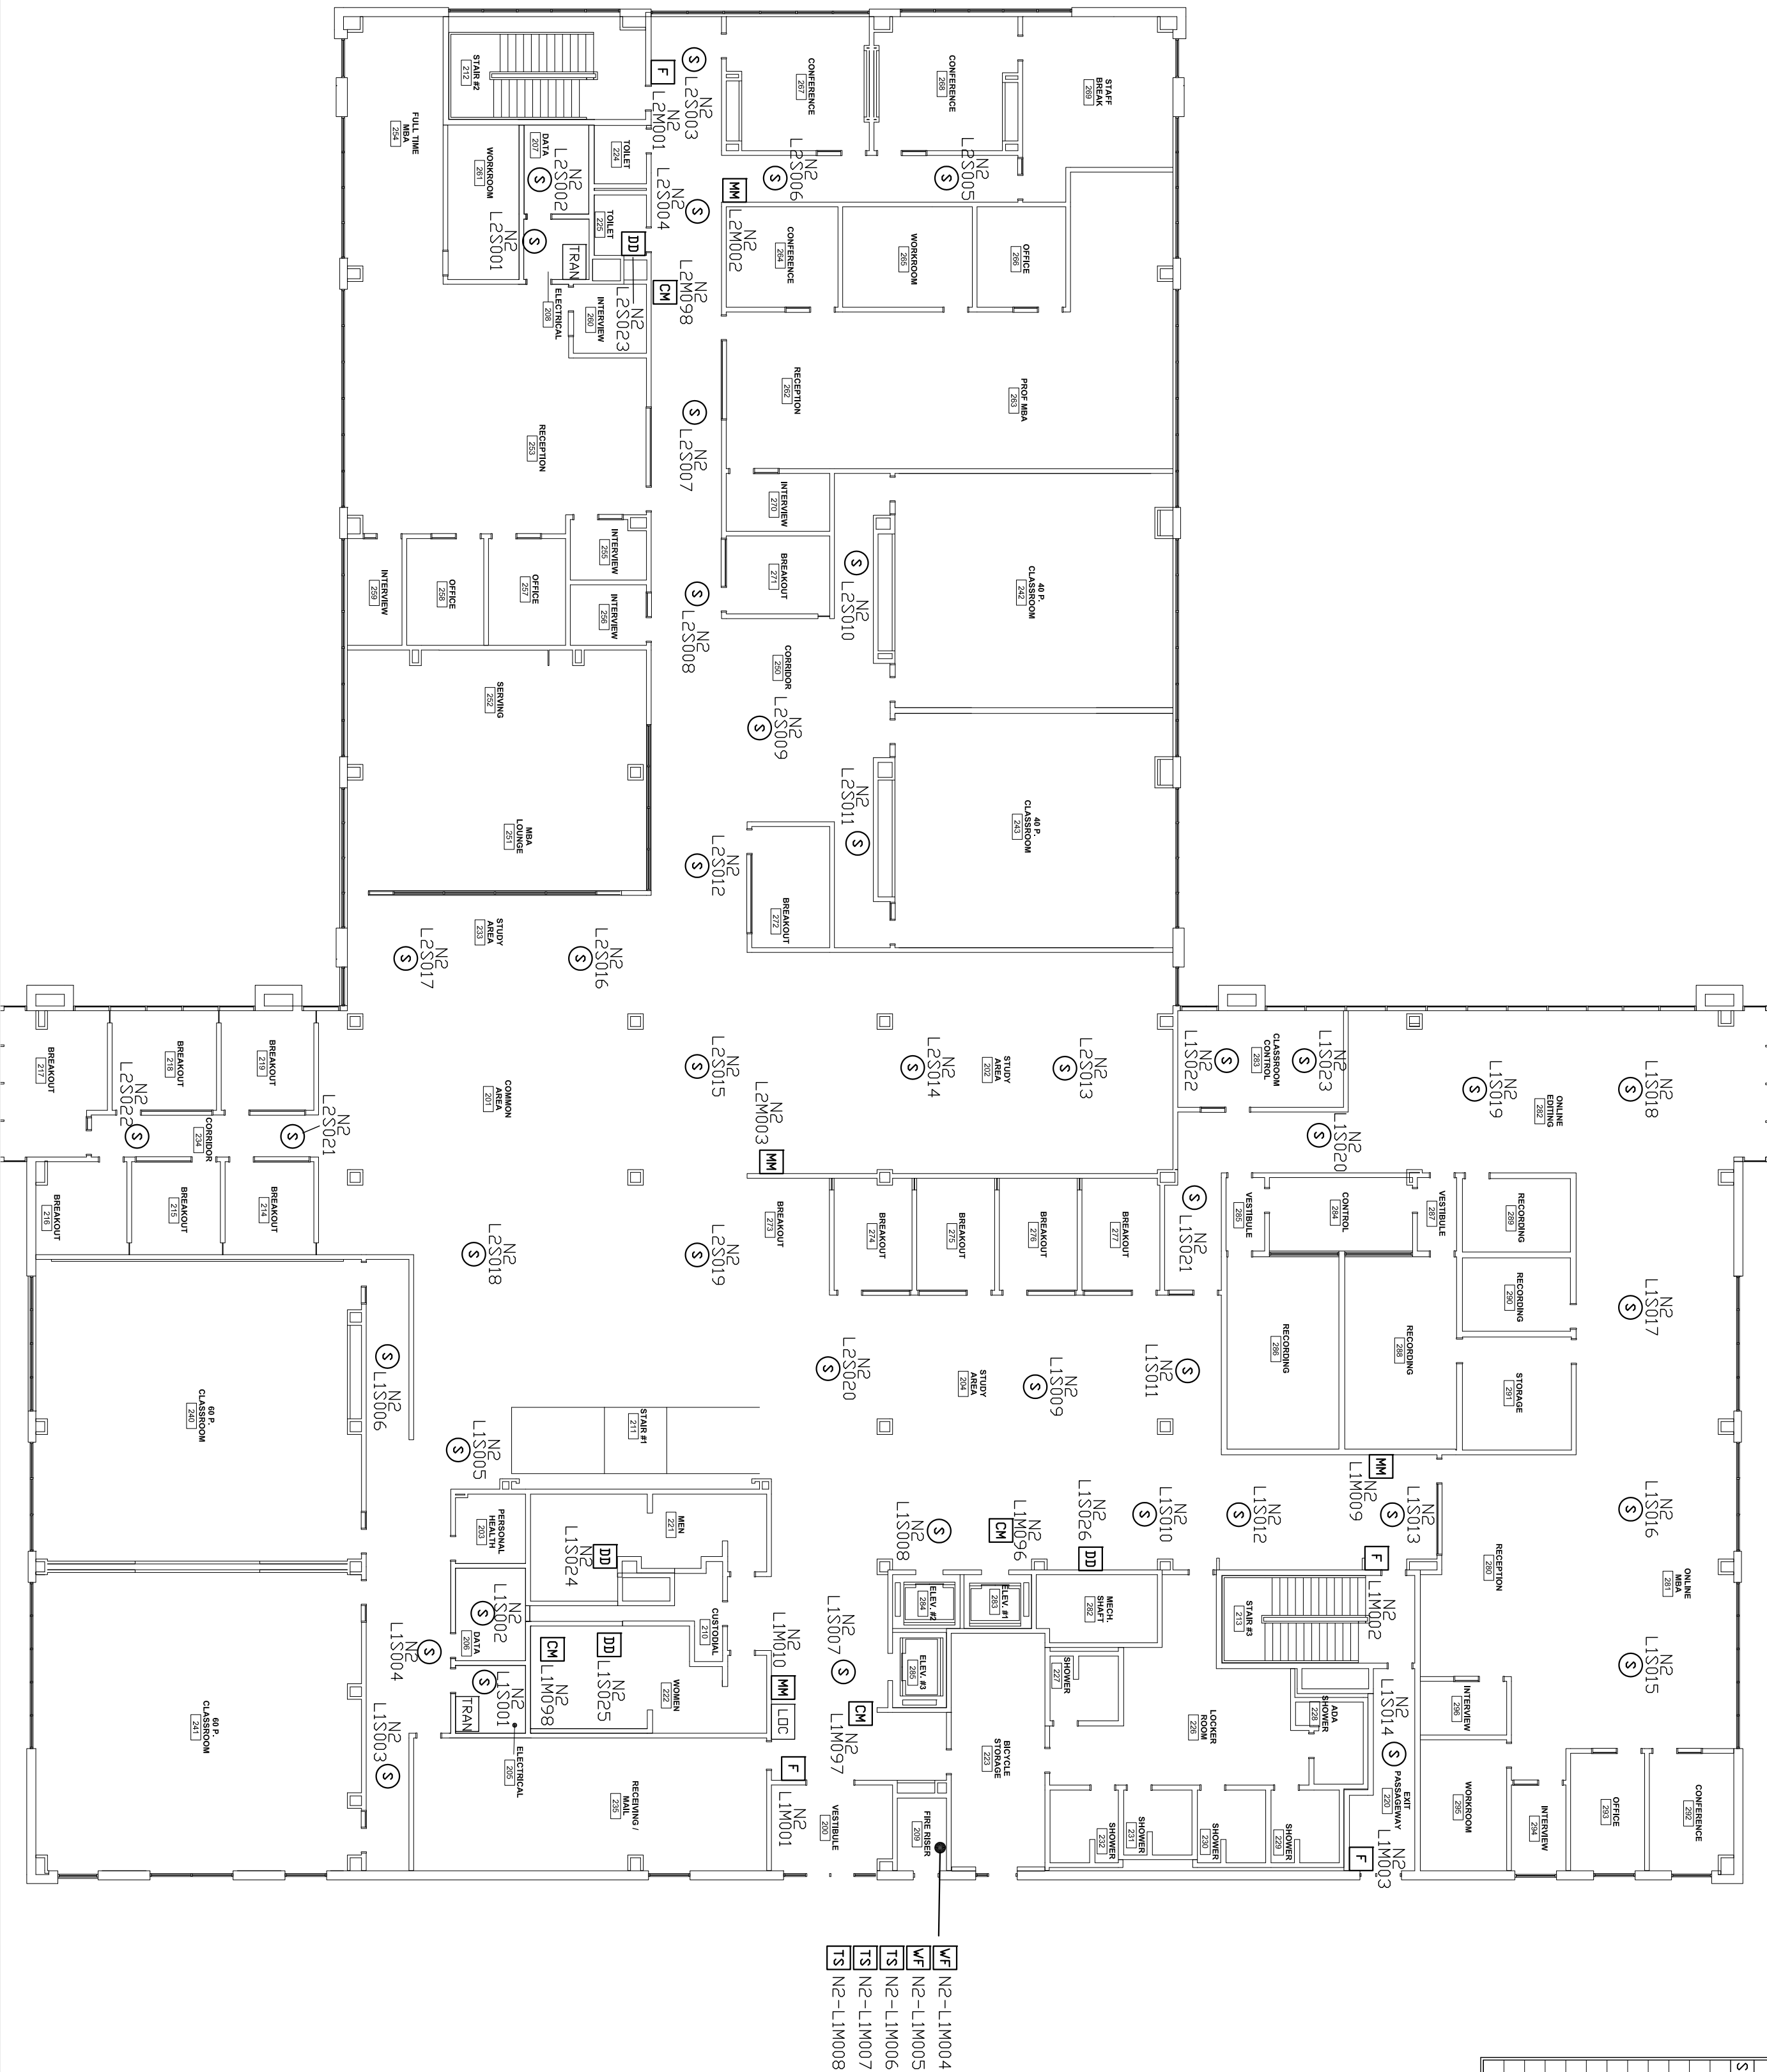

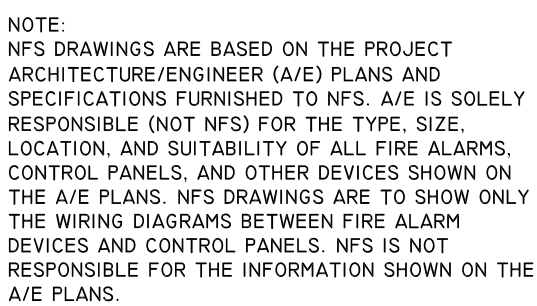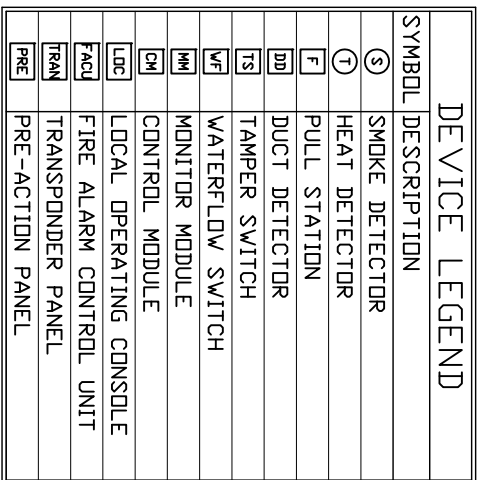


NFS
NELSON FIRE SYSTEMS
801-468-8300

NELSON FIRE SYSTEM

LEVEL 3

PAGE: **FINAL MAP**



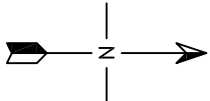

NOTE:
NFS DRAWINGS ARE BASED ON THE PROJECT
ARCHITECTURE/ENGINEER (A/E) PLANS AND
SPECIFICATIONS FURNISHED TO NFS. A/E IS SOLELY
RESPONSIBLE (NOT NFS) FOR THE TYPE, SIZE,
LOCATION, AND SUITABILITY OF ALL FIRE ALARMS,
CONTROL PANELS, AND OTHER DEVICES SHOWN ON
THE A/E PLANS. NFS DRAWINGS ARE TO SHOW ONLY
THE WIRING DIAGRAMS BETWEEN FIRE ALARM
DEVICES AND CONTROL PANELS. NFS IS NOT
RESPONSIBLE FOR THE INFORMATION SHOWN ON THE
A/E PLANS.

GARFF EXECUTIVE EDUCATION BUILDING - LVL 4
UNIVERSITY OF UTAH
1705 EAST CAMPUS CENTER DRIVE
SALT LAKE CITY, UTAH 84112
FIRE ALARM SYSTEM

NFS
NELSON FIRE SYSTEMS
801-468-8300

DRAWN BY: KLM
DESIGNED BY: DPS
APPROVED BY: N.T.S.
DATE: 7/16/18
SCALE: XXXX
PROJECT NO.: XXXX
REVISION NO.: XXXX
DRAWING NAME:
GARFF EXECUTIVE ED 4FM DWG

NELSON FIRE SYSTEMS
LEVEL 4

PAGE:
FINAL MAP

DEVICE LEGEND	
SYMBOL	DESCRIPTION
①	SMOKE DETECTOR
②	HEAT DETECTOR
③	PULL STATION
④	DUCT DETECTOR
⑤	TAMPER SWITCH
⑥	WATERFLOW SWITCH
⑦	MONITOR MODULE
⑧	CONTROL MODULE
⑨	LOCAL OPERATING CONSOLE
⑩	FIRE ALARM CONTROL UNIT
⑪	TRANSPOUNDER PANEL
⑫	PRE-ACTION PANEL

