



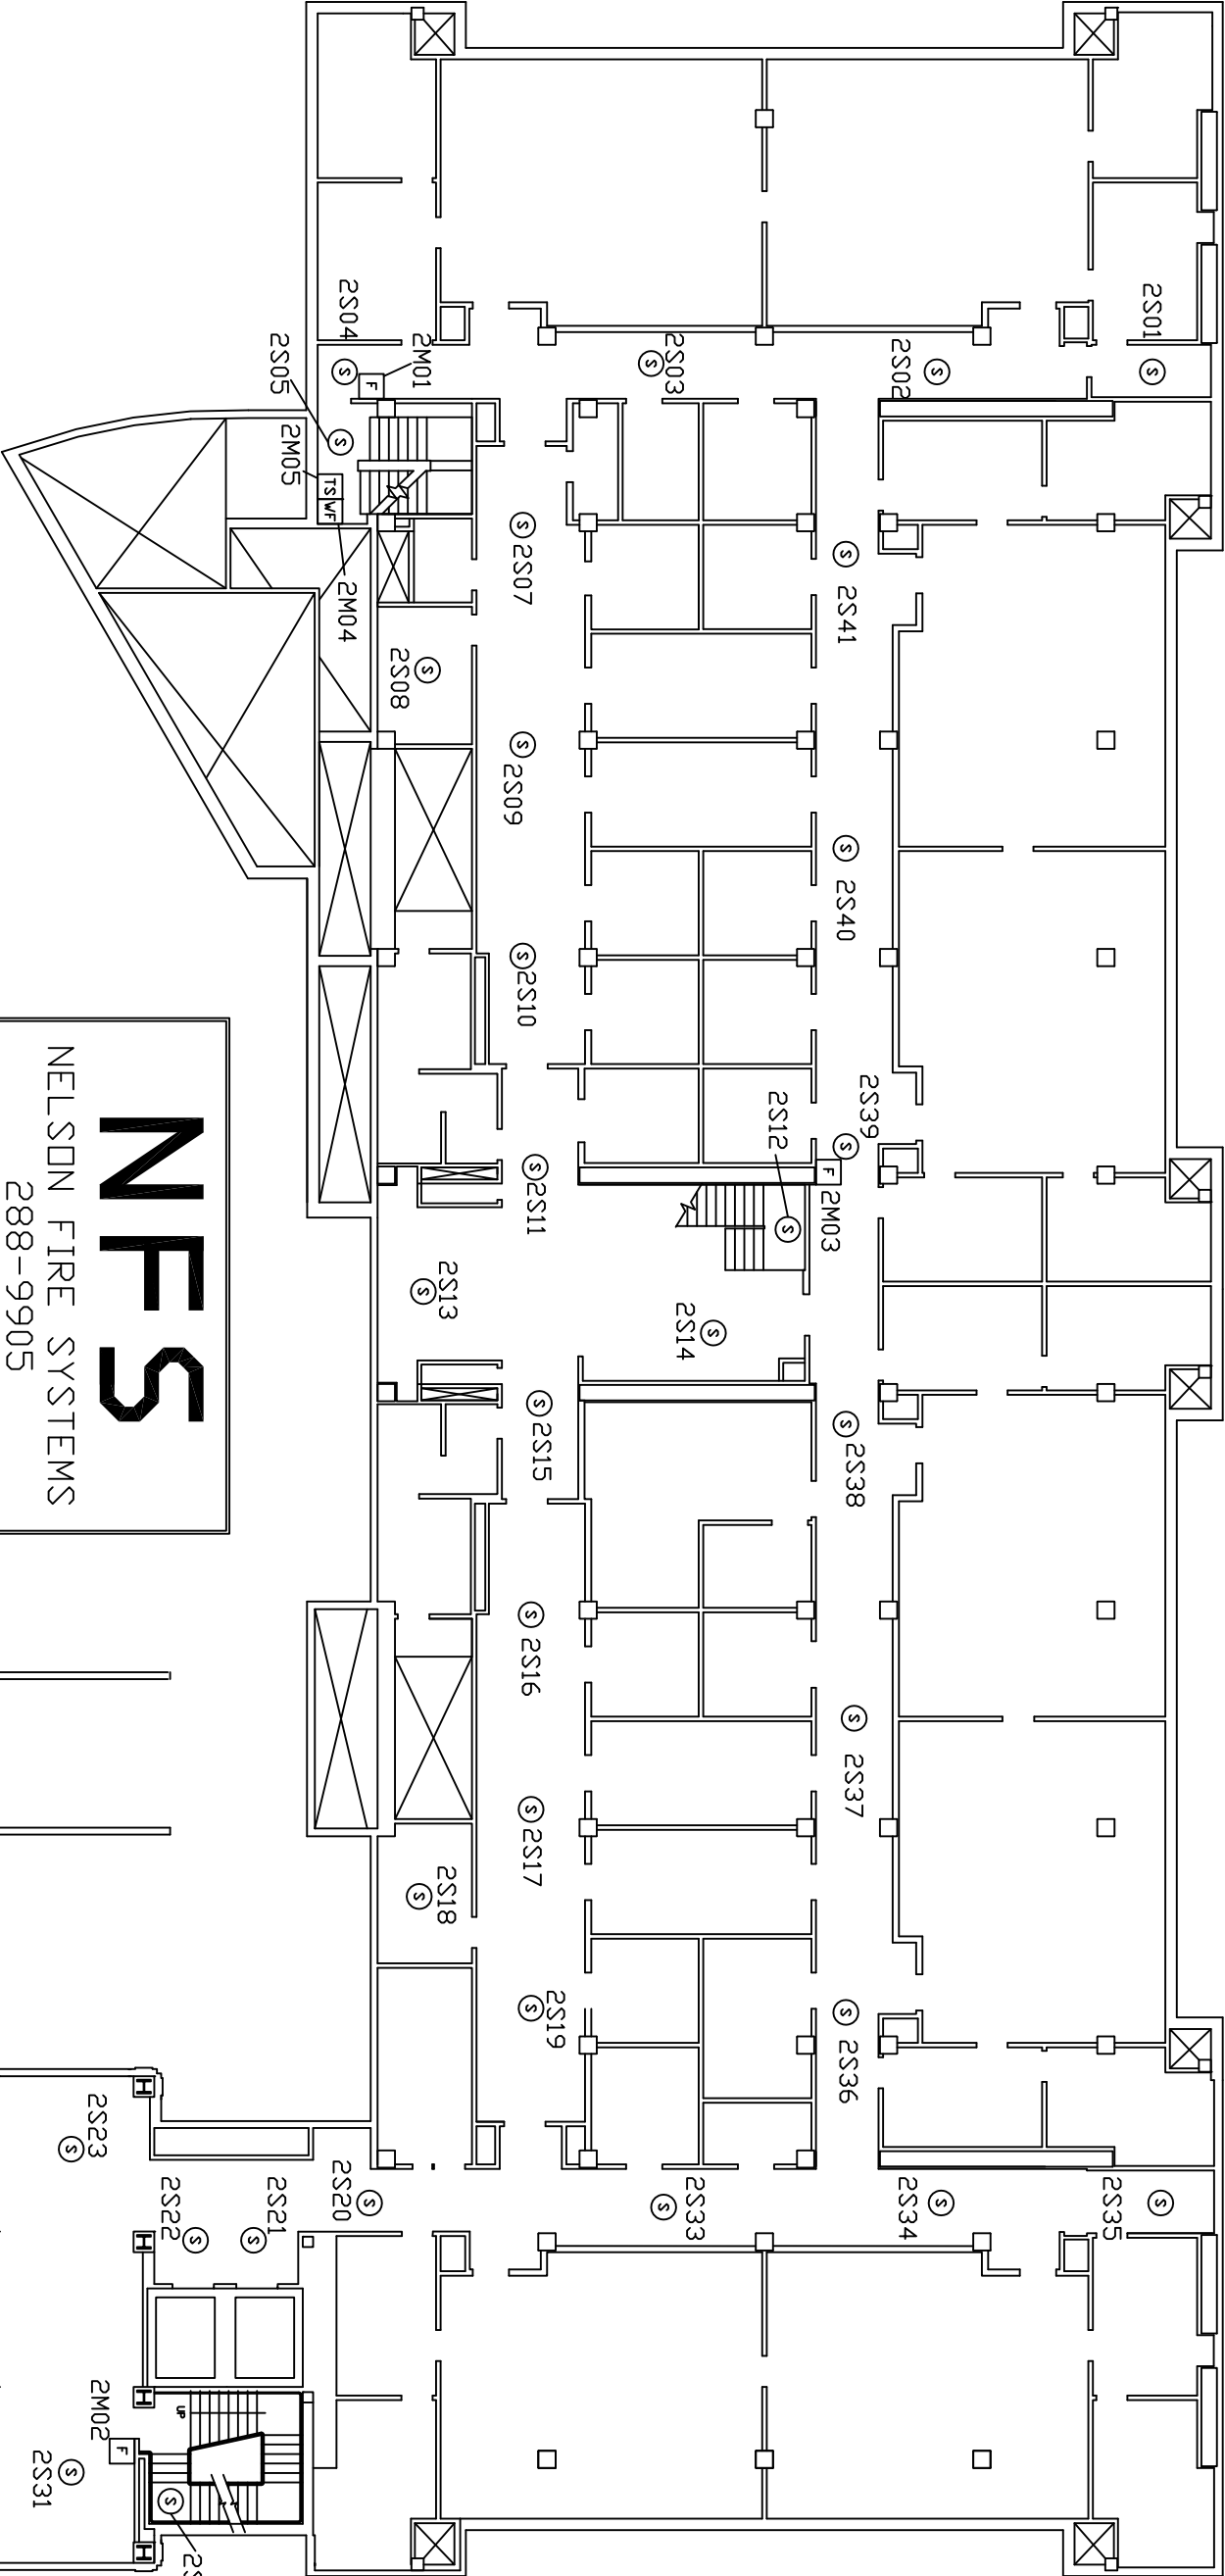

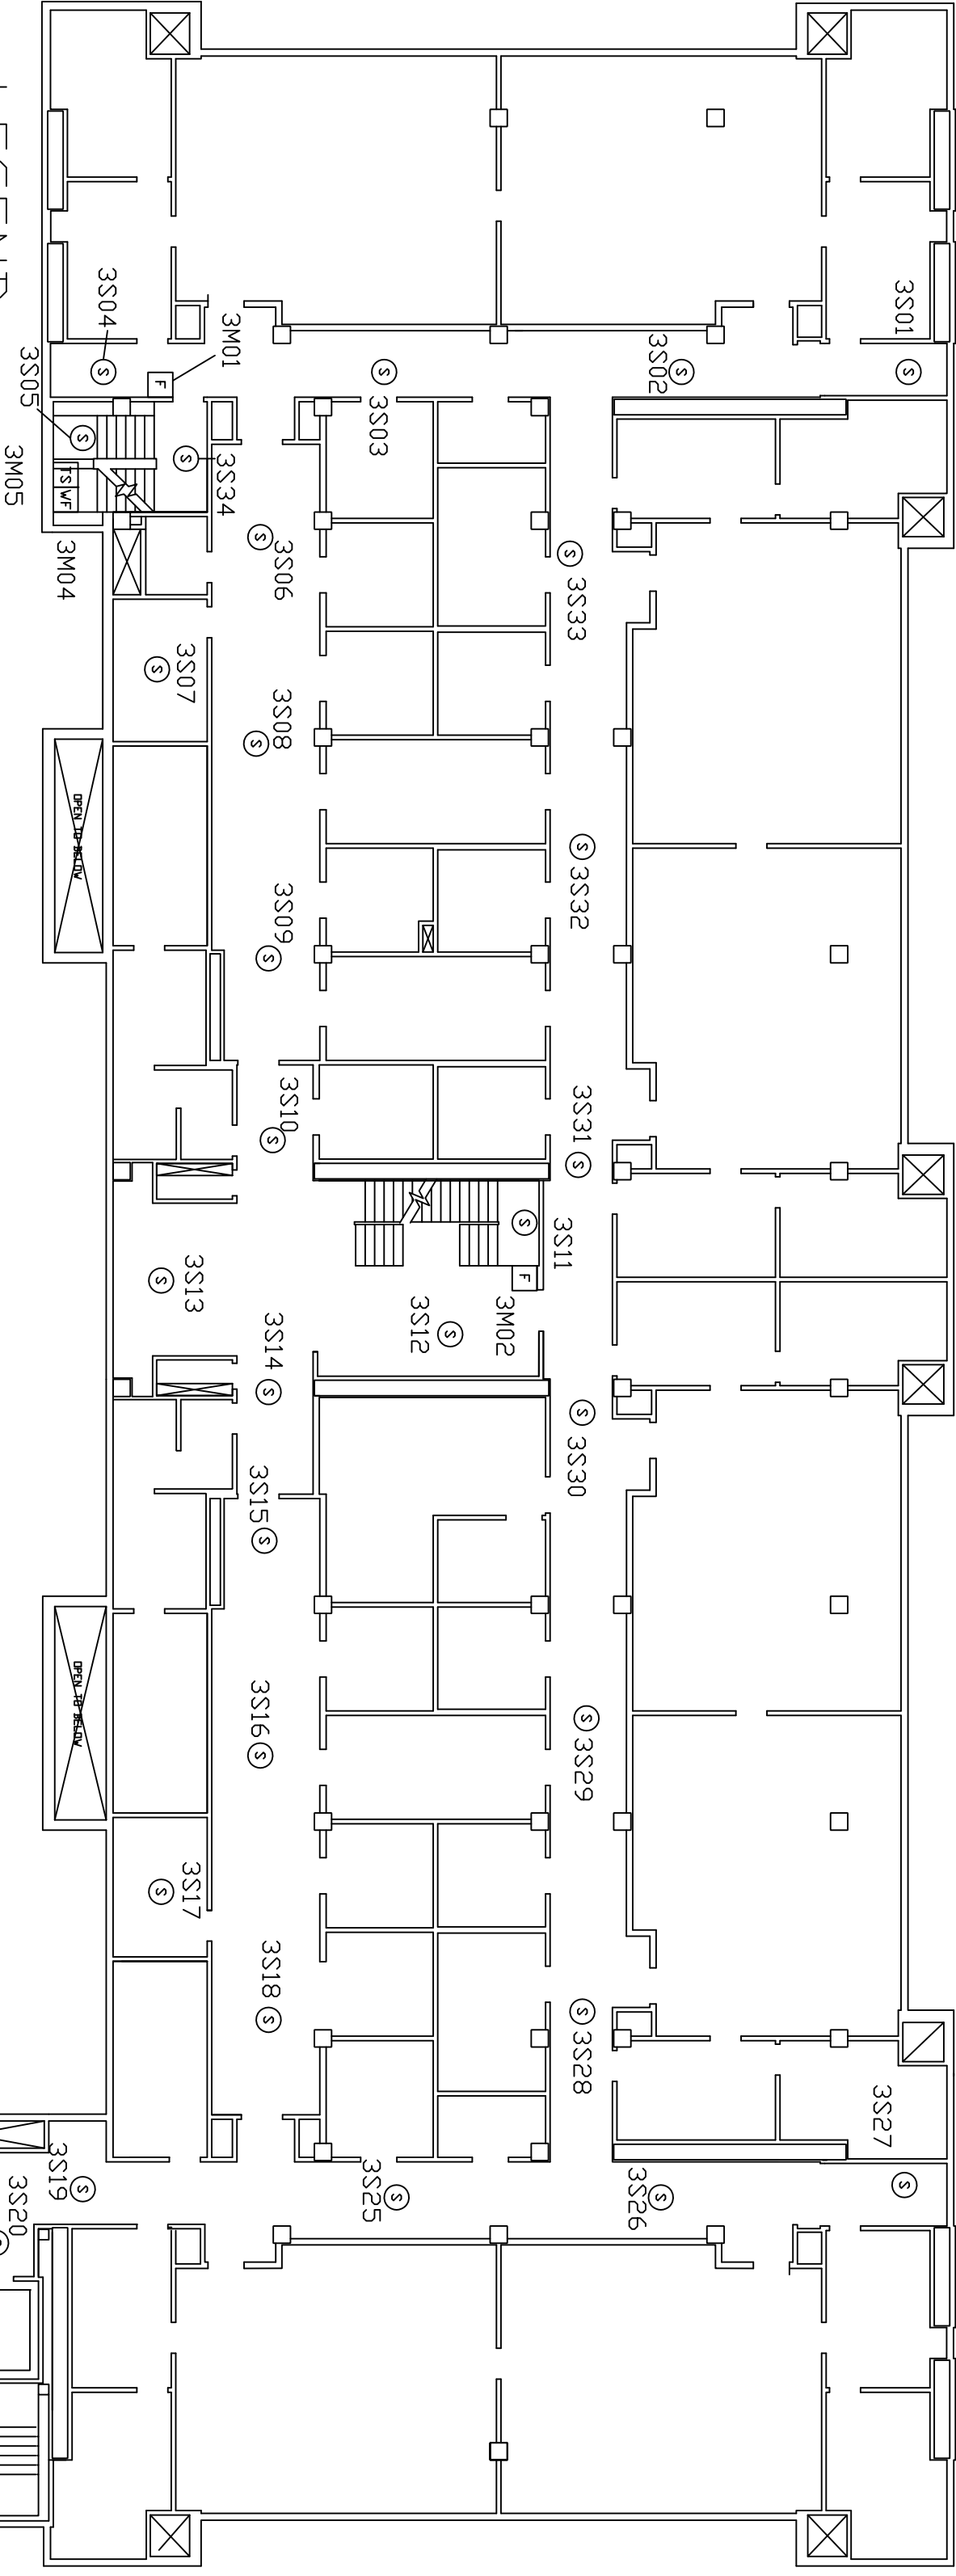


- LEGEND
- Ⓢ SMOKE DETECTOR
 - ⓕ MANUAL PULL STATION
 - ⓓⓓ DUCT DETECTOR
 - Ⓦⓕ WATERFLOW SWITCH
 - ⓉⓈ TAMPER SWITCH


NFS



NELSON FIRE SYSTEMS

288-9905

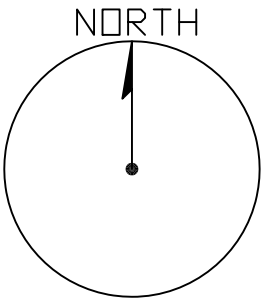

BIOLOGY RESEARCH BUILDING
UNIVERSITY OF UTAH
LEVEL 4
SALT LAKE CITY, UTAH
JUNE 8, 1998
U0UBIDR4.DWG

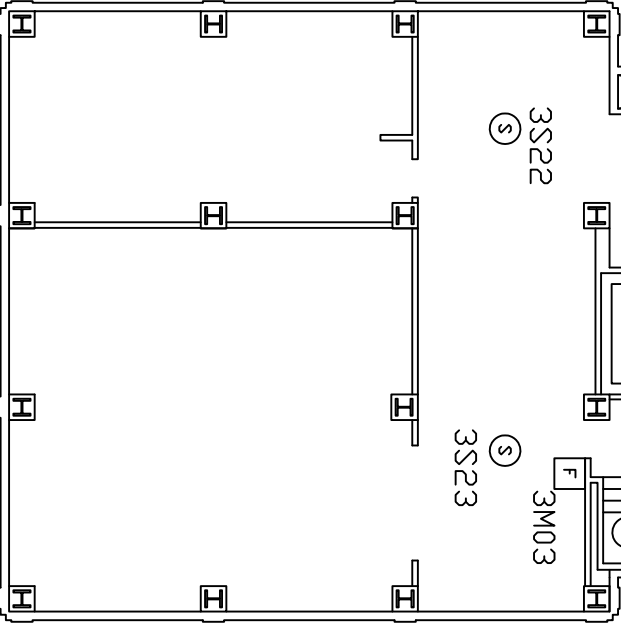

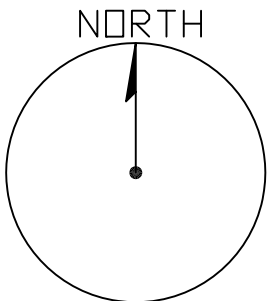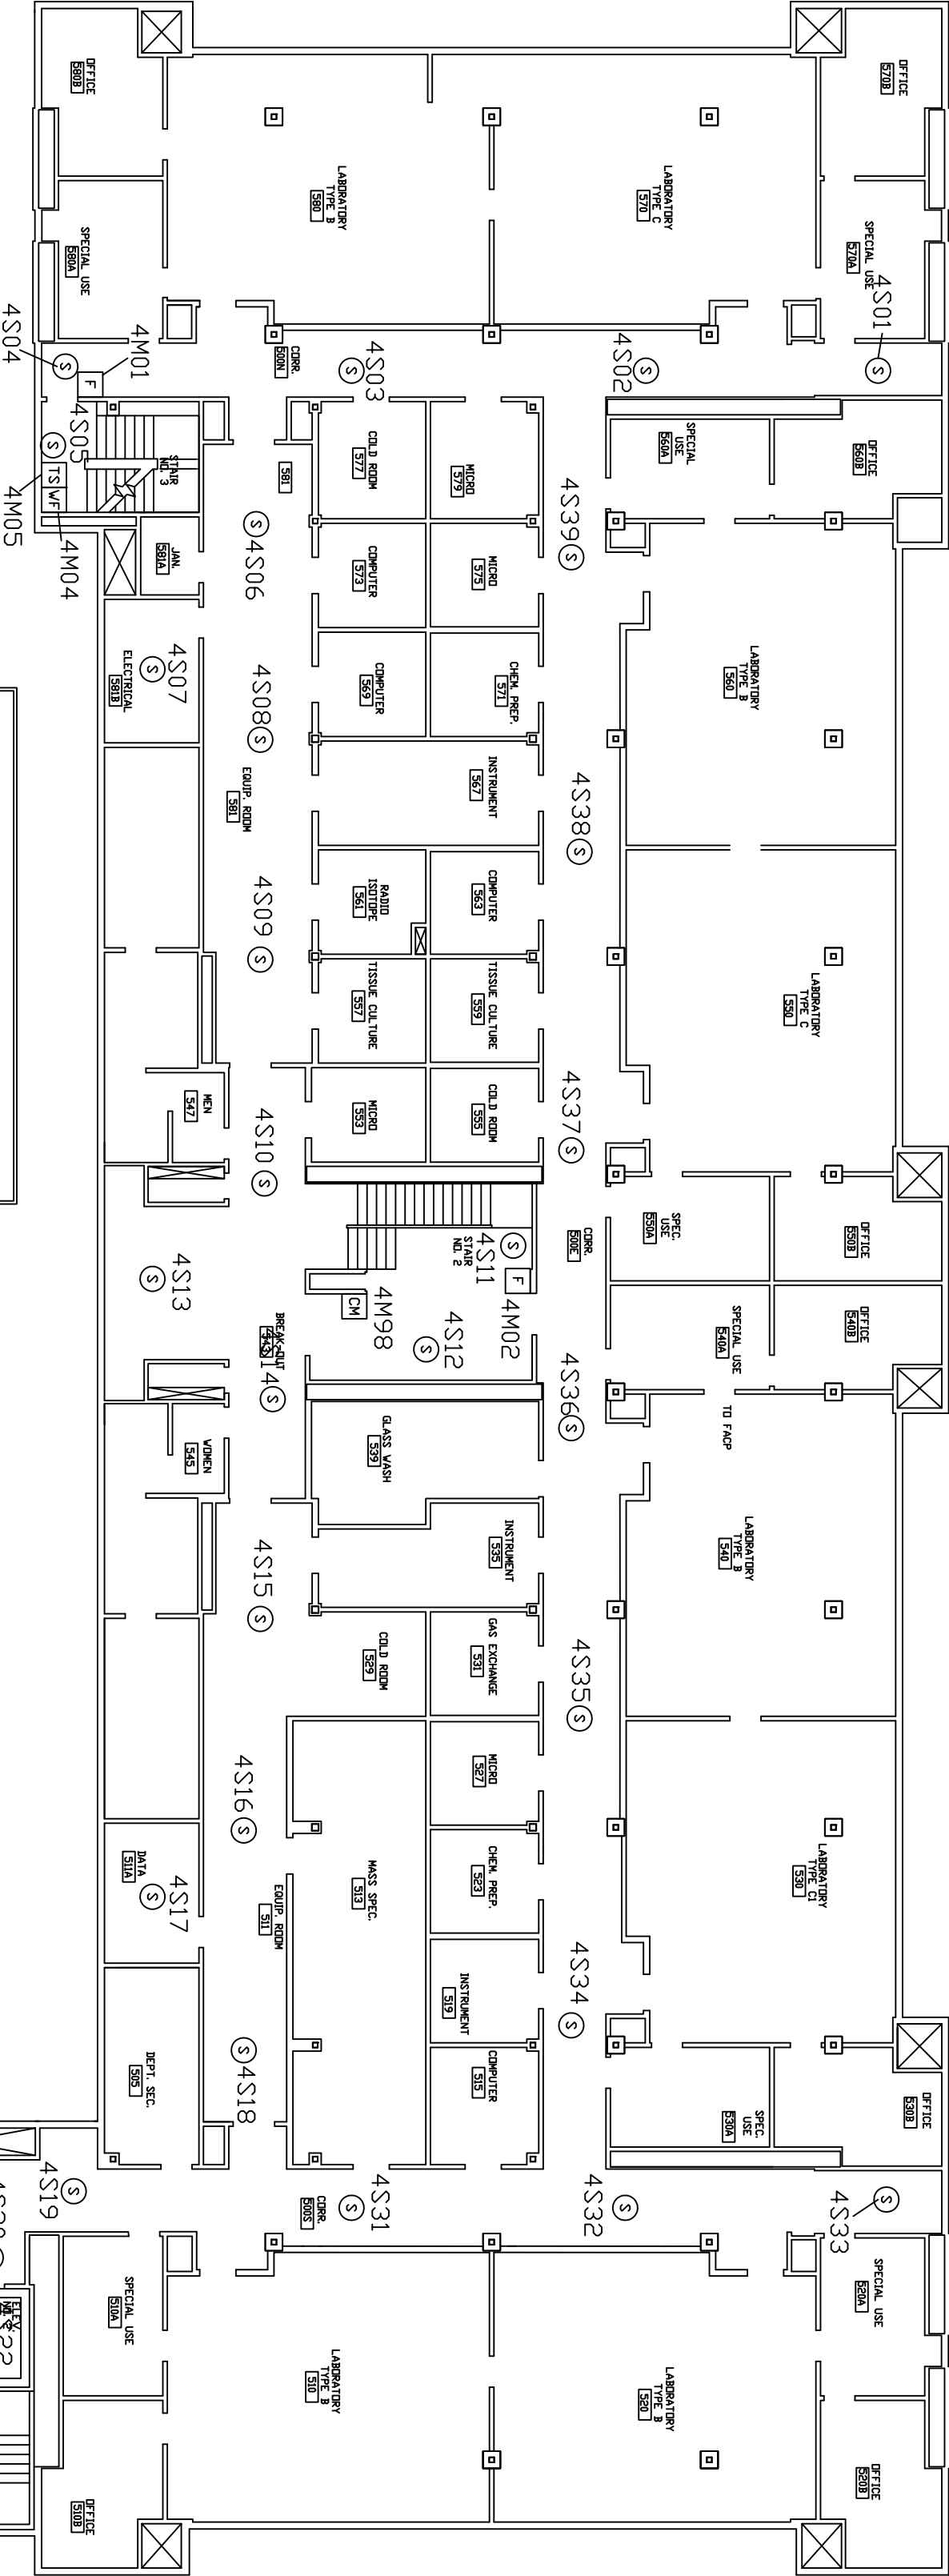

NFS
NELSON FIRE SYSTEMS
288-9905

LEGEND

- Ⓢ SMOKE DETECTOR
- Ⓣ HEAT DETECTOR
- Ⓜ MANUAL PULL STATION
- Ⓢ CONTROL MODULE
- Ⓢ WATERFLOW SWITCH
- Ⓢ TAMPER SWITCH

BIOLOGY RESEARCH BUILDING
UNIVERSITY OF UTAH
SALT LAKE CITY, UTAH
LEVEL 5

JUNE 8, 1998
U00BIDR5.DWG

