

NOTE:
NFS DRAWINGS ARE BASED ON THE PROJECT
ARCHITECT/ENGINEER (A/E) PLANS AND SPECIFICATIONS
FURNISHED TO NFS. A/E IS SOLELY RESPONSIBLE
(NOT NFS) FOR THE TYPE, SIZE, LOCATION, AND
SUITABILITY OF ALL FIRE ALARMS, CONTROL PANELS,
AND OTHER DEVICES SHOWN ON THE A/E PLANS.
NFS DRAWINGS ARE TO SHOW ONLY THE WIRING
DIAGRAMS BETWEEN FIRE ALARM DEVICES AND
CONTROL PANELS. NFS IS NOT RESPONSIBLE FOR
THE INFORMATION SHOWN ON THE A/E PLANS.


BIOLOGY BUILDING
BASEMENT
FIRE ALARM SYSTEM
UNIVERSITY OF UTAH
SALT LAKE CITY, UTAH

NFS
NELSON FIRE SYSTEMS
801-468-8300


DRAWN BY:	DS
DESIGNED BY:	XXXX
APPROVED BY:	XXXX
DATE:	10/5/2016
SCALE:	N.T.S.
PROJECT NO:	XXXX
REV NO:	XXXX
DRAWING NAME:	BIOLOGY BSMT.DWG

FIRE ALARM SYSTEM

PAGE:

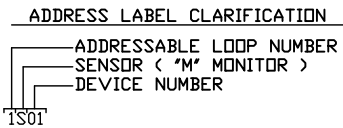


TS01

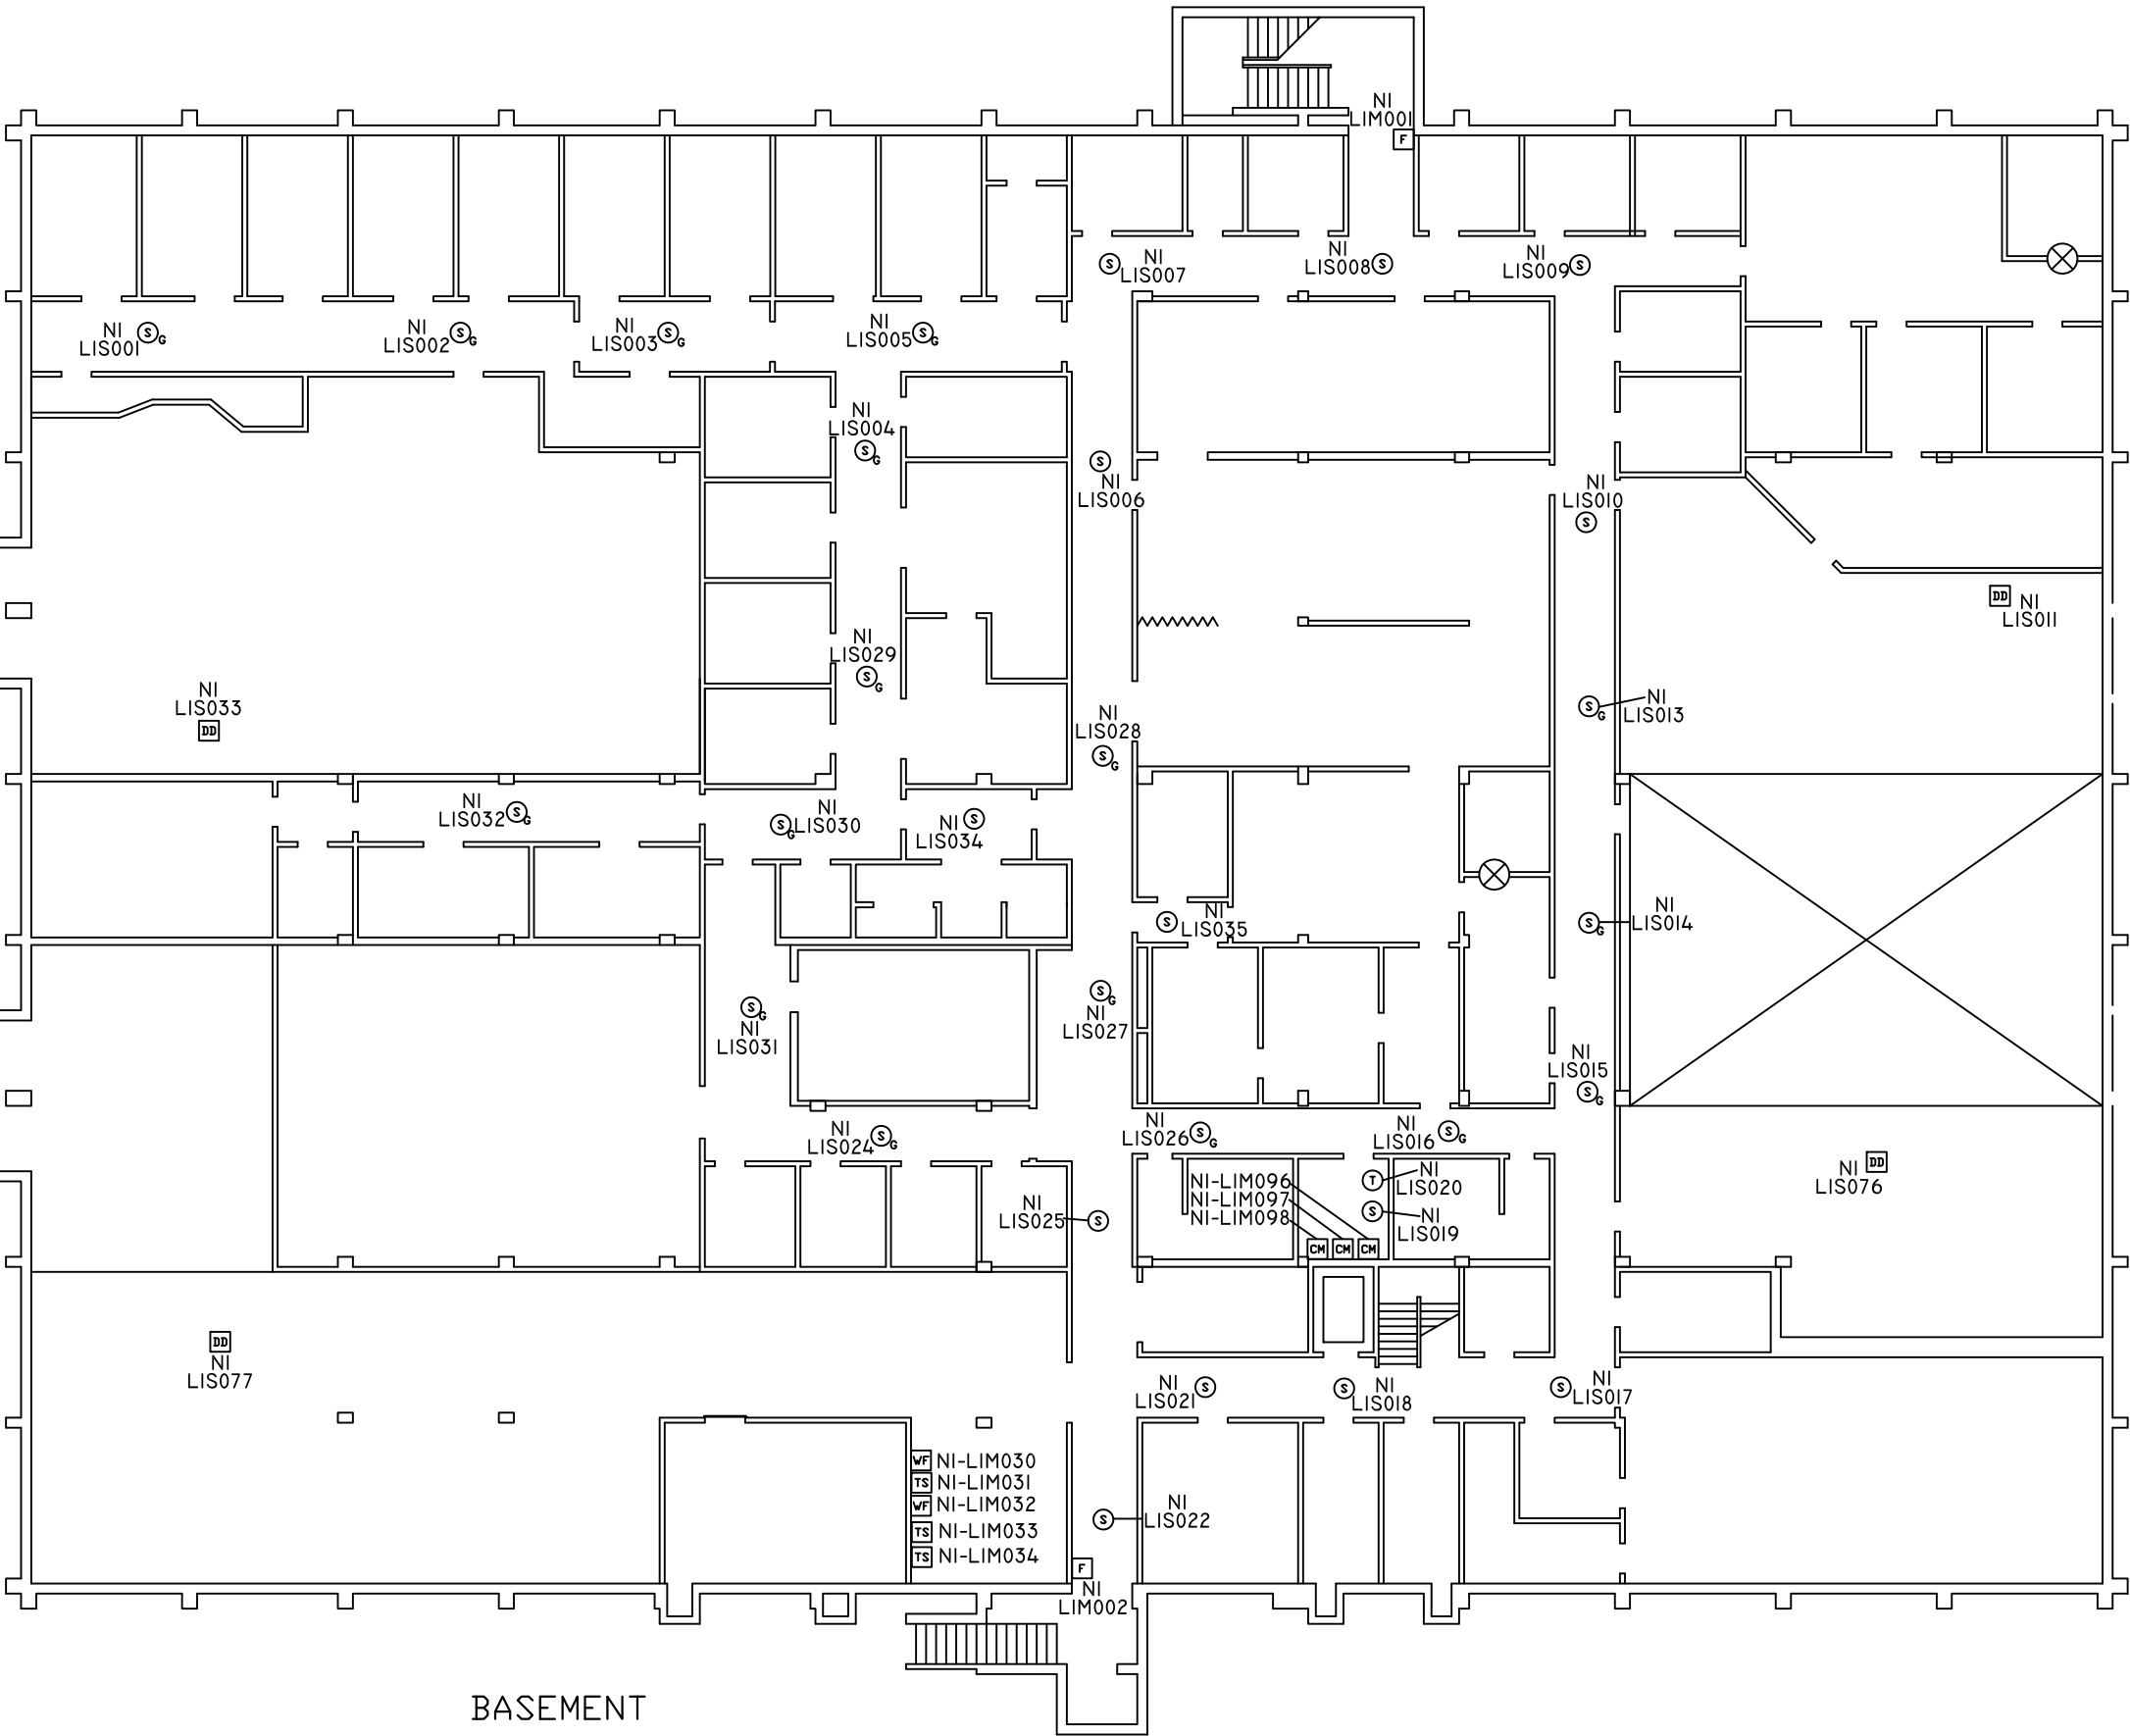

DEVICE LEGEND

SYMBOL	DESCRIPTION
Ⓢ	SMOKE DETECTOR W/BASE
Ⓣ	THERMAL DETECTOR
Ⓜ	MANUAL PULL STATION
Ⓜ	DUCT SMOKE DETECTOR
Ⓜ	WATERFLOW SWITCH MONITOR MODULE
Ⓜ	TAMPER SWITCH MONITOR MODULE
Ⓜ	MONITOR MODULE
Ⓜ	CONTROL MODULE
FACP	FIRE ALARM CONTROL PANEL
TRAN	TRANSPONDER PANEL

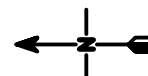

NOTE:
NFS DRAWINGS ARE BASED ON THE PROJECT
ARCHITECT/ENGINEER (A/E) PLANS AND SPECIFICATIONS
FURNISHED TO NFS. A/E IS SOLELY RESPONSIBLE
(NOT NFS) FOR THE TYPE, SIZE, LOCATION, AND
SUITABILITY OF ALL FIRE ALARMS, CONTROL PANELS,
AND OTHER DEVICES SHOWN ON THE A/E PLANS.
NFS DRAWINGS ARE TO SHOW ONLY THE WIRING
DIAGRAMS BETWEEN FIRE ALARM DEVICES AND
CONTROL PANELS. NFS IS NOT RESPONSIBLE FOR
THE INFORMATION SHOWN ON THE A/E PLANS.


BIOLOGY BUILDING
LEVEL 1
FIRE ALARM SYSTEM
UNIVERSITY OF UTAH
SALT LAKE CITY, UTAH

NFS
NELSON FIRE SYSTEMS
801-468-8300


DRAWN BY:	DB
DESIGNED BY:	XXXX
APPROVED BY:	XXXX
DATE:	10/5/2016
SCALE:	N.T.S.
PROJECT NO:	XXXX
REV NO:	XXXX
DRAWING NAME:	BIOLOGY 1ST.DWG

FIRE ALARM SYSTEM



PAGE:

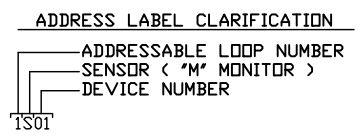

DEVICE LEGEND	
SYMBOL	DESCRIPTION
Ⓢ	SMOKE DETECTOR W/BASE
Ⓢ	THERMAL DETECTOR
F	MANUAL PULL STATION
DB	DUCT SMOKE DETECTOR
WF	WATERFLOW SWITCH MONITOR MODULE
TS	TAMPER SWITCH MONITOR MODULE
MM	MONITOR MODULE
CM	CONTROL MODULE
FACP	FIRE ALARM CONTROL PANEL
TRAN	TRANSPONDER PANEL

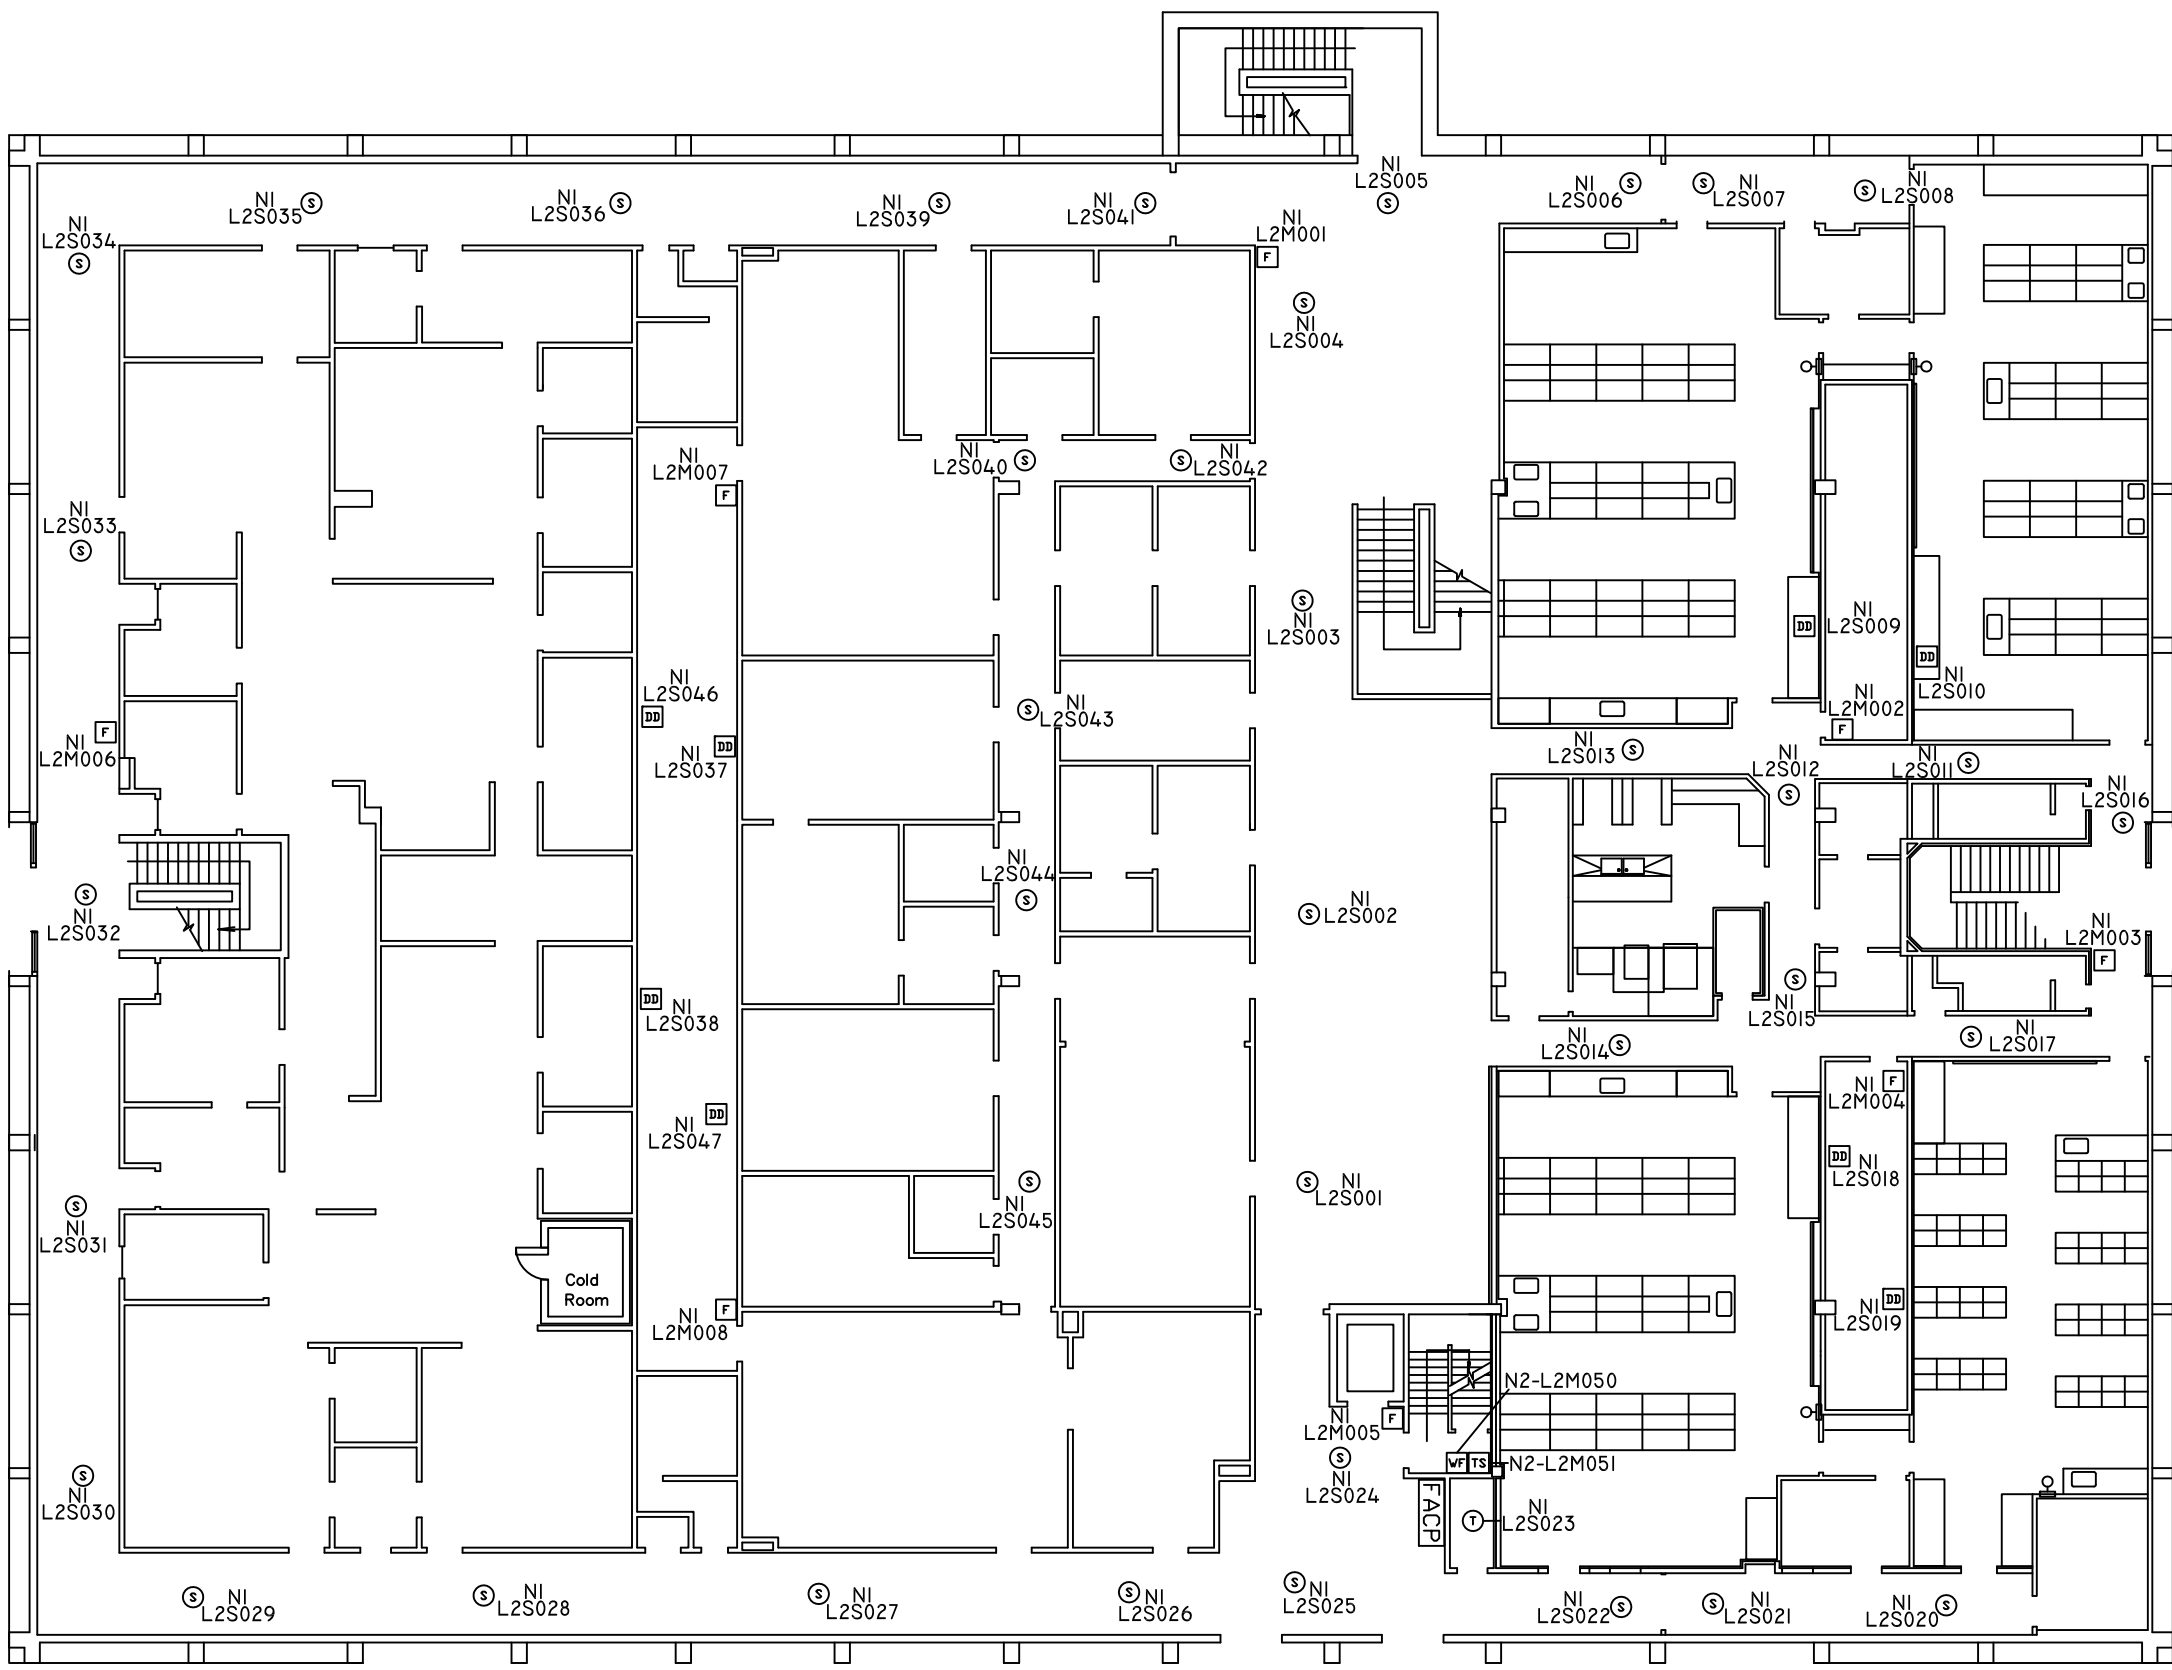

LEVEL 1

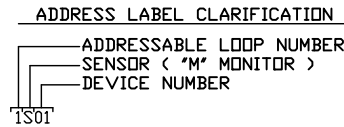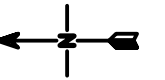

NOTE:
NFS DRAWINGS ARE BASED ON THE PROJECT
ARCHITECT/ENGINEER (A/E) PLANS AND SPECIFICATIONS
FURNISHED TO NFS. A/E IS SOLELY RESPONSIBLE
(NOT NFS) FOR THE TYPE, SIZE, LOCATION, AND
SUITABILITY OF ALL FIRE ALARMS, CONTROL PANELS,
AND OTHER DEVICES SHOWN ON THE A/E PLANS.
NFS DRAWINGS ARE TO SHOW ONLY THE WIRING
DIAGRAMS BETWEEN FIRE ALARM DEVICES AND
CONTROL PANELS. NFS IS NOT RESPONSIBLE FOR
THE INFORMATION SHOWN ON THE A/E PLANS.


BIOLOGY BUILDING
LEVEL 2
FIRE ALARM SYSTEM
UNIVERSITY OF UTAH
SALT LAKE CITY, UTAH

NFS
NELSON FIRE SYSTEMS
801-468-8300

DRAWN BY:	DS
DESIGNED BY:	XXXX
APPROVED BY:	XXXX
DATE:	10/5/2016
SCALE:	N.T.S.
PROJECT NO:	XXXX
REV NO:	XXXX
DRAWING NAME:	BIOLOGY 2ND.DWG



FIRE ALARM SYSTEM

PAGE:

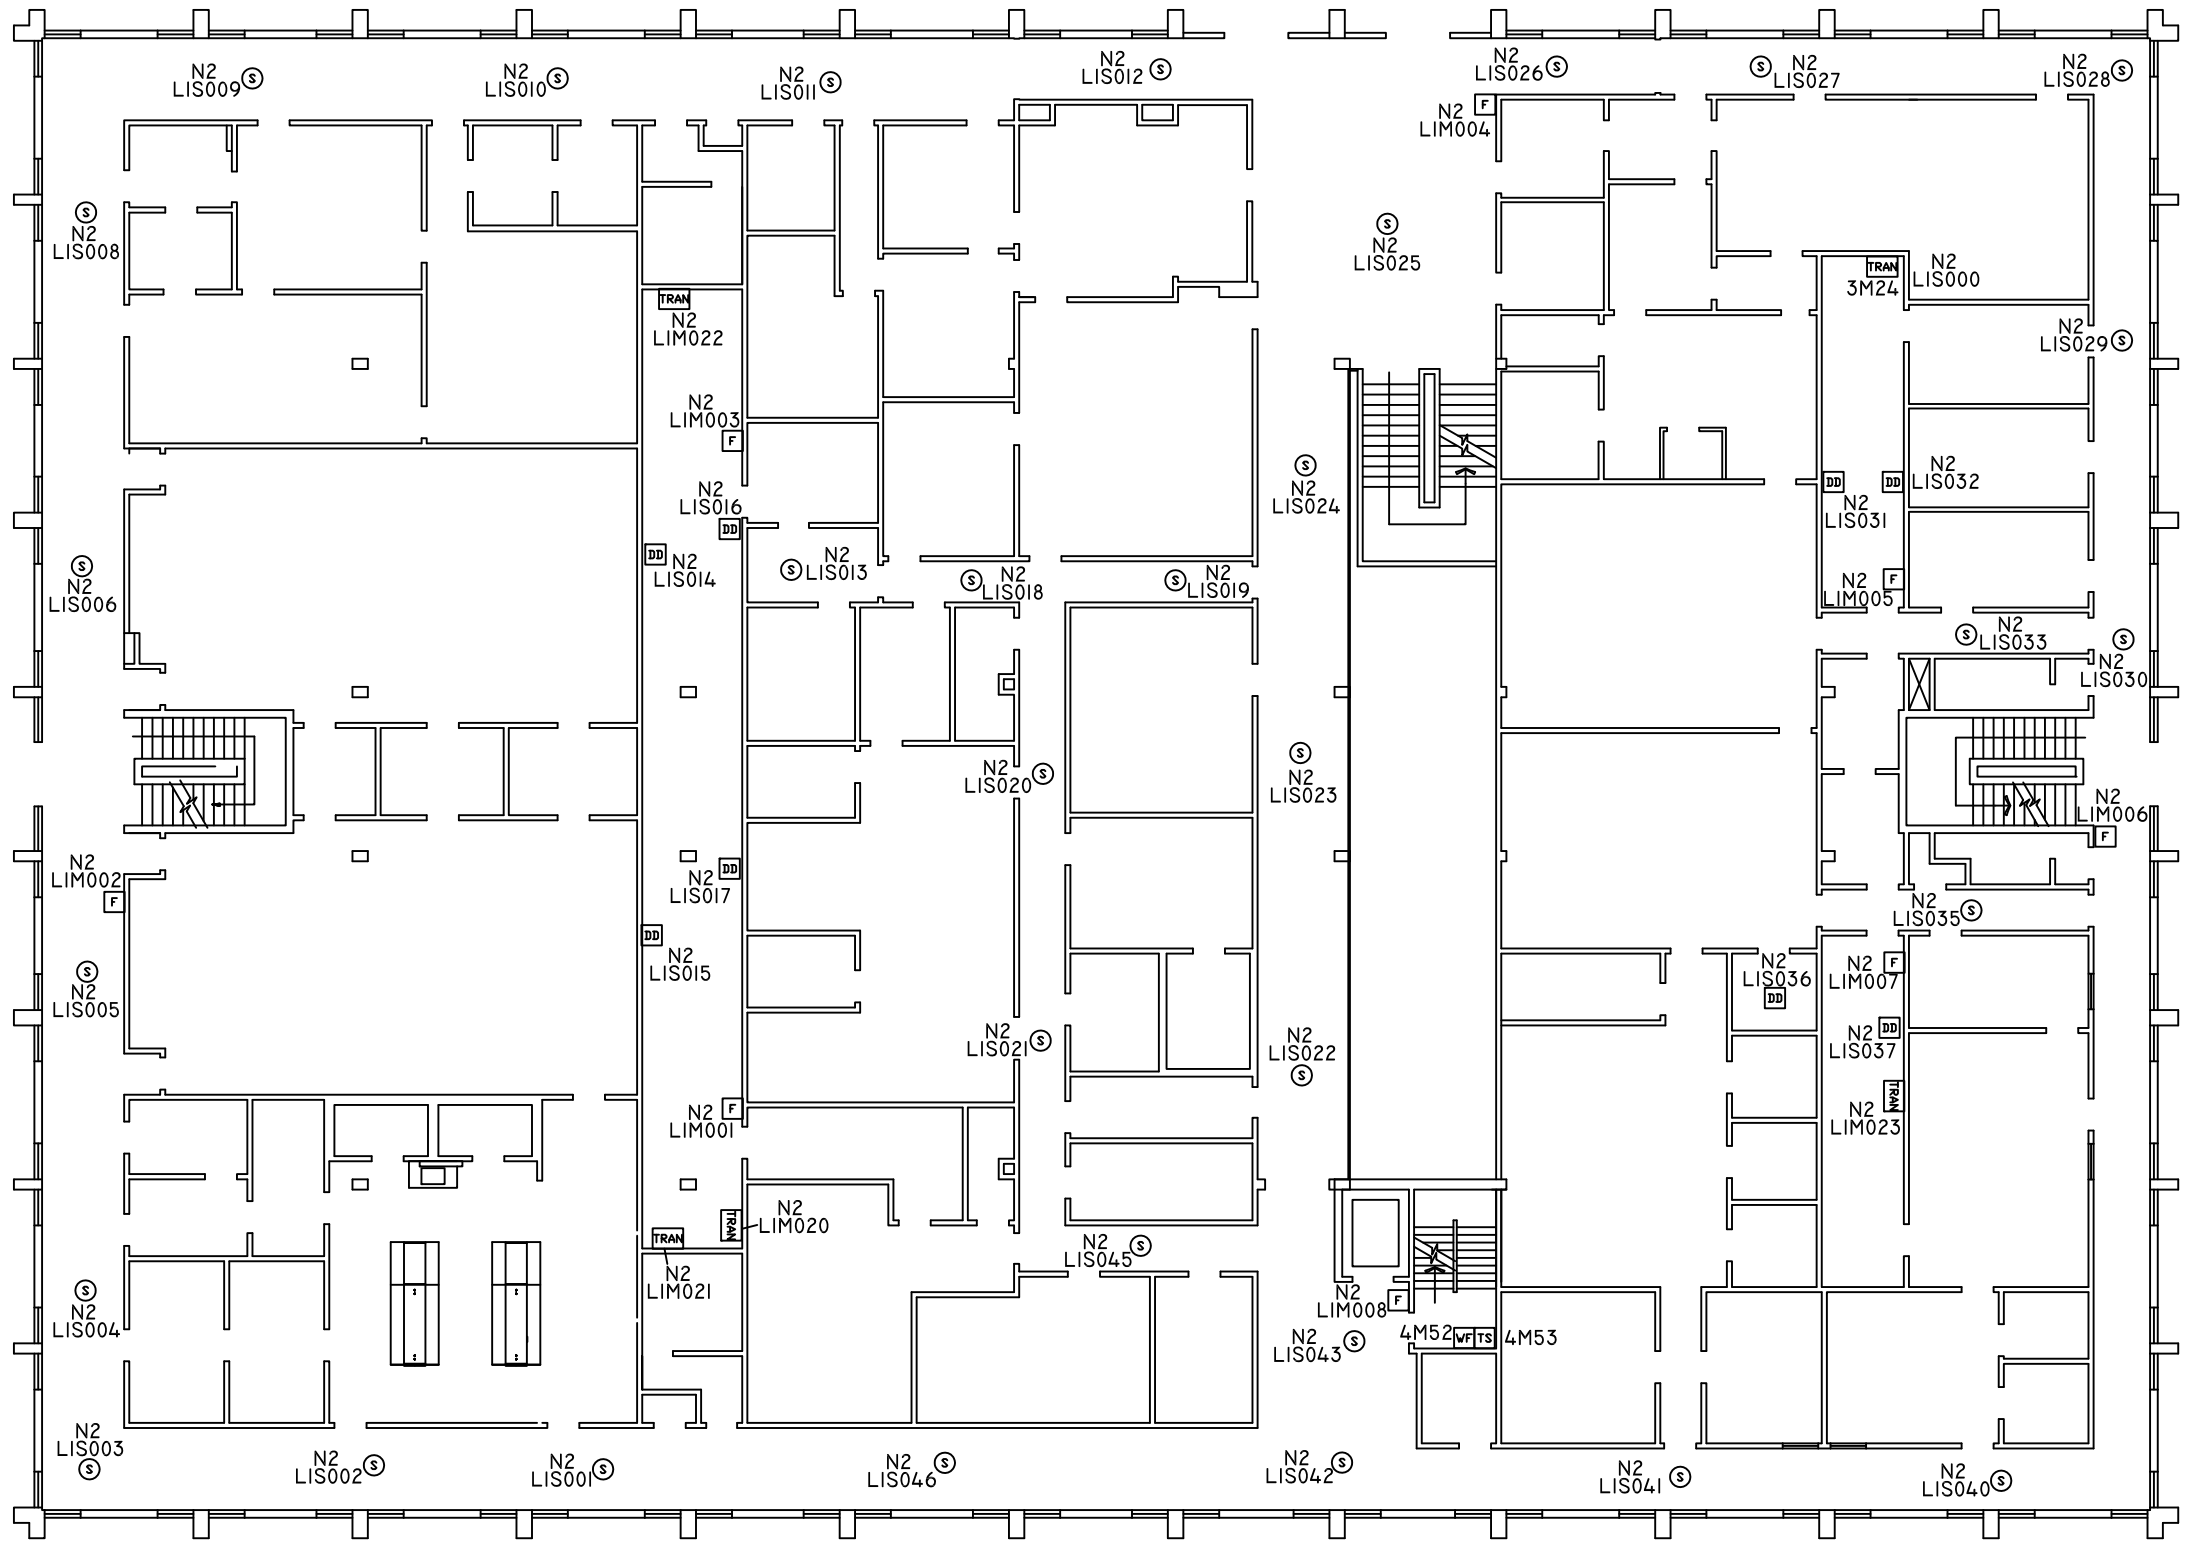

LEVEL 2

DEVICE LEGEND	
SYMBOL	DESCRIPTION
S	SMOKE DETECTOR W/BASE
T	THERMAL DETECTOR
F	MANUAL PULL STATION
DS	DUCT SMOKE DETECTOR
M	WATERFLOW SWITCH MONITOR MODULE
TS	TAMPER SWITCH MONITOR MODULE
M	MONITOR MODULE
C	CONTROL MODULE
FACP	FIRE ALARM CONTROL PANEL
TRAN	TRANSPONDER PANEL

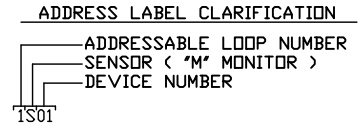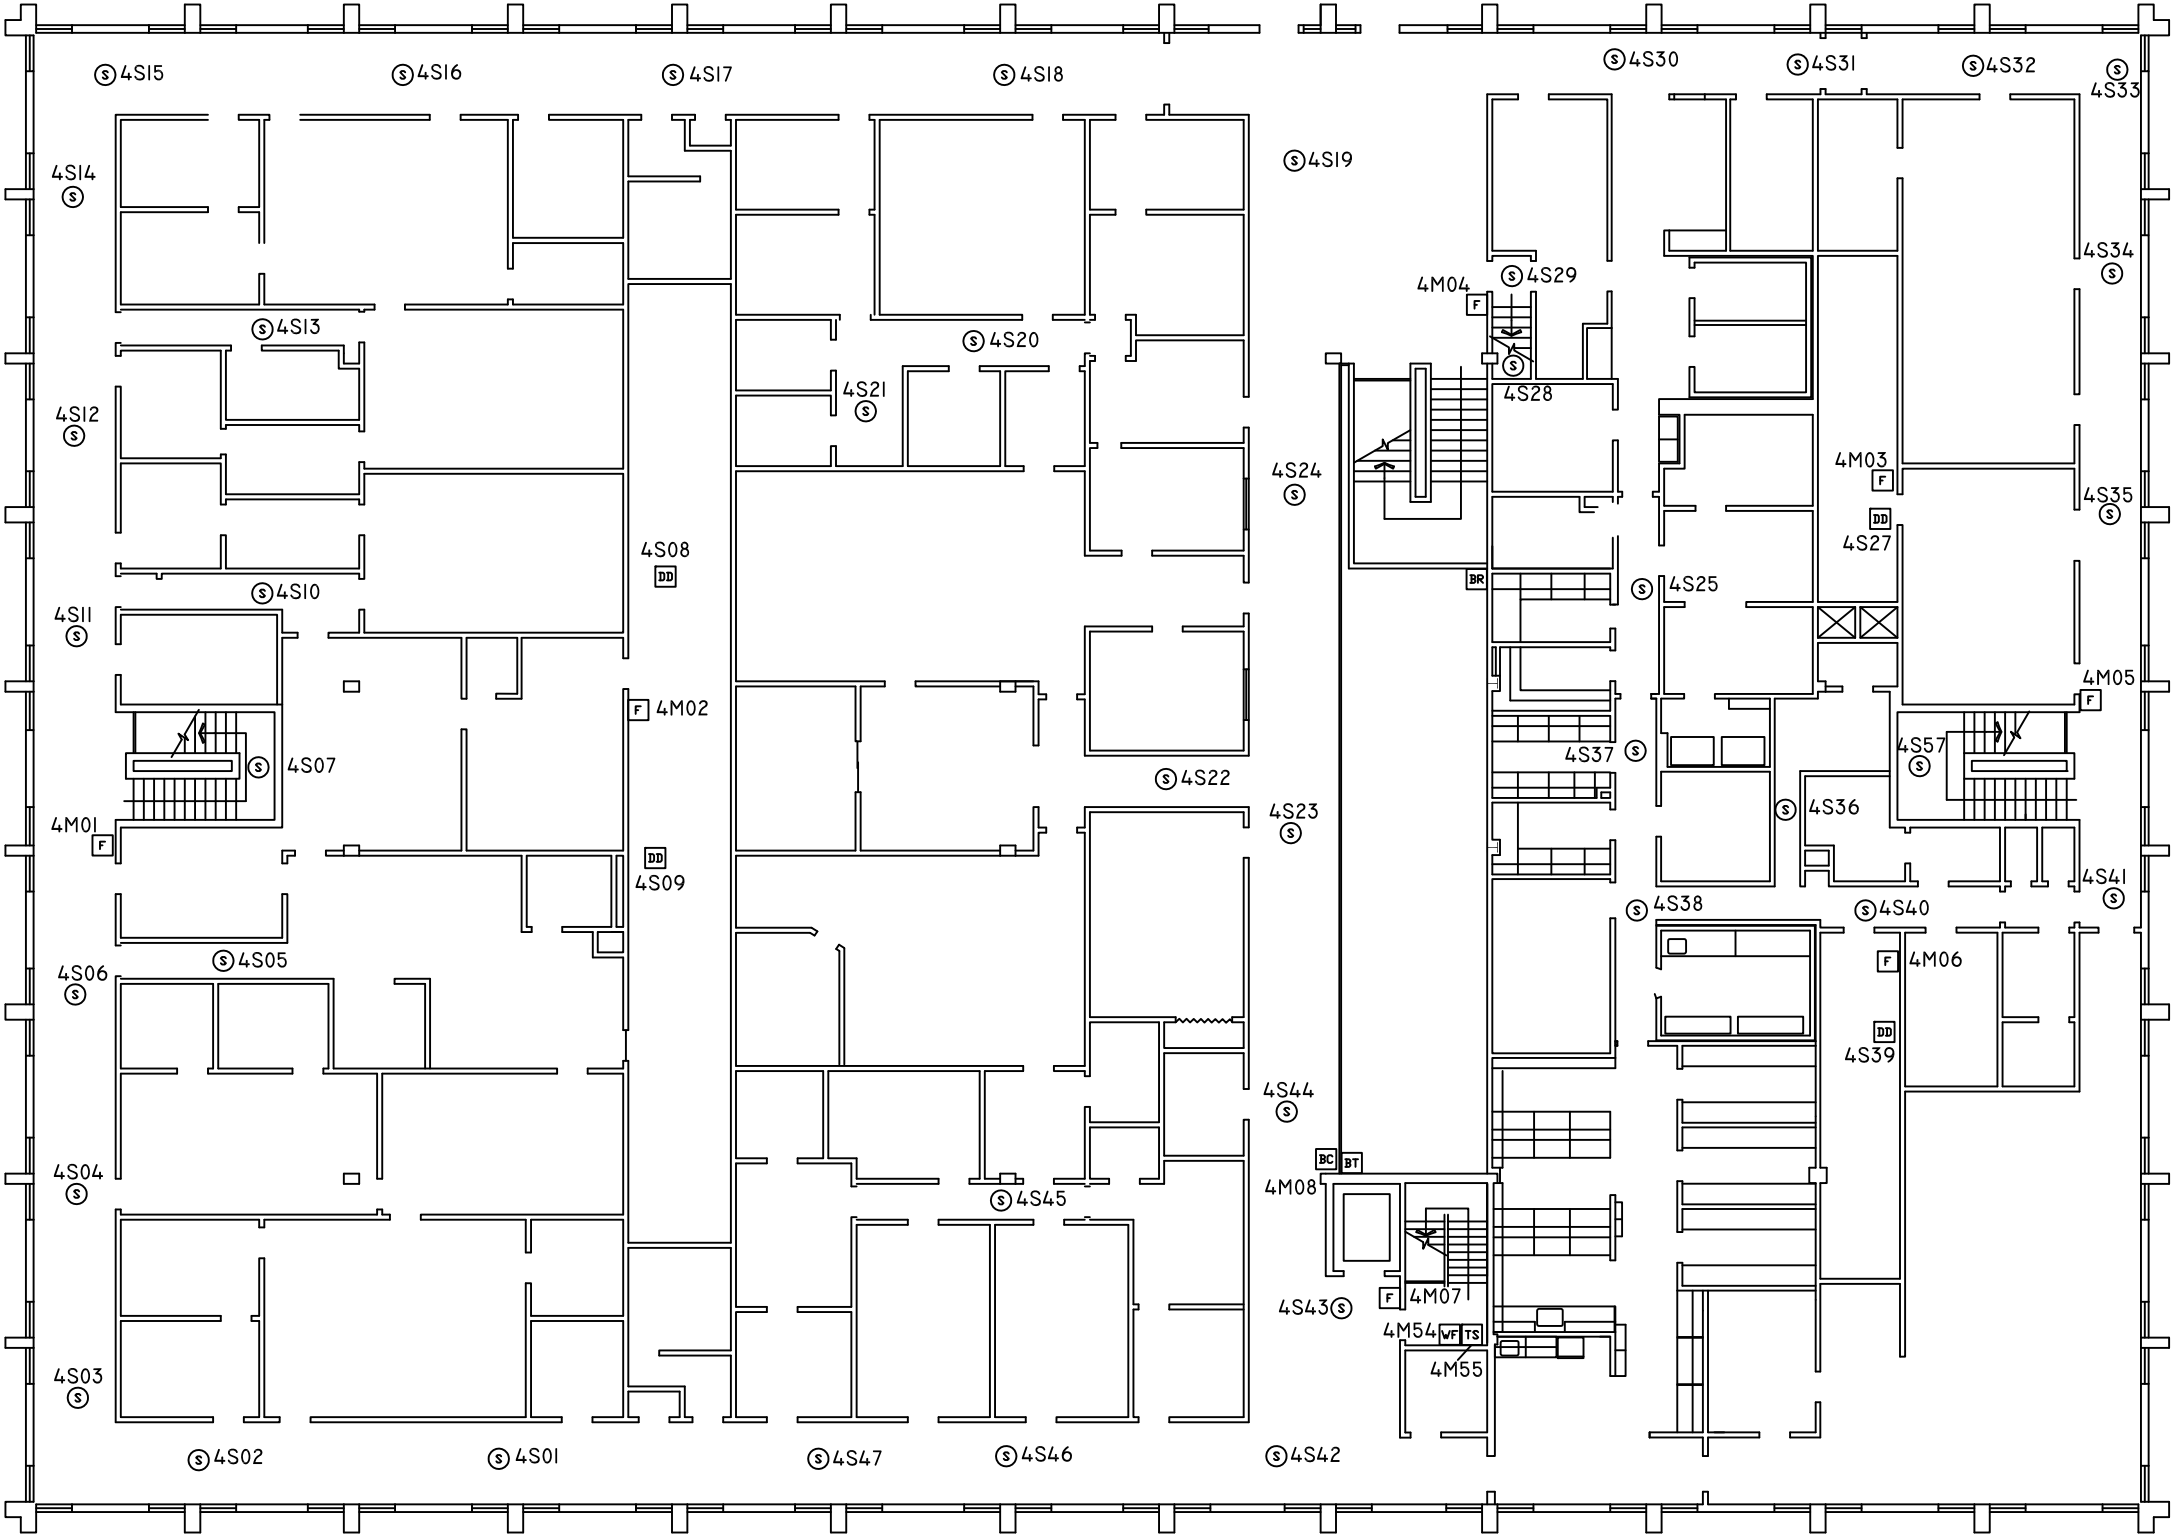

NOTE:
NFS DRAWINGS ARE BASED ON THE PROJECT
ARCHITECT/ENGINEER (A/E) PLANS AND SPECIFICATIONS
FURNISHED TO NFS. A/E IS SOLELY RESPONSIBLE
(NOT NFS) FOR THE TYPE, SIZE, LOCATION, AND
SUITABILITY OF ALL FIRE ALARMS, CONTROL PANELS,
AND OTHER DEVICES SHOWN ON THE A/E PLANS.
NFS DRAWINGS ARE TO SHOW ONLY THE WIRING
DIAGRAMS BETWEEN FIRE ALARM DEVICES AND
CONTROL PANELS. NFS IS NOT RESPONSIBLE FOR
THE INFORMATION SHOWN ON THE A/E PLANS.

BIOLOGY BUILDING
LEVEL 3
FIRE ALARM SYSTEM
UNIVERSITY OF UTAH
SALT LAKE CITY, UTAH

NFS
NELSON FIRE SYSTEMS
801-468-8300


DRAWN BY:	DB
DESIGNED BY:	XXXX
APPROVED BY:	XXXX
DATE:	5/4/2005
SCALE:	N.T.S.
PROJECT NO:	XXXX
REV NO:	XXXX
DRAWING NAME:	BIOLOGY 3RD.DWG

FIRE ALARM SYSTEM

PAGE:

DEVICE LEGEND	
SYMBOL	DESCRIPTION
Ⓢ	SMOKE DETECTOR W/BASE
Ⓣ	THERMAL DETECTOR
F	MANUAL PULL STATION
BD	DUCT SMOKE DETECTOR
WFS	WATERFLOW SWITCH MONITOR MODULE
TS	TAMPER SWITCH MONITOR MODULE
MM	MONITOR MODULE
CM	CONTROL MODULE
FACP	FIRE ALARM CONTROL PANEL
TRAN	TRANSPONDER PANEL

LEVEL 3

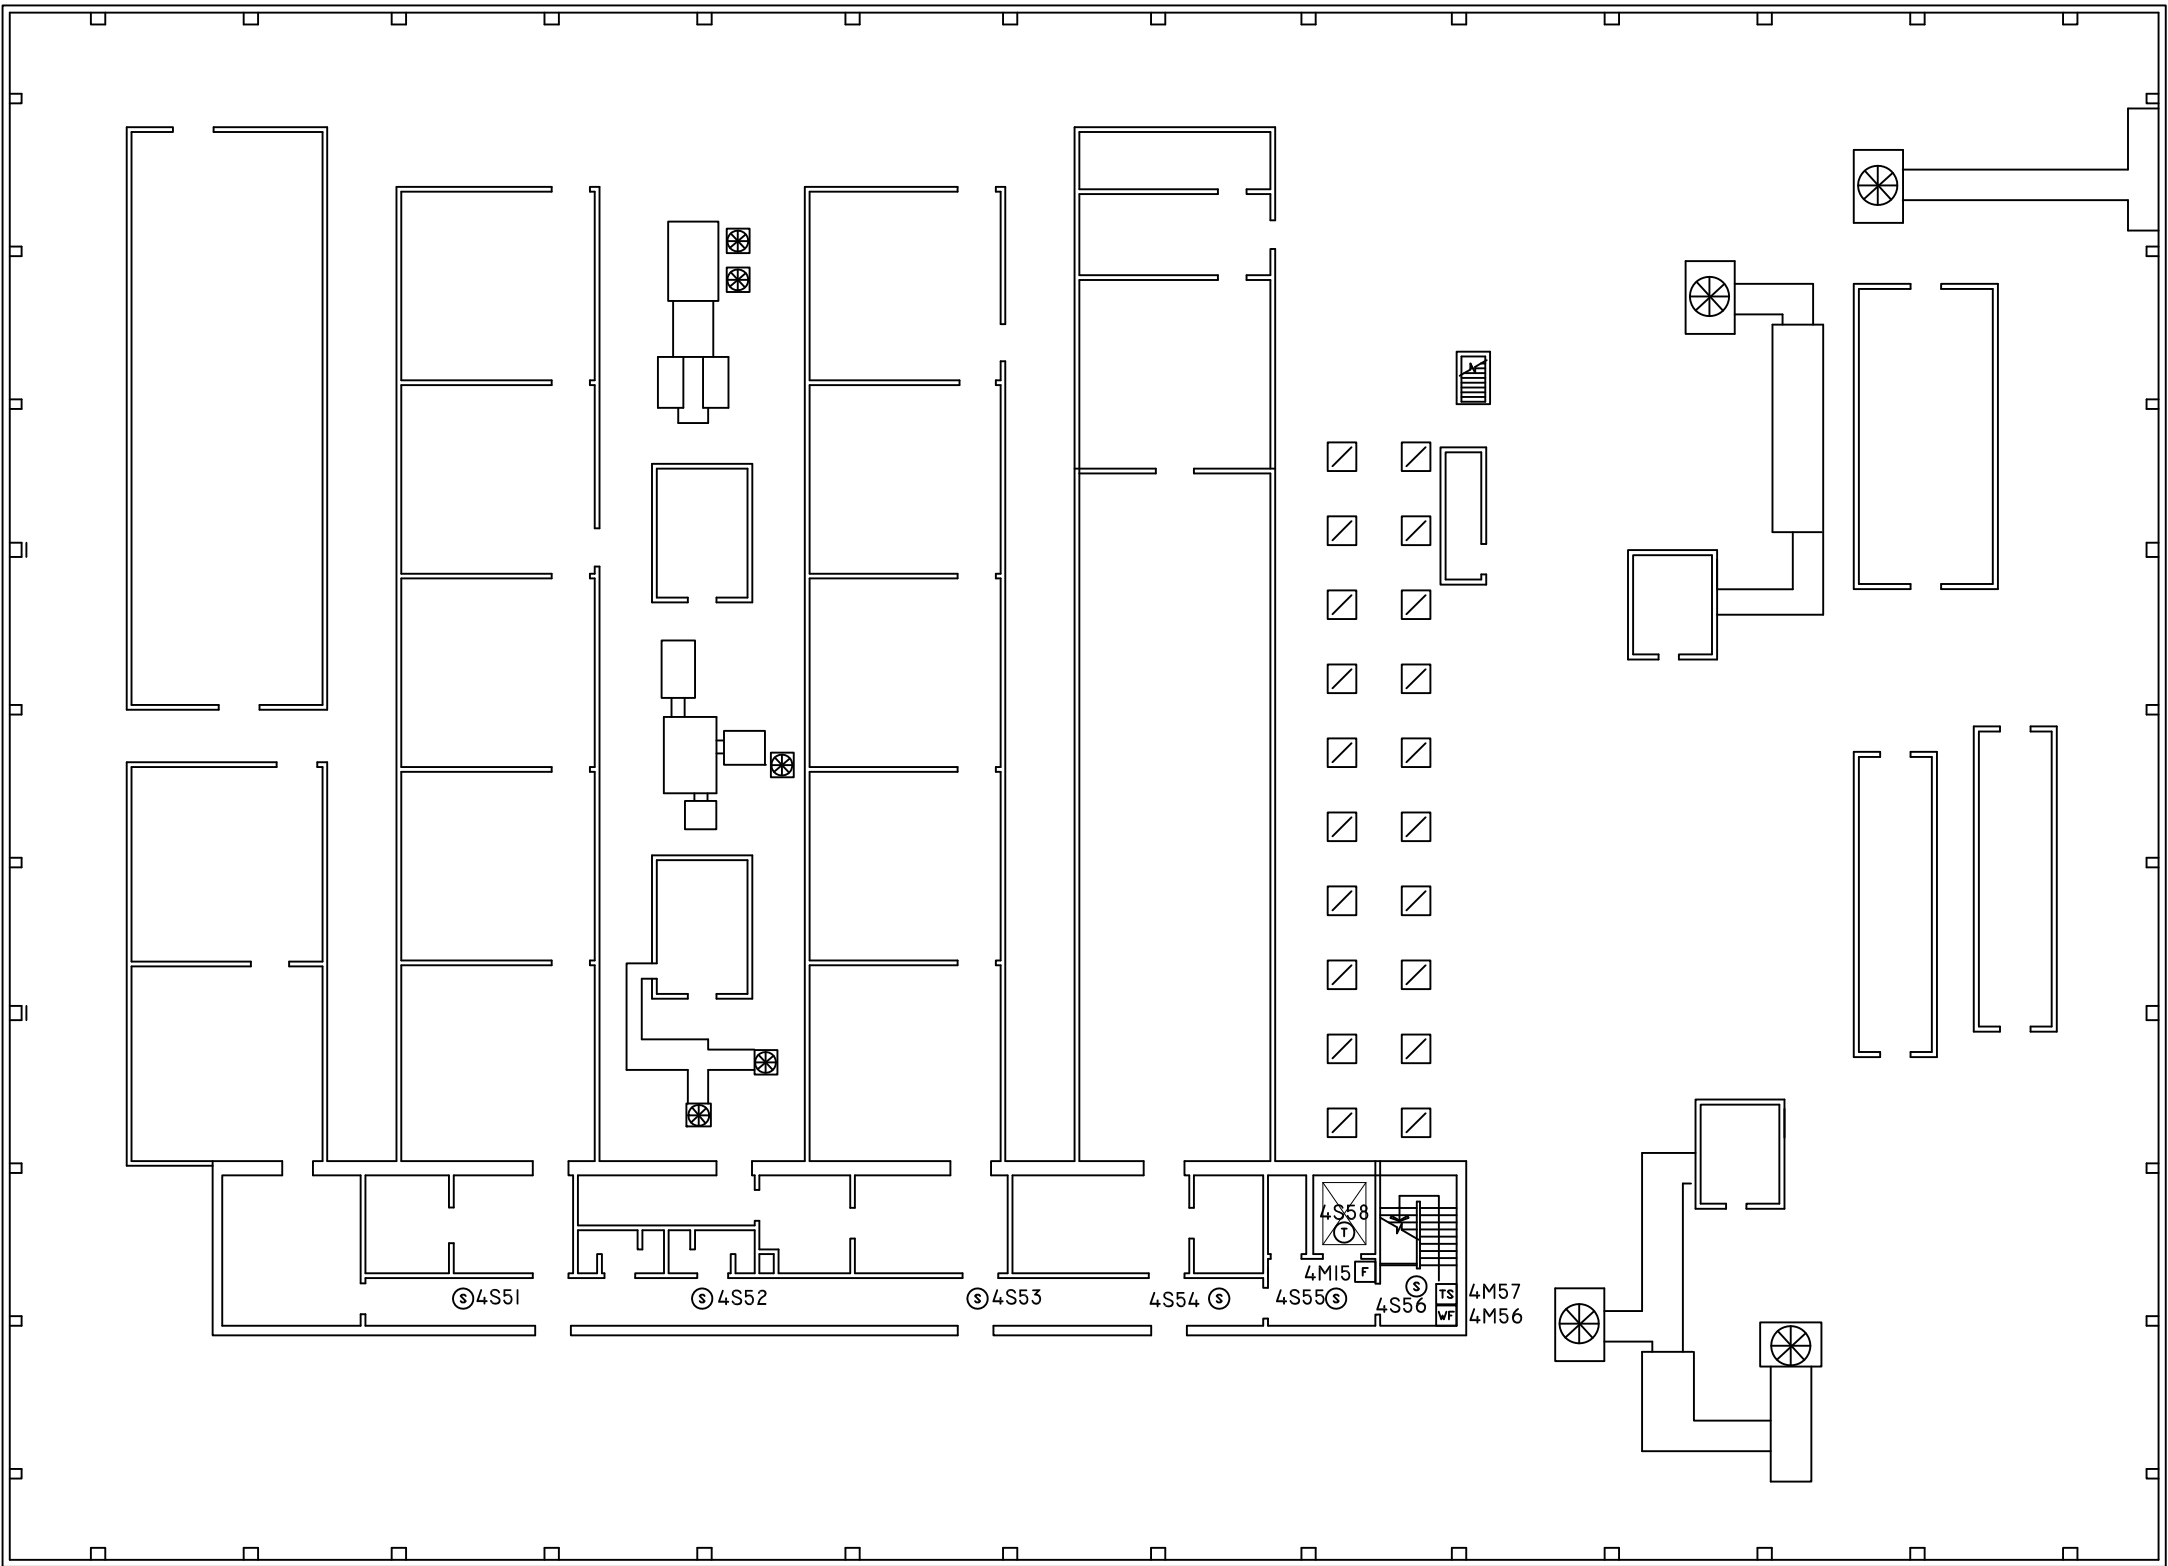


LEVEL 4

ADDRESS LABEL CLARIFICATION

ADDRESSABLE LOOP NUMBER
SENSOR ("M" MONITOR)
DEVICE NUMBER

1S01

DEVICE LEGEND	
SYMBOL	DESCRIPTION
Ⓢ	SMOKE DETECTOR W/BASE
Ⓣ	THERMAL DETECTOR
ⓕ	MANUAL PULL STATION
Ⓛ	DUCT SMOKE DETECTOR
Ⓦ	WATERFLOW SWITCH MONITOR MODULE
Ⓣ	TAMPER SWITCH MONITOR MODULE
Ⓢ	MONITOR MODULE
Ⓢ	CONTROL MODULE
Ⓢ	FIRE ALARM CONTROL PANEL
Ⓢ	TRANSPONDER PANEL

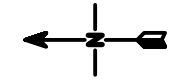

NOTE:
NFS DRAWINGS ARE BASED ON THE PROJECT
ARCHITECT/ENGINEER (A/E) PLANS AND SPECIFICATIONS
FURNISHED TO NFS. A/E IS SOLELY RESPONSIBLE
(NOT NFS) FOR THE TYPE, SIZE, LOCATION, AND
SUITABILITY OF ALL FIRE ALARMS, CONTROL PANELS,
AND OTHER DEVICES SHOWN ON THE A/E PLANS.
NFS DRAWINGS ARE TO SHOW ONLY THE WIRING
DIAGRAMS BETWEEN FIRE ALARM DEVICES AND
CONTROL PANELS. NFS IS NOT RESPONSIBLE FOR
THE INFORMATION SHOWN ON THE A/E PLANS.

BIOLOGY BUILDING
LEVEL 4
FIRE ALARM SYSTEM
UNIVERSITY OF UTAH
SALT LAKE CITY, UTAH

NFS
NELSON FIRE SYSTEMS
801-468-8300

DRAWN BY:	DS
DESIGNED BY:	XXXX
APPROVED BY:	XXXX
DATE:	5/4/2005
SCALE:	N.T.S.
PROJECT NO:	XXXX
REV NO:	XXXX
DRAWING NAME:	BIOLOGY 4TH.DWG

FIRE ALARM SYSTEM

PAGE: