


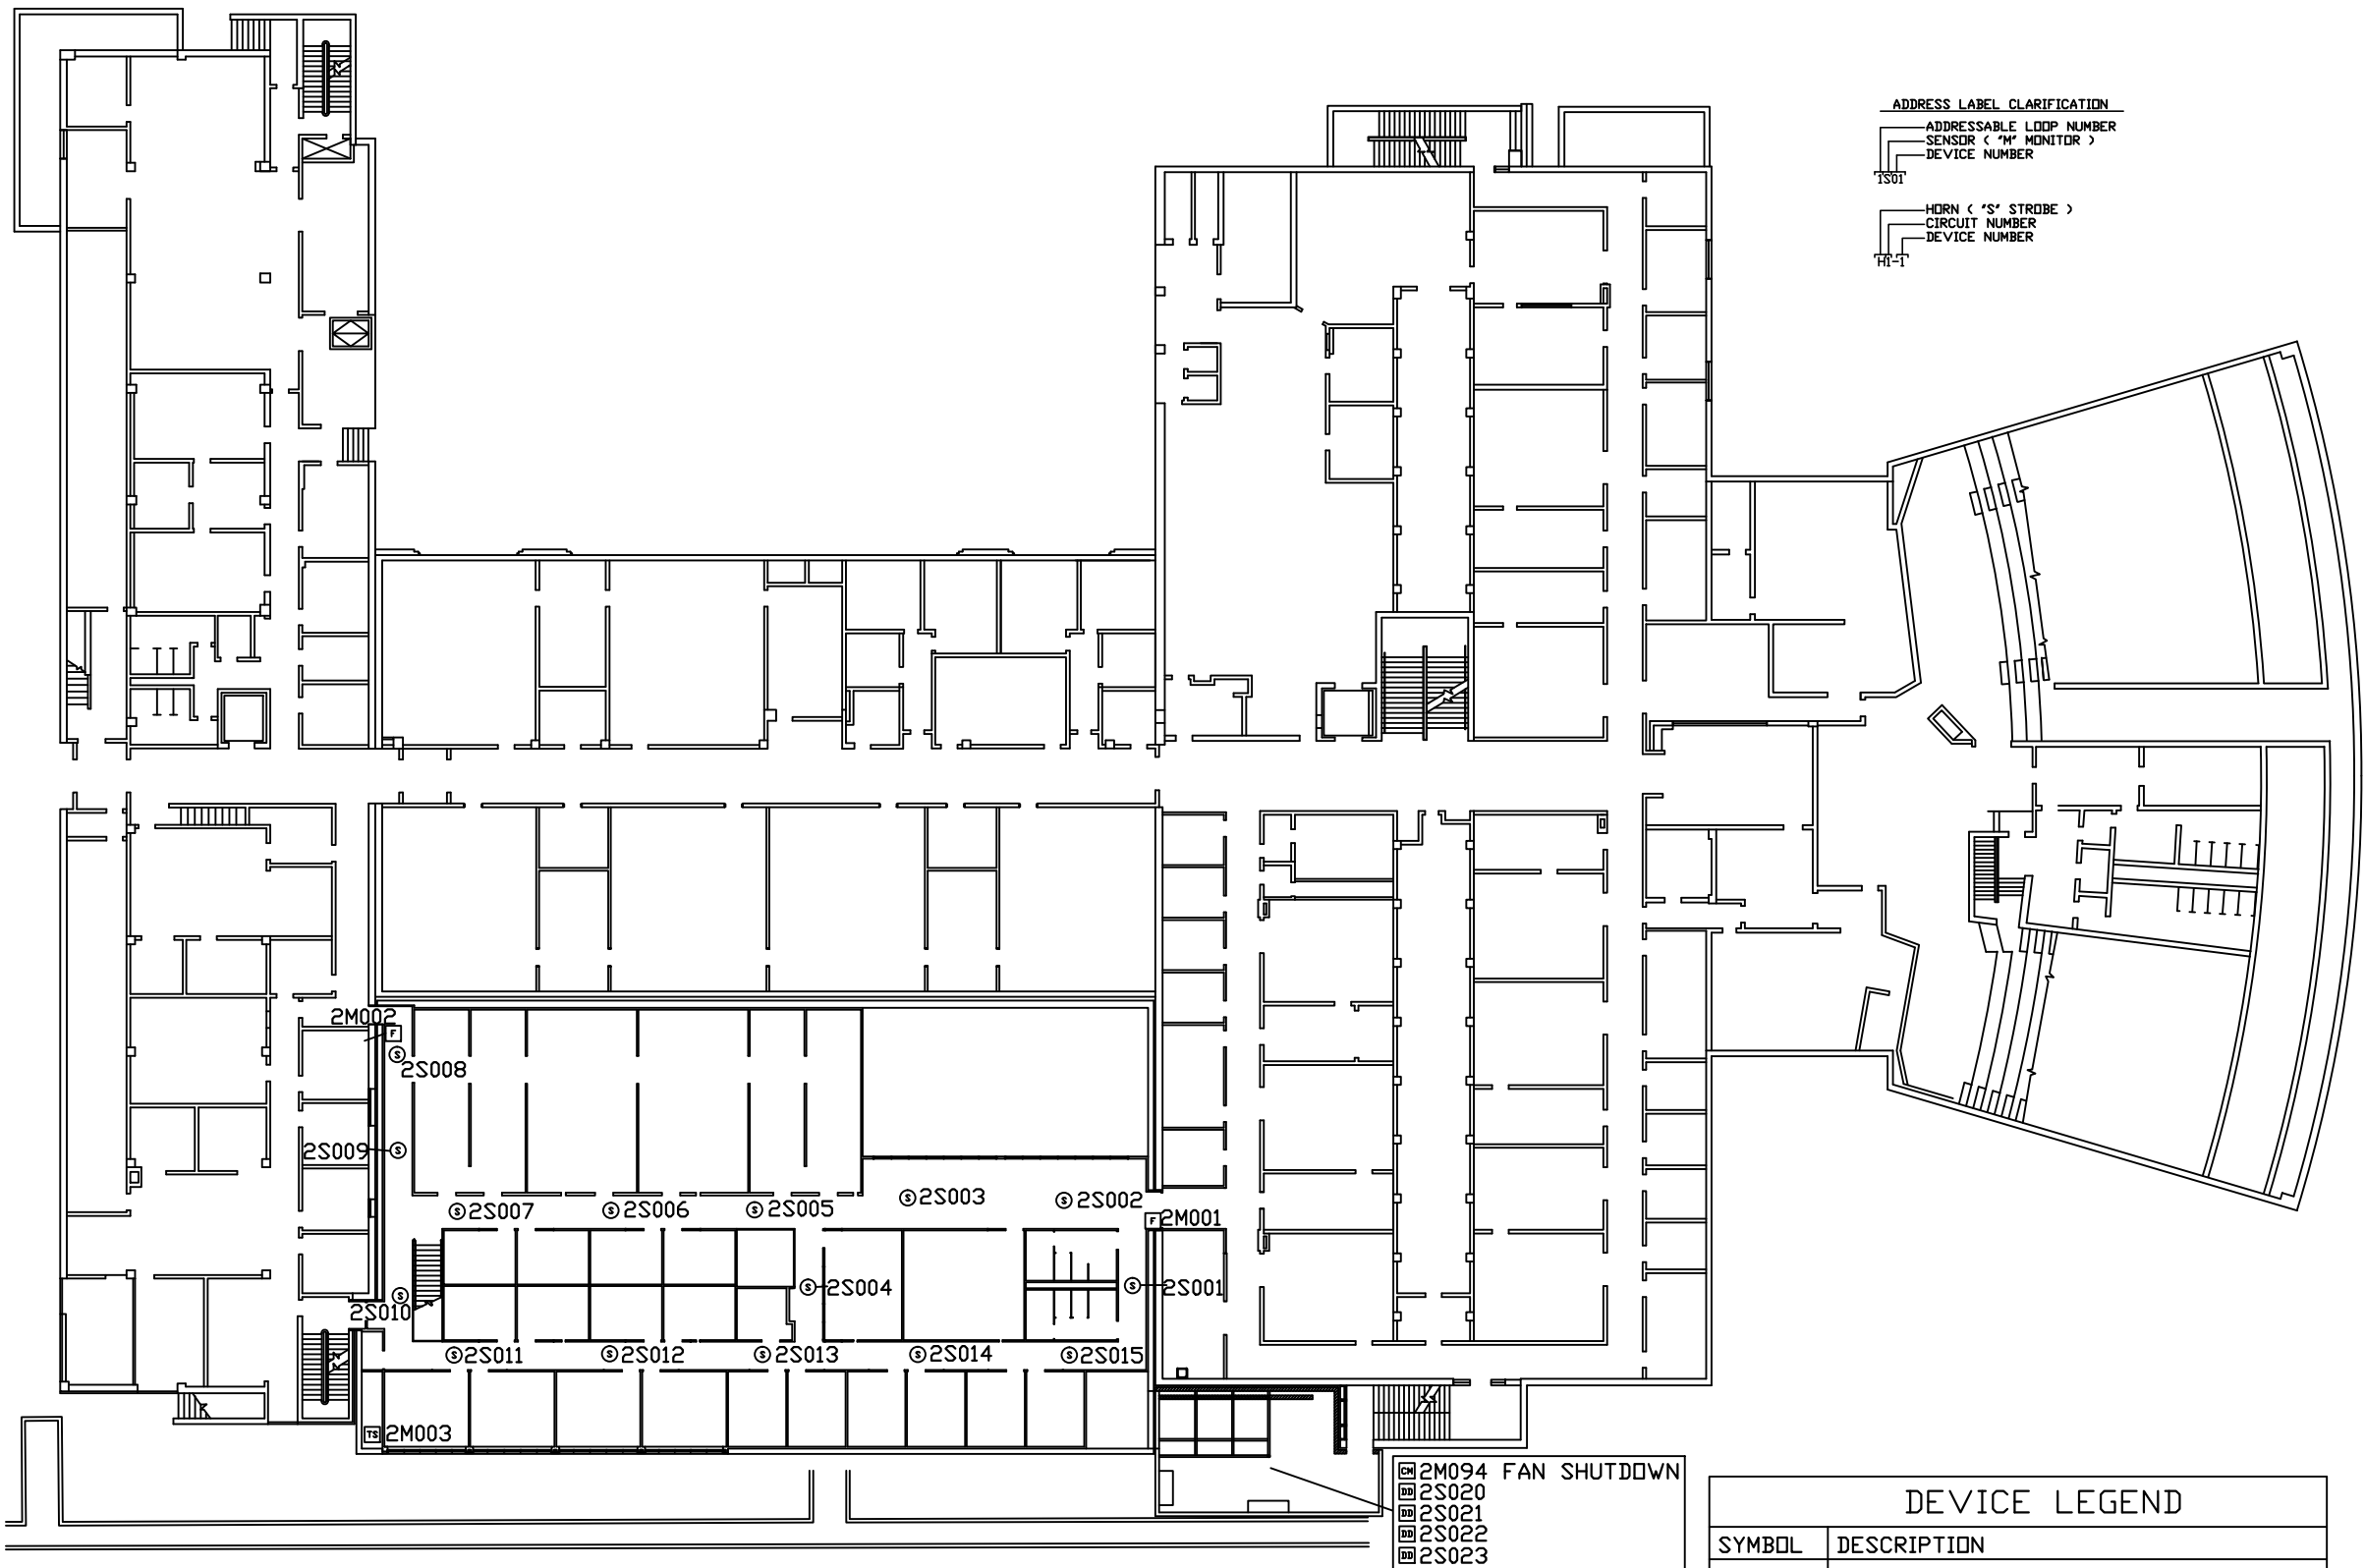


ADDRESS LABEL CLARIFICATION

ADDRESSABLE LOOP NUMBER
SENSOR ("M" MONITOR)
DEVICE NUMBER

HORN ("S" STROBE)
CIRCUIT NUMBER
DEVICE NUMBER

DEVICE LEGEND	
SYMBOL	DESCRIPTION
⊙	SMOKE DETECTOR
⌂	MANUAL PULL STATION
⌂	WATERFLOW SWITCH MONITOR MODULE
⌂	TAMPER SWITCH MONITOR MODULE
⌂	HORN/STROBE
⌂	WEATHERPROOF HORN
⌂	MONITOR MODULE
⌂	CONTROL MODULE
⌂	FIRE ALARM CONTROL PANEL
⌂	TRANSPONDER PANEL

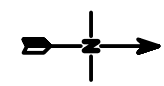

NOTE:
NFS DRAWINGS ARE BASED ON THE PROJECT
ARCHITECT/ENGINEER (A/E) PLANS AND SPECIFICATIONS
FURNISHED TO NFS. A/E IS SOLELY RESPONSIBLE
(NOT NFS) FOR THE TYPE, SIZE, LOCATION, AND
SUITABILITY OF ALL FIRE ALARMS, CONTROL PANELS,
AND OTHER DEVICES SHOWN ON THE A/E PLANS.
NFS DRAWINGS ARE TO SHOW ONLY THE WIRING
DIAGRAMS BETWEEN FIRE ALARM DEVICES AND
CONTROL PANELS. NFS IS NOT RESPONSIBLE FOR
THE INFORMATION SHOWN ON THE A/E PLANS.

HENRY EYRING BUILDING
GAUSS HAUS
UNIVERSITY OF UTAH
LAB LEVEL
FIRE ALARM SYSTEM



NFS
NELSON FIRE SYSTEMS
801-468-8300

DRAWN BY:	DS
DESIGNED BY:	JGA
APPROVED BY:	TCT
DATE:	8/7/2006
SCALE:	N.T.S.
PROJECT NO:	0085-II621
REV NO:	I
DRAWING NAME:	GAUSS HAUS 2.DWG

FIRE ALARM SYSTEM
LAB LEVEL
ADDRESSABLE NUMBERS

NFS
FA-L-01

DEVICE LEGEND	
SYMBOL	DESCRIPTION
⊙	SMOKE DETECTOR
F	MANUAL PULL STATION
WF	WATERFLOW SWITCH MONITOR MODULE
TS	TAMPER SWITCH MONITOR MODULE
HS	HORN/STROBE
H	WEATHERPROOF HORN
MM	MONITOR MODULE
CM	CONTROL MODULE
FACP	FIRE ALARM CONTROL PANEL
TRAN	TRANSPONDER PANEL
VSDA	VESDA PANEL (SUPPLIED BY OTHERS)
LA	LOW AIR SWITCH
PS	PRESSURE SWITCH
SL	PRE ACTION SOLENOID
MT	MULTI-TONE HORN STROBE

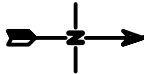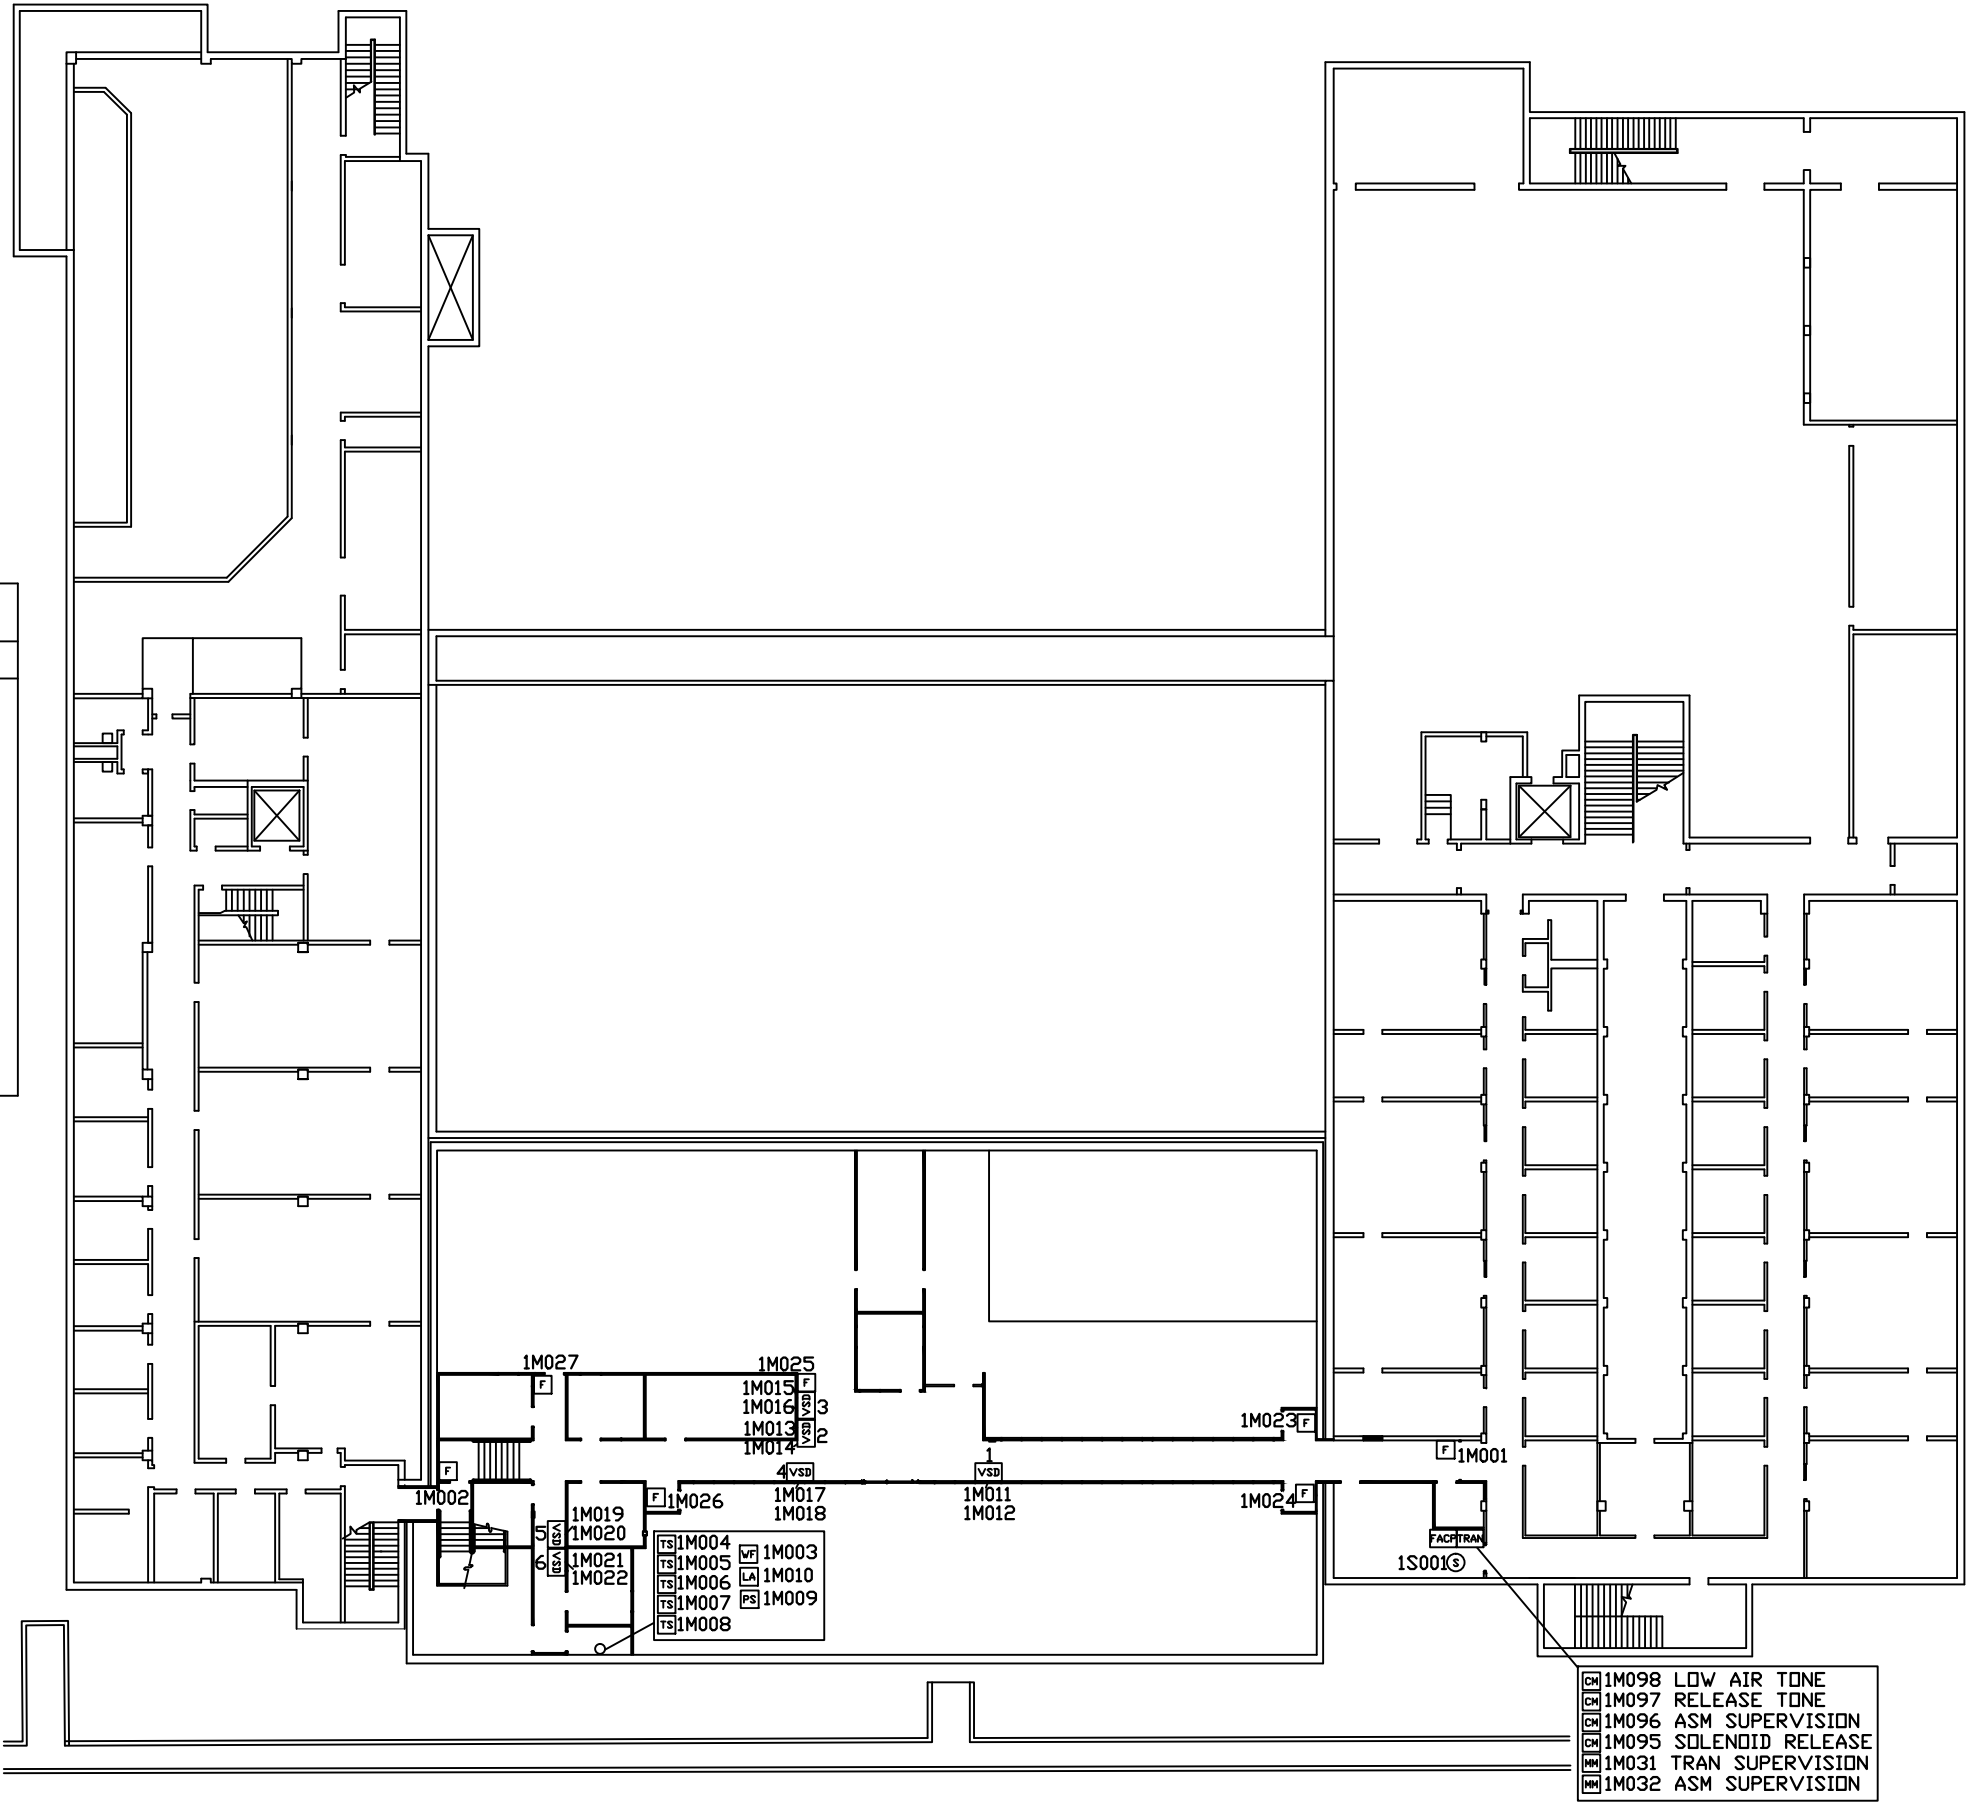

NOTE:
NFS DRAWINGS ARE BASED ON THE PROJECT
ARCHITECT/ENGINEER (A/E) PLANS AND SPECIFICATIONS
FURNISHED TO NFS. A/E IS SOLELY RESPONSIBLE
(NOT NFS) FOR THE TYPE, SIZE, LOCATION, AND
SUITABILITY OF ALL FIRE ALARMS, CONTROL PANELS,
AND OTHER DEVICES SHOWN ON THE A/E PLANS.
NFS DRAWINGS ARE TO SHOW ONLY THE WIRING
DIAGRAMS BETWEEN FIRE ALARM DEVICES AND
CONTROL PANELS. NFS IS NOT RESPONSIBLE FOR
THE INFORMATION SHOWN ON THE A/E PLANS.

HENRY EYRING BUILDING
GAUSS HAUS
UNIVERSITY OF UTAH
MAGNET LEVEL
FIRE ALARM SYSTEM

NFS

NELSON FIRE SYSTEMS
801-468-8300

DRAWN BY: DS
DESIGNED BY: JGA
APPROVED BY: TCT
DATE: 8/7/2006
SCALE: N.T.S.
PROJECT NO: 0085-11621
REV NO: 1
DRAWING NAME:
GAUSS HAUS.DWG

FIRE ALARM SYSTEM
MAGNET LEVEL
ADDRESSABLE NUMBERS

NFS

FA-M-01