



DEVICE LEGEND	
SYMBOL	DESCRIPTION
Ⓢ	SMOKE DETECTOR
F	MANUAL PULL STATION
DD	DUCT SMOKE DETECTOR
FE	MIJA W/ MONITOR MODULE
MM	MONITOR MODULE
WF	WATERFLOW SWITCH
TS	TAMPER SWITCH
CM	CONTROL MODULE
RA	REMOTE ANNUNCIATOR
FACP	FIRE ALARM CONTROL PANEL
TRAN	TRANSPONDER PANEL

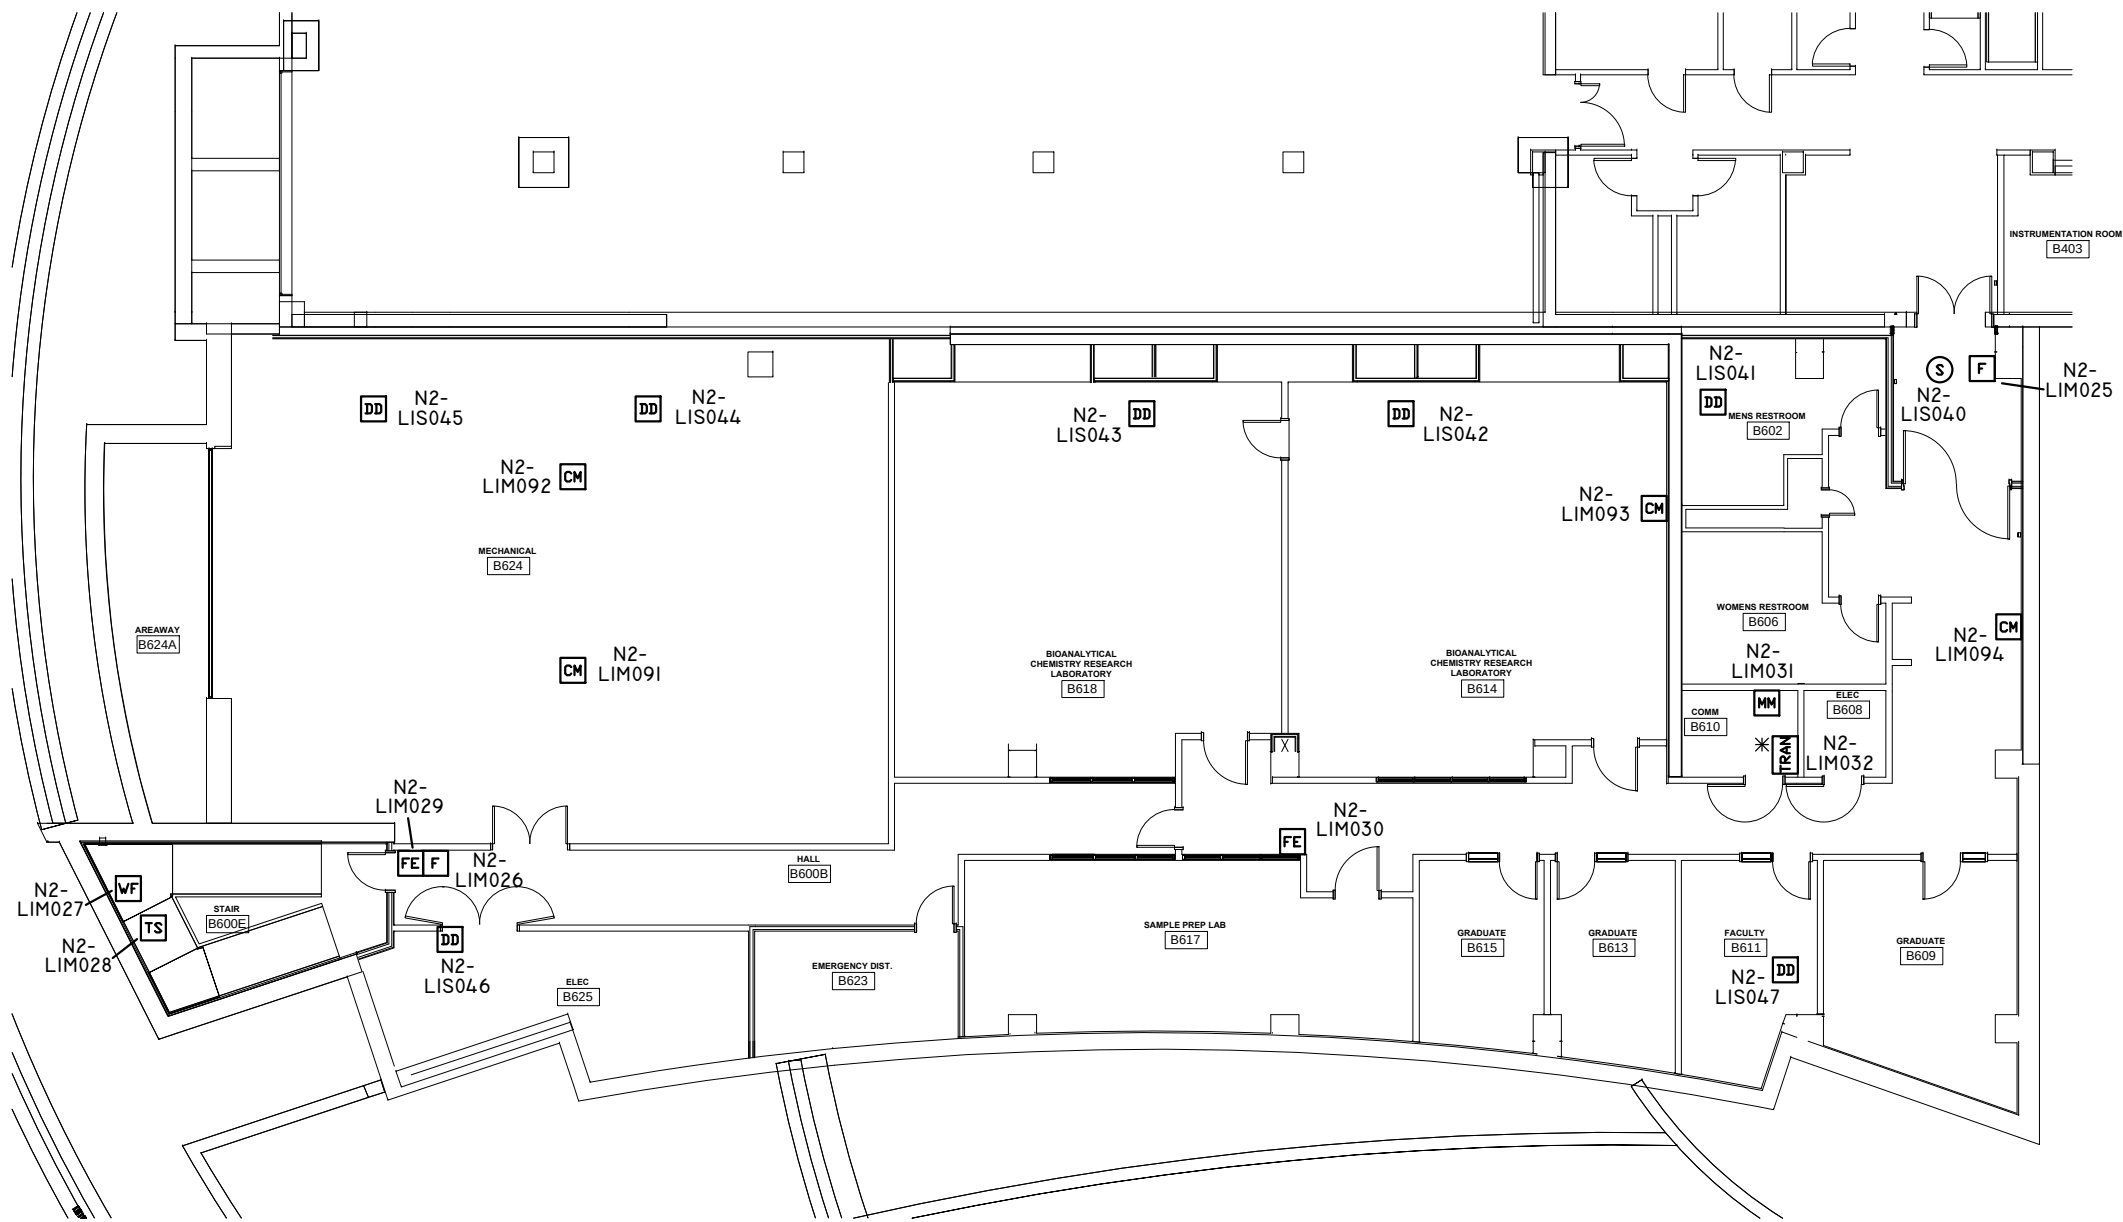

BASEMENT LEVEL

N.I.C.E.T.
LEVEL IV
CERTIFICATION
FIRE ALARM SYSTEMS
DONNY SCHULTZ
#104396

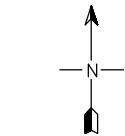

NOTE:
NFS DRAWINGS ARE BASED ON THE PROJECT
ARCHITECT/ENGINEER (A/E) PLANS AND SPECIFICATIONS
FURNISHED TO NFS. A/E IS SOLELY RESPONSIBLE
(NOT NFS) FOR THE TYPE, SIZE, LOCATION, AND
SUITABILITY OF ALL FIRE ALARMS, CONTROL PANELS,
AND OTHER DEVICES SHOWN ON THE A/E PLANS.
NFS DRAWINGS ARE TO SHOW ONLY THE WIRING
DIAGRAMS BETWEEN FIRE ALARM DEVICES AND
CONTROL PANELS. NFS IS NOT RESPONSIBLE FOR
THE INFORMATION SHOWN ON THE A/E PLANS.

UNIVERSITY OF UTAH
THATCHER BUILDING
FOR BIOLOGY AND BIOPHYSICAL CHEMISTRY
315 SOUTH 1400 EAST
SALT LAKE CITY, UTAH 84112
FIRE ALARM SYSTEM


NFS
NELSON FIRE SYSTEMS
801-468-8300

DRAWN BY:	JJG
DESIGNED BY:	SPECTRUM
APPROVED BY:	DPS
DATE:	8/30/12
SCALE:	N.T.S.
PROJECT NO:	10026750
REV NO:	XXXX
DRAWING NAME:	THATCHER B FINAL.DWG

FIRE ALARM SYSTEM
BASEMENT LEVEL
ADDRESSABLE NUMBERS

PAGE:
FA-B

DEVICE LEGEND	
SYMBOL	DESCRIPTION
Ⓢ	SMOKE DETECTOR
F	MANUAL PULL STATION
DD	DUCT SMOKE DETECTOR
FE	MIJA W/ MONITOR MODULE
MM	MONITOR MODULE
VF	WATERFLOW SWITCH
TS	TAMPER SWITCH
CM	CONTROL MODULE
RA	REMOTE ANNUNCIATOR
FACP	FIRE ALARM CONTROL PANEL
TRAN	TRANSPONDER PANEL

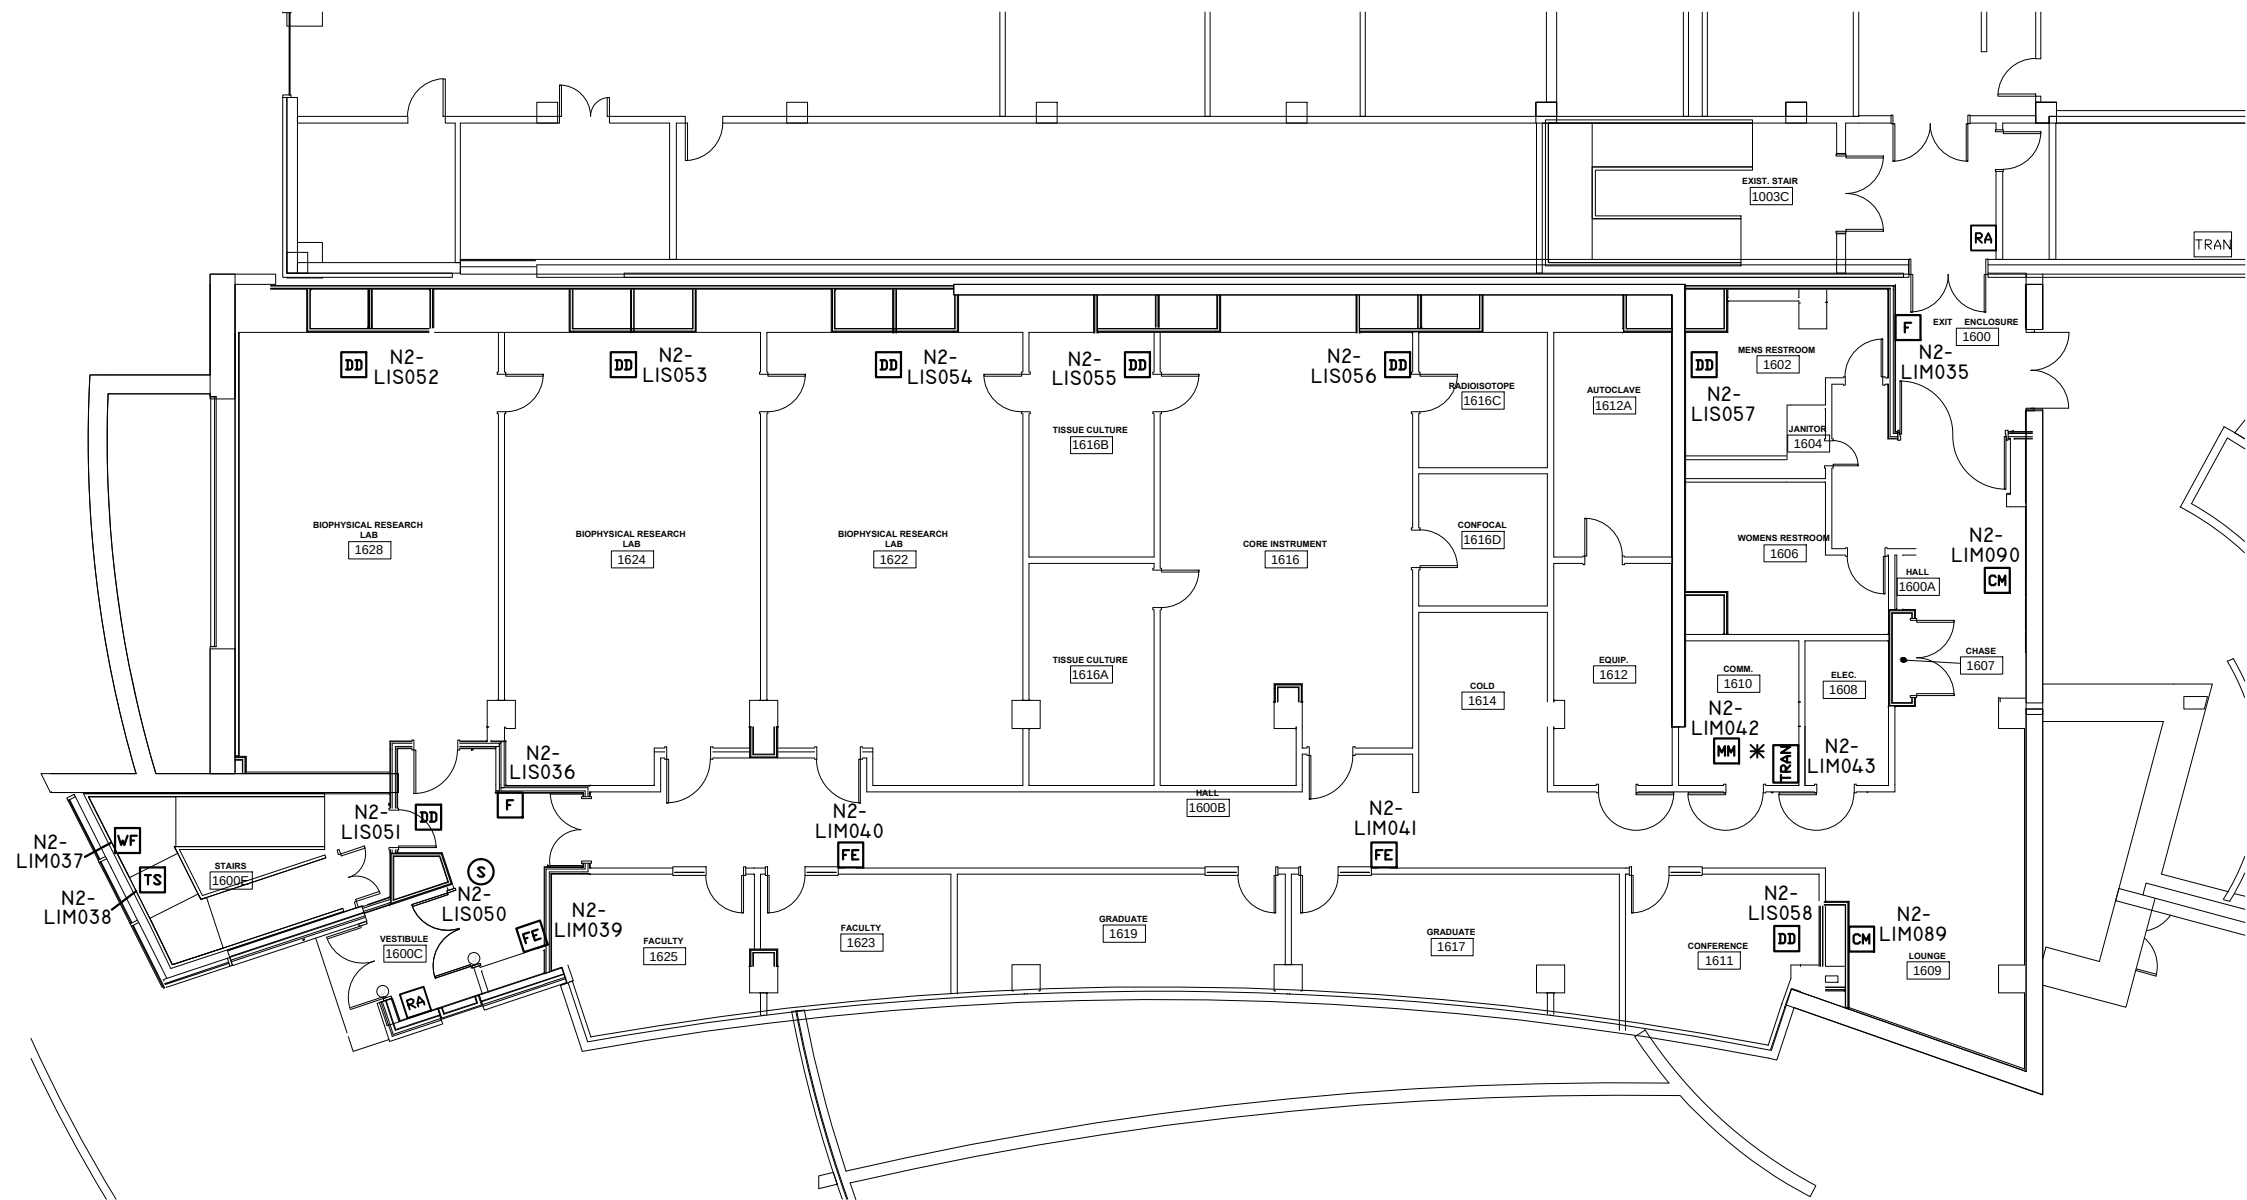

LEVEL ONE

N.I.C.E.T.
LEVEL IV
CERTIFICATION
FIRE ALARM SYSTEMS
DONNY SCHULTZ
#104396

NOTE:
NFS DRAWINGS ARE BASED ON THE PROJECT
ARCHITECT/ENGINEER (A/E) PLANS AND SPECIFICATIONS
FURNISHED TO NFS. A/E IS SOLELY RESPONSIBLE
(NOT NFS) FOR THE TYPE, SIZE, LOCATION, AND
SUITABILITY OF ALL FIRE ALARMS, CONTROL PANELS,
AND OTHER DEVICES SHOWN ON THE A/E PLANS.
NFS DRAWINGS ARE TO SHOW ONLY THE WIRING
DIAGRAMS BETWEEN FIRE ALARM DEVICES AND
CONTROL PANELS. NFS IS NOT RESPONSIBLE FOR
THE INFORMATION SHOWN ON THE A/E PLANS.


UNIVERSITY OF UTAH
THATCHER BUILDING
FOR BIOLOGY AND BIOPHYSICAL CHEMISTRY
315 SOUTH 1400 EAST
SALT LAKE CITY, UTAH 84112
FIRE ALARM SYSTEM

NFS	
NELSON FIRE SYSTEMS 801-468-8300	
DRAWN BY: JJC	
DESIGNED BY: SPECTRUM	
APPROVED BY: DPS	
DATE: 8/30/12	
SCALE: N.T.S.	
PROJECT NO: 10026750	
REV NO: XXXX	
DRAWING NAME:	
THATCHER I FINAL.DWG	


FIRE ALARM SYSTEM
LEVEL ONE
ADDRESSABLE NUMBERS

PAGE:
FA-I

DEVICE LEGEND	
SYMBOL	DESCRIPTION
Ⓢ	SMOKE DETECTOR
F	MANUAL PULL STATION
DD	DUCT SMOKE DETECTOR
FE	MIJA W/ MONITOR MODULE
MM	MONITOR MODULE
WF	WATERFLOW SWITCH
TS	TAMPER SWITCH
CM	CONTROL MODULE
RA	REMOTE ANNUNCIATOR
FACP	FIRE ALARM CONTROL PANEL
TRAN	TRANSPONDER PANEL

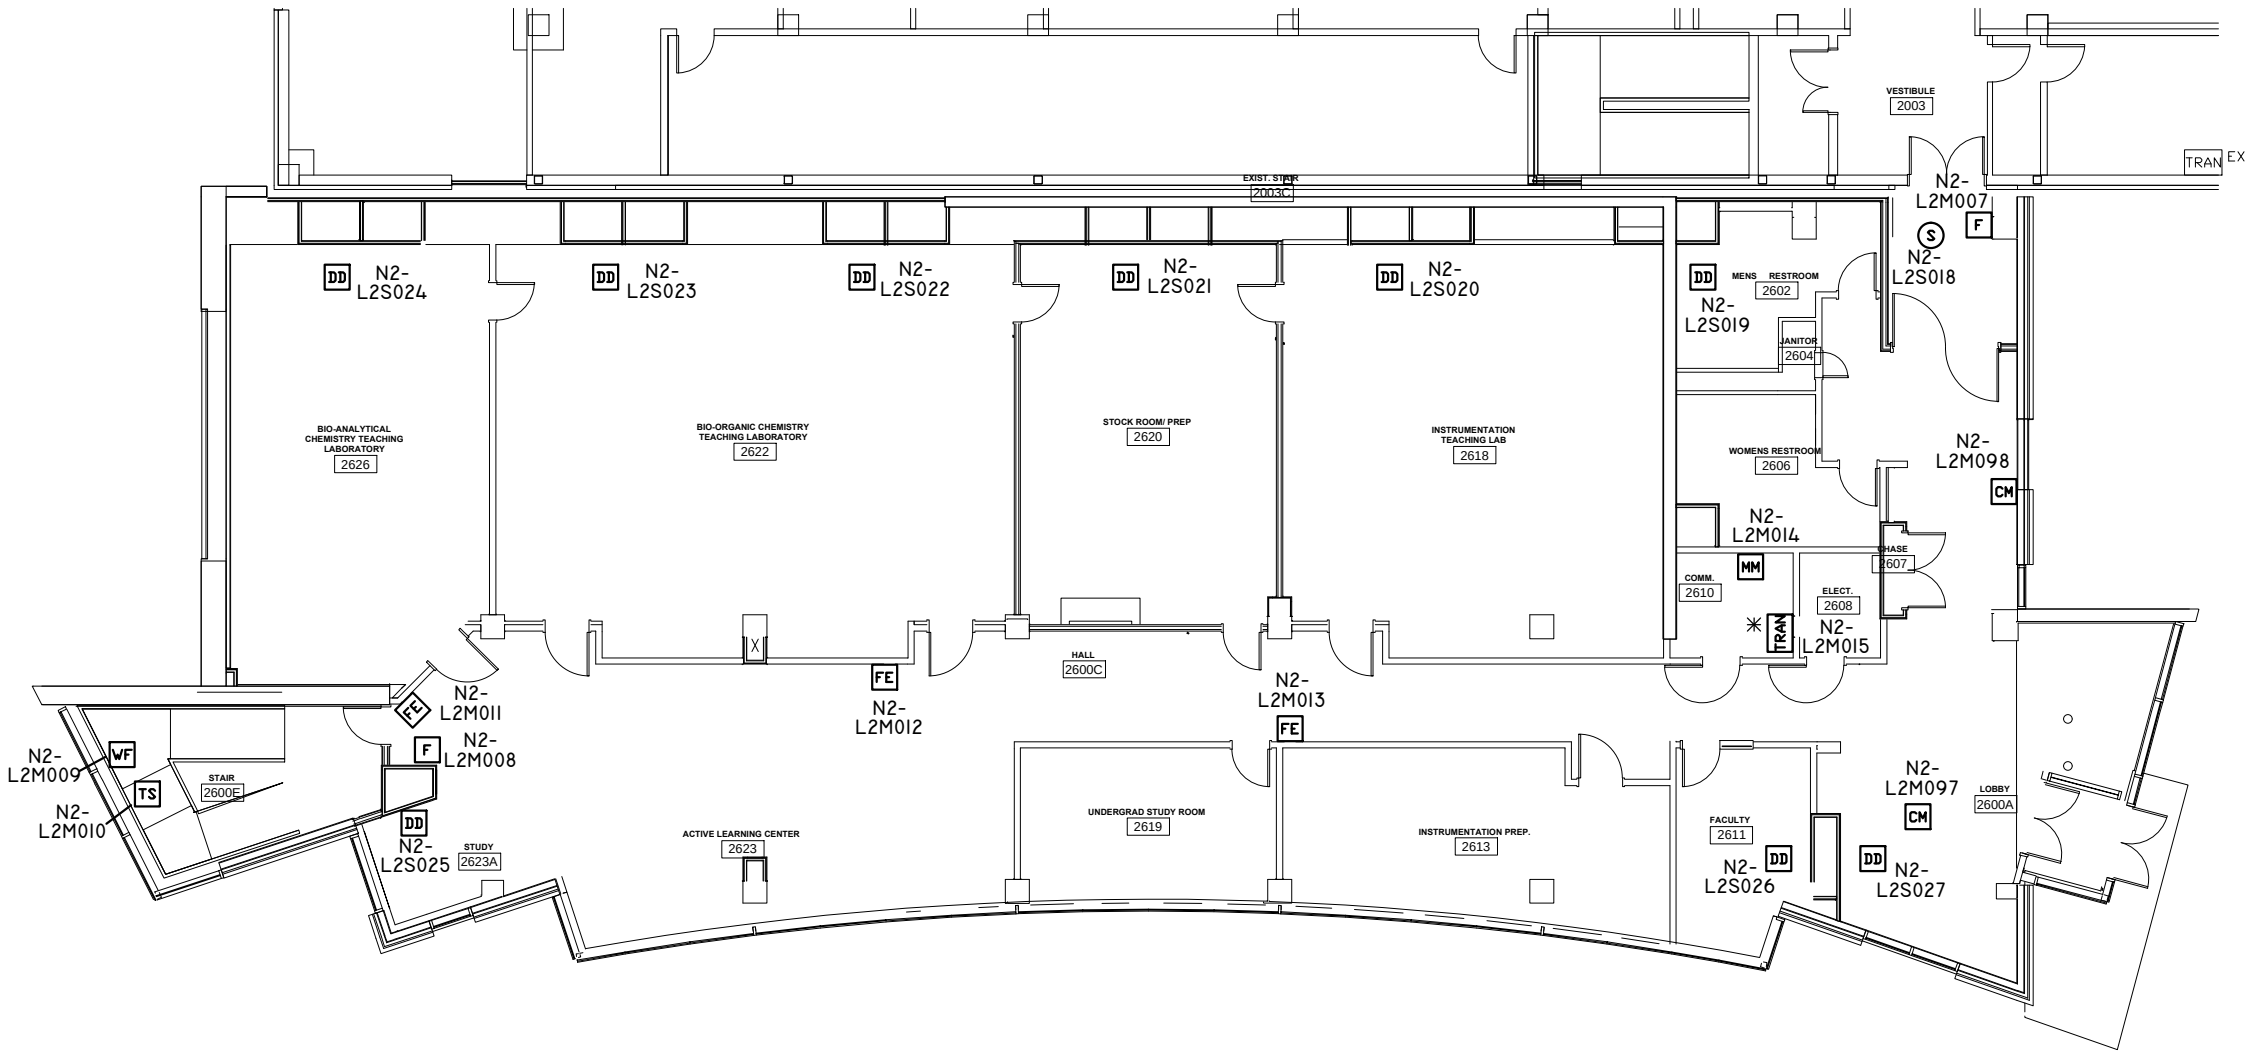

LEVEL TWO

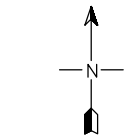

NOTE:
NFS DRAWINGS ARE BASED ON THE PROJECT
ARCHITECT/ENGINEER (A/E) PLANS AND SPECIFICATIONS
FURNISHED TO NFS. A/E IS SOLELY RESPONSIBLE
(NOT NFS) FOR THE TYPE, SIZE, LOCATION, AND
SUITABILITY OF ALL FIRE ALARMS, CONTROL PANELS,
AND OTHER DEVICES SHOWN ON THE A/E PLANS.
NFS DRAWINGS ARE TO SHOW ONLY THE WIRING
DIAGRAMS BETWEEN FIRE ALARM DEVICES AND
CONTROL PANELS. NFS IS NOT RESPONSIBLE FOR
THE INFORMATION SHOWN ON THE A/E PLANS.

UNIVERSITY OF UTAH
THATCHER BUILDING
FOR BIOLOGY AND BIOPHYSICAL CHEMISTRY
315 SOUTH 1400 EAST
SALT LAKE CITY, UTAH 84112
FIRE ALARM SYSTEM

NFS
NELSON FIRE SYSTEMS
801-468-8300

DRAWN BY:	JJG
DESIGNED BY:	SPECTRUM
APPROVED BY:	DPS
DATE:	8/30/12
SCALE:	N.T.S.
PROJECT NO:	10026750
REV NO:	XXXX
DRAWING NAME:	THATCHER 2 FINAL.DWG

FIRE ALARM SYSTEM
LEVEL TWO
ADDRESSABLE NUMBERS

PAGE:
FA-2



UNIVERSITY OF UTAH
THATCHER BUILDING
FOR BIOLOGY AND BIOPHYSICAL
315 SOUTH 1400 EAST
SALT LAKE CITY, UTAH 84143
FIRE ALARM SYSTEM

NFS
NELSON FIRE SYSTEMS
801-468-8300


DRAWN BY:	JJG
DESIGNED BY:	SPECTRUM
APPROVED BY:	DPS
DATE:	8/30/12
SCALE:	N.T.S.
PROJECT NO:	10026750
REV NO:	XXXX
DRAWING NAME:	THATCHER 4 FINAL.DWG

FIRE ALARM SYSTEM
LEVEL FOUR
ADDRESSABLE NUMBERS


PAGE:

FA-4

NOTE:
NFS DRAWINGS ARE BASED ON THE PROJECT
ARCHITECT/ENGINEER (A/E) PLANS AND SPECIFICATIONS
FURNISHED TO NFS. A/E IS SOLELY RESPONSIBLE,
(NOT NFS) FOR THE TYPE, SIZE, LOCATION, AND
SUITABILITY OF ALL FIRE ALARMS, CONTROL PANELS,
AND OTHER DEVICES SHOWN ON THE A/E PLANS.
NFS DRAWINGS ARE TO SHOW ONLY THE WIRING
DIAGRAMS BETWEEN FIRE ALARM DEVICES AND
CONTROL PANELS. NFS IS NOT RESPONSIBLE FOR
THE INFORMATION SHOWN ON THE A/E PLANS.

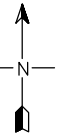


DEVICE LEGEND	
SYMBOL	DESCRIPTION
Ⓢ	SMOKE DETECTOR
F	MANUAL PULL STATION
DD	DUCT SMOKE DETECTOR
FE	MIJA W/ MONITOR MODULE
MM	MONITOR MODULE
WF	WATERFLOW SWITCH
TS	TAMPER SWITCH
CM	CONTROL MODULE
RA	REMOTE ANNUNCIATOR
FACP	FIRE ALARM CONTROL PANEL
TRAN	TRANSPONDER PANEL

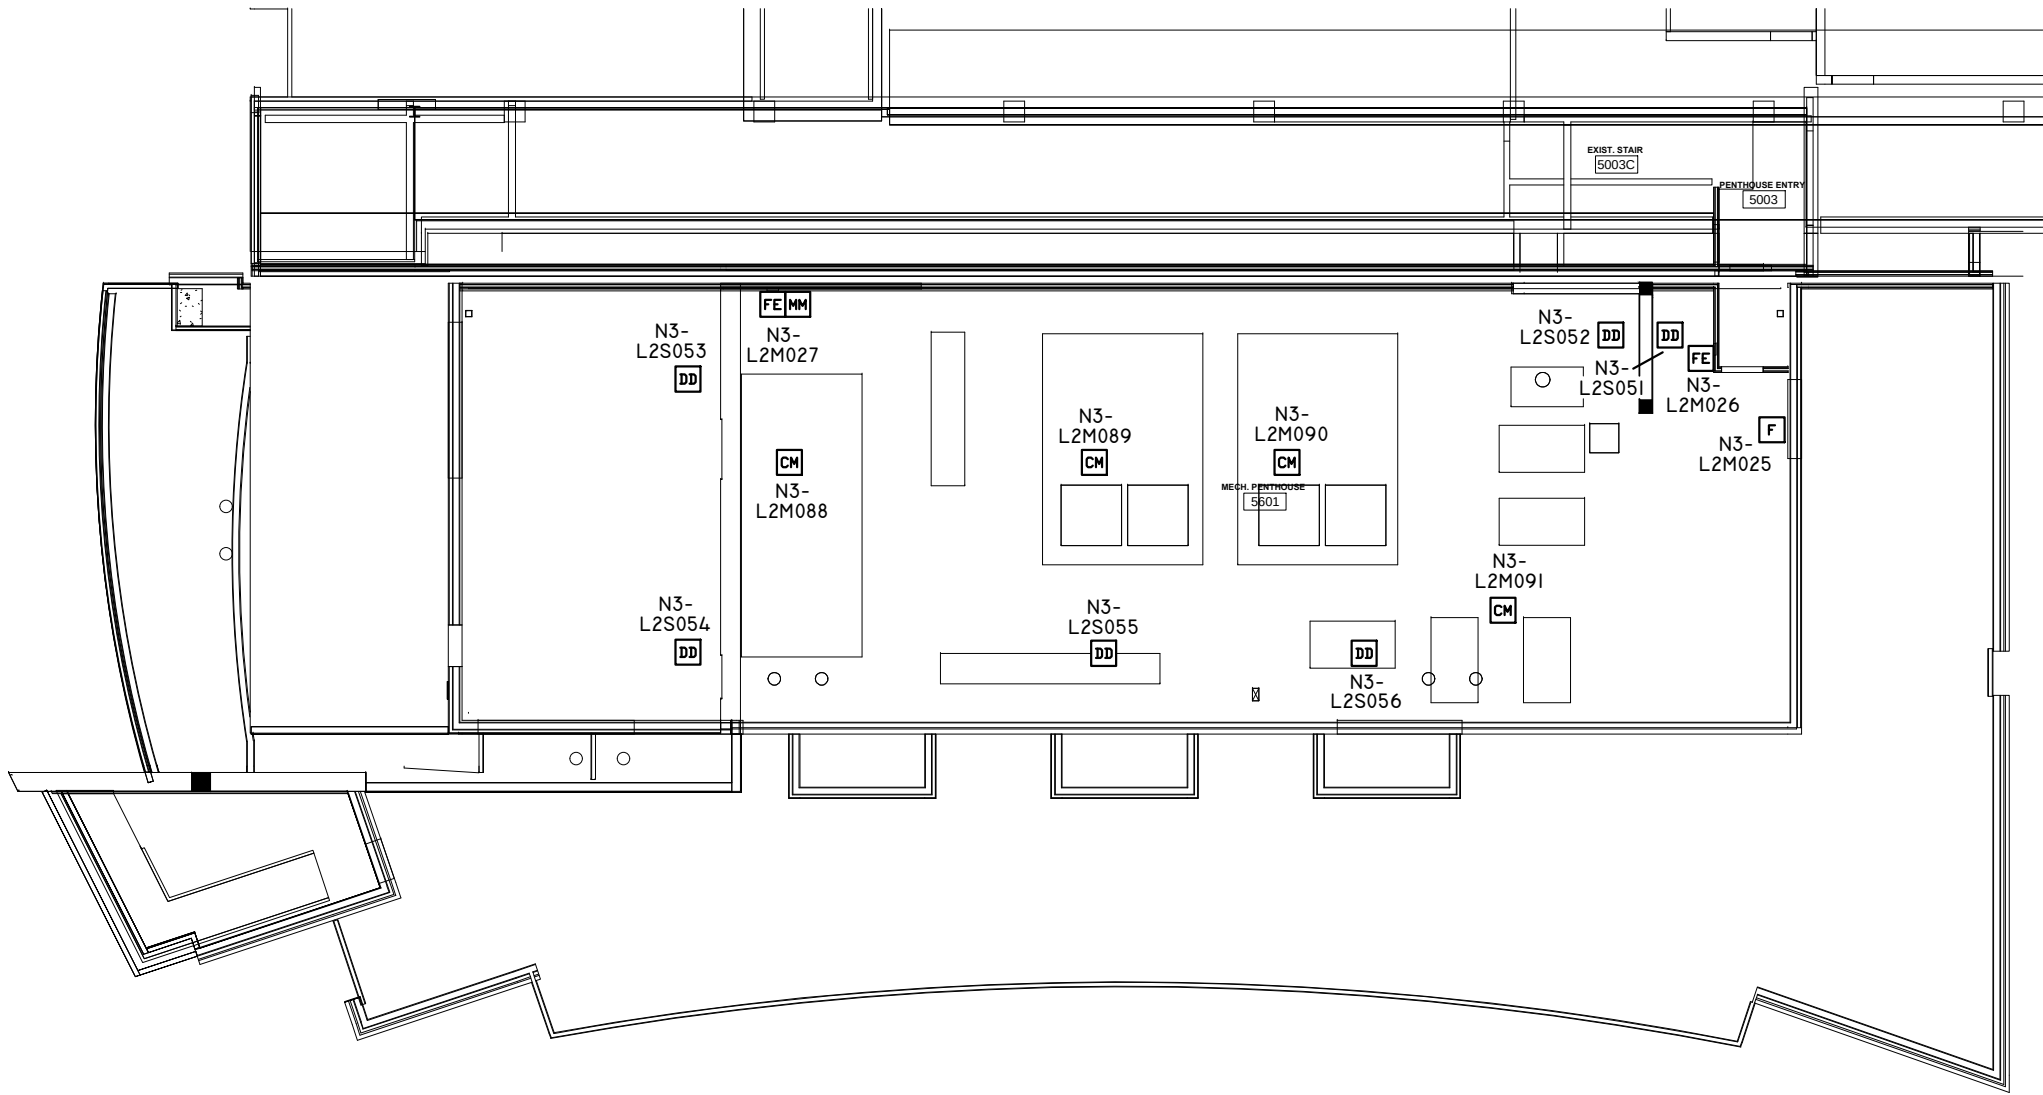

PENTHOUSE LEVEL

N.I.C.E.T.
LEVEL IV
CERTIFICATION
FIRE ALARM SYSTEMS
DONNY SCHULTZ
#104396

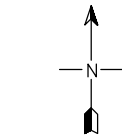

NOTE:
NFS DRAWINGS ARE BASED ON THE PROJECT
ARCHITECT/ENGINEER (A/E) PLANS AND SPECIFICATIONS
FURNISHED TO NFS. A/E IS SOLELY RESPONSIBLE
(NOT NFS) FOR THE TYPE, SIZE, LOCATION, AND
SUITABILITY OF ALL FIRE ALARMS, CONTROL PANELS,
AND OTHER DEVICES SHOWN ON THE A/E PLANS.
NFS DRAWINGS ARE TO SHOW ONLY THE WIRING
DIAGRAMS BETWEEN FIRE ALARM DEVICES AND
CONTROL PANELS. NFS IS NOT RESPONSIBLE FOR
THE INFORMATION SHOWN ON THE A/E PLANS.

UNIVERSITY OF UTAH
THATCHER BUILDING
FOR BIOLOGY AND BIOPHYSICAL CHEMISTRY
315 SOUTH 1400 EAST
SALT LAKE CITY, UTAH 84112
FIRE ALARM SYSTEM

NFS
NELSON FIRE SYSTEMS
801-468-8300

DRAWN BY:	JJG
DESIGNED BY:	SPECTRUM
APPROVED BY:	DPS
DATE:	8/30/12
SCALE:	N.T.S.
PROJECT NO:	10026750
REV NO:	XXXX
DRAWING NAME:	THATCHER 5 FINAL.DWG

FIRE ALARM SYSTEM
PENTHOUSE LEVEL
ADDRESSABLE NUMBERS

PAGE:
FA-5