

_____ NODE ADDRESS
 _____ ADDRESSABLE LOOP NUMBER
 _____ SENSOR ('M' MONITOR)
 _____ DEVICE NUMBER

NOTE: NIS DRAWINGS ARE BASED ON THE PROJECT SPECIFICATIONS FURNISHED TO NIS. A/E IS SOLELY RESPONSIBLE (NOT NIS) FOR THE TYPE, SIZE, LOCATION, AND SUITABILITY OF ALL FIRE ALARMS, CONTROL PANELS, AND OTHER DEVICES SHOWN ON THE A/E PLANS. NIS DRAWINGS ARE TO SHOW ONLY THE WIRING DIAGRAMS BETWEEN FIRE ALARM DEVICES AND CONTROL PANELS. NIS IS NOT RESPONSIBLE FOR THE INFORMATION SHOWN ON THE A/E PLANS.

UNIVERSITY OF UTAH
HUNTSMAN CENTER
MAIN LEVEL
FIRE ALARM SYSTEM

NFS

NELSON FIRE SYSTEMS
801-468-8300

DRAWN BY:	TCT
DESIGNED BY:	XXXX
APPROVED BY:	DPS
DATE:	3/29/2006
SCALE:	N.T.S.
PROJECT NO:	XXXX
REV NO:	XXXX
DRAWING NAME:	HUNTSMANMAIN.DWG

FIRE ALARM SYSTEM


DEVICE NUMBERS

PAGE:


FA-1-01

DEVICE LEGEND	
SYMBOL	DESCRIPTION
	SMOKE DETECTOR
	THERMAL DETECTOR
	MANUAL PULL STATION
	DUCT SMOKE DETECTOR
	WATERFLOW SWITCH
	TAMPER SWITCH
	CONTROL MODULE
	REMOTE ANNUNCIATOR
	FIRE ALARM CONTROL PANEL
	TRANSPONDER PANEL

DEVICE LEGEND	
SYMBOL	DESCRIPTION
⊙	SMOKE DETECTOR W/BASE
⊖	THERMAL DETECTOR
F	MANUAL PULL STATION
I	DUCT SMOKE DETECTOR
WF	WATERFLOW SWITCH MONITOR MODULE
TS	TAMPER SWITCH MONITOR MODULE
MM	MONITOR MODULE
CM	CONTROL MODULE
RA	REMOTE ANNUNCIATOR ENCLOSURE
FACP	FIRE ALARM CONTROL PANEL
TRAN	TRANSPONDER PANEL

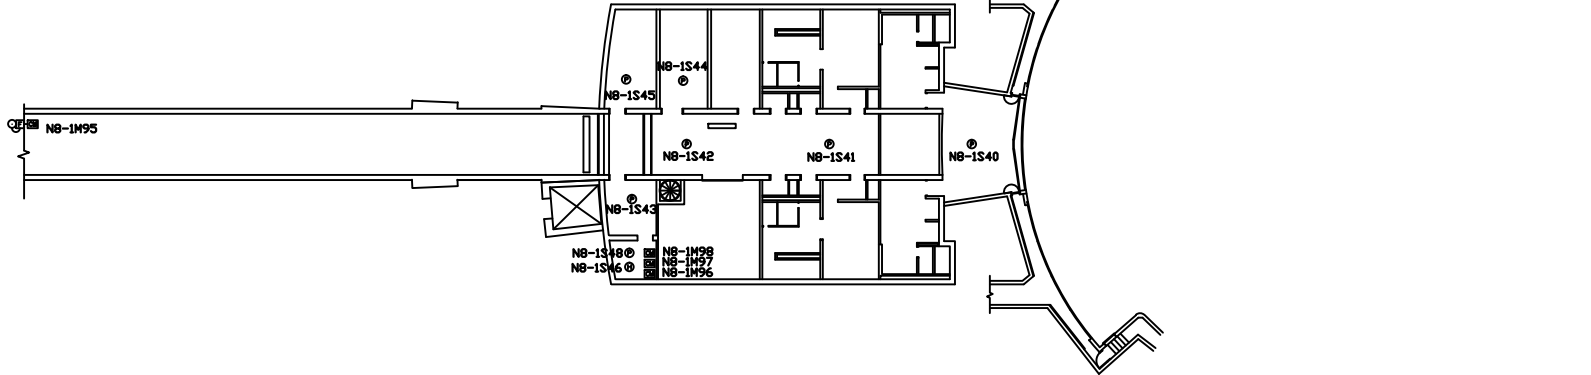

BASEMENT-L

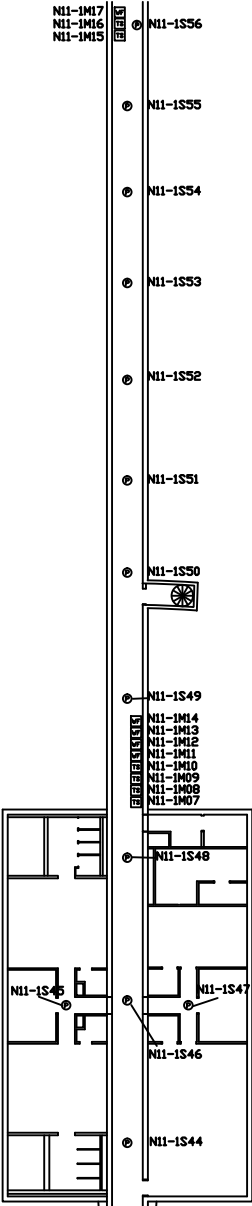

NOTE:
NFS DRAWINGS ARE BASED ON THE PROJECT
ARCHITECT/ENGINEER (A/E) PLANS AND SPECIFICATIONS
FURNISHED TO NFS. A/E IS SOLELY RESPONSIBLE
FOR THE ACCURACY OF THE A/E PLANS AND SPECIFICATIONS.
NFS IS NOT RESPONSIBLE FOR THE ACCURACY OF THE
A/E PLANS AND SPECIFICATIONS.
NFS DRAWINGS ARE FOR INFORMATION ONLY. NFS
IS NOT RESPONSIBLE FOR THE ACCURACY OF THE
A/E PLANS AND SPECIFICATIONS.
NFS IS NOT RESPONSIBLE FOR THE ACCURACY OF THE
A/E PLANS AND SPECIFICATIONS.

UNIVERSITY OF UTAH
HUNTSMAN CENTER
BASEMENT LEVEL L
FIRE ALARM SYSTEM

NFS
NELSON FIRE SYSTEMS
801-468-8300


DRAWN BY:	DS
DESIGNED BY:	JGA
APPROVED BY:	TT
DATE:	4/6/2005
SCALE:	N.T.S.
PROJECT NO:	XXXX
REV NO:	XXXX
DRAWING NAME:	HUNTSMANBASL.DWG

FIRE ALARM SYSTEM

PAGE:

FA-3-01

BASEMENT-U

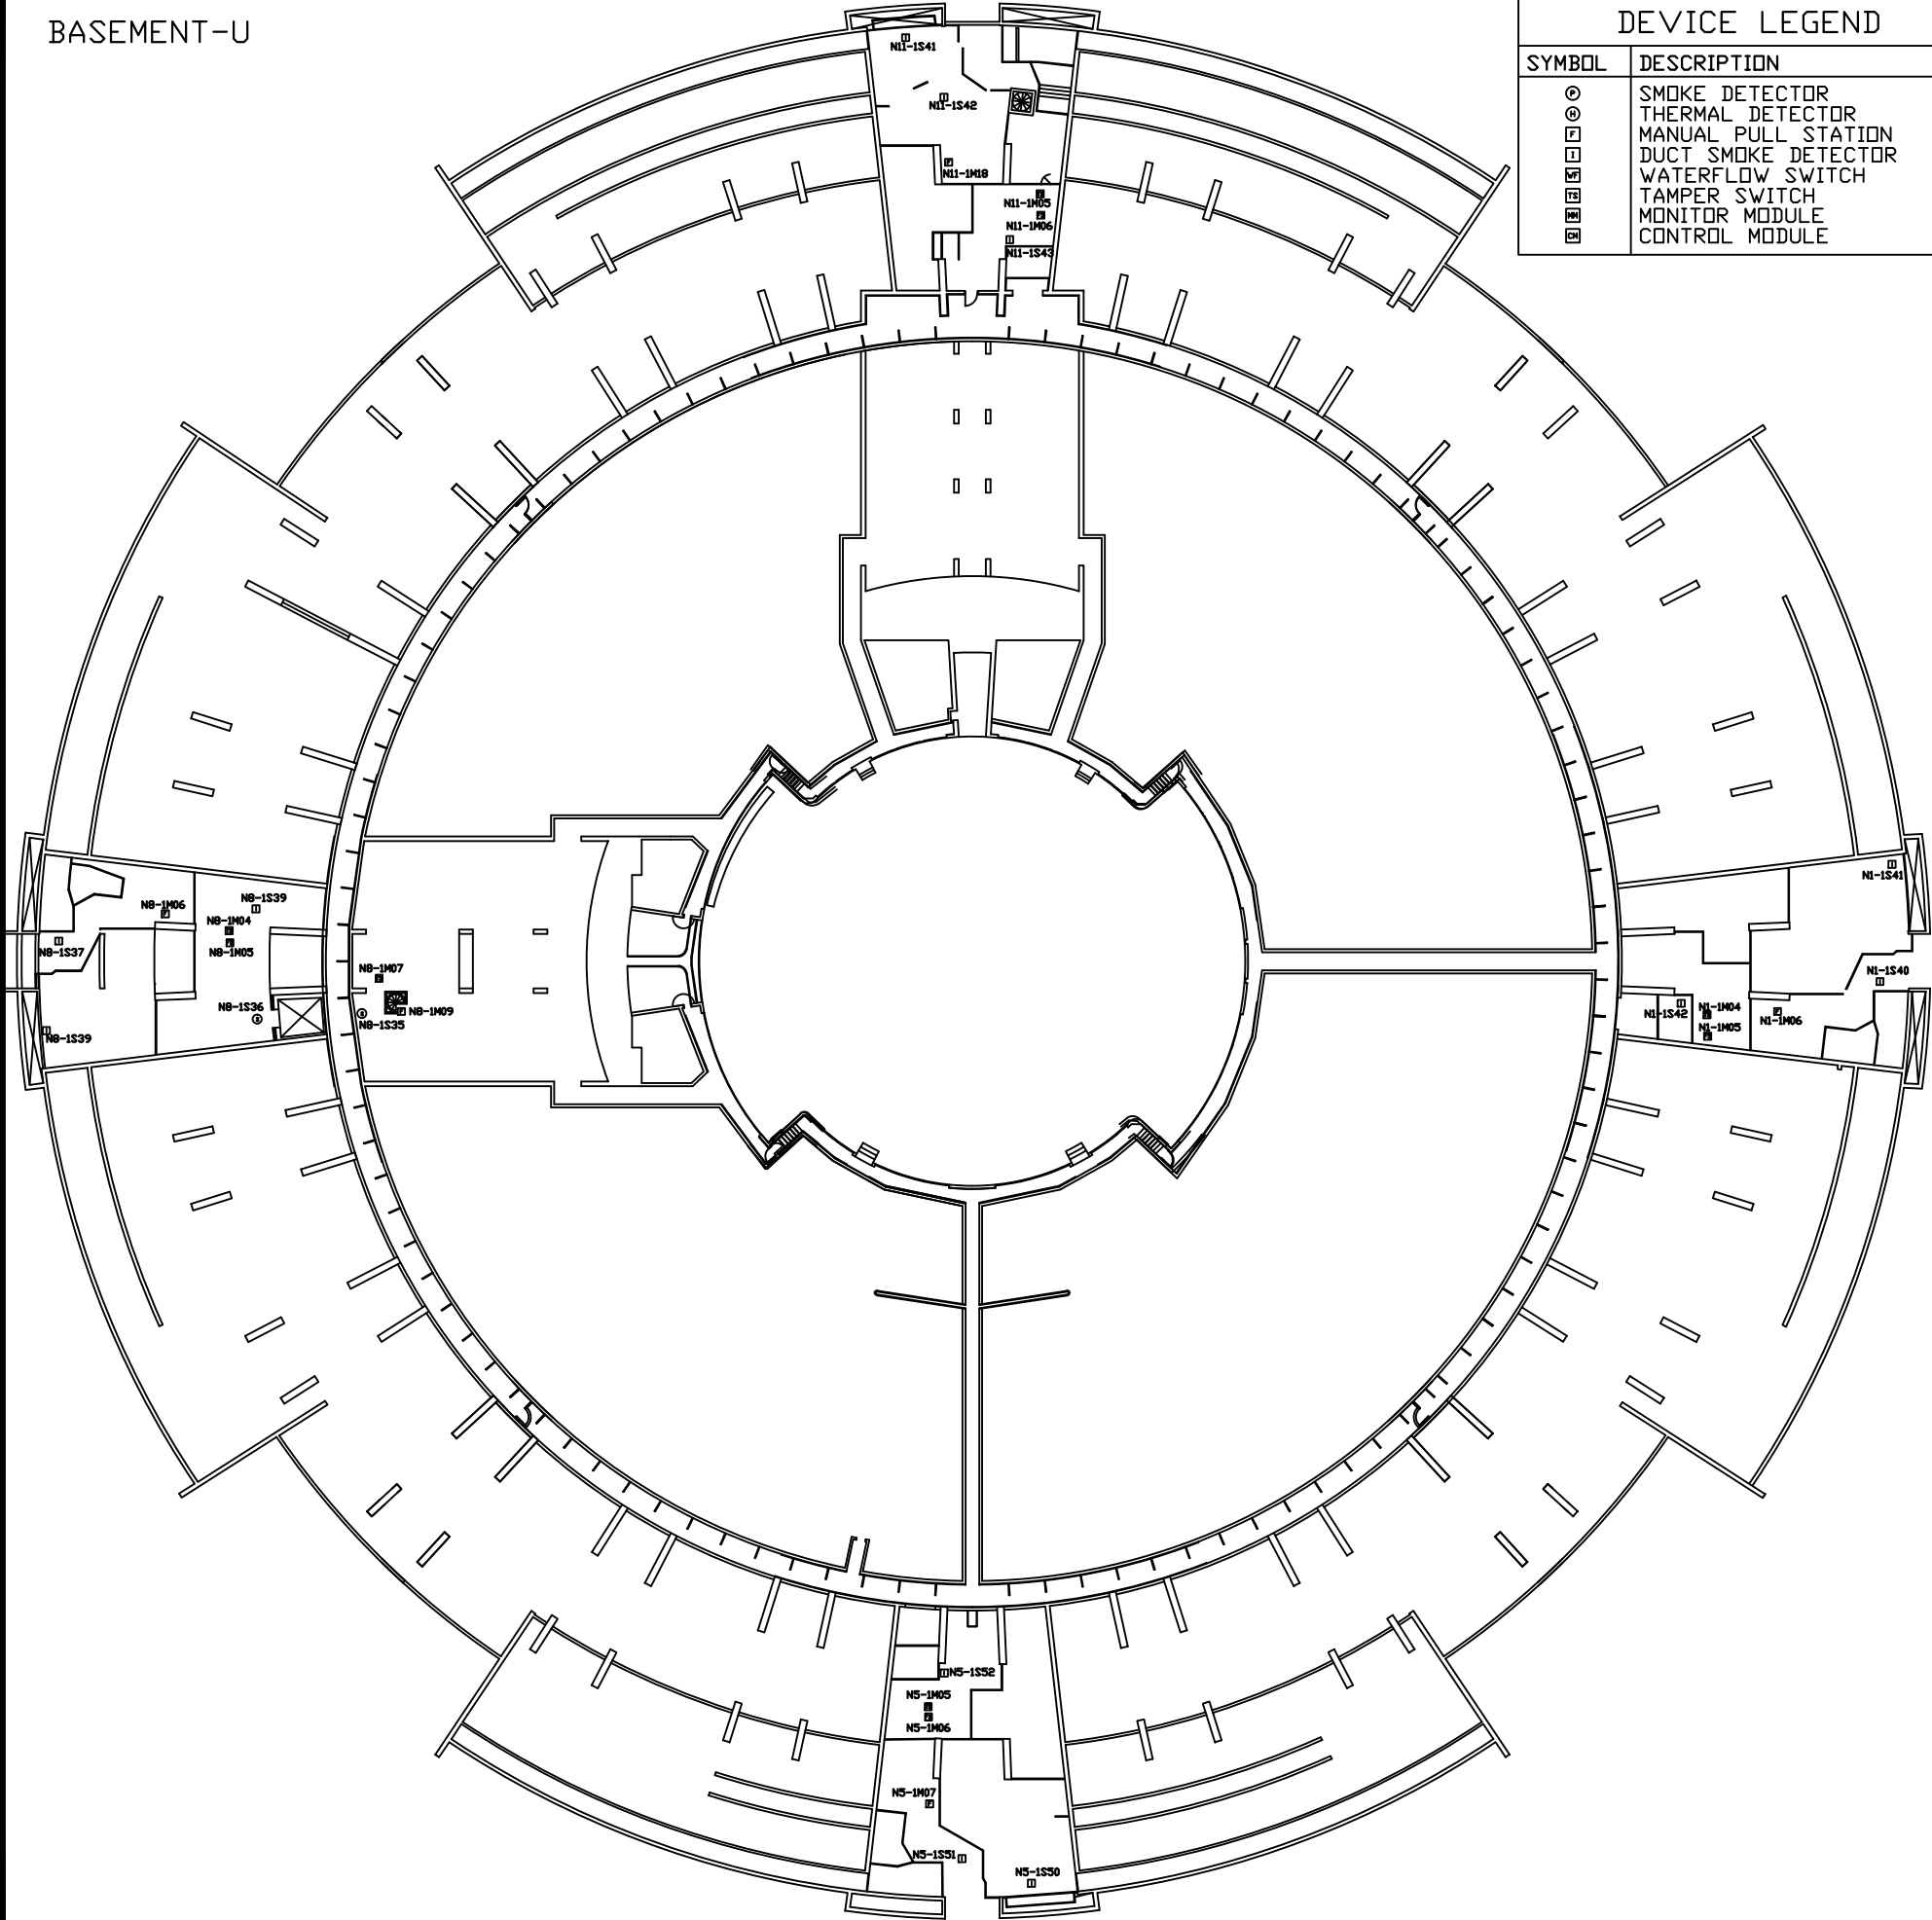

UNIVERSITY OF UTAH
HUNTSMAN CENTER
BASEMENT LEVEL U
FIRE ALARM SYSTEM

NFS

NELSON FIRE SYSTEMS
801-468-8300

DRAWN BY:	DS
DESIGNED BY:	JGA
APPROVED BY:	TT
DATE:	4/6/2005
SCALE:	N.T.S.
PROJECT NO:	XXXX
REV NO:	XXXX
DRAWING NAME:	HUNTSMANBASU.DWG

FIRE ALARM SYSTEM

PAGE:

FA-I-02