


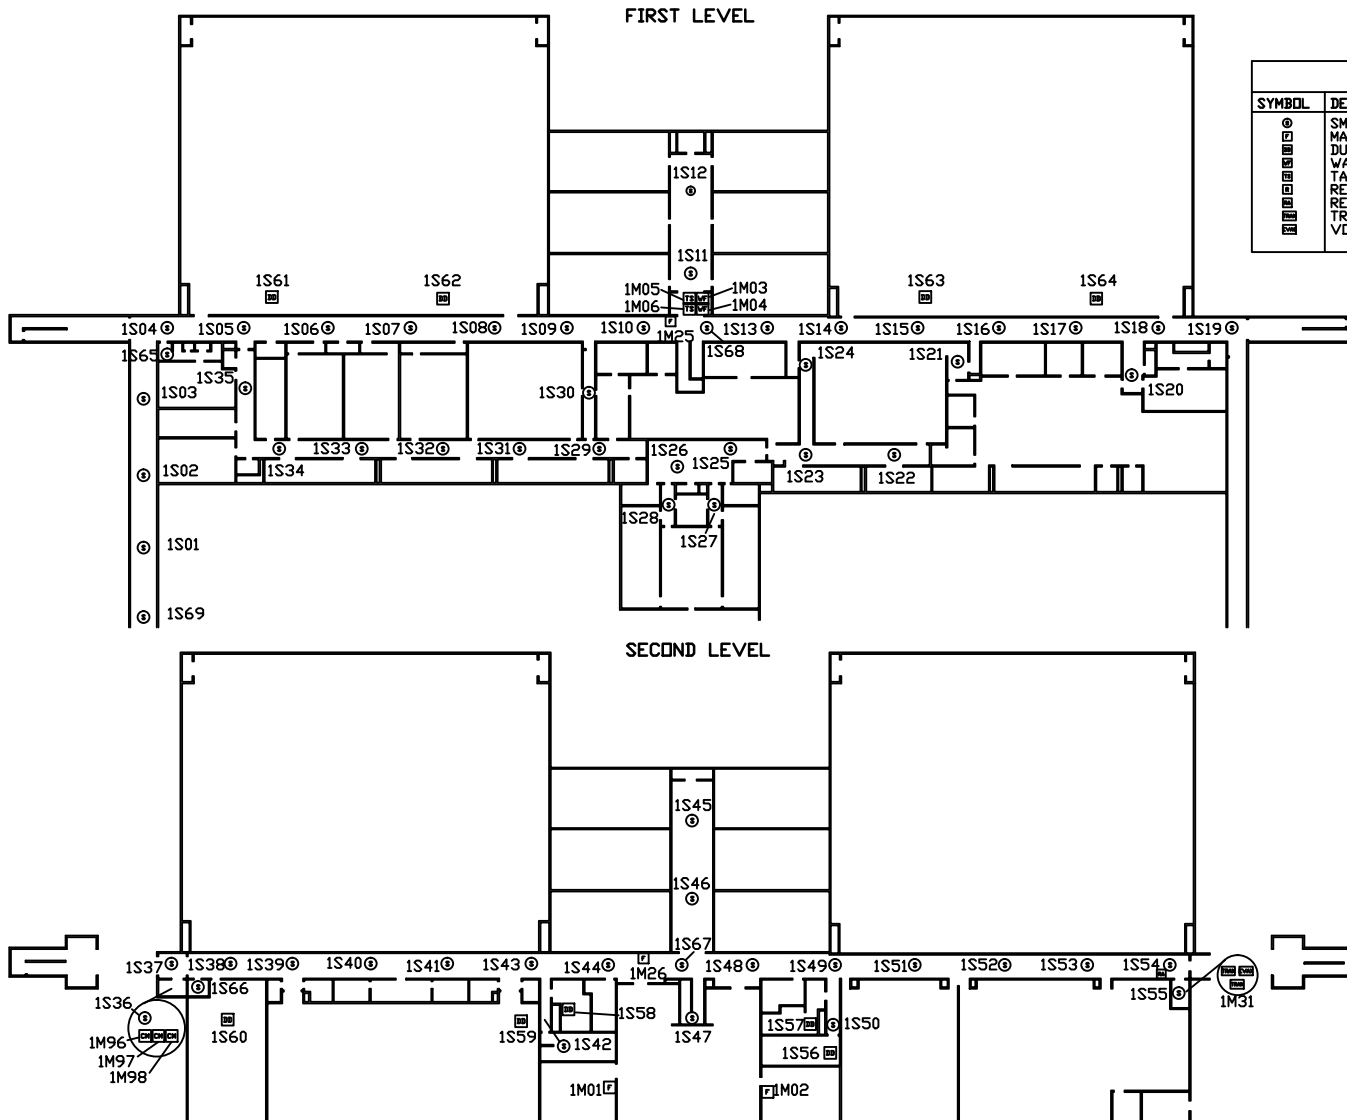

DEVICE LEGEND	
SYMBOL	DESCRIPTION
⊙	SMOKE DETECTOR W/BASE
⊙	MANUAL PULL STATION
⊙	DUCT SMOKE DETECTOR
⊙	WATERFLOW SWITCH MONITOR MODULE
⊙	TAMPER SWITCH MONITOR MODULE
⊙	RELAY- ARB-C
⊙	REMOTE ANNUNCIATOR
⊙	TRANSFONDER PANEL
⊙	VOICE PANEL

ADDRESS LABEL CLARIFICATION	
⊙	ADDRESSABLE LOOP NUMBER
⊙	SENSOR ("M" MONITOR)
⊙	DEVICE NUMBER



NOTE:
NFS DRAWINGS ARE BASED ON THE PROJECT
NOTES. ANY CHANGES TO THE DRAWINGS
(NOT NFS) FOR THE TYPE, SIZE, LOCATION, AND
FUNCTIONS OF THE DEVICES SHOWN ON THE A/E PLANS,
AND OTHER DEVICES SHOWN ON THE A/E PLANS,
NFS DRAWINGS ARE TO SHOW ONLY THE WIRING
AND CONNECTIONS TO THE DEVICES SHOWN ON THE
CONTROL PANELS. NFS IS NOT RESPONSIBLE FOR
THE INFORMATION SHOWN ON THE A/E PLANS.

HPER COMPLEX
BUILDING #91
UNIVERSITY OF UTAH
FIRE ALARM SYSTEM


NFS
NELSON FIRE SYSTEMS
801-468-8300

DRAWN BY:	TCT
DESIGNED BY:	XXXX
APPROVED BY:	OPS
DATE:	6/10/10
SCALE:	N.T.S.
PROJECT NO.:	XXXX
REV NO.:	XXXX
DRAWING NAME:	HPER91.DWG



FIRE ALARM SYSTEM
FLOOR PLAN
DEVICE NUMBERS

NFS:
91

DEVICE LEGEND	
SYMBOL	DESCRIPTION
⊙	SMOKE DETECTOR
⊙ _{vp}	THERMAL DETECTOR
⊞	MANUAL PULL STATION
⊞ _{vp}	DUCT SMOKE DETECTOR
⊞ _{vp}	WATERFLOW SWITCH MONITOR MODULE
⊞ _{vp}	TAMPER SWITCH MONITOR MODULE
⊞ _{vp}	RELAY- ARB-C


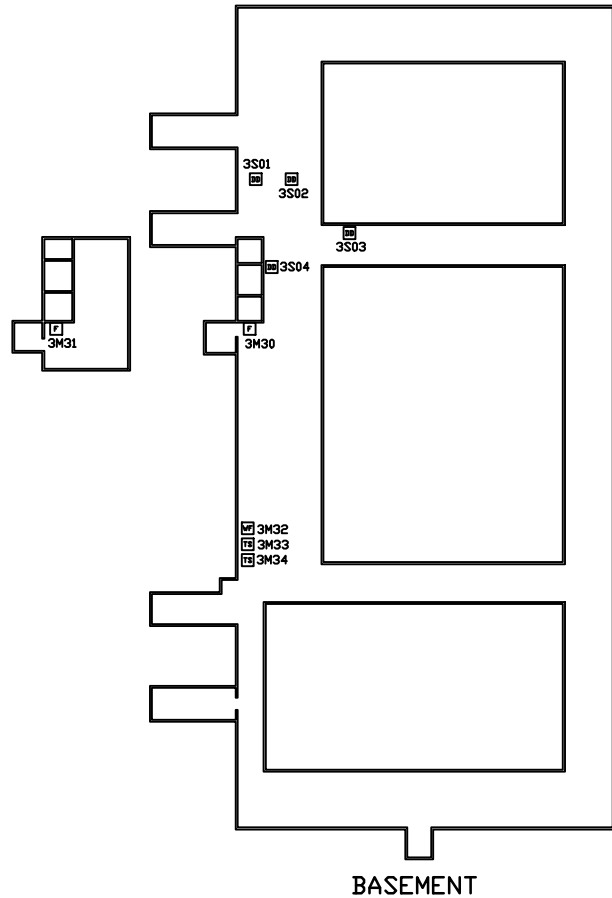


KEY PLAN

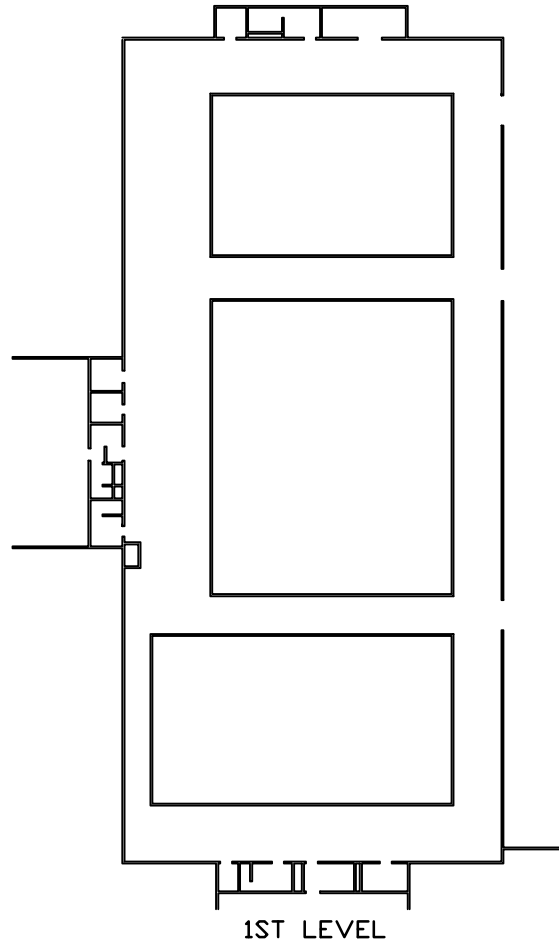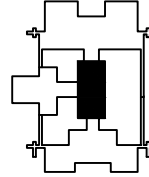

ADDRESS LABEL CLARIFICATION

ADDRESSABLE LOOP NUMBER
SENSOR ("M" MONITOR)
DEVICE NUMBER

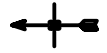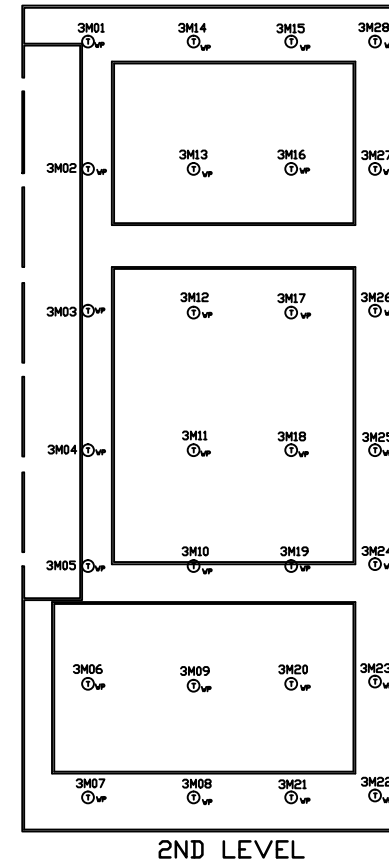

NOTE:
NFS DRAWINGS ARE BASED ON THE PROJECT
PROVIDED INFORMATION AND ASSUMPTIONS
(NOT NFS) FOR THE TYPE, SIZE, LOCATION, AND
PURPOSE OF THE SYSTEM. NFS IS NOT RESPONSIBLE
FOR THE ACCURACY OF THE INFORMATION, DIMENSIONS,
AND OTHER DEVICES SHOWN ON THE A/E PLANS.
NFS DRAWINGS ARE TO SHOW ONLY THE WIRING
AND NOT THE LOCATION OF THE DEVICES. NFS IS NOT RESPONSIBLE FOR
THE INFORMATION SHOWN ON THE A/E PLANS.

HPER COMPLEX
BUILDING #93
UNIVERSITY OF UTAH
FIRE ALARM SYSTEM


NFS
NELSON FIRE SYSTEMS
801-468-8500

DRAWN BY: TCT
DESIGNED BY: XXXXX
APPROVED BY: OPS
DATE: 4/06/04
SCALE: N.T.S.
PROJECT NO: XXXXX
REV NO: XXXXX
DRAWING NAME: HPER93.DWG


FIRE ALARM SYSTEM
FLOOR PLAN
DEVICE NUMBERS

NFS:
93


ADDRESS LABEL CLARIFICATION

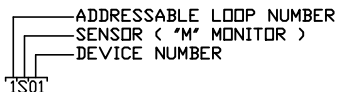

FIRST LEVEL

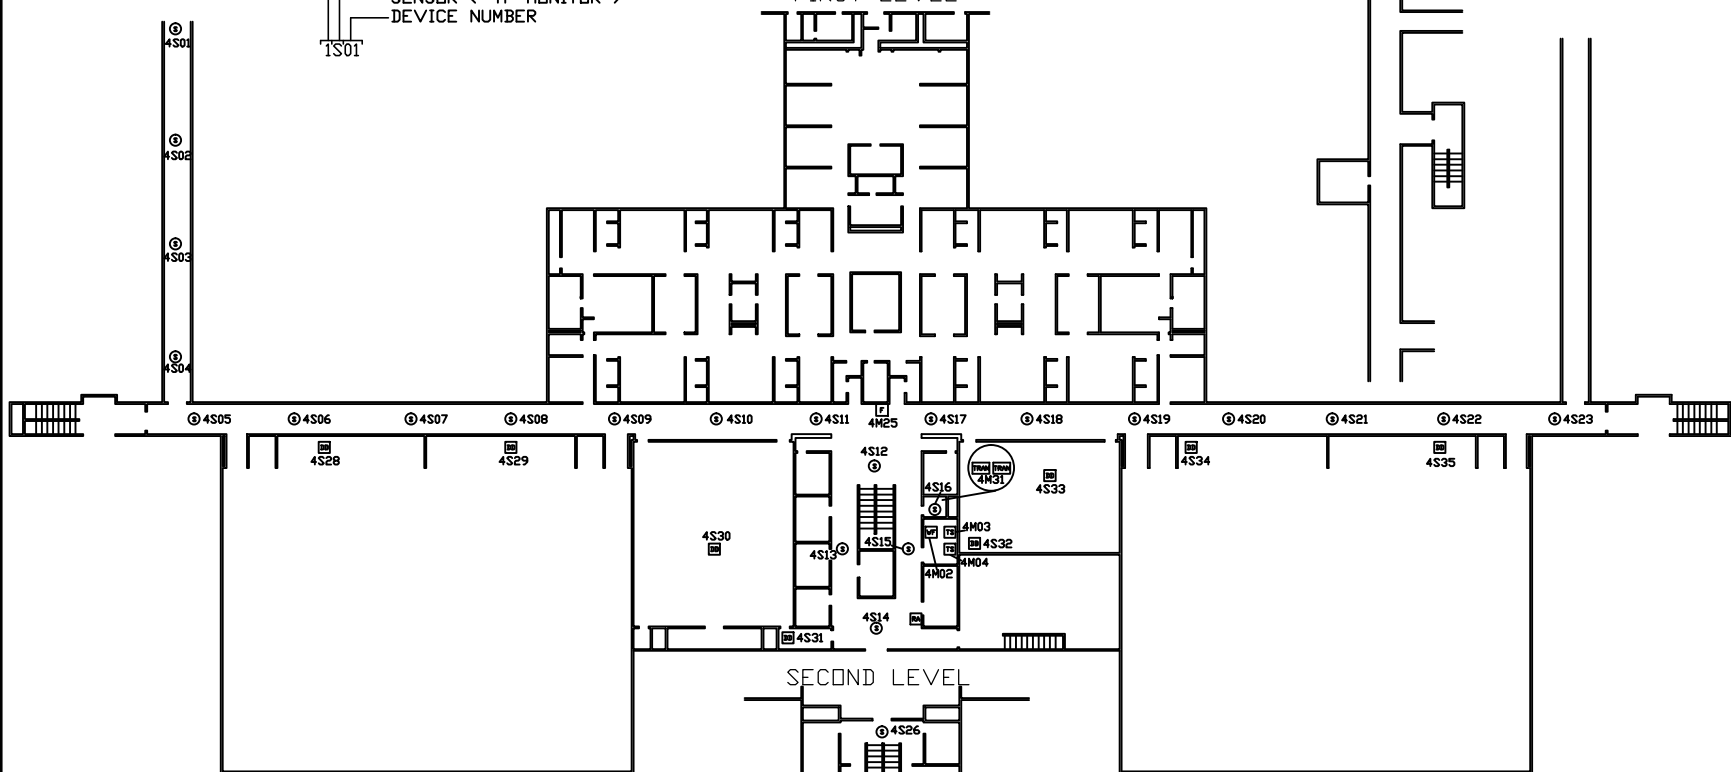


SECOND LEVEL

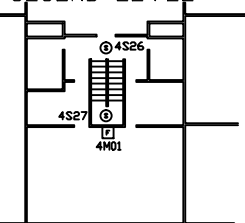

MEZZANINE

KEY PLAN

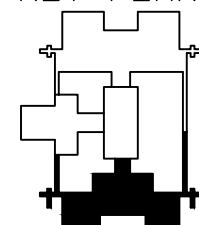

DEVICE LEGEND

SYMBOL	DESCRIPTION
⊙	SMOKE DETECTOR W/BASE
□	MANUAL PULL STATION
▣	DUCT SMOKE DETECTOR
▤	WATERFLOW SWITCH MONITOR MODULE
▥	TAMPER SWITCH MONITOR MODULE
▦	RELAY
▧	REMOTE ANNUNCIATOR
▨	TRANSPONDER PANEL



NOTE:
NFS DRAWINGS ARE BASED ON THE PROJECT INFORMATION PROVIDED BY THE CLIENT. NFS ASSUMES NO RESPONSIBILITY FOR THE ACCURACY OF THE INFORMATION PROVIDED BY THE CLIENT. NFS IS NOT RESPONSIBLE FOR THE INFORMATION SHOWN ON THE A/E PLANS.


HPER COMPLEX
BUILDING #94
UNIVERSITY OF UTAH
FIRE ALARM SYSTEM

NFS
NELSON FIRE SYSTEMS
801-468-8300

DRAWN BY: TCT
DESIGNED BY: XXXX
APPROVED BY: OPS
DATE: 11/14/03
SCALE: N.T.S.
PROJECT NO: XXXX
REV NO: XXXX
DRAWING NAME: HPER94.DWG

FIRE ALARM SYSTEM
FLOOR PLAN
DEVICE NUMBERS

NFS:
94

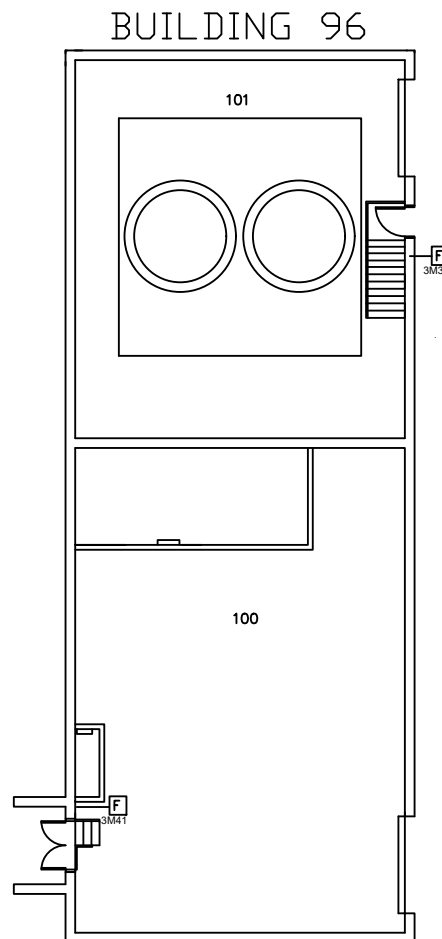

DEVICE LEGEND	
DESCRIPTION	
SMOKE DETECTOR W/BASE	
MANUAL PULL STATION	
DUCT SMOKE DETECTOR	
WATERFLOW SWITCH MONITOR MODULE	
TAMPER SWITCH MONITOR MODULE	
RELAY- ARB-C	
REMOTE ANNUNCIATOR	
TRANSPONDER PANEL	

ADDRESS LABEL CLARIFICATION
ADDRESSABLE LOOP NUMBER
SENSOR ("M" MONITOR)

NOTE: THE DRAWINGS ARE BASED ON THE PROJECT ARCHITECT/ENGINEER (A/E) PLANS AND SPECIFICATIONS. A/E IS SOLELY RESPONSIBLE FOR THE ACCURACY OF THE TYPE, SIZE, LOCATION, AND NUMBER OF ALL FIRE ALARMS, CONTROL PANELS, AND OTHER DEVICES SHOWN ON THE A/E PLANS. THE DRAWINGS ARE TO SHOW ONLY THE WIRING CONNECTIONS. THE A/E IS NOT RESPONSIBLE FOR THE INFORMATION SHOWN ON THE A/E PLANS.

HPER COMPLEX
BUILDING #95 & 96
UNIVERSITY OF UTAH
FIRE ALARM SYSTEM

NFS
NELSON FIRE SYSTEMS
801-468-8300

DRAWN BY:	TCT
DESIGNED BY:	XXXX
APPROVED BY:	DPS
DATE:	4/06/04
SCALE:	N.T.S.
PROJECT NO:	XXXX
REV NO:	XXXX
DRAWING NAME:	

HPER9L.DWG

FIRE ALARM SYSTEM
FLOOR PLAN
DEVICE NUMBERS

NFS: