



LEVEL 1

DEVICE LEGEND	
SYMBOL	DESCRIPTION
	SMOKE DETECTOR
	HEAT DETECTOR
	PULL STATION
	DUCT DETECTOR
	WATER FLOW SWITCH MODULE
	TAMPER SWITCH MODULE
	FIRE EXTINGUISHER
	FIRE ALARM CONTROL UNIT
	TRANSPONDER PANEL



NOTE: NFS DRAWINGS ARE BASED ON THE PROJECT ARCHITECTURE/ENGINEER (A/E) PLANS AND SPECIFICATIONS FURNISHED TO NFS. A/E IS SOLELY RESPONSIBLE (NOT NFS) FOR THE TYPE, SIZE, LOCATION, AND SUITABILITY OF ALL FIRE ALARMS, CONTROL PANELS, AND OTHER DEVICES SHOWN ON THE A/E PLANS. NFS DRAWINGS ARE TO SHOW ONLY THE WIRING DIAGRAMS BETWEEN FIRE ALARM DEVICES AND CONTROL PANELS. NFS IS NOT RESPONSIBLE FOR THE INFORMATION SHOWN ON THE A/E PLANS.

97 DUMKE GYMNASTICS
UNIVERSITY OF UTAH
1825 E. SOUTH CAMPUS DRIVE
SALT LAKE CITY, UT 84112
FIRE ALARM SYSTEM

NFS

NELSON FIRE SYSTEMS
801-468-8300

DRAWN BY:	BH
DESIGNED BY:	XXXX
APPROVED BY:	KK
DATE:	09/07/2023
SCALE:	N.T.S.
PROJECT NO:	XXXX
REVISION NO:	XXXX
DRAWING NAME:	DUMKE GYMNASTICS 1 FM.DWG

NELSON FIRE SYSTEMS

LEVEL 1

PAGE:

FINAL MAP





97 DUMKE GYMNASICS
UNIVERSITY OF UTAH
1825 E. SOUTH CAMPUS DRIVE
SALT LAKE CITY, UT 84112
FIRE ALARM SYSTEM


NFS

DRAWN BY:	BH
DESIGNED BY:	XXXX
APPROVED BY:	KK
DATE:	09/07/2023
SCALE:	N.T.S.
PROJECT NO:	XXXX
REVISION NO:	XXXX
DRAWING NAME:	DUMKE GYMNASTICS 2 FM.DWG

LEVEL 2

FINAL MAP



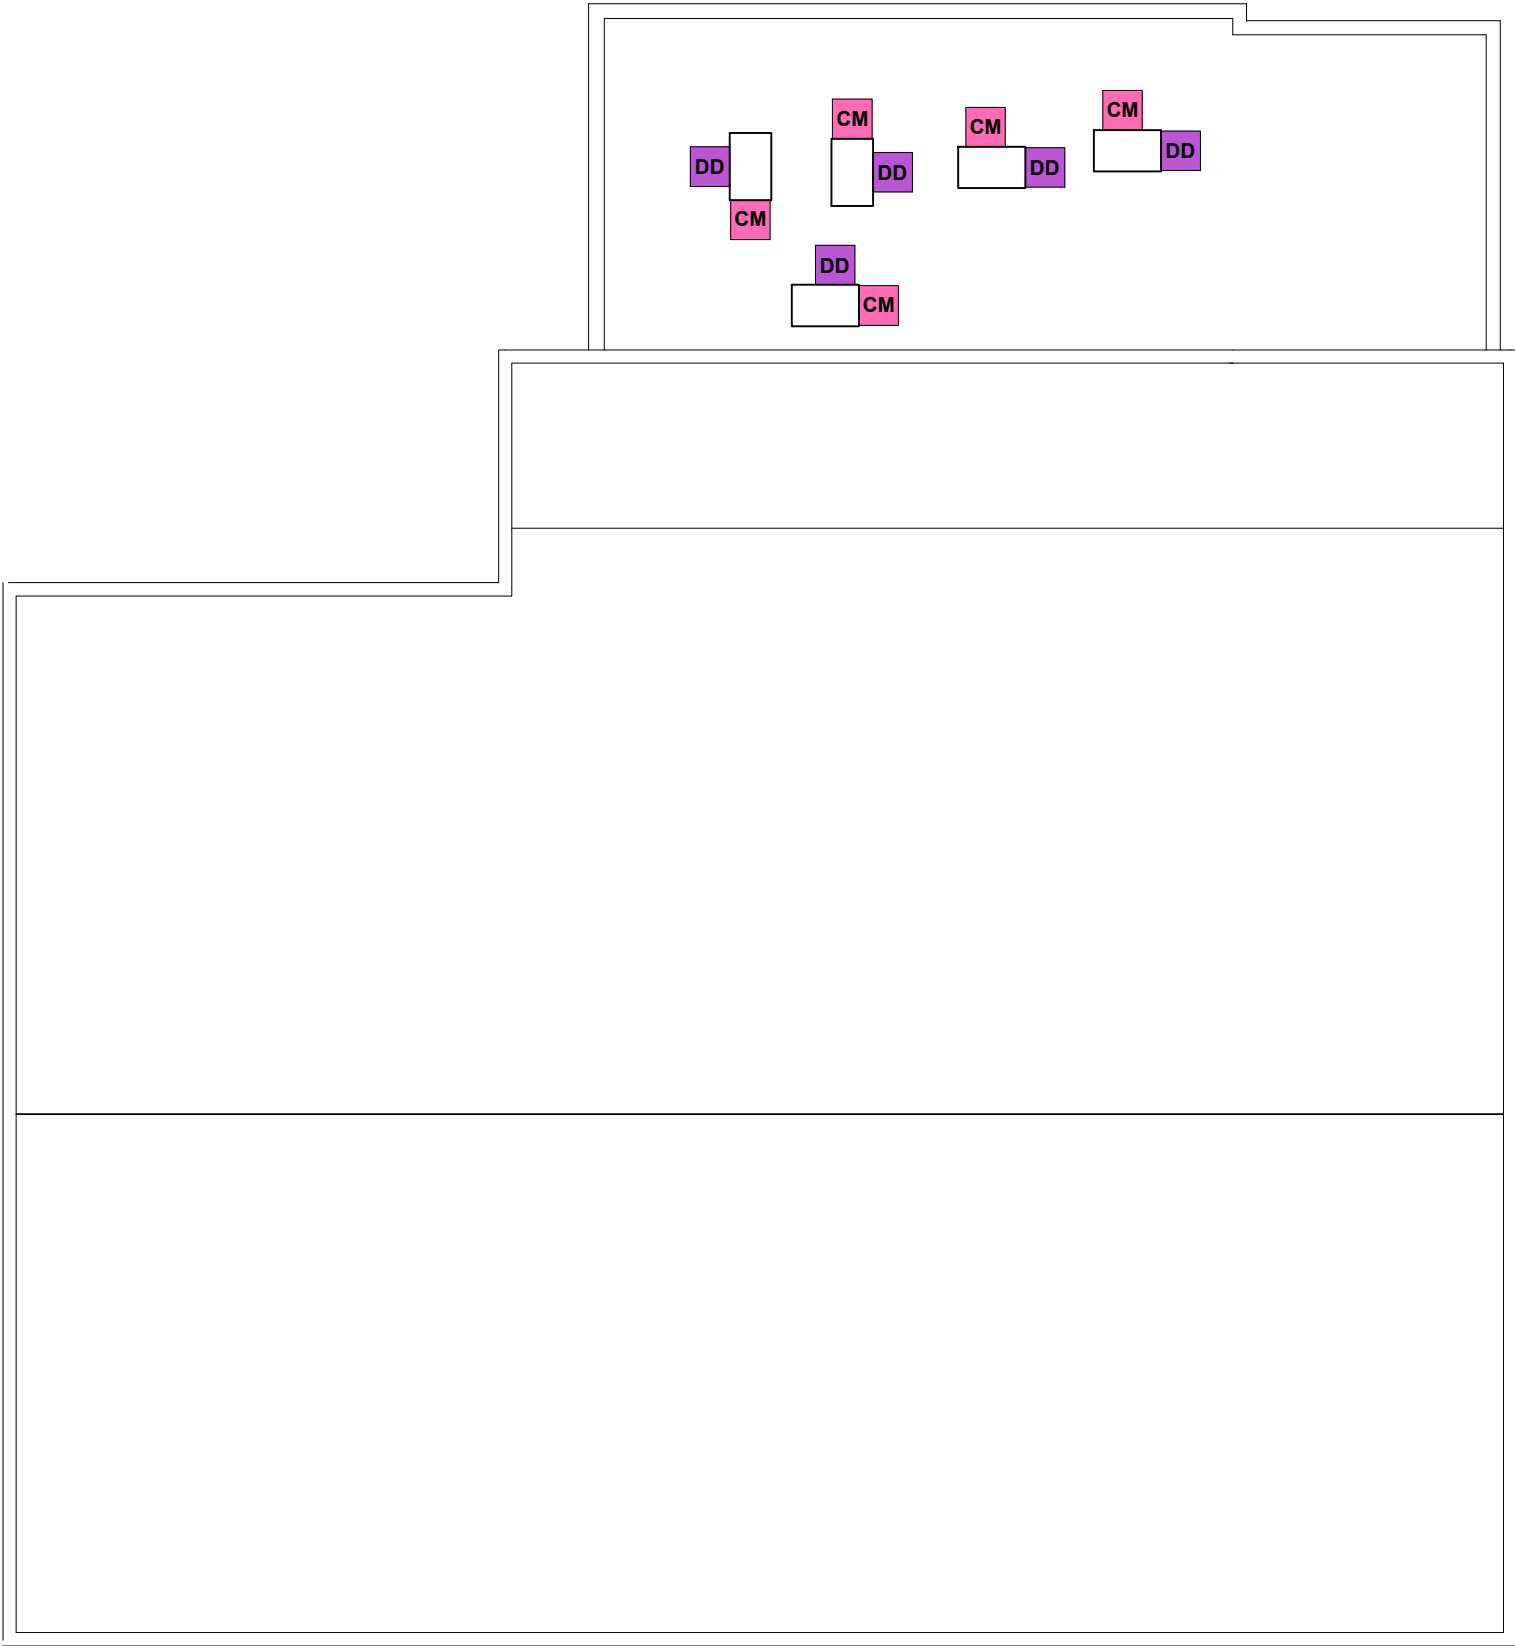

ROOFTOP

DEVICE LEGEND	
SYMBOL	DESCRIPTION
DD	DUCT DETECTOR
CM	CONTROL MODULE



NOTE:
NFS DRAWINGS ARE BASED ON THE PROJECT ARCHITECTURE/ENGINEER (A/E) PLANS AND SPECIFICATIONS FURNISHED TO NFS. A/E IS SOLELY RESPONSIBLE (NOT NFS) FOR THE TYPE, SIZE, LOCATION, AND SUITABILITY OF ALL FIRE ALARMS, CONTROL PANELS, AND OTHER DEVICES SHOWN ON THE A/E PLANS. NFS DRAWINGS ARE TO SHOW ONLY THE WIRING DIAGRAMS BETWEEN FIRE ALARM DEVICES AND CONTROL PANELS. NFS IS NOT RESPONSIBLE FOR THE INFORMATION SHOWN ON THE A/E PLANS.

97 DUMKE GYMNASTICS
UNIVERSITY OF UTAH
1825 E. SOUTH CAMPUS DRIVE
SALT LAKE CITY, UT 84112
FIRE ALARM SYSTEM

NFS
NELSON FIRE SYSTEMS
801-468-8300

DRAWN BY:	BH
DESIGNED BY:	XXXX
APPROVED BY:	KK
DATE:	09/07/2023
SCALE:	N.T.S.
PROJECT NO:	XXXX
REVISION NO:	XXXX
DRAWING NAME:	

DUMKE GYMNASTICS ROOF FM.DWG

NELSON FIRE SYSTEMS
ROOFTOP

PAGE:
FINAL MAP

