


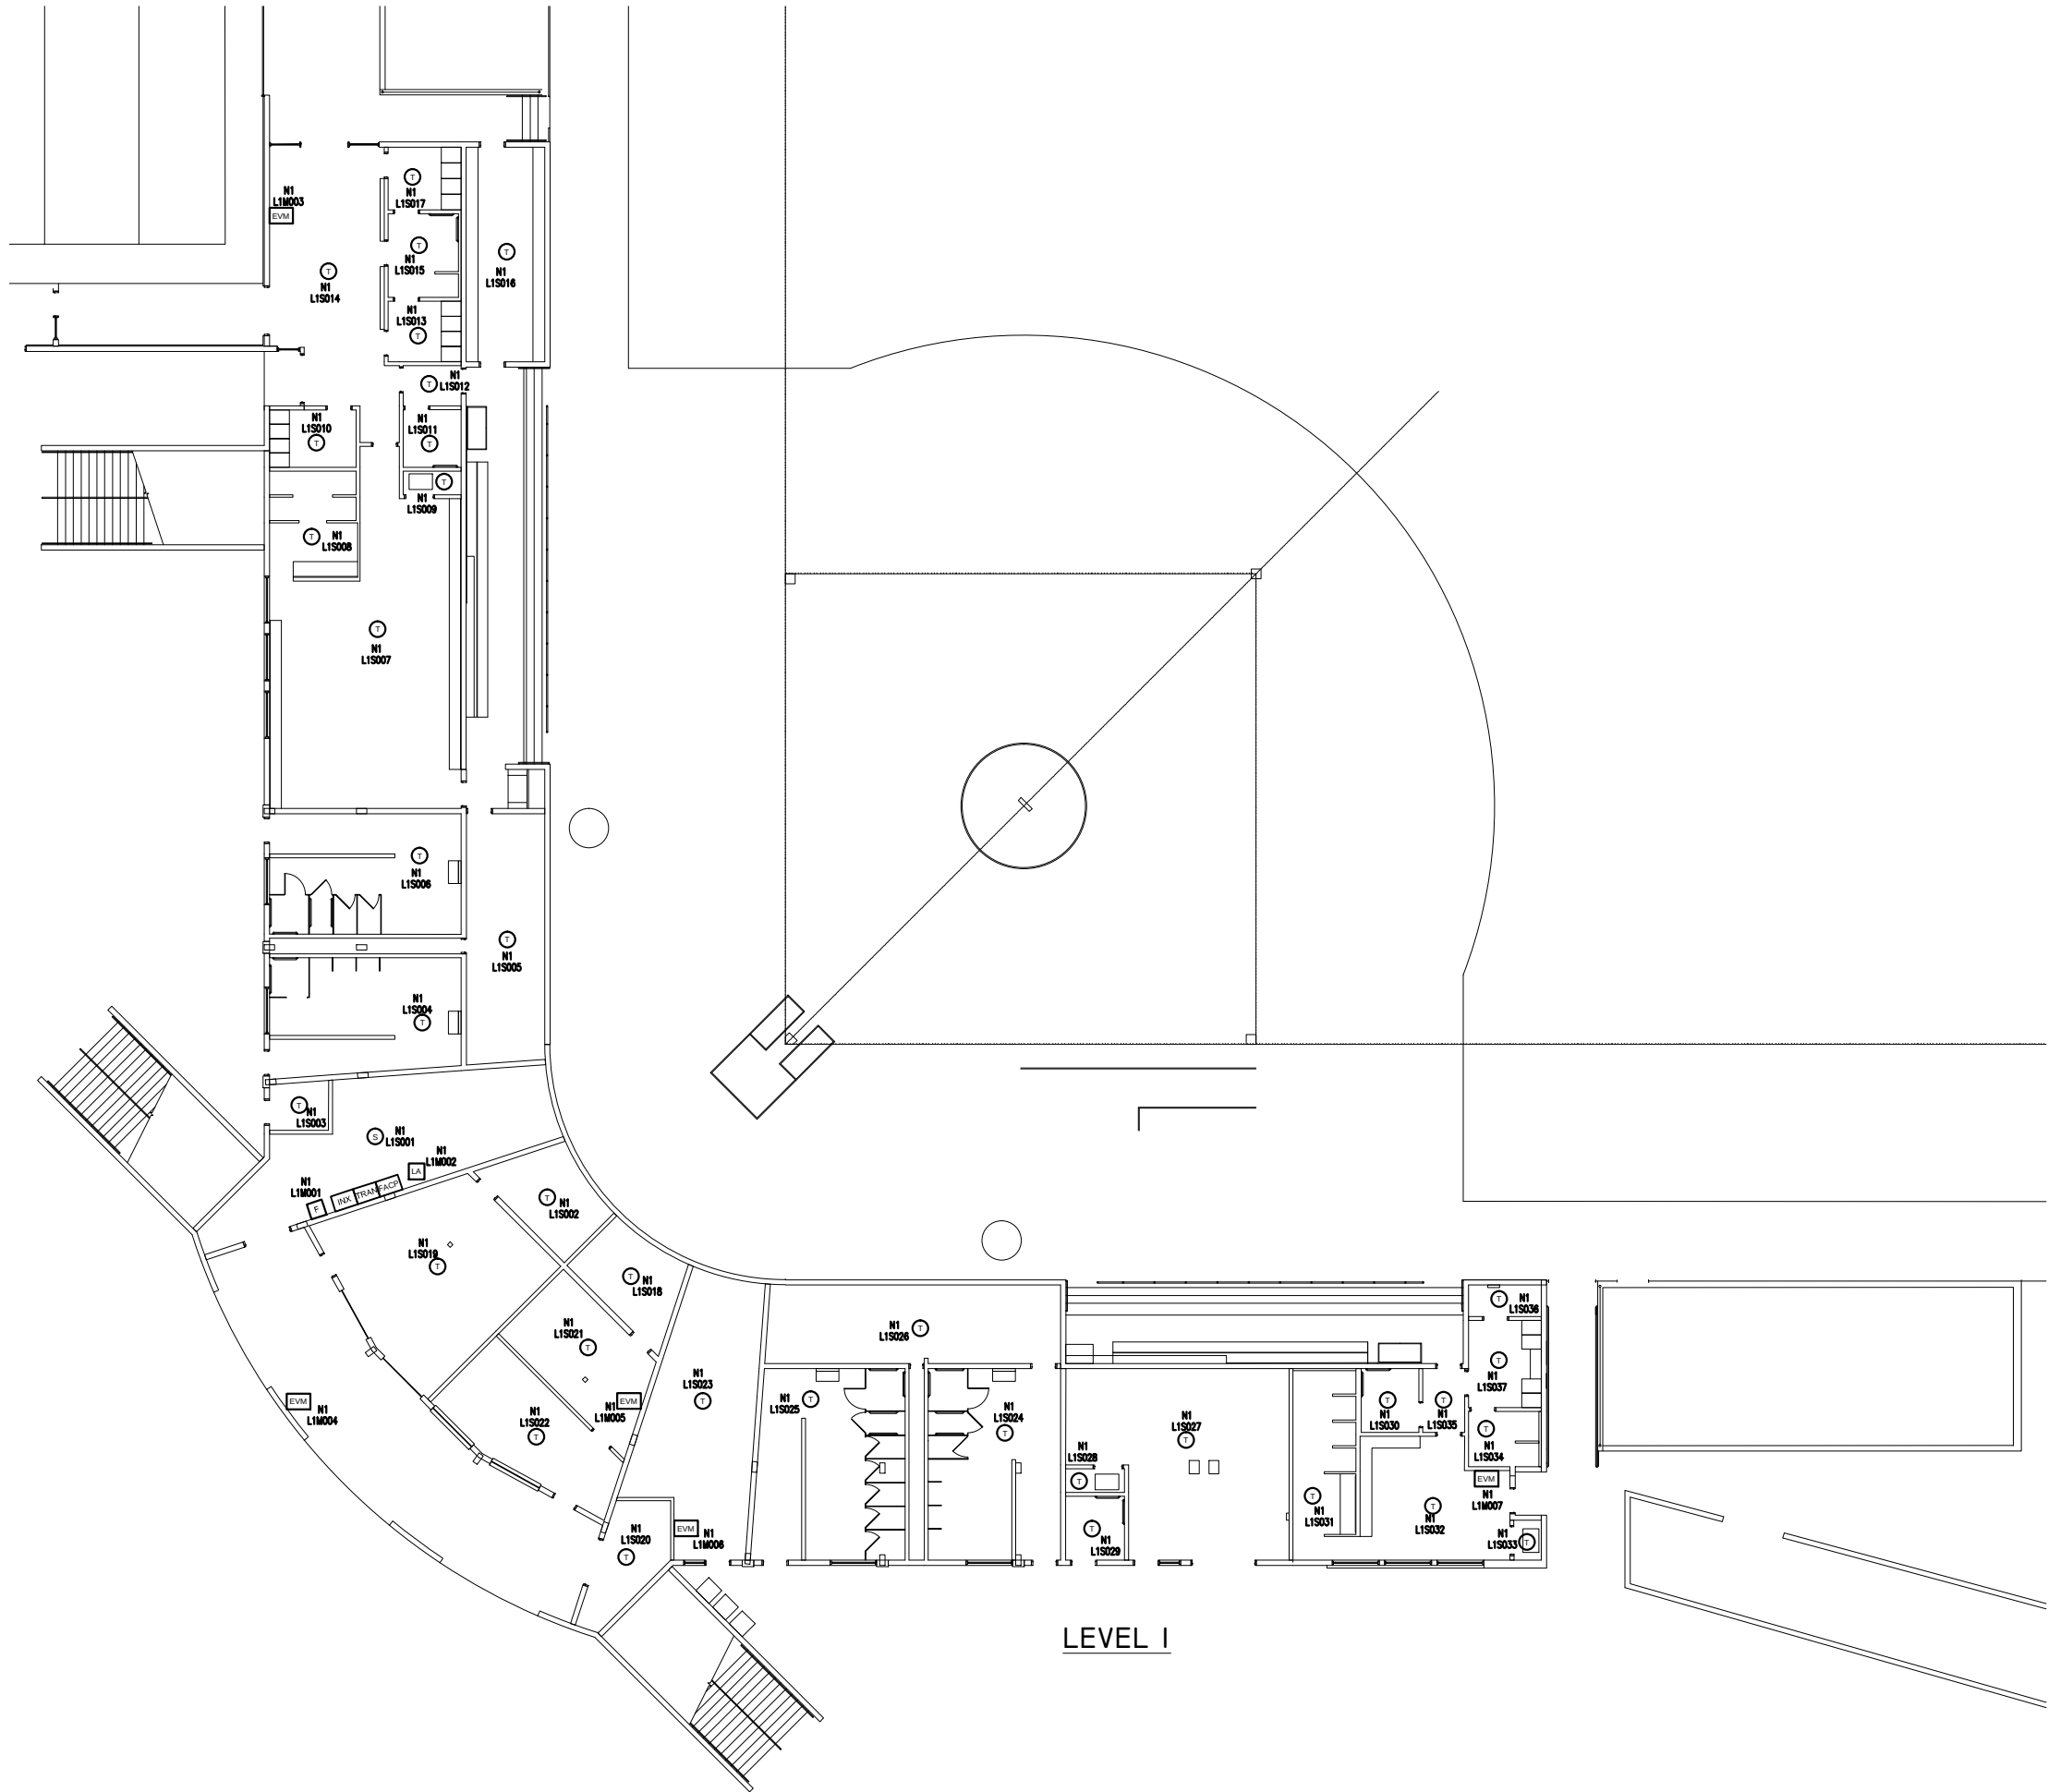

LEVEL I

DEVICE LEGEND	
SYMBOL	DESCRIPTION
	SMOKE DETECTOR
	PULL STATION
	DUCT DETECTOR
	CONTROL MODULE
	LOW AIR TEMPERATURE SENSOR
	REMOTE ANNUNCIATOR
	FIRE ALARM CONTROL PANEL
	TRANSPONDER PANEL
	VOICE PANEL
	ENGAGE FIRE EXTINGUISHER MODULE

NOTE:
NFS DRAWINGS ARE BASED ON THE PROJECT
ARCHITECT/ENGINEER (A/E) PLANS AND SPECIFICATIONS
FURNISHED TO NFS. A/E IS SOLELY RESPONSIBLE
(NOT NFS) FOR THE TYPE, SIZE, LOCATION, AND
SUITABILITY OF ALL FIRE ALARMS, CONTROL PANELS,
AND OTHER DEVICES SHOWN ON THE A/E PLANS.
NFS DRAWINGS ARE TO SHOW ONLY THE WIRING
DIAGRAMS BETWEEN FIRE ALARM DEVICES AND
CONTROL PANELS. NFS IS NOT RESPONSIBLE FOR
THE INFORMATION SHOWN ON THE A/E PLANS.

ATHLETICS DEPARTMENT WOMEN'S SOFTBALL
UNIVERSITY OF UTAH
WOMEN'S SOFTBALL STADIUM
SALT LAKE CITY, UTAH 84112
FIRE ALARM SYSTEM

NFS
NELSON FIRE SYSTEMS
801-468-8300

DRAWN BY: JYG
DESIGNED BY: XXXX
APPROVED BY: DPS
DATE: 8/29/13
SCALE: N.T.S.
PROJECT NO: XXXX
REV NO: XXXX
DRAWING NAME:
SOFTBALL 1ST FM.DWG

FIRE ALARM SYSTEM
LEVEL I

PAGE:

FA-I

N.I.C.E.T.
LEVEL IV
CERTIFICATION
FIRE ALARM SYSTEMS
DONNY SCHULTZ
#104396

