





N.I.C.E.T.
LEVEL IV
CERTIFICATION
FIRE ALARM SYSTEMS
DONNY SCHULTZ
#104396

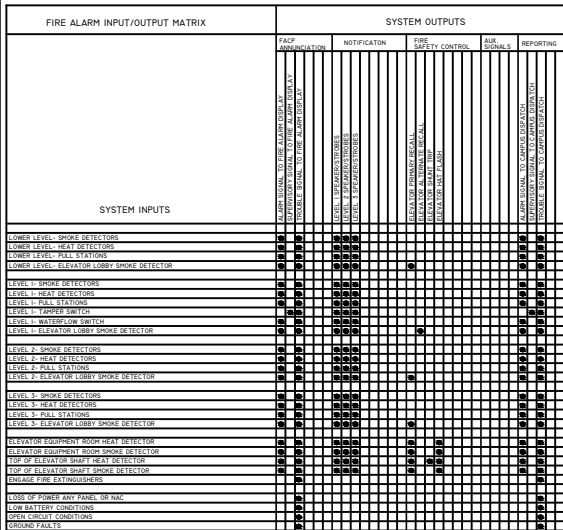

NOTE:
NFS DRAWINGS ARE BASED ON THE PROJECT ARCHITECT/ENGINEER (A/E) PLANS AND SPECIFICATIONS FURNISHED TO NFS. A/E IS SOLELY RESPONSIBLE (NOT NFS) FOR THE TYPE, SIZE, LOCATION, AND SUITABILITY OF ALL FIRE ALARMS, CONTROL PANELS, AND OTHER DEVICES SHOWN ON THE A/E PLANS. NFS DRAWINGS ARE TO SHOW ONLY THE WIRING DIAGRAMS BETWEEN FIRE ALARM DEVICES AND CONTROL PANELS. NFS IS NOT RESPONSIBLE FOR THE INFORMATION SHOWN ON THE A/E PLANS.

DEVICE LEGEND	
SYMBOL	DESCRIPTION
③	SMOKE DETECTOR
①	HEAT DETECTOR
① 190°	HIGH TEMP. HEAT DETECTOR
F	MANUAL PULL STATION
DD	DUCT DETECTOR
TS	TAMPER SWITCH
WF	WATERFLOW SWITCH
FE	FIRE EXTINGUISHER
CM	CONTROL MODULE
R	RELAY
RA	REMOTE ANNUNCIATOR
TRAN	TRANSPONDER PANEL
FACP	FIRE ALARM CONTROL PANEL
INX	VOICE PANEL
CC	COMMAND CENTER

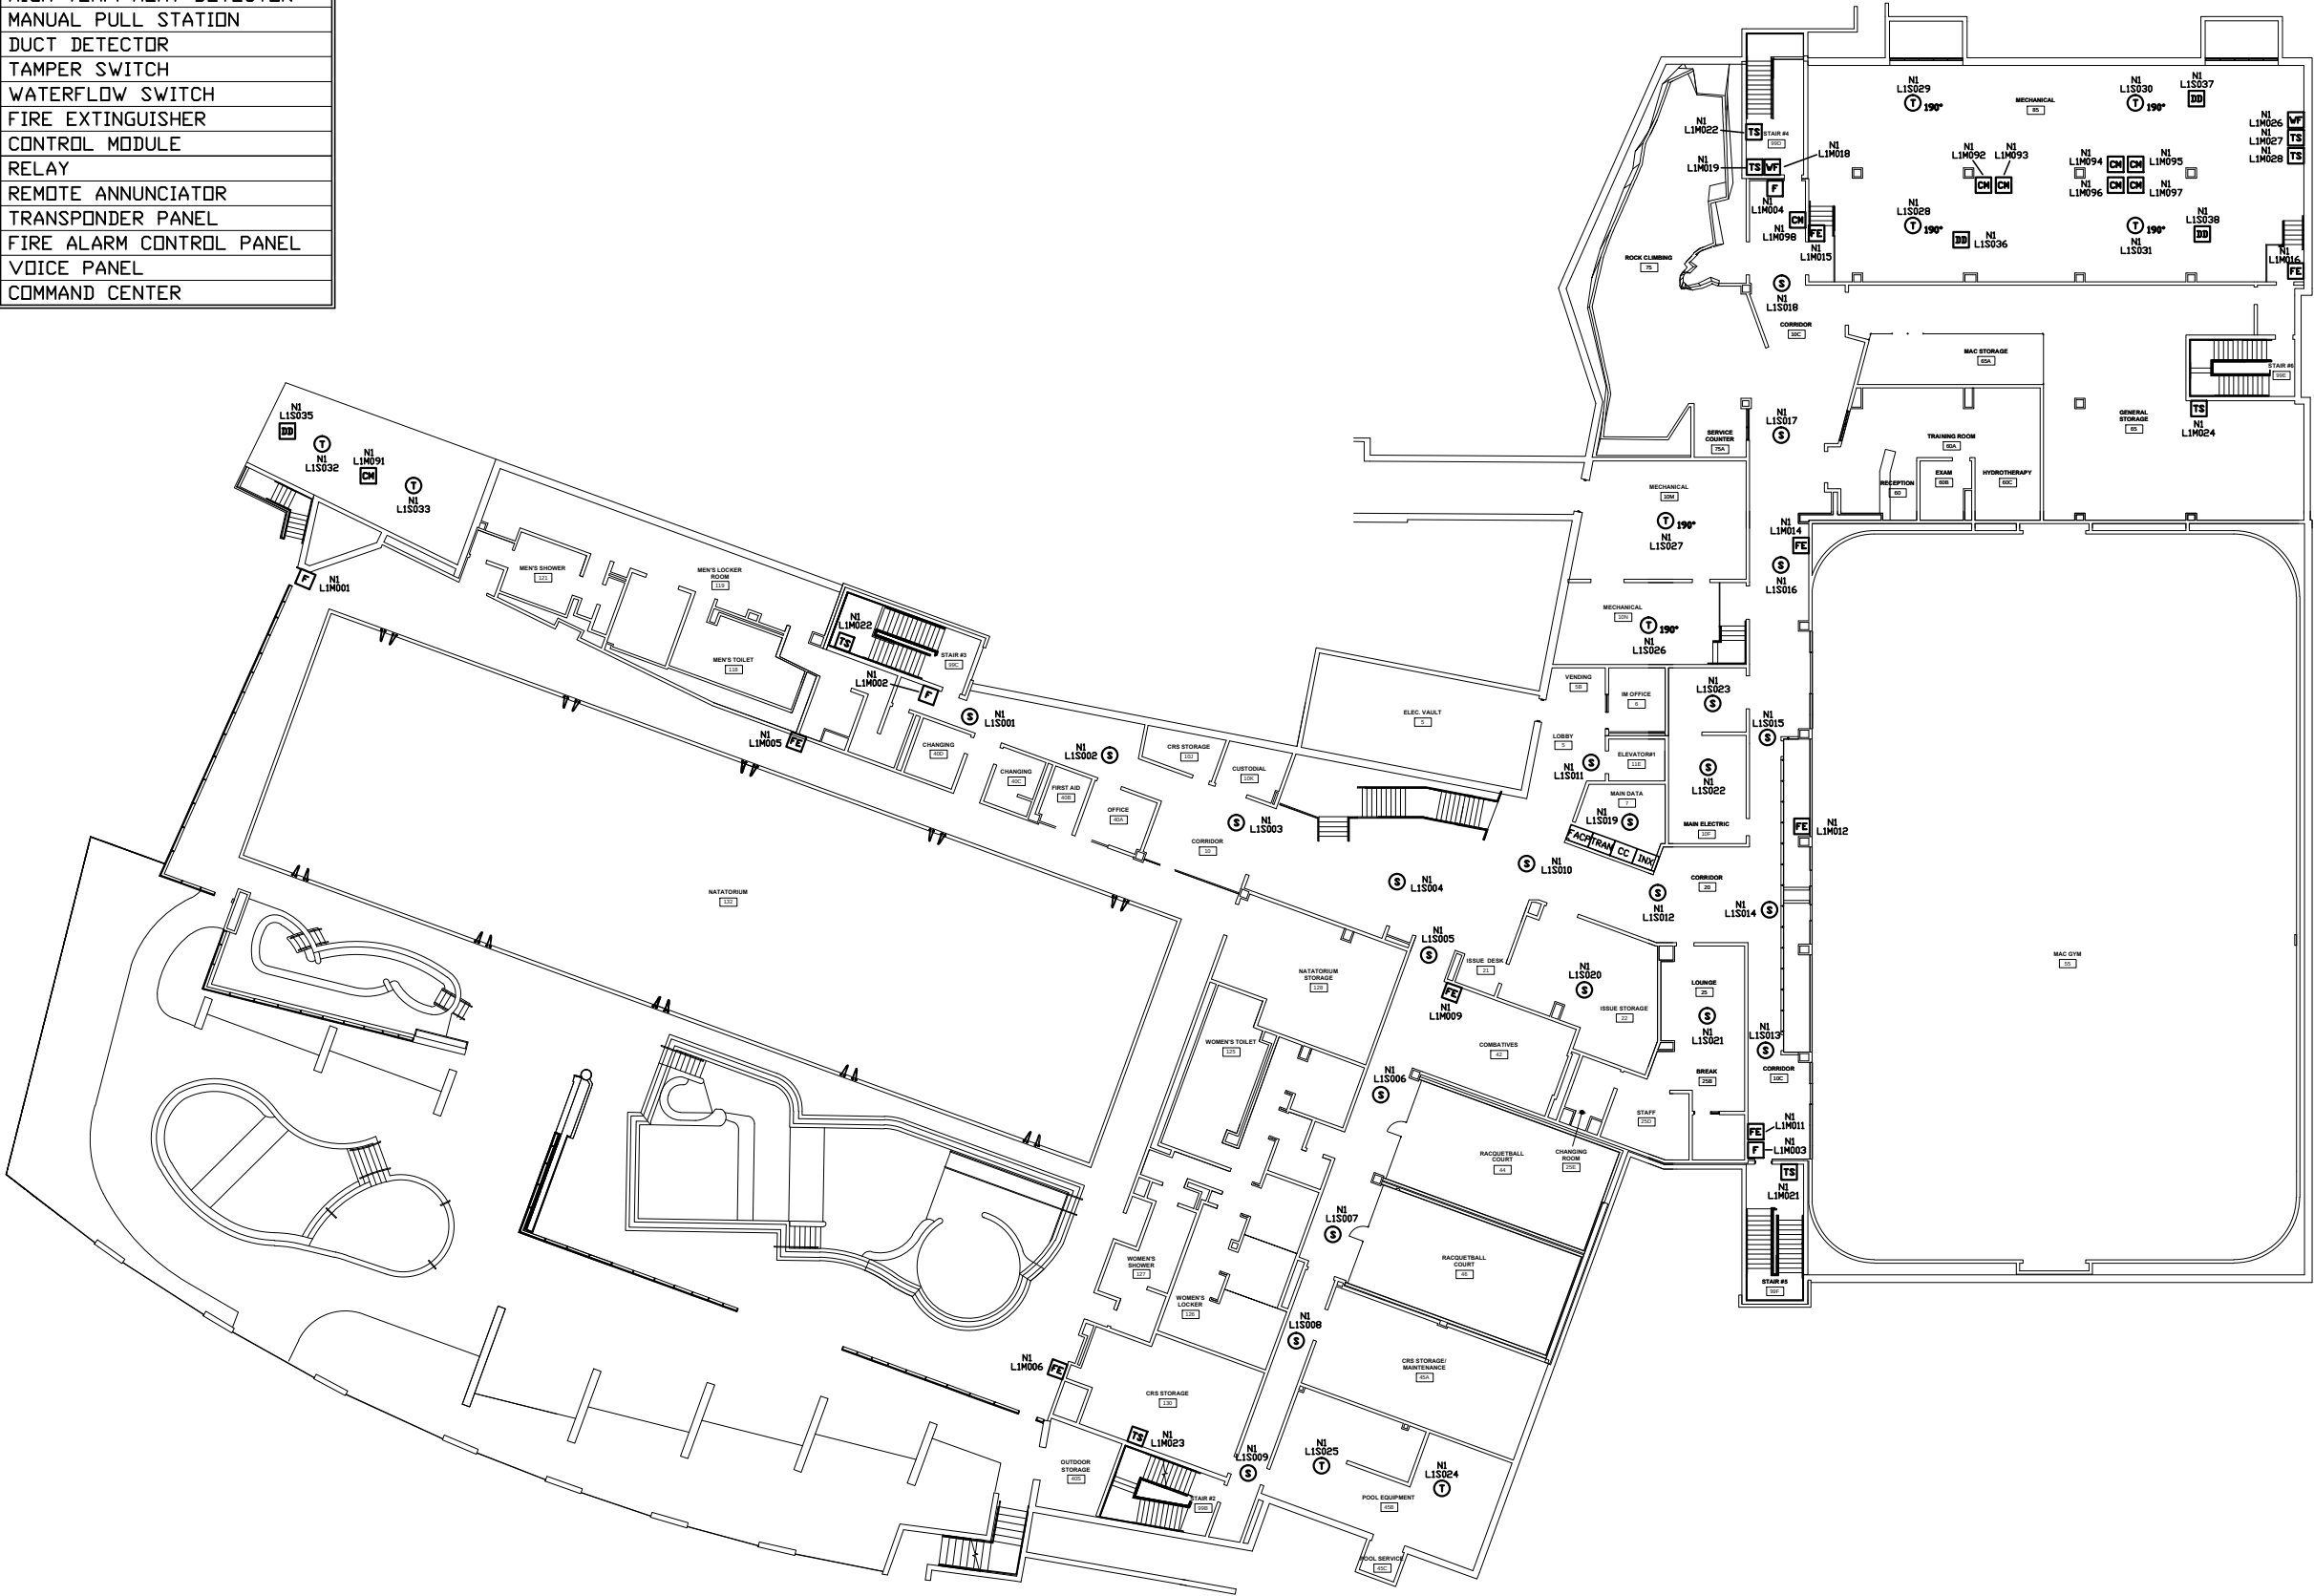

0' 5' 10' 15' 25' 50'
SCALE

N.I.C.E.T.
LEVEL IV
CERTIFICATION
FIRE ALARM SYSTEMS
DONNY SCHULTZ
#043396

UNIVERSITY OF UTAH
STUDENT LIFE CENTER
LOWER LEVEL
1836 BALLIF ROAD
SALT LAKE CITY, UTAH
FIRE ALARM SYSTEM

NFS

NELSON FIRE SYSTEMS
801-468-8300




DRAWN BY: AK
DESIGNED BY: XXXX
APPROVED BY: DS
DATE: 12/6/14
SCALE: (ARCH C) N.T.S.
PROJECT NO: XXXX
REV NO: XXXX
DRAWING NAME:
UofU STUDENT CENTER LFM.DWG

FIRE ALARM SYSTEM
LOWER LEVEL
NUMBERS

PAGE:
FA-L

NOTE:
NFS DRAWINGS ARE BASED ON THE PROJECT
ARCHITECT/ENGINEER (A/E) PLANS AND SPECIFICATIONS
FURNISHED TO NFS. A/E IS SOLELY RESPONSIBLE
(NOT NFS) FOR THE TYPE, SIZE, LOCATION, AND
SUITABILITY OF ALL FIRE ALARMS, CONTROL PANELS,
AND OTHER DEVICES SHOWN ON THE A/E PLANS.
NFS DRAWINGS ARE TO SHOW ONLY THE WIRING
DIAGRAMS BETWEEN FIRE ALARM DEVICES AND
CONTROL PANELS. NFS IS NOT RESPONSIBLE FOR
THE INFORMATION SHOWN ON THE A/E PLANS.

DEVICE LEGEND	
SYMBOL	DESCRIPTION
(S)	SMOKE DETECTOR
(T)	HEAT DETECTOR
(T) 190°	HIGH TEMP. HEAT DETECTOR
(F)	MANUAL PULL STATION
(DD)	DUCT DETECTOR
(TS)	TAMPER SWITCH
(VF)	WATERFLOW SWITCH
(FE)	FIRE EXTINGUISHER
(CH)	CONTROL MODULE
(R)	RELAY
(RA)	REMOTE ANNUNCIATOR
(TRAN)	TRANSPONDER PANEL
(FACP)	FIRE ALARM CONTROL PANEL
(INX)	VOICE PANEL
(CC)	COMMAND CENTER

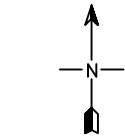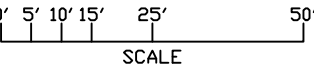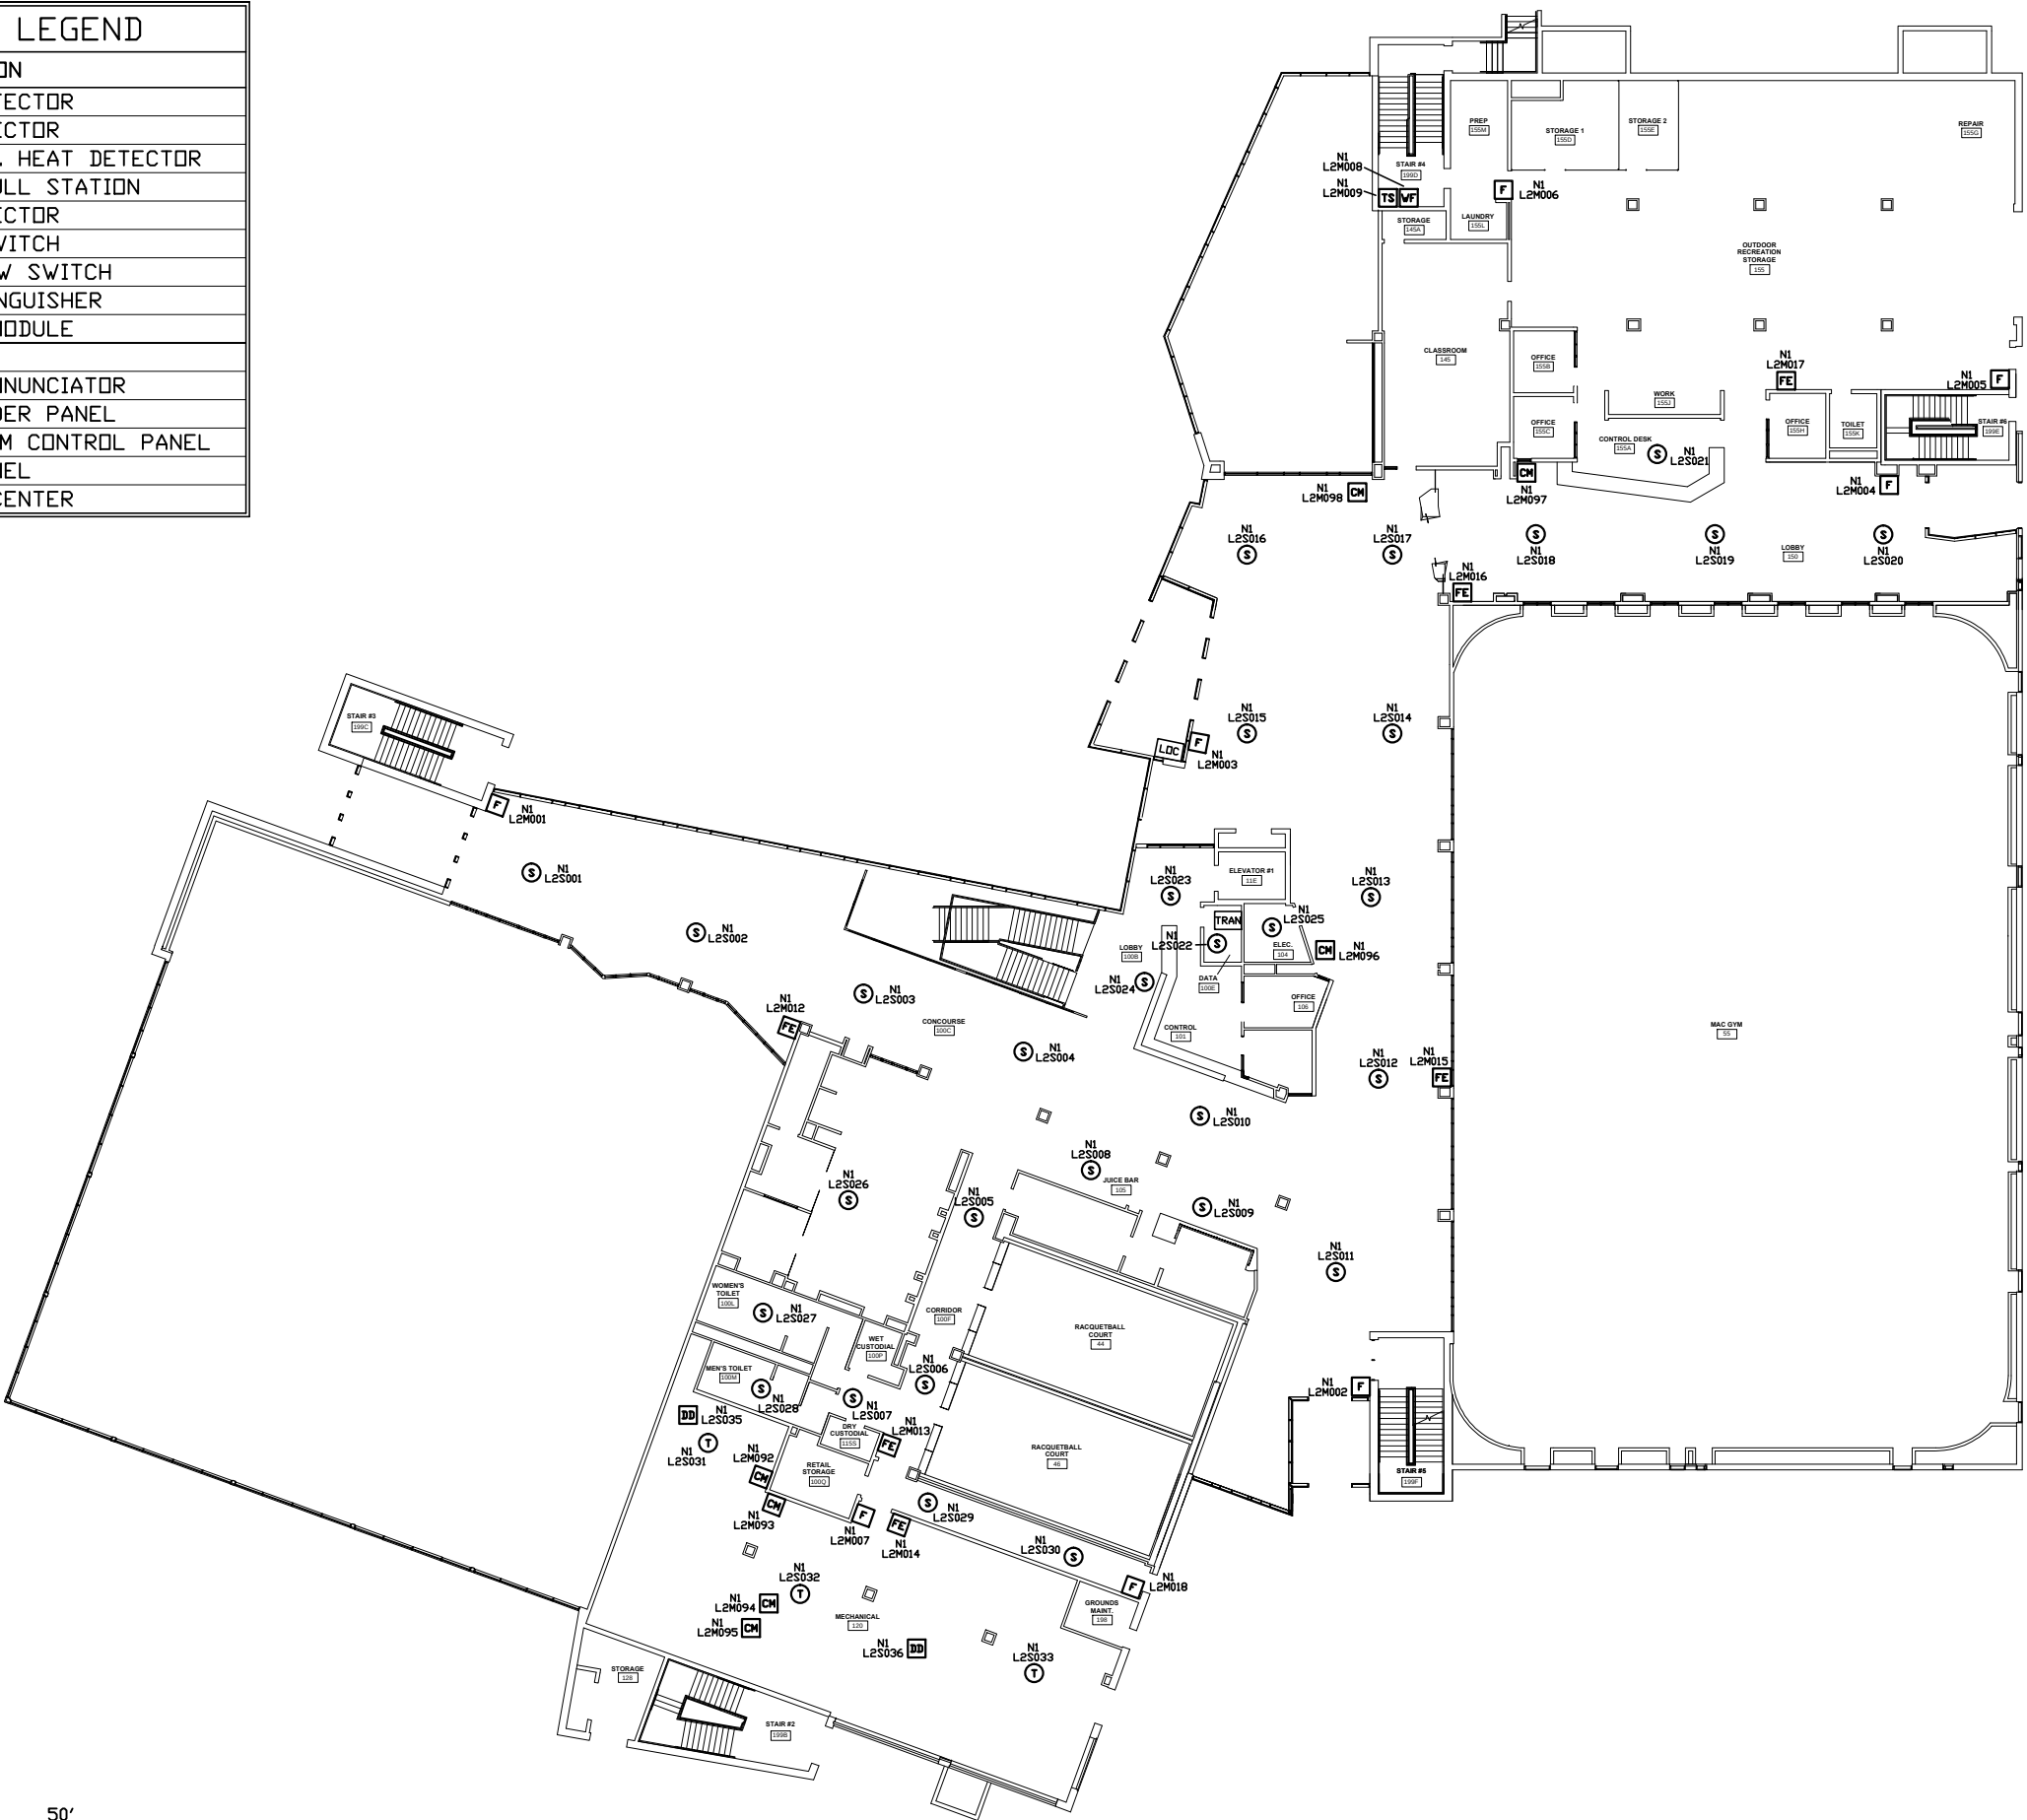

NOTE:
NFS DRAWINGS ARE BASED ON THE PROJECT
ARCHITECT/ENGINEER (A/E) PLANS AND SPECIFICATIONS
FURNISHED TO NFS. A/E IS SOLELY RESPONSIBLE
(NOT NFS) FOR THE TYPE, SIZE, LOCATION, AND
SUITABILITY OF ALL FIRE ALARMS, CONTROL PANELS,
AND OTHER DEVICES SHOWN ON THE A/E PLANS.
NFS DRAWINGS ARE TO SHOW ONLY THE WIRING
DIAGRAMS BETWEEN FIRE ALARM DEVICES AND
CONTROL PANELS. NFS IS NOT RESPONSIBLE FOR
THE INFORMATION SHOWN ON THE A/E PLANS.

UNIVERSITY OF UTAH
STUDENT LIFE CENTER
LEVEL I
1836 BALLIF ROAD
SALT LAKE CITY, UTAH
FIRE ALARM SYSTEM


NFS
NELSON FIRE SYSTEMS
801-468-8300

DRAWN BY:	AK
DESIGNED BY:	XXXX
APPROVED BY:	DS
DATE:	12/6/14
SCALE:	(ARCH C) N.T.S.
PROJECT NO:	XXXX
REV NO:	XXXX
DRAWING NAME:	UofU STUDENT CENTER IFM.DWG

FIRE ALARM SYSTEM
LEVEL I
NUMBERS

PAGE:
FA-I

DEVICE LEGEND	
SYMBOL	DESCRIPTION
Ⓢ	SMOKE DETECTOR
Ⓣ	HEAT DETECTOR
Ⓣ 190°	HIGH TEMP. HEAT DETECTOR
F	MANUAL PULL STATION
DD	DUCT DETECTOR
TS	TAMPER SWITCH
WF	WATERFLOW SWITCH
FE	FIRE EXTINGUISHER
CM	CONTROL MODULE
R	RELAY
RA	REMOTE ANNUNCIATOR
TRAN	TRANSPONDER PANEL
FACP	FIRE ALARM CONTROL PANEL
INX	VOICE PANEL
CC	COMMAND CENTER

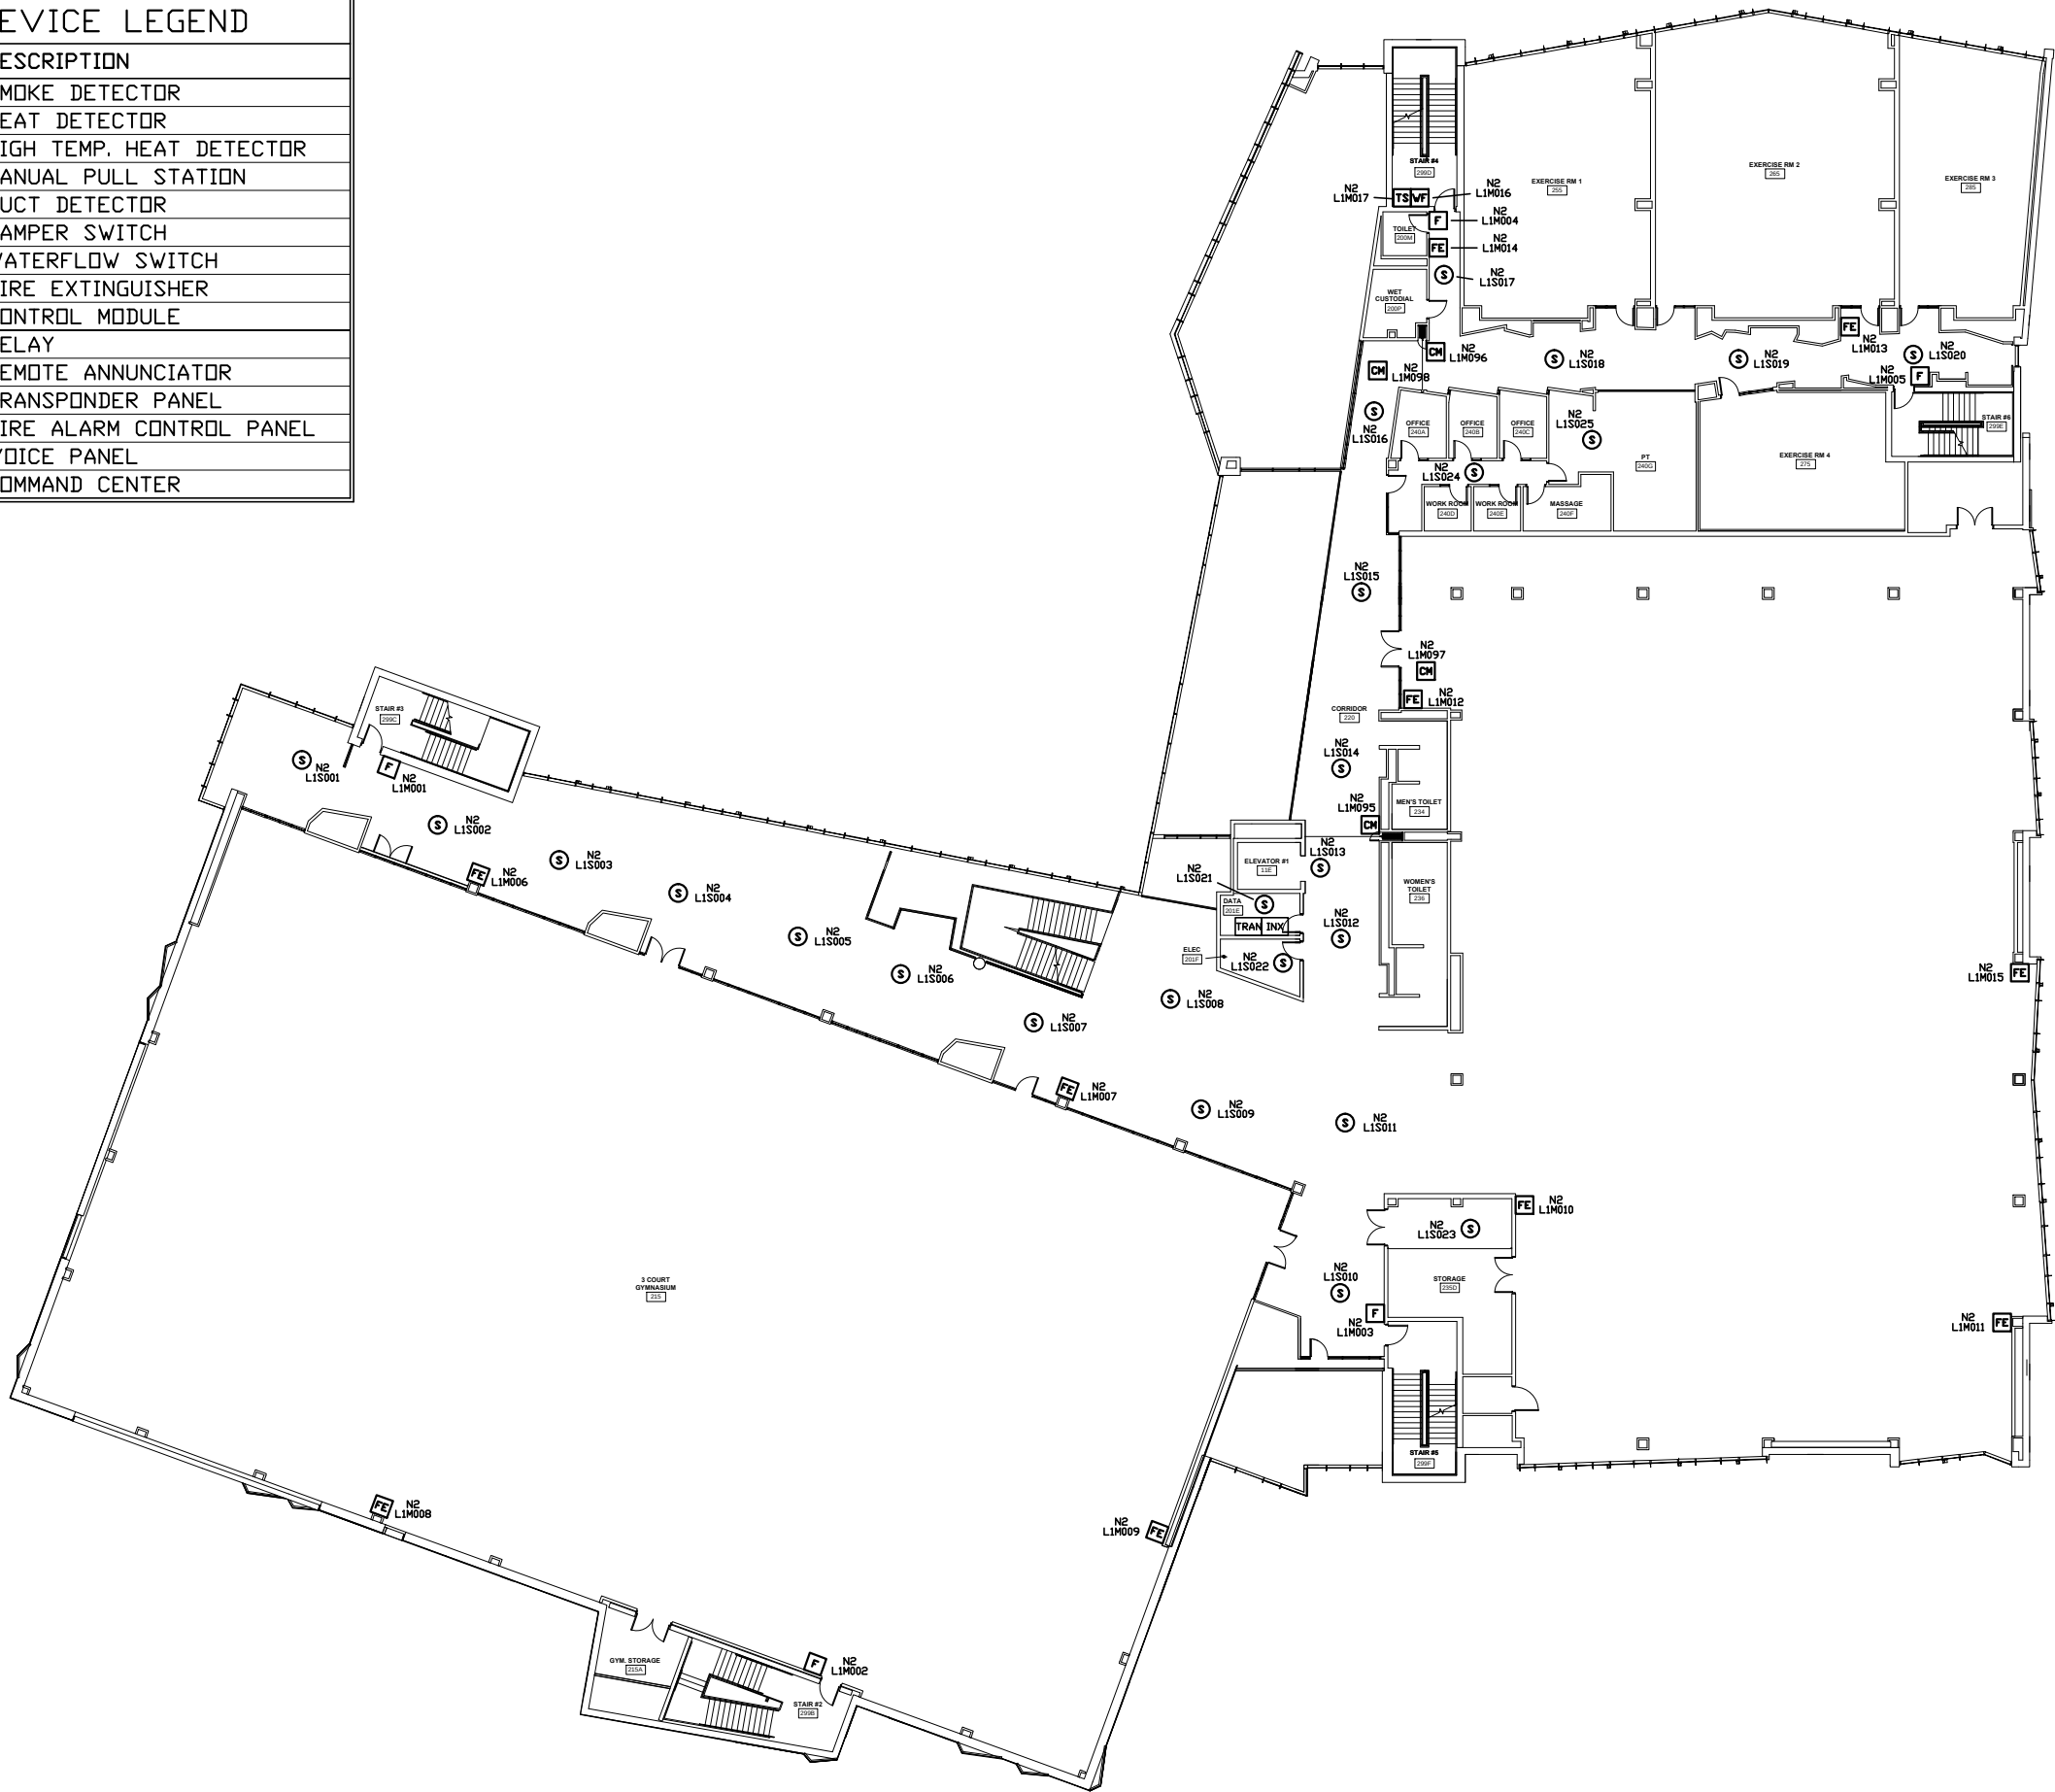

UNIVERSITY OF UTAH
STUDENT LIFE CENTER
LEVEL 2
1836 BALLIF ROAD
SALT LAKE CITY, UTAH
FIRE ALARM SYSTEM

NFS
NELSON FIRE SYSTEMS
801-468-8300




DRAWN BY: AK
DESIGNED BY: XXXX
APPROVED BY: DS
DATE: 12/6/14
SCALE: (ARCH C) N.T.S.
PROJECT NO: XXXX
REV NO: XXXX
DRAWING NAME:
UofU STUDENT CENTER 2FM.DWG

FIRE ALARM SYSTEM
LEVEL 2
FINAL MAP

PAGE:
FA-2

N.I.C.E.T.
LEVEL IV
CERTIFICATION
DONNY SCHULTZ
#046396

DEVICE LEGEND	
SYMBOL	DESCRIPTION
(S)	SMOKE DETECTOR
(T)	HEAT DETECTOR
(T) 190°	HIGH TEMP. HEAT DETECTOR
(F)	MANUAL PULL STATION
(DD)	DUCT DETECTOR
(TS)	TAMPER SWITCH
(VF)	WATERFLOW SWITCH
(FE)	FIRE EXTINGUISHER
(CH)	CONTROL MODULE
(R)	RELAY
(RA)	REMOTE ANNUNCIATOR
(TRAN)	TRANSPONDER PANEL
(FACP)	FIRE ALARM CONTROL PANEL
(INX)	VOICE PANEL
(CC)	COMMAND CENTER

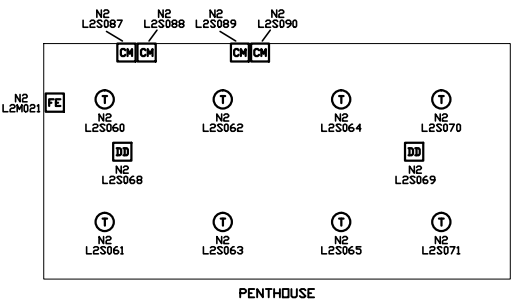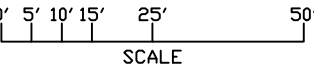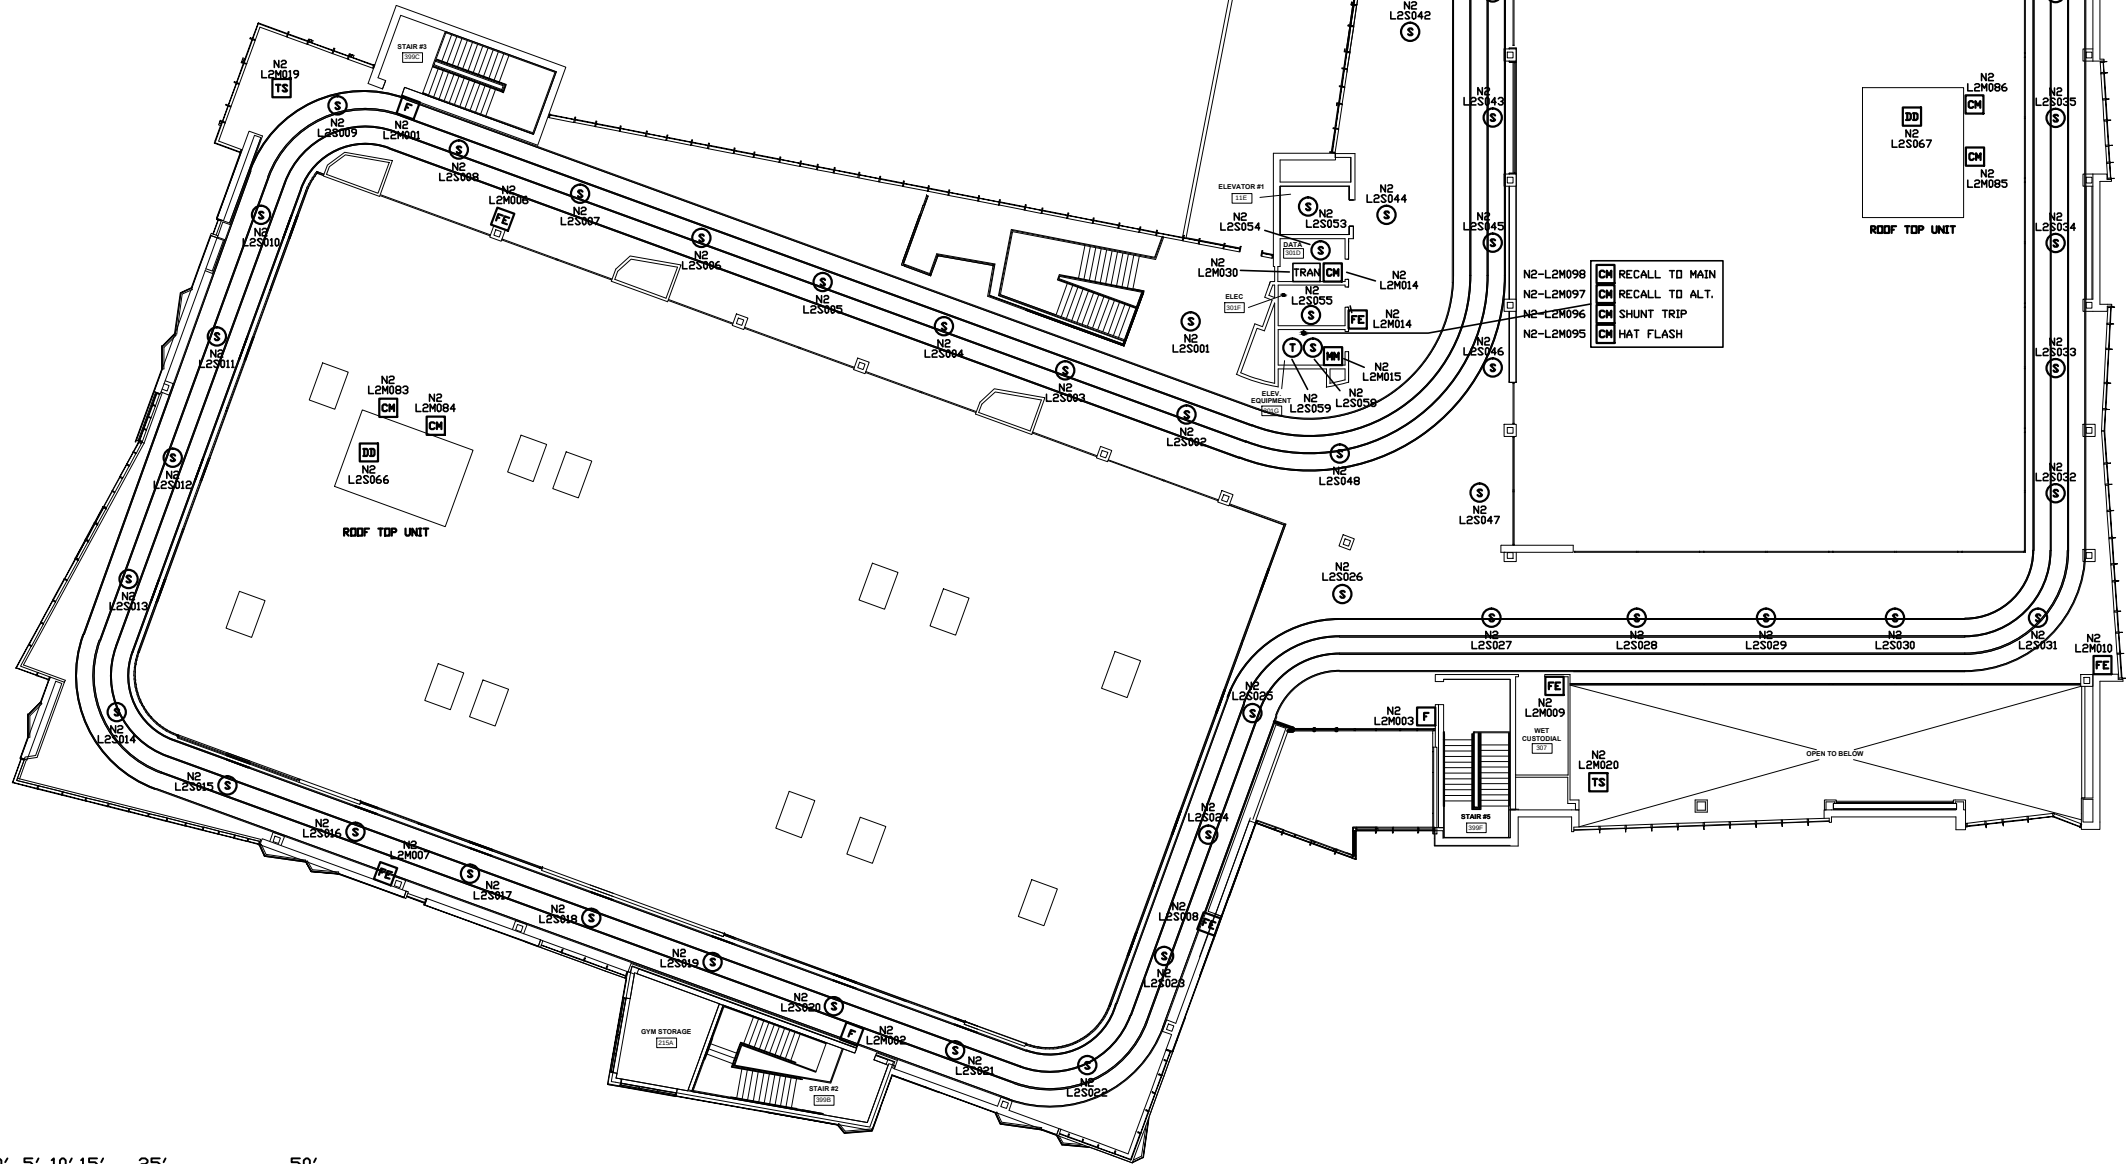

UNIVERSITY OF UTAH
STUDENT LIFE CENTER
LEVEL 3
1836 BALLIF ROAD
SALT LAKE CITY, UTAH
FIRE ALARM SYSTEM

NFS
NELSON FIRE SYSTEMS
801-468-8300

DRAWN BY:	AK
DESIGNED BY:	XXXX
APPROVED BY:	DS
DATE:	12/6/14
SCALE:	(ARCH C) N.T.S.
PROJECT NO:	XXXX
REV NO:	XXXX
DRAWING NAME:	UofU STUDENT CENTER 3FM.DWG

FIRE ALARM SYSTEM
LEVEL 3
FINAL MAP

PAGE:
FA-3

