


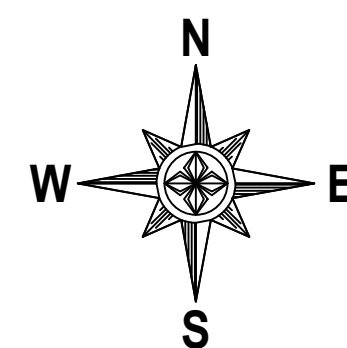

NOTE:
NFS DRAWINGS ARE BASED ON THE PROJECT
ARCHITECTURE/ENGINEER (A/E) PLANS AND
SPECIFICATIONS FURNISHED TO NFS. A/E IS SOLELY
RESPONSIBLE (NOT NFS) FOR THE TYPE, SIZE,
LOCATION, AND SUITABILITY OF ALL FIRE ALARMS,
CONTROL PANELS, AND OTHER DEVICES SHOWN ON
THE A/E PLANS. NFS DRAWINGS ARE TO SHOW ONLY
THE WIRING DIAGRAMS BETWEEN FIRE ALARM
DEVICES AND CONTROL PANELS. NFS IS NOT
RESPONSIBLE FOR THE INFORMATION SHOWN ON THE
A/E PLANS.

UNIVERSITY OF UTAH BLDG #114
SO. CAMPUS STUDENT HOUSING LEVEL 1
250 SOUTH 1770 EAST
SALT LAKE CITY, UTAH 84112
FIRE ALARM SYSTEM

NFS
NELSON FIRE SYSTEMS
801-468-8300


DRAWN BY: BH
DESIGNED BY: XXXX
APPROVED BY: KK
DATE: 09/11/2023
SCALE: N.T.S.
PROJECT NO: XXXX
REVISION NO: XXXX
DRAWING NAME:
114 KAHLERT VILLAGE FM 1.DWG

NELSON FIRE SYSTEMS
FIRST LEVEL & BASEMENT

PAGE:
FINAL MAP



DEVICE LEGEND	
SYMBOL	DESCRIPTION
S	SMOKE DETECTOR
H	HEAT DETECTOR
CO	CARBON MONOXIDE DETECTOR
P	PULL STATION
DD	DUCT DETECTOR
MM	MONITOR MODULE
WF	WATER FLOW SWITCH MODULE
TS	TAMPER SWITCH MODULE
KH	KITCHEN HOOD MODULE
CM	CONTROL MODULE
RA	REMOTE ANNUNCIATOR
FACU	FIRE ALARM CONTROL UNIT
TRAN	TRANSPONDER PANEL
INX	VOICE PANEL
SEC	SECURITY PANEL
VLP	VESDA LASER PLUS
TW2	TWO-WAY COMM. PANEL
TW	TWO-WAY COMM. STATION

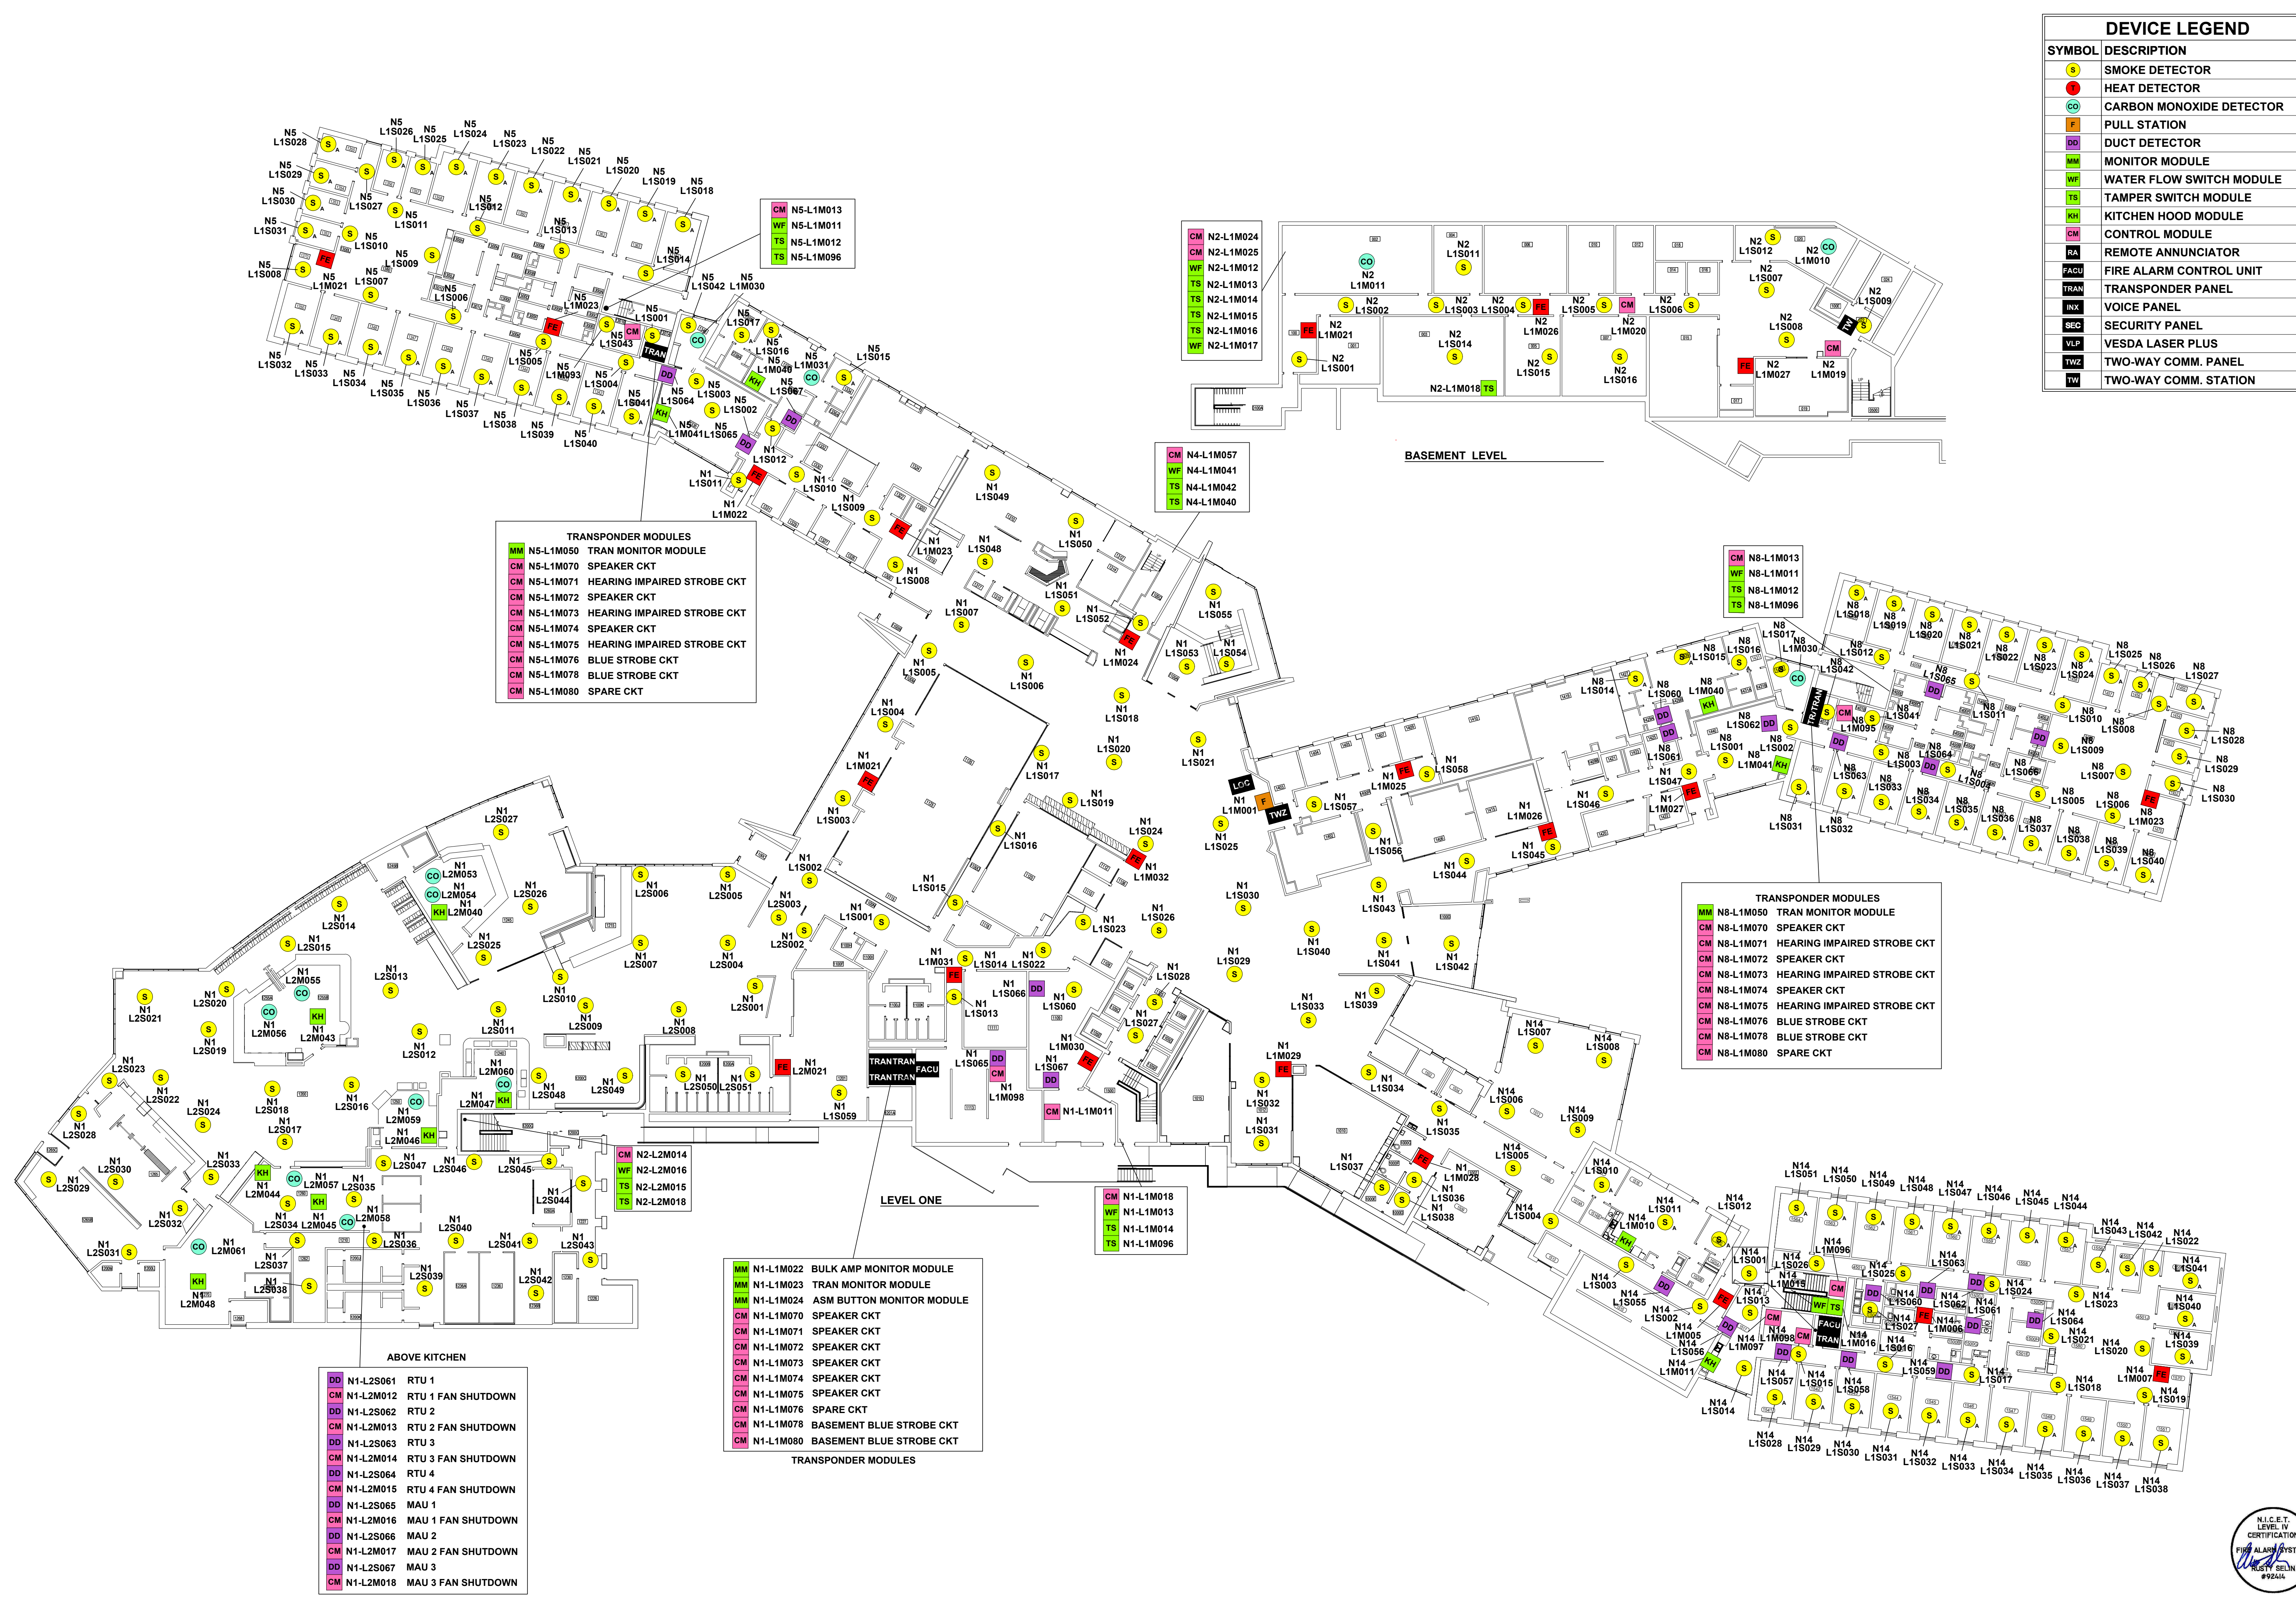



SECOND LEVEL

DEVICE LEGEND	
SYMBOL	DESCRIPTION
	SMOKE DETECTOR
	SMOKE DETECTOR- AUDIBLE BASE
	CARBON MONOXIDE DETECTOR
	DUCT DETECTOR
	WATER FLOW SWITCH MODULE
	TAMPER SWITCH MODULE
	KITCHEN HOOD MODULE
	CONTROL MODULE
	FIRE EXTINGUISHER
	TRANSPONDER PANEL
	TWO-WAY COMM. STATION

W

N

E

S

NOTE:
NFS DRAWINGS ARE BASED ON THE PROJECT ARCHITECTURE/ENGINEER (A/E) PLANS AND SPECIFICATIONS FURNISHED TO NFS. A/E IS SOLELY RESPONSIBLE (NOT NFS) FOR THE TYPE, SIZE, LOCATION, AND SUITABILITY OF ALL FIRE ALARMS, CONTROL PANELS, AND OTHER DEVICES SHOWN ON THE A/E PLANS. NFS DRAWINGS ARE TO SHOW ONLY THE WIRING DIAGRAMS BETWEEN FIRE ALARM DEVICES AND CONTROL PANELS. NFS IS NOT RESPONSIBLE FOR THE INFORMATION SHOWN ON THE A/E PLANS.

UNIVERSITY OF UTAH BLDG #114
CAMPUS STUDENT HOUSING LEVEL 2
250 SOUTH 1770 EAST
SALT LAKE CITY, UTAH 84112
FIRE ALARM SYSTEM

NFS

NELSON FIRE SYSTEMS
801-468-8300

DRAWN BY: BH

DESIGNED BY: XXXX

APPROVED BY: KK

DATE: 09/14/2023

SCALE: N.T.S.

PROJECT NO: XXXX

REVISION NO: XXXX

DRAWING NAME: 114 KAHLERT VILLAGE FM 2.DWG


NELSON FIRE SYSTEMS

LEVEL 2

PAGE:

FINAL MAP



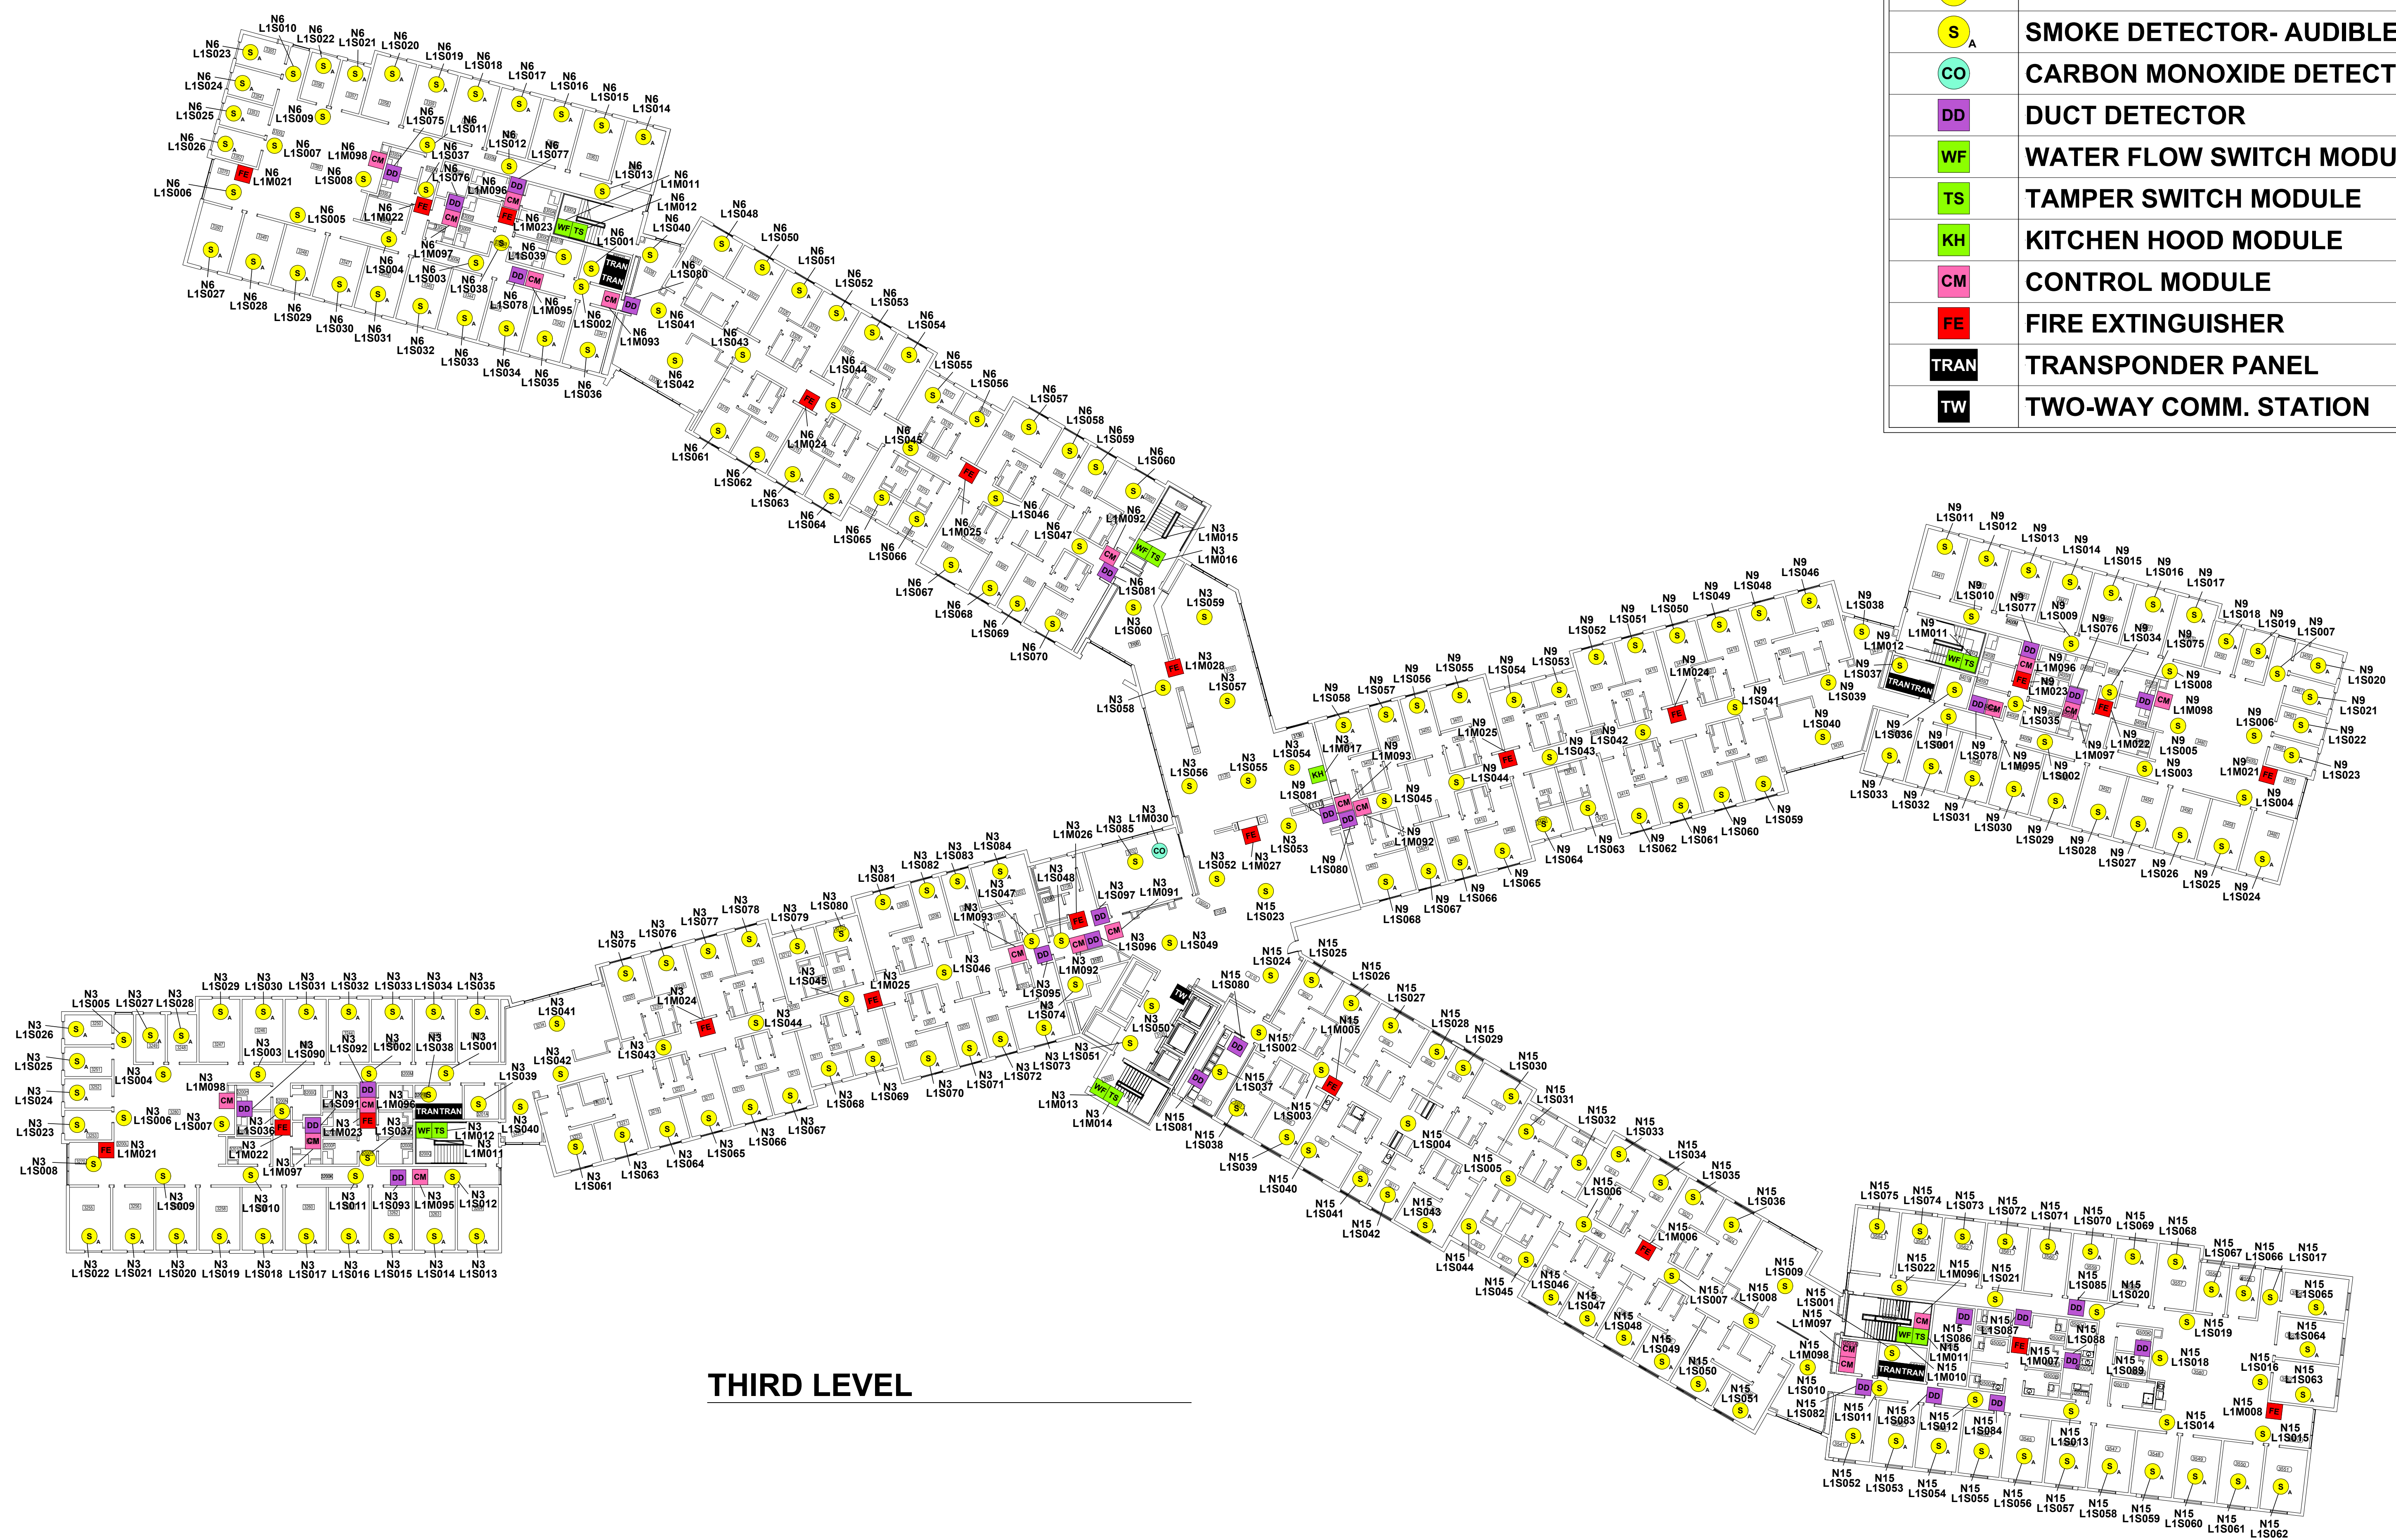

THIRD LEVEL

DEVICE LEGEND	
SYMBOL	DESCRIPTION
	SMOKE DETECTOR
	SMOKE DETECTOR- AUDIBLE BASE
	CARBON MONOXIDE DETECTOR
	DUCT DETECTOR
	WATER FLOW SWITCH MODULE
	TAMPER SWITCH MODULE
	KITCHEN HOOD MODULE
	CONTROL MODULE
	FIRE EXTINGUISHER
	TRANSPONDER PANEL
	TWO-WAY COMM. STATION

W

N

E

S

NOTE:
NFS DRAWINGS ARE BASED ON THE PROJECT ARCHITECTURE/ENGINEER (A/E) PLANS AND SPECIFICATIONS FURNISHED TO NFS. A/E IS SOLELY RESPONSIBLE (NOT NFS) FOR THE TYPE, SIZE, LOCATION, AND SUITABILITY OF ALL FIRE ALARMS, CONTROL PANELS, AND OTHER DEVICES SHOWN ON THE A/E PLANS. NFS DRAWINGS ARE TO SHOW ONLY THE WIRING DIAGRAMS BETWEEN FIRE ALARM DEVICES AND CONTROL PANELS. NFS IS NOT RESPONSIBLE FOR THE INFORMATION SHOWN ON THE A/E PLANS.

UNIVERSITY OF UTAH BLDG #114
CAMPUS STUDENT HOUSING LEVEL 3
250 SOUTH 1770 EAST
SALT LAKE CITY, UTAH 84112
FIRE ALARM SYSTEM

SO.

NFS

NELSON FIRE SYSTEMS
801-468-8300

DRAWN BY:	BH
DESIGNED BY:	XXXX
APPROVED BY:	KK
DATE:	09/14/2023
SCALE:	N.T.S.
PROJECT NO:	XXXX
REVISION NO:	XXXX
DRAWING NAME:	114 KAHLERT VILLAGE FM 3.DWG

NELSON FIRE SYSTEMS

LEVEL 3

PAGE:

FINAL MAP





FOURTH LEVEL

DEVICE LEGEND	
SYMBOL	DESCRIPTION
	SMOKE DETECTOR
	SMOKE DETECTOR- AUDIBLE BASE
	CARBON MONOXIDE DETECTOR
	DUCT DETECTOR
	WATER FLOW SWITCH MODULE
	TAMPER SWITCH MODULE
	KITCHEN HOOD MODULE
	CONTROL MODULE
	FIRE EXTINGUISHER
	FIRE ALARM CONTROL UNIT
	TRANSPONDER PANEL
	TWO-WAY COMM. STATION

W

N

E

S

NOTE:
NFS DRAWINGS ARE BASED ON THE PROJECT ARCHITECTURE/ENGINEER (A/E) PLANS AND SPECIFICATIONS FURNISHED TO NFS. A/E IS SOLELY RESPONSIBLE (NOT NFS) FOR THE TYPE, SIZE, LOCATION, AND SUITABILITY OF ALL FIRE ALARMS, CONTROL PANELS, AND OTHER DEVICES SHOWN ON THE A/E PLANS. NFS DRAWINGS ARE TO SHOW ONLY THE WIRING DIAGRAMS BETWEEN FIRE ALARM DEVICES AND CONTROL PANELS. NFS IS NOT RESPONSIBLE FOR THE INFORMATION SHOWN ON THE A/E PLANS.

UNIVERSITY OF UTAH BLDG #114
CAMPUS STUDENT HOUSING LEVEL 4
250 SOUTH 1770 EAST
SALT LAKE CITY, UTAH 84112
SO.
FIRE ALARM SYSTEM

NFS

NELSON FIRE SYSTEMS
801-468-8300

DRAWN BY: BH

DESIGNED BY: XXXX

APPROVED BY: KK

DATE: 09/15/2023

SCALE: N.T.S.

PROJECT NO: XXXX

REVISION NO: XXXX

DRAWING NAME: 114 KAHLERT VILLAGE FM 4.DWG

NELSON FIRE SYSTEMS

LEVEL 4

PAGE:

FINAL MAP



DEVICE LEGEND	
SYMBOL	DESCRIPTION
	SMOKE DETECTOR
	SMOKE DETECTOR- AUDIBLE BASE
	CARBON MONOXIDE DETECTOR
	DUCT DETECTOR
	MONITOR MODULE
	WATER FLOW SWITCH MODULE
	TAMPER SWITCH MODULE
	KITCHEN HOOD MODULE
	CONTROL MODULE
	FIRE EXTINGUISHER
	TRANSPONDER PANEL
	TWO-WAY COMM. STATION

NOTE:
NFS DRAWINGS ARE BASED ON THE PROJECT ARCHITECTURE/ENGINEER (A/E) PLANS AND SPECIFICATIONS FURNISHED TO NFS. A/E IS SOLELY RESPONSIBLE (NOT NFS) FOR THE TYPE, SIZE, LOCATION, AND SUITABILITY OF ALL FIRE ALARMS, CONTROL PANELS, AND OTHER DEVICES SHOWN ON THE A/E PLANS. NFS DRAWINGS ARE TO SHOW ONLY THE WIRING DIAGRAMS BETWEEN FIRE ALARM DEVICES AND CONTROL PANELS. NFS IS NOT RESPONSIBLE FOR THE INFORMATION SHOWN ON THE A/E PLANS.

UNIVERSITY OF UTAH BLDG #114
SO. CAMPUS
STUDENT HOUSING LEVEL 5
250 SOUTH 1770 EAST
SALT LAKE CITY, UTAH 84112
FIRE ALARM SYSTEM

NFS
NELSON FIRE SYSTEMS
801-468-8300

DRAWN BY: BH
DESIGNED BY: XXXX
APPROVED BY: KK
DATE: 09/15/2023
SCALE: N.T.S.
PROJECT NO: XXXX
REVISION NO: XXXX
DRAWING NAME:
114 KAHLERT VILLAGE FM 5.DWG

NELSON FIRE SYSTEMS
LEVEL 5

PAGE:
FINAL MAP

