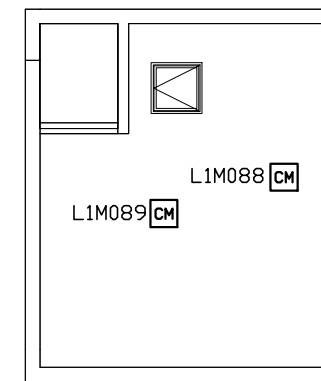
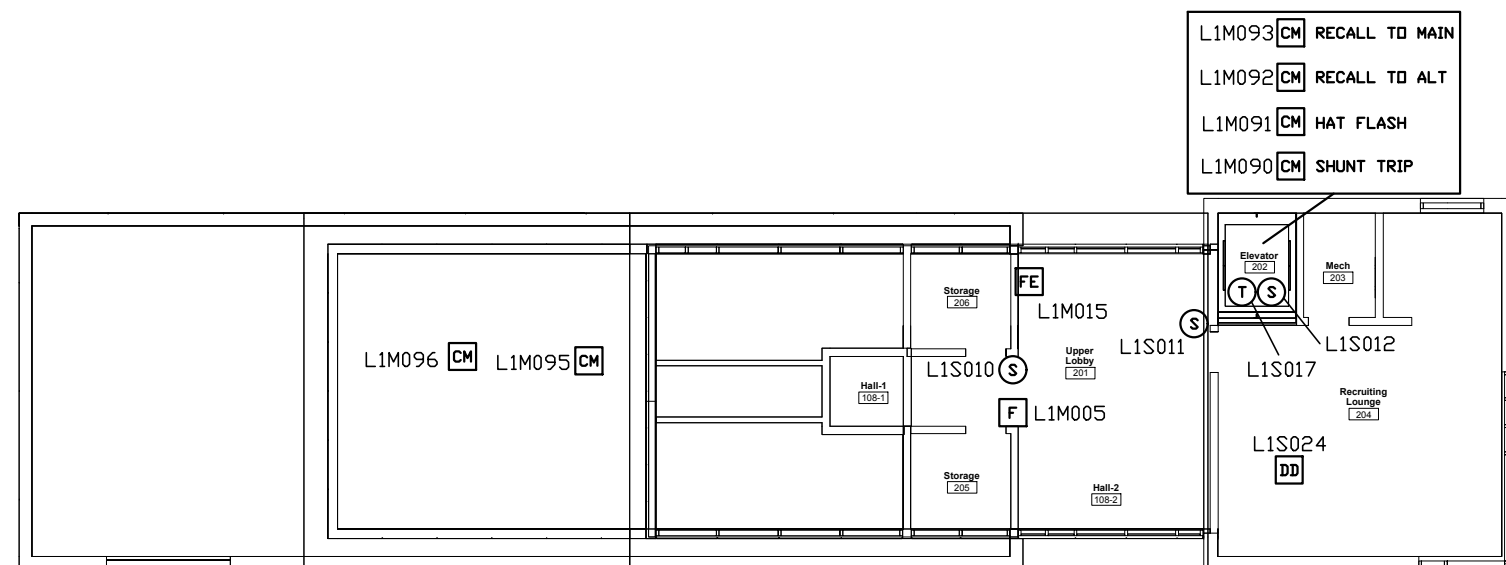
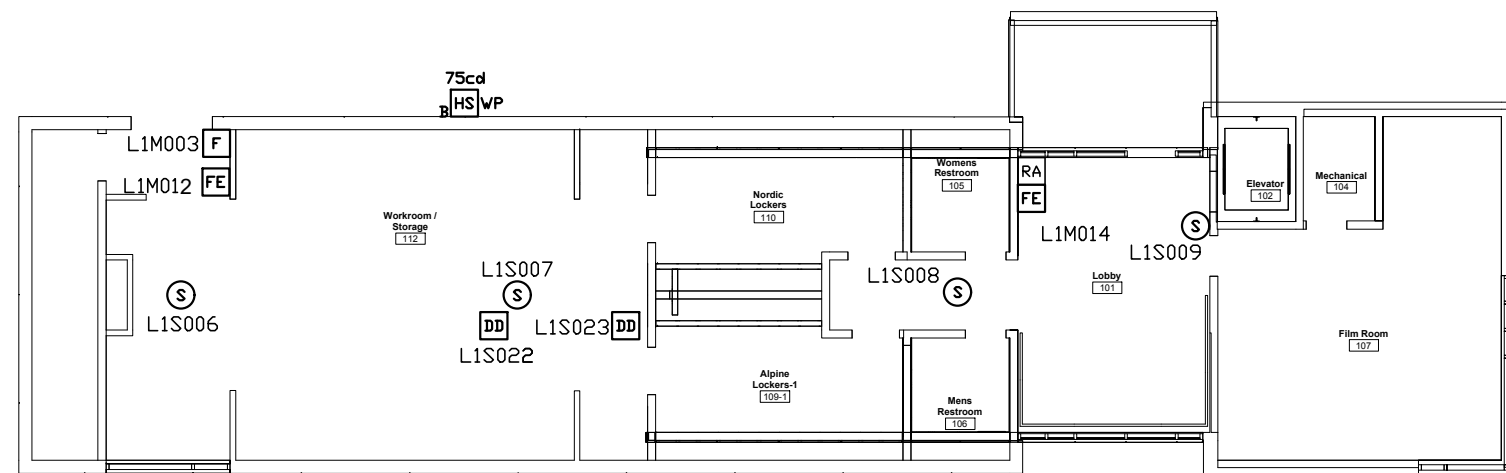
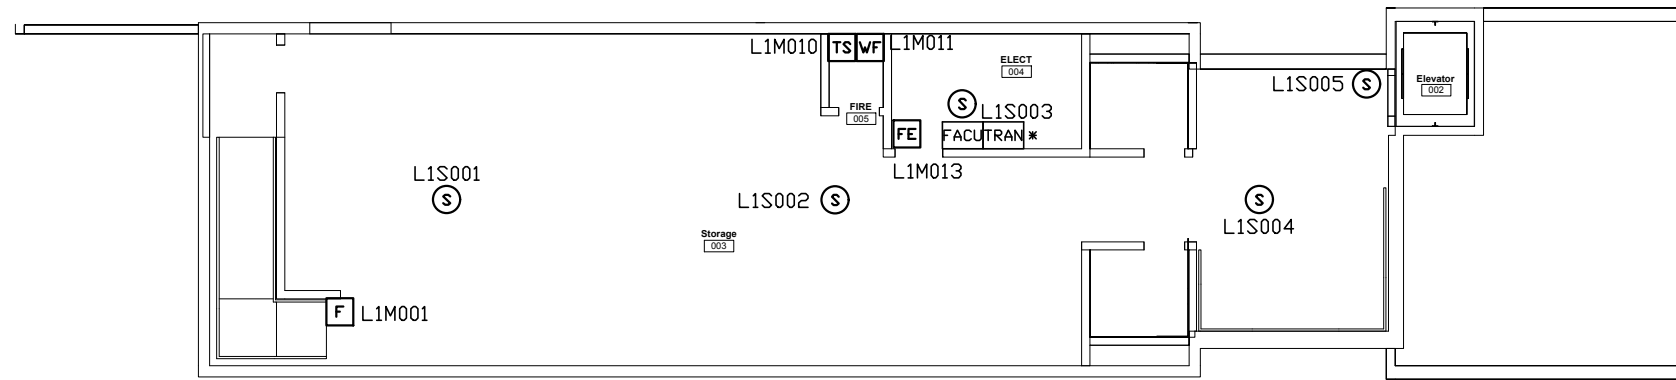


NOTE:
NFS DRAWINGS ARE BASED ON THE PROJECT ARCHITECTURE/ENGINEER (A/E) PLANS AND SPECIFICATIONS FURNISHED TO NFS. A/E IS SOLELY RESPONSIBLE (NOT NFS) FOR THE TYPE, SIZE, LOCATION, AND SUITABILITY OF ALL FIRE ALARMS, CONTROL PANELS, AND OTHER DEVICES SHOWN ON THE A/E PLANS. NFS DRAWINGS ARE TO SHOW ONLY THE WIRING DIAGRAMS BETWEEN FIRE ALARM DEVICES AND CONTROL PANELS. NFS IS NOT RESPONSIBLE FOR THE INFORMATION SHOWN ON THE A/E PLANS.

UNIVERSITY OF UTAH
SKI TEAM BUILDING
FLOORPLAN LEVELS B,1,2,R
UNIVERSITY OF UTAH CAMPUS
SALT LAKE CITY, UTAH
FIRE ALARM SYSTEM

NFS
NELSON FIRE SYSTEMS
801-468-8300

DRAWN BY:	BDT
DESIGNED BY:	XXXX
APPROVED BY:	DS
DATE:	2/22/2017
SCALE:	N.T.S.
PROJECT NO:	XXXX
REVISION NO:	XXXX
DRAWING NAME:	U OF U SKI BUILDING.DWG

NELSON FIRE SYSTEMS

FLOORPLAN LEVELS B,I,2,R

UPDATED ON 1/3/20 BY JSN

PAGE:

FINAL MAP