


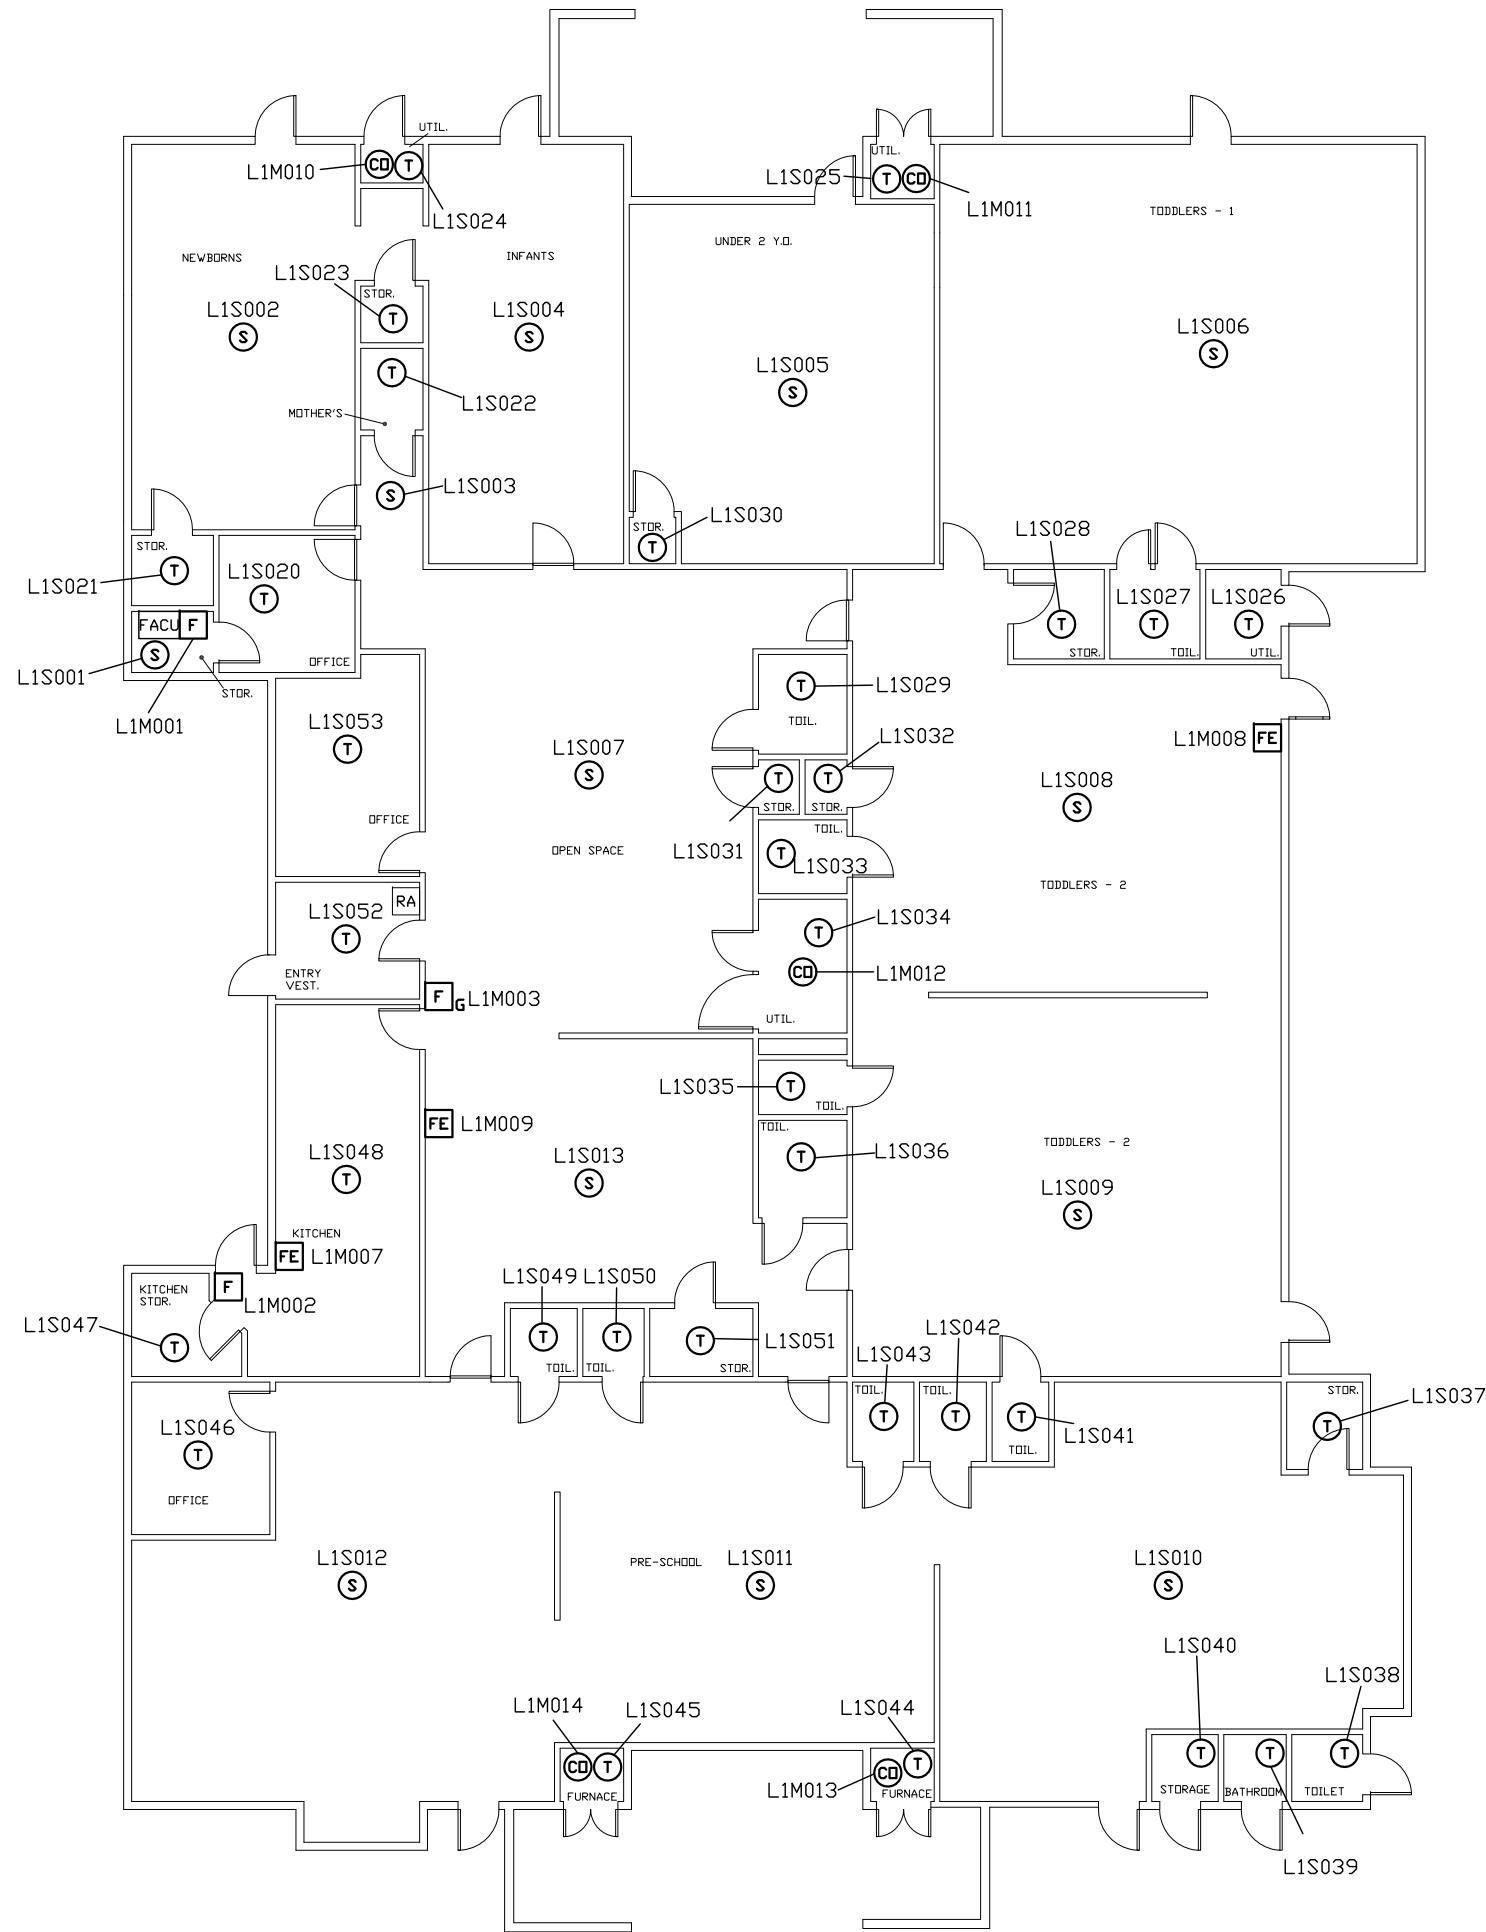

DEVICE LEGEND	
SYMBOL	DESCRIPTION
(S)	SMOKE DETECTOR
(T)	HEAT DETECTOR
(CD)	CARBON MONOXIDE DETECTOR
[F]	PULL STATION
[MM]	MONITOR MODULE
[L]	STROBE ONLY
[L] ^B	STROBE ONLY w/BLUE LENS
[HS]	HORN/STROBE
[HS] _{LF}	HORN/STROBE-LOW FREQUENCY
[C]	CEILING MOUNT
[G]	DEVICE W/ GUARD
[RA]	REMOTE ANNUNCIATOR
[FE]	FIRE EXTINGUISHER
[FACU]	FIRE ALARM CONTROL UNIT
[TRAN]	TRANSPONDER PANEL

NOTE:
NFS DRAWINGS ARE BASED ON THE PROJECT ARCHITECTURE/ENGINEER (A/E) PLANS AND SPECIFICATIONS FURNISHED TO NFS. A/E IS SOLELY RESPONSIBLE (NOT NFS) FOR THE TYPE, SIZE, LOCATION, AND SUITABILITY OF ALL FIRE ALARMS, CONTROL PANELS, AND OTHER DEVICES SHOWN ON THE A/E PLANS. NFS DRAWINGS ARE TO SHOW ONLY THE WIRING DIAGRAMS BETWEEN FIRE ALARM DEVICES AND CONTROL PANELS. NFS IS NOT RESPONSIBLE FOR THE INFORMATION SHOWN ON THE A/E PLANS.

UNIVERSITY OF UTAH
UNIVERSITY KIDS
545 GUARDSMAN WAY
SALT LAKE CITY, UT 84108
FIRE ALARM SYSTEM

NFS

NELSON FIRE SYSTEMS
801-468-8300

DRAWN BY: JPK
DESIGNED BY: XXXX
APPROVED BY: RS
DATE: 12/18/2018
SCALE: N.T.S.
PROJECT NO: XXXX
REVISION NO: XXXX
DRAWING NAME: KIDS BUILDING FM.DWG

NELSON FIRE SYSTEMS

FINAL MAP

PAGE: