DEVICE LEGEND

SYMBOL	DESCRIPTION
S	SMOKE DETECTOR
T	HEAT DETECTOR
F	PULL STATION
DD	DUCT DETECTOR
SN	SPRINKLER NOTIFICATION MODULE
WF	WATER FLOW SWITCH MODULE
TS	TAMPER SWITCH MODULE
MM	MONITOR MODULE
FE	FIRE EXTINGUISHER
CM	CONTROL MODULE
LOC	LOCAL OPERATING CONSOLE
FACU	FIRE ALARM CONTROL UNIT
TRAN	TRANSPONDER PANEL
INX	VOICE PANEL
SURG	SURGE PROTECTOR

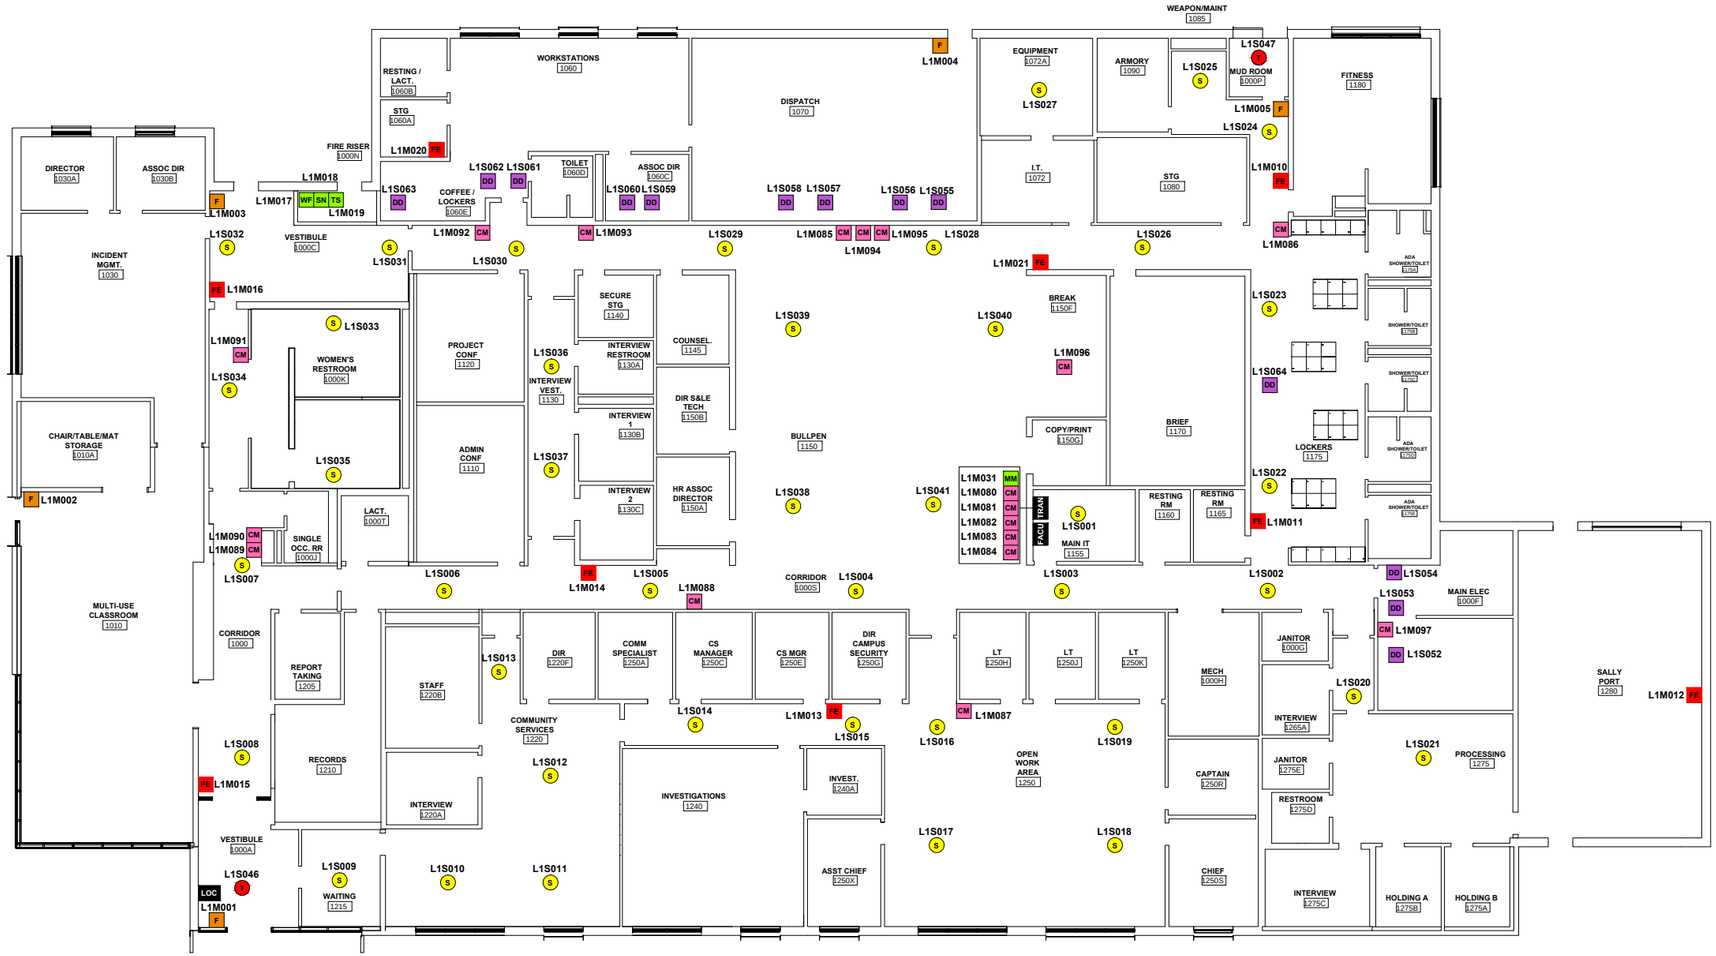

NOTE:
NFS DRAWINGS ARE BASED ON THE PROJECT ARCHITECTURE/ENGINEER (A/E) PLANS AND SPECIFICATIONS FURNISHED TO NFS. A/E IS SOLELY RESPONSIBLE (NOT NFS) FOR THE TYPE, SIZE, LOCATION, AND SUITABILITY OF ALL FIRE ALARMS, CONTROL PANELS, AND OTHER DEVICES SHOWN ON THE A/E PLANS. NFS DRAWINGS ARE TO SHOW ONLY THE WIRING DIAGRAMS BETWEEN FIRE ALARM DEVICES AND CONTROL PANELS. NFS IS NOT RESPONSIBLE FOR THE INFORMATION SHOWN ON THE A/E PLANS.

UNIVERSITY OF UTAH
PUBLIC SAFETY BUILDING
500 SOUTH & GUARDSMAN WAY
SALT LAKE CITY, UT 84112
FIRE ALARM SYSTEM

NFS
NELSON FIRE SYSTEMS
801-468-8300

DRAWN BY:	KK
DESIGNED BY:	XXXX
APPROVED BY:	KK
DATE:	5/5/2022 8:26:17 AM
SCALE:	N.T.S.
PROJECT NO:	XXXX
REVISION NO:	XXXX
DRAWING NAME:	UOFU PUBLIC SAFETY FM.DWG

NELSON FIRE SYSTEMS
BUILDING

PAGE:
FINAL MAP

N.I.C.E.T. LEVEL IV CERTIFICATION FIRE ALARM SYSTEMS