



HAT FLASH - L1M096
RECALL TO ALT. - L1M097
RECALL TO MAIN - L1M098

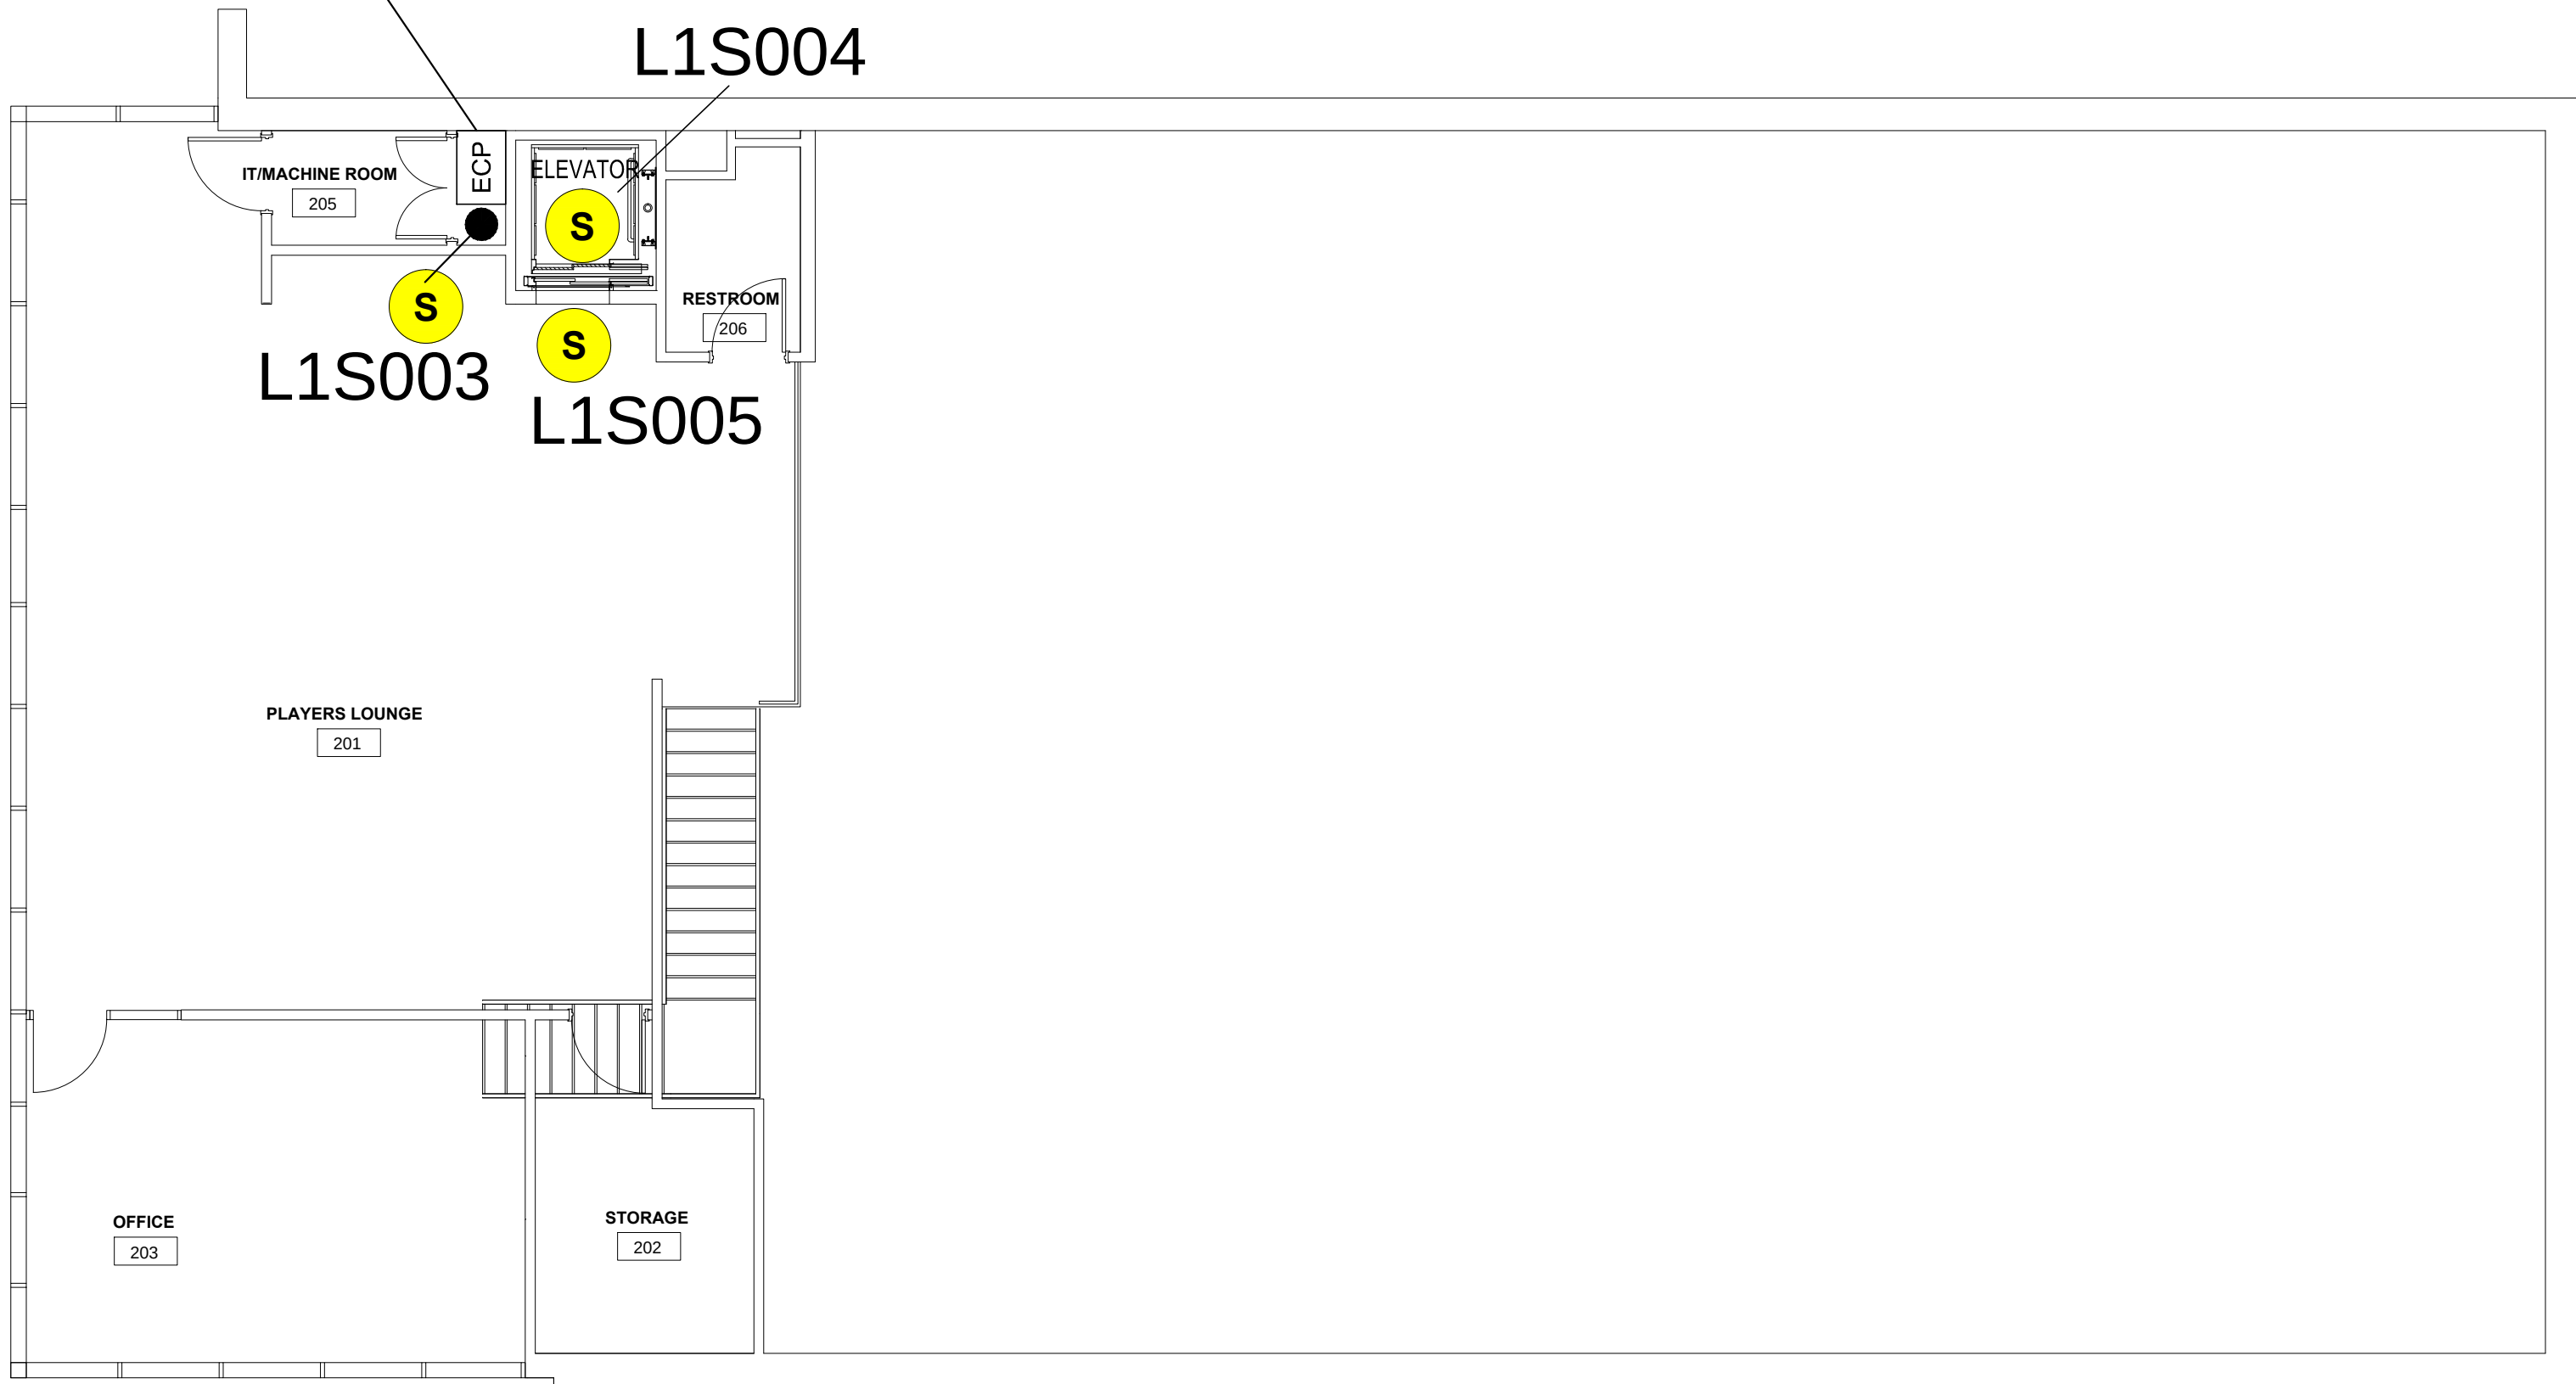


LEVEL 2

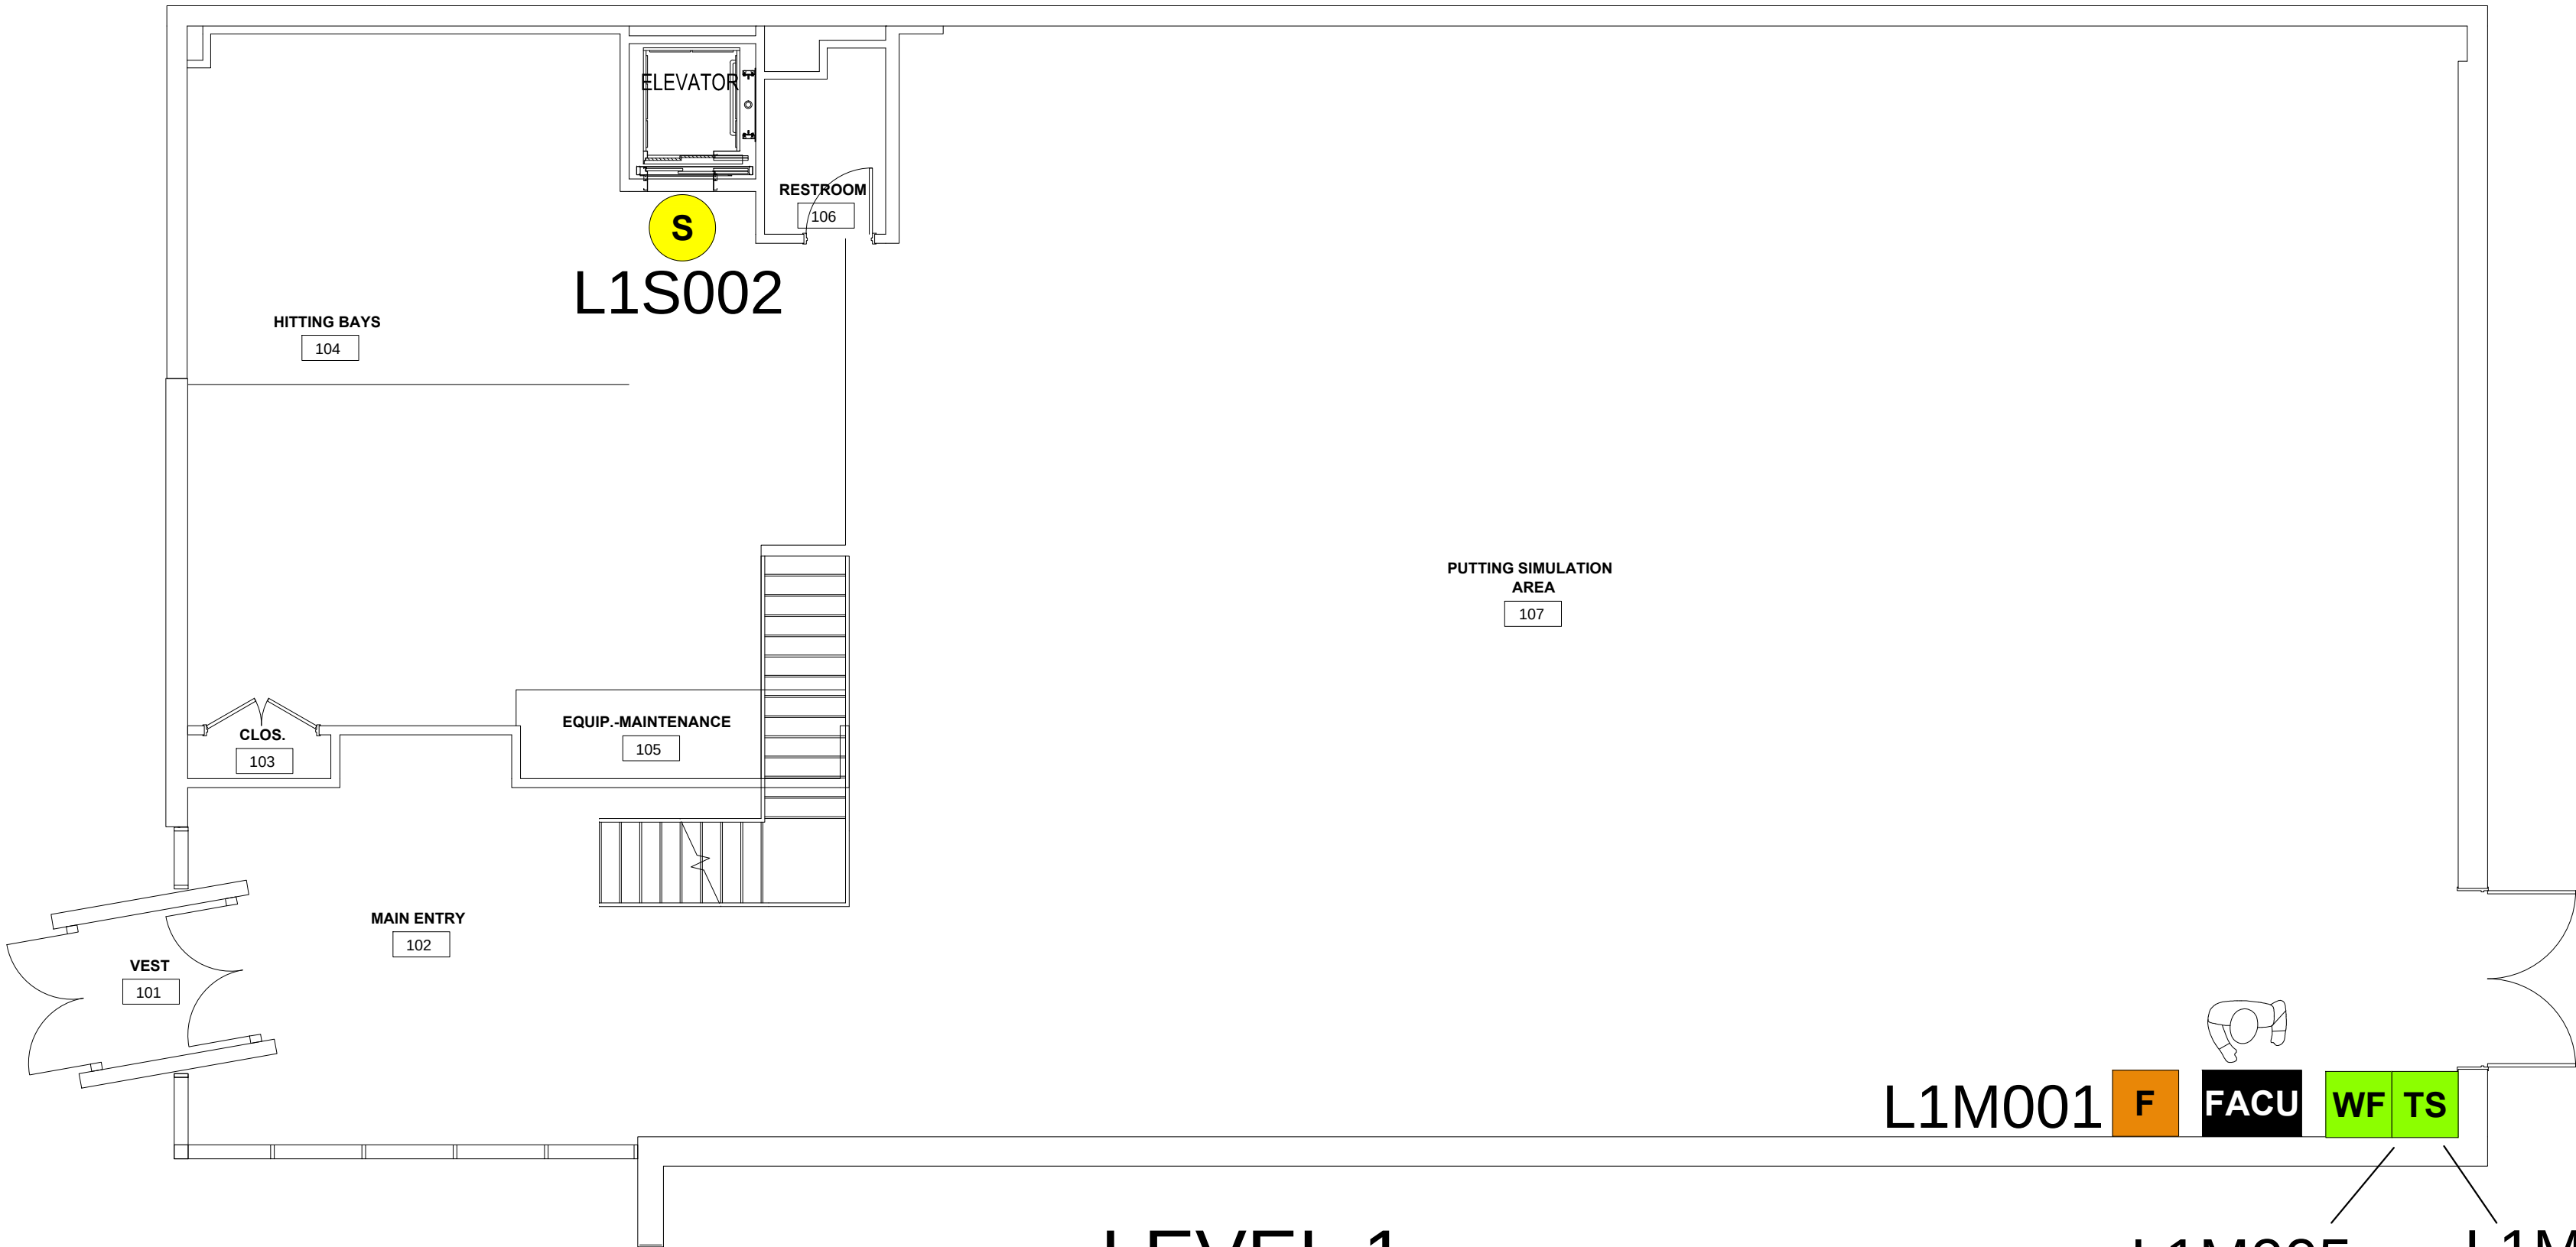

LEVEL 1

DEVICE LEGEND	
SYMBOL	DESCRIPTION
	SMOKE DETECTOR
	PULL STATION
	WATER FLOW SWITCH MODULE
	TAMPER SWITCH MODULE
	CONTROL MODULE
	FIRE ALARM CONTROL UNIT

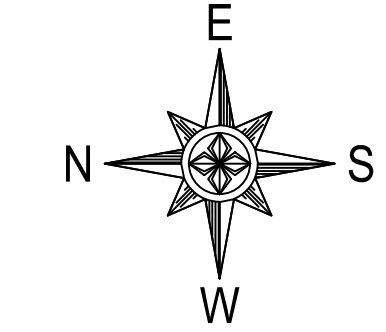

NOTE:
NFS DRAWINGS ARE BASED ON THE PROJECT
ARCHITECTURE/ENGINEER (A/E) PLANS AND
SPECIFICATIONS FURNISHED TO NFS. A/E IS SOLELY
RESPONSIBLE (NOT NFS) FOR THE TYPE, SIZE,
LOCATION, AND SUITABILITY OF ALL FIRE ALARMS,
CONTROL PANELS, AND OTHER DEVICES SHOWN ON
THE A/E PLANS. NFS DRAWINGS ARE TO SHOW ONLY
THE WIRING DIAGRAMS BETWEEN FIRE ALARM
DEVICES AND CONTROL PANELS. NFS IS NOT
RESPONSIBLE FOR THE INFORMATION SHOWN ON THE
A/E PLANS.

NEW GOLF BUILDING 211
UNIVERSITY OF UTAH
555 SOUTH GUARDSMAN WAY
SALT LAKE CITY, UT 84112
FIRE ALARM SYSTEM

NFS
NELSON FIRE SYSTEMS
801-468-8300

DRAWN BY: AK
DESIGNED BY: XXXX
APPROVED BY: KK
DATE: 12/22/2020 9:31:09 AM
SCALE: N.T.S.
PROJECT NO: XXXX
REVISION NO: XXXX
DRAWING NAME:
UOFU GOLF 211 FM.DWG

NELSON FIRE SYSTEMS

PAGE:
FINAL MAP