



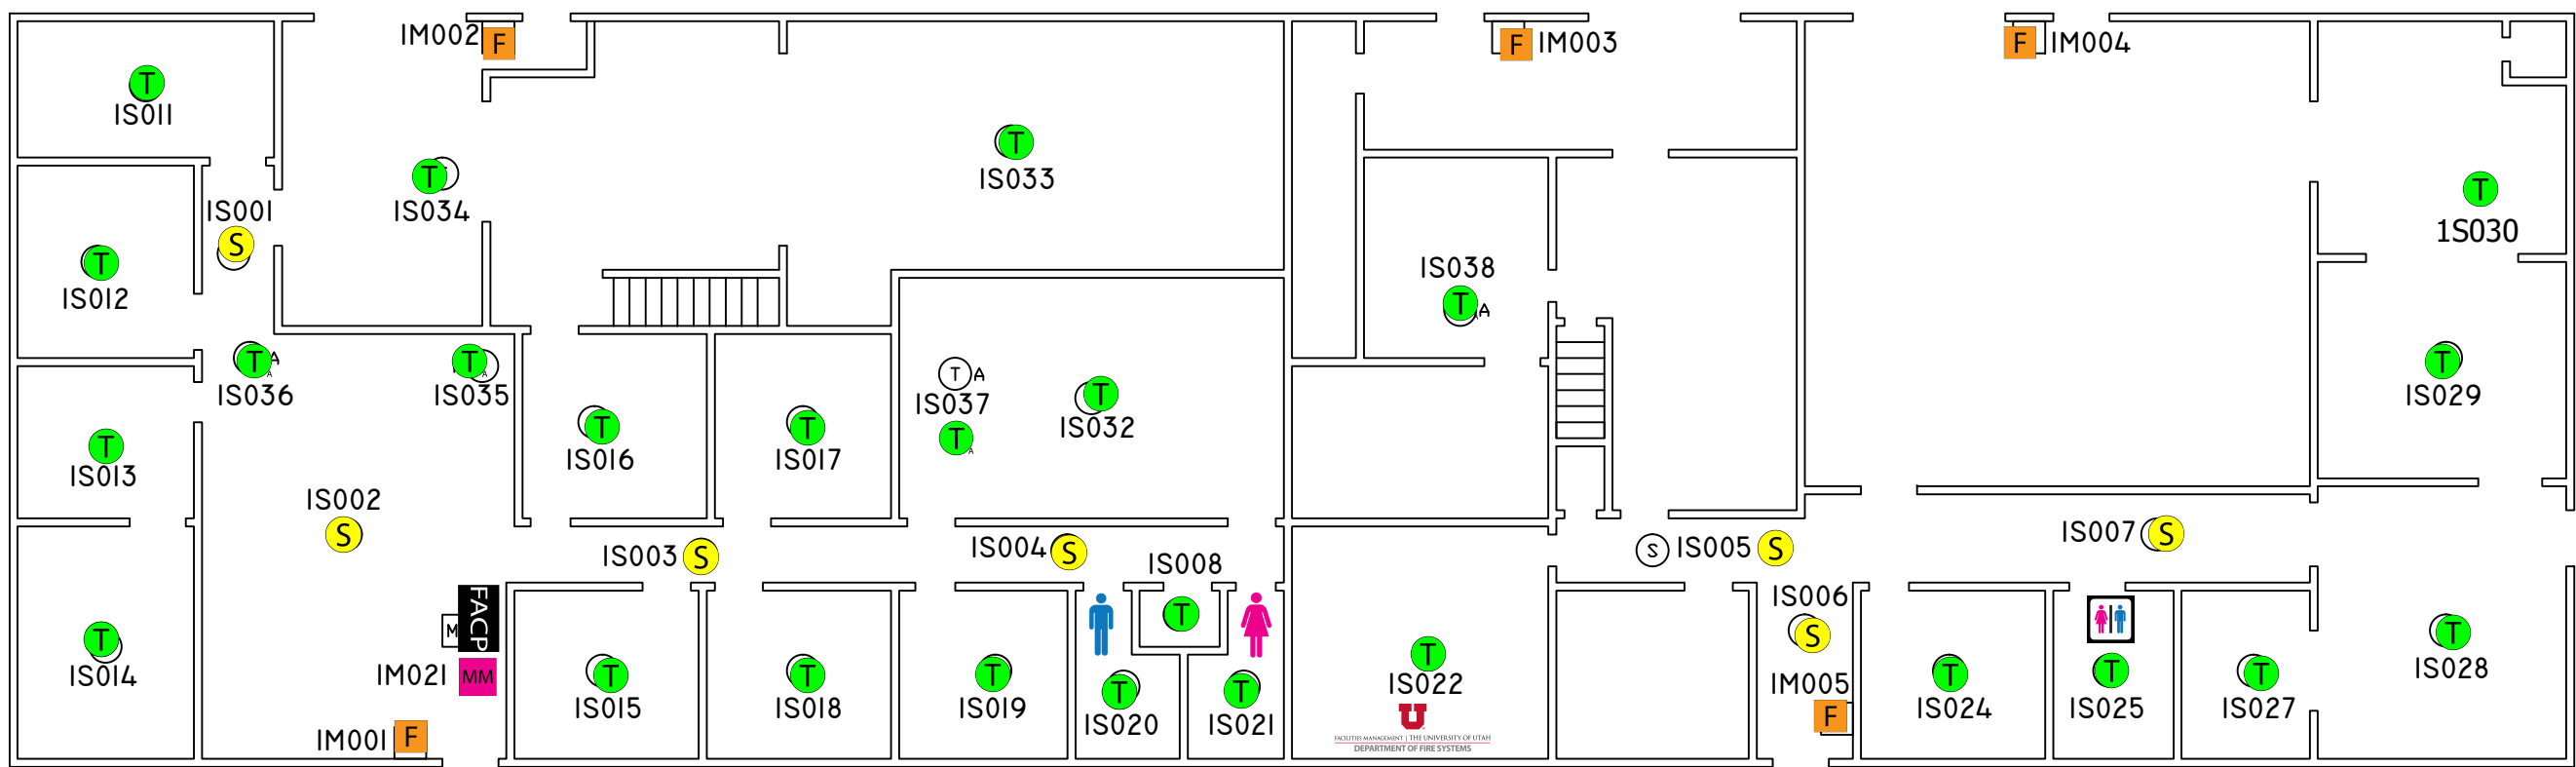

DEVICE LEGEND	
SYMBOL	DESCRIPTION
S	SMOKE DETECTOR
T _A	THERMAL DETECTOR ABOVE CEILING
T	THERMAL DETECTOR
F	MANUAL PULL STATION
MM	MONITOR MODULE
FACP	FIRE ALARM CONTROL PANEL

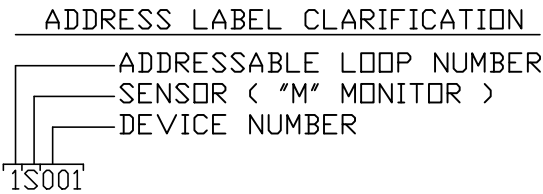

NOTE:
NFS DRAWINGS ARE BASED ON THE PROJECT
ARCHITECT/ENGINEER (A/E) PLANS AND SPECIFICATIONS
FURNISHED TO NFS. A/E IS SOLELY RESPONSIBLE
(NOT NFS) FOR THE TYPE, SIZE, LOCATION, AND
SUITABILITY OF ALL FIRE ALARMS, CONTROL PANELS,
AND OTHER DEVICES SHOWN ON THE A/E PLANS.
NFS DRAWINGS ARE TO SHOW ONLY THE WIRING
DIAGRAMS BETWEEN FIRE ALARM DEVICES AND
CONTROL PANELS. NFS IS NOT RESPONSIBLE FOR
THE INFORMATION SHOWN ON THE A/E PLANS.

BUILDING #305
UNIVERSITY OF UTAH
FIRE ALARM SYSTEM

NFS	
NELSON FIRE SYSTEMS	
801-468-8300	
DRAWN BY:	DS
DESIGNED BY:	DS
APPROVED BY:	TCT
DATE:	7/11/2006
SCALE:	1/16" = 1'
PROJECT NO:	-
REV NO:	1
DRAWING NAME:	BLDG305.DWG

FIRE ALARM SYSTEM

ADDRESSABLE DEVICE NUMBERS

NFS

FA-I-01