


DEVICE LEGEND	
SYMBOL	DESCRIPTION
(S)	SMOKE DETECTOR
(T)	HEAT DETECTOR
[F]	MANUAL PULL STATION
[RA]	REMOTE ANNUNCIATOR
[FACP]	FIRE ALARM CONTROL PANEL
[TRAN]	TRANSPONDER PANEL

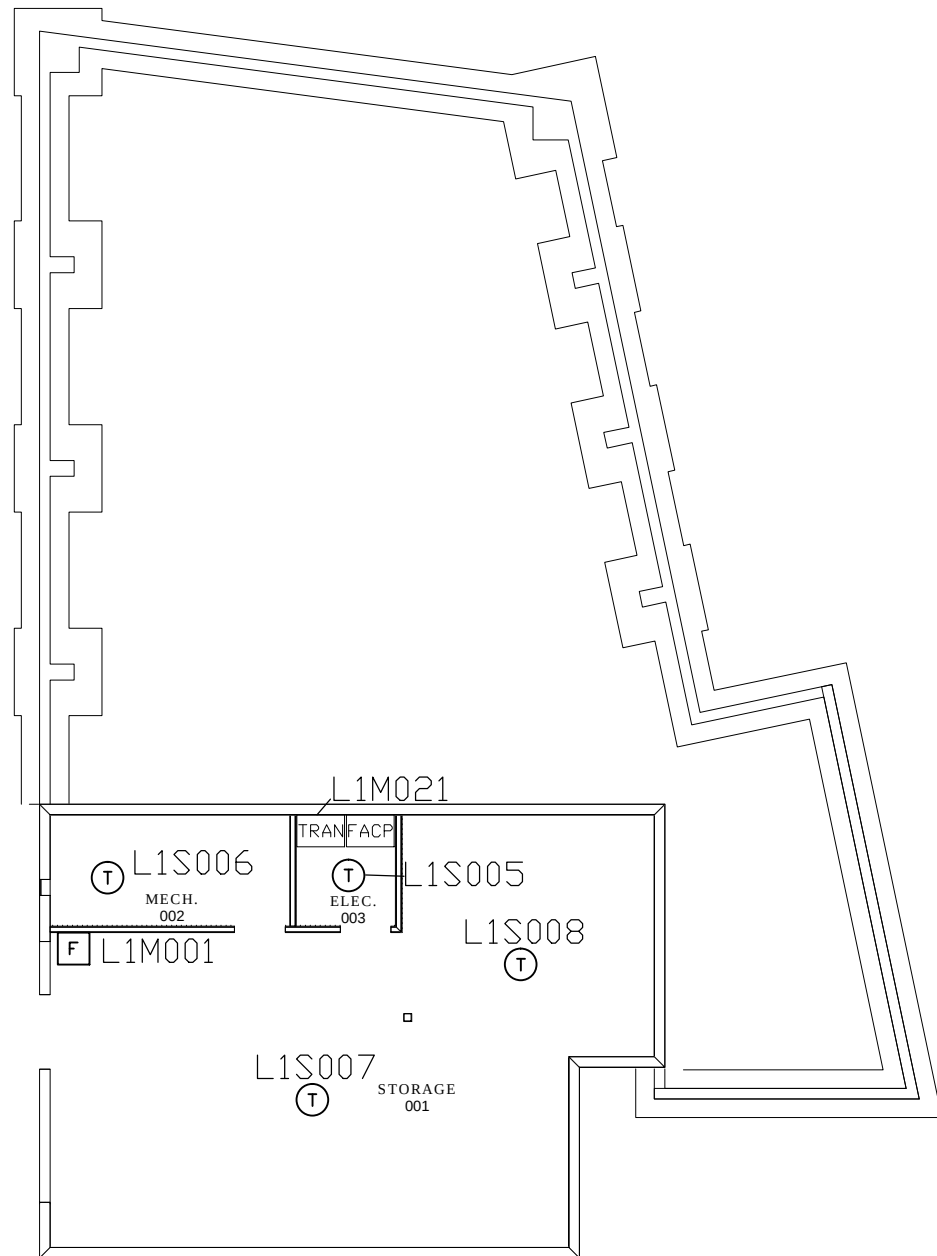

Floor plan of the first floor of the building. The plan shows a large central area with a 'RECEPTION' area. Surrounding the reception area are several rooms labeled L1S001 through L1S021. To the left of the reception area are the 'MEN'S DRESS'G RM.' (104) and 'WOMEN'S DRESS'G RM.' (105). To the right of the reception area are the 'MEN'S DRESS'G RM.' (109) and 'WOMEN'S DRESS'G RM.' (110). The plan also includes a 'JAN. CLOS.' (106), a 'SERVING RM.' (108), a 'RESTROOM/SHOWER RM.' (113), and a 'RESTROOM' (112). The plan is oriented with North at the top.

Rooms and areas shown include:

- RECEPTION
- L1S001
- L1S002
- L1S003
- L1S004
- L1S009
- L1S010
- L1S011
- L1S012
- L1S013
- L1S014
- L1S015
- L1S016
- L1S017
- L1S018
- L1S019
- L1S020
- L1S021
- MEN'S DRESS'G RM. 104
- WOMEN'S DRESS'G RM. 105
- JAN. CLOS. 106
- SERVING RM. 108
- RESTROOM/SHOWER RM. 113
- RESTROOM 112
- STORAGE 110
- HALL 103
- MEN'S DRESS'G RM. 109
- WOMEN'S DRESS'G RM. 110

NOTE:
NFS DRAWINGS ARE BASED ON THE PROJECT ARCHITECT/ENGINEER (A/E) PLANS AND SPECIFICATIONS FURNISHED TO NFS. A/E IS SOLELY RESPONSIBLE (NOT NFS) FOR THE TYPE, SIZE, LOCATION, AND SUITABILITY OF ALL FIRE ALARMS, CONTROL PANELS, AND OTHER DEVICES SHOWN ON THE A/E PLANS. NFS DRAWINGS ARE TO SHOW ONLY THE WIRING DIAGRAMS BETWEEN FIRE ALARM DEVICES AND CONTROL PANELS. NFS IS NOT RESPONSIBLE FOR THE INFORMATION SHOWN ON THE A/E PLANS.

RED BUTTE GARDENS
ROSE HOUSE
MAIN AND LOWER LEVELS
UNIVERSITY OF UTAH
FIRE ALARM SYSTEM

NFS

NELSON FIRE SYSTEMS
801-468-8300

DRAWN BY:	AK
DESIGNED BY:	XXXX
CHECKED BY:	DS
DATE:	11/19/2012
SCALE:	1/8"=1'
PROJECT NO:	XXXX
REV NO:	XXXX
DRAWING NAME:	
RED BUTTE ROSE HOUSE MAIN.DWG	

FIRE ALARM SYSTEM

NUMBERS

PAGE:

FA-I-03

