


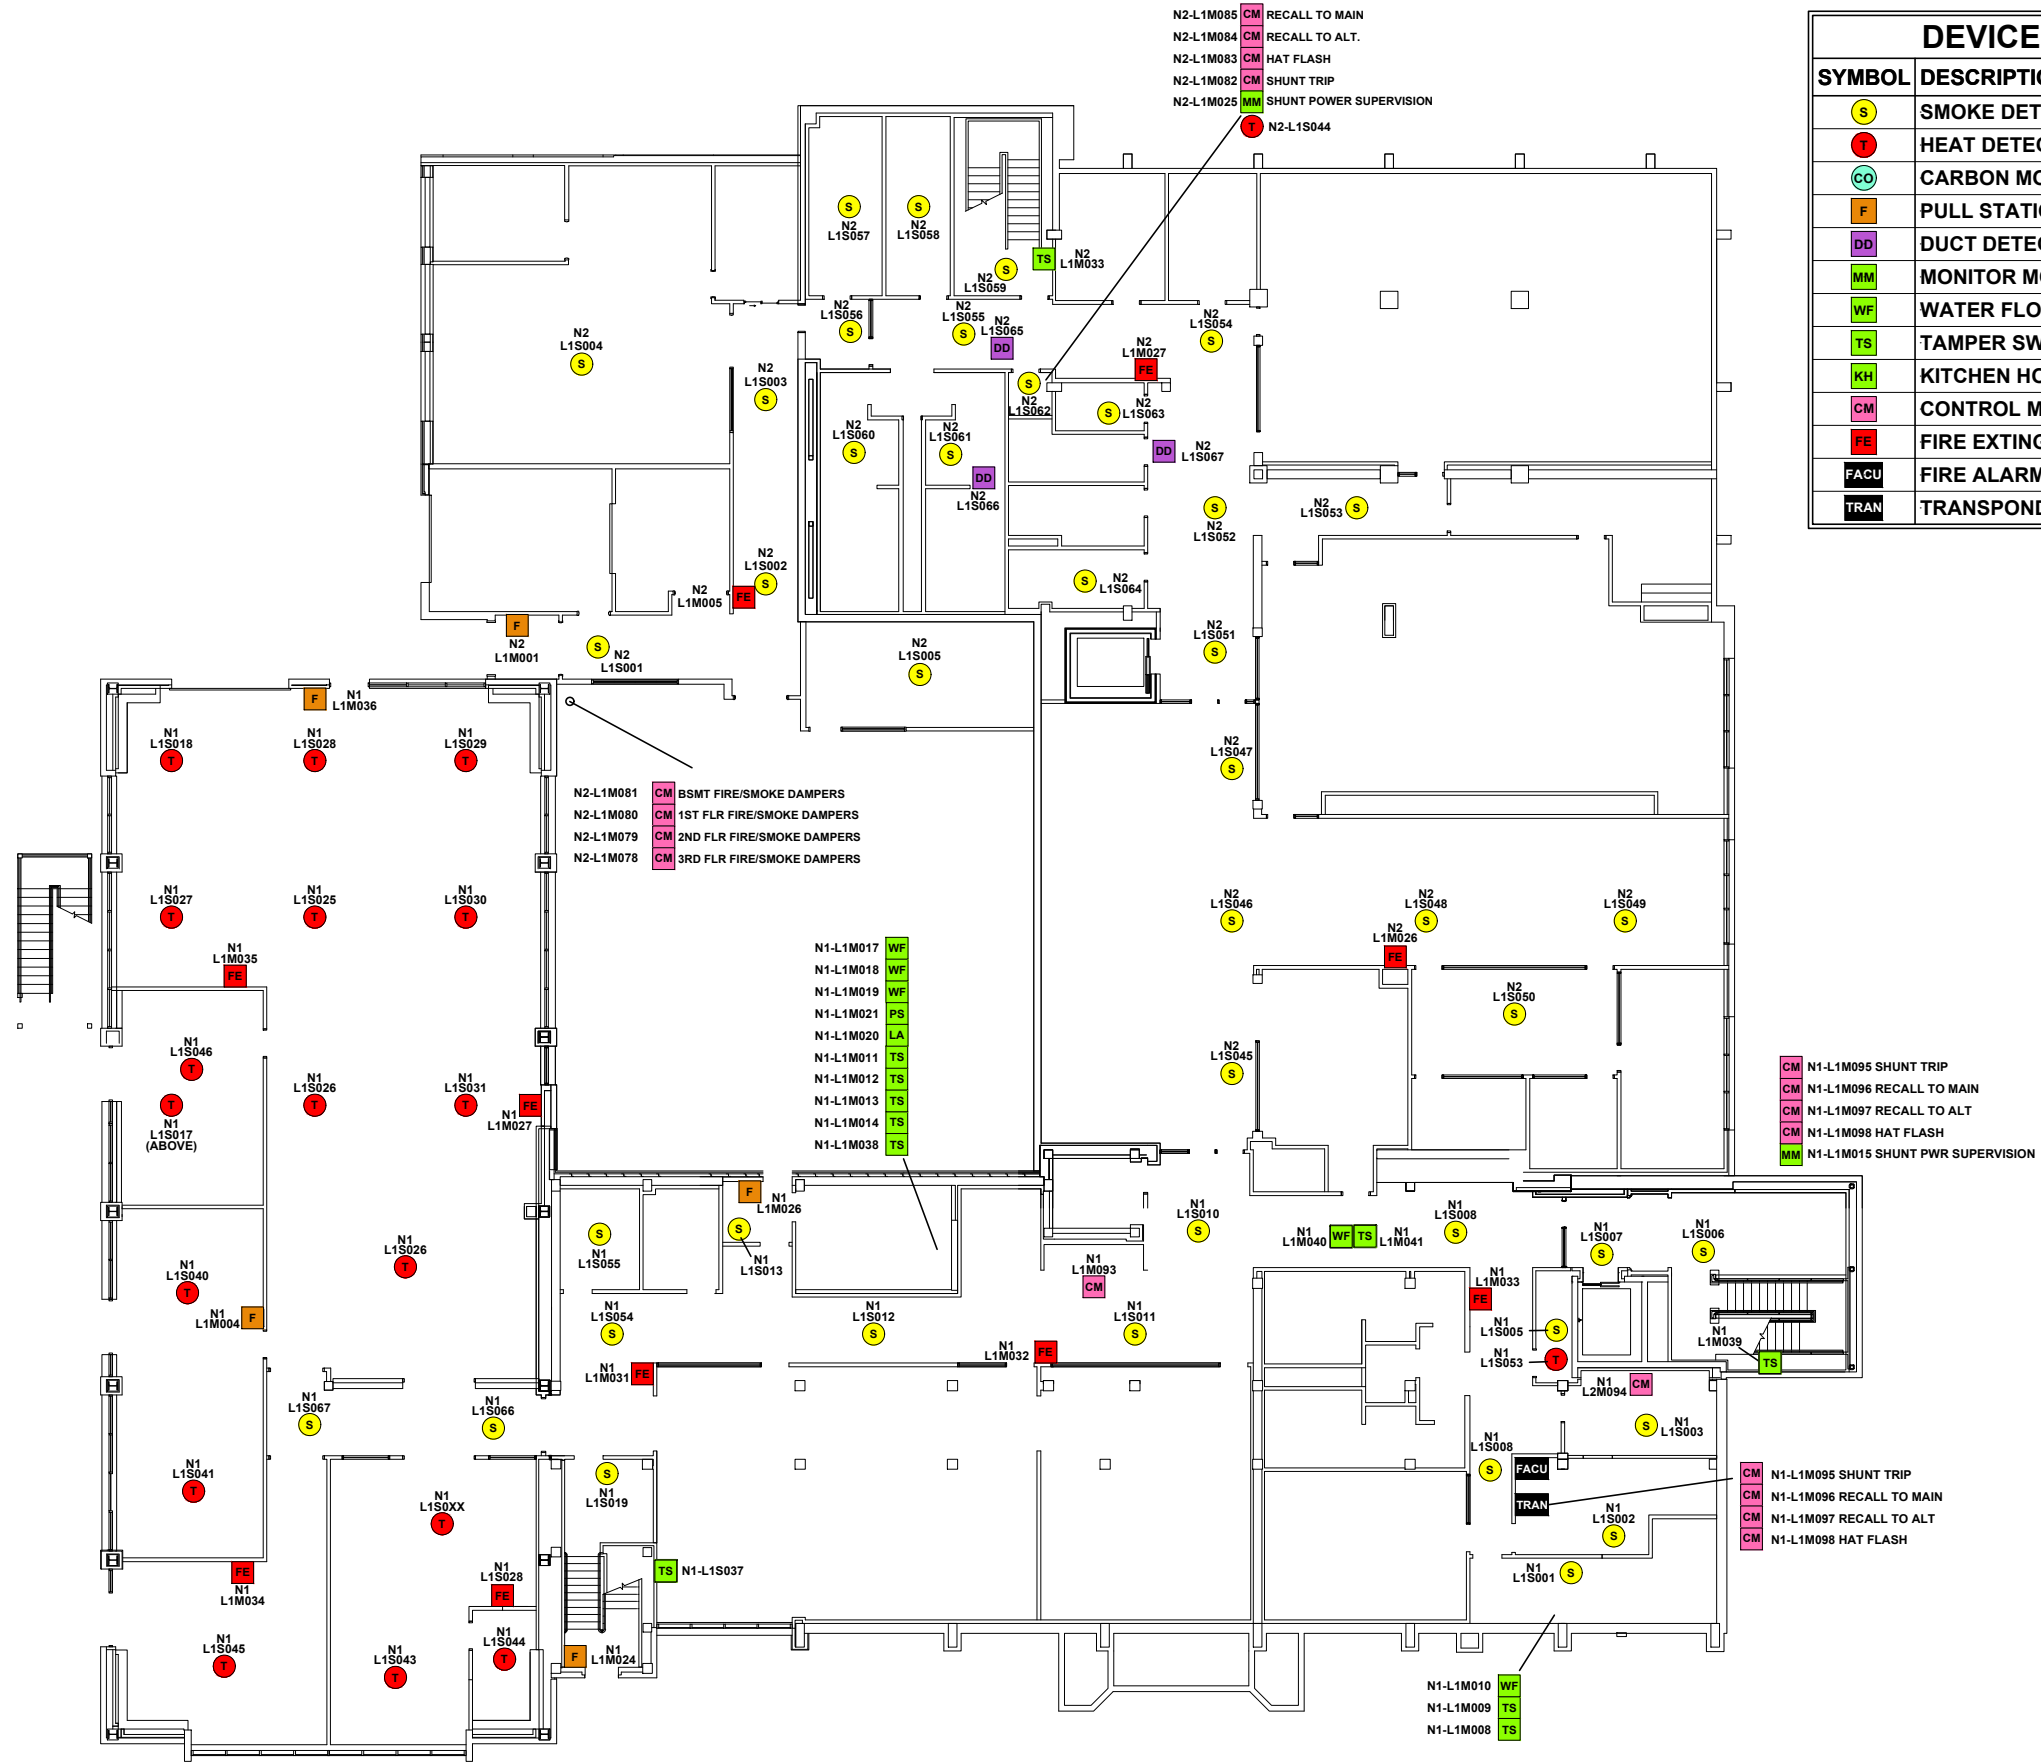

DEVICE LEGEND	
SYMBOL	DESCRIPTION
	SMOKE DETECTOR
	HEAT DETECTOR
	CARBON MONOXIDE DETECTOR
	PULL STATION
	DUCT DETECTOR
	MONITOR MODULE
	WATER FLOW SWITCH MODULE
	TAMPER SWITCH MODULE
	KITCHEN HOOD MODULE
	CONTROL MODULE
	FIRE EXTINGUISHER
	FIRE ALARM CONTROL UNIT
	TRANSPONDER PANEL



NOTE:
NFS DRAWINGS ARE BASED ON THE PROJECT ARCHITECTURE/ENGINEER (A/E) PLANS AND SPECIFICATIONS FURNISHED TO NFS. A/E IS SOLELY RESPONSIBLE (NOT NFS) FOR THE TYPE, SIZE, LOCATION, AND SUITABILITY OF ALL FIRE ALARMS, DETECTORS, AND SUPPLEMENTARY DEVICES SHOWN ON THE A/E PLANS. NFS DRAWINGS ARE TO SHOW ONLY THE WIRING DIAGRAMS BETWEEN FIRE ALARM DEVICES AND CONTROL PANELS. NFS IS NOT RESPONSIBLE FOR THE INFORMATION SHOWN ON THE A/E PLANS.

UNIVERSITY OF UTAH
KENNECOTT BUILDING PHASE 2
LOWER LEVEL
1495 EAST 100 SOUTH
SALT LAKE CITY, UTAH 84112
FIRE ALARM SYSTEM


NFS
NELSON FIRE SYSTEMS
801-468-8300

DRAWN BY:	BH
DESIGNED BY:	XXXX
APPROVED BY:	KK
DATE:	08/12/2022
SCALE:	N.T.S.
PROJECT NO:	XXXX
REVISION NO:	XXXX
DRAWING NAME:	KENNECOTT LOWER LVL FM.DWG

NELSON FIRE SYSTEMS
LOWER LEVEL

PAGE:
FINAL MAP



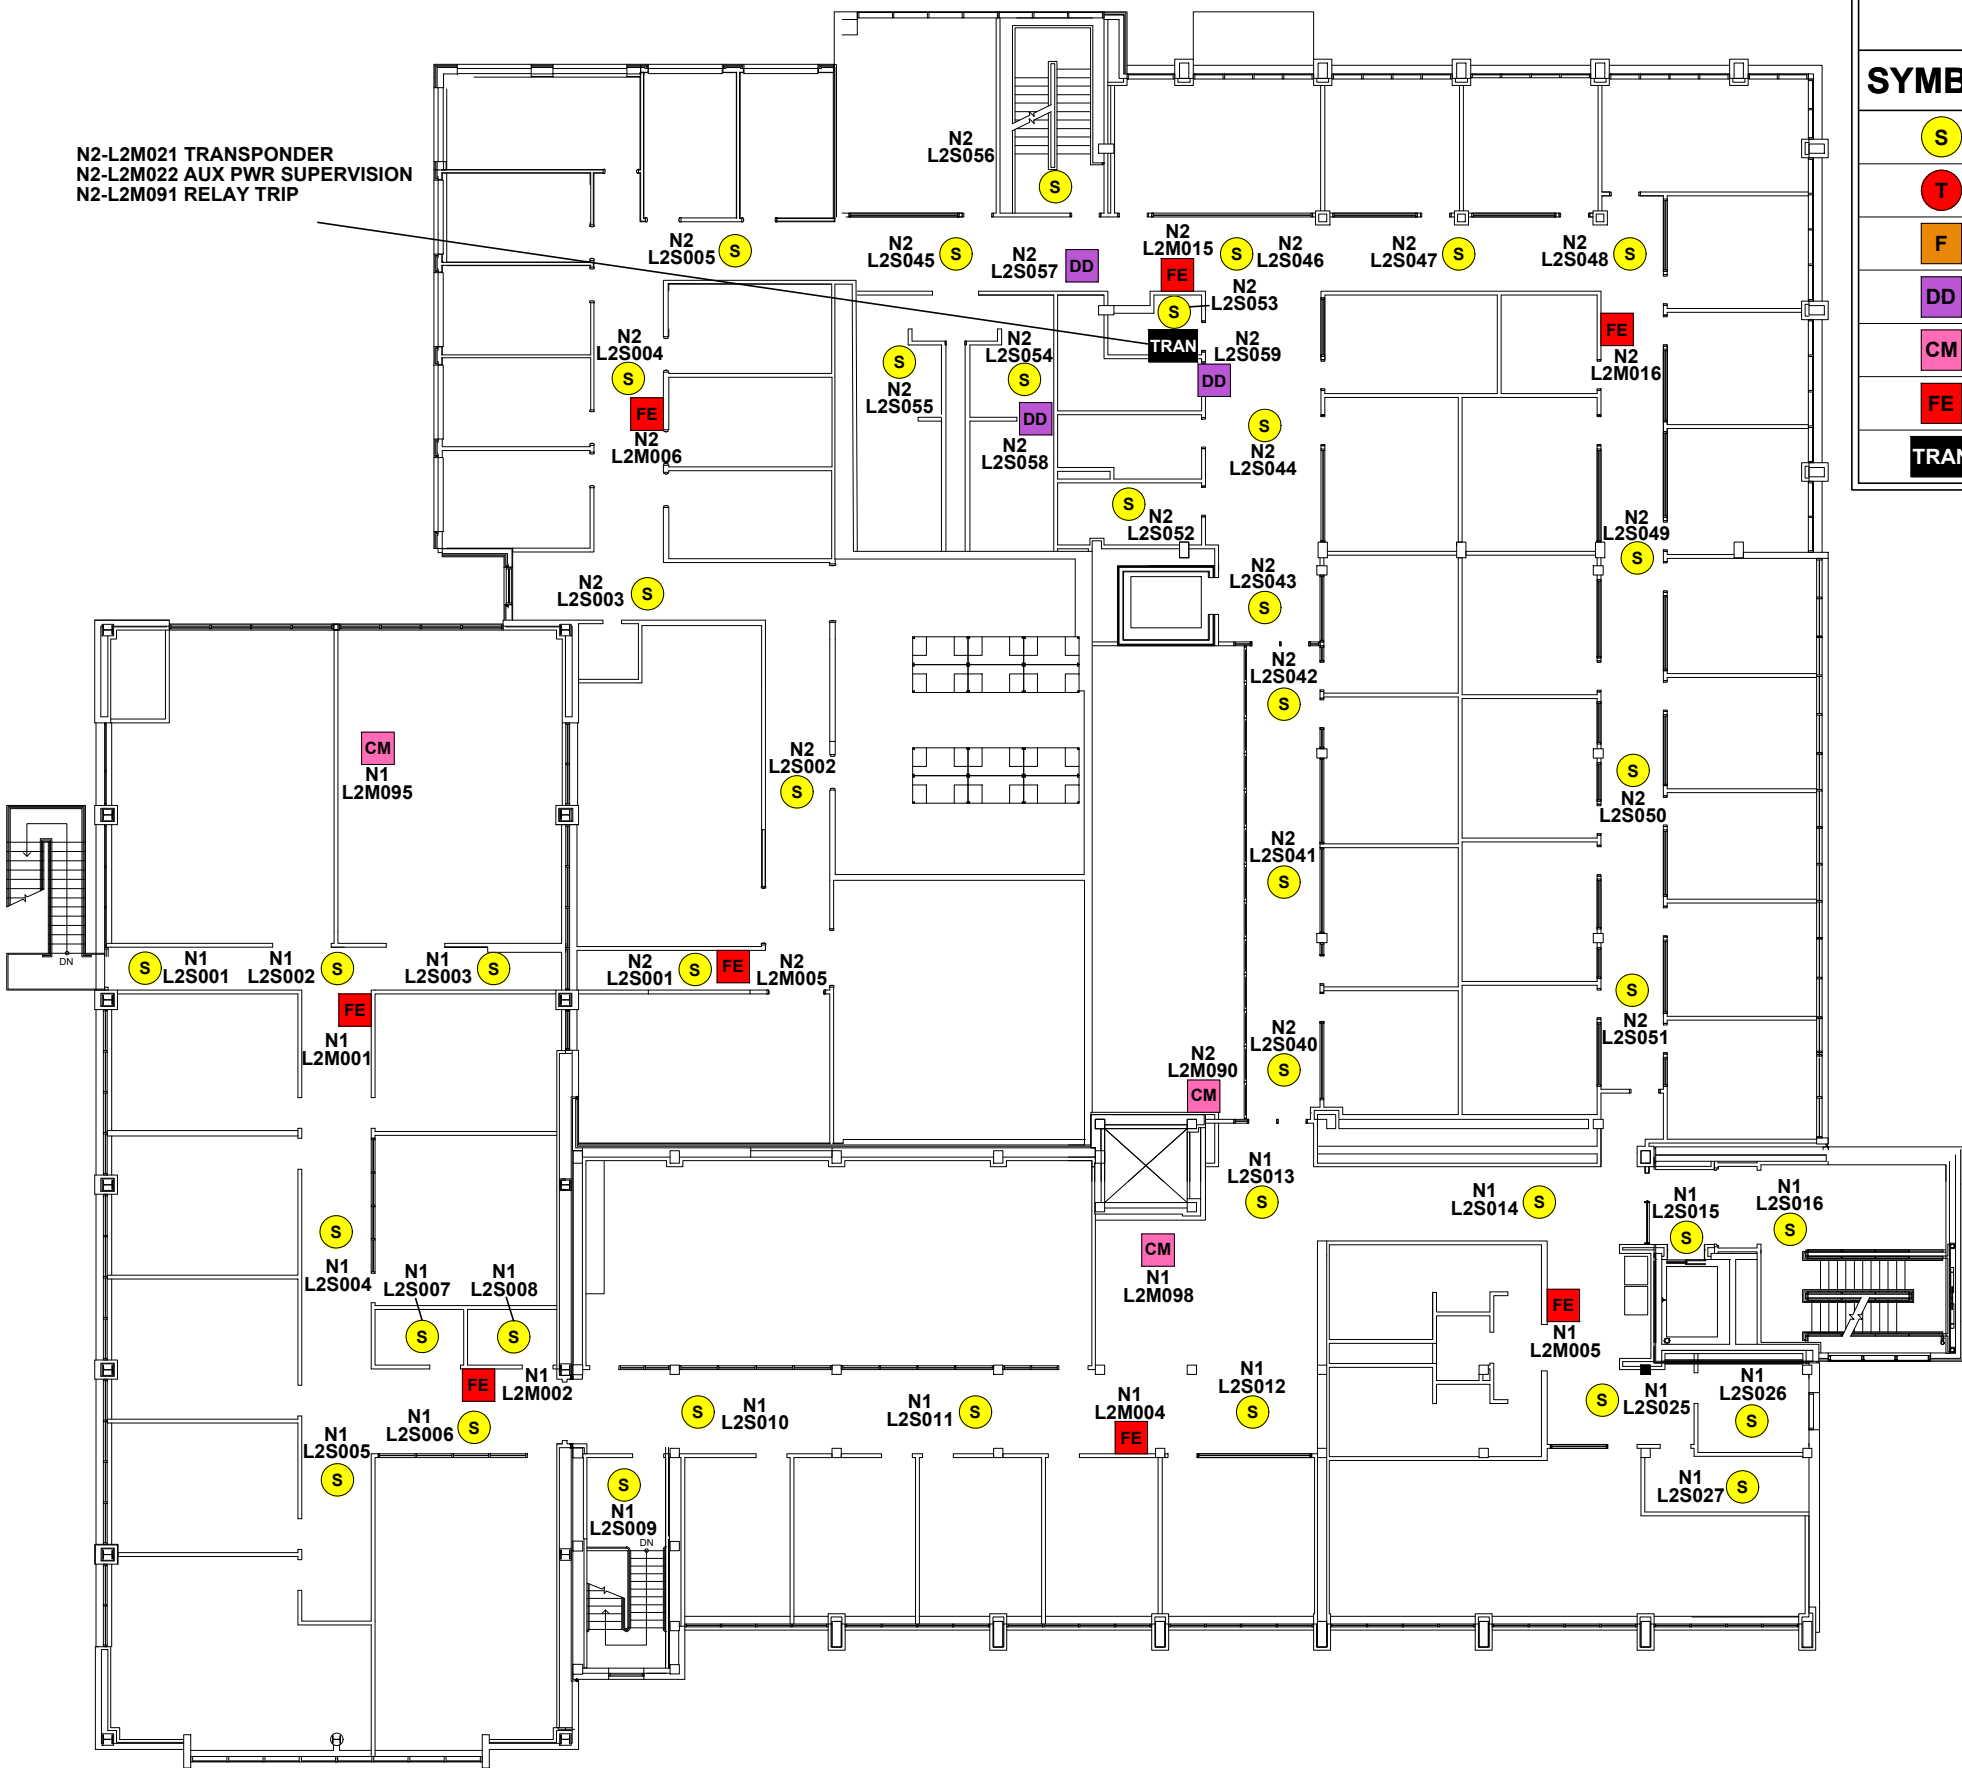

DEVICE LEGEND	
SYMBOL	DESCRIPTION
	SMOKE DETECTOR
	HEAT DETECTOR
	PULL STATION
	DUCT DETECTOR
	CONTROL MODULE
	FIRE EXTINGUISHER
	TRANSPONDER PANEL



NOTE:
NFS DRAWINGS ARE BASED ON THE PROJECT
ARCHITECTURE/ENGINEER (A/E) PLANS AND
SPECIFICATIONS FURNISHED TO NFS. A/E IS SOLELY
RESPONSIBLE (NOT NFS) FOR THE TYPE, SIZE,
LOCATION, AND SUBMITTAL OF ALL FIRE ALARMS,
CUTTING, AND OTHER DEVICES SHOWN ON
THE A/E PLANS. NFS DRAWINGS ARE TO SHOW ONLY
THE WIRING DIAGRAMS BETWEEN FIRE ALARM
DEVICES AND CONTROL PANELS. NFS IS NOT
RESPONSIBLE FOR THE INFORMATION SHOWN ON THE
A/E PLANS.

KENNECOTT BUILDING PHASE 2
LEVEL 2
UNIVERSITY OF UTAH
1495 EAST 100 SOUTH
SALT LAKE CITY, UTAH 84112
FIRE ALARM SYSTEM

NFS
NELSON FIRE SYSTEMS
801-468-8300


DRAWN BY: BH
DESIGNED BY: XXXX
APPROVED BY: KK
DATE: 08/15/2022
SCALE: N.T.S.
PROJECT NO: XXXX
REVISION NO: XXXX
DRAWING NAME:
KENNECOTT LEVEL 2 FM.DWG

NELSON FIRE SYSTEMS
SECOND LEVEL

PAGE:
FINAL MAP



SYMBOL	DESCRIPTION
	SMOKE DETECTOR
	HEAT DETECTOR
	PULL STATION
	DUCT DETECTOR
	WINCH STATUS
	CONTROL MODULE
	FIRE EXTINGUISHER

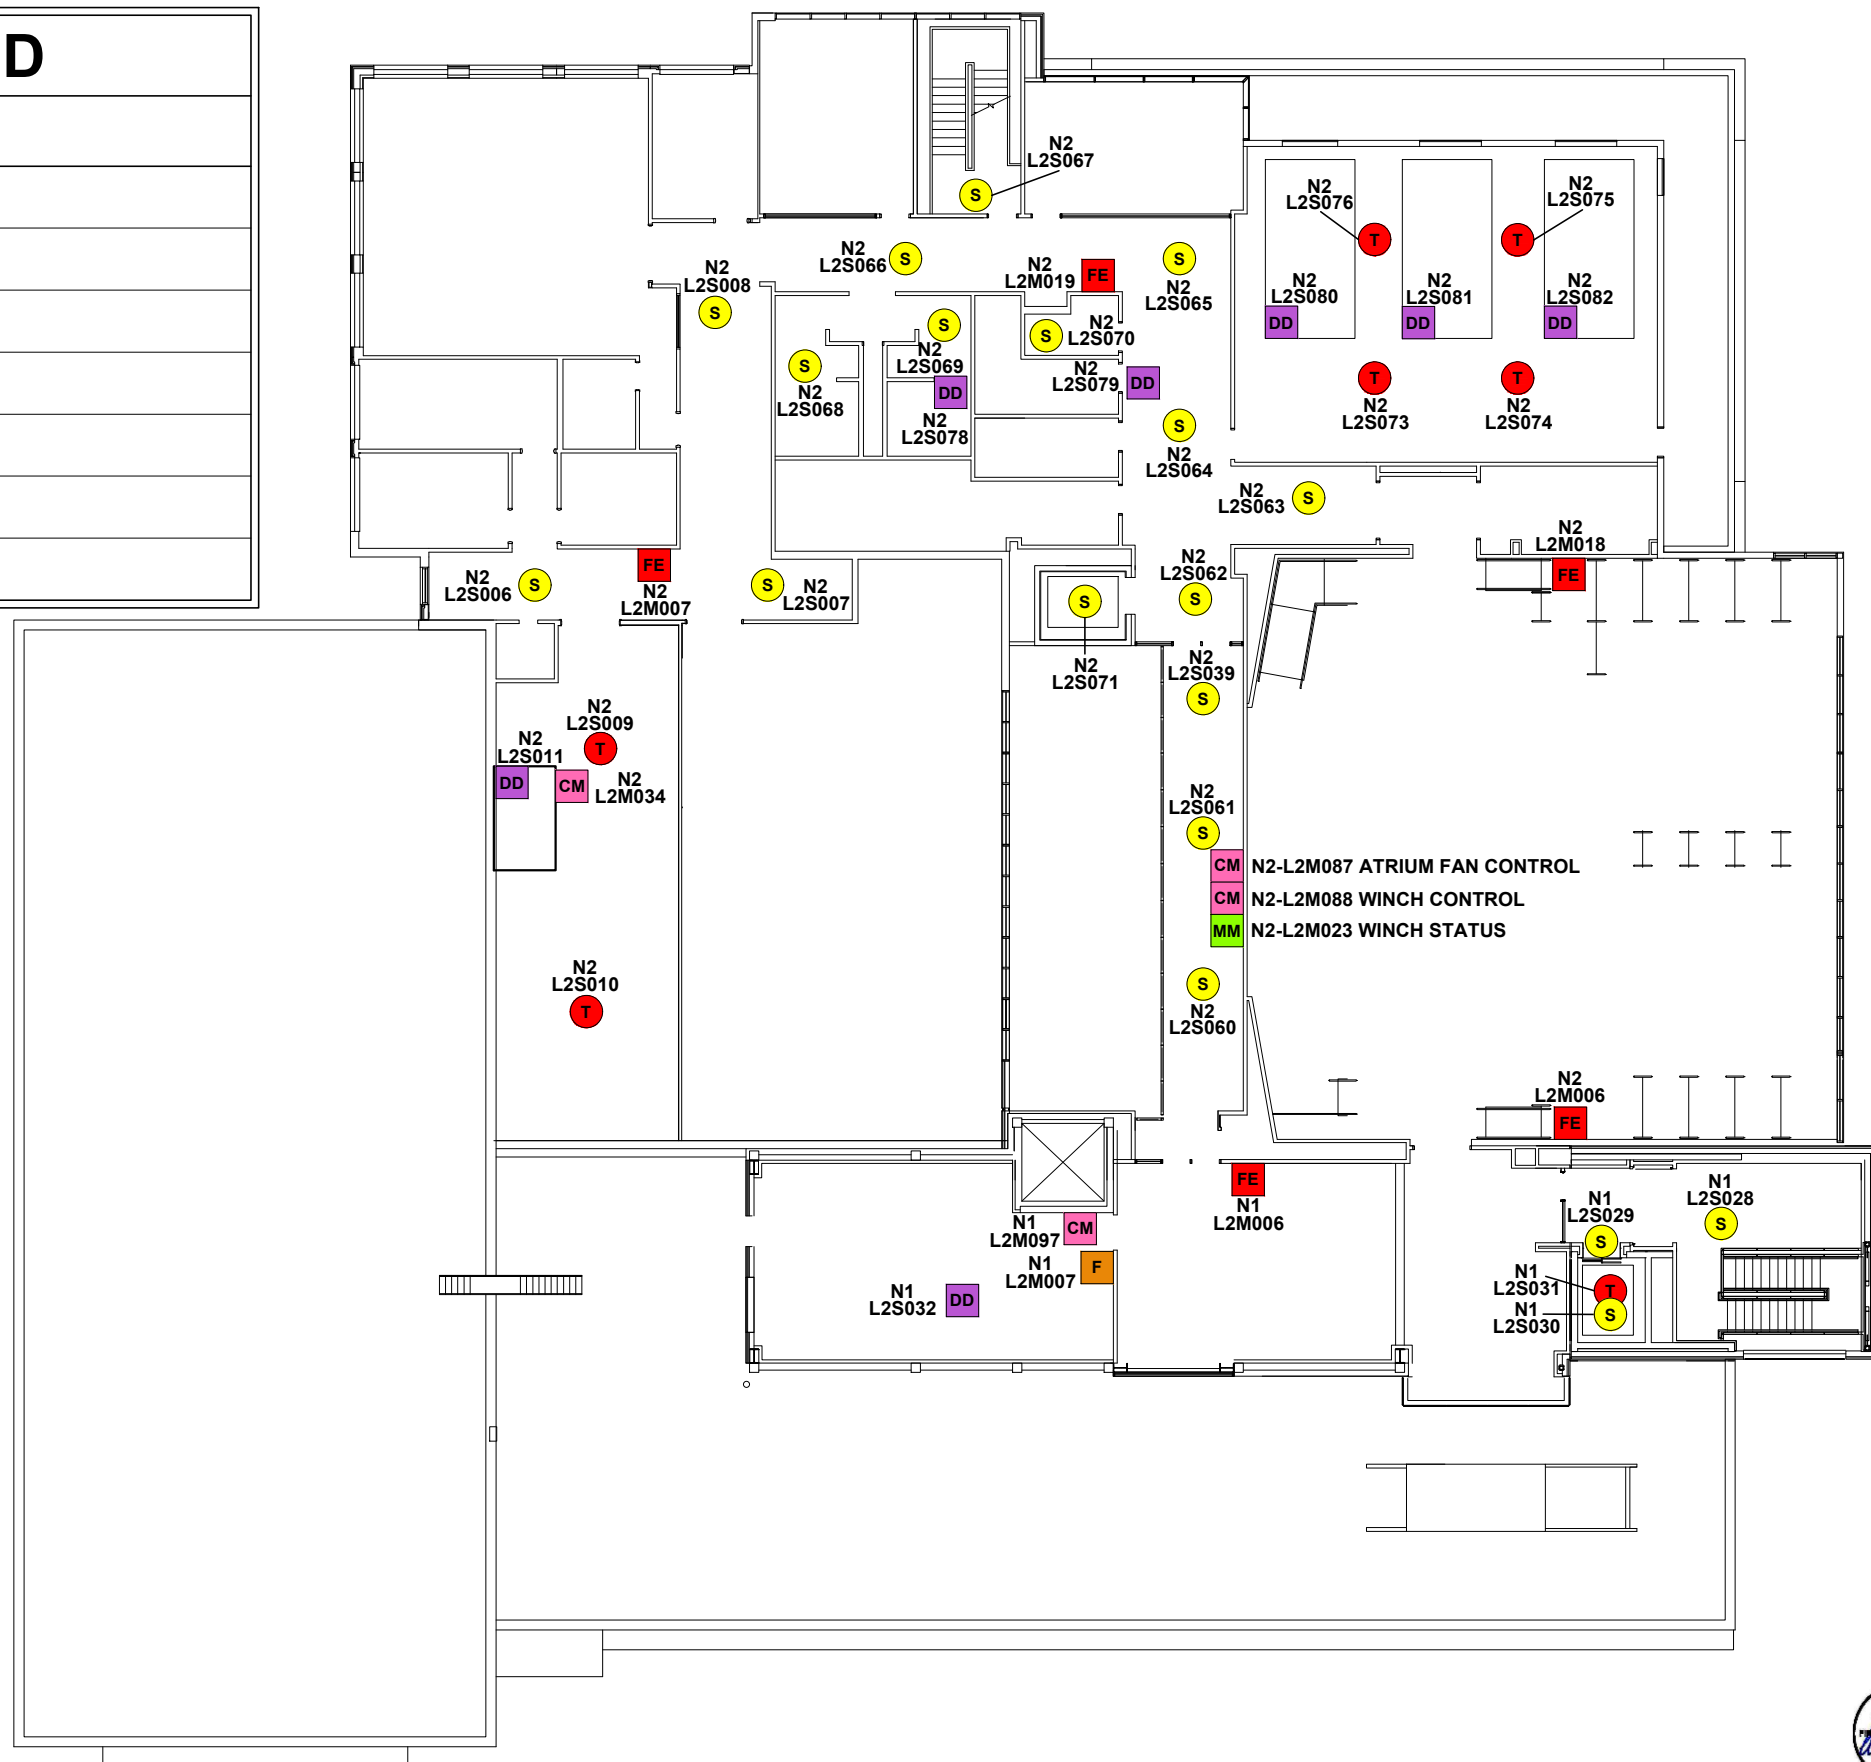

NOTE:
NFS DRAWINGS ARE BASED ON THE PROJECT ARCHITECTURE/ENGINEER (A/E) PLANS AND SPECIFICATIONS FURNISHED TO NFS. A/E IS SOLELY RESPONSIBLE (NOT NFS) FOR THE TYPE, SIZE, LOCATION, AND SUITABILITY OF ALL FIRE ALARMS, CONTROL PANELS, AND OTHER DEVICES SHOWN ON THE A/E PLANS. NFS DRAWINGS ARE TO SHOW ONLY THE WIRING DIAGRAMS BETWEEN FIRE ALARM DEVICES AND CONTROL PANELS. NFS IS NOT RESPONSIBLE FOR THE INFORMATION SHOWN ON THE A/E PLANS.

**KENNECOTT BUILDING PHASE 2
LEVEL 3
UNIVERSITY OF UTAH
1495 EAST 100 SOUTH
SALT LAKE CITY, UTAH 84112
FIRE ALARM SYSTEM**

NFS

NELSON FIRE SYSTEMS
801-468-8300

DRAWN BY:	BH
DESIGNED BY:	XXXX
APPROVED BY:	KK
DATE:	8/15/2022 2:21:00 PM
SCALE:	N.T.S.
PROJECT NO:	XXXX
REVISION NO:	XXXX
DRAWING NAME:	KENNECOTT LEVEL 3 FM.DWG

NELSON FIRE SYSTEMS

THIRD LEVEL

PAGE:
FINAL MAP

