
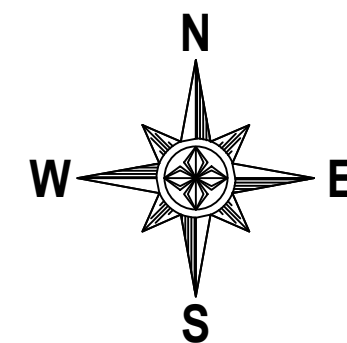


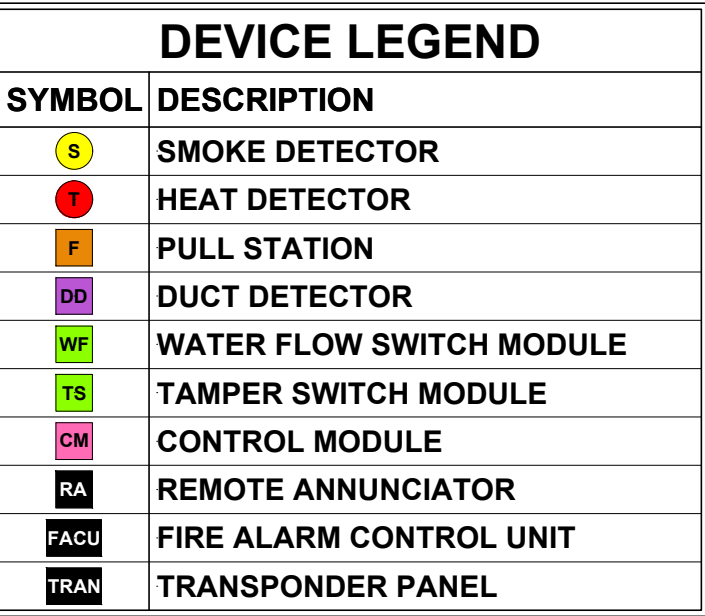

NOTE: NF'S DRAWINGS ARE BASED ON THE PROJECT ARCHITECTURE/ENGINEER (A/E) PLANS AND SPECIFICATIONS FURNISHED TO NF'S. A/E IS SOLELY RESPONSIBLE (NOT NF'S) FOR THE TYPE, SIZE, LOCATION, AND SUITABILITY OF ALL FIRE ALARMS, CONTROL PANELS, AND OTHER DEVICES SHOWN ON THE A/E PLANS. NF'S DRAWINGS ARE TO SHOW ONLY THE WIRING DIAGRAMS BETWEEN FIRE ALARM DEVICES AND CONTROL PANELS. NF'S IS NOT RESPONSIBLE FOR THE INFORMATION SHOWN ON THE A/E PLANS.

JAMES LEVOY SORENSON CENTER
FOR MEDICAL INNOVATION
UNIVERSITY OF UTAH
15 S. MARIO CAPECCHI DR, SLC, UT 84113
FIRE ALARM SYSTEM

NFS

NELSON FIRE SYSTEMS
801-468-8300

DRAWN BY:	XXXX
DESIGNED BY:	XXXX
APPROVED BY:	XXXX
DATE:	12/15/2025 6:57:14 AM
SCALE:	N.T.S.
PROJECT NO:	XXXX
REVISION NO:	XXXX
DRAWING NAME:	BASEMENT FM.DWG


NELSON FIRE SYSTEMS

BASEMENT LEVEL

PAGE:

FINAL MAP



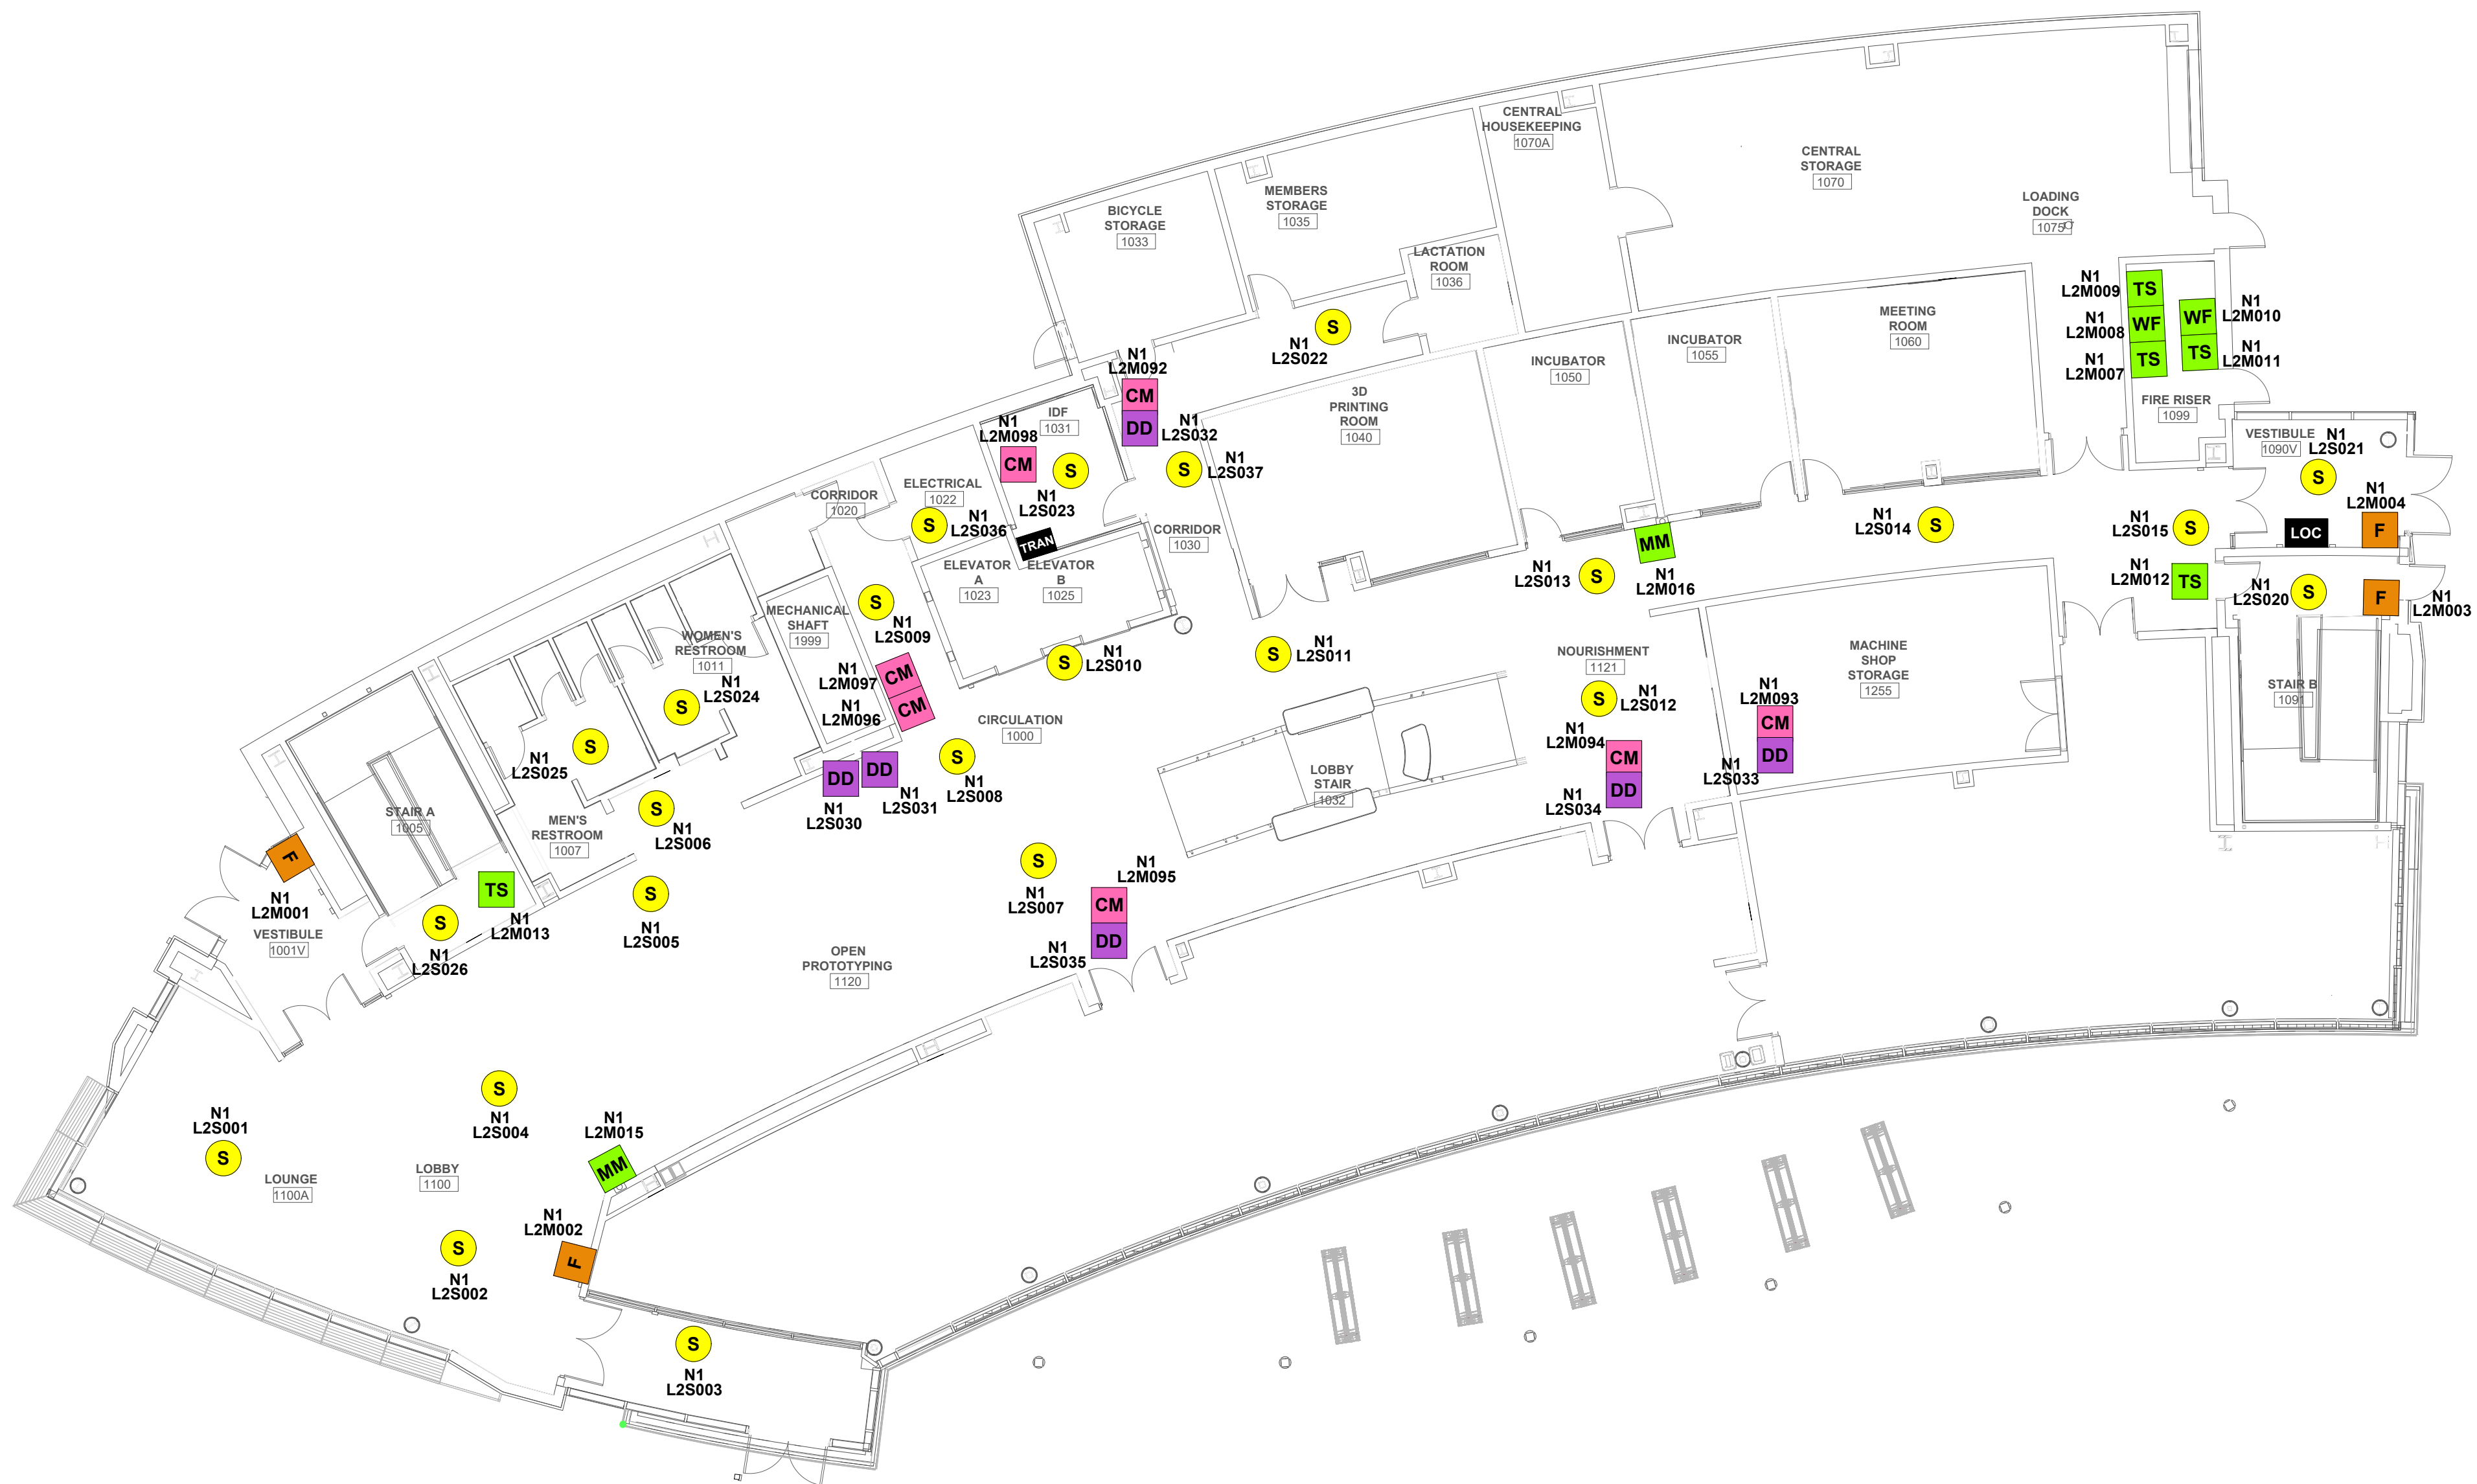

DEVICE LEGEND	
SYMBOL	DESCRIPTION
	SMOKE DETECTOR
	HEAT DETECTOR
	PULL STATION
	DUCT DETECTOR
	WATER FLOW SWITCH MODULE
	TAMPER SWITCH MODULE
	CONTROL MODULE
	LOCAL OPERATING CONSOLE
	FIRE ALARM CONTROL UNIT
	TRANSPONDER PANEL

NOTE:
NFS DRAWINGS ARE BASED ON THE PROJECT ARCHITECTURE/ENGINEER (A/E) PLANS AND SPECIFICATIONS FURNISHED TO NFS. A/E IS SOLELY RESPONSIBLE (NOT NFS) FOR THE TYPE, SIZE, LOCATION, AND SUITABILITY OF ALL FIRE ALARMS, CONTROL PANELS, AND OTHER DEVICES SHOWN ON THE A/E PLANS. NFS DRAWINGS ARE TO SHOW ONLY THE WIRING DIAGRAMS BETWEEN FIRE ALARM DEVICES AND CONTROL PANELS. NFS IS NOT RESPONSIBLE FOR THE INFORMATION SHOWN ON THE A/E PLANS.

JAMES LEVOY SORENSON CENTER
FOR MEDICAL INNOVATION
UNIVERSITY OF UTAH
15 S. MARIO CAPECCHI DR. SLC, UT 84113
FIRE ALARM SYSTEM

NFS

NELSON FIRE SYSTEMS

801-468-8300

DRAWN BY:	XXXX
DESIGNED BY:	XXXX
APPROVED BY:	XXXX
DATE:	12/10/2025 5:13:08 AM
SCALE:	N.T.S.
PROJECT NO:	XXXX
REVISION NO:	XXXX
DRAWING NAME:	LEVEL 1 FM.DWG


NELSON FIRE SYSTEMS
LEVEL 1

PAGE:

FINAL MAP



DEVICE LEGEND	
SYMBOL	DESCRIPTION
	SMOKE DETECTOR
	HEAT DETECTOR
	PULL STATION
	DUCT DETECTOR
	WATER FLOW SWITCH MODULE
	TAMPER SWITCH MODULE
	CONTROL MODULE
	REMOTE ANNUNCIATOR
	FIRE ALARM CONTROL UNIT
	TRANSPONDER PANEL

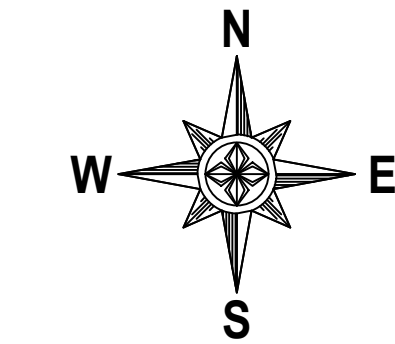

NOTE:
NFS DRAWINGS ARE BASED ON THE PROJECT ARCHITECTURE/ENGINEER (A/E) PLANS AND SPECIFICATIONS FURNISHED TO NFS. A/E IS SOLELY RESPONSIBLE (NOT NFS) FOR THE TYPE, SIZE, LOCATION, AND SUITABILITY OF ALL FIRE ALARMS, CONTROL PANELS, AND OTHER DEVICES SHOWN ON THE A/E PLANS. NFS DRAWINGS ARE TO SHOW ONLY THE WIRING DIAGRAMS BETWEEN FIRE ALARM DEVICES AND CONTROL PANELS. NFS IS NOT RESPONSIBLE FOR THE INFORMATION SHOWN ON THE A/E PLANS.

JAMES LEVOY SORENSON CENTER
FOR MEDICAL INNOVATION
UNIVERSITY OF UTAH
15 S. MARIO CAPECCHI DR. SLC, UT 84113
FIRE ALARM SYSTEM

NFS

NELSON FIRE SYSTEMS
801-468-8300


DRAWN BY: XXXX
DESIGNED BY: XXXX
APPROVED BY: XXXX
DATE: 12/15/2025 6:55:09 AM
SCALE: N.T.S.
PROJECT NO: XXXX
REVISION NO: XXXX
DRAWING NAME:
LEVEL 2 FM.DWG

NELSON FIRE SYSTEMS


LEVEL 2

PAGE:

FINAL MAP

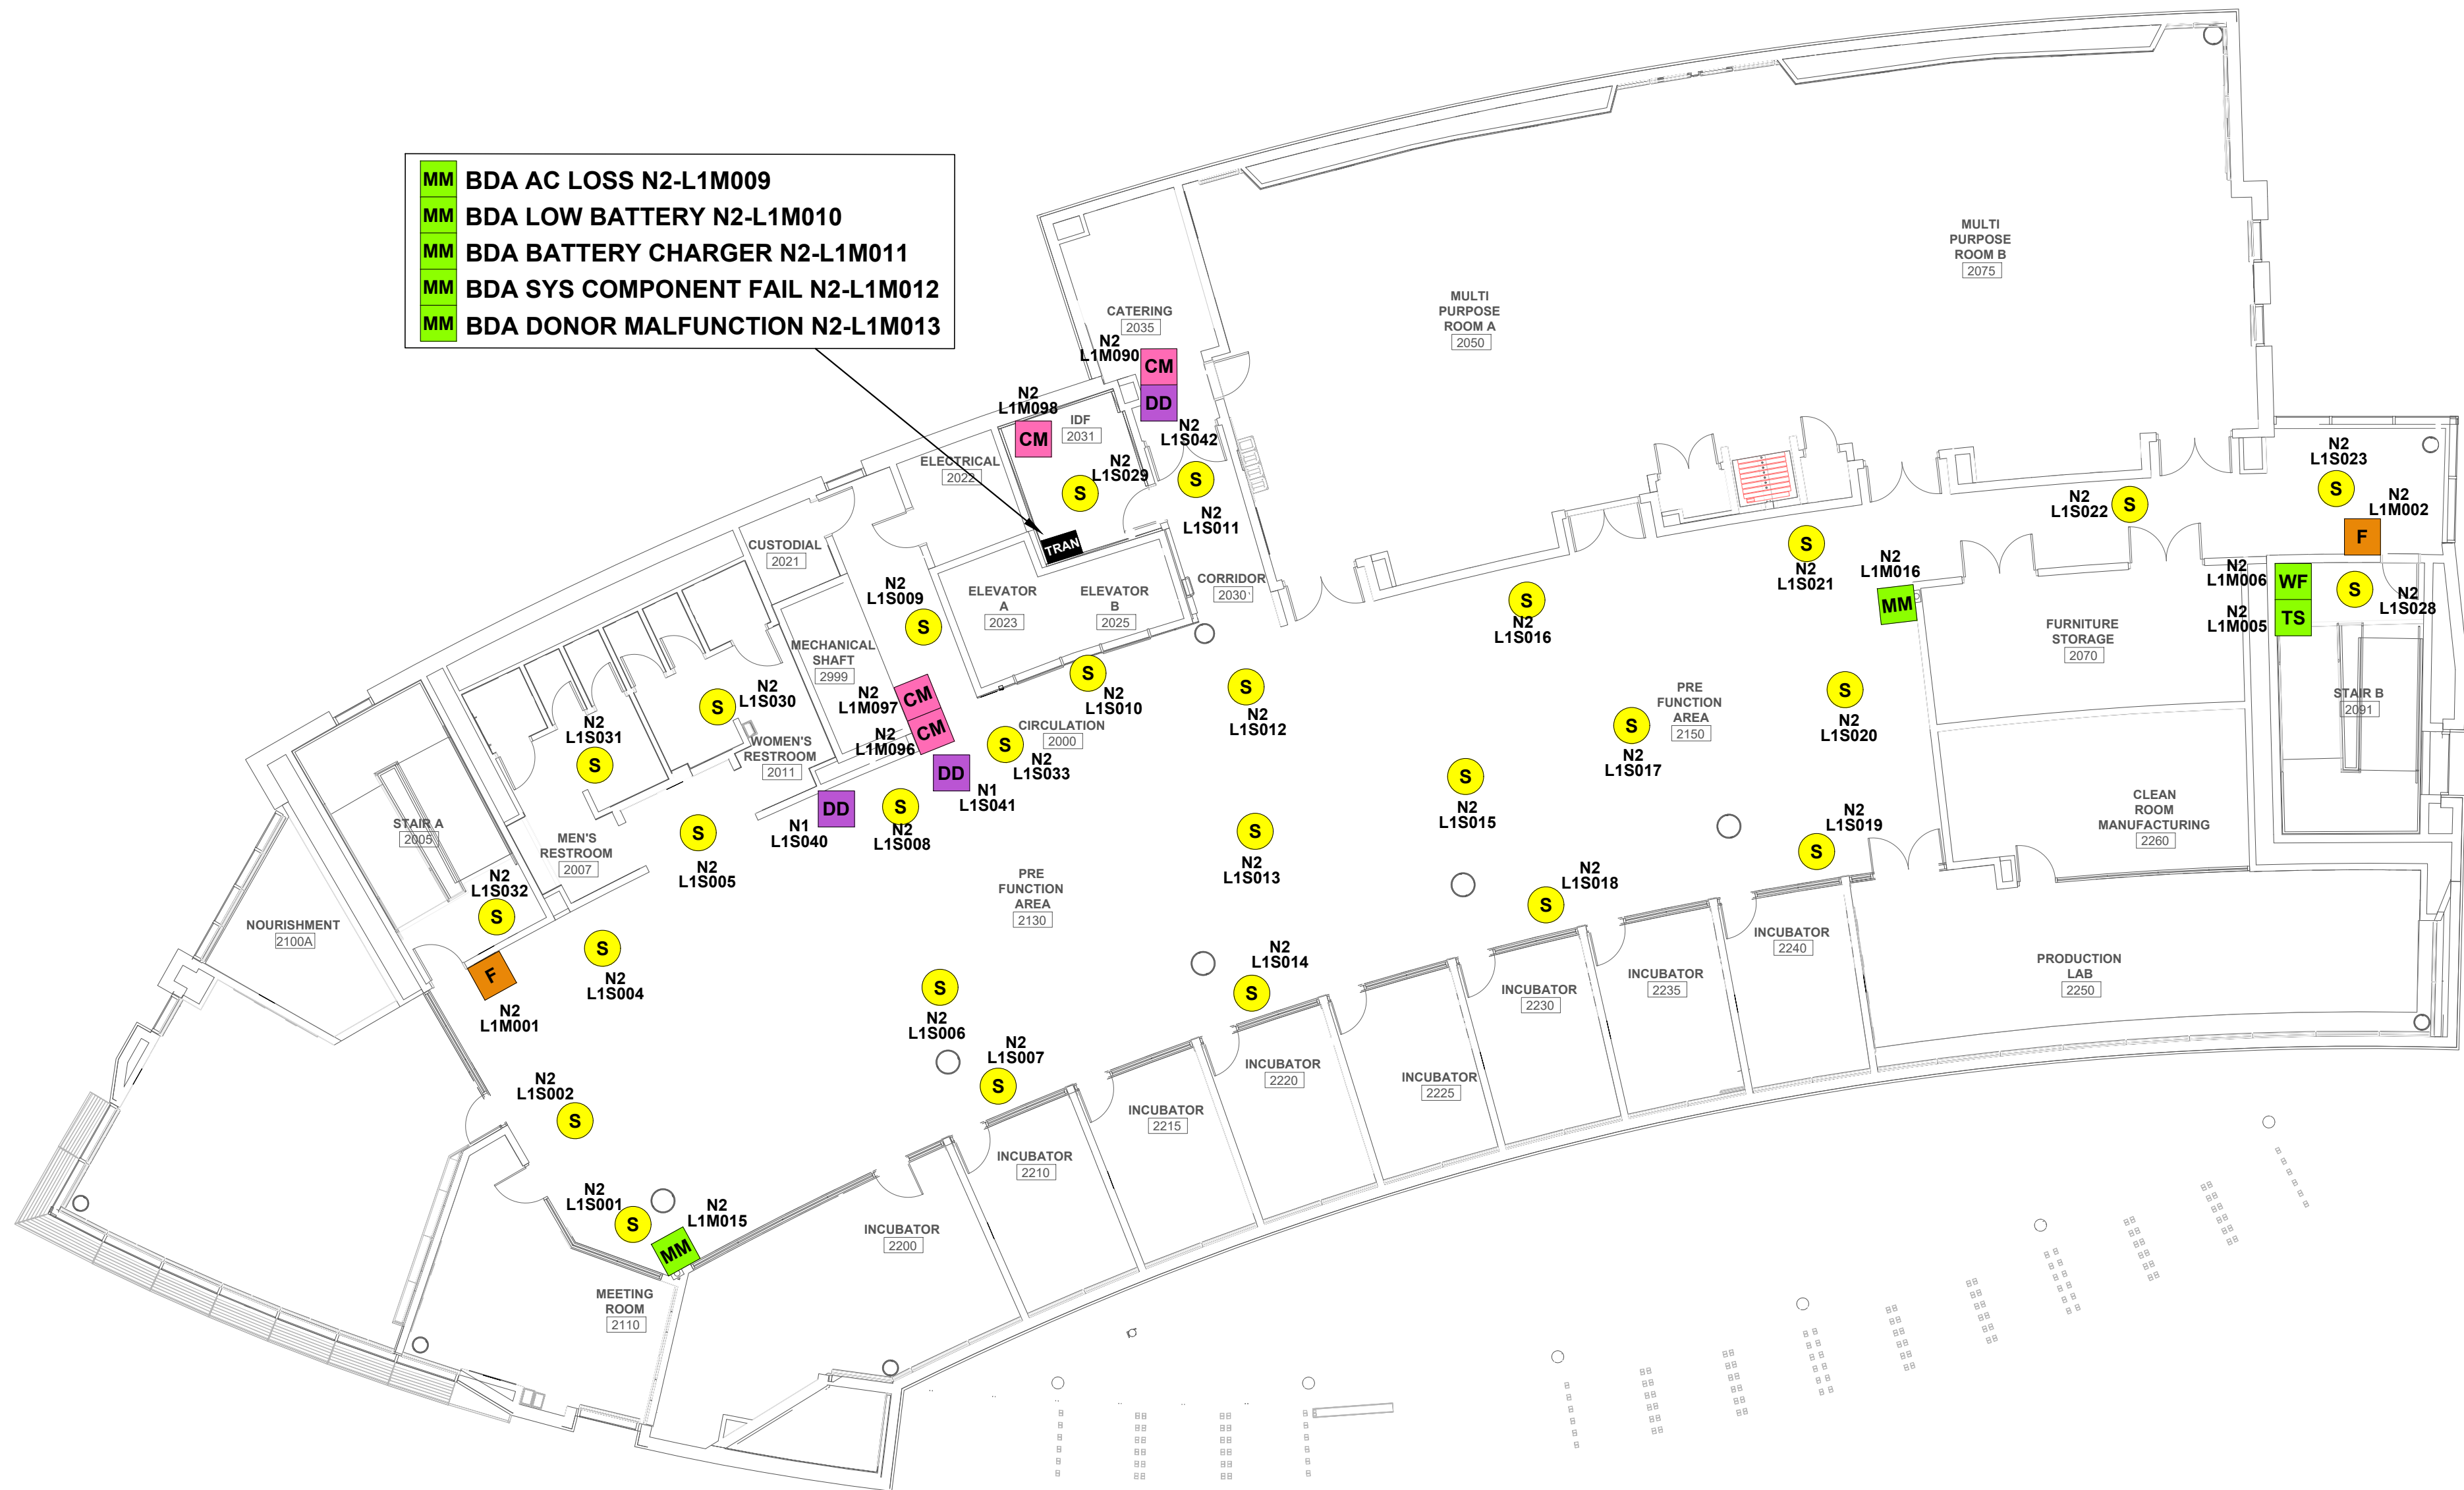

NOTE: NFS DRAWINGS ARE BASED ON THE PROJECT ARCHITECTURE/ENGINEER (A/E) PLANS AND SPECIFICATIONS FURNISHED TO NFS. A/E IS SOLELY RESPONSIBLE (NOT NFS) FOR THE TYPE, SIZE, LOCATION, AND SUITABILITY OF ALL FIRE ALARMS, CONTROL PANELS, AND OTHER DEVICES SHOWN ON THE A/E PLANS. NFS DRAWINGS ARE TO SHOW ONLY THE WIRING DIAGRAMS BETWEEN FIRE ALARM DEVICES AND CONTROL PANELS. NFS IS NOT RESPONSIBLE FOR THE INFORMATION SHOWN ON THE A/E PLANS.

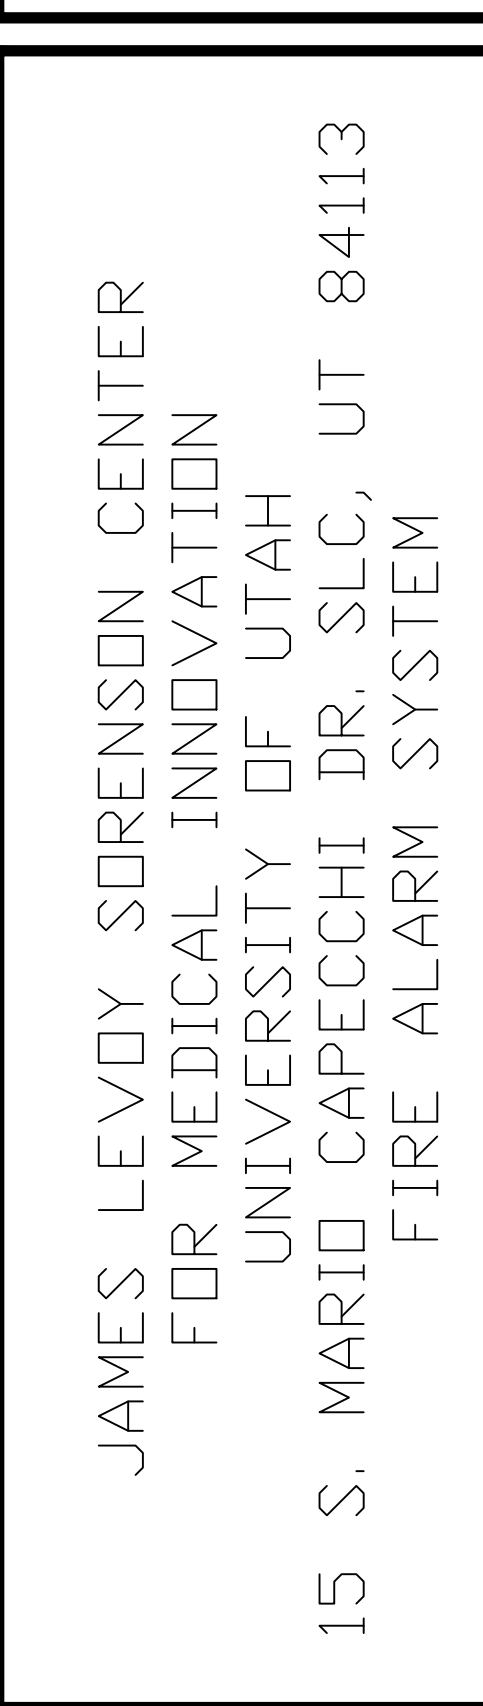


DRAWN BY:	XX
DESIGNED BY:	XX
APPROVED BY:	XX
DATE:	12/10/2025 5:09:36
SCALE:	N.T.
PROJECT NO:	XX
REVISION NO:	XX
DRAWING NAME:	
LEVEL 3 FM.DWG	

PAGE:

FINAL MAP



NOTE:
NFS DRAWINGS ARE BASED ON THE PROJECT ARCHITECTURE/ENGINEER (A/E) PLANS AND SPECIFICATIONS FURNISHED TO NFS. A/E IS SOLELY RESPONSIBLE (NOT NFS) FOR THE TYPE, SIZE, LOCATION, AND SUITABILITY OF ALL FIRE ALARMS, CONTROL PANELS, AND OTHER DEVICES SHOWN ON THE A/E PLANS. NFS DRAWINGS ARE TO SHOW ONLY THE WIRING DIAGRAMS BETWEEN FIRE ALARM DEVICES AND CONTROL PANELS. NFS IS NOT RESPONSIBLE FOR THE INFORMATION SHOWN ON THE A/E PLANS.

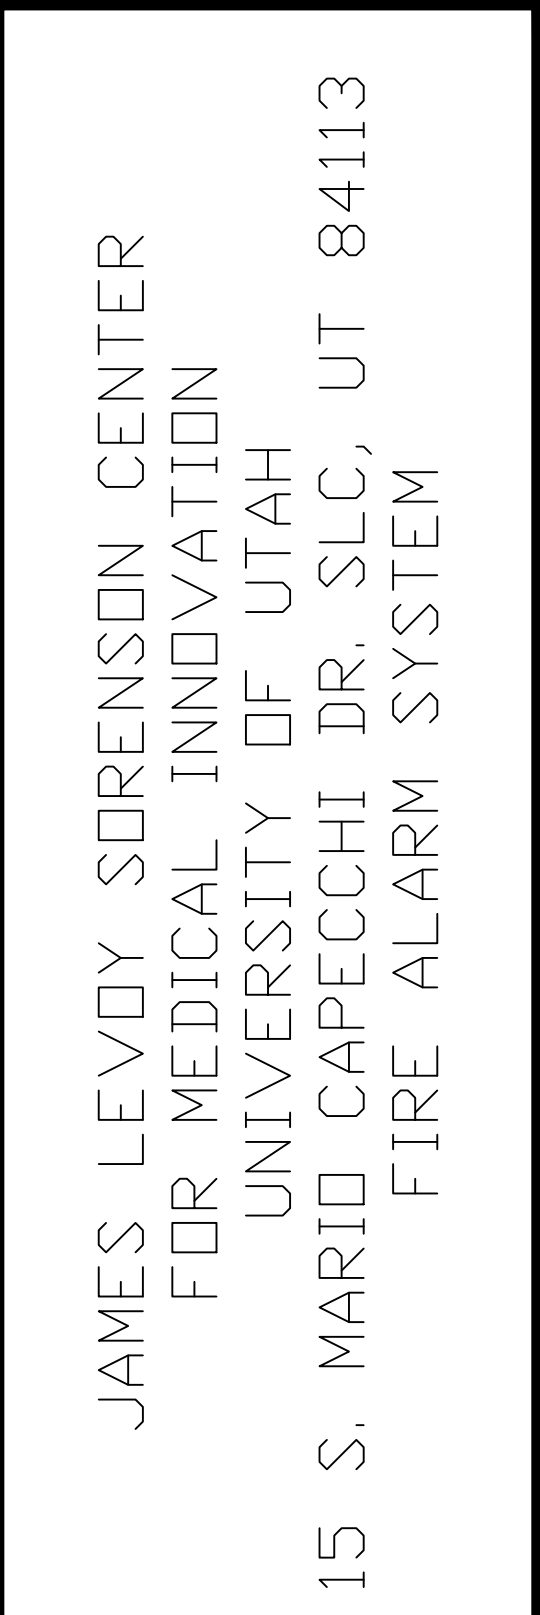

DRAWN BY:	XXXX
DESIGNED BY:	XXXX
APPROVED BY:	XXXX
DATE:	12/10/2025 5:15:06 AM
SCALE:	N.T.S.
PROJECT NO:	XXXX
REVISION NO:	XXXX
DRAWING NAME:	LEVEL 4 FM.DWG

PAGE: **FINAL MAP**

