
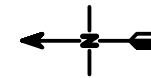


_____ NODE NUMBER
 _____ ADDRESSABLE LOOP NUMBER
 _____ SENSOR ('M' MONITOR)
 _____ DEVICE NUMBER
 N1-1S01

DEVICE LEGEND	
SYMBOL	DESCRIPTION
Ⓢ	SMOKE DETECTOR
Ⓣ	THERMAL DETECTOR
ⓕ	MANUAL PULL STATION
ⓓⓓ	DUCT SMOKE DETECTOR
ⓌⓉ	WATERFLOW SWITCH MONITOR MODULE
ⓉⓈ	TAMPER SWITCH MONITOR MODULE
ⓂⓂ	MONITOR MODULE
ⓐⓂ	CONTROL MODULE
Ⓡⓐ	REMOTE ANNUNCIATOR
ⓕⓐⓐ	FIRE ALARM CONTROL PANEL
ⓉⓇⓐⓂ	TRANSPONDER PANEL
ⓕⓐⓐ	FIRE ALARM CONTROL PANEL
Ⓡⓓⓕ	VOICE PANEL
Ⓡⓐⓐ	REMOTE COMMAND CENTER
ⓓⓓ	ATRIUM VESDA PANEL

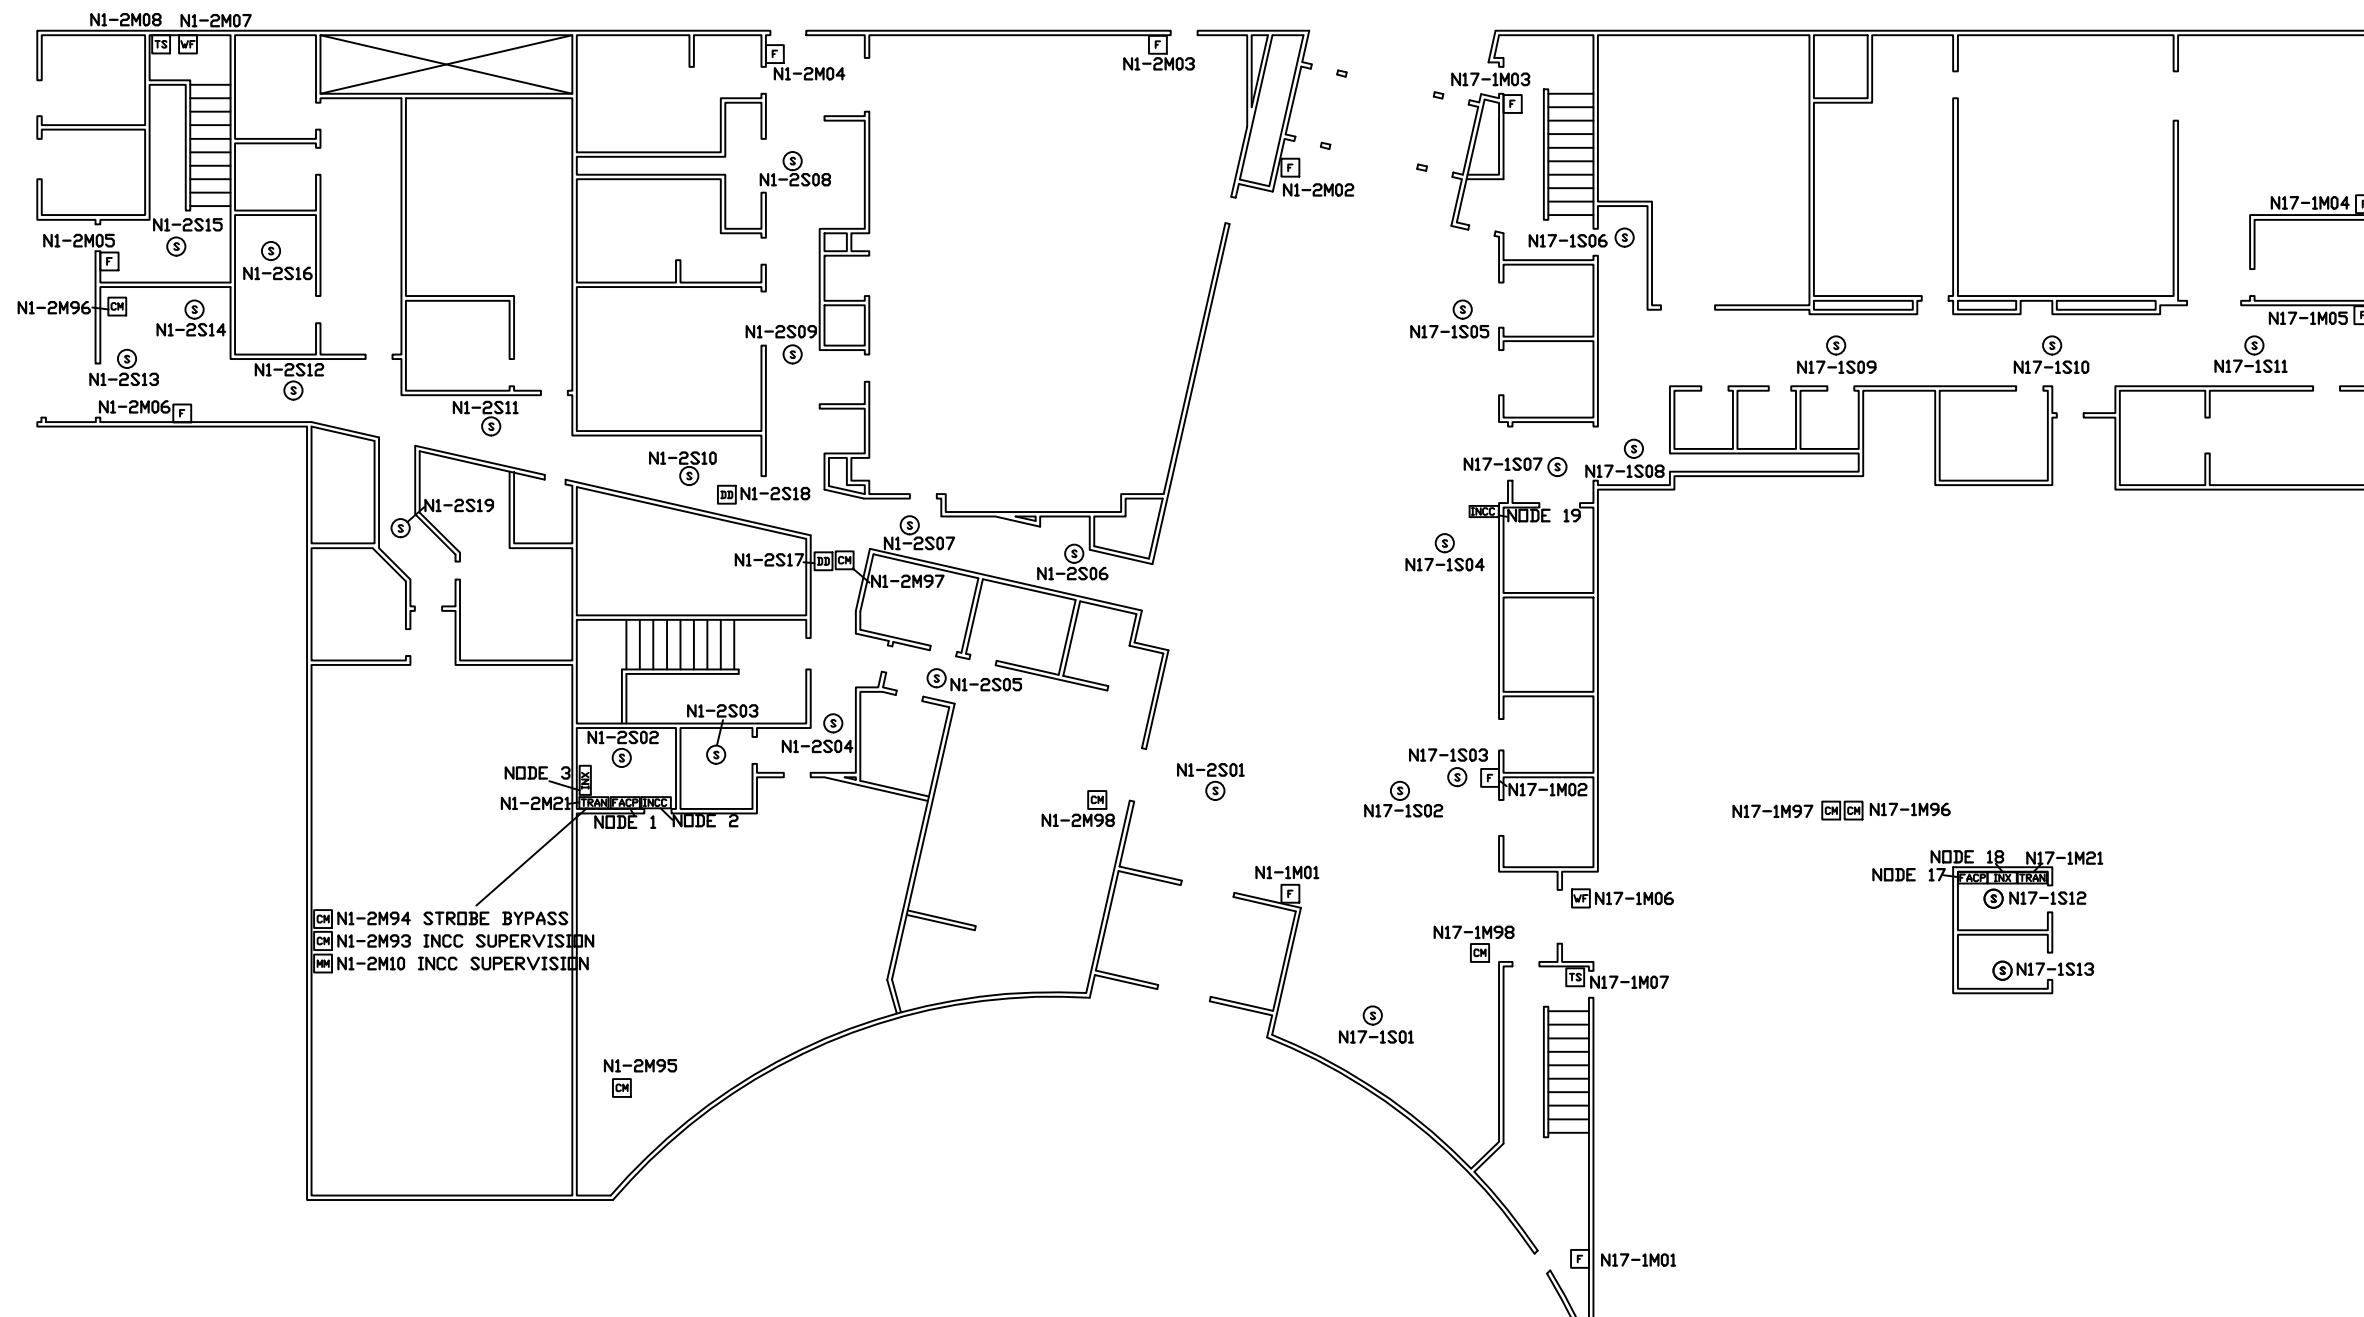

NOTE: NFS DRAWINGS ARE BASED ON THE PROJECT ARCHITECT/ENGINEER (A/E) PLANS AND SPECIFICATIONS FURNISHED TO NFS. A/E IS SOLELY RESPONSIBLE (NOT NFS) FOR THE TYPE, SIZE, LOCATION, AND SUITABILITY OF ALL FIRE ALARMS, CONTROL PANELS, AND OTHER DEVICES SHOWN ON THE A/E PLANS. NFS DRAWINGS ARE TO SHOW ONLY THE WIRING DIAGRAMS BETWEEN FIRE ALARM DEVICES AND CONTROL PANELS. NFS IS NOT RESPONSIBLE FOR THE INFORMATION SHOWN ON THE A/E PLANS.

MORAN EYE CENTER II
LEVEL I
FIRE ALARM SYSTEM
UNIVERSITY OF UTAH
SALT LAKE CITY, UTAH

NFS
NELSON FIRE SYSTEMS
801-468-8300

DRAWN BY:	DS
DATE:	3/20/2013
ADDENDUM #'S:	1,2,3,4
CHANGE ORDERS:	
SCALE:	N.T.S.
PROJECT NO:	XXXX
REV NO:	XXXX
DRAWING NAME:	
MORAN II LEVEL I.DWG	


FIRE ALARM SYSTEM

LEVEL I



ADDRESSABLE LOOP NUMBERS

NFS

NFS I

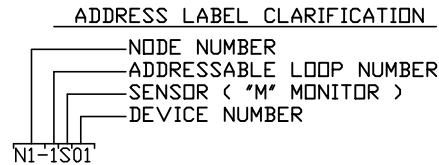

DEVICE LEGEND	
SYMBOL	DESCRIPTION
Ⓢ	SMOKE DETECTOR
Ⓣ	THERMAL DETECTOR
F	MANUAL PULL STATION
DB	DUCT SMOKE DETECTOR
WF	WATERFLOW SWITCH MONITOR MODULE
TS	TAMPER SWITCH MONITOR MODULE
CM	MONITOR MODULE
CH	CONTROL MODULE
RA	REMOTE ANNUNCIATOR
FACP	FIRE ALARM CONTROL PANEL
TRAN	TRANSPONDER PANEL
FACP	FIRE ALARM CONTROL PANEL
INX	VOICE PANEL
INCC	REMOTE COMMAND CENTER
VSD	ATRIUM VESDA PANEL

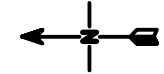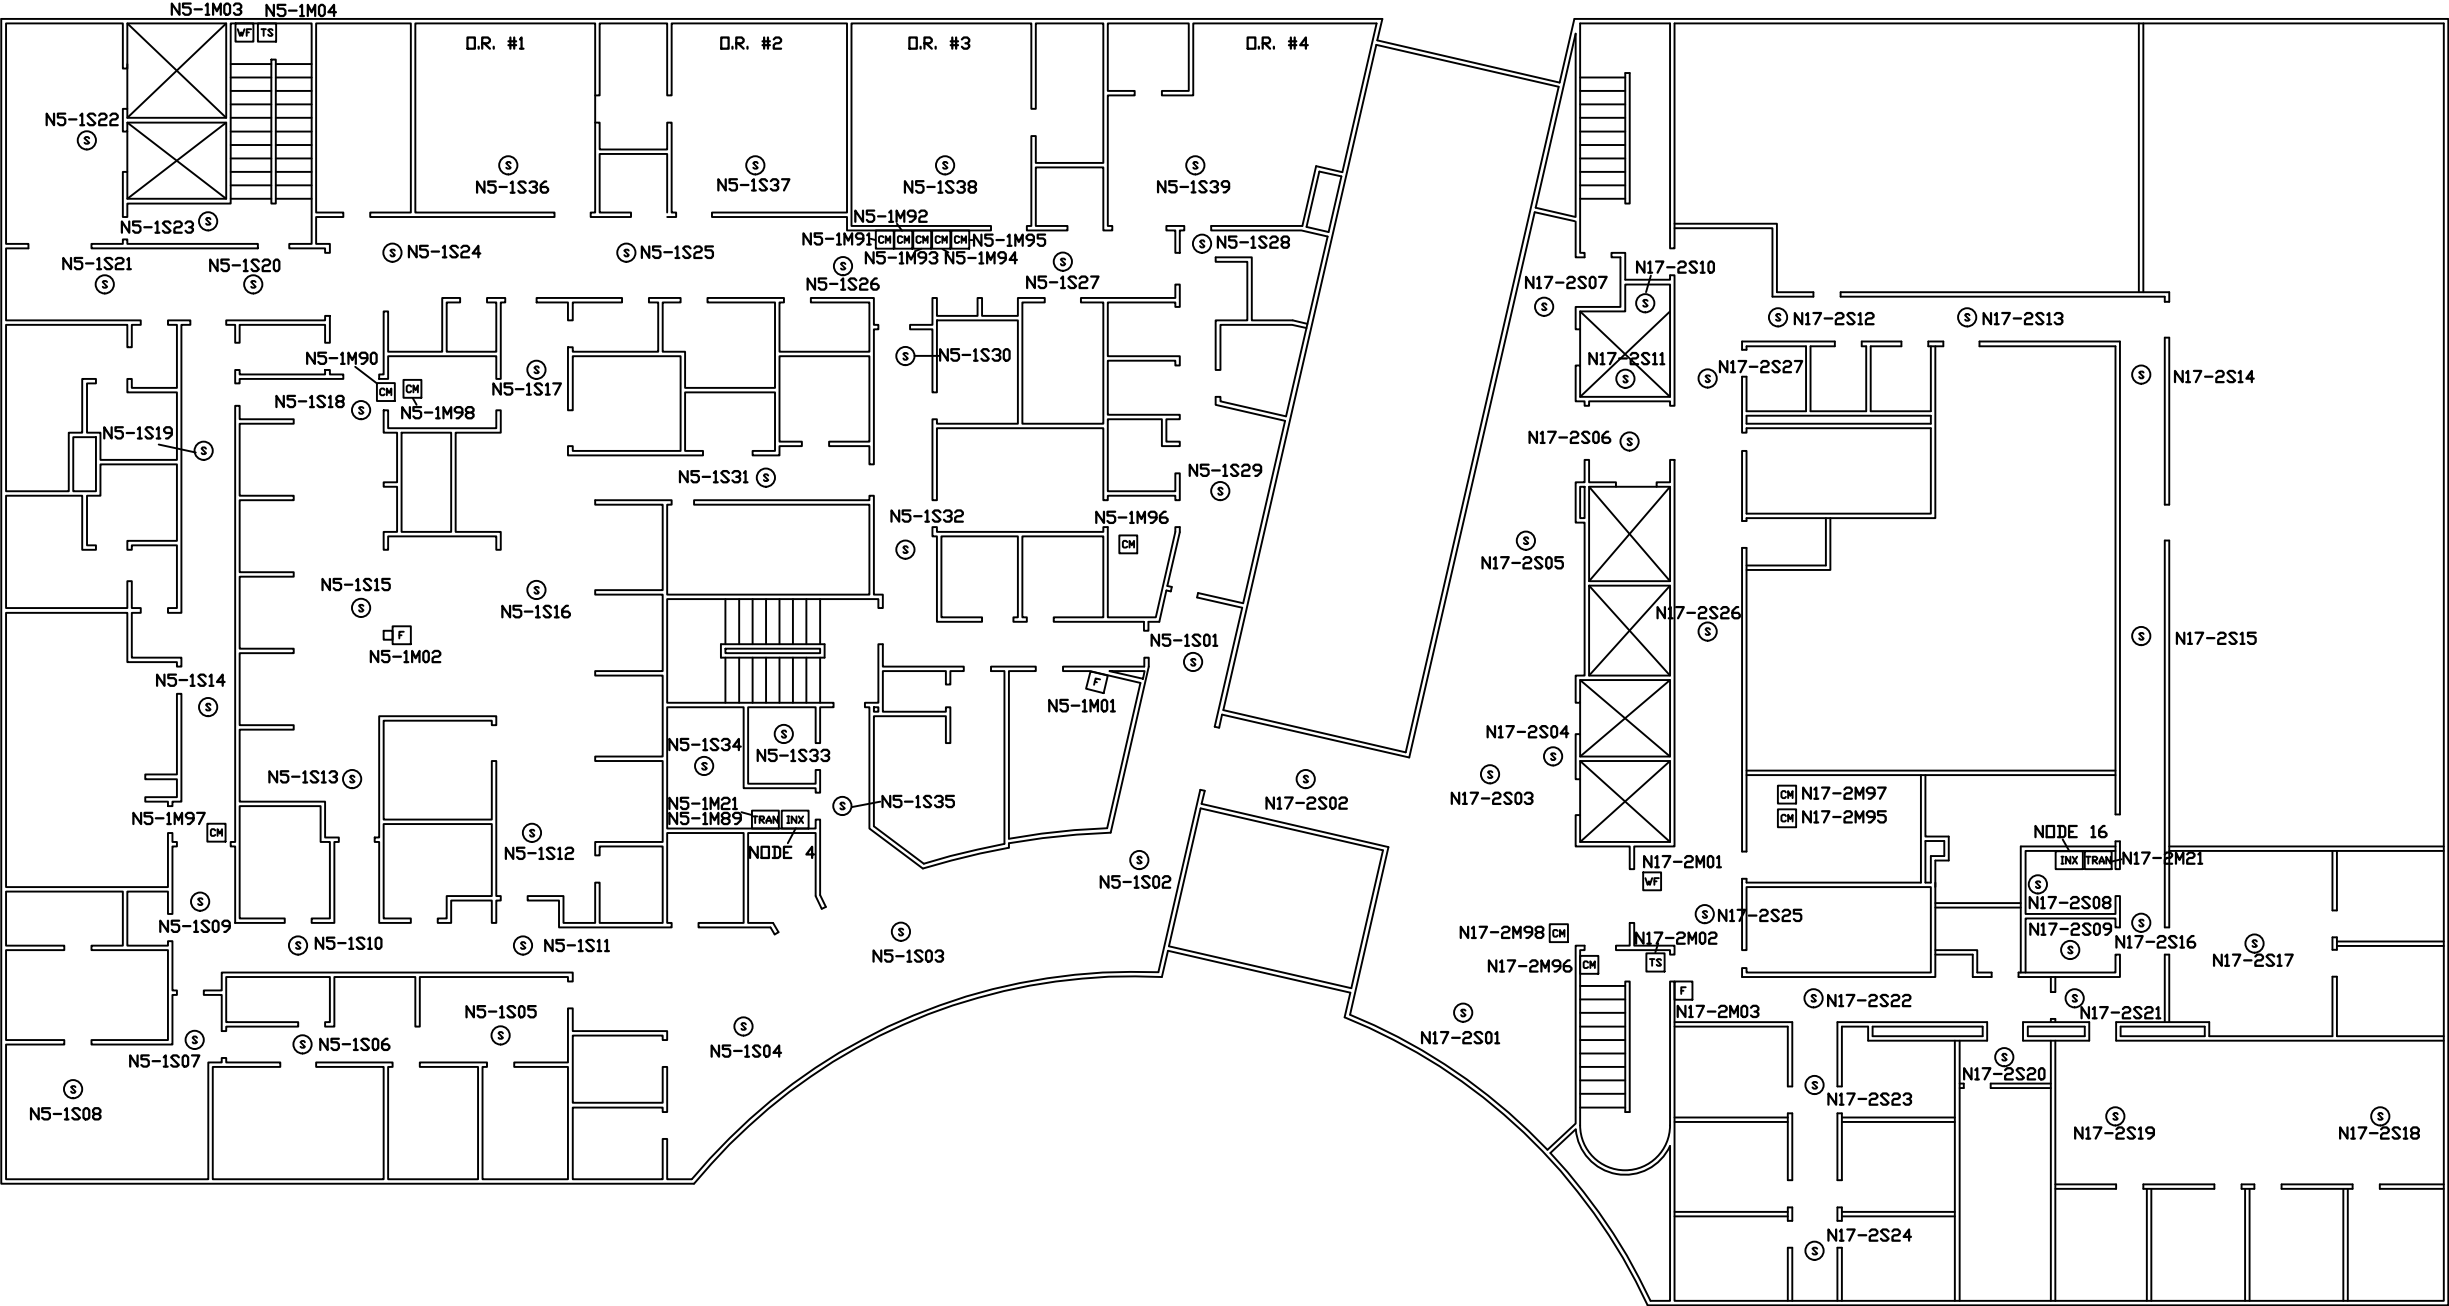

NOTE:
NFS DRAWINGS ARE BASED ON THE PROJECT
ARCHITECT/ENGINEER (A/E) PLANS AND SPECIFICATIONS
FURNISHED TO NFS. A/E IS SOLELY RESPONSIBLE
(NOT NFS) FOR THE TYPE, SIZE, LOCATION, AND
SUITABILITY OF ALL FIRE ALARMS, CONTROL PANELS,
AND OTHER DEVICES SHOWN ON THE A/E PLANS.
NFS DRAWINGS ARE TO SHOW ONLY THE WIRING
DIAGRAMS BETWEEN FIRE ALARM DEVICES AND
CONTROL PANELS. NFS IS NOT RESPONSIBLE FOR
THE INFORMATION SHOWN ON THE A/E PLANS.


MORAN EYE CENTER II
LEVEL 2
FIRE ALARM SYSTEM
UNIVERSITY OF UTAH
SALT LAKE CITY, UTAH

NFS
NELSON FIRE SYSTEMS
801-468-8300



DRAWN BY: DS
DATE: 11/11/2011
ADDENDUM #'S: 1,2,3,4
CHANGE ORDERS:
SCALE: N.T.S.
PROJECT NO: XXXX
REV NO: XXXX
DRAWING NAME:
MORAN II LEVEL 2.DWG

FIRE ALARM SYSTEM
LEVEL 2
ADDRESSABLE LOOP NUMBERS

PAGE:
NFS 2

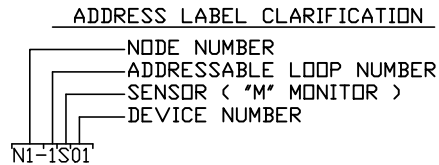

DEVICE LEGEND	
SYMBOL	DESCRIPTION
Ⓢ	SMOKE DETECTOR
①	THERMAL DETECTOR
F	MANUAL PULL STATION
BD	DUCT SMOKE DETECTOR
WF	WATERFLOW SWITCH MONITOR MODULE
TS	TAMPER SWITCH MONITOR MODULE
MM	MONITOR MODULE
CM	CONTROL MODULE
RA	REMOTE ANNUNCIATOR
FACP	FIRE ALARM CONTROL PANEL
TRAN	TRANSPONDER PANEL
FACP	FIRE ALARM CONTROL PANEL
TRK	VOICE PANEL
INCC	REMOTE COMMAND CENTER
VSD	ATRIUM VESDA PANEL

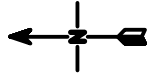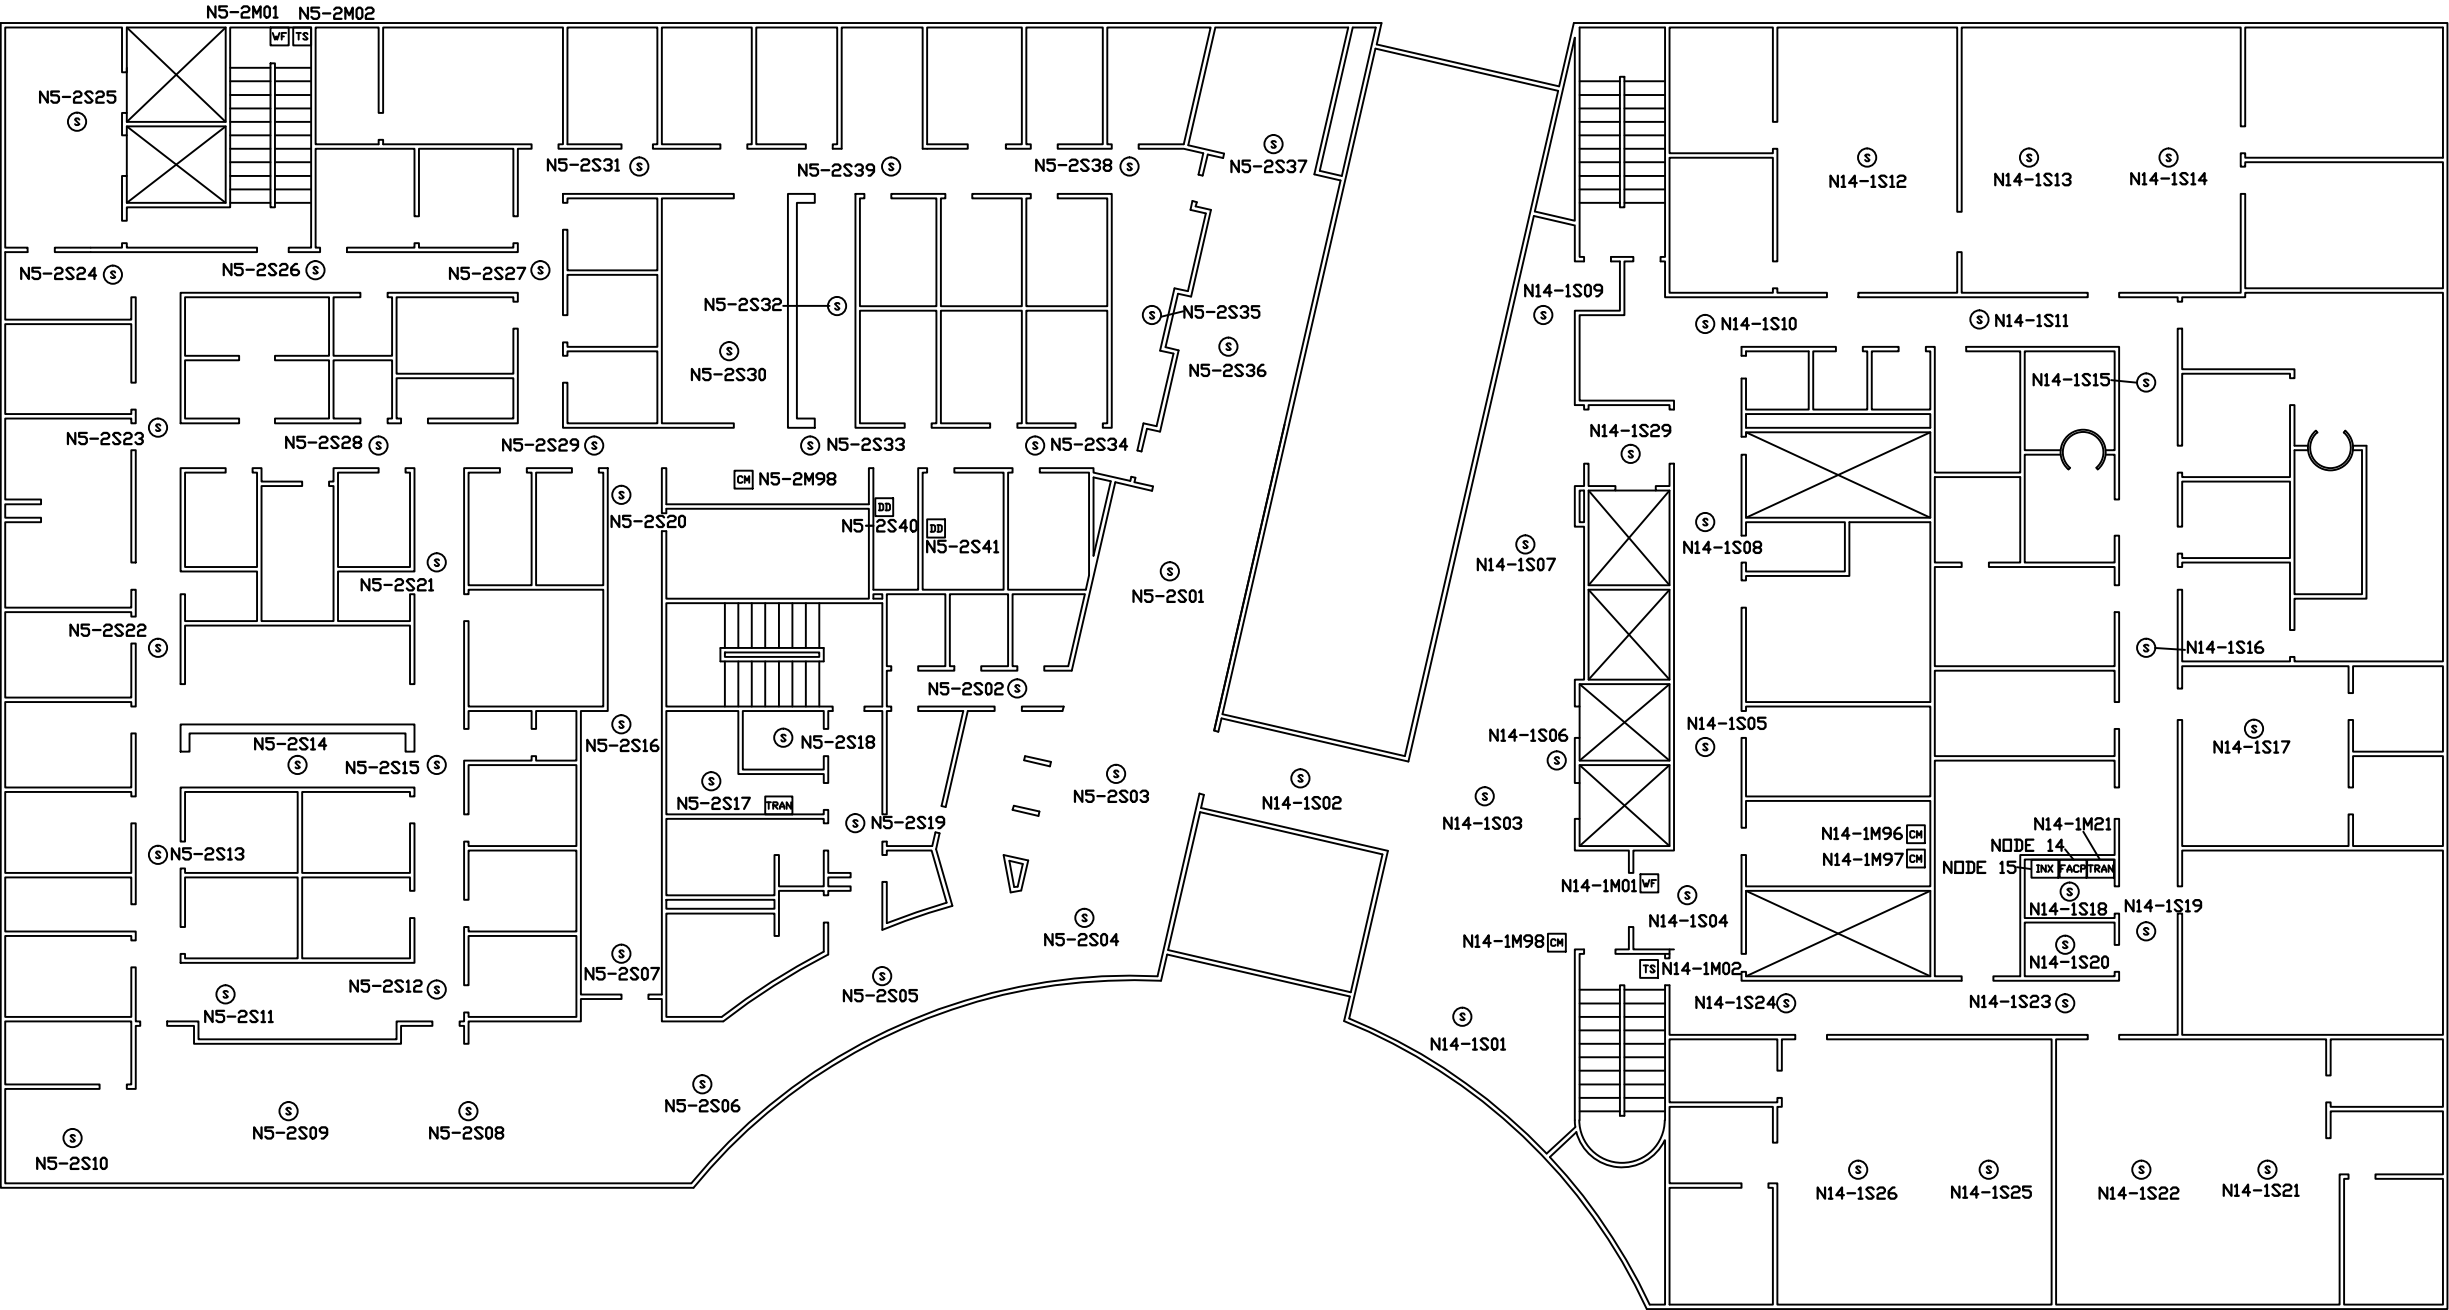

NOTE:
NFS DRAWINGS ARE BASED ON THE PROJECT
ARCHITECT/ENGINEER (A/E) PLANS AND SPECIFICATIONS
FURNISHED TO NFS. A/E IS SOLELY RESPONSIBLE
(NOT NFS) FOR THE TYPE, SIZE, LOCATION, AND
SUITABILITY OF ALL FIRE ALARMS, CONTROL PANELS,
AND OTHER DEVICES SHOWN ON THE A/E PLANS.
NFS DRAWINGS ARE TO SHOW ONLY THE WIRING
DIAGRAMS BETWEEN FIRE ALARM DEVICES AND
CONTROL PANELS. NFS IS NOT RESPONSIBLE FOR
THE INFORMATION SHOWN ON THE A/E PLANS.


MORAN EYE CENTER II
LEVEL 3
FIRE ALARM SYSTEM
UNIVERSITY OF UTAH
SALT LAKE CITY, UTAH

NFS
NELSON FIRE SYSTEMS
801-468-8300


DRAWN BY: DS
DESIGNED BY: XXXX
APPROVED BY: XXXX
DATE: 5/8/2006
SCALE: N.T.S.
PROJECT NO: XXXX
REV NO: XXXX
DRAWING NAME:
MORAN II LEVEL 3.DWG



FIRE ALARM SYSTEM
LEVEL 3
ADDRESSABLE LOOP NUMBERS

PAGE:
NFS 3

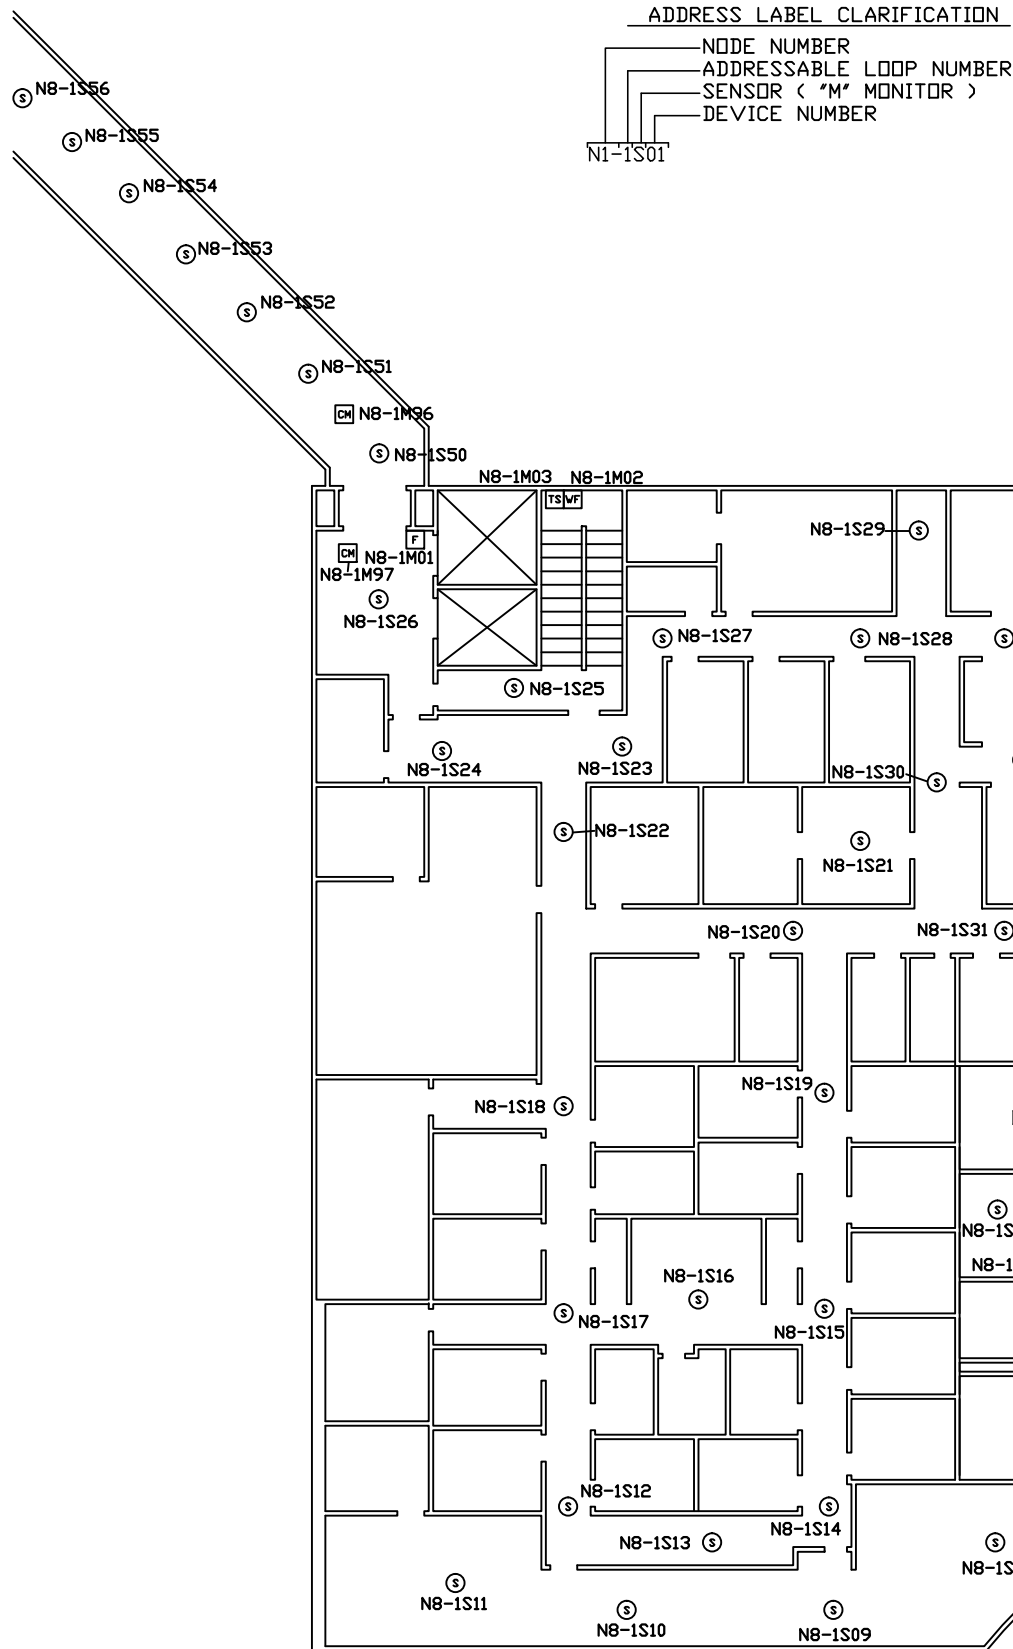


DEVICE LEGEND	
SYMBOL	DESCRIPTION
Ⓢ	SMOKE DETECTOR
Ⓣ	THERMAL DETECTOR
F	MANUAL PULL STATION
DB	DUCT SMOKE DETECTOR
WF	WATERFLOW SWITCH MONITOR MODULE
TS	TAMPER SWITCH MONITOR MODULE
MM	MONITOR MODULE
CM	CONTROL MODULE
RA	REMOTE ANNUNCIATOR
FACP	FIRE ALARM CONTROL PANEL
TRAN	TRANSPONDER PANEL
FACP	FIRE ALARM CONTROL PANEL
INX	VOICE PANEL
DNCC	REMOTE COMMAND CENTER
VSD	ATRIUM VESDA PANEL

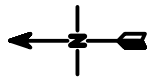

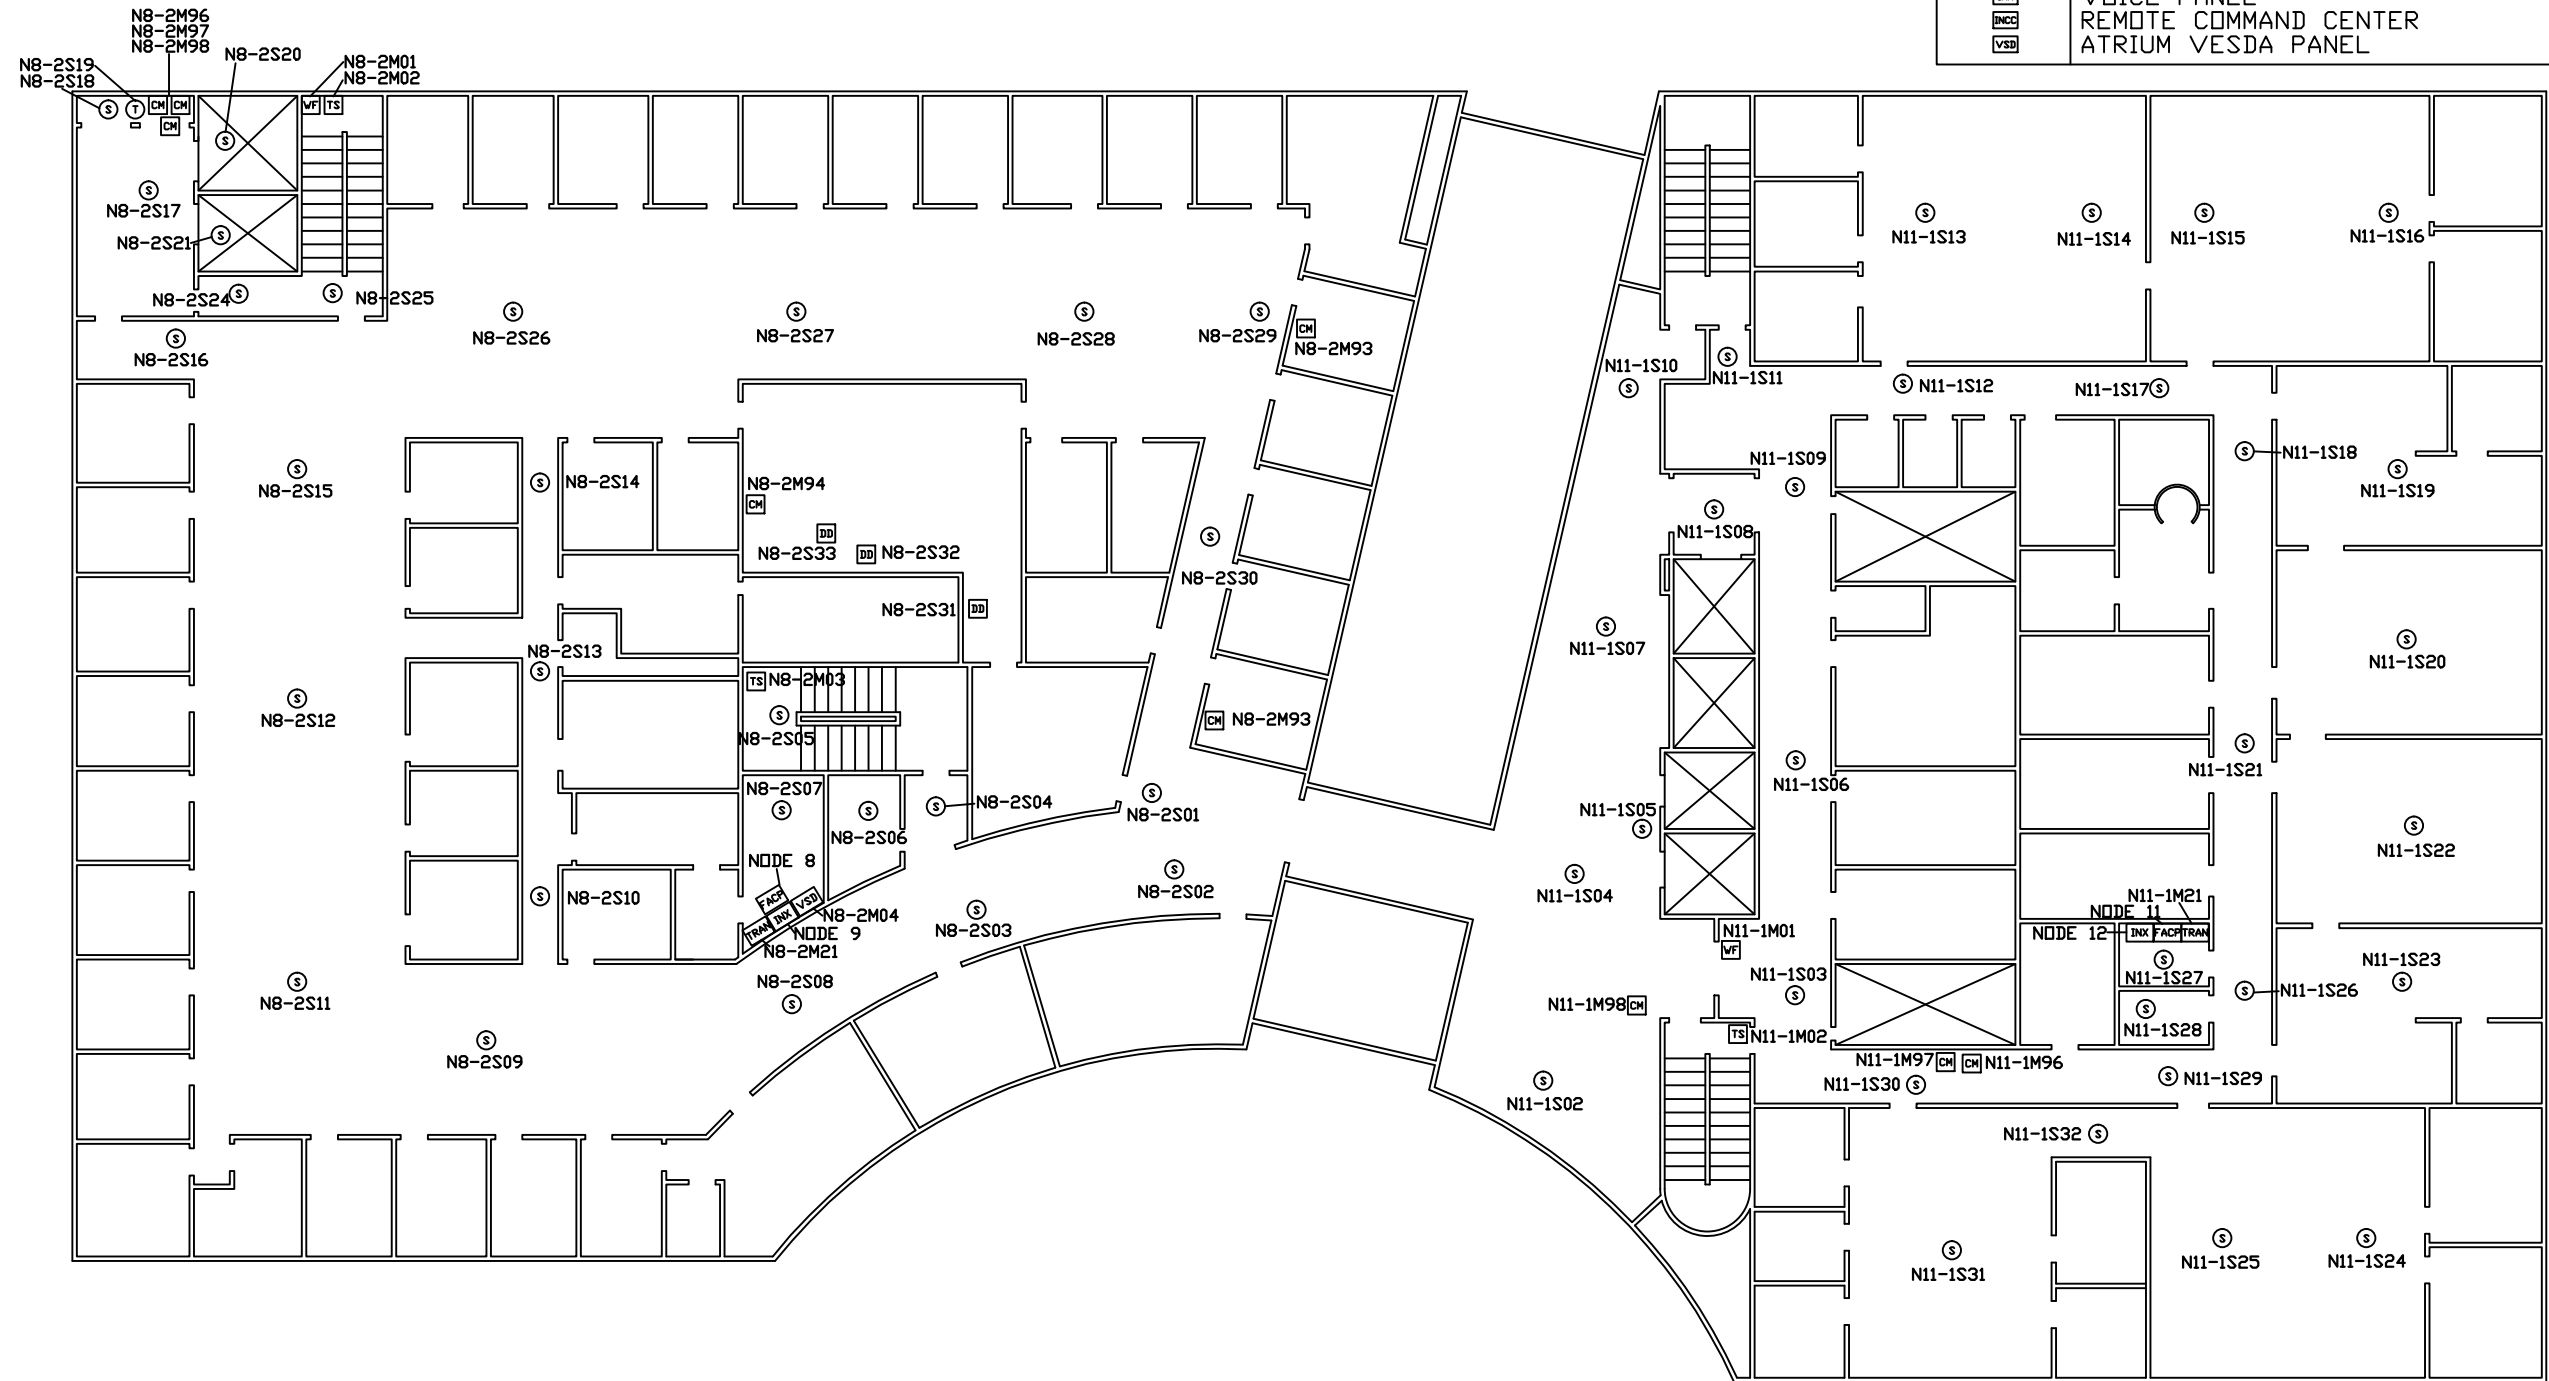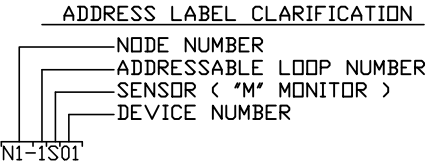

DEVICE LEGEND	
SYMBOL	DESCRIPTION
Ⓢ	SMOKE DETECTOR
Ⓢ	THERMAL DETECTOR
Ⓢ	MANUAL PULL STATION
Ⓢ	DUCT SMOKE DETECTOR
Ⓢ	WATERFLOW SWITCH MONITOR MODULE
Ⓢ	TAMPER SWITCH MONITOR MODULE
Ⓢ	MONITOR MODULE
Ⓢ	CONTROL MODULE
Ⓢ	REMOTE ANNUNCIATOR
Ⓢ	FIRE ALARM CONTROL PANEL
Ⓢ	TRANSPONDER PANEL
Ⓢ	FIRE ALARM CONTROL PANEL
Ⓢ	VOICE PANEL
Ⓢ	REMOTE COMMAND CENTER
Ⓢ	ATRIUM VESDA PANEL

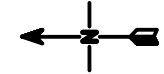

NOTE:
NFS DRAWINGS ARE BASED ON THE PROJECT
ARCHITECT/ENGINEER (A/E) PLANS AND SPECIFICATIONS
FURNISHED TO NFS. A/E IS SOLELY RESPONSIBLE
(NOT NFS) FOR THE TYPE, SIZE, LOCATION, AND
SUITABILITY OF ALL FIRE ALARMS, CONTROL PANELS,
AND OTHER DEVICES SHOWN ON THE A/E PLANS.
NFS DRAWINGS ARE TO SHOW ONLY THE WIRING
DIAGRAMS BETWEEN FIRE ALARM DEVICES AND
CONTROL PANELS. NFS IS NOT RESPONSIBLE FOR
THE INFORMATION SHOWN ON THE A/E PLANS.

MORAN EYE CENTER II
LEVEL 5
FIRE ALARM SYSTEM
UNIVERSITY OF UTAH
SALT LAKE CITY, UTAH




NFS
NELSON FIRE SYSTEMS
801-468-8300

DRAWN BY: DS
DESIGNED BY: XXXX
APPROVED BY: TCT
DATE: 5/8/2006
SCALE: N.T.S.
PROJECT NO: XXXX
REV NO: XXXX
DRAWING NAME:
MORAN II LEVEL 5.DWG

FIRE ALARM SYSTEM
LEVEL 5
ADDRESSABLE LOOP NUMBERS

PAGE:
NFS 5

DEVICE LEGEND	
SYMBOL	DESCRIPTION
Ⓢ	SMOKE DETECTOR
Ⓣ	THERMAL DETECTOR
F	MANUAL PULL STATION
DD	DUCT SMOKE DETECTOR
WF	WATERFLOW SWITCH MONITOR MODULE
TS	TAMPER SWITCH MONITOR MODULE
MM	MONITOR MODULE
CM	CONTROL MODULE
RA	REMOTE ANNUNCIATOR
FACP	FIRE ALARM CONTROL PANEL
TRAN	TRANSPONDER PANEL
FACP	FIRE ALARM CONTROL PANEL
INX	VOICE PANEL
INCC	REMOTE COMMAND CENTER
VSD	ATRIUM VESDA PANEL

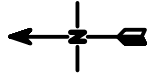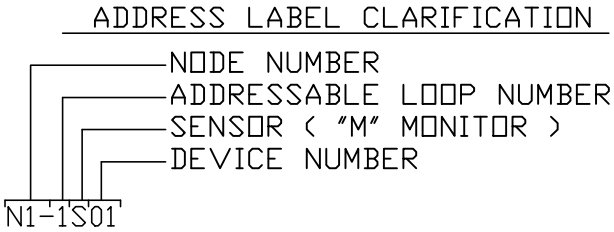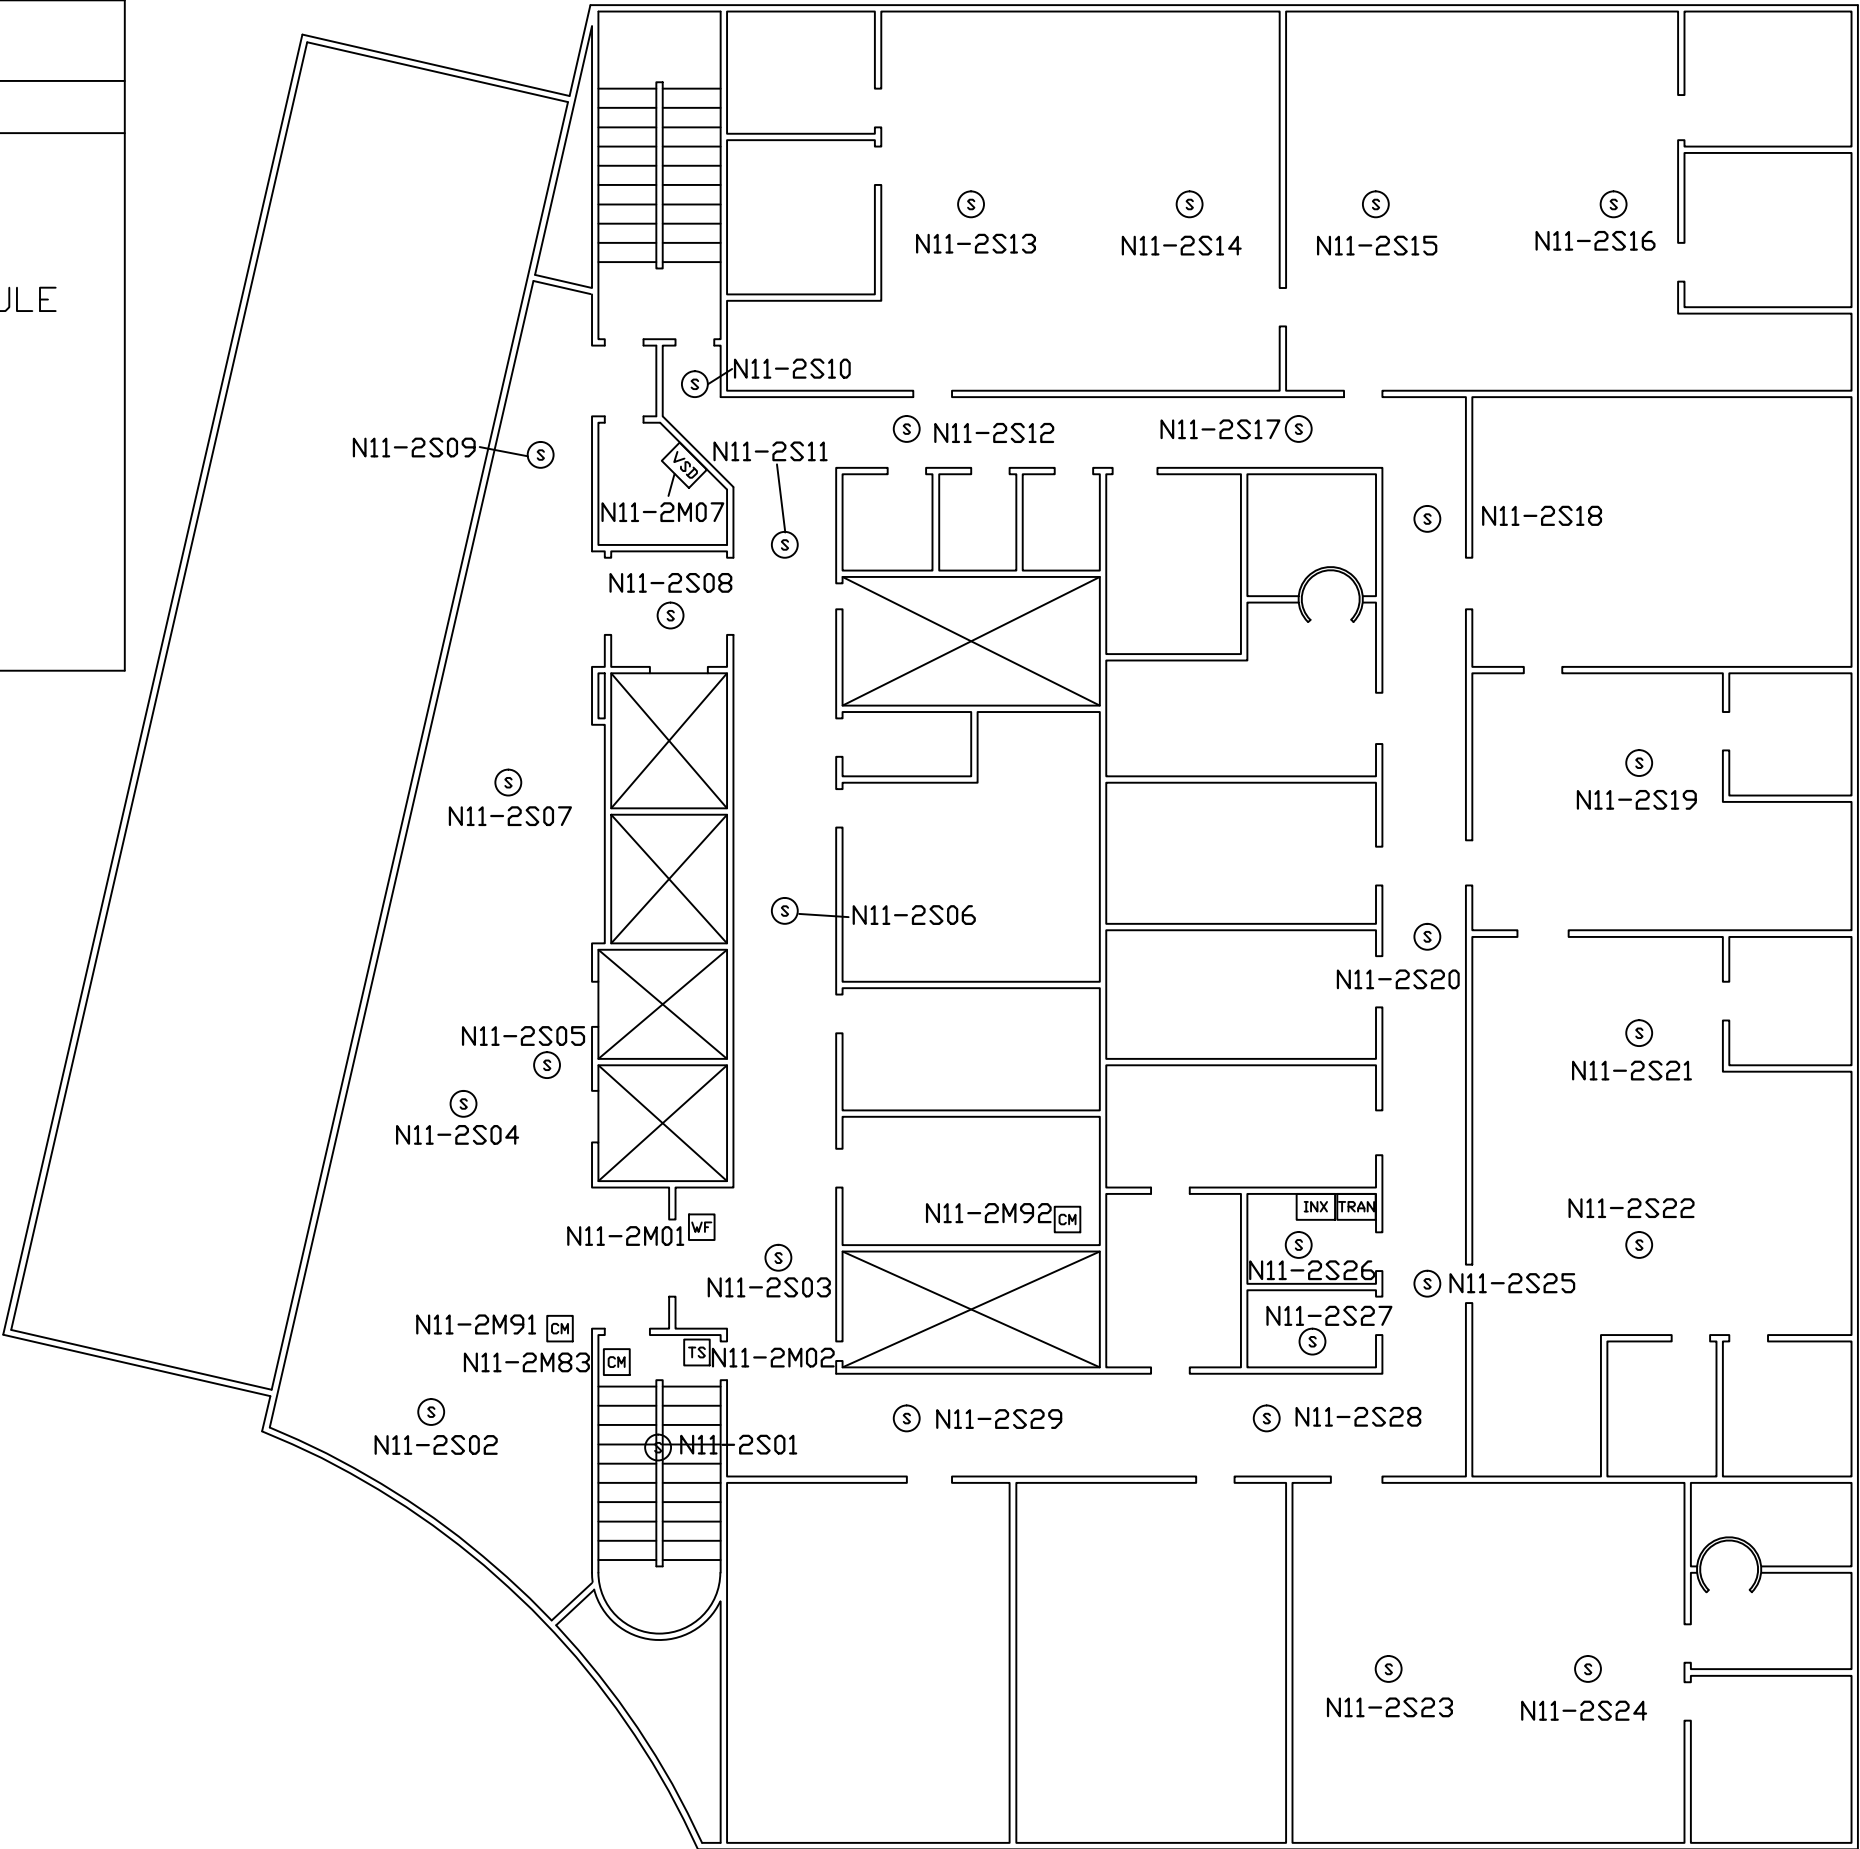

NOTE:
NFS DRAWINGS ARE BASED ON THE PROJECT
ARCHITECT/ENGINEER (A/E) PLANS AND SPECIFICATIONS
FURNISHED TO NFS. A/E IS SOLELY RESPONSIBLE
(NOT NFS) FOR THE TYPE, SIZE, LOCATION, AND
SUITABILITY OF ALL FIRE ALARMS, CONTROL PANELS,
AND OTHER DEVICES SHOWN ON THE A/E PLANS.
NFS DRAWINGS ARE TO SHOW ONLY THE WIRING
DIAGRAMS BETWEEN FIRE ALARM DEVICES AND
CONTROL PANELS. NFS IS NOT RESPONSIBLE FOR
THE INFORMATION SHOWN ON THE A/E PLANS.


MORAN EYE CENTER II
LEVEL 6
FIRE ALARM SYSTEM
UNIVERSITY OF UTAH
SALT LAKE CITY, UTAH

NFS
NELSON FIRE SYSTEMS
801-468-8300

DRAWN BY:	DS
DESIGNED BY:	XXXX
APPROVED BY:	TCT
DATE:	5/8/2006
SCALE:	N.T.S.
PROJECT NO:	XXXX
REV NO:	XXXX
DRAWING NAME:	MORAN II LEVEL 6.DWG


FIRE ALARM SYSTEM
LEVEL 6
ADDRESSABLE LOOP NUMBERS

ADDRESS LABEL CLARIFICATION

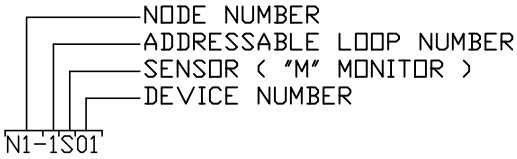

DEVICE LEGEND

SYMBOL	DESCRIPTION
Ⓢ	SMOKE DETECTOR
Ⓣ	THERMAL DETECTOR
F	MANUAL PULL STATION
DB	DUCT SMOKE DETECTOR
WF	WATERFLOW SWITCH MONITOR MODULE
TS	TAMPER SWITCH MONITOR MODULE
LA	LOW AIR SWITCH
PS	PRESSURE SWITCH
MM	MONITOR MODULE
CM	CONTROL MODULE
RA	REMOTE ANNUNCIATOR
FACP	FIRE ALARM CONTROL PANEL
TRAN	TRANSPONDER PANEL
FACP	FIRE ALARM CONTROL PANEL
INX	VOICE PANEL
INCC	REMOTE COMMAND CENTER
VSD	ATRIUM VESDA PANEL

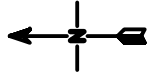

NOTE:
NFS DRAWINGS ARE BASED ON THE PROJECT ARCHITECT/ENGINEER (A/E) PLANS AND SPECIFICATIONS FURNISHED TO NFS. A/E IS SOLELY RESPONSIBLE (NOT NFS) FOR THE TYPE, SIZE, LOCATION, AND SUITABILITY OF ALL FIRE ALARMS, CONTROL PANELS, AND OTHER DEVICES SHOWN ON THE A/E PLANS. NFS DRAWINGS ARE TO SHOW ONLY THE WIRING DIAGRAMS BETWEEN FIRE ALARM DEVICES AND CONTROL PANELS. NFS IS NOT RESPONSIBLE FOR THE INFORMATION SHOWN ON THE A/E PLANS.



JOHN MORAN EYE CENTER II
LEVELS A AND B FIRE ALARM SYSTEM
UNIVERSITY OF UTAH
SALT LAKE CITY, UTAH

NFS
NELSON FIRE SYSTEMS
801-468-8300

DRAWN BY: DS
DATE: 7/26/2006
ADDENDUM #'S: 1,2,3,4
CHANGE ORDERS: 7/26/2006
SCALE: N.T.S.
PROJECT NO: XXXX
REV NO: XXXX
DRAWING NAME: JOHN MORAN LEVEL A.DWG

FIRE ALARM SYSTEM
LEVELS A AND B
ADDRESSABLE NUMBERS

PAGE:
NFS- A AND B

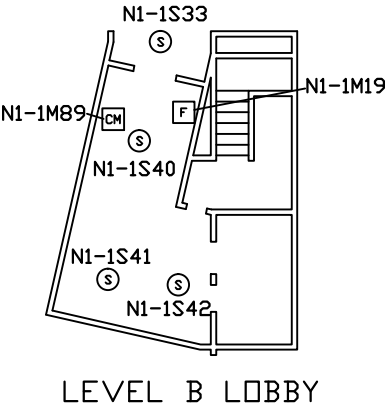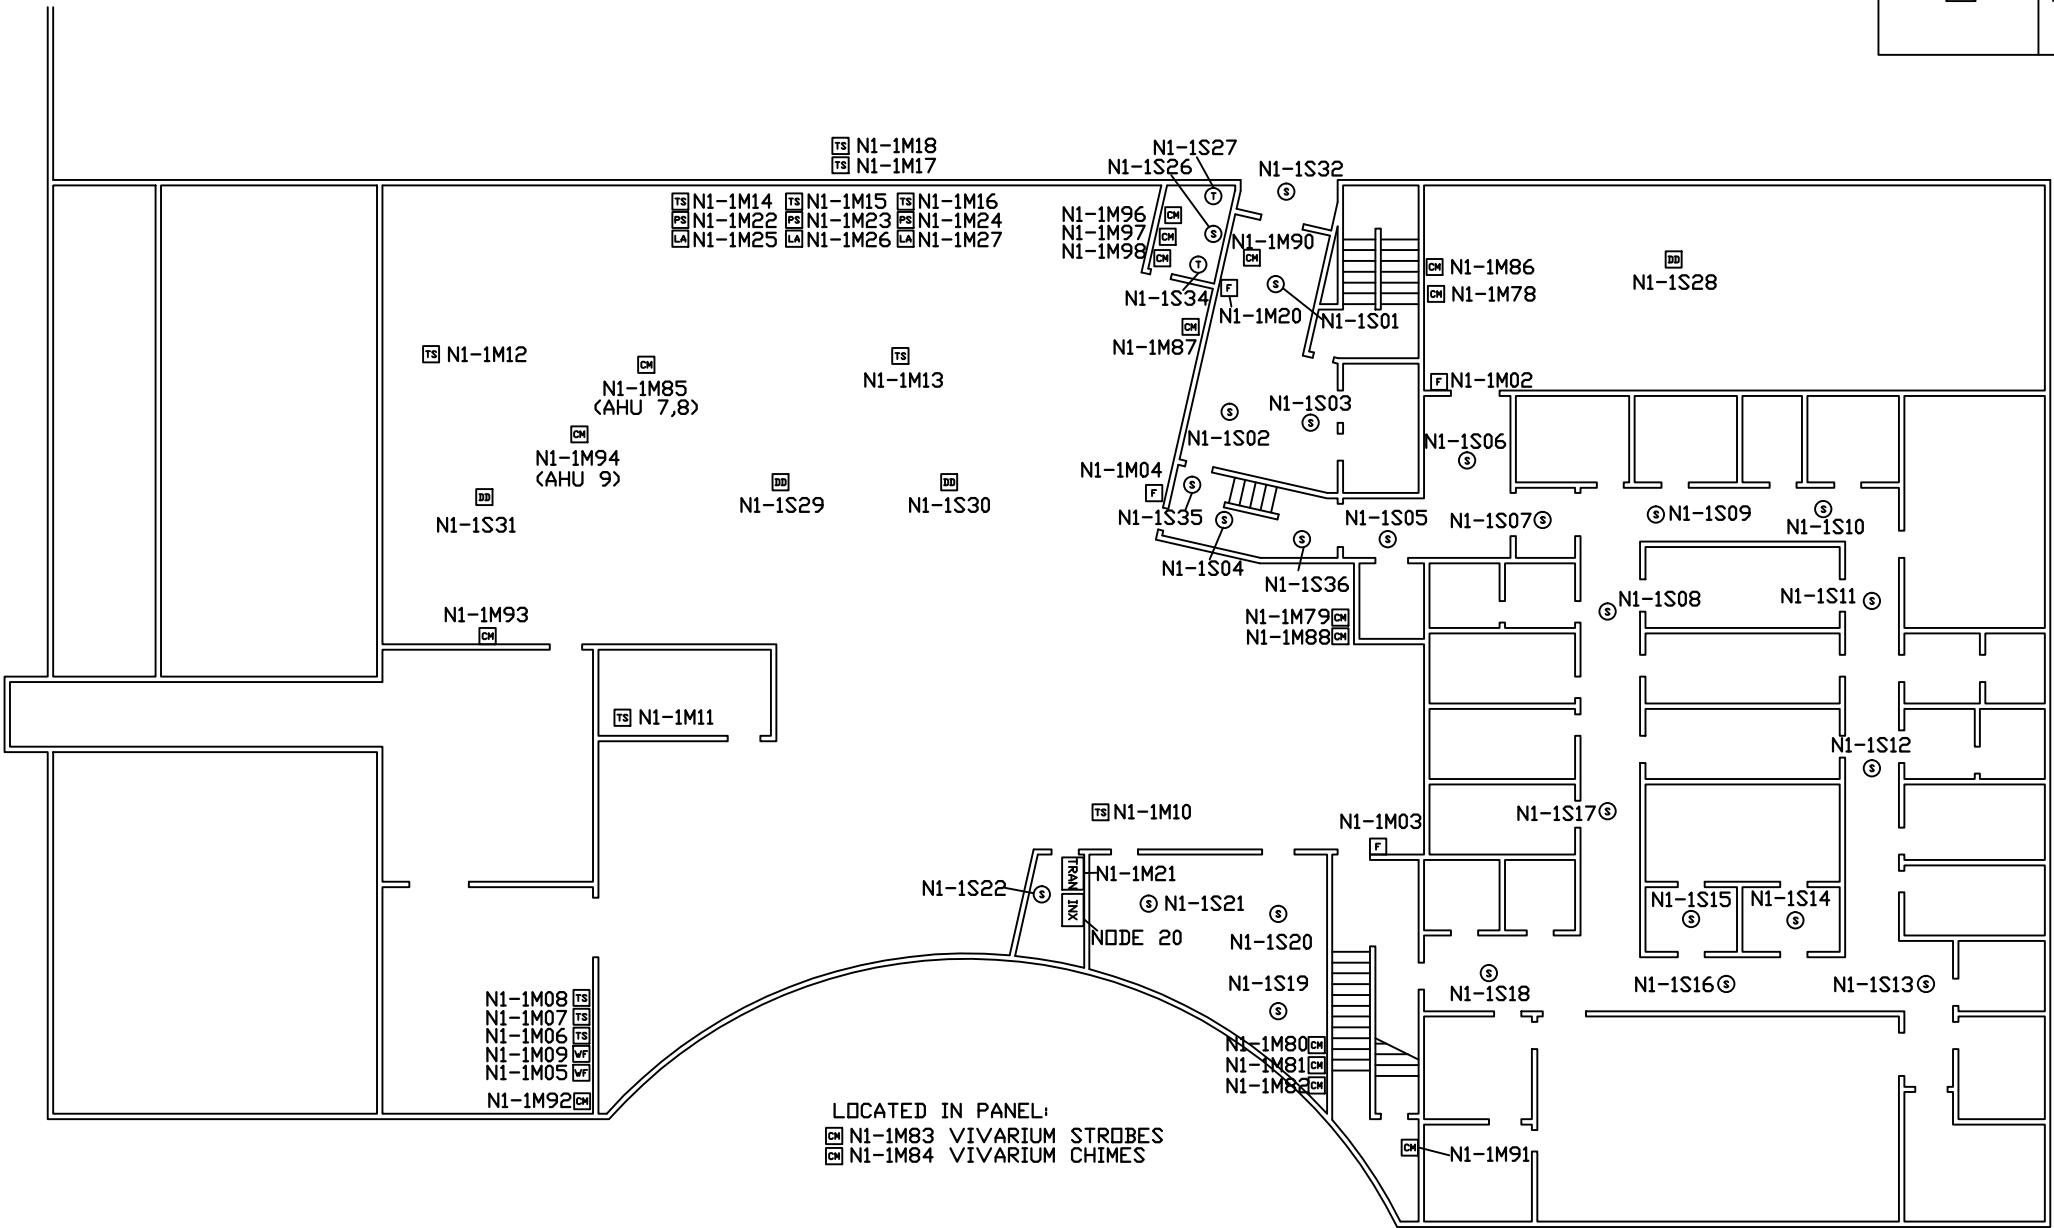


* ALL SPEAKER & STROBE CIRCUITS FROM
PARKING GARAGE SHALL BE WIRED TO LEVEL A
TRANSPONDER LOCATION

* FIELD LOCATE LEVEL A FIRE ALARM
TRANSPONDER & POWER SUPPLIES
SEE RISER DIAGRAM FOR LAYOUT

- SYSTEM NOTES:
- ① TO LEVEL A TRANSPONDER
 - ② TO LEVEL 1 TRANSPONDER
 - ③ TO 120VAC WITH GROUND

WIRE SCHEDULE		
SYMBOL	DESCRIPTION	SIZE
A	ADDRESSABLE LOOP #1	2#14'S TWISTED
B	FIREFLY 24VDC AUX POWER	2#14'S
C	STROBE CIRCUIT #1	2#14'S
D	SPEAKER CIRCUIT #1	2#14'S TWISTED
E	FIREFLY RELAY CIRCUIT	2#14'S
F		
G		
H		
J	120 VAC W/GROUND	3#12'S
K	ELEVATOR CONTROL CIRCUIT	2#14'S
L	FAN SHUTDOWN	2#14'S
M	REMOTE ANNUNCIATOR	2 PAIRS #14'S TWISTED & 4#14'S
N	TRANSPONDER INTERCONNECT	2 PAIRS #14 TWISTED FIRE RATED CABLE

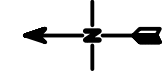

NOTE:
NFS DRAWINGS ARE BASED ON THE PROJECT
ARCHITECT/ENGINEER (A/E) PLANS AND SPECIFICATIONS
FURNISHED TO NFS. A/E IS SOLELY RESPONSIBLE
(NOT NFS) FOR THE TYPE, SIZE, LOCATION, AND
SUITABILITY OF ALL FIRE ALARMS, CONTROL PANELS,
AND OTHER DEVICES SHOWN ON THE A/E PLANS.
NFS DRAWINGS ARE TO SHOW ONLY THE WIRING
DIAGRAMS BETWEEN FIRE ALARM DEVICES AND
CONTROL PANELS. NFS IS NOT RESPONSIBLE FOR
THE INFORMATION SHOWN ON THE A/E PLANS.

JOHN MORAN EYE CENTER II
LEVEL B FIRE ALARM SYSTEM
UNIVERSITY OF UTAH
SALT LAKE CITY, UTAH




NFS
NELSON FIRE SYSTEMS
801-468-8300



DRAWN BY:	DB
DESIGNED BY:	XXXX
APPROVED BY:	XXXX
DATE:	6/1/2005
SCALE:	N.T.S.
PROJECT NO:	XXXX
REV NO:	XXXX
DRAWING NAME:	JOHN MORAN LEVEL B.DWG

FIRE ALARM SYSTEM
LEVEL B
ADDRESSABLE LOOP NUMBERS


PAGE:
FA-B-04

ADDRESS LABEL CLARIFICATION

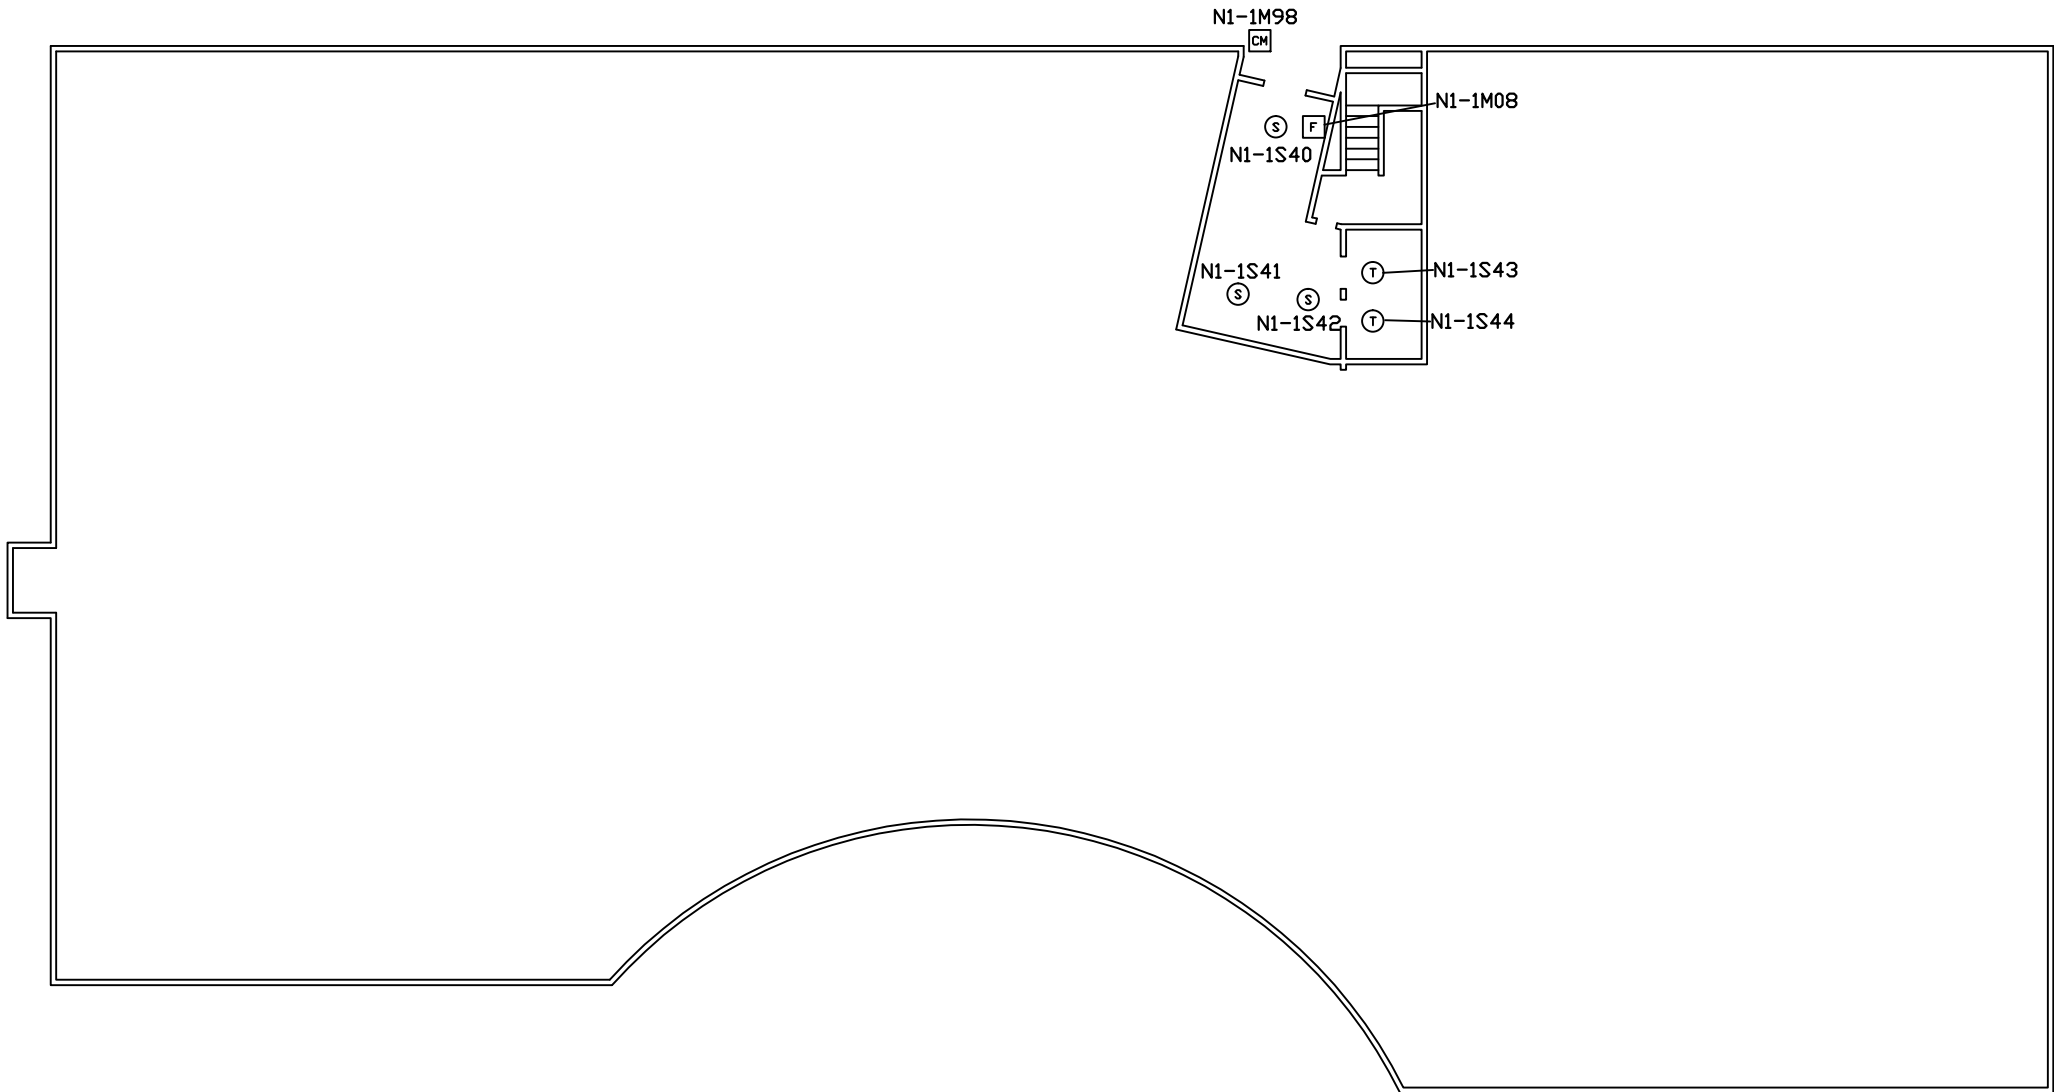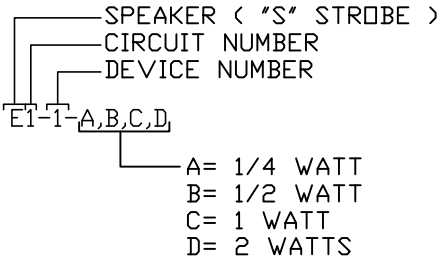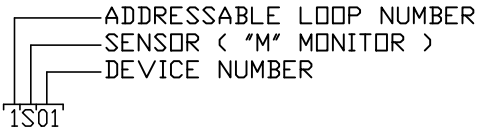

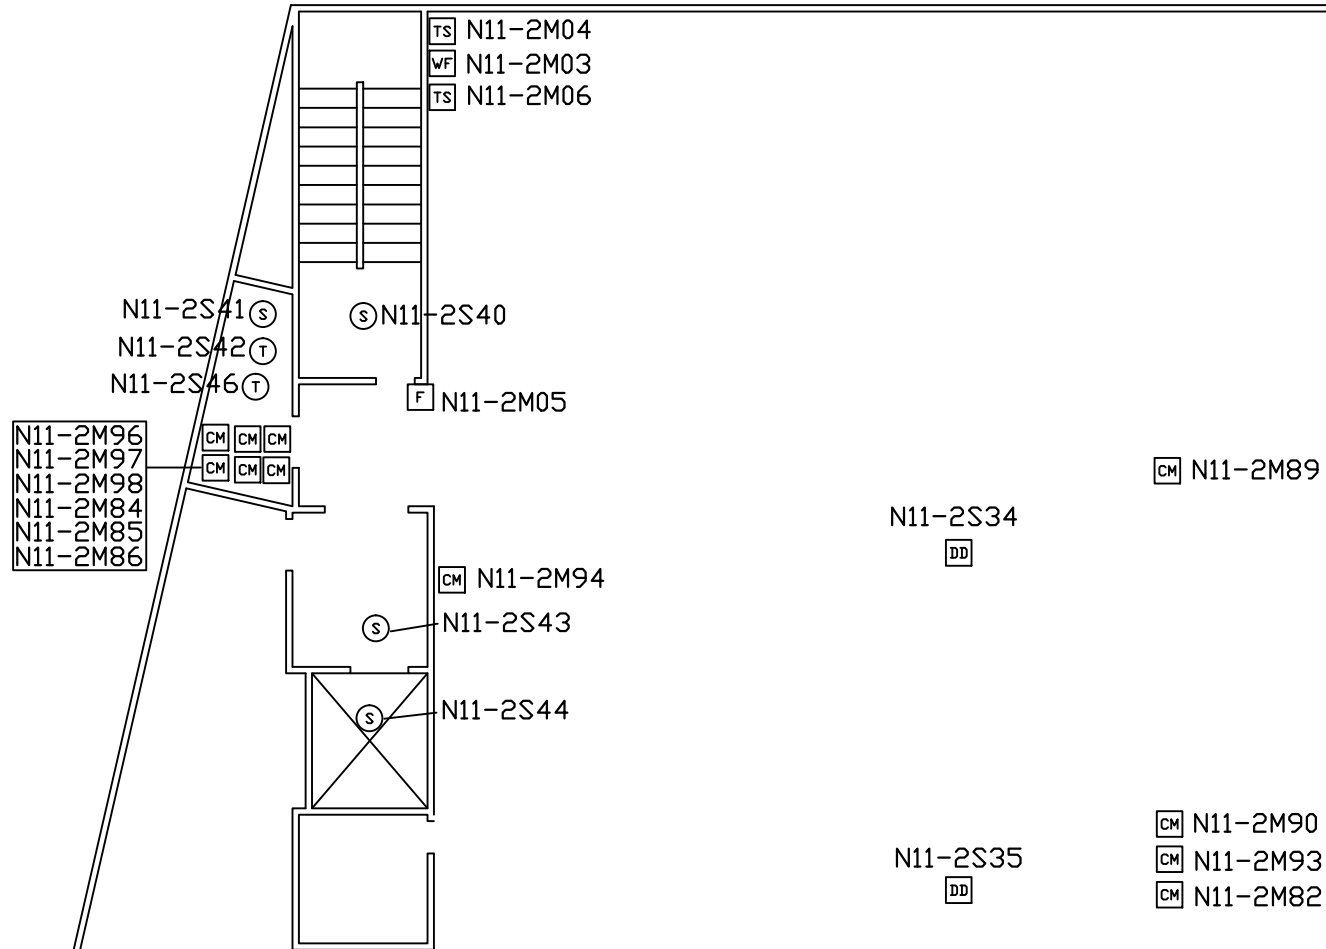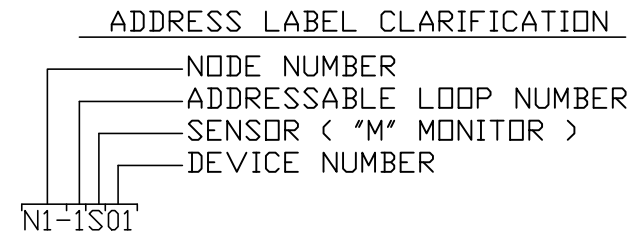

DEVICE LEGEND	
SYMBOL	DESCRIPTION
Ⓢ	SMOKE DETECTOR
Ⓣ	THERMAL DETECTOR
F	MANUAL PULL STATION
DD	DUCT SMOKE DETECTOR
WF	WATERFLOW SWITCH MONITOR MODULE
TS	TAMPER SWITCH MONITOR MODULE
MM	MONITOR MODULE
CM	CONTROL MODULE
RA	REMOTE ANNUNCIATOR
FACP	FIRE ALARM CONTROL PANEL
TRAN	TRANSPONDER PANEL
FACP	FIRE ALARM CONTROL PANEL
INX	VOICE PANEL
INCC	REMOTE COMMAND CENTER
VSD	ATRIUM VESDA PANEL

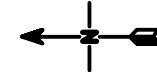

NOTE:
NFS DRAWINGS ARE BASED ON THE PROJECT ARCHITECT/ENGINEER (A/E) PLANS AND SPECIFICATIONS FURNISHED TO NFS. A/E IS SOLELY RESPONSIBLE (NOT NFS) FOR THE TYPE, SIZE, LOCATION, AND SUITABILITY OF ALL FIRE ALARMS, CONTROL PANELS, AND OTHER DEVICES SHOWN ON THE A/E PLANS. NFS DRAWINGS ARE TO SHOW ONLY THE WIRING DIAGRAMS BETWEEN FIRE ALARM DEVICES AND CONTROL PANELS. NFS IS NOT RESPONSIBLE FOR THE INFORMATION SHOWN ON THE A/E PLANS.

MORAN EYE CENTER II
PENTHOUSE/MECHANICAL LEVEL
FIRE ALARM SYSTEM
UNIVERSITY OF UTAH
SALT LAKE CITY, UTAH

NFS
NELSON FIRE SYSTEMS
801-468-8300

DRAWN BY: DS
DESIGNED BY: XXXX
APPROVED BY: TCT
DATE: 5/8/2006
SCALE: N.T.S.
PROJECT NO: XXXX
REV NO: XXXX
DRAWING NAME:
MORAN II PENTHOUSE LEVEL.DWG

FIRE ALARM SYSTEM
PENTHOUSE
ADDRESSABLE LOOP NUMBERS

PAGE:
NFS 7