



LEGEND

- Ⓢ SMOKE DETECTOR
- Ⓛ HEAT DETECTOR
- MANUAL PULL STATION
- DD DUCT DETECTOR
- WF WATER FLOW SWITCH
- TS TAMPER SWITCH
- J FIREMANS PHONE JACK

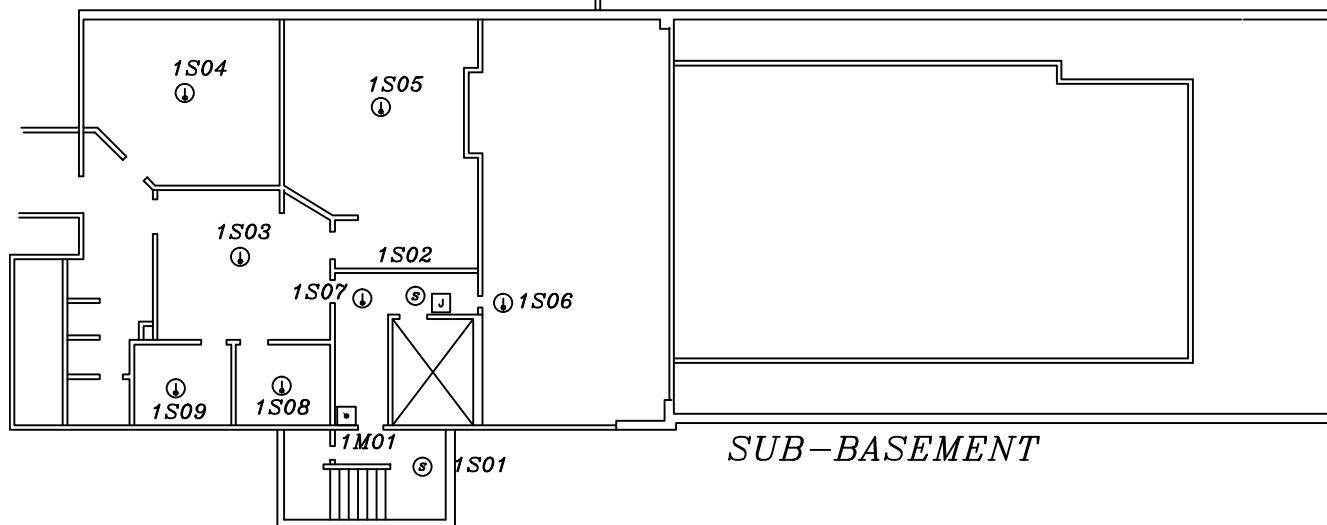


WINTROBE/MREB BUILDING
UNIVERSITY OF UTAH
SALT LAKE CITY, UTAH
JANUARY 7, 1997
UOUWINB.DWG

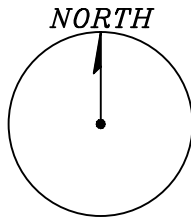

LEGEND

- Ⓢ SMOKE DETECTOR
- Ⓛ HEAT DETECTOR
- ⬢ MANUAL PULL STATION
- Ⓛ DUCT DETECTOR
- WF WATER FLOW SWITCH
- TS TAMPER SWITCH
- J FIREMANS PHONE JACK

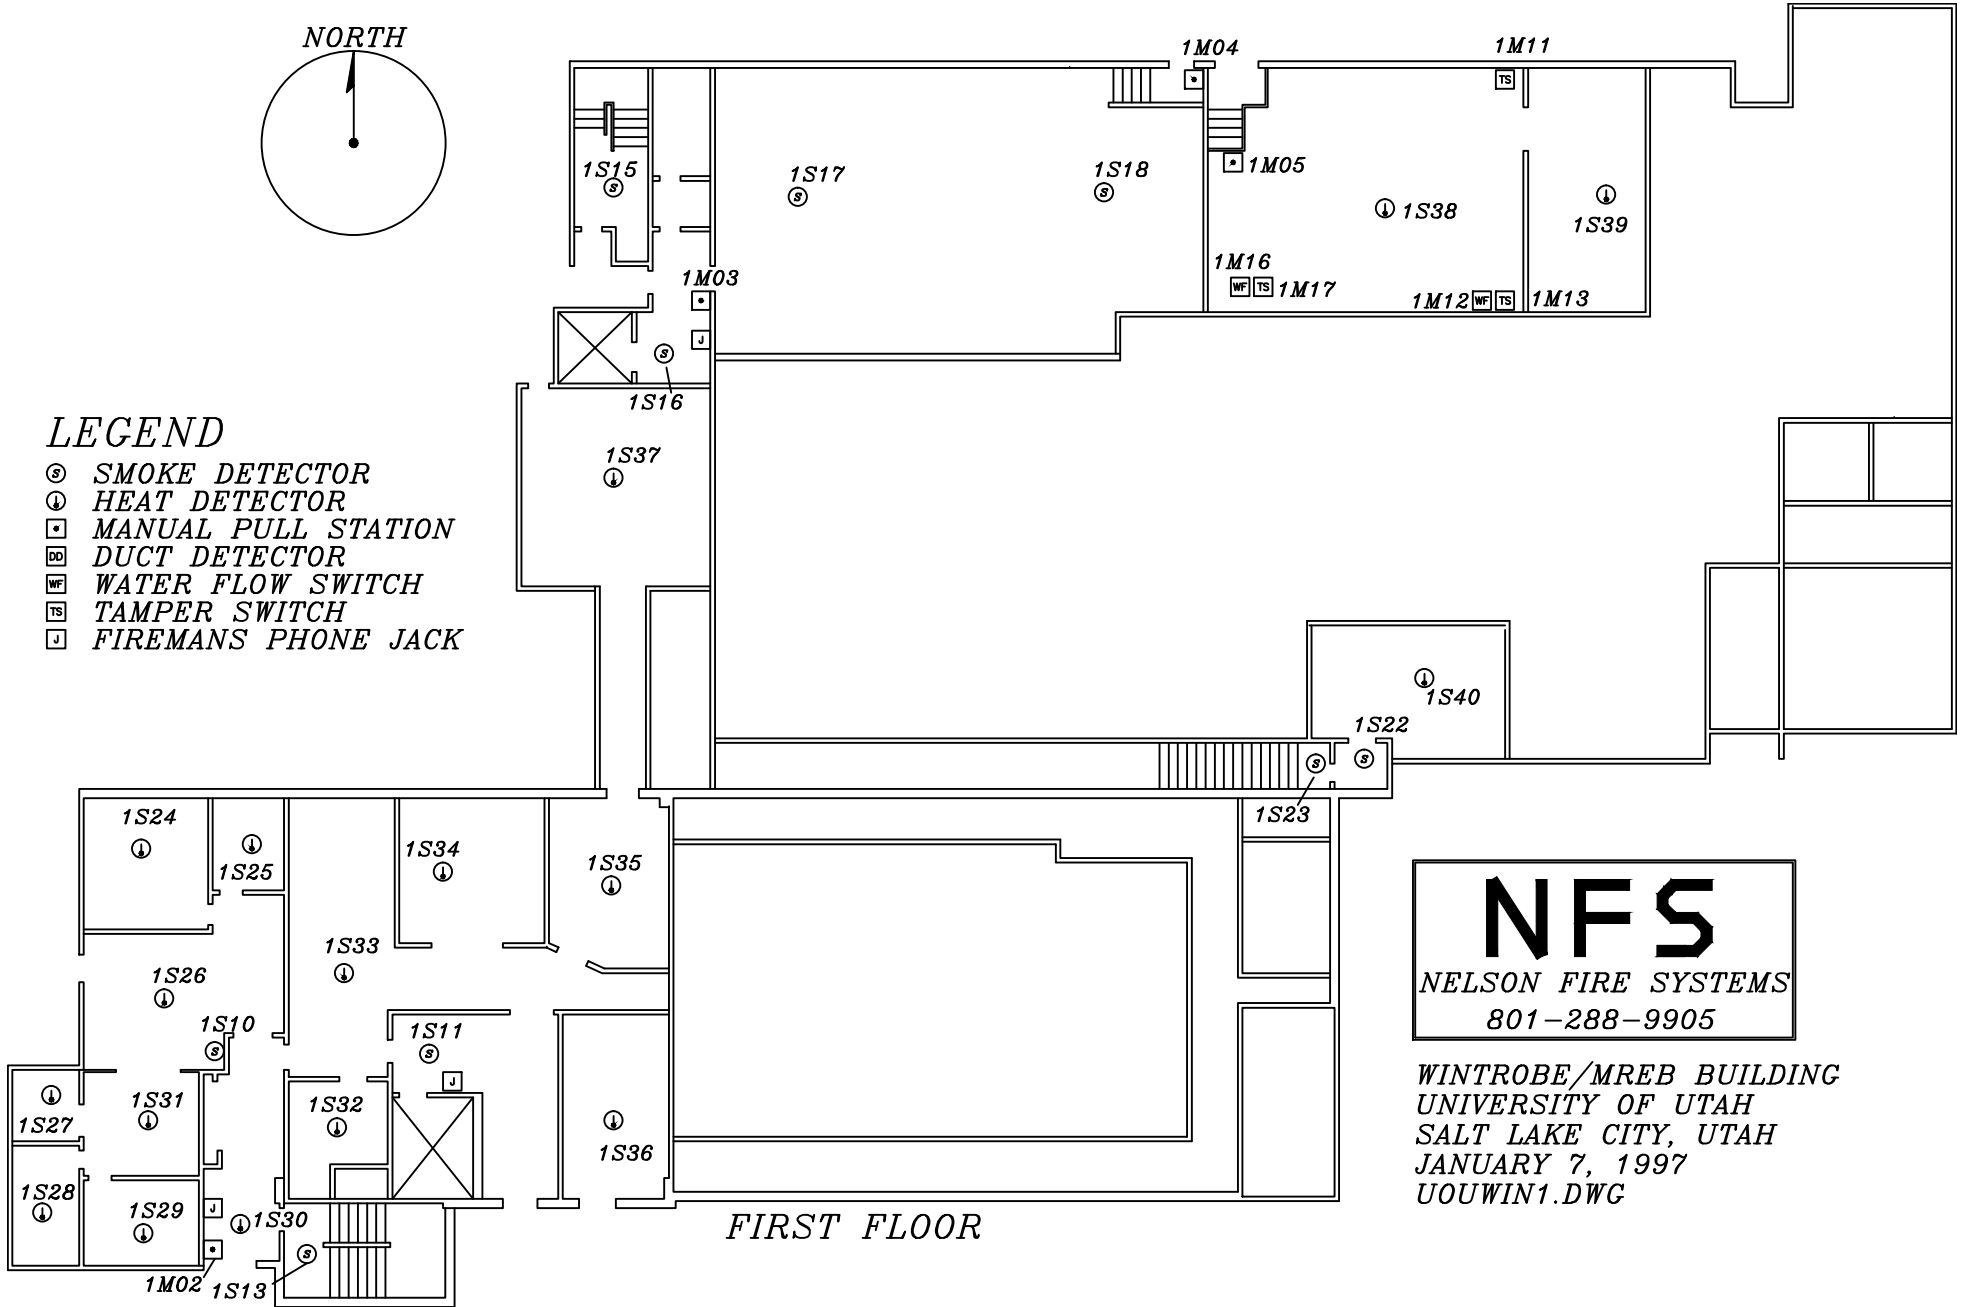

FIRST FLOOR


NFS

NELSON FIRE SYSTEMS
801-288-9905

WINTROBE/MREB BUILDING
UNIVERSITY OF UTAH
SALT LAKE CITY, UTAH
JANUARY 7, 1997
UOUWIN1.DWG




- | | |
|---|----------------------------|
|  | <i>SMOKE DETECTOR</i> |
|  | <i>HEAT DETECTOR</i> |
|  | <i>MANUAL PULL STATION</i> |
|  | <i>FIREMANS PHONE JACK</i> |
|  | <i>WATER FLOW SWITCH</i> |
|  | <i>TAMPER SWITCH</i> |

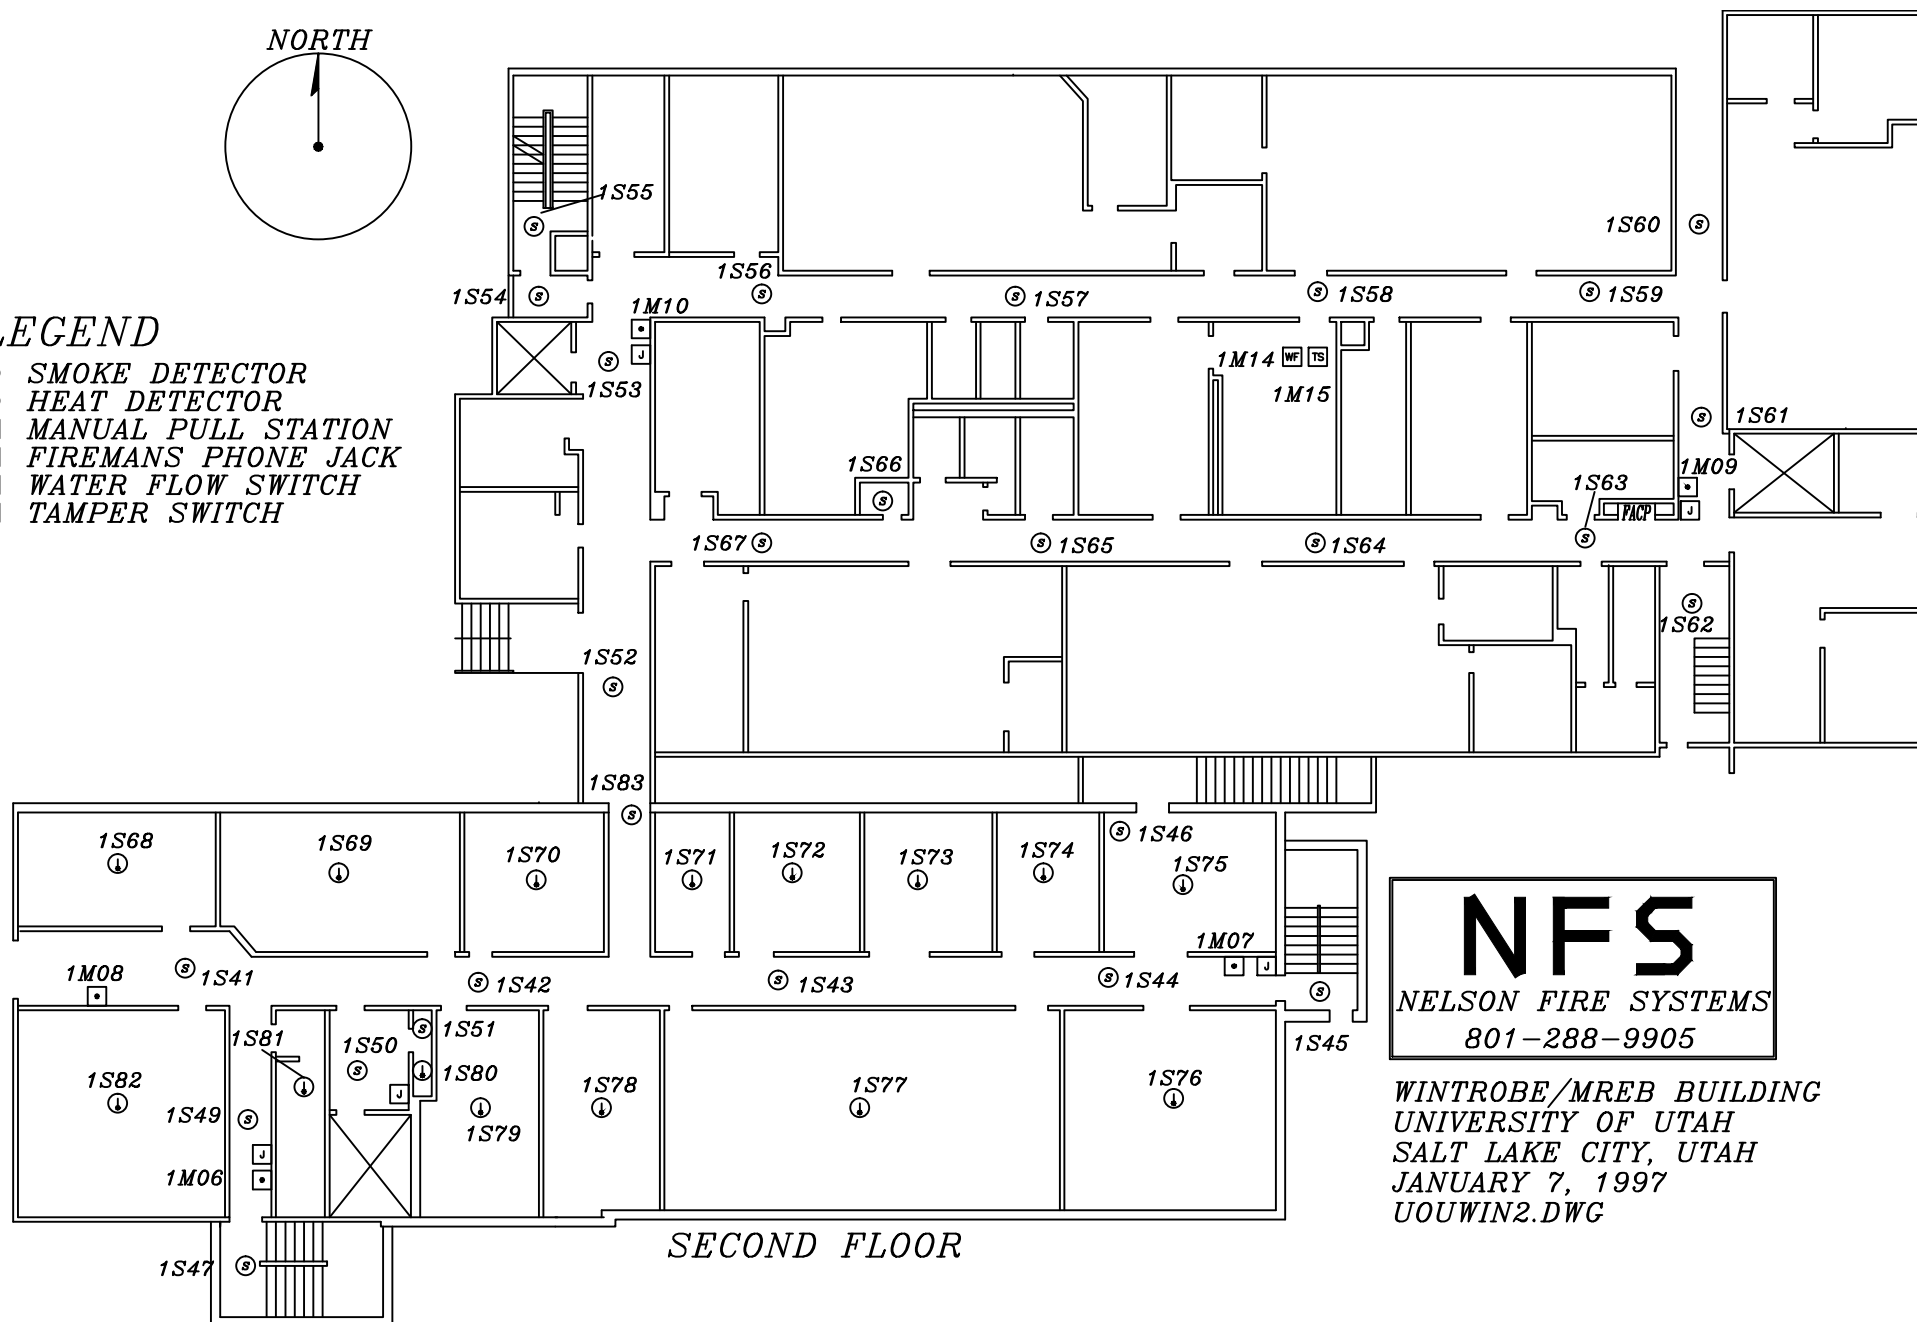

NFS


NELSON FIRE SYSTEMS
801-288-9905

WINTROBE/MREB BUILDING
UNIVERSITY OF UTAH
SALT LAKE CITY, UTAH
JANUARY 7, 1997
UOUWIN2.DWG

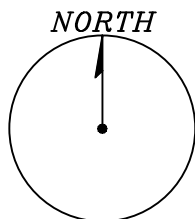

LEGEND

- Ⓢ SMOKE DETECTOR
- Ⓛ HEAT DETECTOR
- MANUAL PULL STATION
- Ⓜ FIREMANS PHONE JACK
- WF WATER FLOW SWITCH
- TS TAMPER SWITCH
- DD DUCT DETECTORS
- CM CONTROL MODULES

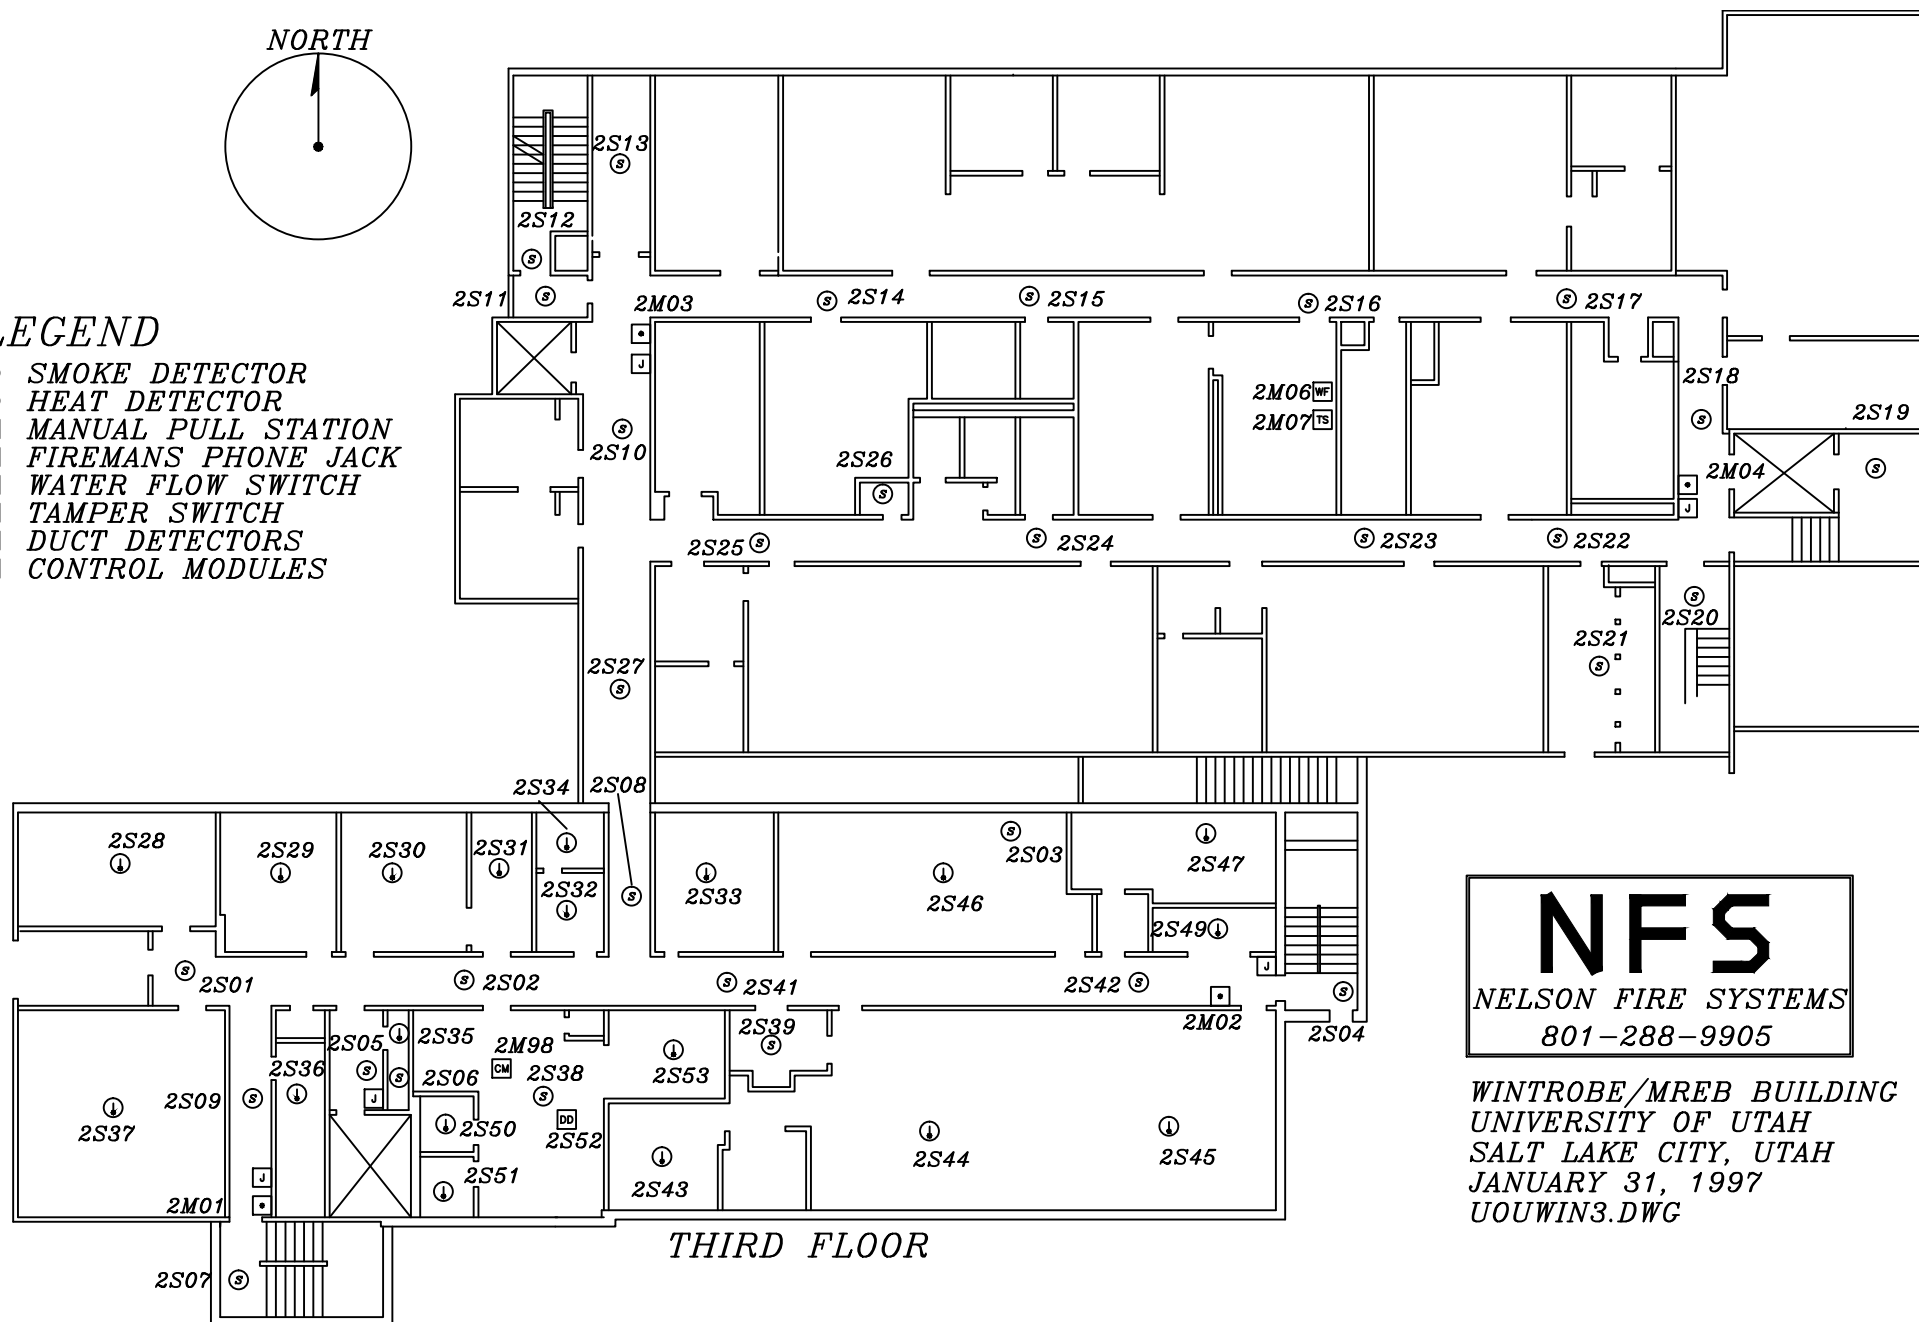


THIRD FLOOR

NFS


NELSON FIRE SYSTEMS
801-288-9905

WINTROBE/MREB BUILDING
UNIVERSITY OF UTAH
SALT LAKE CITY, UTAH
JANUARY 31, 1997
UOUWIN3.DWG

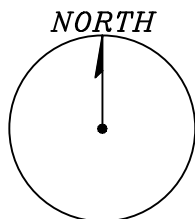


LEGEND

- Ⓢ SMOKE DETECTOR
- Ⓛ HEAT DETECTOR
- Ⓜ MANUAL PULL STATION
- Ⓜ FIREMANS PHONE JACK
- WF WATER FLOW SWITCH
- TS TAMPER SWITCH

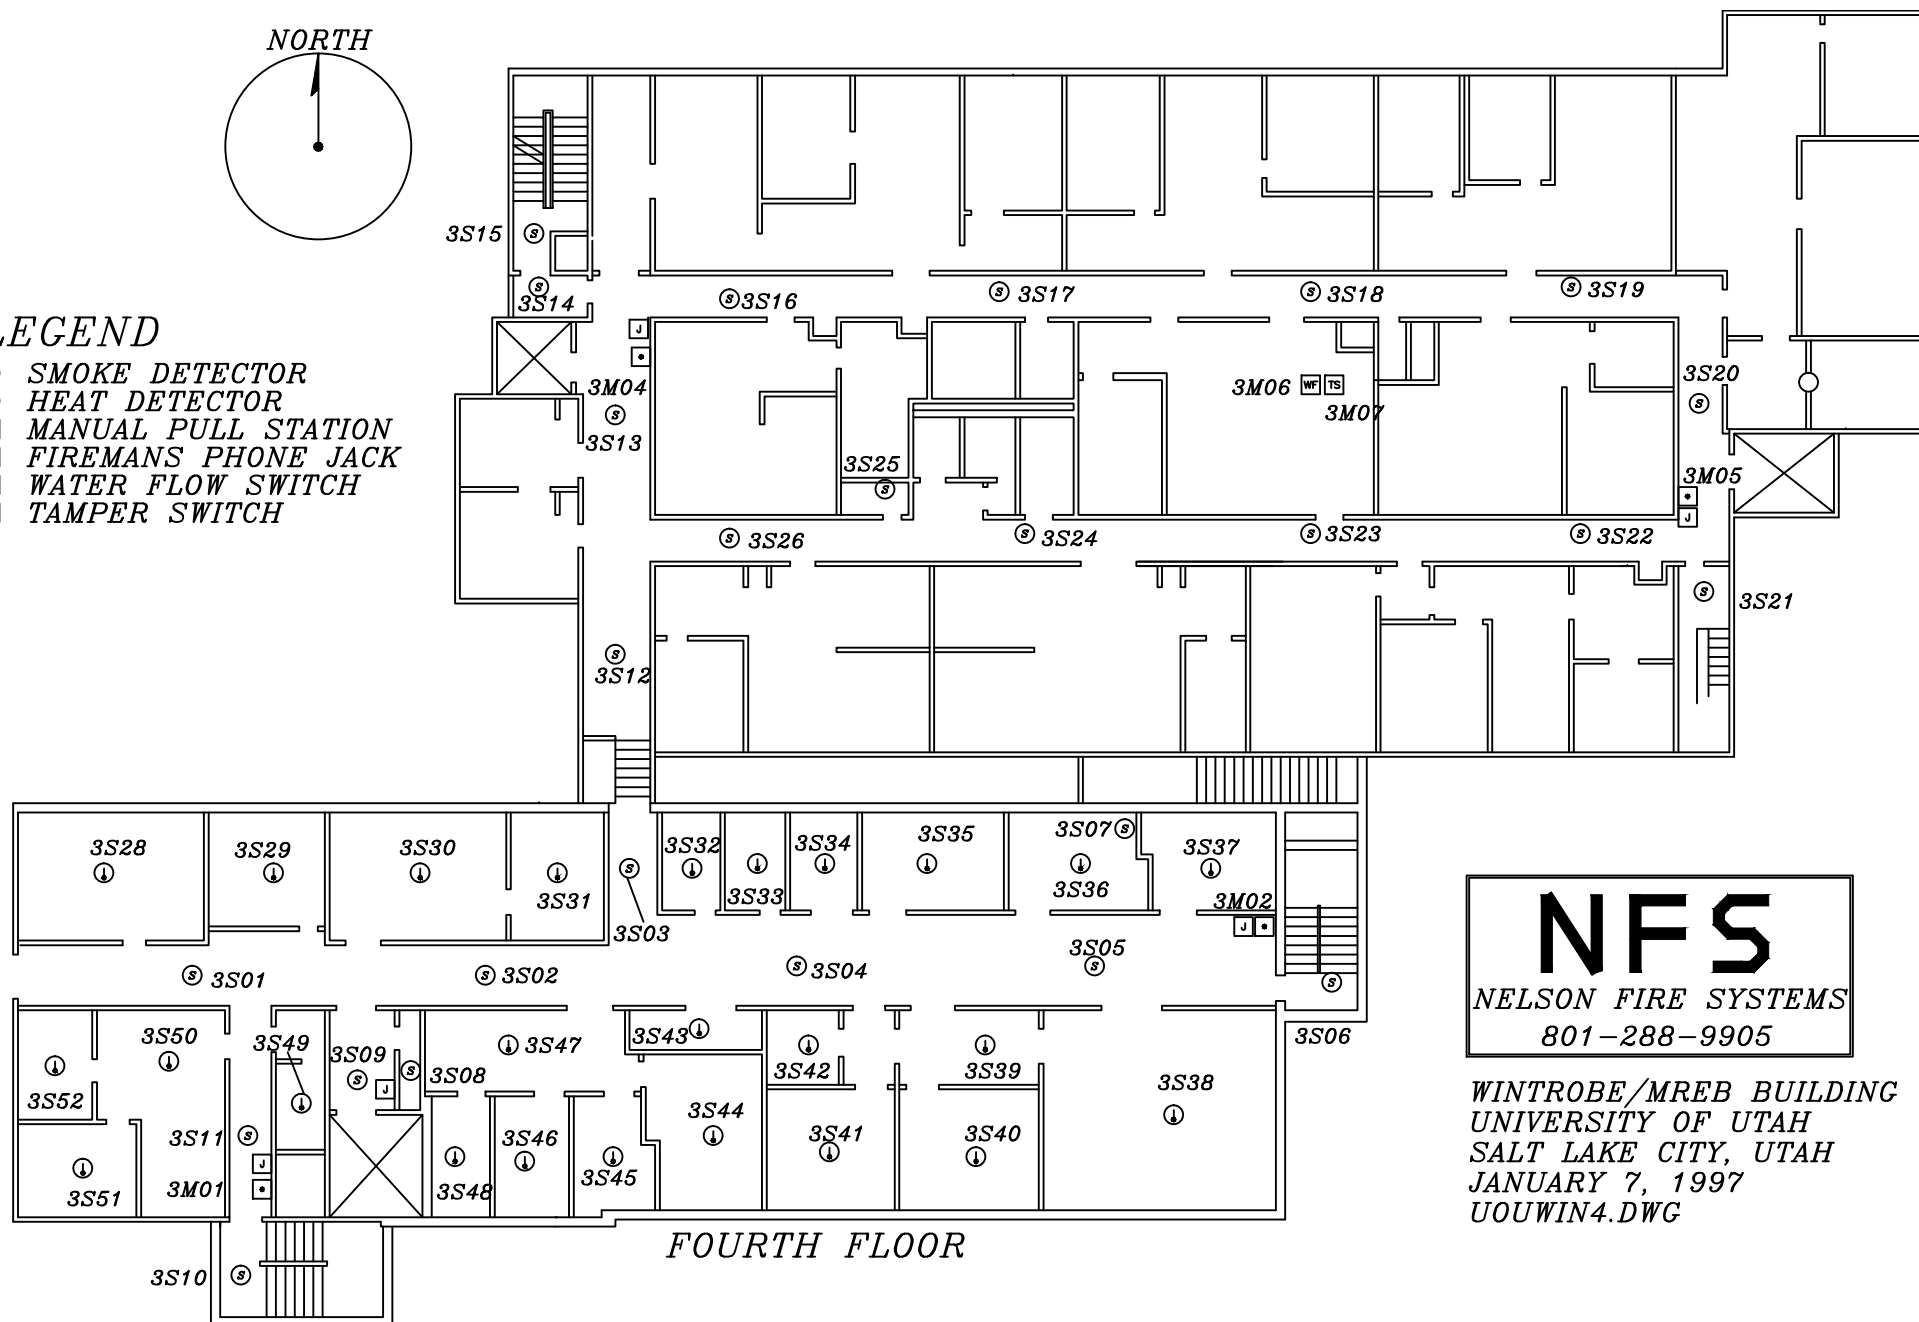



NFS
 NELSON FIRE SYSTEMS
 801-288-9905

WINTROBE/MREB BUILDING
 UNIVERSITY OF UTAH
 SALT LAKE CITY, UTAH
 JANUARY 7, 1997
 UOUWIN4.DWG

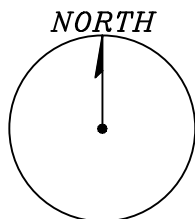

LEGEND

- Ⓢ SMOKE DETECTOR
- Ⓡ HEAT DETECTOR
- Ⓜ MANUAL PULL STATION
- Ⓜ FIREMANS PHONE JACK
- WF WATER FLOW SWITCH
- TS TAMPER SWITCH
- CM CONTROL MODULE

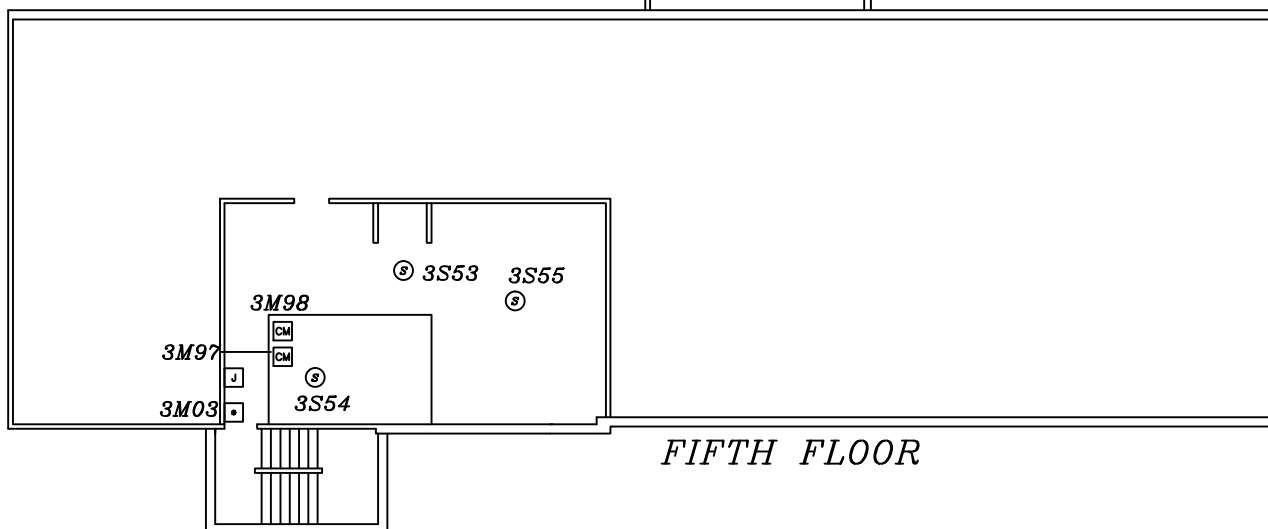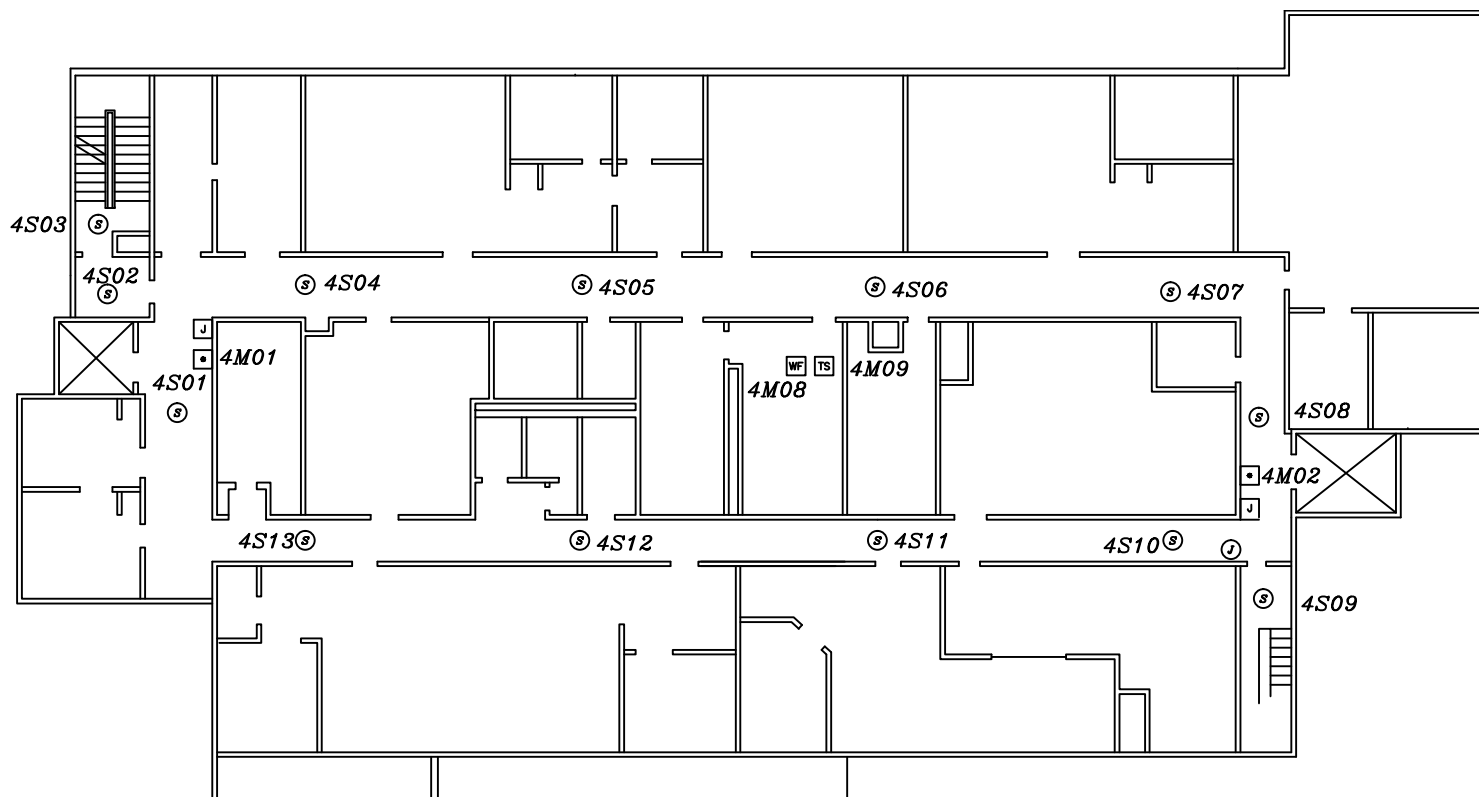


FIFTH FLOOR

NFS


NELSON FIRE SYSTEMS
801-288-9905

WINTROBE/MREB BUILDING
UNIVERSITY OF UTAH
SALT LAKE CITY, UTAH
JANUARY 7, 1997
UOUWIN5.DWG

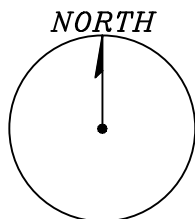

LEGEND

- Ⓢ SMOKE DETECTOR
- Ⓛ HEAT DETECTOR
- Ⓜ MANUAL PULL STATION
- Ⓜ FIREMANS PHONE JACK
- WF WATER FLOW SWITCH
- TS TAMPER SWITCH

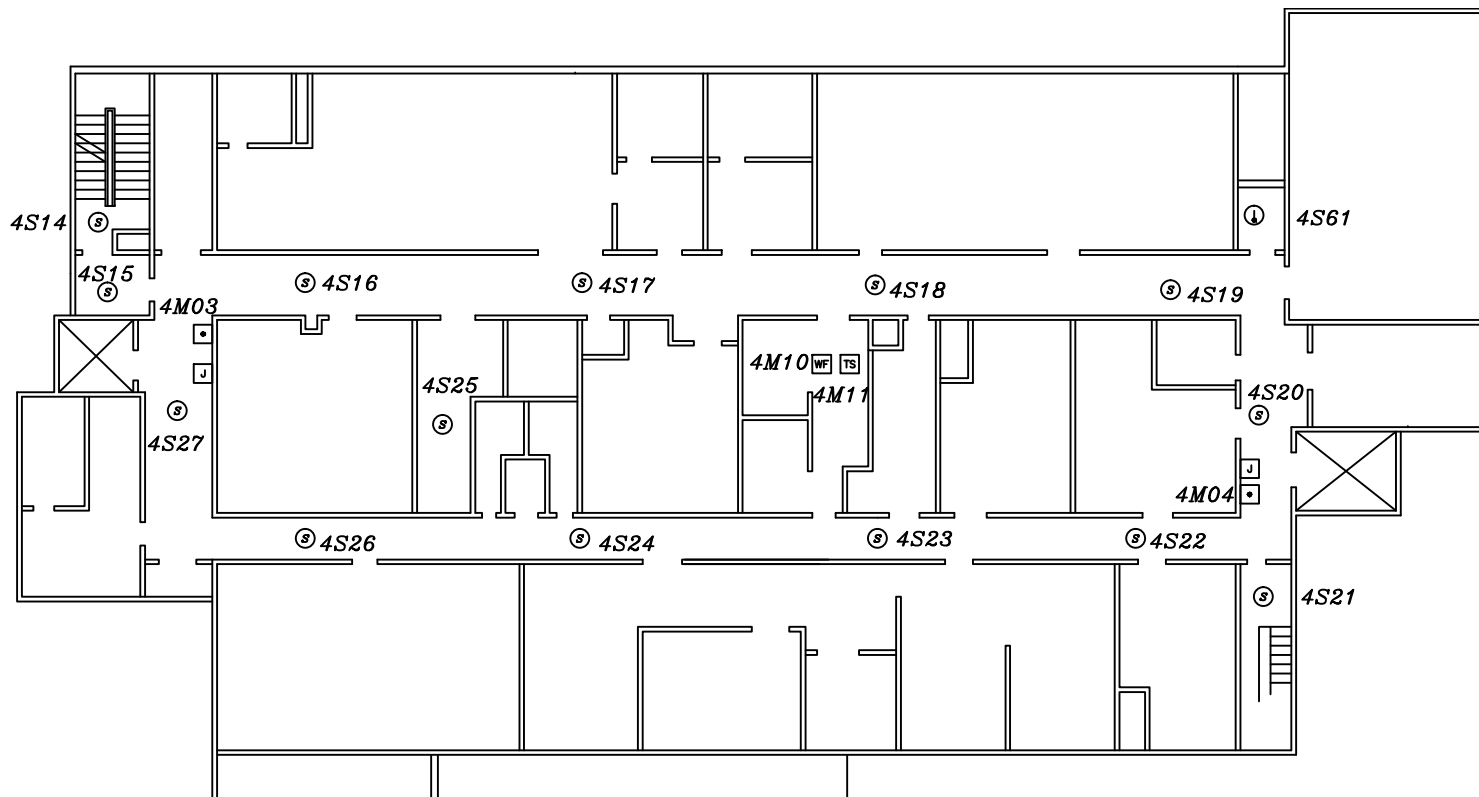


SIXTH FLOOR

NFS


NELSON FIRE SYSTEMS
801-288-9905

WINTROBE/MREB BUILDING
UNIVERSITY OF UTAH
SALT LAKE CITY, UTAH
JANUARY 7, 1997
UOUWIN6.DWG

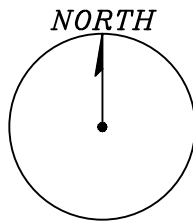

LEGEND

- Ⓢ SMOKE DETECTOR
- Ⓡ HEAT DETECTOR
- MANUAL PULL STATION
- Ⓜ FIREMANS PHONE JACK
- WF WATER FLOW SWITCH
- TS TAMPER SWITCH

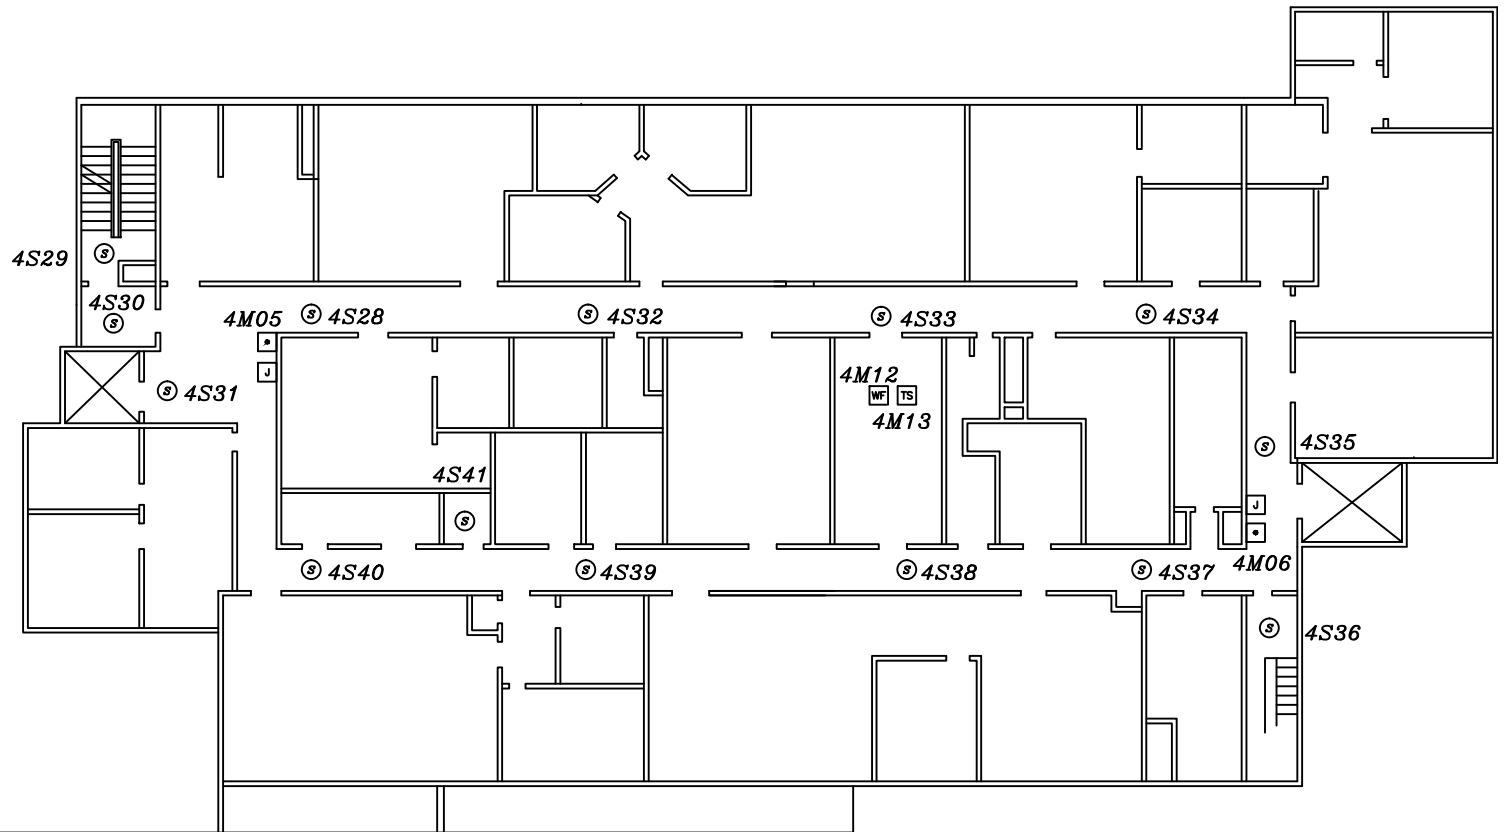


SEVENTH FLOOR

NFS


NELSON FIRE SYSTEMS
801-288-9905

WINTROBE/MREB BUILDING
UNIVERSITY OF UTAH
SALT LAKE CITY, UTAH
JANUARY 7, 1997
UOUWIN7.DWG

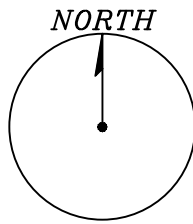

LEGEND

- Ⓢ SMOKE DETECTOR
- Ⓡ HEAT DETECTOR
- ⬢ MANUAL PULL STATION
- Ⓜ FIREMANS PHONE JACK
- WF WATER FLOW SWITCH
- TS TAMPER SWITCH

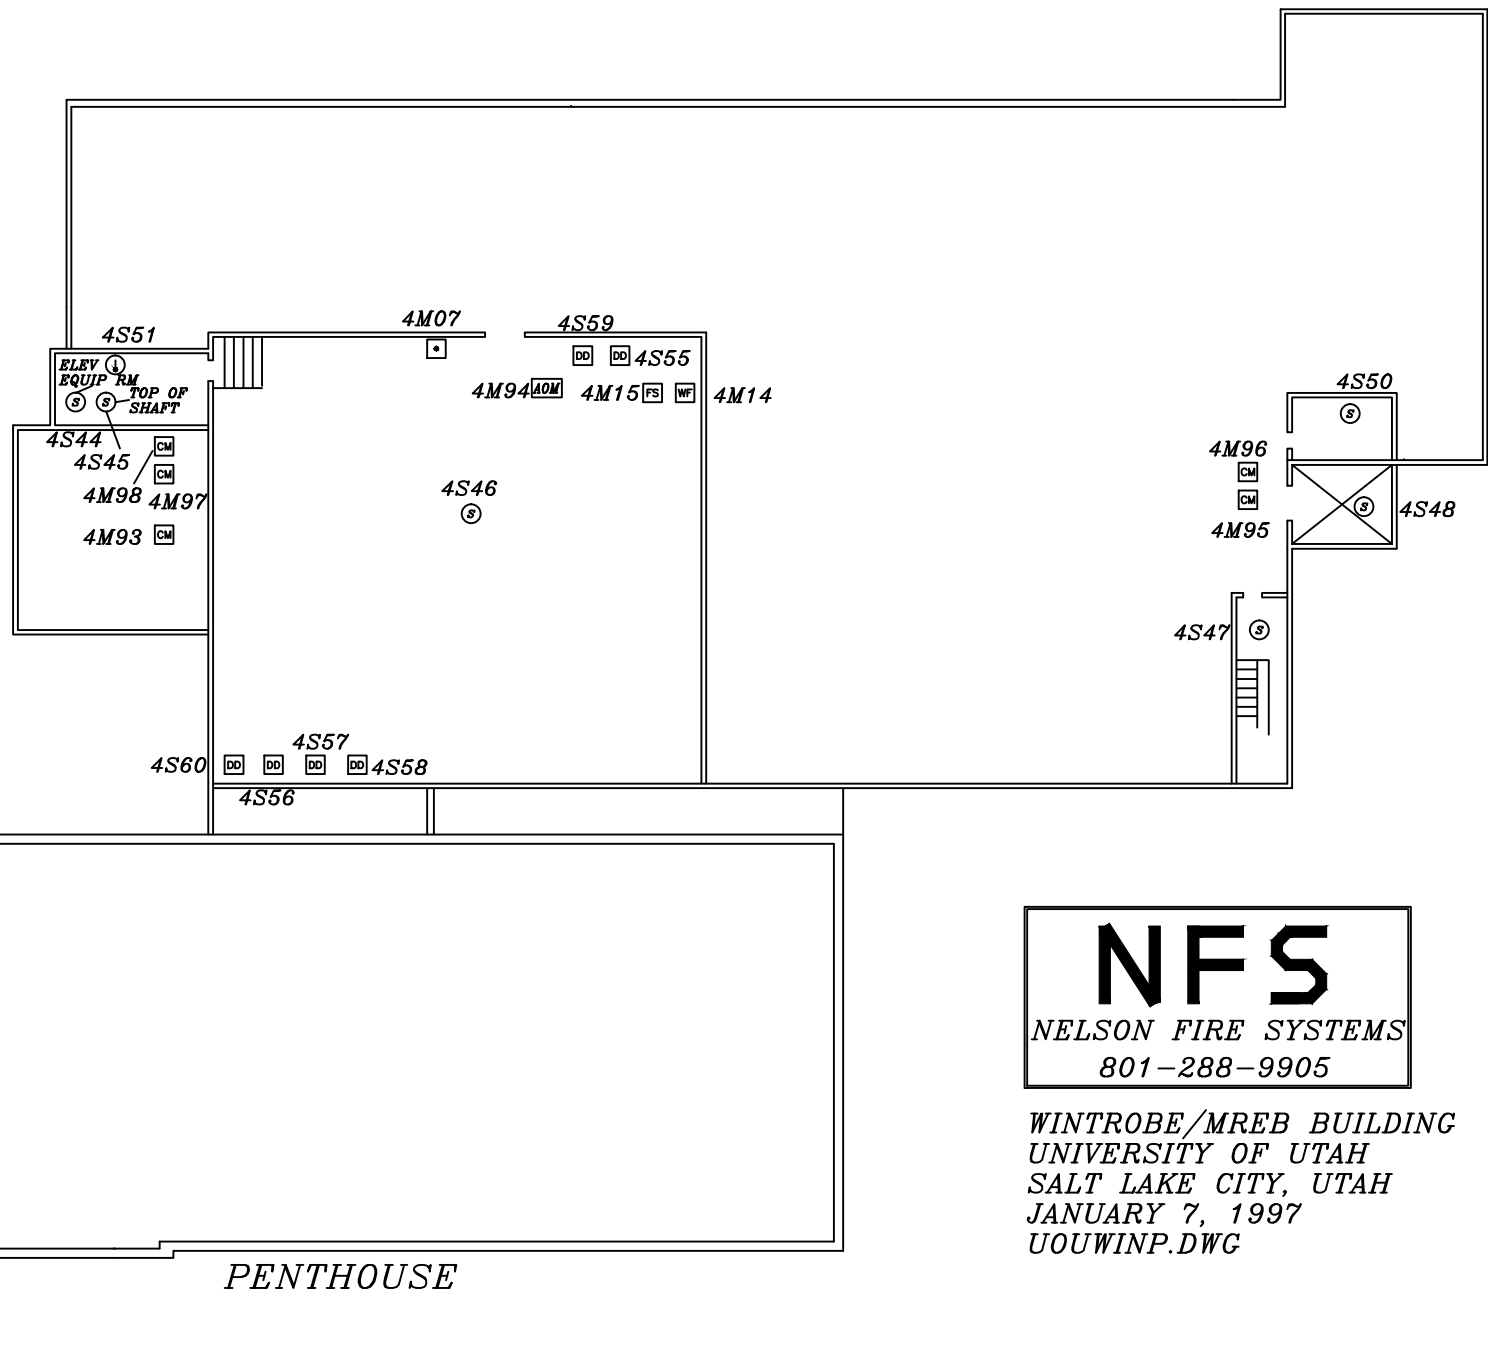

NFS
NELSON FIRE SYSTEMS
801-288-9905

WINTROBE/MREB BUILDING
UNIVERSITY OF UTAH
SALT LAKE CITY, UTAH
JANUARY 7, 1997
UOUWINP.DWG