




FIRST FLOOR

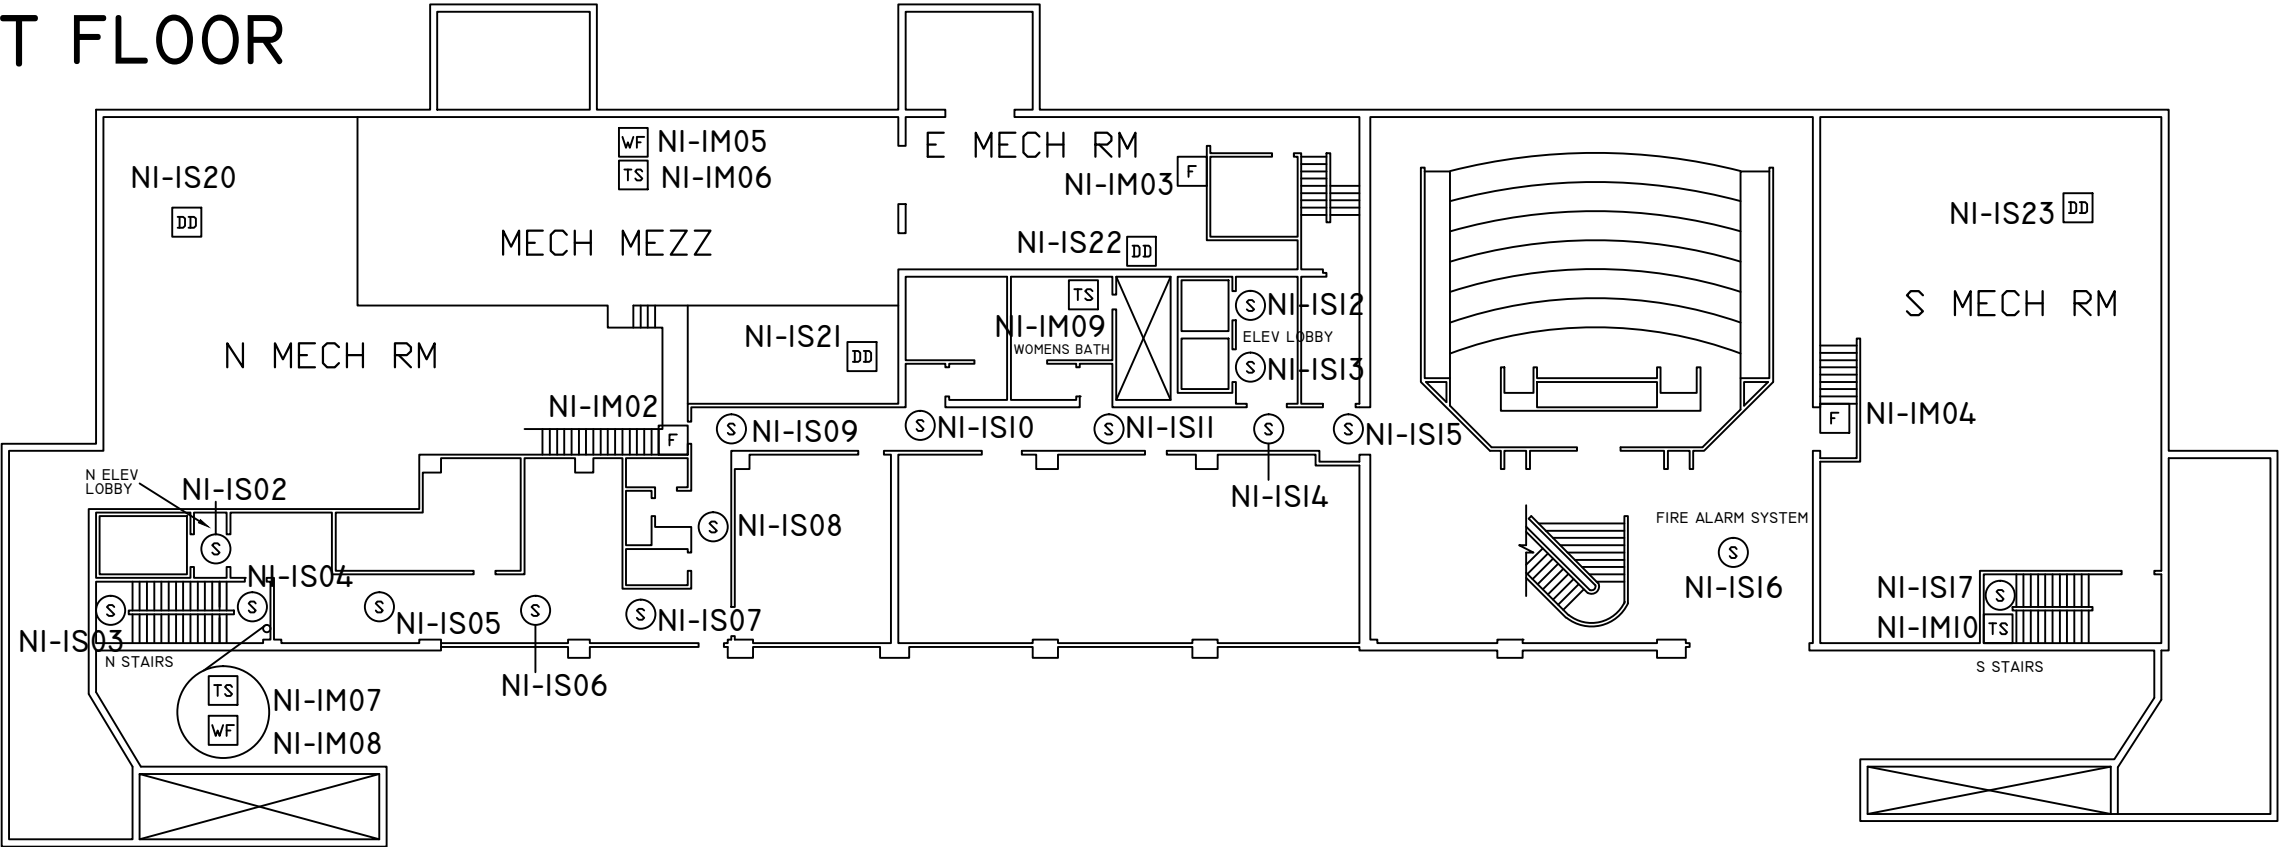

ADDRESS LABEL CLARIFICATION

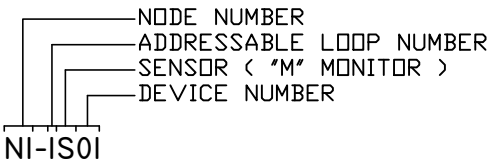


LEVEL 0

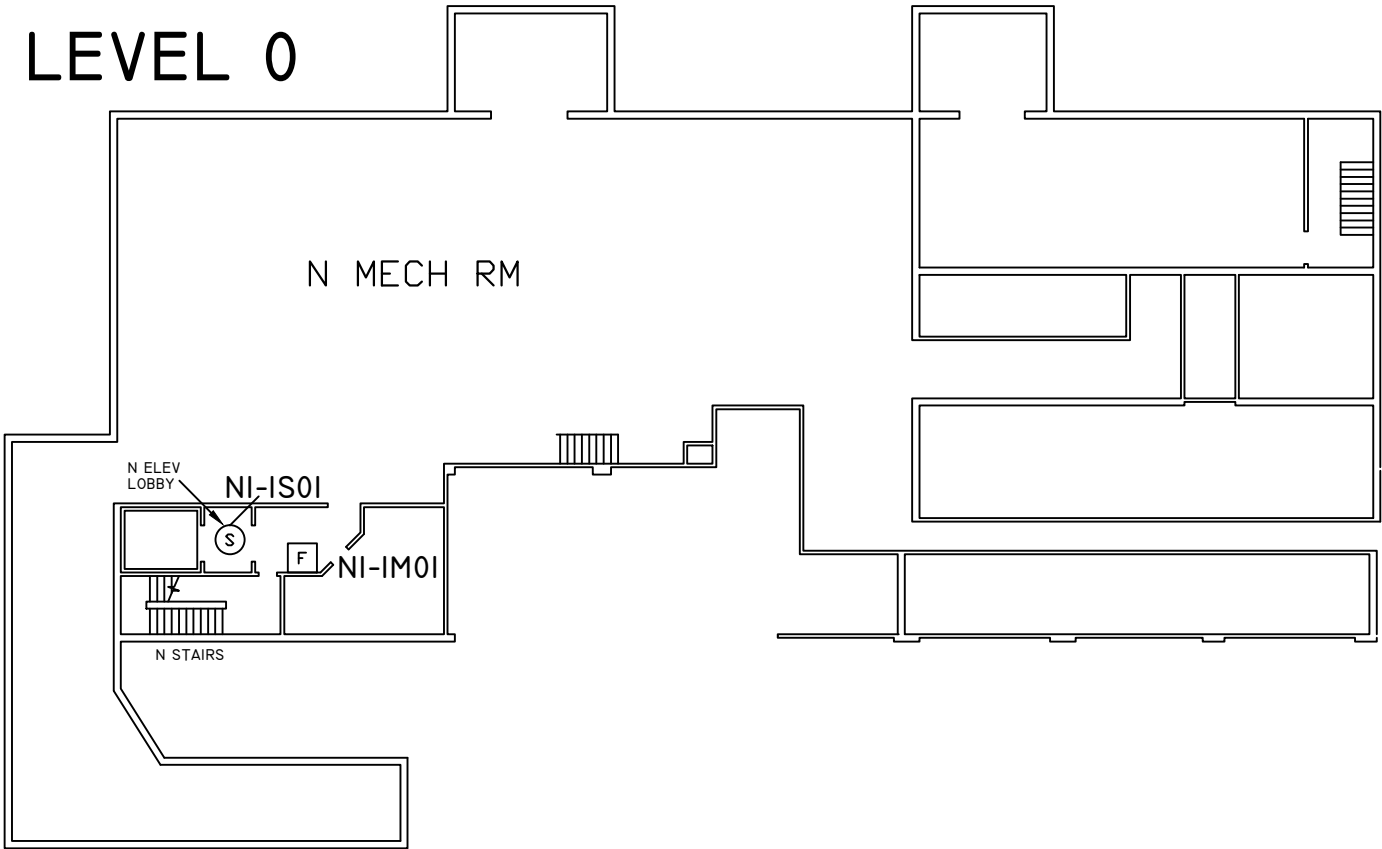

DEVICE LEGEND

SYMBOL	DESCRIPTION
(S)	SMOKE DETECTOR
(T)	THERMAL DETECTOR
(F)	MANUAL PULL STATION
(DD)	DUCT SMOKE DETECTOR
(WF)	WATERFLOW SWITCH MONITOR MODULE
(TS)	TAMPER SWITCH MONITOR MODULE
(MM)	MONITOR MODULE
(CM)	CONTROL MODULE
(R)	RELAY- ARB-C
(DH)	DOORHOLDER
(RA)	REMOTE ANNUNCIATOR ENCLOSURE
(FACP)	FIRE ALARM CONTROL PANEL
(TRAN)	TRANSPONDER PANEL

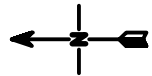

NOTE:
NFS DRAWINGS ARE BASED ON THE PROJECT
ARCHITECT/ENGINEER (A/E) PLANS AND SPECIFICATIONS
FURNISHED TO NFS. A/E IS SOLELY RESPONSIBLE
(NOT NFS) FOR THE TYPE, SIZE, LOCATION, AND
SUITABILITY OF ALL FIRE ALARMS, CONTROL PANELS,
AND OTHER DEVICES SHOWN ON THE A/E PLANS.
NFS DRAWINGS ARE TO SHOW ONLY THE WIRING
DIAGRAMS BETWEEN FIRE ALARM DEVICES AND
CONTROL PANELS. NFS IS NOT RESPONSIBLE FOR
THE INFORMATION SHOWN ON THE A/E PLANS.

UNIVERSITY OF UTAH
GENETICS BUILDING
SALT LAKE CITY, UTAH
FIRE ALARM SYSTEM

NFS

NELSON FIRE SYSTEMS
801-468-8300


DRAWN BY: ZM
DESIGNED BY: XXXX
APPROVED BY: BN
DATE: 10/18/05
SCALE: N.T.S.
PROJECT NO: XXXX
REV NO: XXXX
DRAWING NAME:
GENETICS081.DWG

FIRE ALARM SYSTEM



PAGE:

FA-I

THIRD FLOOR

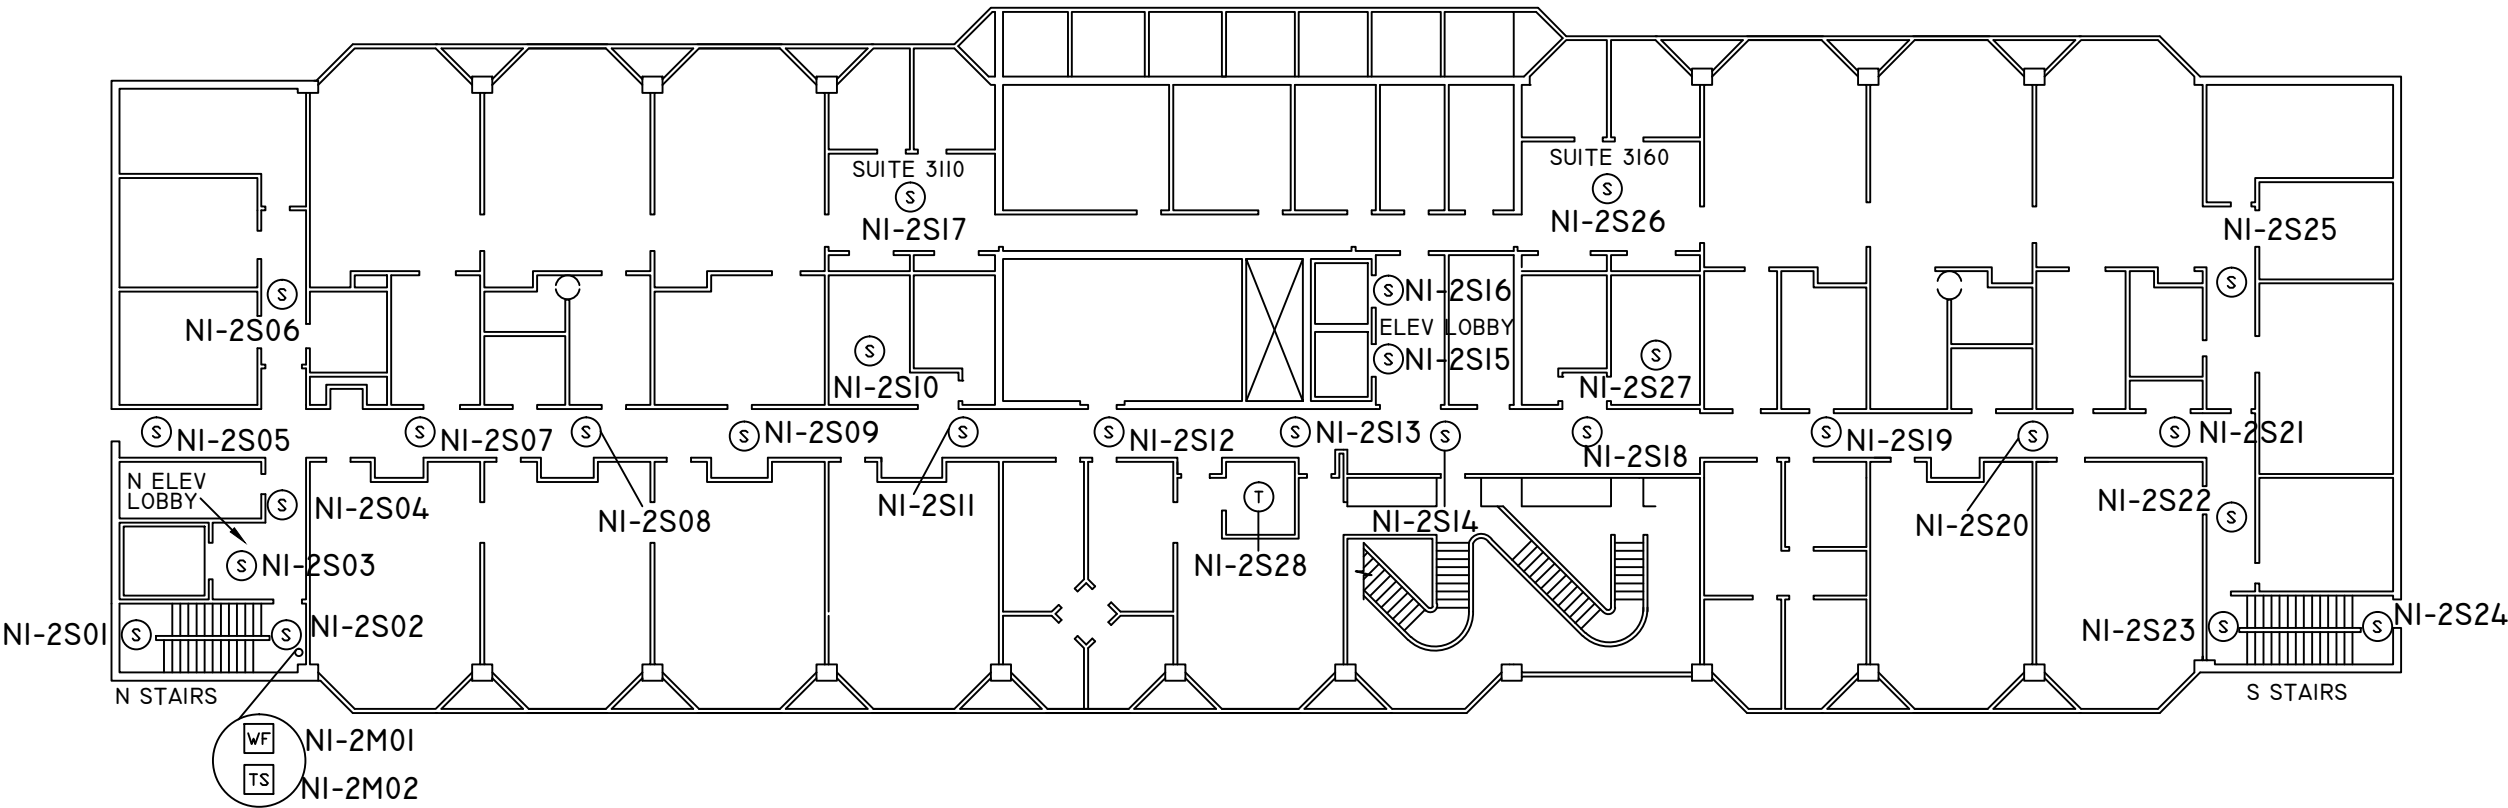

SECOND FLOOR

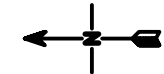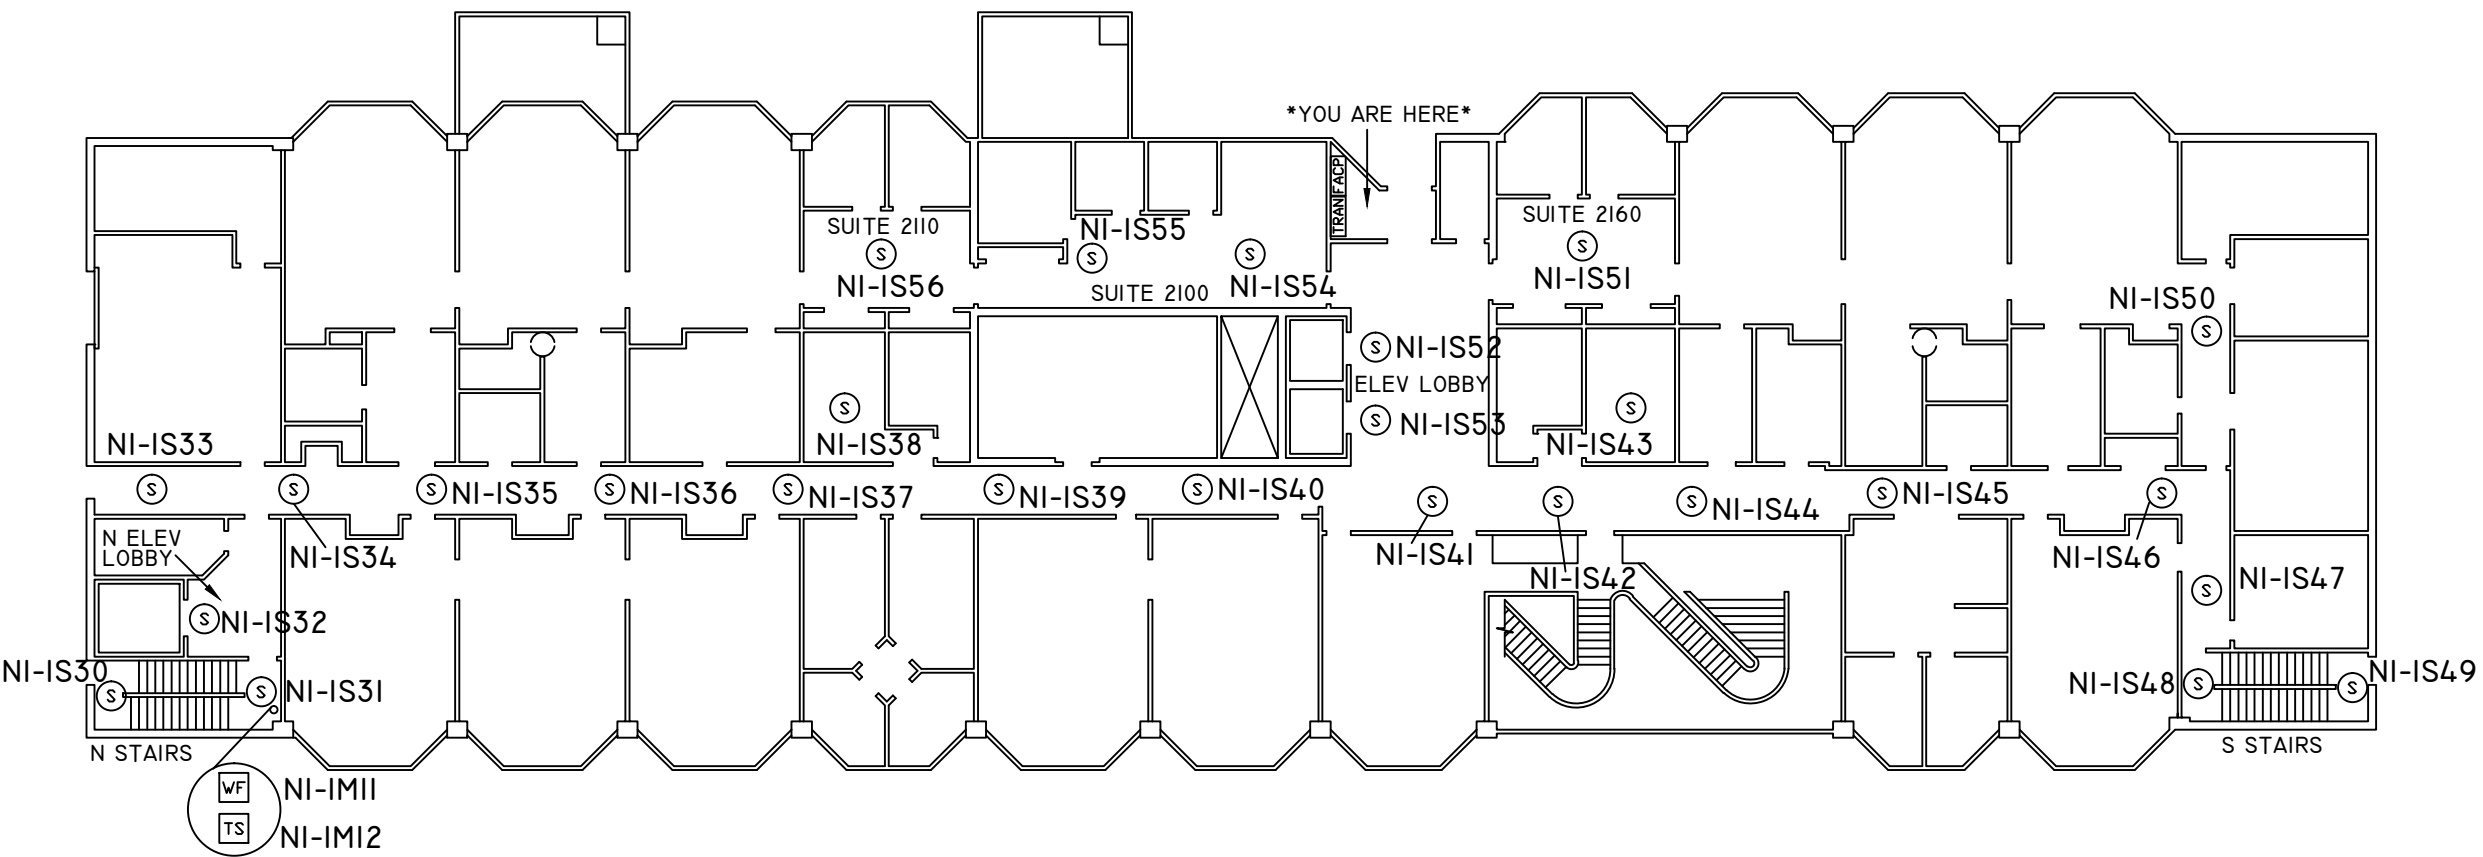

NOTE: NFS DRAWINGS ARE BASED ON THE PROJECT ARCHITECT/ENGINEER (A/E) PLANS AND SPECIFICATIONS FURNISHED TO NFS. A/E IS SOLELY RESPONSIBLE (NOT NFS) FOR THE TYPE, SIZE, LOCATION, AND SUITABILITY OF ALL FIRE ALARMS, CONTROL PANELS, AND OTHER DEVICES SHOWN ON THE A/E PLANS. NFS DRAWINGS ARE TO SHOW ONLY THE WIRING DIAGRAMS BETWEEN FIRE ALARM DEVICES AND CONTROL PANELS. NFS IS NOT RESPONSIBLE FOR THE INFORMATION SHOWN ON THE A/E PLANS.

UNIVERSITY OF UTAH
GENETICS BUILDING
SALT LAKE CITY, UTAH
FIRE ALARM SYSTEM


NFS
NELSON FIRE SYSTEMS
801-468-8300

DRAWN BY:	ZM
DESIGNED BY:	XXXX
APPROVED BY:	BN
DATE:	10/18/05
SCALE:	N.T.S.
PROJECT NO:	XXXX
REV NO:	XXXX
DRAWING NAME:	GENETICS2&3.DWG



FIRE ALARM SYSTEM

PAGE:
FA-2

FIFTH FLOOR

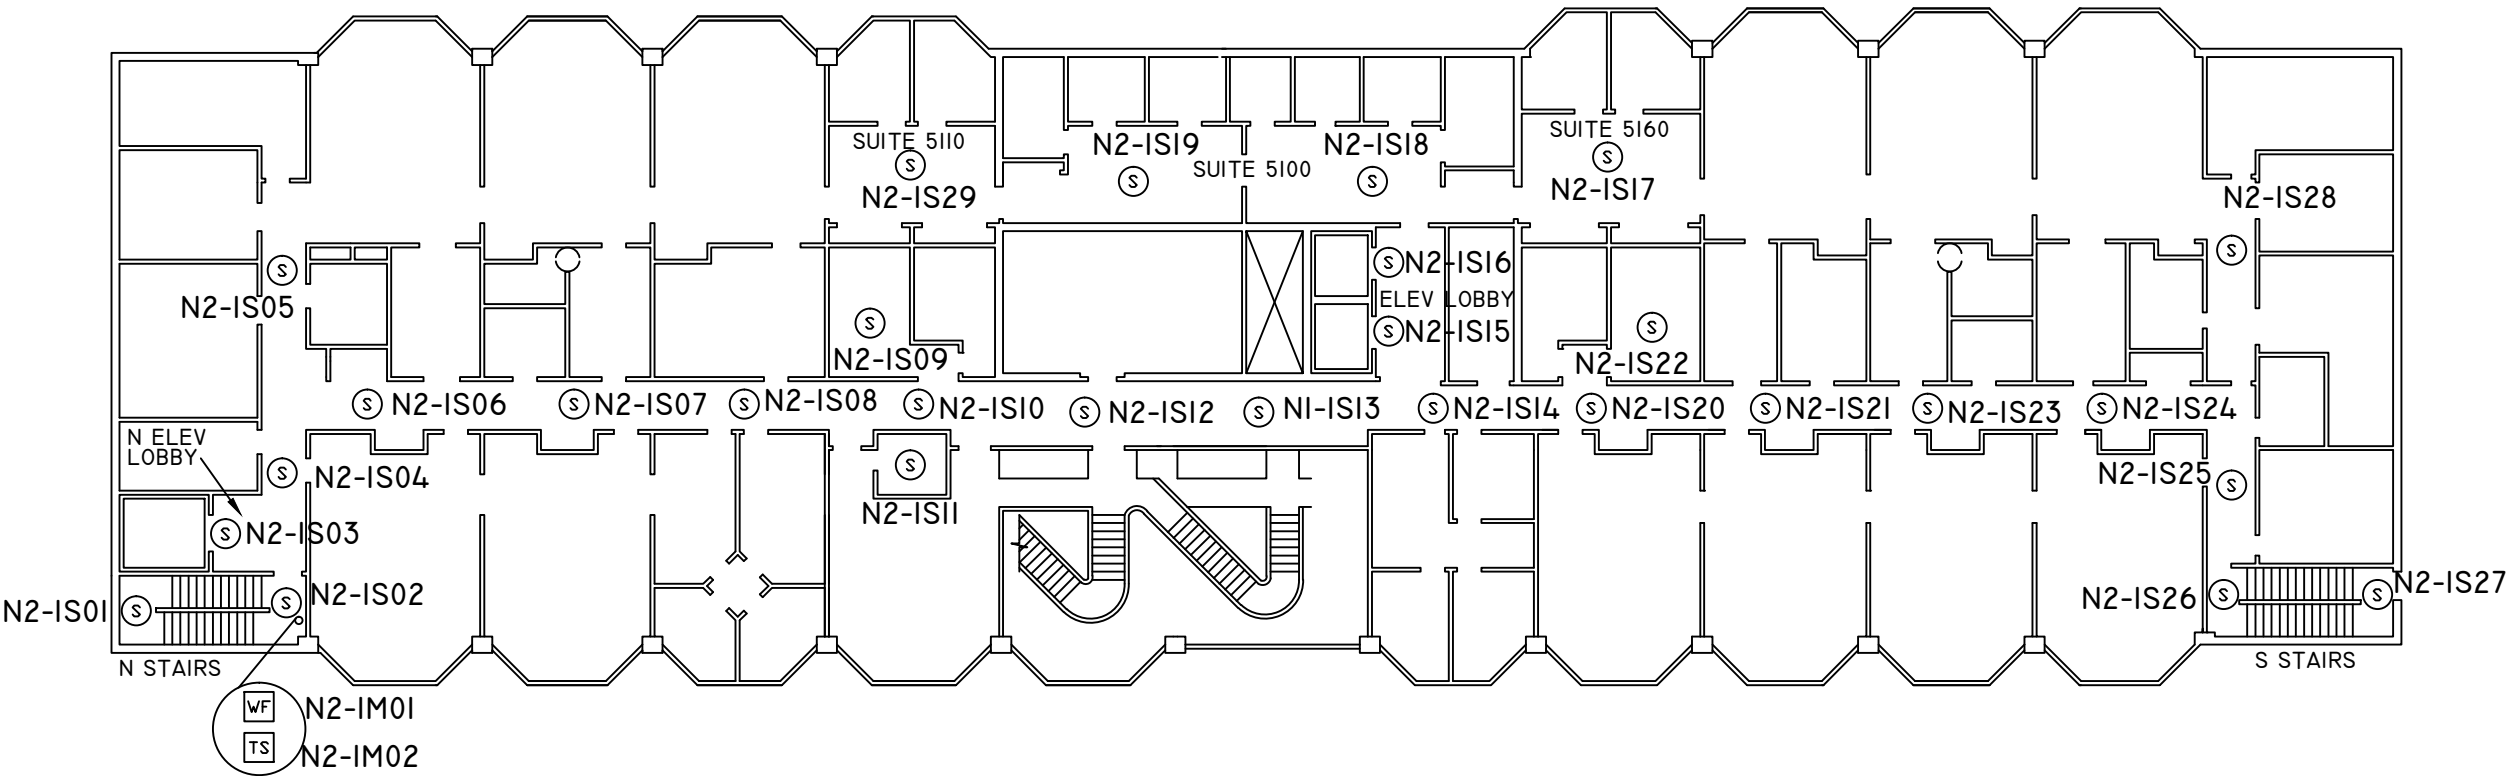

FOURTH FLOOR

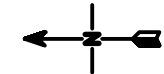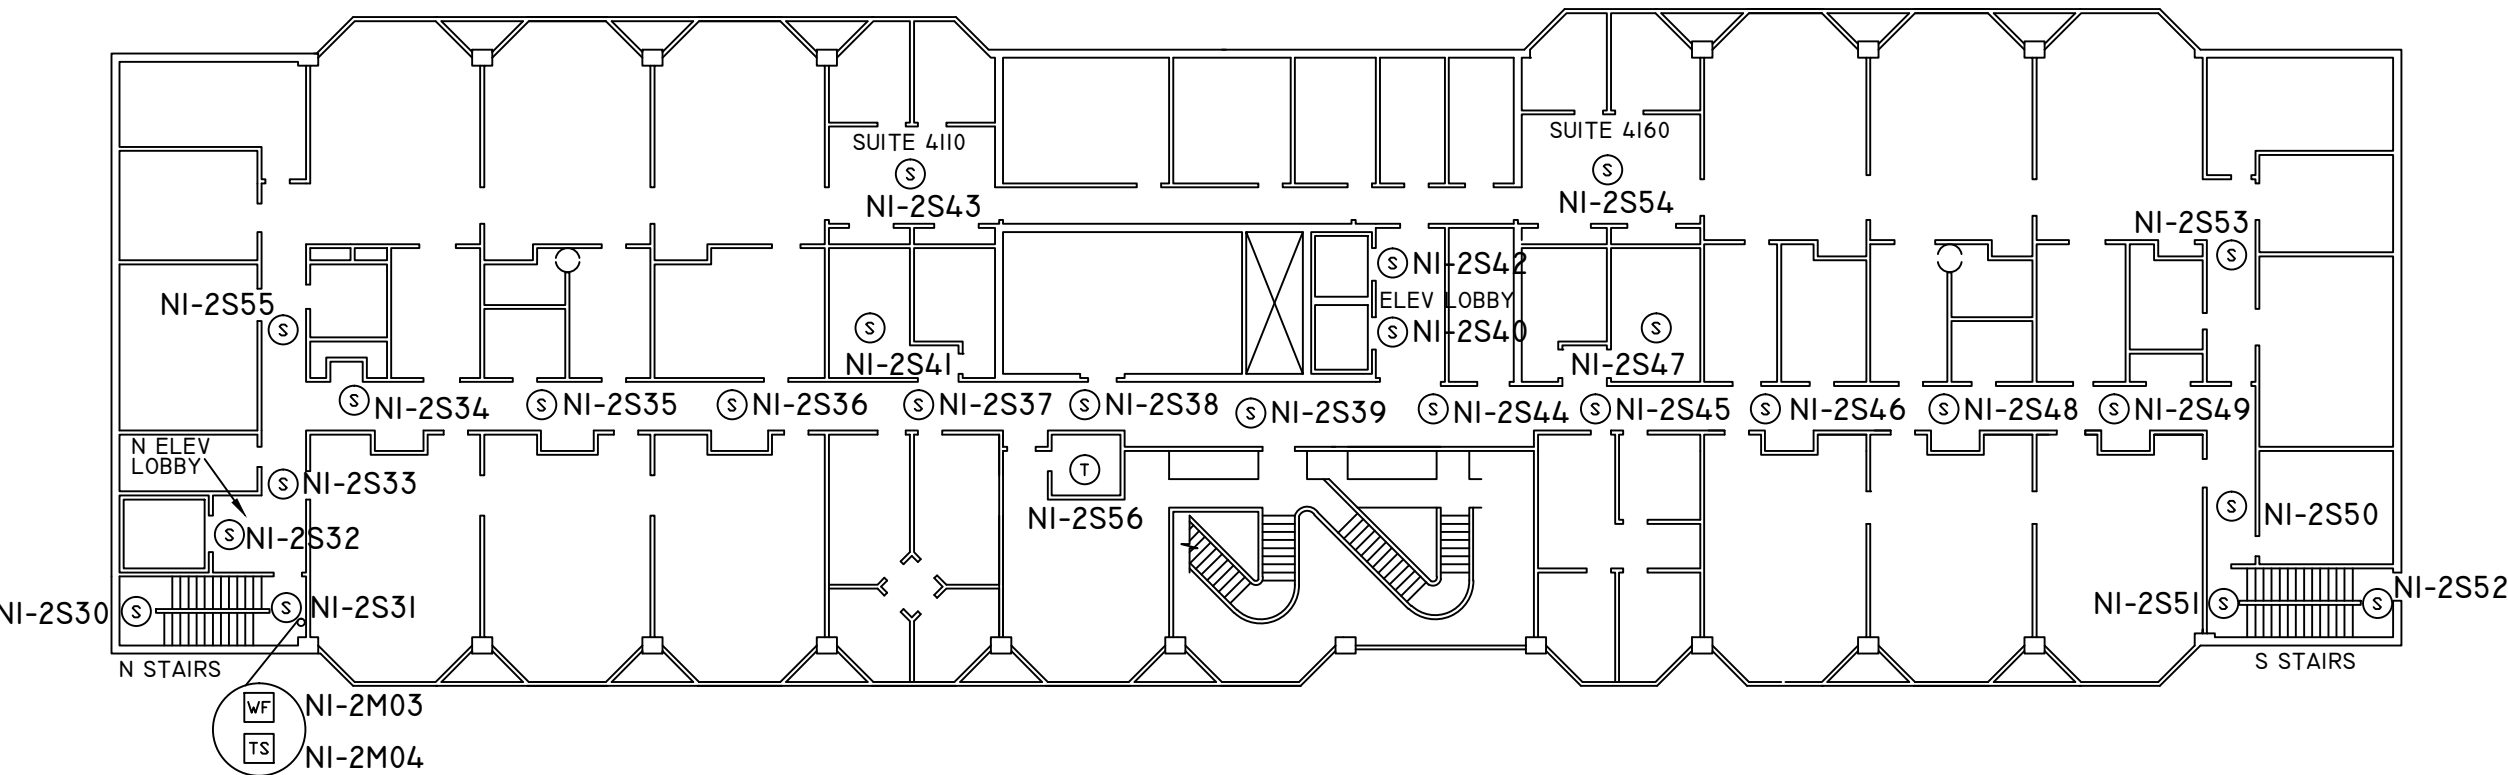




NOTE:
NFS DRAWINGS ARE BASED ON THE PROJECT
ARCHITECT/ENGINEER (A/E) PLANS AND SPECIFICATIONS
FURNISHED TO NFS. A/E IS SOLELY RESPONSIBLE
(NOT NFS) FOR THE TYPE, SIZE, LOCATION, AND
SUITABILITY OF ALL FIRE ALARMS, CONTROL PANELS,
AND OTHER DEVICES SHOWN ON THE A/E PLANS.
NFS DRAWINGS ARE TO SHOW ONLY THE WIRING
DIAGRAMS BETWEEN FIRE ALARM DEVICES AND
CONTROL PANELS. NFS IS NOT RESPONSIBLE FOR
THE INFORMATION SHOWN ON THE A/E PLANS.

UNIVERSITY OF UTAH
GENETICS BUILDING
SALT LAKE CITY, UTAH
FIRE ALARM SYSTEM

NFS
NELSON FIRE SYSTEMS
801-468-8300

DRAWN BY:	ZM
DESIGNED BY:	XXXX
APPROVED BY:	BN
DATE:	10/18/05
SCALE:	N.T.S.
PROJECT NO:	XXXX
REV NO:	XXXX
DRAWING NAME:	GENETICS4&5.DWG

FIRE ALARM SYSTEM
DEVICE NUMBERS

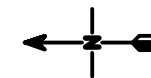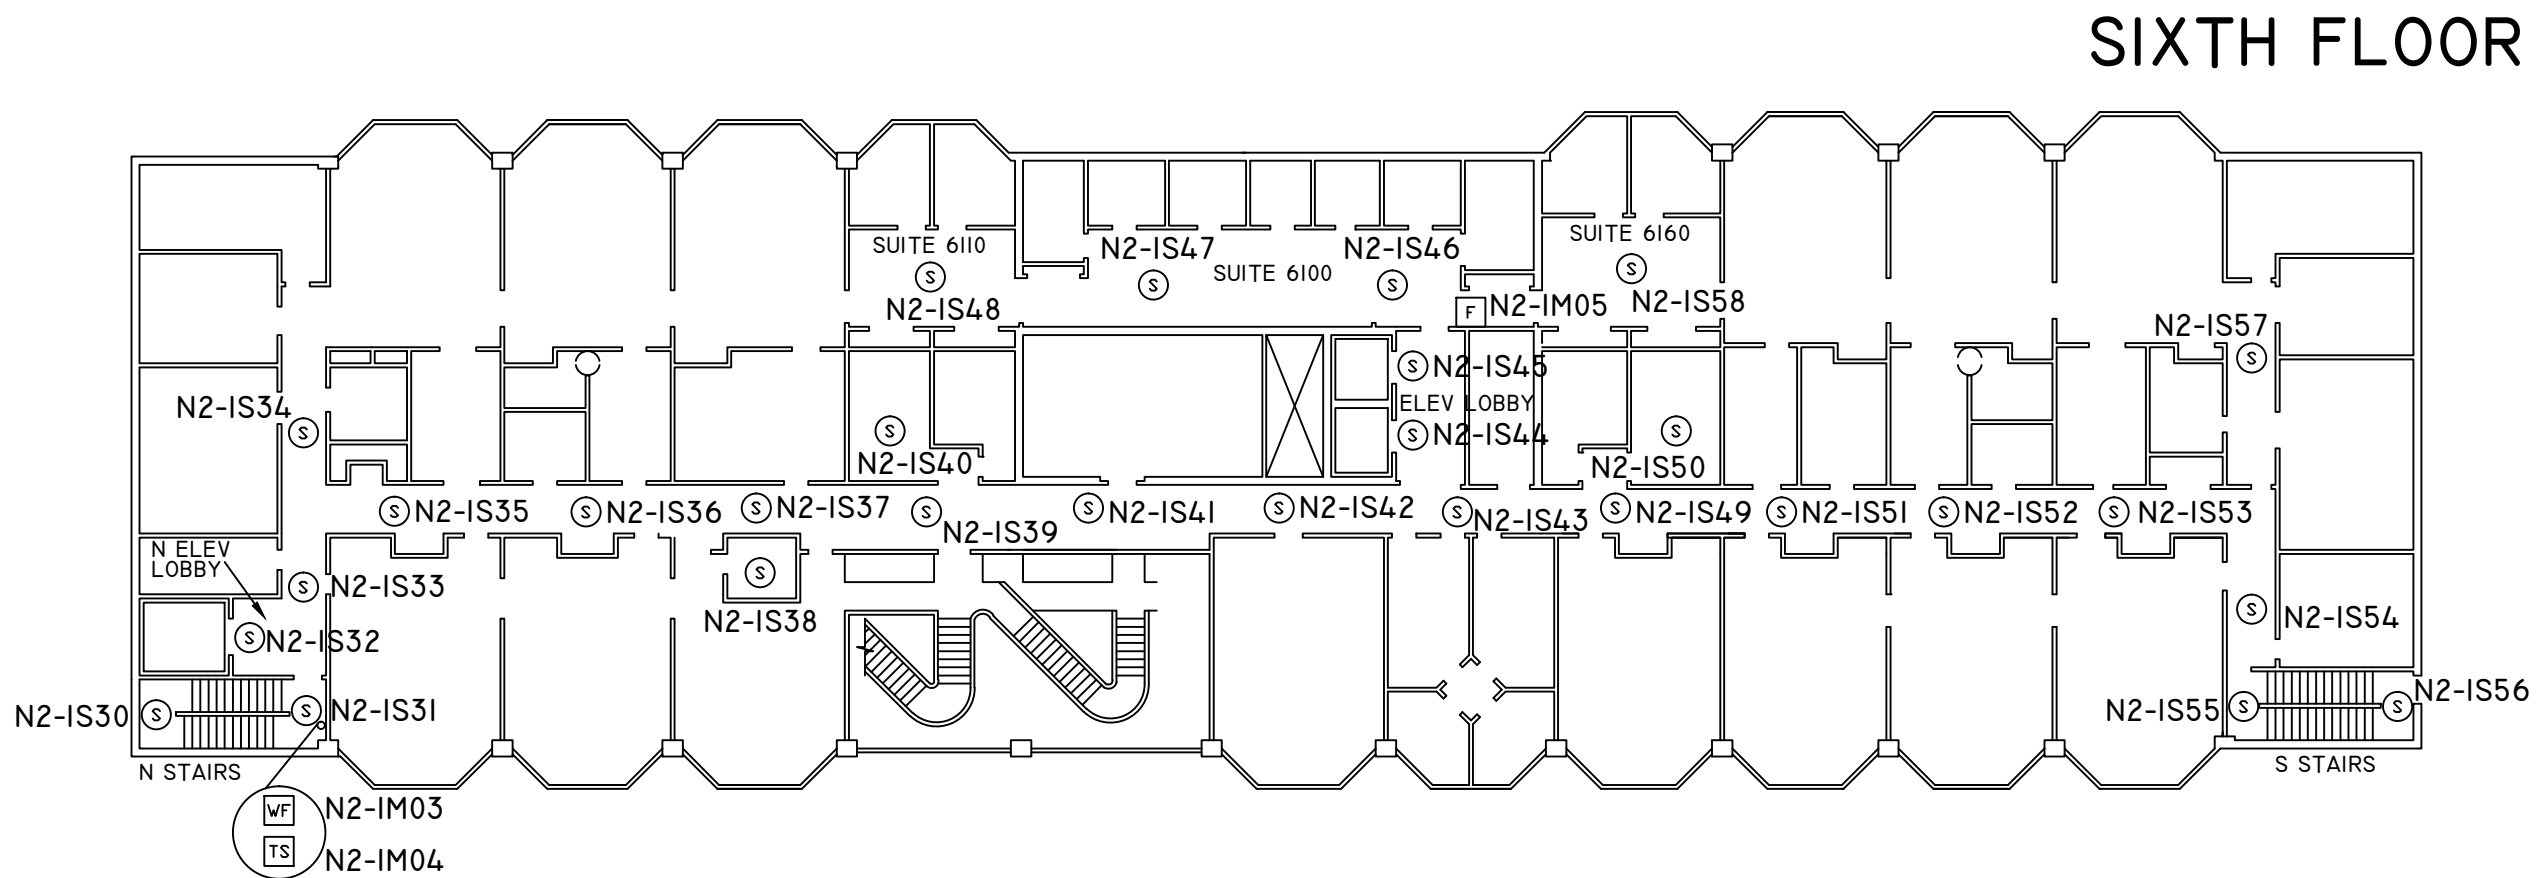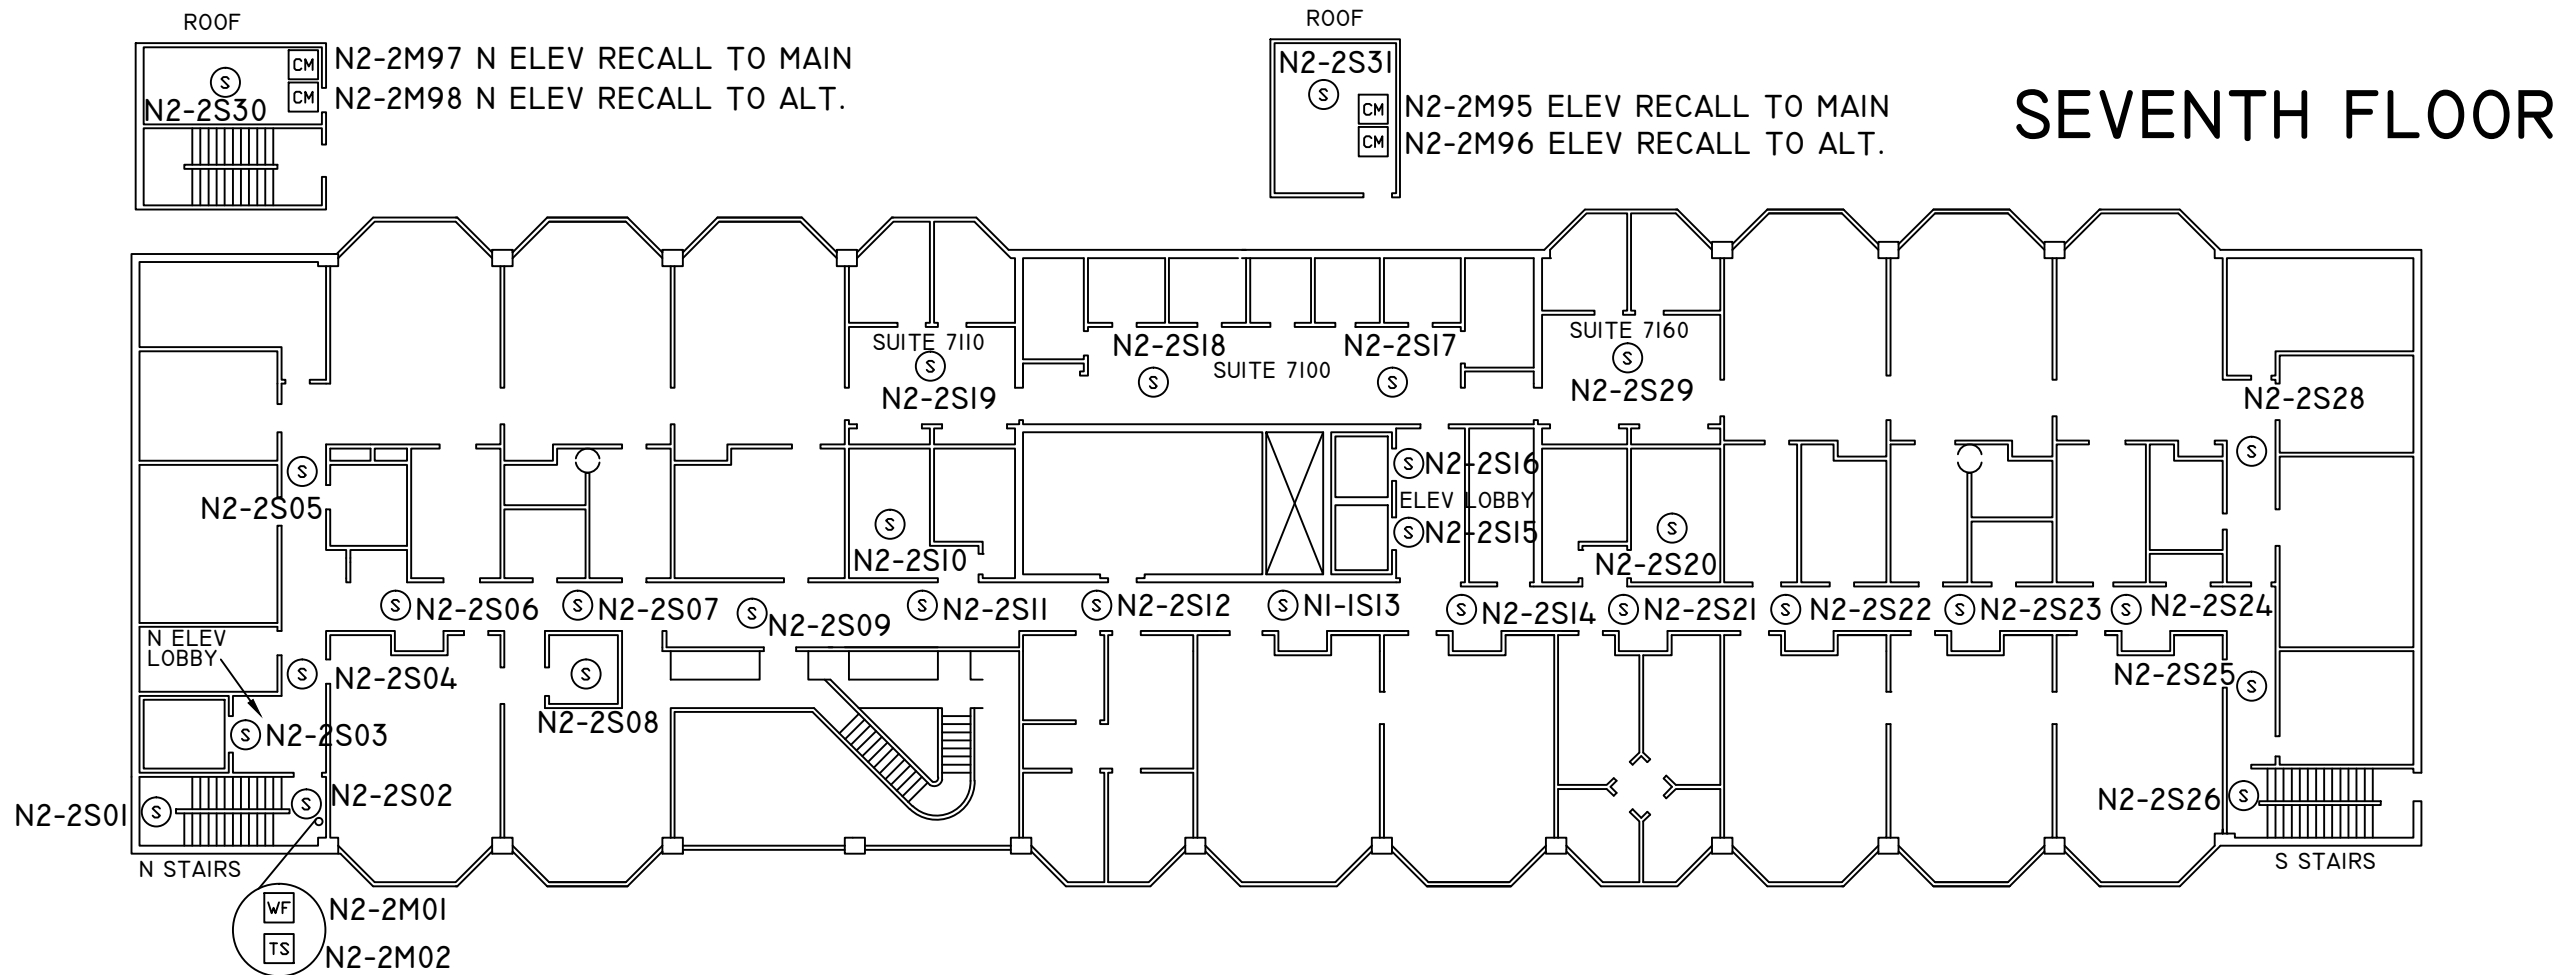

NOTE:
NFS DRAWINGS ARE BASED ON THE PROJECT
ARCHITECT/ENGINEER (A/E) PLANS AND SPECIFICATIONS
FURNISHED TO NFS. A/E IS SOLELY RESPONSIBLE
(NOT NFS) FOR THE TYPE, SIZE, LOCATION, AND
SUITABILITY OF ALL FIRE ALARMS, CONTROL PANELS,
AND OTHER DEVICES SHOWN ON THE A/E PLANS.
NFS DRAWINGS ARE TO SHOW ONLY THE WIRING
DIAGRAMS BETWEEN FIRE ALARM DEVICES AND
CONTROL PANELS. NFS IS NOT RESPONSIBLE FOR
THE INFORMATION SHOWN ON THE A/E PLANS.

UNIVERSITY OF UTAH
GENETICS BUILDING
SALT LAKE CITY, UTAH
FIRE ALARM SYSTEM

NFS

NELSON FIRE SYSTEMS
801-468-8300

DRAWN BY: ZM
DESIGNED BY: XXXX
APPROVED BY: BN
DATE: 10/18/05
SCALE: N.T.S.
PROJECT NO: XXXX
REV NO: XXXX
DRAWING NAME:
GENETICS4&5.DWG

FIRE ALARM SYSTEM
DEVICE NUMBERS

PAGE:

FA-4