
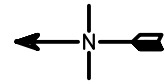


DEVICE LEGEND	
SYMBOL	DESCRIPTION
Ⓢ	SMOKE DETECTOR
Ⓣ	HEAT DETECTOR
DD	DUCT SMOKE DETECTOR
CM	CONTROL MODULE
MM	MONITOR MODULE
R	RELAY
HS	HORN/STROBE
HS _{WP}	WEATHERPROOF HORN/STROBE
L	STROBE
WF	WATERFLOW SWITCH
TS	TAMPER SWITCH
FACP	FIRE ALARM CONTROL PANEL
TRAN	TRANSPONDER PANEL

FOURTH LEVEL

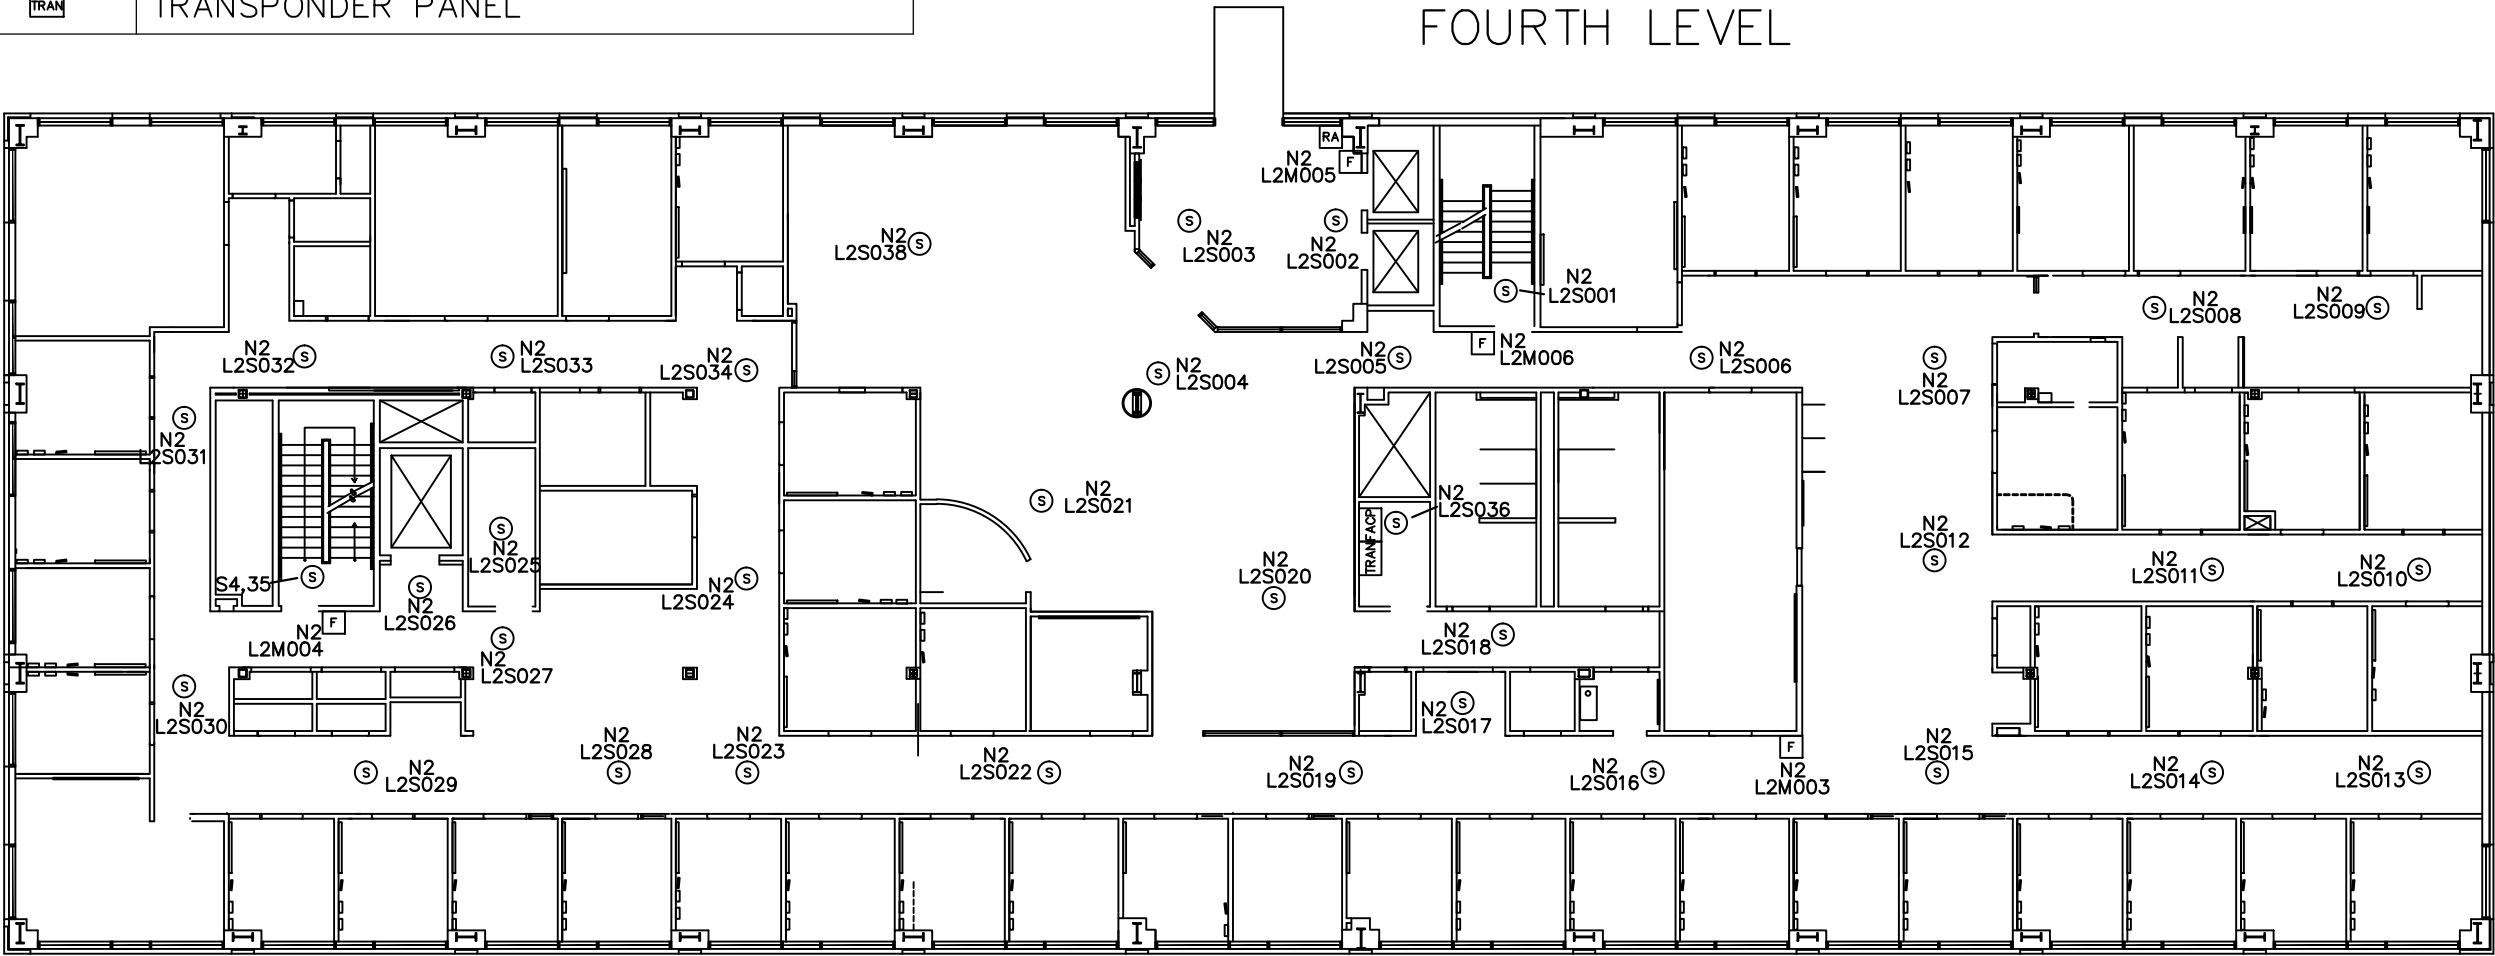


NOTE:
NFS DRAWINGS ARE BASED ON THE PROJECT
ARCHITECT/ENGINEER (A/E) PLANS AND SPECIFICATIONS
FURNISHED TO NFS. A/E IS SOLELY RESPONSIBLE
(NOT NFS) FOR THE TYPE, SIZE, LOCATION, AND
SUITABILITY OF ALL FIRE ALARMS, CONTROL PANELS,
AND OTHER DEVICES SHOWN ON THE A/E PLANS.
NFS DRAWINGS ARE TO SHOW ONLY THE WIRING
DIAGRAMS BETWEEN FIRE ALARM DEVICES AND
CONTROL PANELS. NFS IS NOT RESPONSIBLE FOR
THE INFORMATION SHOWN ON THE A/E PLANS.

U OF U BUILDING 550
CLINICAL NEUROSCIENCE CENTER
LEVEL 4
FIRE ALARM SYSTEM

NFS
NELSON FIRE SYSTEMS
801-468-8300



DRAWN BY:	DS
DESIGNED BY:	XXXX
APPROVED BY:	DS
DATE:	5/27/08
SCALE:	N.T.S.
PROJECT NO:	XXXX
REV NO:	XXXX
DRAWING NAME:	BLDG550LEVEL4.DWG

FIRE ALARM SYSTEM
ADDRESSABLE NUMBERS

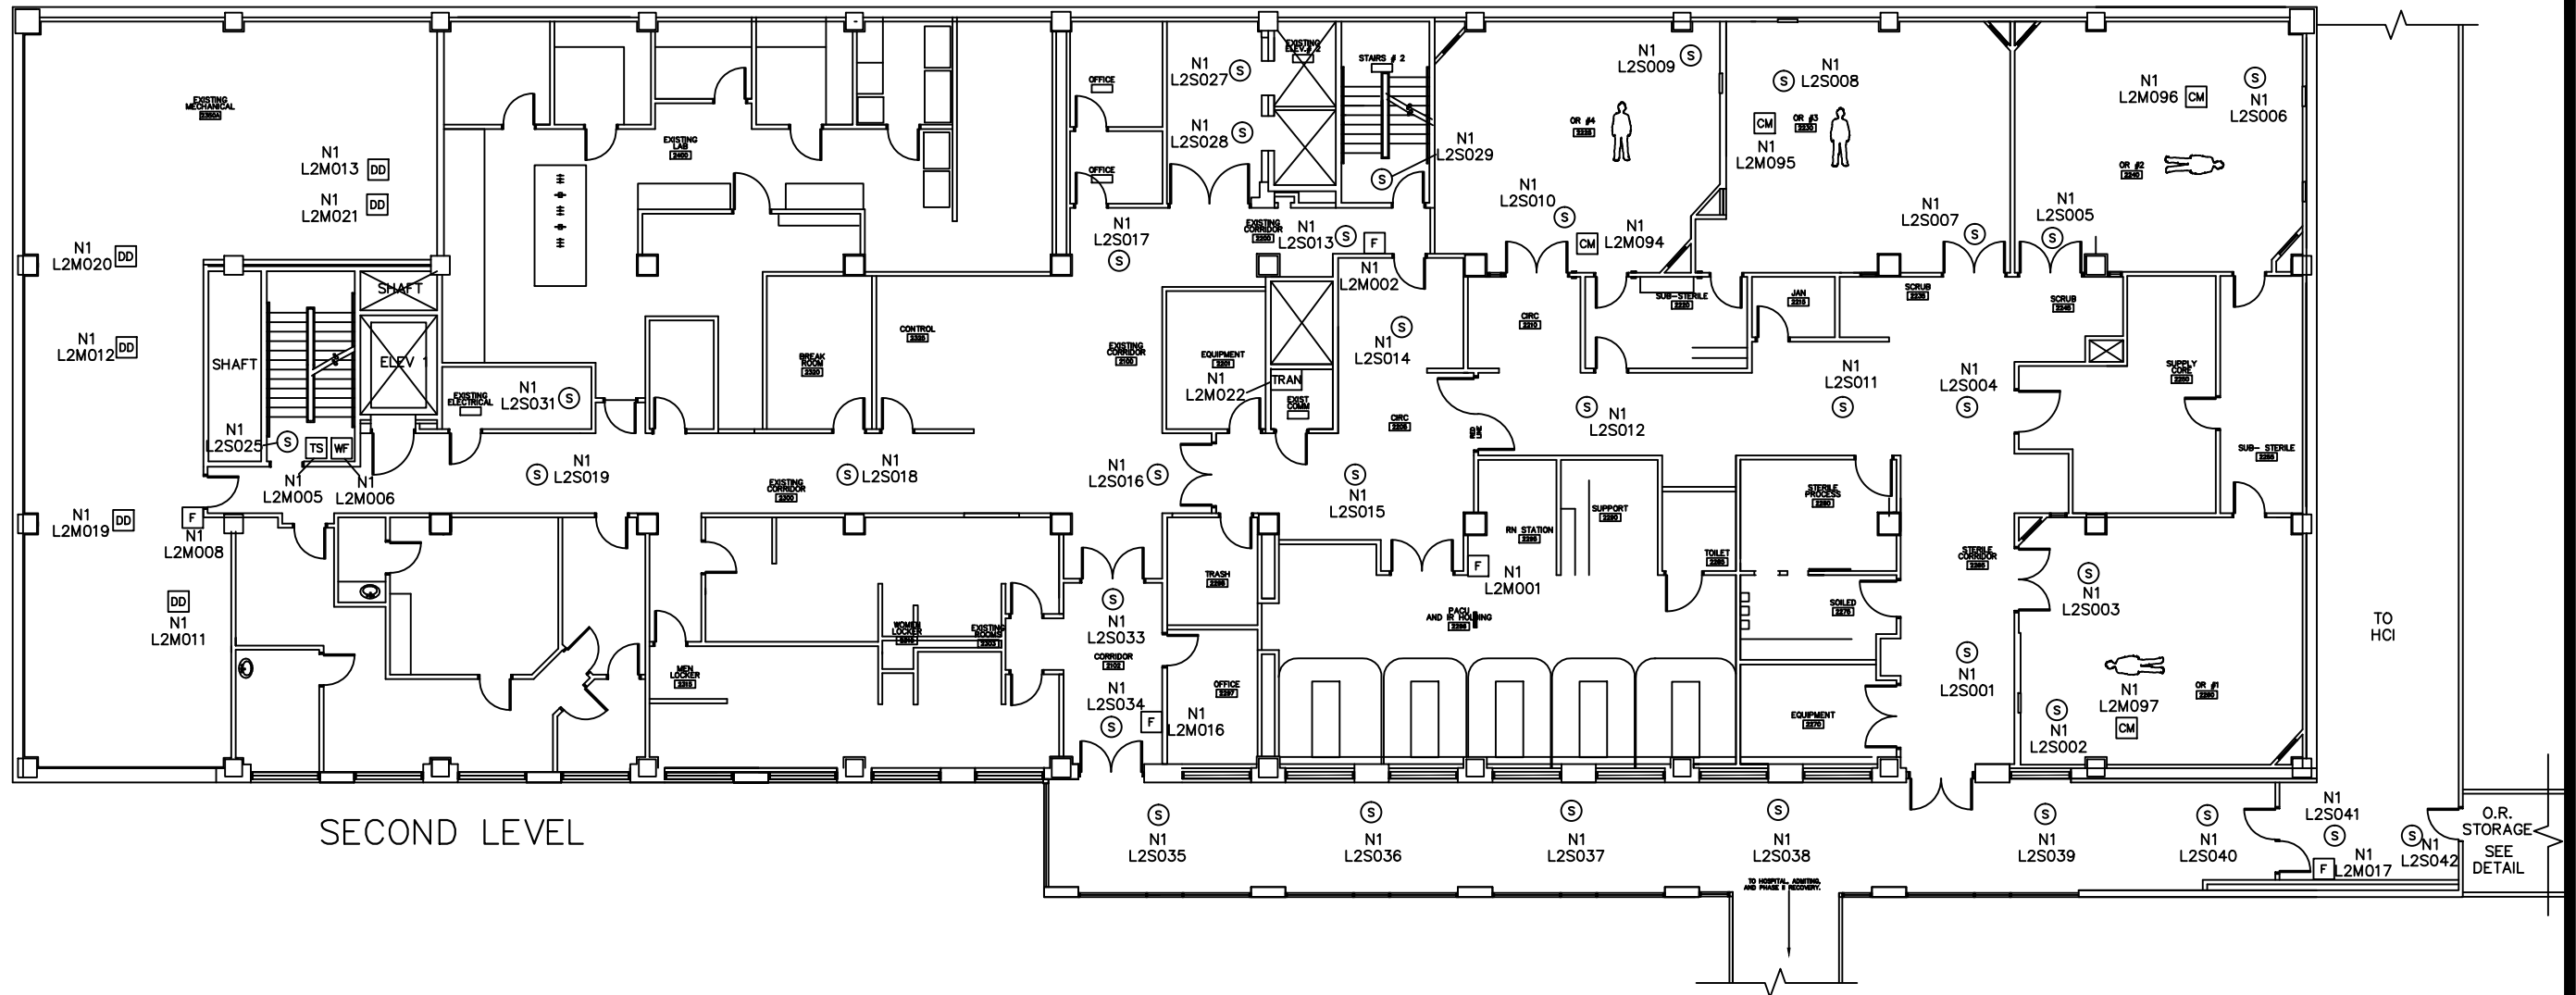

SECOND LEVEL

DEVICE LEGEND	
SYMBOL	DESCRIPTION
⊙	SMOKE DETECTOR
⊙	HEAT DETECTOR
⊙	DUCT SMOKE DETECTOR
CM	CONTROL MODULE
MM	MONITOR MODULE
R	RELAY
HS	HORN/STROBE
HS WP	WEATHERPROOF HORN/STROBE
L	STROBE
WF	WATERFLOW SWITCH
TS	TAMPER SWITCH
FACP	FIRE ALARM CONTROL PANEL
TRAN	TRANSPONDER PANEL

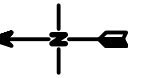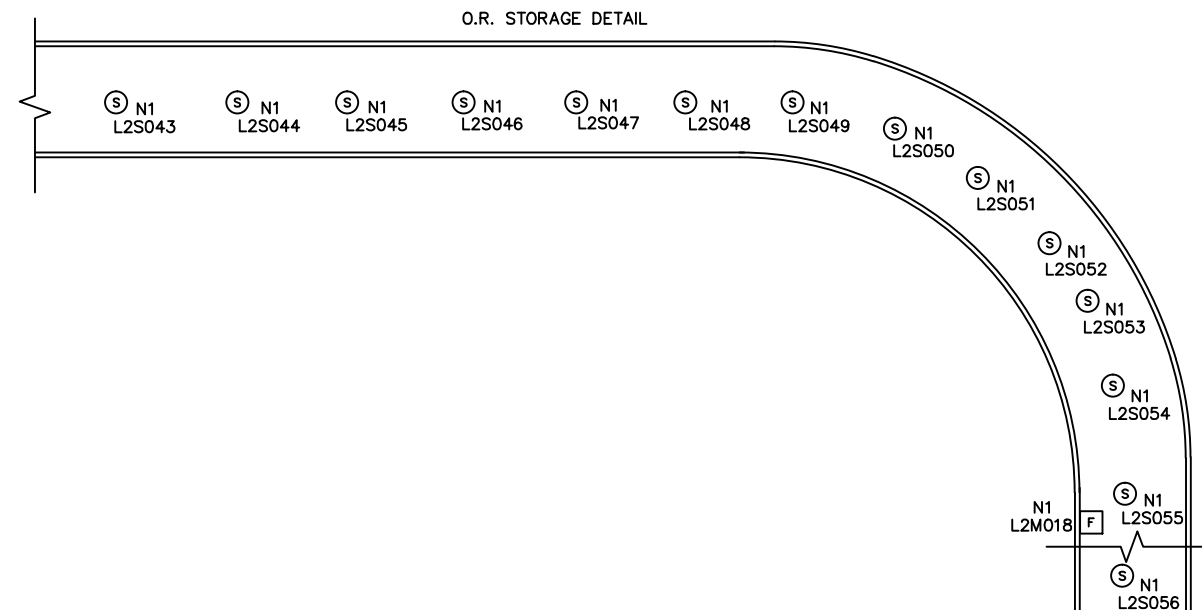

NOTE:
NFS DRAWINGS ARE BASED ON THE PROJECT
ARCHITECT/ENGINEER (A/E) PLANS AND SPECIFICATIONS
FURNISHED TO NFS. A/E IS SOLELY RESPONSIBLE
(NOT NFS) FOR THE TYPE, SIZE, LOCATION, AND
SUITABILITY OF ALL FIRE ALARMS, CONTROL PANELS,
AND OTHER DEVICES SHOWN ON THE A/E PLANS.
NFS DRAWINGS ARE TO SHOW ONLY THE WIRING
DIAGRAMS BETWEEN FIRE ALARM DEVICES AND
CONTROL PANELS. NFS IS NOT RESPONSIBLE FOR
THE INFORMATION SHOWN ON THE A/E PLANS.


U OF U BUILDING 550
CLINICAL NEUROSCIENCE CENTER
LEVEL 2
FIRE ALARM SYSTEM

NFS
NELSON FIRE SYSTEMS
801-468-8300

DRAWN BY: DS
DESIGNED BY: XXXX
APPROVED BY: DS
DATE: 1/16/2009
SCALE: N.T.S.
PROJECT NO: XXXX
REV NO: XXXX
DRAWING NAME:
BLDG550LEVEL2.DWG


FIRE ALARM SYSTEM

DEVICE LEGEND	
SYMBOL	DESCRIPTION
Ⓢ	SMOKE DETECTOR
Ⓜ	HEAT DETECTOR
Ⓛ	DUCT SMOKE DETECTOR
Ⓜ	CONTROL MODULE
Ⓜ	MONITOR MODULE
Ⓜ	RELAY
Ⓜ	HORN/STROBE
Ⓜ	WEATHERPROOF HORN/STROBE
Ⓜ	STROBE
Ⓜ	WATERFLOW SWITCH
Ⓜ	TAMPER SWITCH
Ⓜ	FIRE ALARM CONTROL PANEL
Ⓜ	TRANSPONDER PANEL

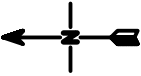

NOTE:
NFS DRAWINGS ARE BASED ON THE PROJECT
ARCHITECT/ENGINEER (A/E) PLANS AND SPECIFICATIONS
FURNISHED TO NFS. A/E IS SOLELY RESPONSIBLE
(NOT NFS) FOR THE TYPE, SIZE, LOCATION, AND
SUITABILITY OF ALL FIRE ALARMS, CONTROL PANELS,
AND OTHER DEVICES SHOWN ON THE A/E PLANS.
NFS DRAWINGS ARE TO SHOW ONLY THE WIRING
DIAGRAMS BETWEEN FIRE ALARM DEVICES AND
CONTROL PANELS. NFS IS NOT RESPONSIBLE FOR
THE INFORMATION SHOWN ON THE A/E PLANS.

THIRD LEVEL

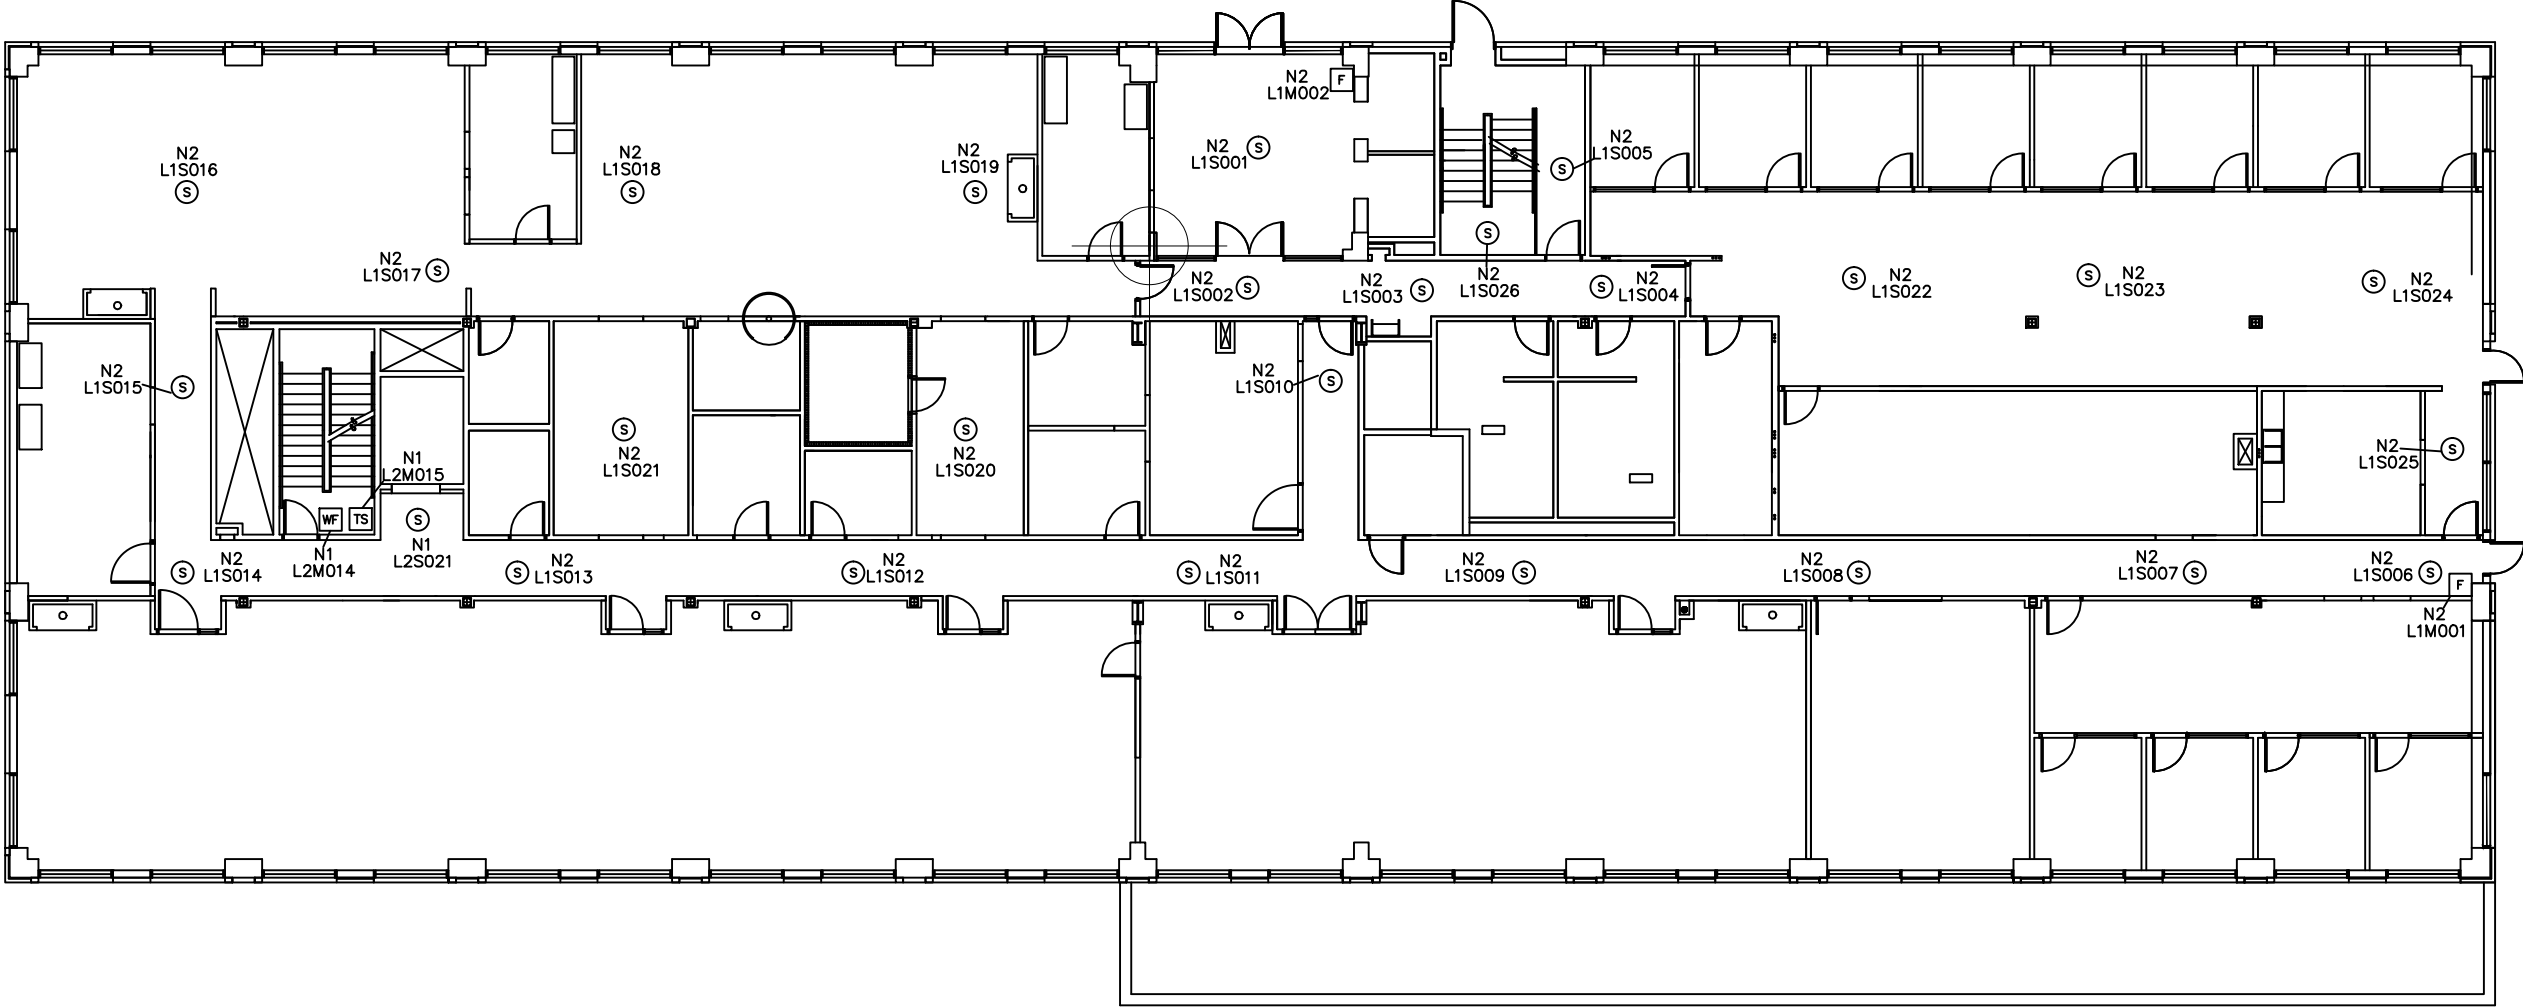

U OF U BUILDING 550
CLINICAL NEUROSCIENCE CENTER
LEVEL 3
FIRE ALARM SYSTEM

NFS
NELSON FIRE SYSTEMS
801-468-8300

DRAWN BY:	DS
DESIGNED BY:	XXXX
APPROVED BY:	XXXX
DATE:	2/10/2009
SCALE:	N.T.S.
PROJECT NO:	XXXX
REV NO:	XXXX
DRAWING NAME:	BLDG550LEVEL3.DWG

FIRE ALARM SYSTEM

PAGE