


DEVICE LEGEND	
SYMBOL	DESCRIPTION
	SMOKE DETECTOR
	HEAT DETECTOR
	MANUAL PULL STATION
	DUCT DETECTOR
	TAMPER SWITCH
	WATERFLOW SWITCH
	MONITOR MODULE
	CONTROL MODULE
	LOCAL OPERATING CONSOLE
	TRANSPONDER PANEL
	FIRE ALARM CONTROL UNIT

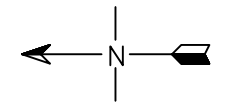

NOTE:
NFS DRAWINGS ARE BASED ON THE PROJECT ARCHITECT/ENGINEER (A/E) PLANS AND SPECIFICATIONS FURNISHED TO NFS. A/E IS SOLELY RESPONSIBLE (NOT NFS) FOR THE TYPE, SIZE, LOCATION, AND SUITABILITY OF ALL FIRE ALARMS, CONTROL PANELS, AND OTHER DEVICES SHOWN ON THE A/E PLANS. NFS DRAWINGS ARE TO SHOW ONLY THE WIRING DIAGRAMS BETWEEN FIRE ALARM DEVICES AND CONTROL PANELS. NFS IS NOT RESPONSIBLE FOR THE INFORMATION SHOWN ON THE A/E PLANS.

UNIVERSITY OF UTAH
HUNTSMAN CANCER INSTITUTE
PHASE IV - PRIMARY CHILDRENS & FAMILIES
2000 CIRCLE OF HOPE DR.
SALT LAKE CITY, UTAH 84112
FIRE ALARM SYSTEM

NFS


NELSON FIRE SYSTEMS
801-468-8300

DRAWN BY: AK
DESIGNED BY: XXXX
APPROVED BY: DPS
DATE: 5/31/17
SCALE: N.T.S.
PROJECT NO: XXXX
REV NO: XXXX
DRAWING NAME:
HUNTSMAN INSTITUTE B FM.DWG

FIRE ALARM SYSTEM


FINAL MAP

PAGE:
BASEMENT

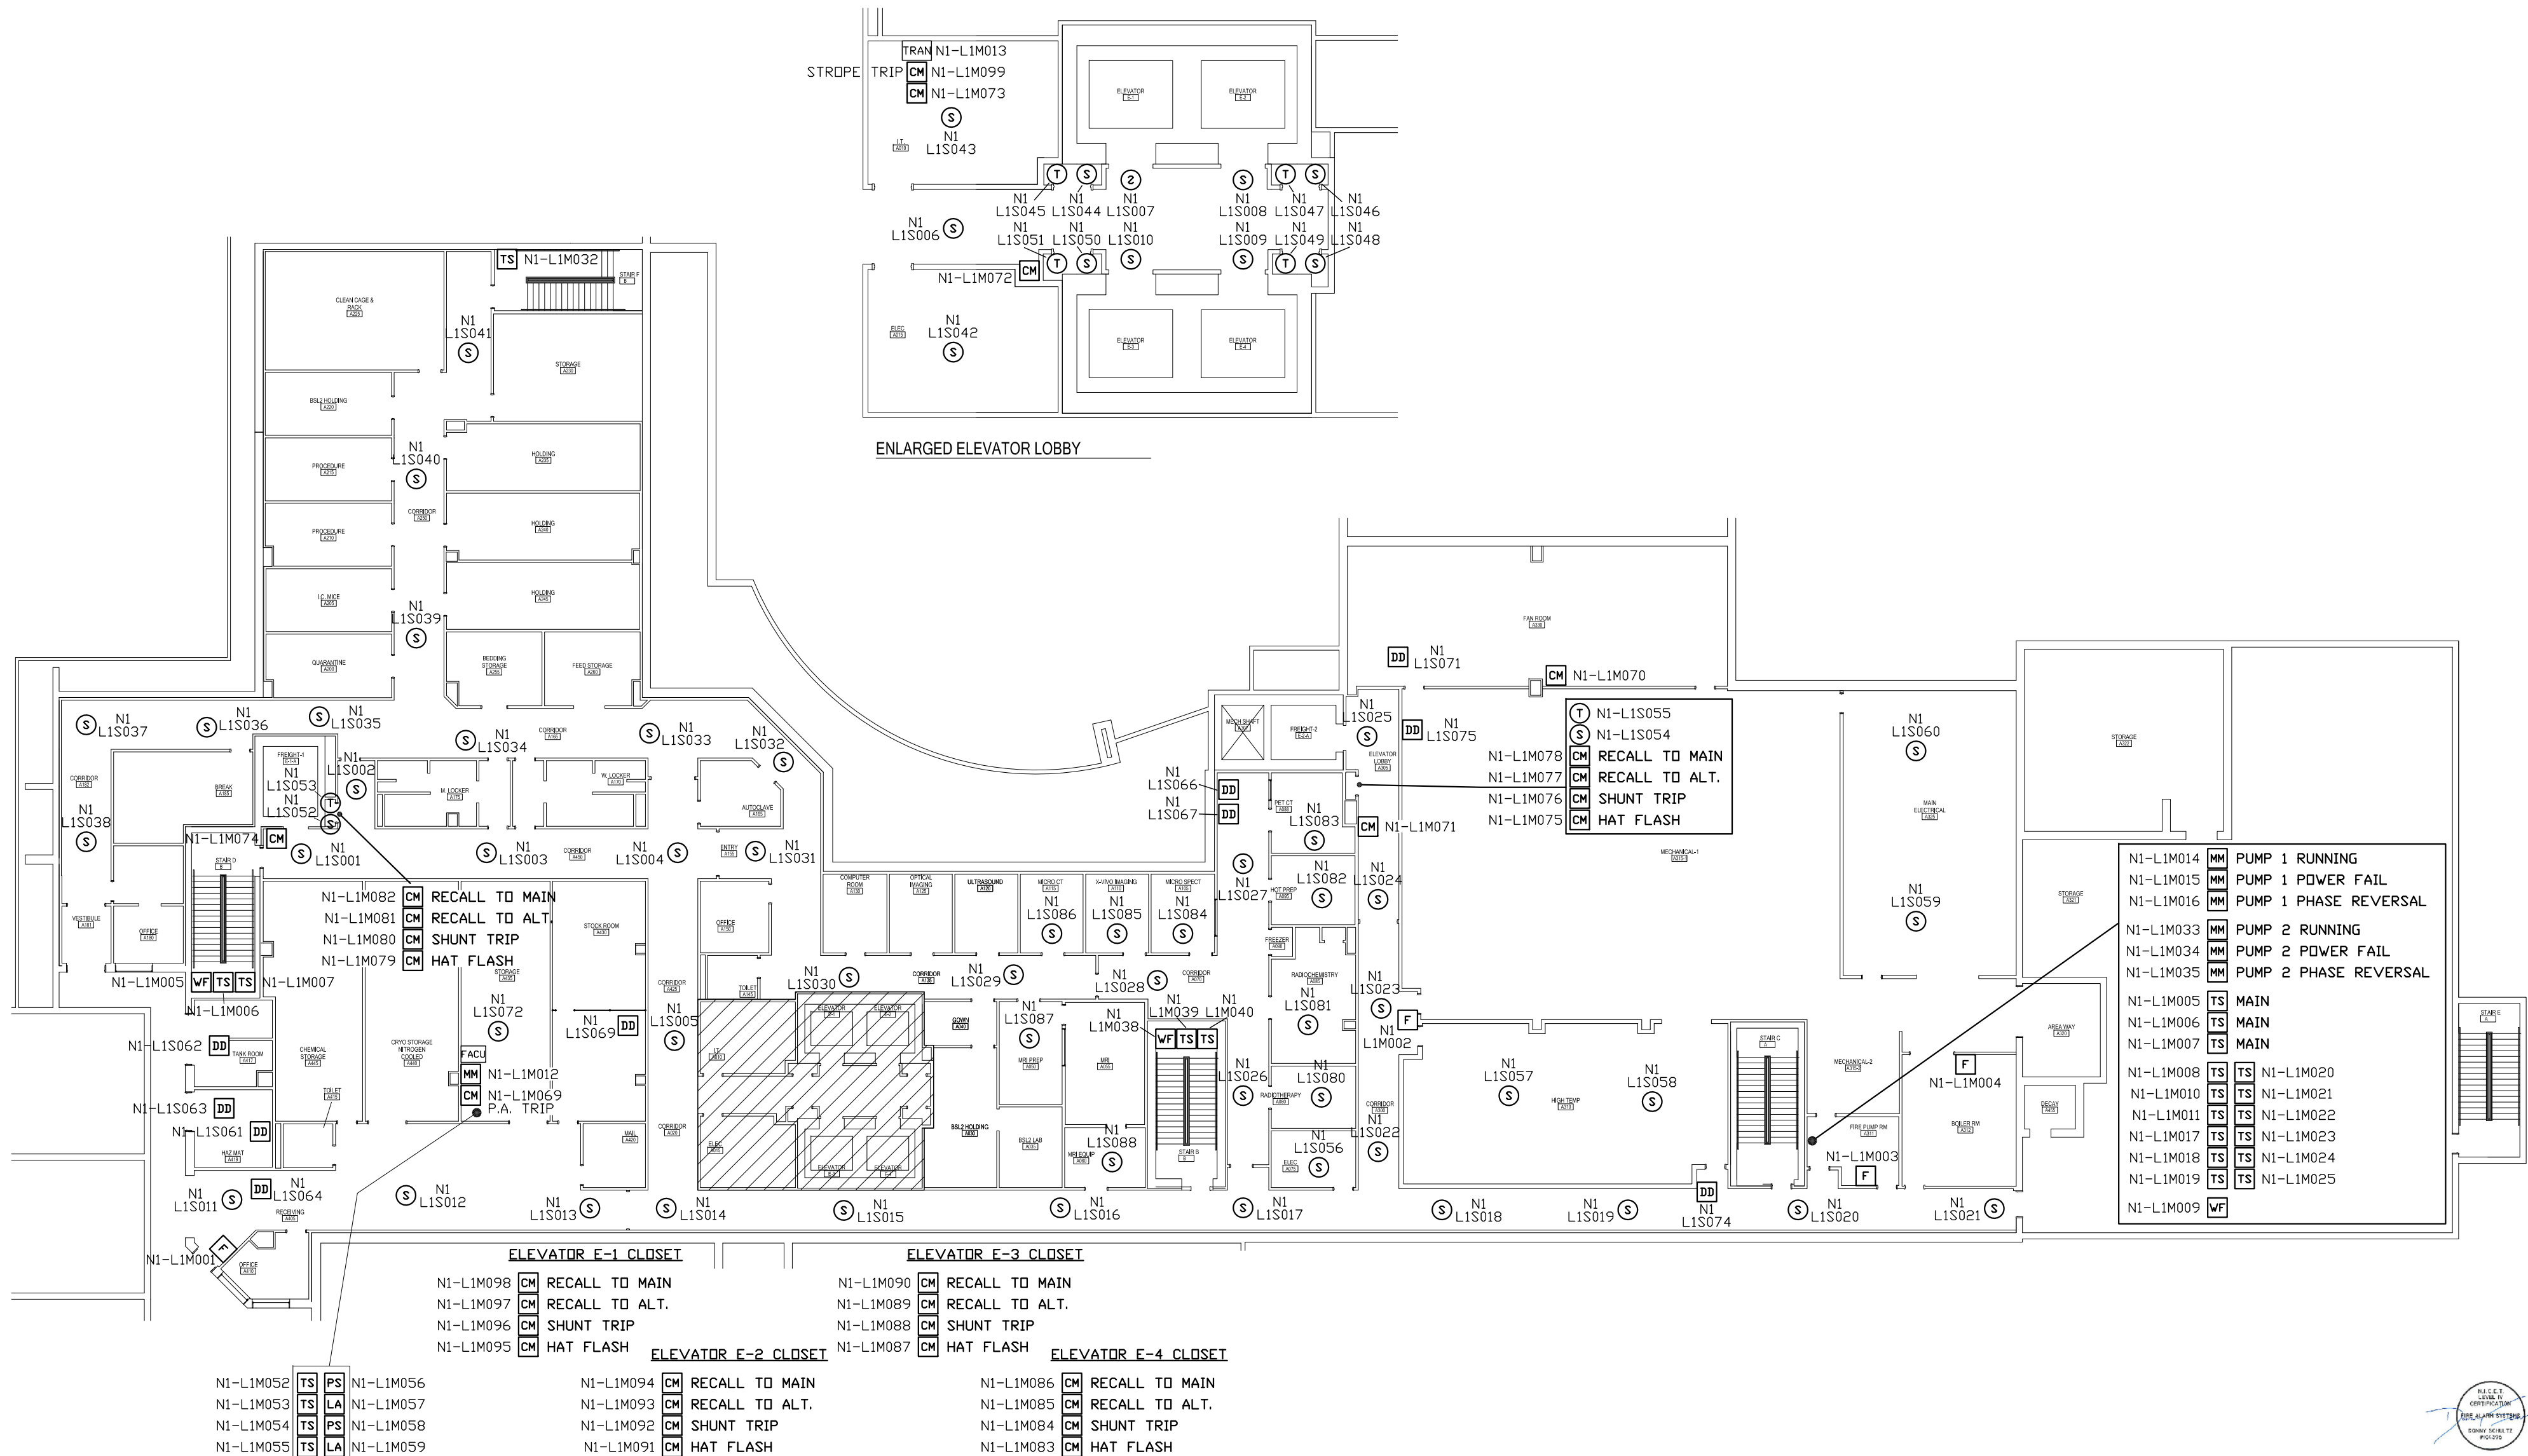



DEVICE LEGEND	
SYMBOL	DESCRIPTION
(S)	SMOKE DETECTOR
(H)	HEAT DETECTOR
(F)	MANUAL PULL STATION
(DD)	DUCT DETECTOR
(TS)	TAMPER SWITCH
(WF)	WATERFLOW SWITCH
(MM)	MONITOR MODULE
(CM)	CONTROL MODULE
(LOC)	LOCAL OPERATING CONSOLE
(TRAN)	TRANSPONDER PANEL
(FACU)	FIRE ALARM CONTROL UNIT

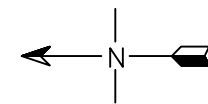

NOTE:
NFS DRAWINGS ARE BASED ON THE PROJECT
ARCHITECT/ENGINEER (A/E) PLANS AND SPECIFICATIONS
FURNISHED TO NFS. A/E IS SOLELY RESPONSIBLE
(NOT NFS) FOR THE TYPE, SIZE, LOCATION, AND
SUITABILITY OF ALL FIRE ALARMS, CONTROL PANELS,
AND OTHER DEVICES SHOWN ON THE A/E PLANS.
NFS DRAWINGS ARE TO SHOW ONLY THE WIRING
DIAGRAMS BETWEEN FIRE ALARM DEVICES AND
CONTROL PANELS. NFS IS NOT RESPONSIBLE FOR
THE INFORMATION SHOWN ON THE A/E PLANS.

UNIVERSITY OF UTAH
HUNTSMAN CANCER INSTITUTE
PHASE IV - PRIMARY CHILDRENS & FAMILIES
2000 CIRCLE OF HOPE DR.
SALT LAKE CITY, UTAH 84112
FIRE ALARM SYSTEM

NFS
NELSON FIRE SYSTEMS
801-468-8300

DRAWN BY:	AK
DESIGNED BY:	XXXX
APPROVED BY:	DPS
DATE:	5/31/17
SCALE:	N.T.S.
PROJECT NO:	XXXX
REV NO:	XXXX
DRAWING NAME:	HUNTSMAN INSTITUTE 2 FM.DWG


FIRE ALARM SYSTEM
FINAL MAP

PAGE:
LEVEL 2





DEVICE LEGEND	
SYMBOL	DESCRIPTION
(S)	SMOKE DETECTOR
(H)	HEAT DETECTOR
(F)	MANUAL PULL STATION
(DD)	DUCT DETECTOR
(TS)	TAMPER SWITCH
(WF)	WATERFLOW SWITCH
(MM)	MONITOR MODULE
(CM)	CONTROL MODULE
(LOC)	LOCAL OPERATING CONSOLE
(TRAN)	TRANSPONDER PANEL
(FACU)	FIRE ALARM CONTROL UNIT

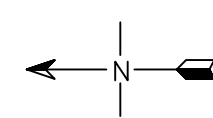

NOTE:
NFS DRAWINGS ARE BASED ON THE PROJECT
ARCHITECT/ENGINEER (A/E) PLANS AND SPECIFICATIONS
FURNISHED TO NFS. A/E IS SOLELY RESPONSIBLE
(NOT NFS) FOR THE TYPE, SIZE, LOCATION, AND
SUITABILITY OF ALL FIRE ALARMS, CONTROL PANELS,
AND OTHER DEVICES SHOWN ON THE A/E PLANS.
NFS DRAWINGS ARE TO SHOW ONLY THE WIRING
DIAGRAMS BETWEEN FIRE ALARM DEVICES AND
CONTROL PANELS. NFS IS NOT RESPONSIBLE FOR
THE INFORMATION SHOWN ON THE A/E PLANS.

UNIVERSITY OF UTAH
HUNTSMAN CANCER INSTITUTE
PHASE IV - PRIMARY CHILDRENS & FAMILIES
2000 CIRCLE OF HOPE DR.
SALT LAKE CITY, UTAH 84112
FIRE ALARM SYSTEM

NFS

NELSON FIRE SYSTEMS
801-468-8300

DRAWN BY: AK
DESIGNED BY: XXXX
APPROVED BY: DPS
DATE: 5/31/17
SCALE: N.T.S.
PROJECT NO: XXXX
REV NO: XXXX
DRAWING NAME:
HUNTSMAN INSTITUTE 3 FM.DWG



FIRE ALARM SYSTEM

FINAL MAP

PAGE:
LEVEL 3



DEVICE LEGEND	
SYMBOL	DESCRIPTION
Ⓢ	SMOKE DETECTOR
Ⓢ	HEAT DETECTOR
F	MANUAL PULL STATION
DD	DUCT DETECTOR
TS	TAMPER SWITCH
WF	WATERFLOW SWITCH
MM	MONITOR MODULE
CM	CONTROL MODULE
LDC	LOCAL OPERATING CONSOLE
TRAN	TRANSPONDER PANEL
FACU	FIRE ALARM CONTROL UNIT

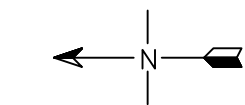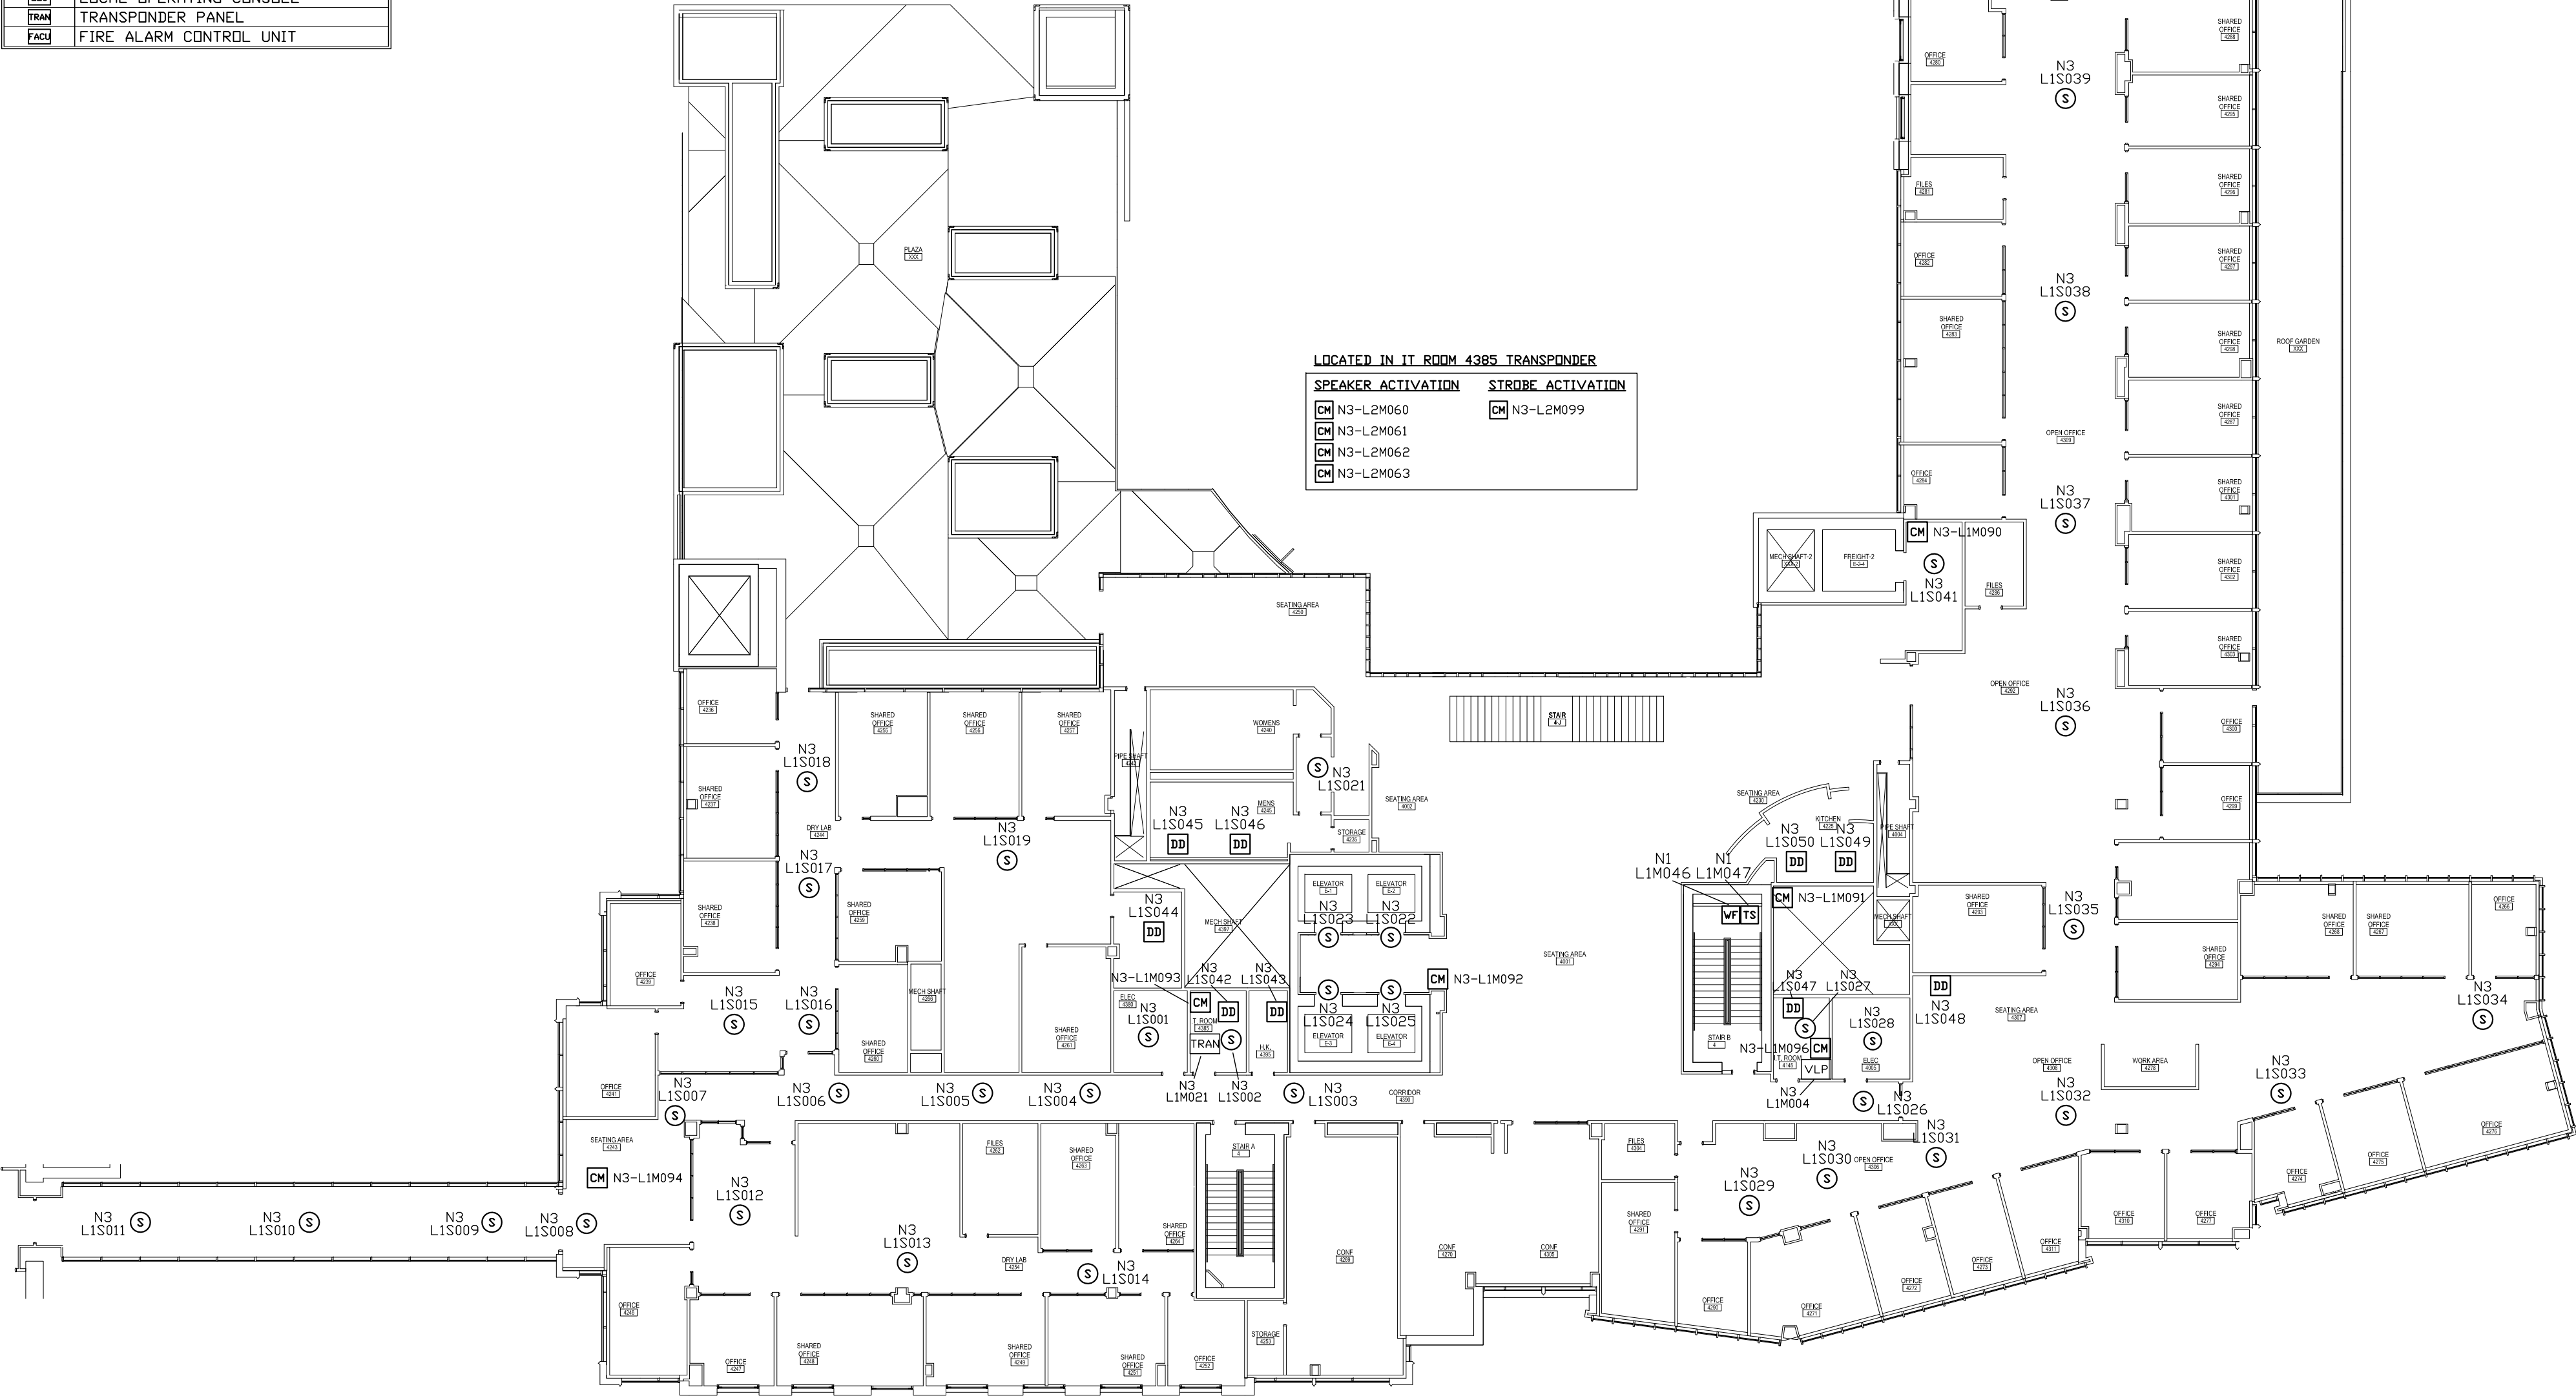

NOTE:
NFS DRAWINGS ARE BASED ON THE PROJECT
ARCHITECT/ENGINEER (A/E) PLANS AND SPECIFICATIONS
FURNISHED TO NFS. A/E IS SOLELY RESPONSIBLE
(NOT NFS) FOR THE TYPE, SIZE, LOCATION, AND
SUITABILITY OF ALL FIRE ALARMS, CONTROL PANELS,
AND OTHER DEVICES SHOWN ON THE A/E PLANS.
NFS DRAWINGS ARE TO SHOW ONLY THE WIRING
DIAGRAMS BETWEEN FIRE ALARM DEVICES AND
CONTROL PANELS. NFS IS NOT RESPONSIBLE FOR
THE INFORMATION SHOWN ON THE A/E PLANS.

UNIVERSITY OF UTAH
HUNTSMAN CANCER INSTITUTE
PHASE IV - PRIMARY CHILDRENS & FAMILIES
2000 CIRCLE OF HOPE DR.
SALT LAKE CITY, UTAH 84112
FIRE ALARM SYSTEM

NFS
NELSON FIRE SYSTEMS
801-468-8300

DRAWN BY: AK
DESIGNED BY: XXXX
APPROVED BY: DPS
DATE: 5/31/17
SCALE: N.T.S.
PROJECT NO: XXXX
REV NO: XXXX
DRAWING NAME:
HUNTSMAN INSTITUTE 4 FM.DWG

FIRE ALARM SYSTEM
FINAL MAPS

PAGE:
LEVEL 4



LOCATED IN IT ROOM 5300 TRANSPONDER

SPEAKER ACTIVATION	STROBE ACTIVATION
CM N3-L2M058	CM N3-L2M098
CM N3-L2M059	CM N3-L2M099
CM N3-L2M060	
CM N3-L2M061	
CM N3-L2M062	

DEVICE LEGEND	
SYMBOL	DESCRIPTION
(S)	SMOKE DETECTOR
(T)	HEAT DETECTOR
(F)	MANUAL PULL STATION
(DD)	DUCT DETECTOR
(TS)	TAMPER SWITCH
(W)	WATERFLOW SWITCH
(M)	MONITOR MODULE
(CM)	CONTROL MODULE
(LOC)	LOCAL OPERATING CONSOLE
(TRAN)	TRANSPONDER PANEL
(FACU)	FIRE ALARM CONTROL UNIT

NOTE:
NFS DRAWINGS ARE BASED ON THE PROJECT
ARCHITECT/ENGINEER (A/E) PLANS AND SPECIFICATIONS
FURNISHED TO NFS. A/E IS SOLELY RESPONSIBLE
(NOT NFS) FOR THE TYPE, SIZE, LOCATION, AND
SUITABILITY OF ALL FIRE ALARMS, CONTROL PANELS,
AND OTHER DEVICES SHOWN ON THE A/E PLANS.
NFS DRAWINGS ARE TO SHOW ONLY THE WIRING
DIAGRAMS BETWEEN FIRE ALARM DEVICES AND
CONTROL PANELS. NFS IS NOT RESPONSIBLE FOR
THE INFORMATION SHOWN ON THE A/E PLANS.

UNIVERSITY OF UTAH
HUNTSMAN CANCER INSTITUTE
PHASE IV - PRIMARY CHILDRENS & FAMILIES
2000 CIRCLE OF HOPE DR.
SALT LAKE CITY, UTAH 84112
FIRE ALARM SYSTEM

NFS

NELSON FIRE SYSTEMS
801-468-8300



DRAWN BY: AK
DESIGNED BY: XXXX
APPROVED BY: DPS
DATE: 5/31/17
SCALE: N.T.S.
PROJECT NO: XXXX
REV NO: XXXX
DRAWING NAME:
HUNTSMAN INSTITUTE 5 FM.DWG

FIRE ALARM SYSTEM
FINAL MAP

PAGE:
LEVEL 5



DEVICE LEGEND	
SYMBOL	DESCRIPTION
⑤	SMOKE DETECTOR
①	HEAT DETECTOR
F	MANUAL PULL STATION
DD	DUCT DETECTOR
TS	TAMPER SWITCH
WF	WATERFLOW SWITCH
MM	MONITOR MODULE
CM	CONTROL MODULE
LOC	LOCAL OPERATING CONSOLE
TRAN	TRANSPONDER PANEL
FACU	FIRE ALARM CONTROL UNIT

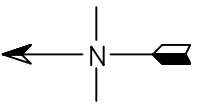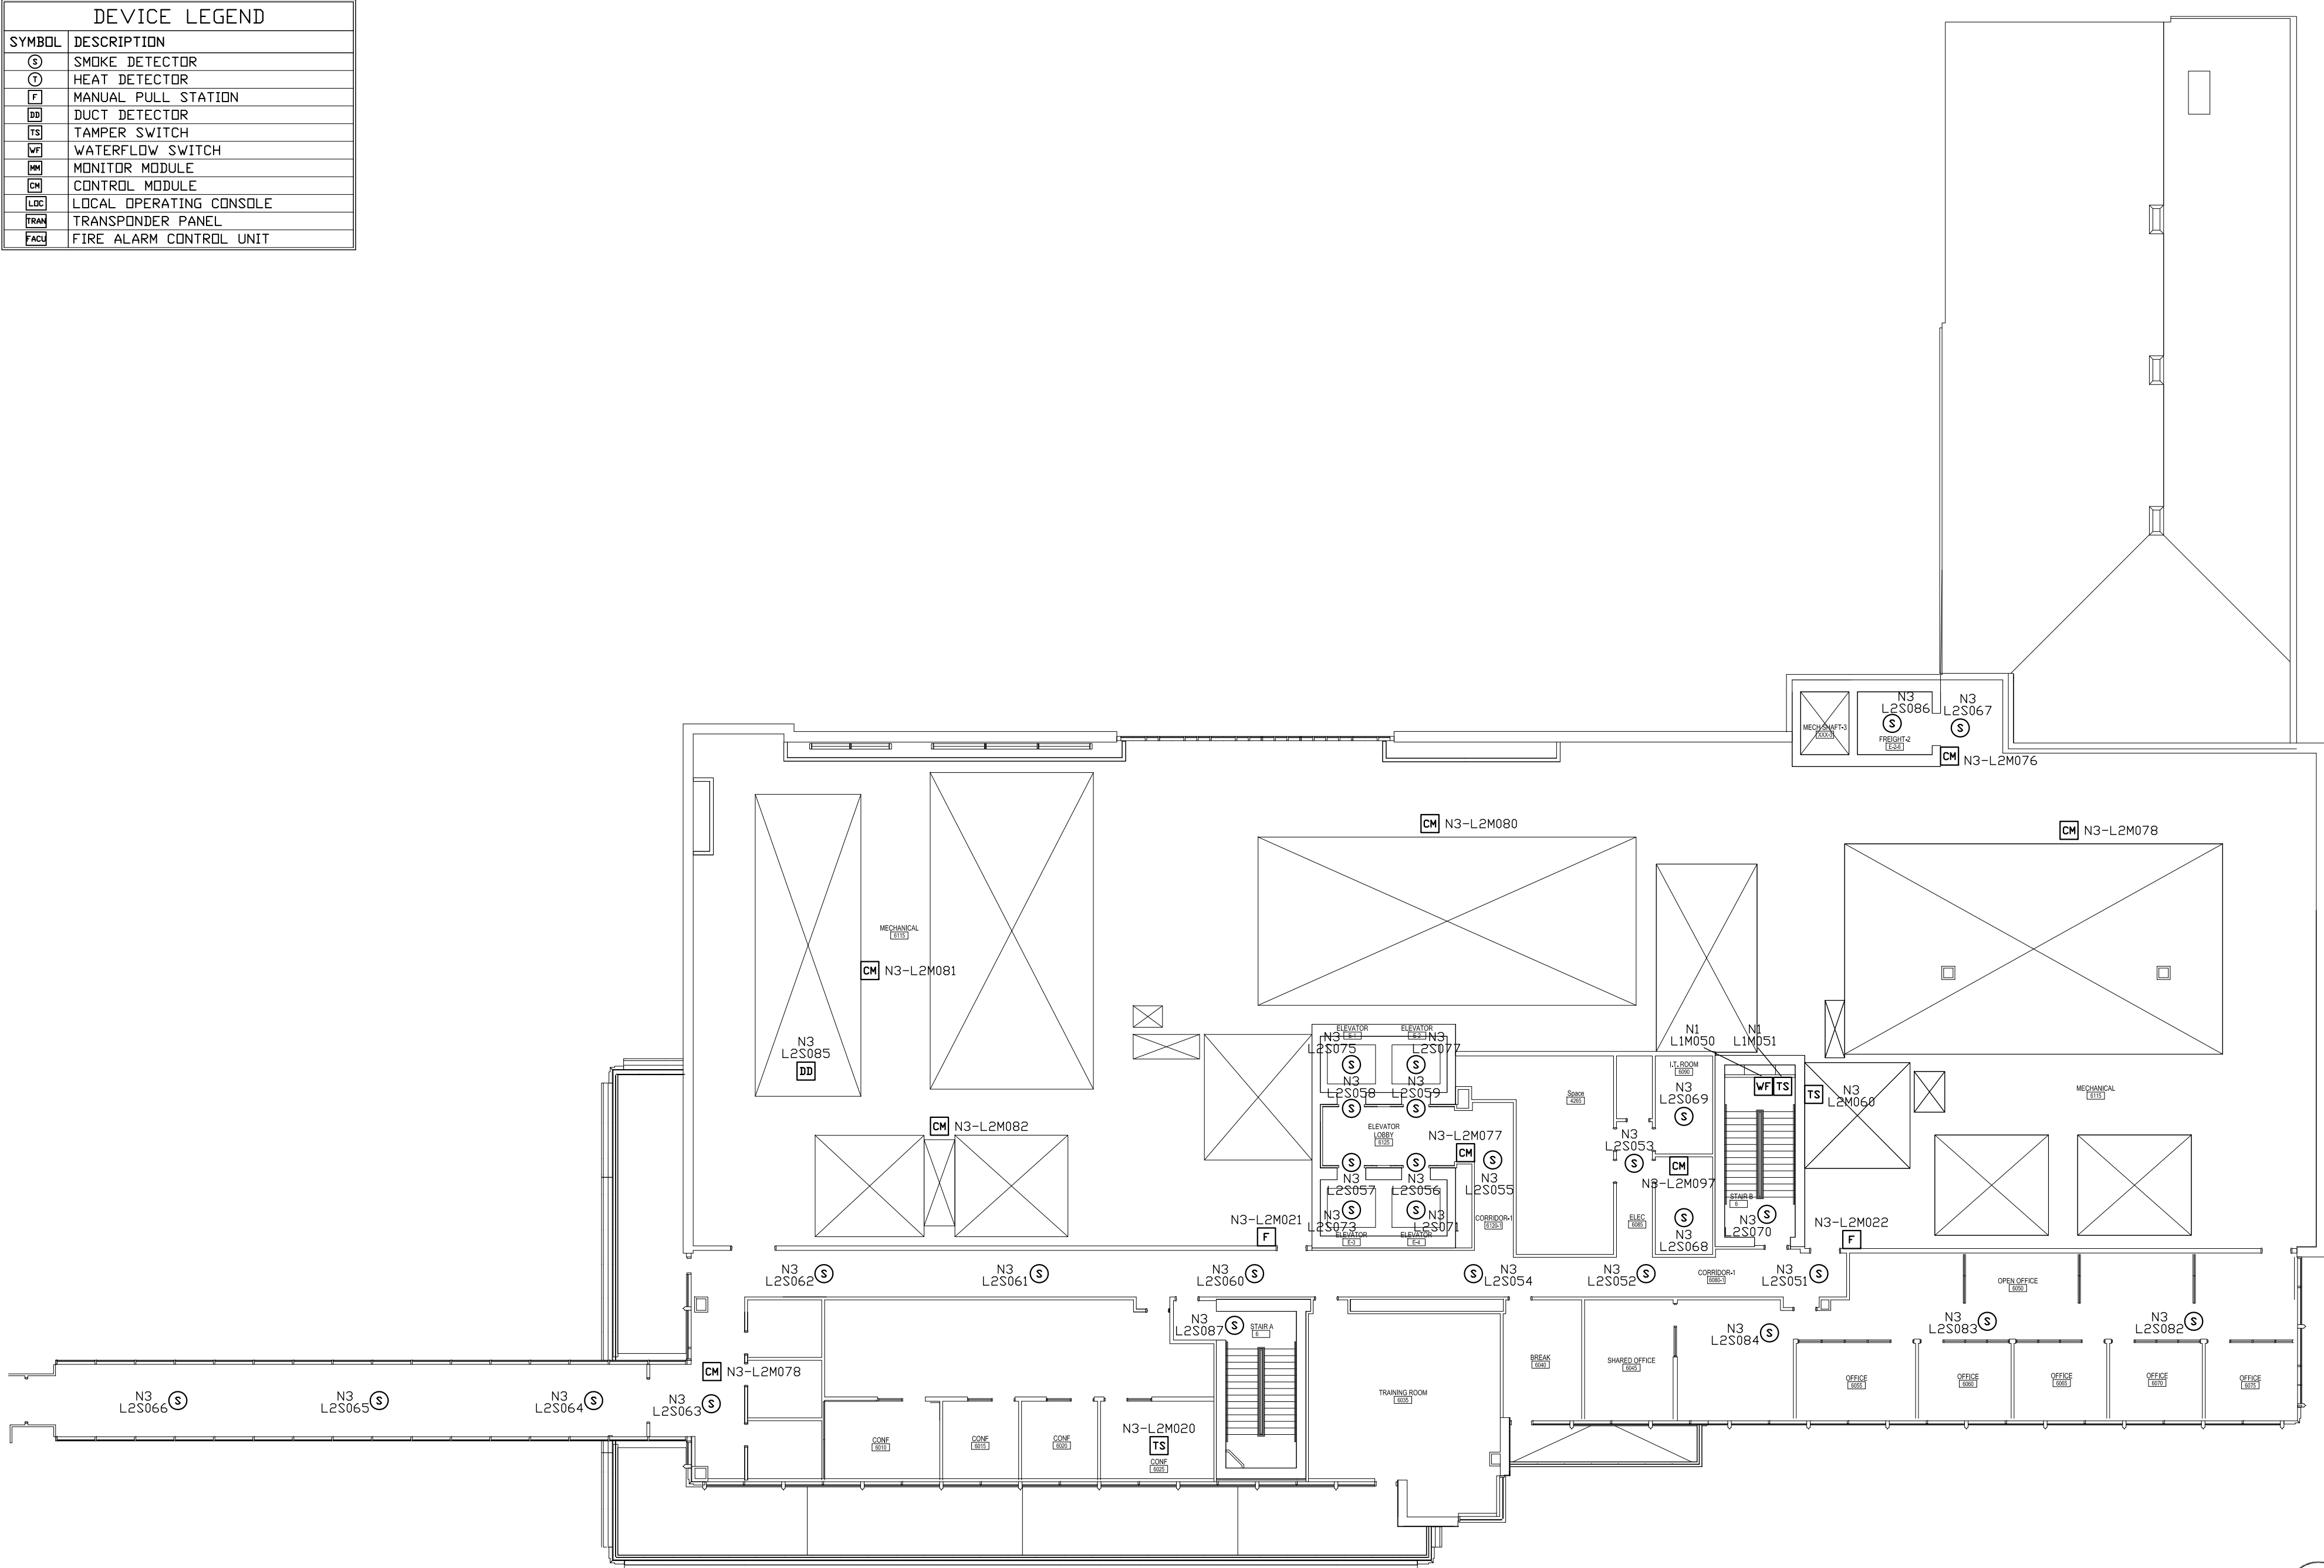

NOTE:
NFS DRAWINGS ARE BASED ON THE PROJECT ARCHITECT/ENGINEER (A/E) PLANS AND SPECIFICATIONS FURNISHED TO NFS. A/E IS SOLELY RESPONSIBLE FOR THE TYPE, SIZE, LOCATION, AND SUITABILITY OF ALL FIRE ALARMS, CONTROL PANELS, AND OTHER DEVICES ARE TO SHOW ON THE A/E PLANS. NFS DRAWINGS ARE TO SHOW ONLY THE WIRING DIAGRAMS BETWEEN FIRE ALARM DEVICES AND CONTROL PANELS. NFS IS NOT RESPONSIBLE FOR THE INFORMATION SHOWN ON THE A/E PLANS.

UNIVERSITY OF UTAH
HUNTSMAN CANCER INSTITUTE
PHASE IV - PRIMARY CHILDRENS & FAMILIES
2000 CIRCLE OF HOPE DR.
SALT LAKE CITY, UTAH 84112
FIRE ALARM SYSTEM

NFS

NELSON FIRE SYSTEMS
801-468-8300

DRAWN BY:	AK
DESIGNED BY:	XXXX
APPROVED BY:	DPS
DATE:	5/31/17
SCALE:	N. T. S.
PROJECT NO:	XXXX
REV NO:	XXXX
DRAWING NAME:	
HUNTSMAN INSTITUTE 6 FM.DWG	

FIRE ALARM SYSTEM

FINAL MAP

PAGE:

LEVEL 6

