
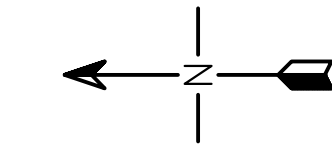


DEVICE LEGEND	
SYMBOL	DESCRIPTION
S	SMOKE DETECTOR
F	MANUAL PULL STATION
DD	DUCT DETECTOR
TS	TAMPER SWITCH
WF	WATERFLOW SWITCH
CM	CONTROL MODULE
TRAN	TRANSPONDER PANEL
FACP	FIRE ALARM CONTROL PANEL
INX	VOICE PANEL

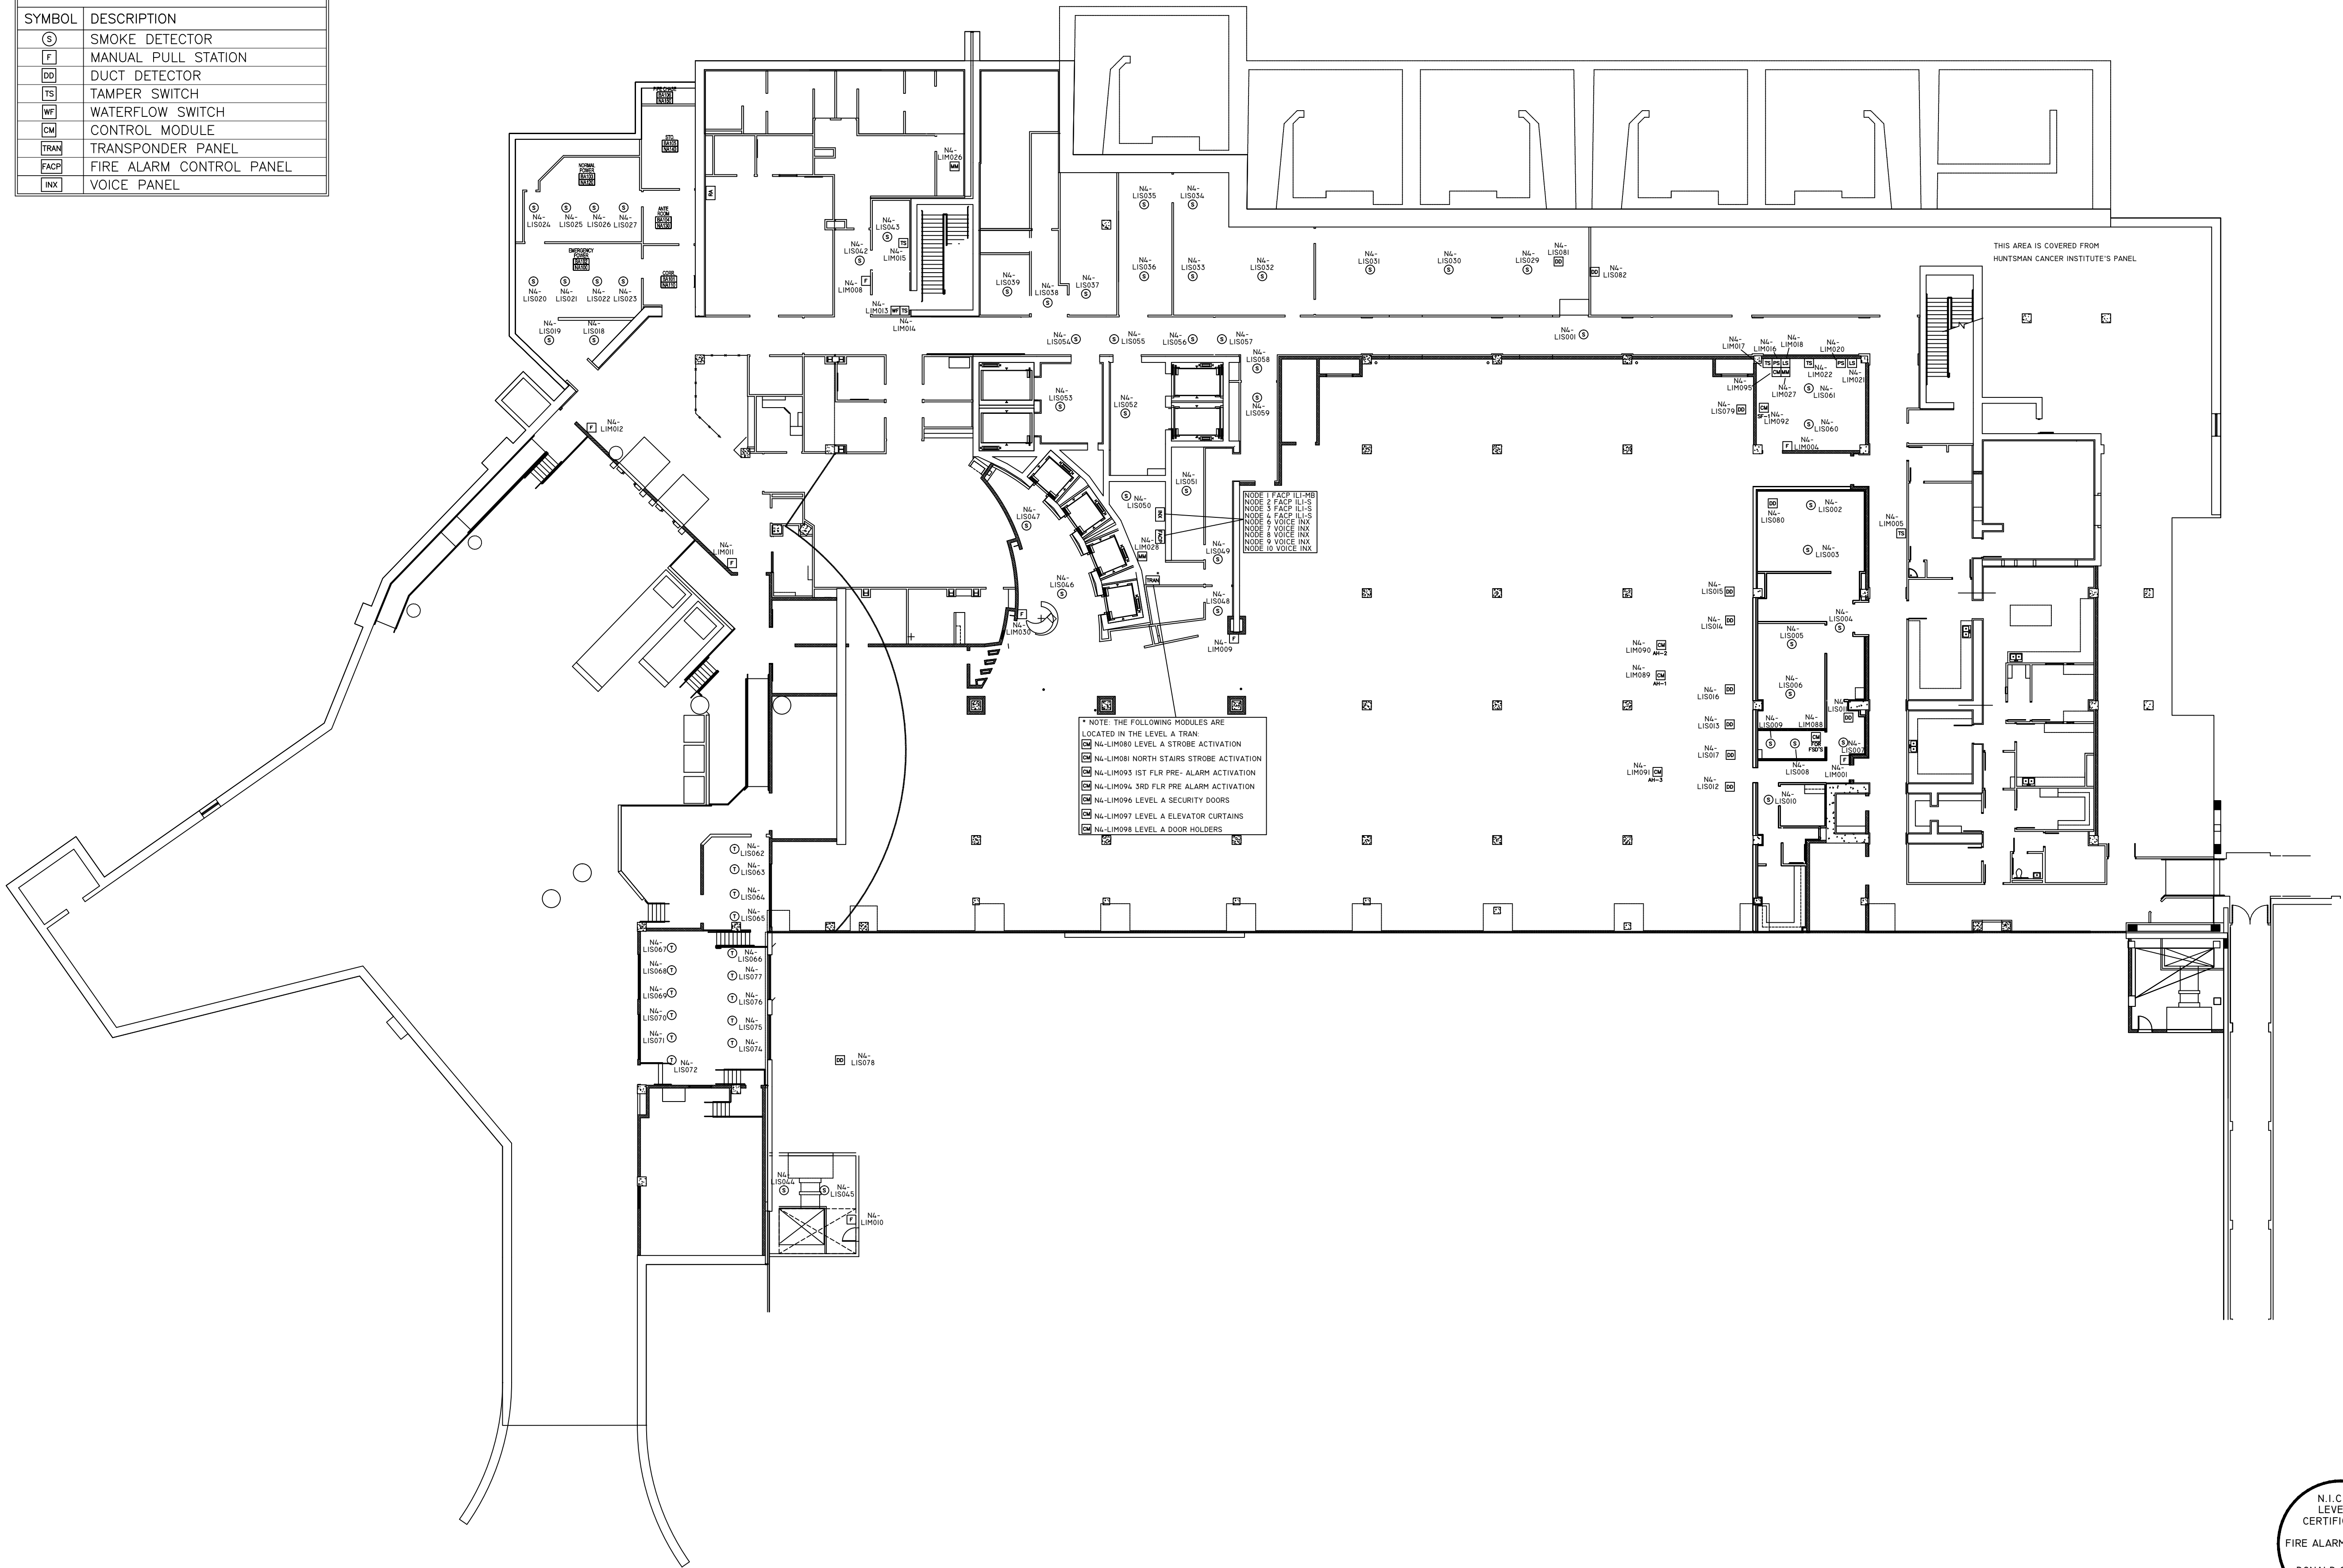

NOTE:
NFS DRAWINGS ARE BASED ON THE PROJECT ARCHITECT/ENGINEER (A/E) PLANS AND SPECIFICATIONS. NFS IS NOT RESPONSIBLE FOR THE ACCURACY OF THE (NOT NFS) FOR THE TYPE, SIZE, LOCATION, AND SUITABILITY OF ALL FIRE ALARMS, CONTROL PANELS, AND OTHER DEVICES SHOWN ON THE A/E PLANS. NFS DRAWINGS ARE TO SHOW ONLY THE WIRING DIAGRAMS BETWEEN FIRE ALARM DEVICES AND CONTROL PANELS. NFS IS NOT RESPONSIBLE FOR THE INFORMATION SHOWN ON THE A/E PLANS.

HUNTSMAN CANCER HOSPITAL
UNIVERSITY OF UTAH
LEVEL A
FINAL MAP
FIRE ALARM SYSTEM

NFS
NELSON FIRE SYSTEMS
801-468-8300


DRAWN BY: JJG
DESIGNED BY: XXXX
CHECKED BY: DS
DATE: 11/1/11
SCALE: N.T.S.
PROJECT NO: XXXX
REV NO: XXXX
DRAWING NAME:
HUNTSMAN A FINAL.DWG

FIRE ALARM SYSTEM


NFS
FA-A-01

N.I.C.E.T.
LEVEL IV
CERTIFICATION
FIRE ALARM SYSTEMS
DONALD SCHULTZ
#104396

DEVICE LEGEND	
SYMBOL	DESCRIPTION
Ⓢ	SMOKE DETECTOR
F	MANUAL PULL STATION
DD	DUCT DETECTOR
TS	TAMPER SWITCH
WF	WATERFLOW SWITCH
CM	CONTROL MODULE
TRAN	TRANSPONDER PANEL
FACP	FIRE ALARM CONTROL PANEL
INX	VOICE PANEL

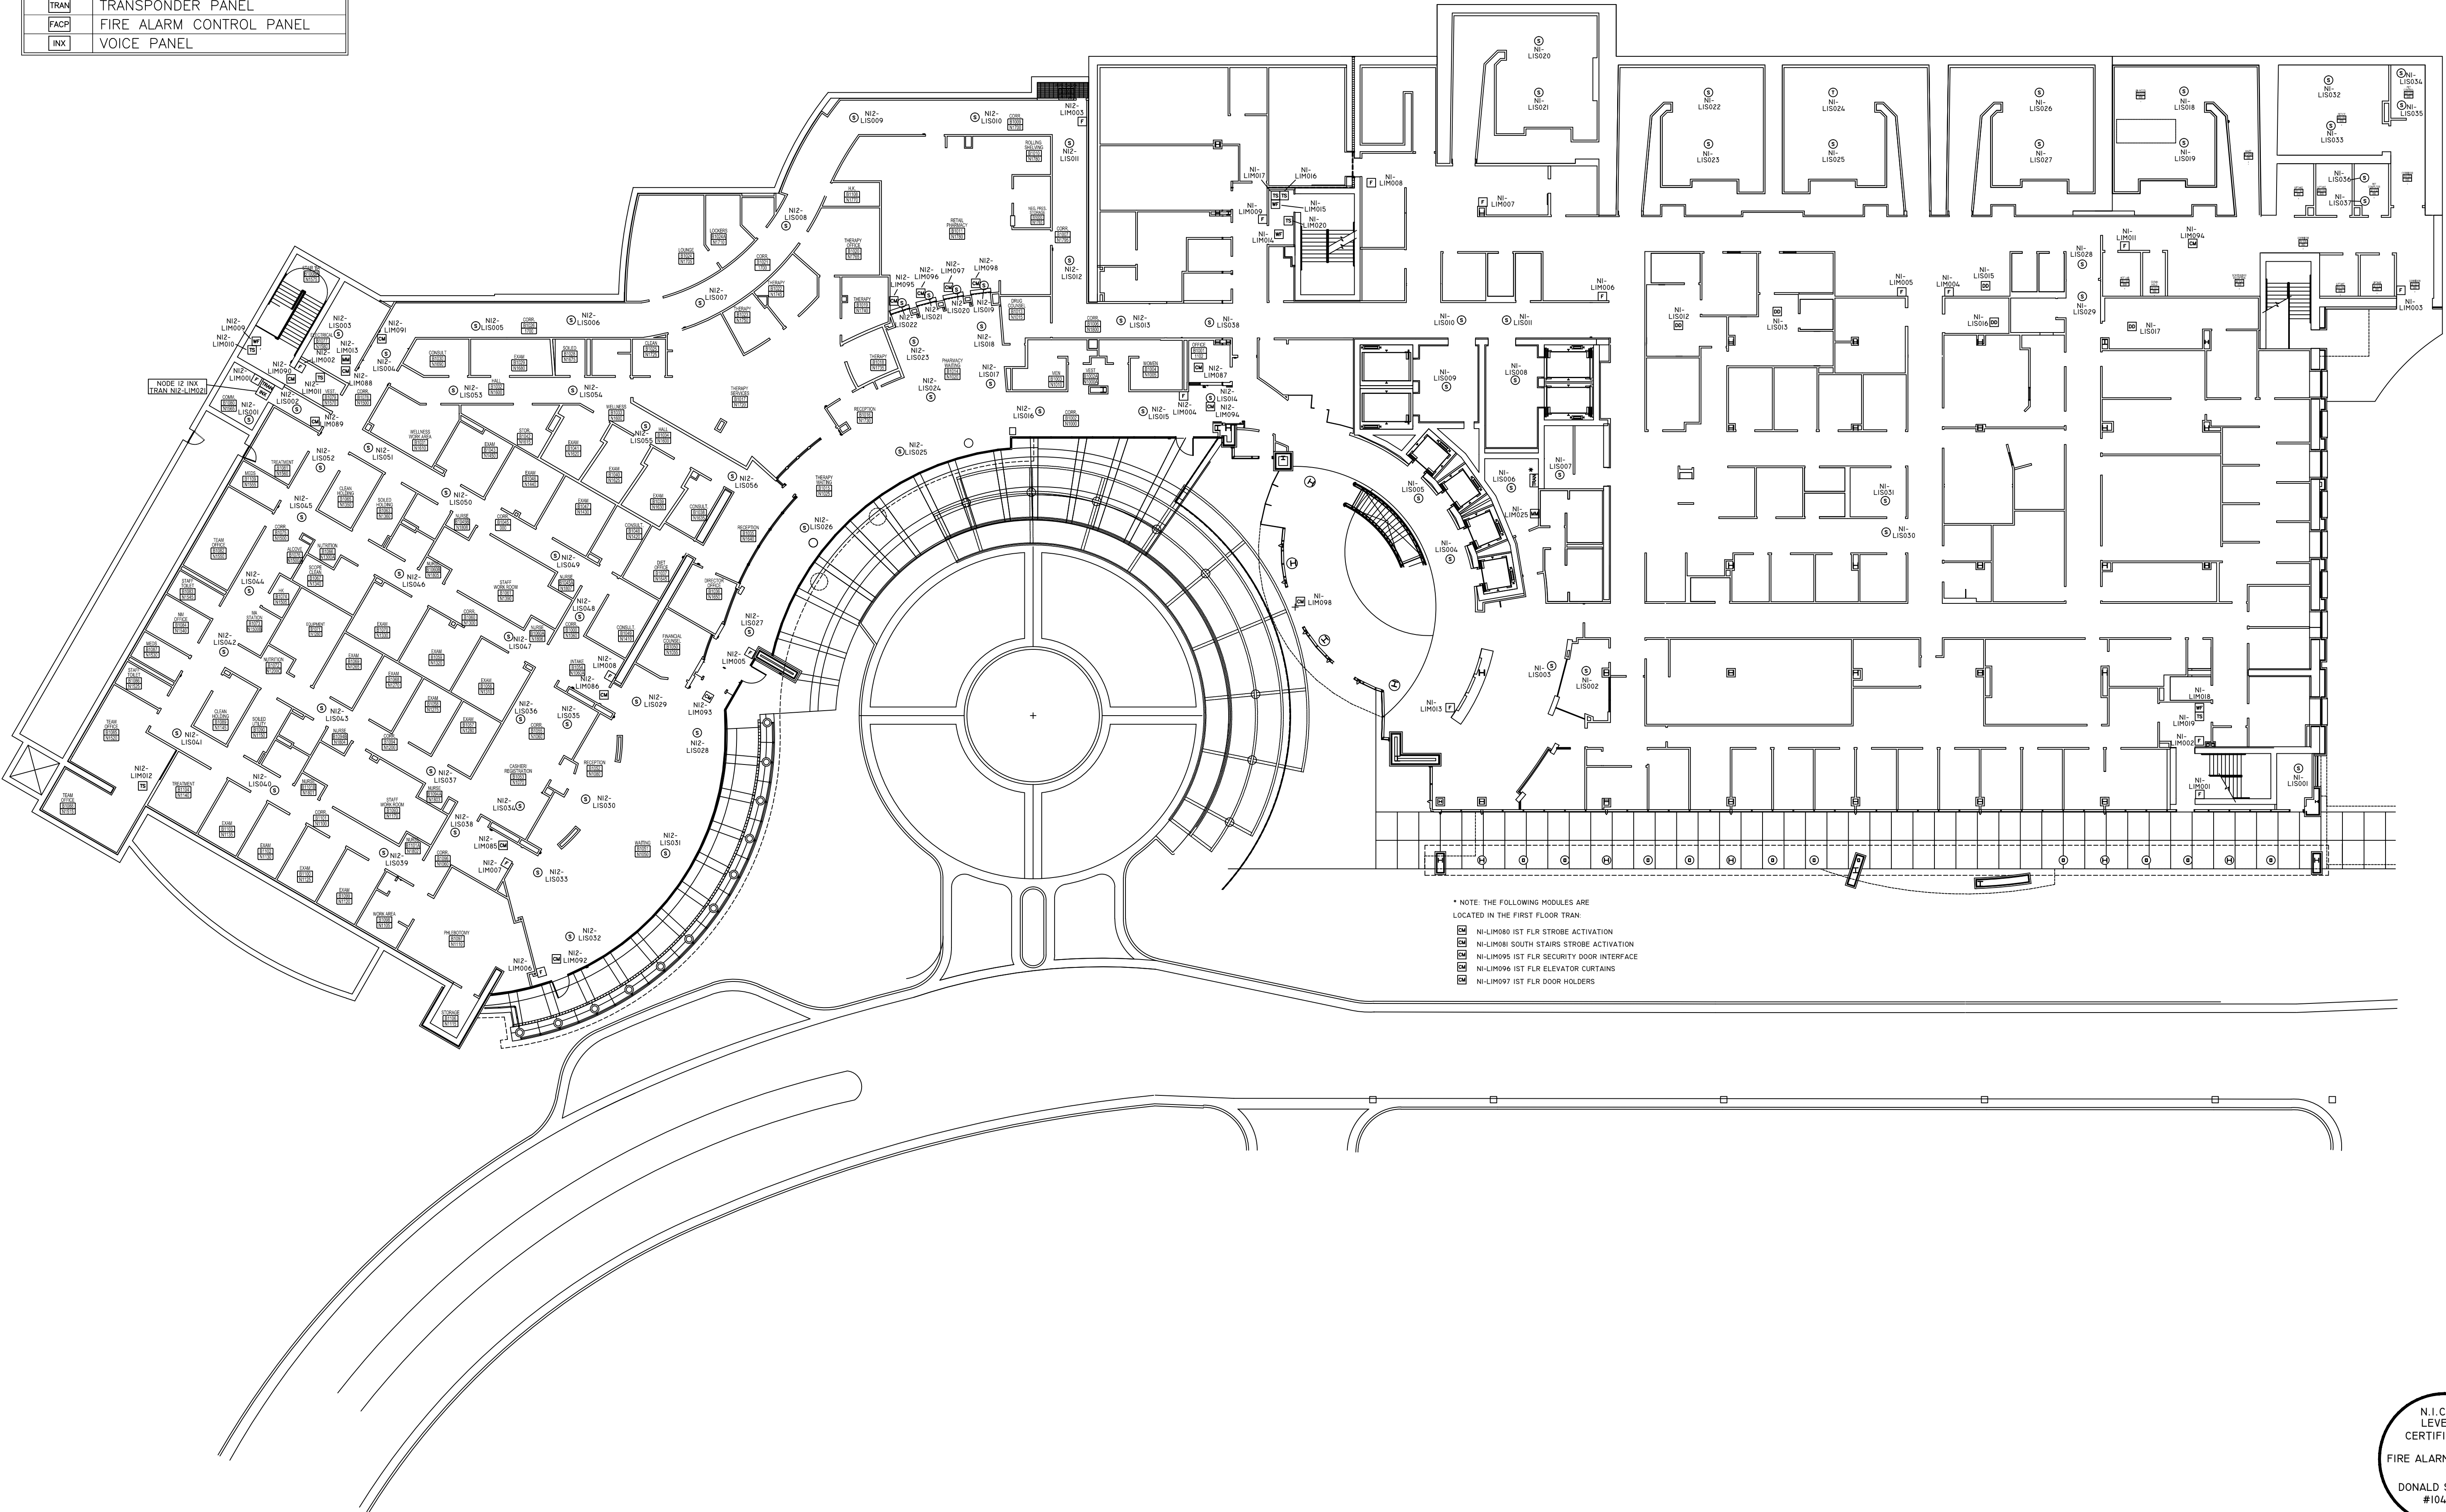

* NOTE: THE FOLLOWING MODULES ARE
LOCATED IN THE FIRST FLOOR TRAN:
NI-LIM040 1ST FLR STROBE ACTIVATION
NI-LIM081 SOUTH STAIRS STROBE ACTIVATION
NI-LIM095 1ST FLR SECURITY DOOR INTERFACE
NI-LIM096 1ST FLR ELEVATOR CURTAINS
NI-LIM097 1ST FLR DOOR HOLDERS

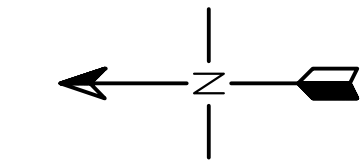

NOTE:
NFS DRAWINGS ARE BASED ON THE PROJECT
ARCHITECT/ENGINEER (A/E) PLANS AND SPECIFICATIONS
FURNISHED TO NFS. A/E IS SOLELY RESPONSIBLE
(NOT NFS) FOR THE TYPE, SIZE, LOCATION, AND
SUITABILITY OF ALL FIRE ALARMS, CONTROL PANELS,
AND OTHER DEVICES SHOWN ON THE A/E PLANS.
NFS DRAWINGS ARE TO SHOW ONLY THE WIRING
DIAGRAMS BETWEEN FIRE ALARM DEVICES AND
CONTROL PANELS. NFS IS NOT RESPONSIBLE FOR
THE INFORMATION SHOWN ON THE A/E PLANS.

HUNTSMAN CANCER HOSPITAL
UNIVERSITY OF UTAH
LEVEL I
FINAL MAP
FIRE ALARM SYSTEM

NFS

NELSON FIRE SYSTEMS
801-468-8300

DRAWN BY:	JJG
DESIGNED BY:	XXXX
CHECKED BY:	DS
DATE:	11/1/11
SCALE:	N.T.S.
PROJECT NO:	XXXX
REV NO:	XXXX
DRAWING NAME:	HUNTSMAN I FINAL.DWG


FIRE ALARM SYSTEM

NFS

FA-I-01

N.I.C.E.T.
LEVEL IV
CERTIFICATION
FIRE ALARM SYSTEMS
DONALD SCHULTZ
#104396


DEVICE LEGEND	
SYMBOL	DESCRIPTION
Ⓢ	SMOKE DETECTOR
F	MANUAL PULL STATION
DD	DUCT DETECTOR
TS	TAMPER SWITCH
WF	WATERFLOW SWITCH
CM	CONTROL MODULE
TRAN	TRANSPONDER PANEL
FACP	FIRE ALARM CONTROL PANEL
INX	VOICE PANEL

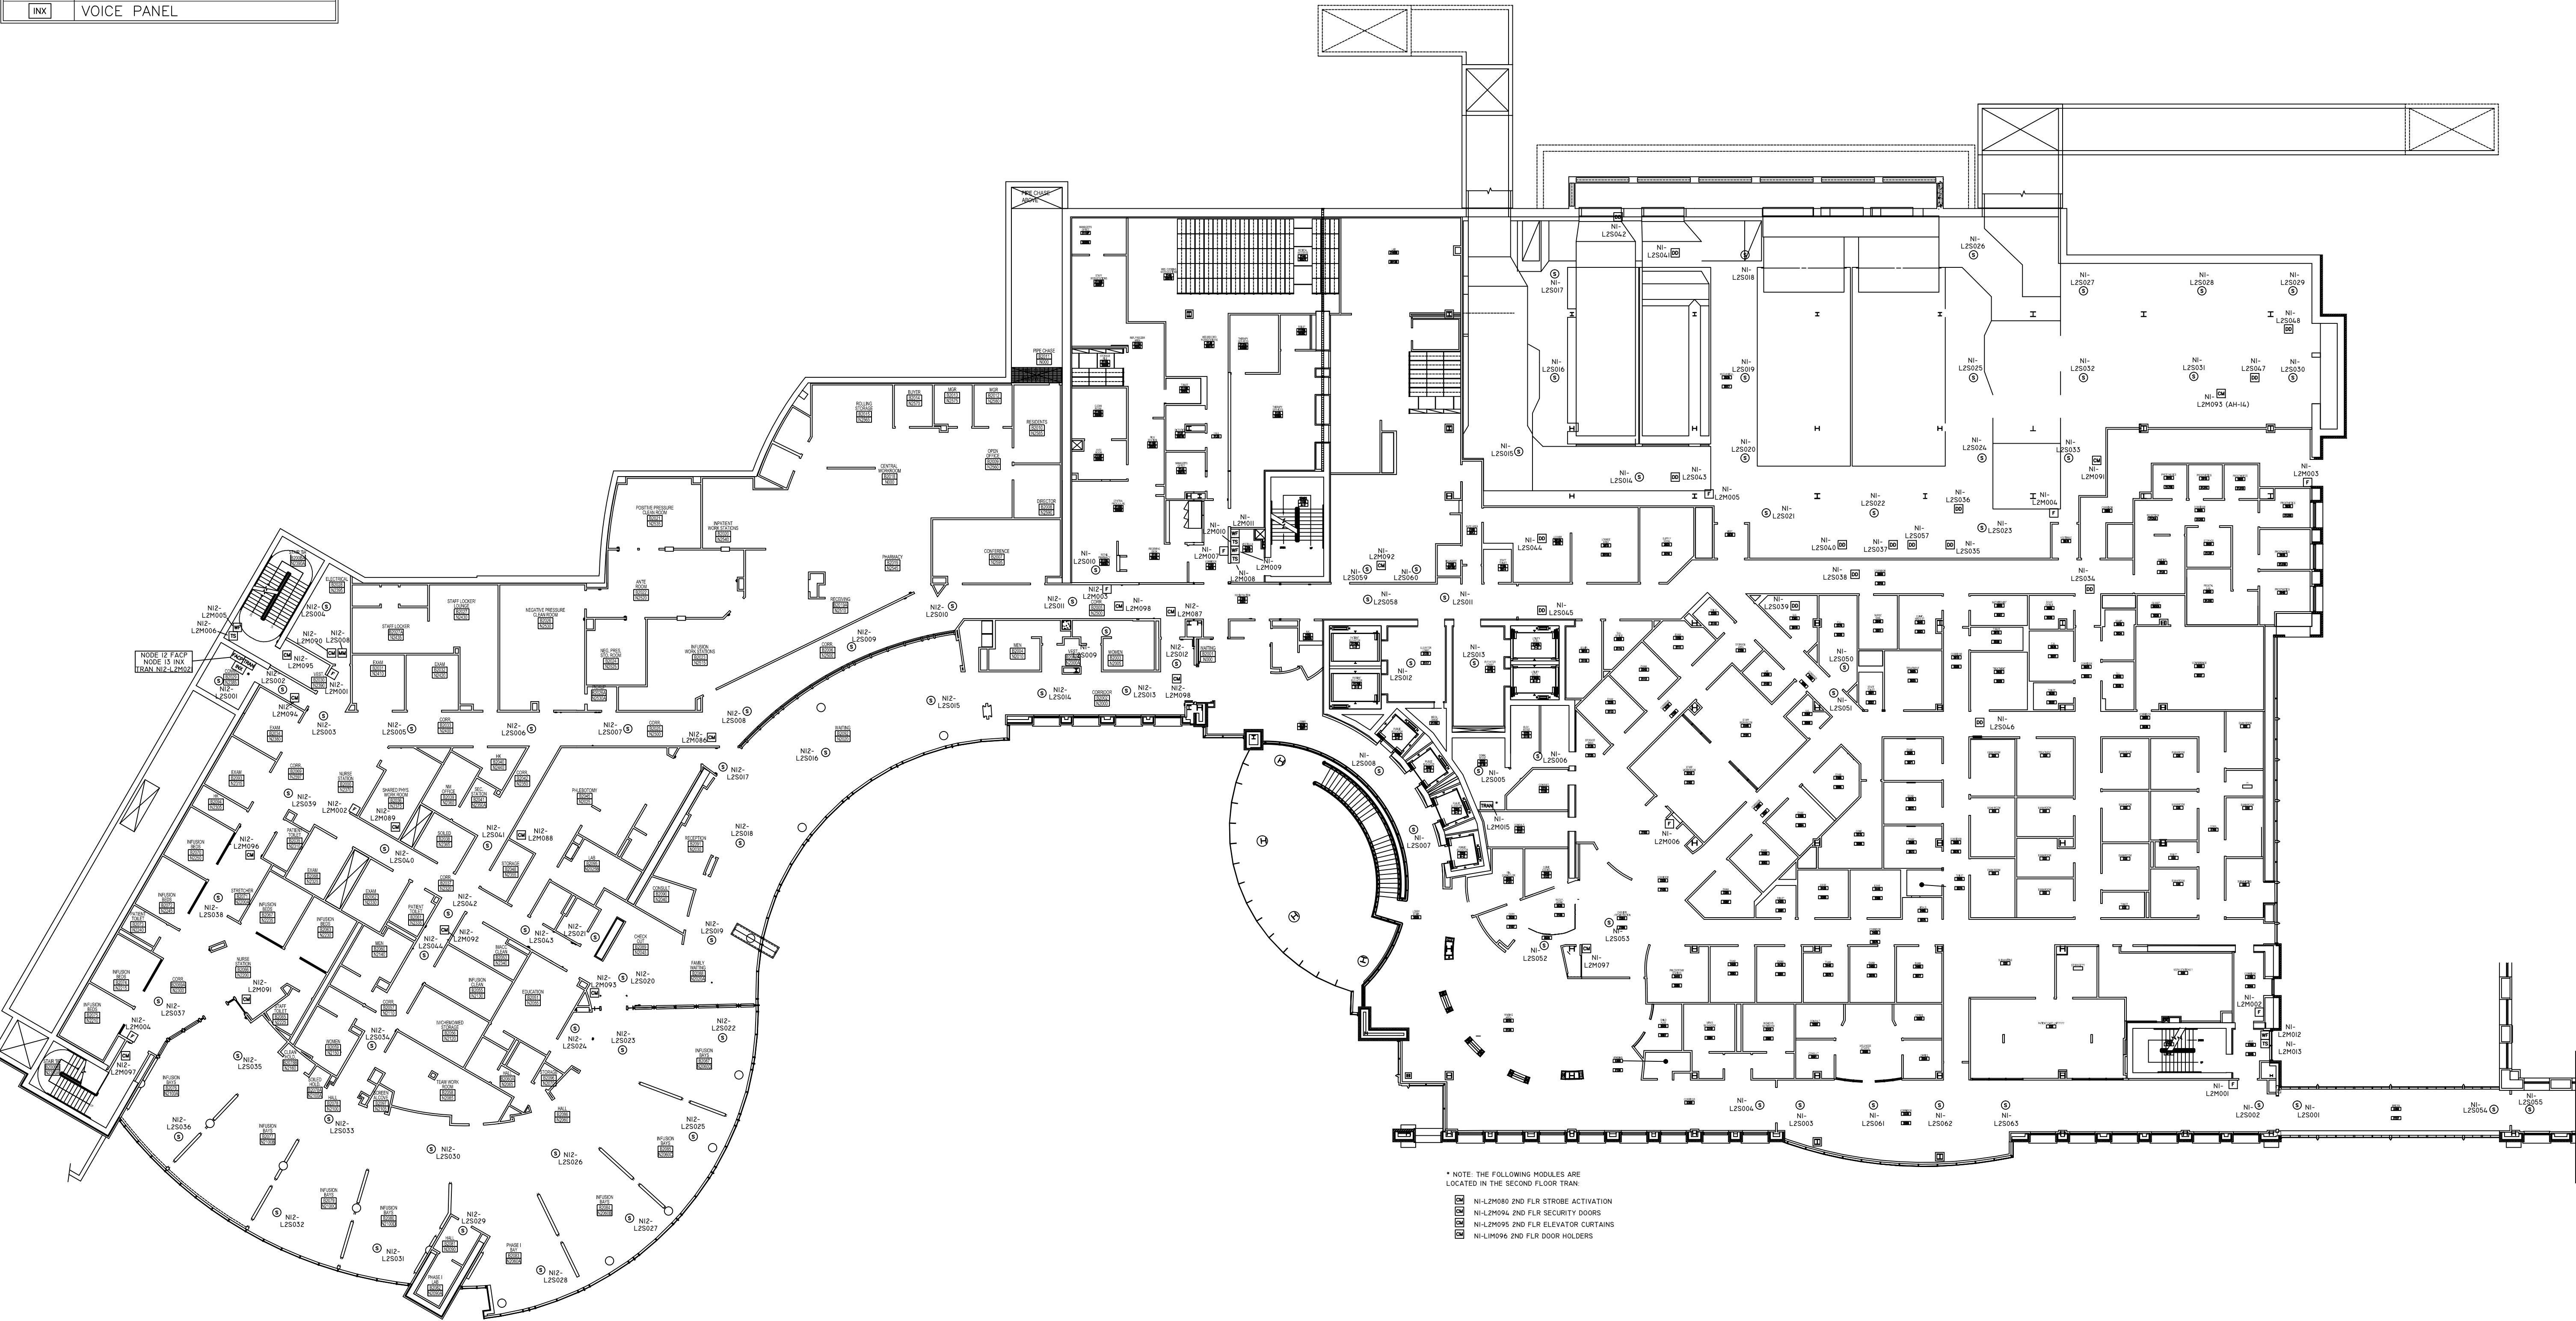

* NOTE: THE FOLLOWING MODULES ARE
LOCATED IN THE SECOND FLOOR TRAN

- NI-L2M080 2ND FLR STROBE ACTIVATION
- NI-L2M094 2ND FLR SECURITY DOORS
- NI-L2M096 2ND FLR ELEVATOR CURTAINS
- NI-L2M095 2ND FLR DOOR HOLDERS

N.I.C.E.T.
LEVEL IV
CERTIFICATION
FIRE ALARM SYSTEMS
DONALD SCHULTZ
#104396

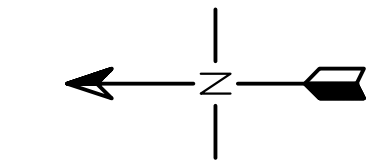

NOTE:
NFS DRAWINGS ARE BASED ON THE PROJECT
ARCHITECT/ENGINEER (A/E) PLANS AND SPECIFICATIONS
FURNISHED TO NFS. A/E IS SOLELY RESPONSIBLE
(NOT NFS) FOR THE TYPE, SIZE, LOCATION, AND
SUITABILITY OF ALL FIRE ALARMS, CONTROL PANELS,
AND OTHER DEVICES SHOWN ON THE A/E PLANS.
NFS DRAWINGS ARE TO SHOW ONLY THE WIRING
DIAGRAMS BETWEEN FIRE ALARM DEVICES AND
CONTROL PANELS. NFS IS NOT RESPONSIBLE FOR
THE INFORMATION SHOWN ON THE A/E PLANS.

HUNTSMAN CANCER HOSPITAL
UNIVERSITY OF UTAH
LEVEL 2
FINAL MAP
FIRE ALARM SYSTEM

NFS
NELSON FIRE SYSTEMS
801-468-8300

DRAWN BY:	JJG
DESIGNED BY:	XXXX
CHECKED BY:	DS
DATE:	2/5/2014
SCALE:	N.T.S.
PROJECT NO:	XXXX
REV NO:	XXXX
DRAWING NAME:	HUNTSMAN 2 FINAL.DWG

FIRE ALARM SYSTEM

NFS
FA-2-01


DEVICE LEGEND	
SYMBOL	DESCRIPTION
	SMOKE DETECTOR
	MANUAL PULL STATION
	DUCT DETECTOR
	TAMPER SWITCH
	WATERFLOW SWITCH
	CONTROL MODULE
	TRANSPONDER PANEL
	FIRE ALARM CONTROL PANEL
	VOICE PANEL

* NOTE: THE FOLLOWING MODULES
ARE LOCATED IN THE 3RD FLOOR CORR. ROOM 8309S:

- NODE 14
- NODE 15
- N6-LM021 3RD FLR NORTH TRANSPONDER SUPERVISION
- N6-LIS001 STAIR BC FIREPHONE MODULE
- N6-LM089 IHRIS CONTROL ROOM STROBE TRIP

* NOTE: THE FOLLOWING MODULES
ARE LOCATED IN THE 3RD FLOOR TRAN:

- N2-LM080 3RD FLR STROBE ACTIVATION
- N2-LM096 3RD FLR SECURITY DOORS
- N2-LM097 3RD FLR ELEV CURTAINS
- N2-LM098 3RD FLR DOOR HOLDERS

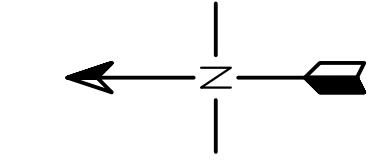

NOTE:
NFS DRAWINGS ARE BASED ON THE PROJECT
ARCHITECT/ENGINEER (A/E) PLANS AND SPECIFICATIONS
FURNISHED TO NFS. A/E IS SOLELY RESPONSIBLE
(NOT NFS) FOR THE TYPE, SIZE, LOCATION, AND
SUITABILITY OF ALL FIRE ALARMS, CONTROL PANELS,
AND OTHER DEVICES SHOWN ON THE A/E PLANS.
NFS DRAWINGS ARE TO SHOW ONLY THE WIRING
DIAGRAMS BETWEEN FIRE ALARM DEVICES AND
CONTROL PANELS. NFS IS NOT RESPONSIBLE FOR
THE INFORMATION SHOWN ON THE A/E PLANS.

HUNTSMAN CANCER HOSPITAL
UNIVERSITY OF UTAH
LEVEL 3
FINAL MAP
FIRE ALARM SYSTEM

NFS
NELSON FIRE SYSTEMS
801-468-8300

DRAWN BY: JJC
DESIGNED BY: XXXX
CHECKED BY: DS
DATE: 11/1/11
SCALE: N.T.S.
PROJECT NO: XXXX
REV NO: XXXX
DRAWING NAME:
HUNTSMAN 3 FINAL.DWG


FIRE ALARM SYSTEM

NFS

FA-3-01

N.I.C.E.T.
LEVEL IV
CERTIFICATION
FIRE ALARM SYSTEMS
DONALD SCHULTZ
#104396

DEVICE LEGEND	
SYMBOL	DESCRIPTION
Ⓢ	SMOKE DETECTOR
F	MANUAL PULL STATION
DD	DUCT DETECTOR
TS	TAMPER SWITCH
WF	WATERFLOW SWITCH
CM	CONTROL MODULE
TRAN	TRANSPONDER PANEL
FACP	FIRE ALARM CONTROL PANEL
INX	VOICE PANEL

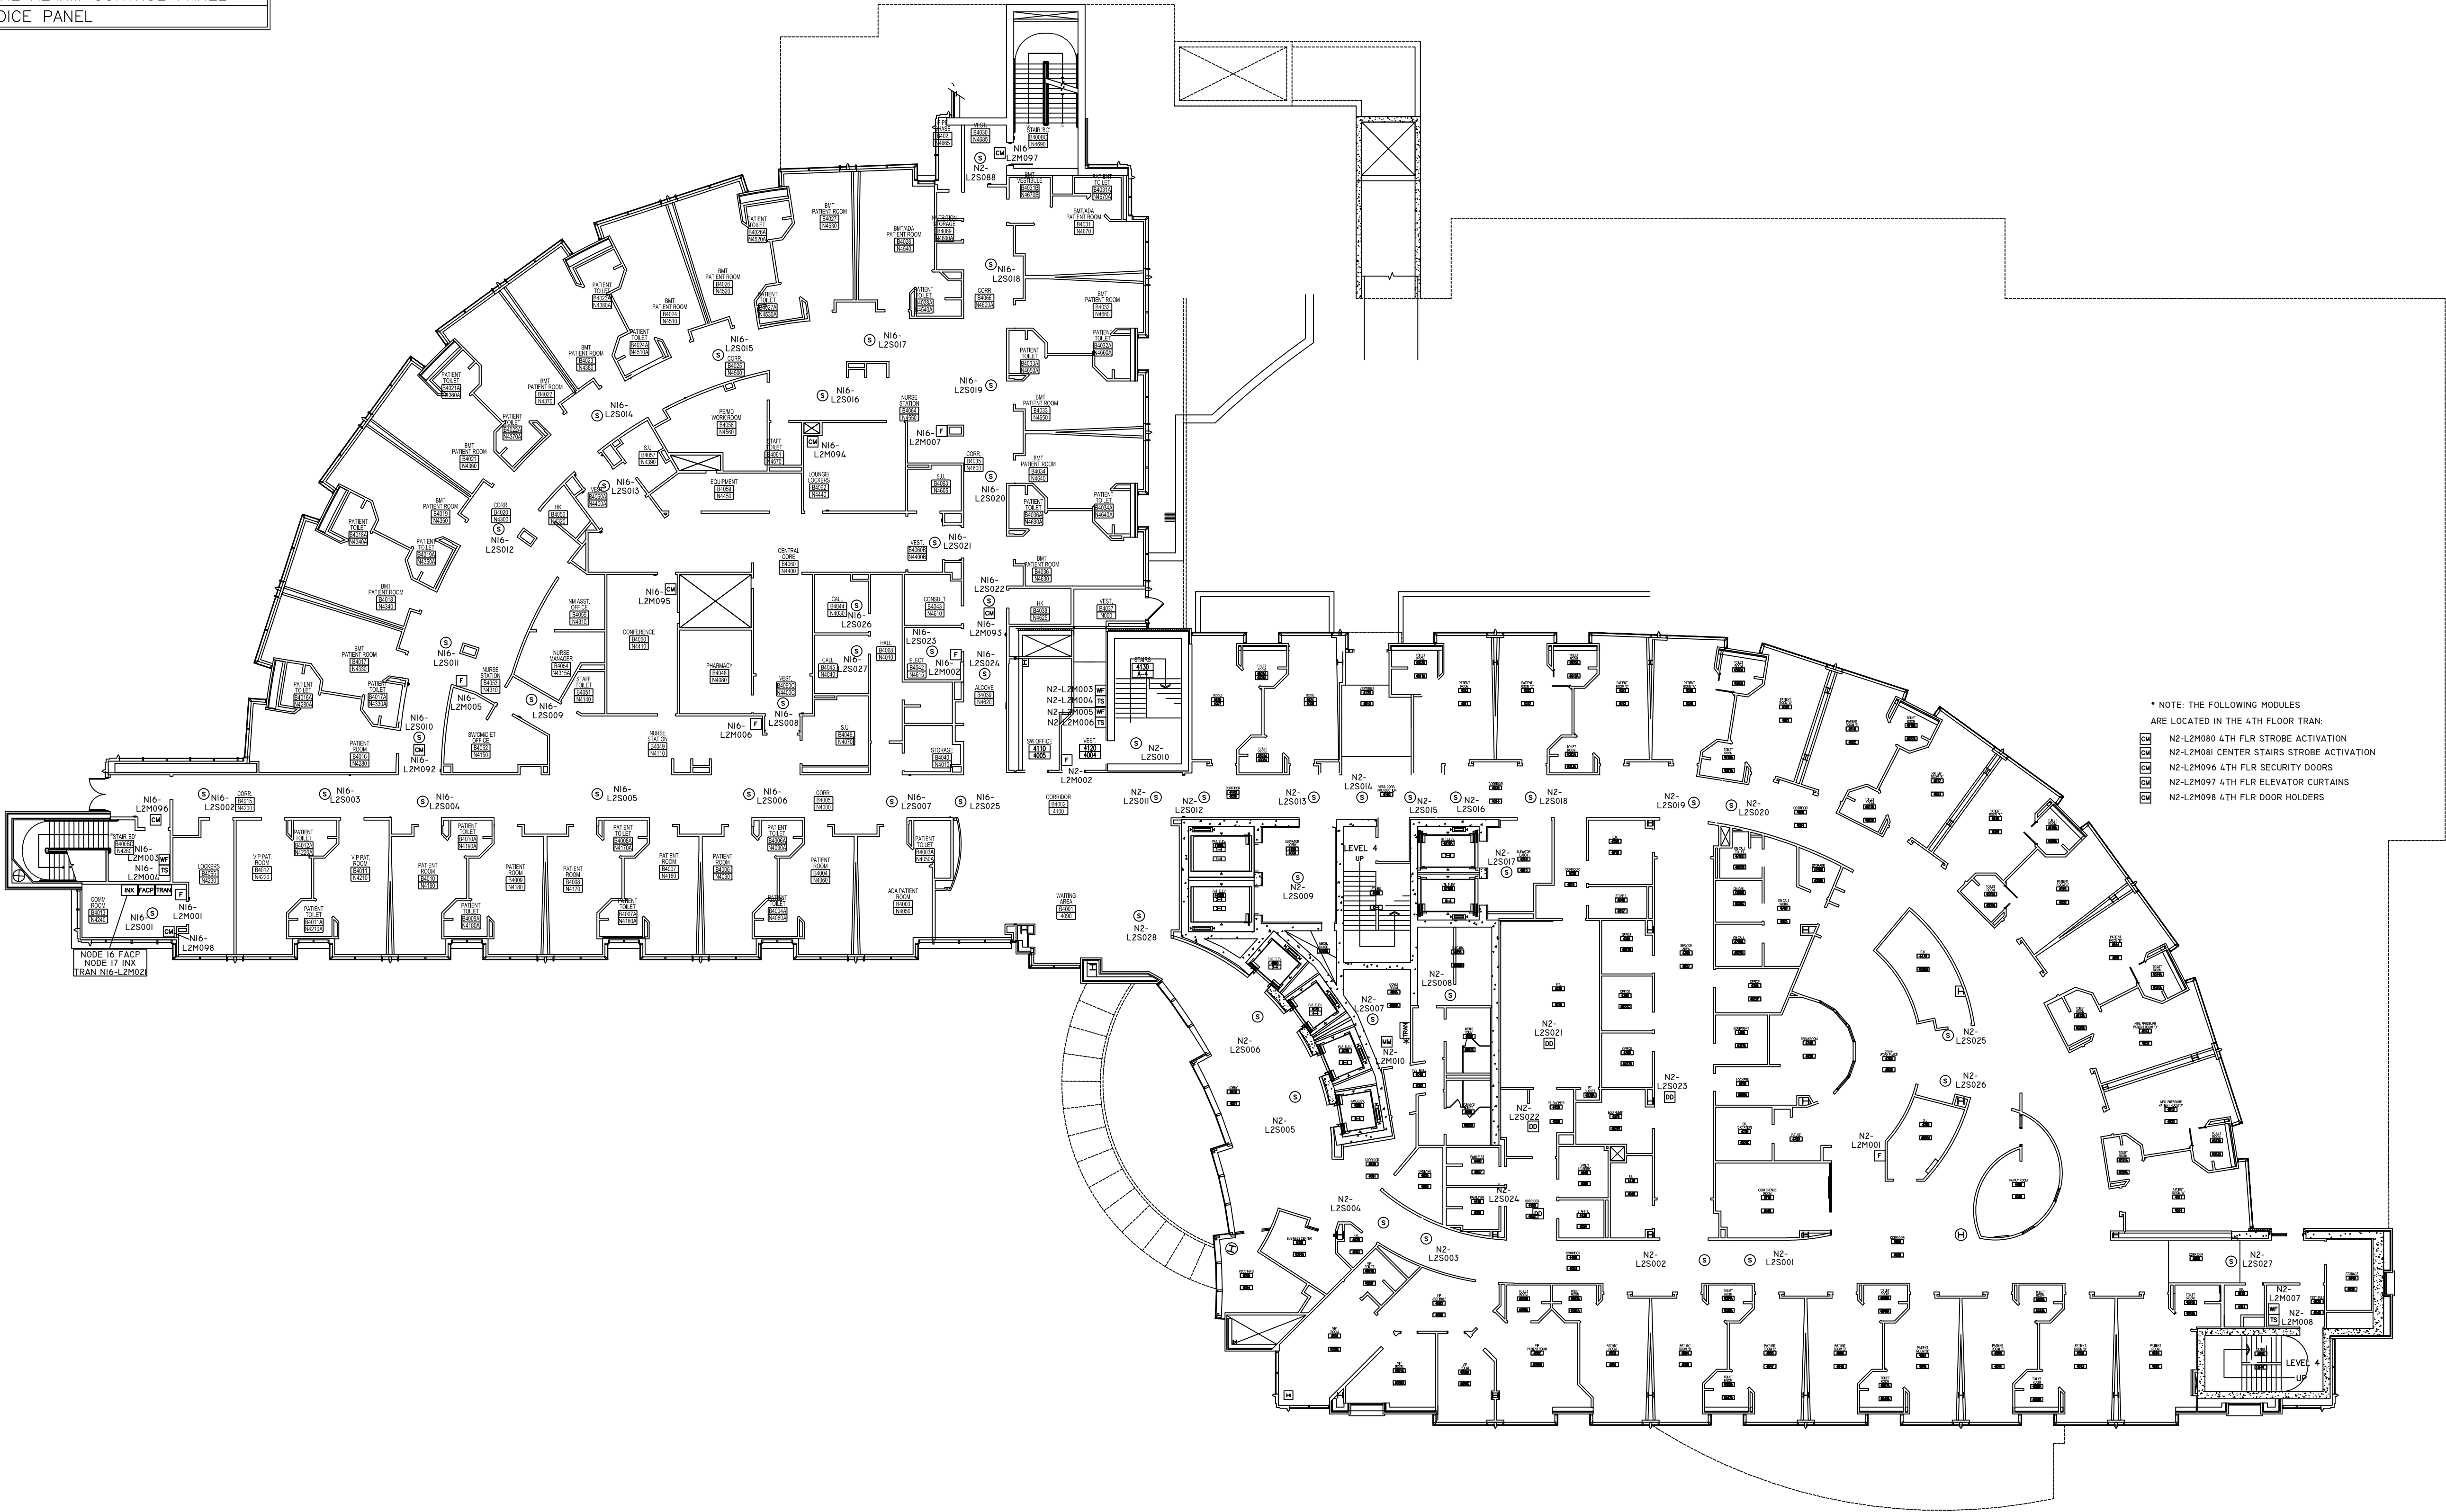

* NOTE: THE FOLLOWING MODULES
ARE LOCATED IN THE 4TH FLOOR TRAN:
N2-L2M080 4TH FLR STROBE ACTIVATION
N2-L2M081 CENTER STAIRS STROBE ACTIVATION
N2-L2M096 4TH FLR SECURITY DOORS
N2-L2M097 4TH FLR ELEVATOR CURTAINS
N2-L2M098 4TH FLR DOOR HOLDERS

HUNTSMAN CANCER HOSPITAL
UNIVERSITY OF UTAH
LEVEL 4
FINAL MAP
FIRE ALARM SYSTEM

NOTE:
NFS DRAWINGS ARE BASED ON THE PROJECT
ARCHITECT/ENGINEER (A/E) PLANS AND SPECIFICATIONS
FURNISHED TO NFS. A/E IS SOLELY RESPONSIBLE
(NOT NFS) FOR THE TYPE, SIZE, LOCATION AND
SUITABILITY OF ALL FIRE ALARMS, CONTROL PANELS,
AND OTHER DEVICES SHOWN ON THE A/E PLANS.
NFS DRAWINGS ARE TO SHOW ONLY THE WIRING
DIAGRAMS BETWEEN FIRE ALARM DEVICES AND
CONTROL PANELS. NFS IS NOT RESPONSIBLE FOR
THE INFORMATION SHOWN ON THE A/E PLANS.

NFS

NELSON FIRE SYSTEMS
801-468-8300

DRAWN BY:	JJG
DESIGNED BY:	XXXX
CHECKED BY:	DS
DATE:	2/5/2014
SCALE:	N.T.S.
PROJECT NO:	XXXX
REV NO:	XXXX
DRAWING NAME:	HUNTSMAN 4 FINAL.DWG

FIRE ALARM SYSTEM


NFS
FA-4-01

N.I.C.E.T.
LEVEL IV
CERTIFICATION


FIRE ALARM SYSTEMS

DONALD SCHULTZ
#104396

DEVICE LEGEND	
SYMBOL	DESCRIPTION
Ⓢ	SMOKE DETECTOR
F	MANUAL PULL STATION
DD	DUCT DETECTOR
TS	TAMPER SWITCH
WF	WATERFLOW SWITCH
CM	CONTROL MODULE
TRAN	TRANSPONDER PANEL
FACP	FIRE ALARM CONTROL PANEL
INX	VOICE PANEL

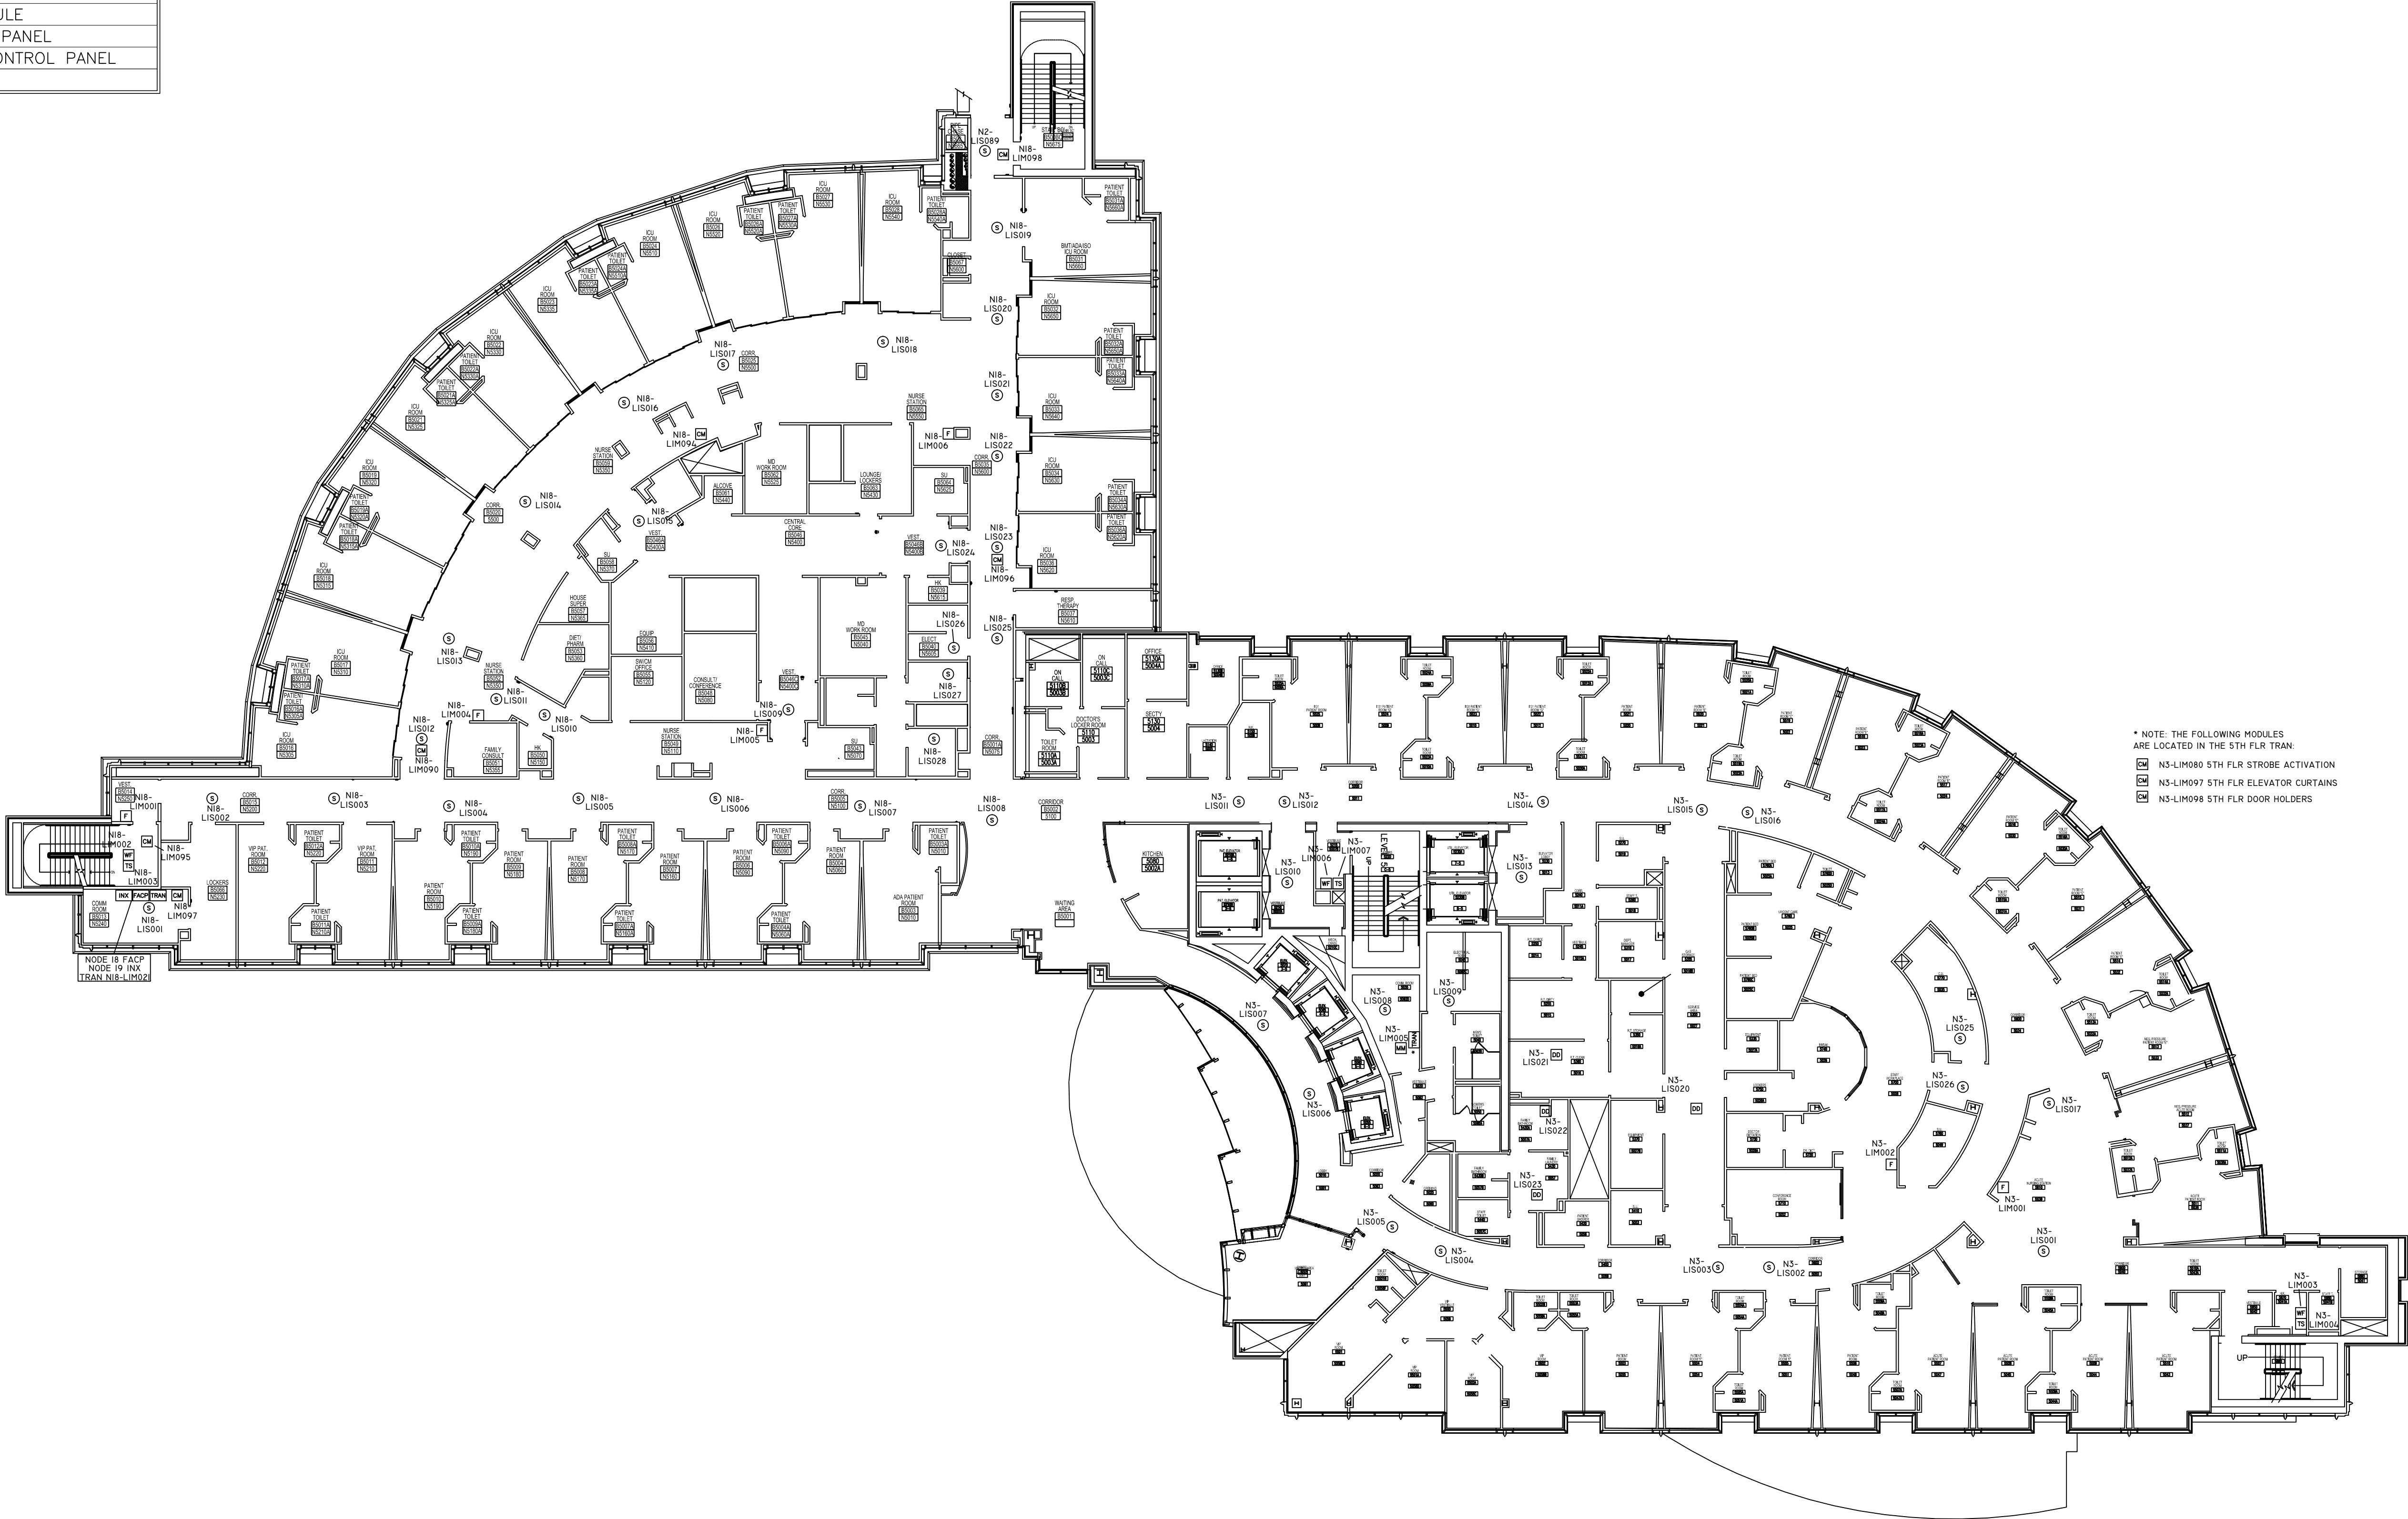

* NOTE: THE FOLLOWING MODULES
ARE LOCATED IN THE 5TH FLR TRAN:
N3-LIM080 5TH FLR STROBE ACTIVATION
N3-LIM097 5TH FLR ELEVATOR CURTAINS
N3-LIM098 5TH FLR DOOR HOLDERS

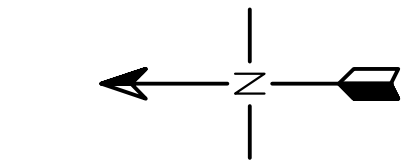

NOTE:
NFS DRAWINGS ARE BASED ON THE PROJECT
ARCHITECT/ENGINEER (A/E) PLANS AND SPECIFICATIONS
FURNISHED TO NFS. A/E IS SOLELY RESPONSIBLE
(NOT NFS) FOR THE TYPE, SIZE, LOCATION, AND
SUITABILITY OF ALL FIRE ALARMS, CONTROL PANELS,
AND OTHER DEVICES SHOWN ON THE A/E PLANS.
NFS DRAWINGS ARE TO SHOW ONLY THE WIRING
DIAGRAMS BETWEEN FIRE ALARM DEVICES AND
CONTROL PANELS. NFS IS NOT RESPONSIBLE FOR
THE INFORMATION SHOWN ON THE A/E PLANS.

HUNTSMAN CANCER HOSPITAL
UNIVERSITY OF UTAH
LEVEL 5
FINAL MAP
FIRE ALARM SYSTEM

NFS

NELSON FIRE SYSTEMS
801-468-8300

DRAWN BY:	JJG
DESIGNED BY:	XXXX
CHECKED BY:	DS
DATE:	11/1/11
SCALE:	N.T.S.
PROJECT NO:	XXXX
REV NO:	XXXX
DRAWING NAME:	HUNTSMAN 5 FINAL.DWG

FIRE ALARM SYSTEM

NFS
FA-5-01

N.I.C.E.T.
LEVEL IV
CERTIFICATION



FIRE ALARM SYSTEMS

DONALD SCHULTZ
#104396

DEVICE LEGEND	
SYMBOL	DESCRIPTION
Ⓢ	SMOKE DETECTOR
F	MANUAL PULL STATION
DD	DUCT DETECTOR
TS	TAMPER SWITCH
WF	WATERFLOW SWITCH
CM	CONTROL MODULE
TRAN	TRANSPONDER PANEL
FACP	FIRE ALARM CONTROL PANEL
INX	VOICE PANEL

* NOTE: THE FOLLOWING MODULES
ARE LOCATED IN THE 6TH FLR ELECTRICAL ROOM N6S60

Ⓢ N18-L2M090 6TH FLR FIRE/SMOKE DAMPER CONTROL
Ⓢ N18-L2M091 5TH FLR FIRE/SMOKE DAMPER CONTROL
Ⓢ N18-L2M092 4TH FLR FIRE/SMOKE DAMPER CONTROL
Ⓢ N18-L2M093 3RD FLR FIRE/SMOKE DAMPER CONTROL
Ⓢ N18-L2M094 EXHAUST DAMPERS CONTROL
Ⓢ N18-L2M095 EXHAUST FAN #20 STATUS MODULE
Ⓢ N18-L2M097 EXHAUST FAN #27 STATUS MODULE
Ⓢ N18-L2M099 EXHAUST FAN #29 STATUS MODULE

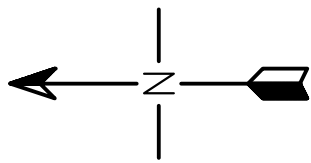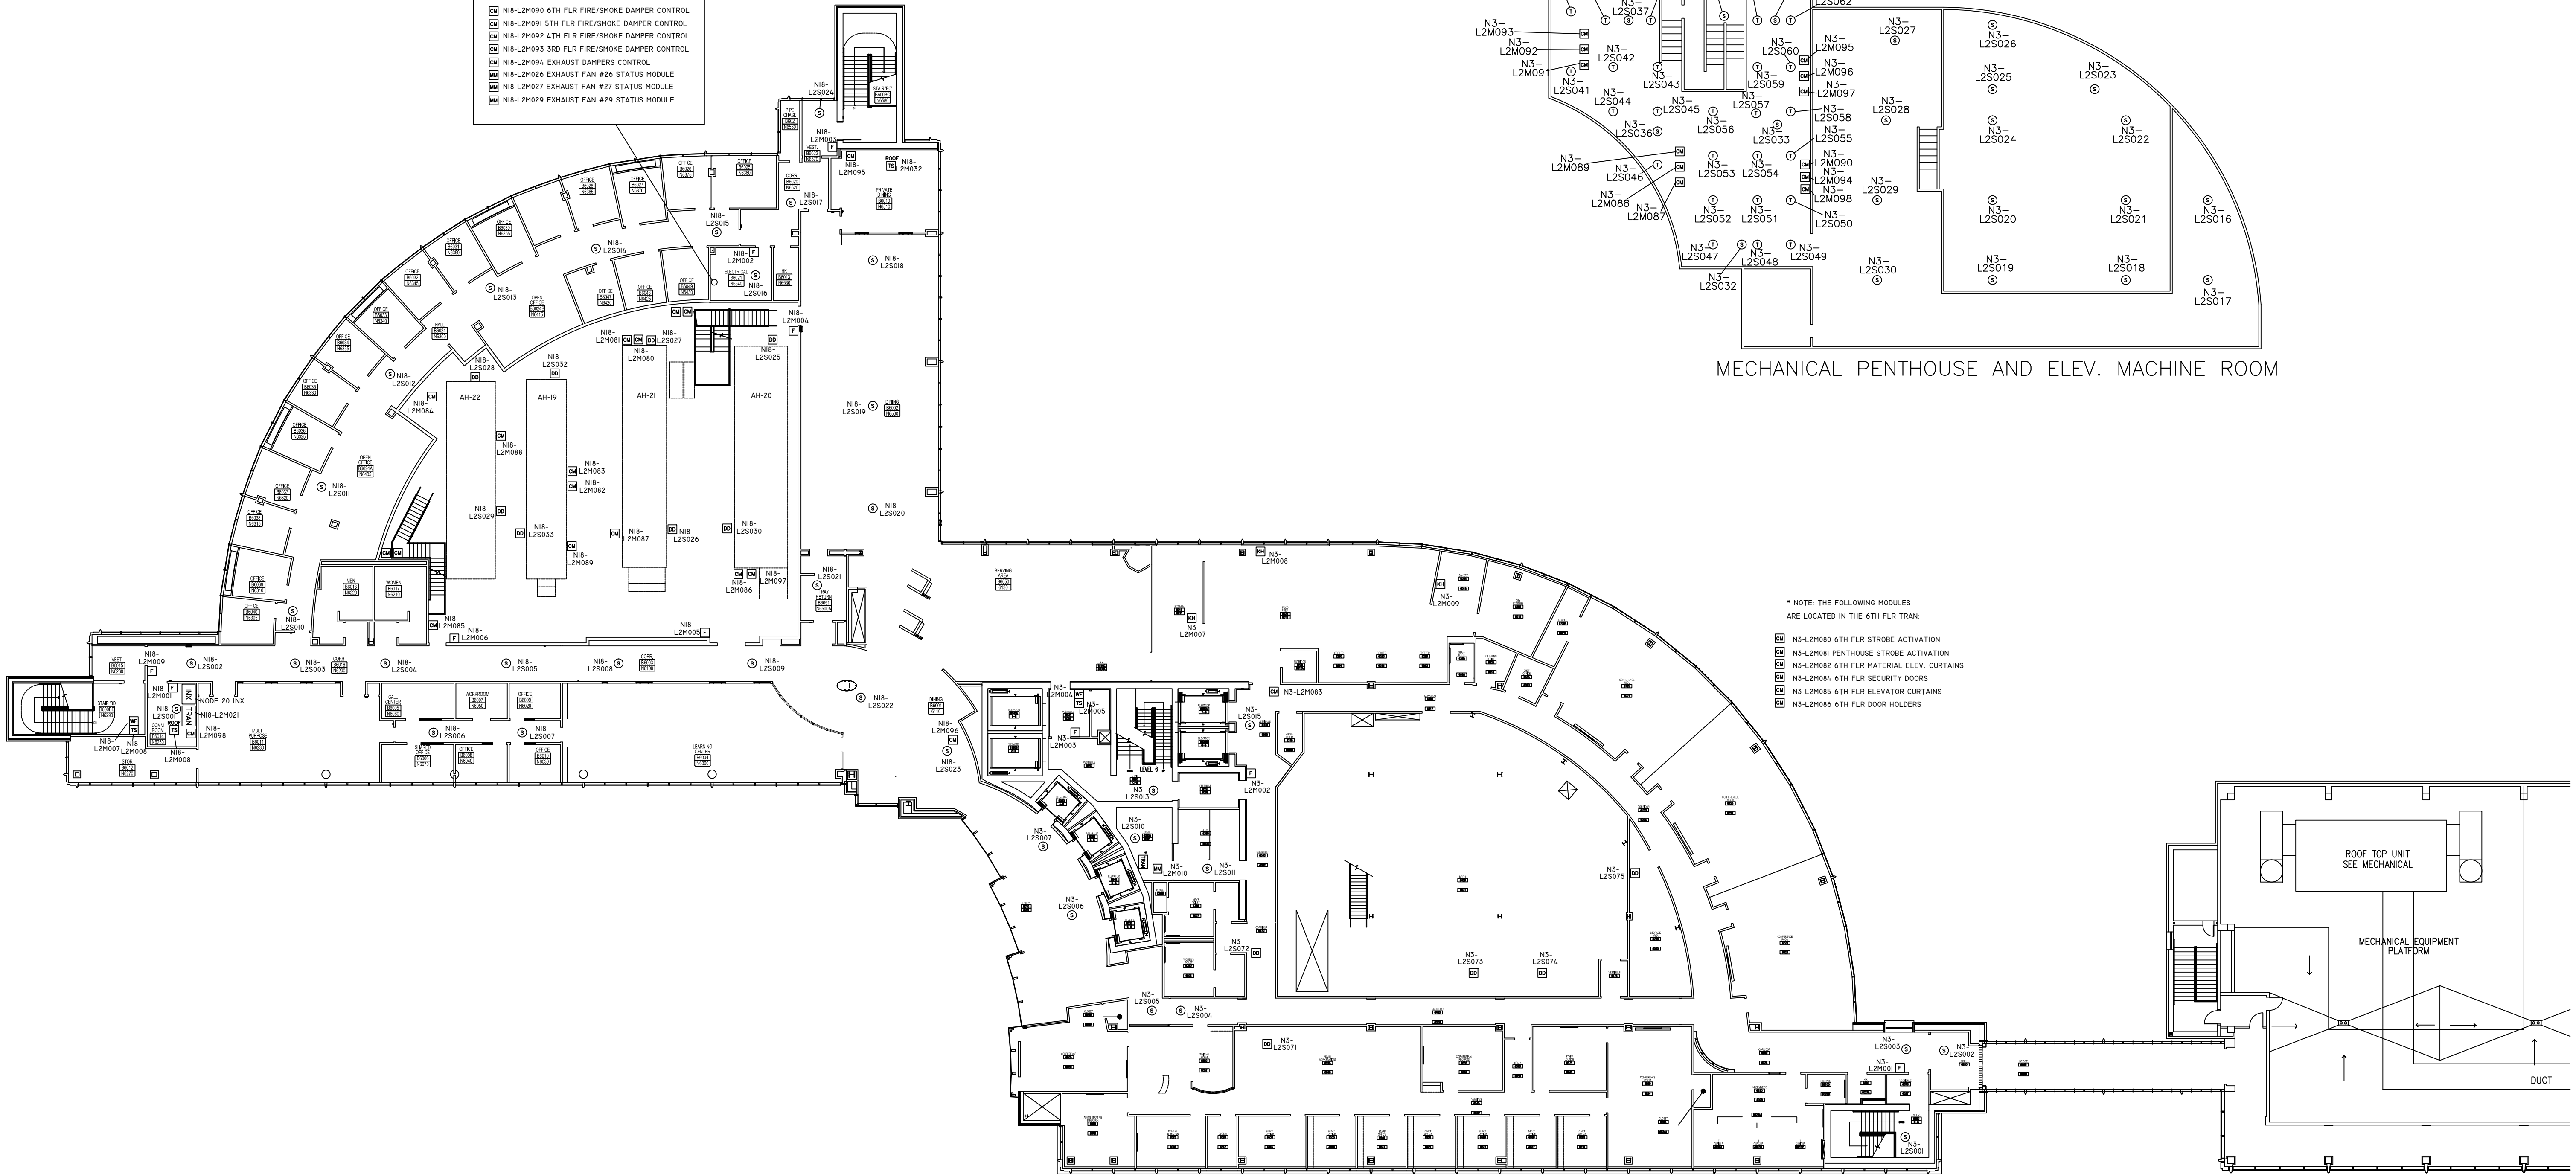

NOTE:
NFS DRAWINGS ARE BASED ON THE PROJECT
ARCHITECT/ENGINEER (A/E) PLANS AND SPECIFICATIONS
FURNISHED TO NFS. A/E IS SOLELY RESPONSIBLE
(NOT NFS) FOR THE TYPE, SIZE, LOCATION, AND
SUITABILITY OF ALL FIRE ALARMS, CONTROL PANELS,
AND OTHER DEVICES SHOWN ON THE A/E PLANS.
NFS DRAWINGS ARE TO SHOW ONLY THE WIRING
DIAGRAMS BETWEEN FIRE ALARM DEVICES AND
CONTROL PANELS. NFS IS NOT RESPONSIBLE FOR
THE INFORMATION SHOWN ON THE A/E PLANS.

HUNTSMAN CANCER HOSPITAL
UNIVERSITY OF UTAH
LEVEL 6 AND PENTHOUSE
FINAL MAP
FIRE ALARM SYSTEM

NFS

NELSON FIRE SYSTEMS
801-468-8300

DRAWN BY:	JJG
DESIGNED BY:	XXXX
CHECKED BY:	DS
DATE:	11/1/11
SCALE:	N.T.S.
PROJECT NO:	XXXX
REV NO:	XXXX
DRAWING NAME:	HUNTSMAN 6 FINAL.DWG

FIRE ALARM SYSTEM

NFS

FA-6-01

N.I.C.E.T.
LEVEL IV
CERTIFICATION
FIRE ALARM SYSTEMS
DONALD SCHULTZ
#104396