



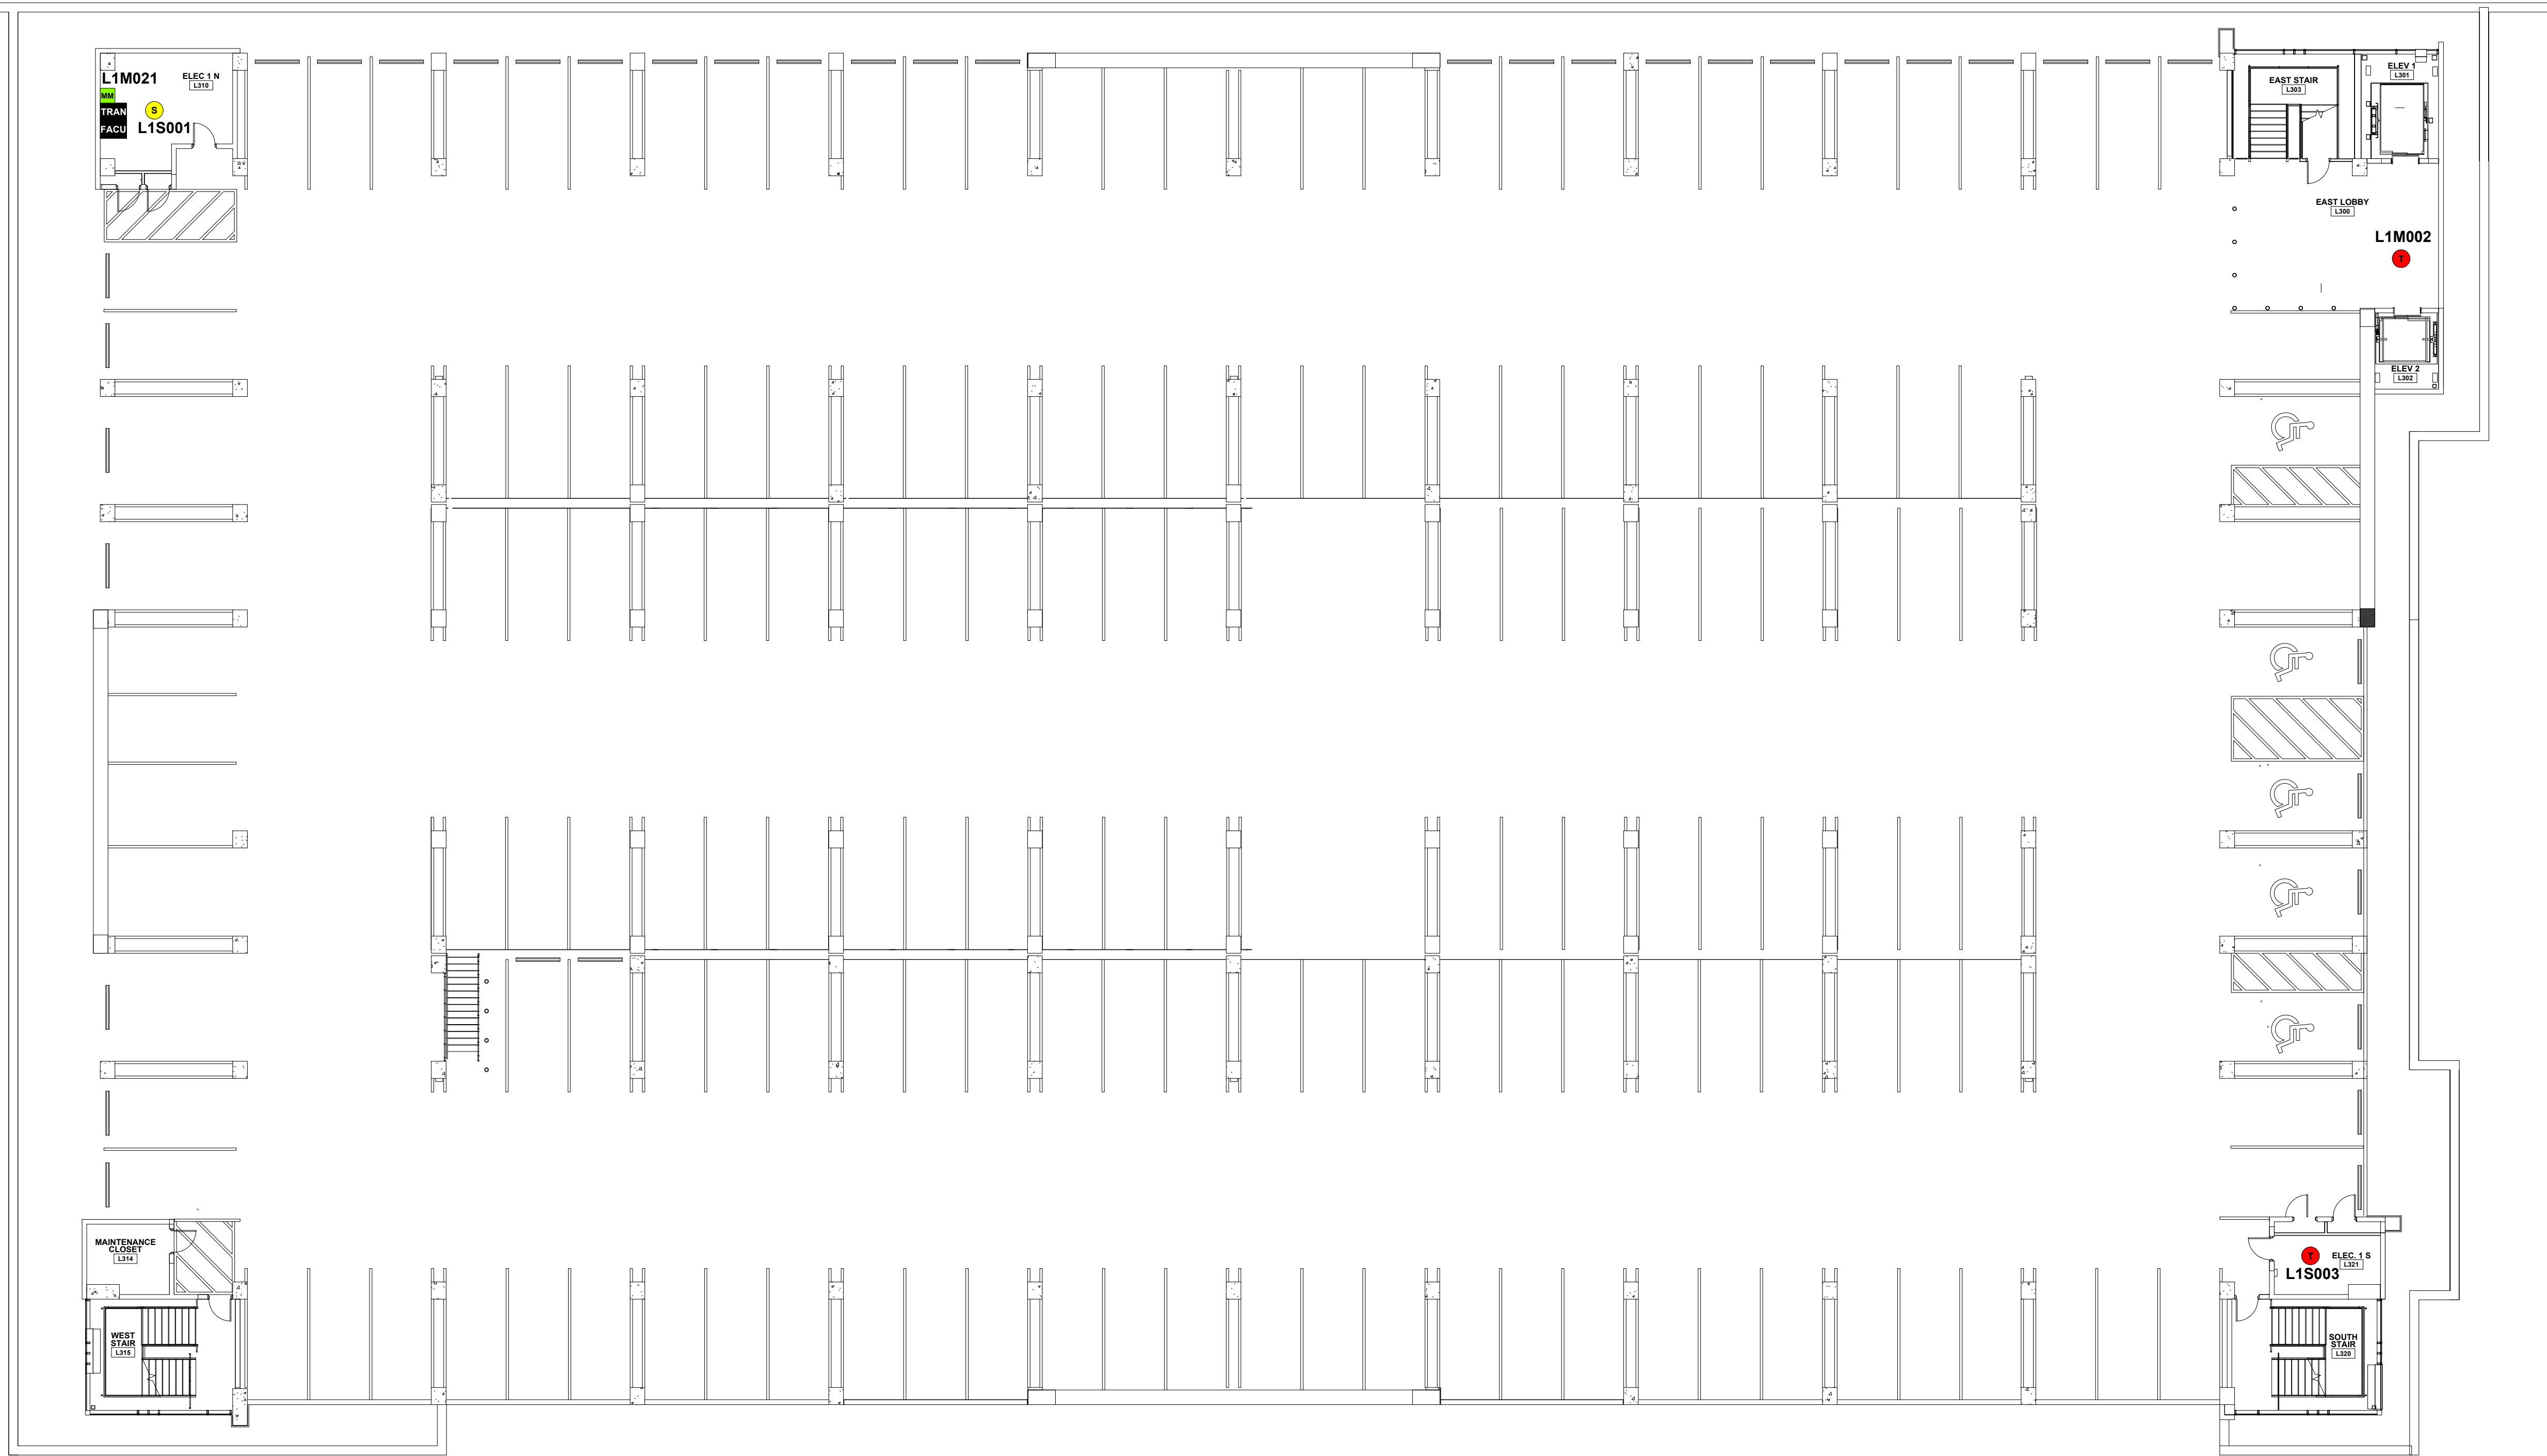

PARKING LEVEL 1

| DEVICE LEGEND |                         |
|---------------|-------------------------|
| SYMBOL        | DESCRIPTION             |
| S             | SMOKE DETECTOR          |
| H             | HEAT DETECTOR           |
| MM            | MONITOR MODULE          |
| CM            | CONTROL MODULE          |
| FACU          | FIRE ALARM CONTROL UNIT |
| TRAN          | TRANSPONDER PANEL       |

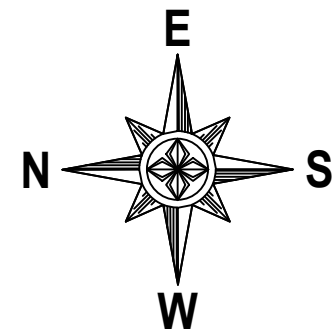

NOTE:  
NFS DRAWINGS ARE BASED ON THE PROJECT  
ARCHITECTURE/ENGINEER (A/E) PLANS AND  
SPECIFICATIONS FURNISHED TO NFS. A/E IS SOLELY  
RESPONSIBLE (NOT NFS) FOR THE TYPE, SIZE,  
LOCATION, AND SUITABILITY OF ALL FIRE ALARMS,  
CONTROL PANELS, AND OTHER DEVICES SHOWN ON  
THE A/E PLANS. NFS DRAWINGS ARE TO SHOW ONLY  
THE WIRING DIAGRAMS BETWEEN FIRE ALARM  
DEVICES AND CONTROL PANELS. NFS IS NOT  
RESPONSIBLE FOR THE INFORMATION SHOWN ON THE  
A/E PLANS.

NORTH PATIENT PARKING GARAGE  
1865 EAST MEDICAL DRIVE NORTH  
SALT LAKE CITY, UTAH 84132  
FIRE ALARM SYSTEM

**NFS**

NELSON FIRE SYSTEMS  
801-468-8300

DRAWN BY: XXXX  
DESIGNED BY: XXXX  
APPROVED BY: XXXX  
DATE: 11/30/2023 8:11:23 AM  
SCALE: N.T.S.  
PROJECT NO: XXXX  
REVISION NO: XXXX  
DRAWING NAME:  
UOFU PATIENT P1.DWG


NELSON FIRE SYSTEMS

PARKING 1


PAGE:

**FINAL MAP**



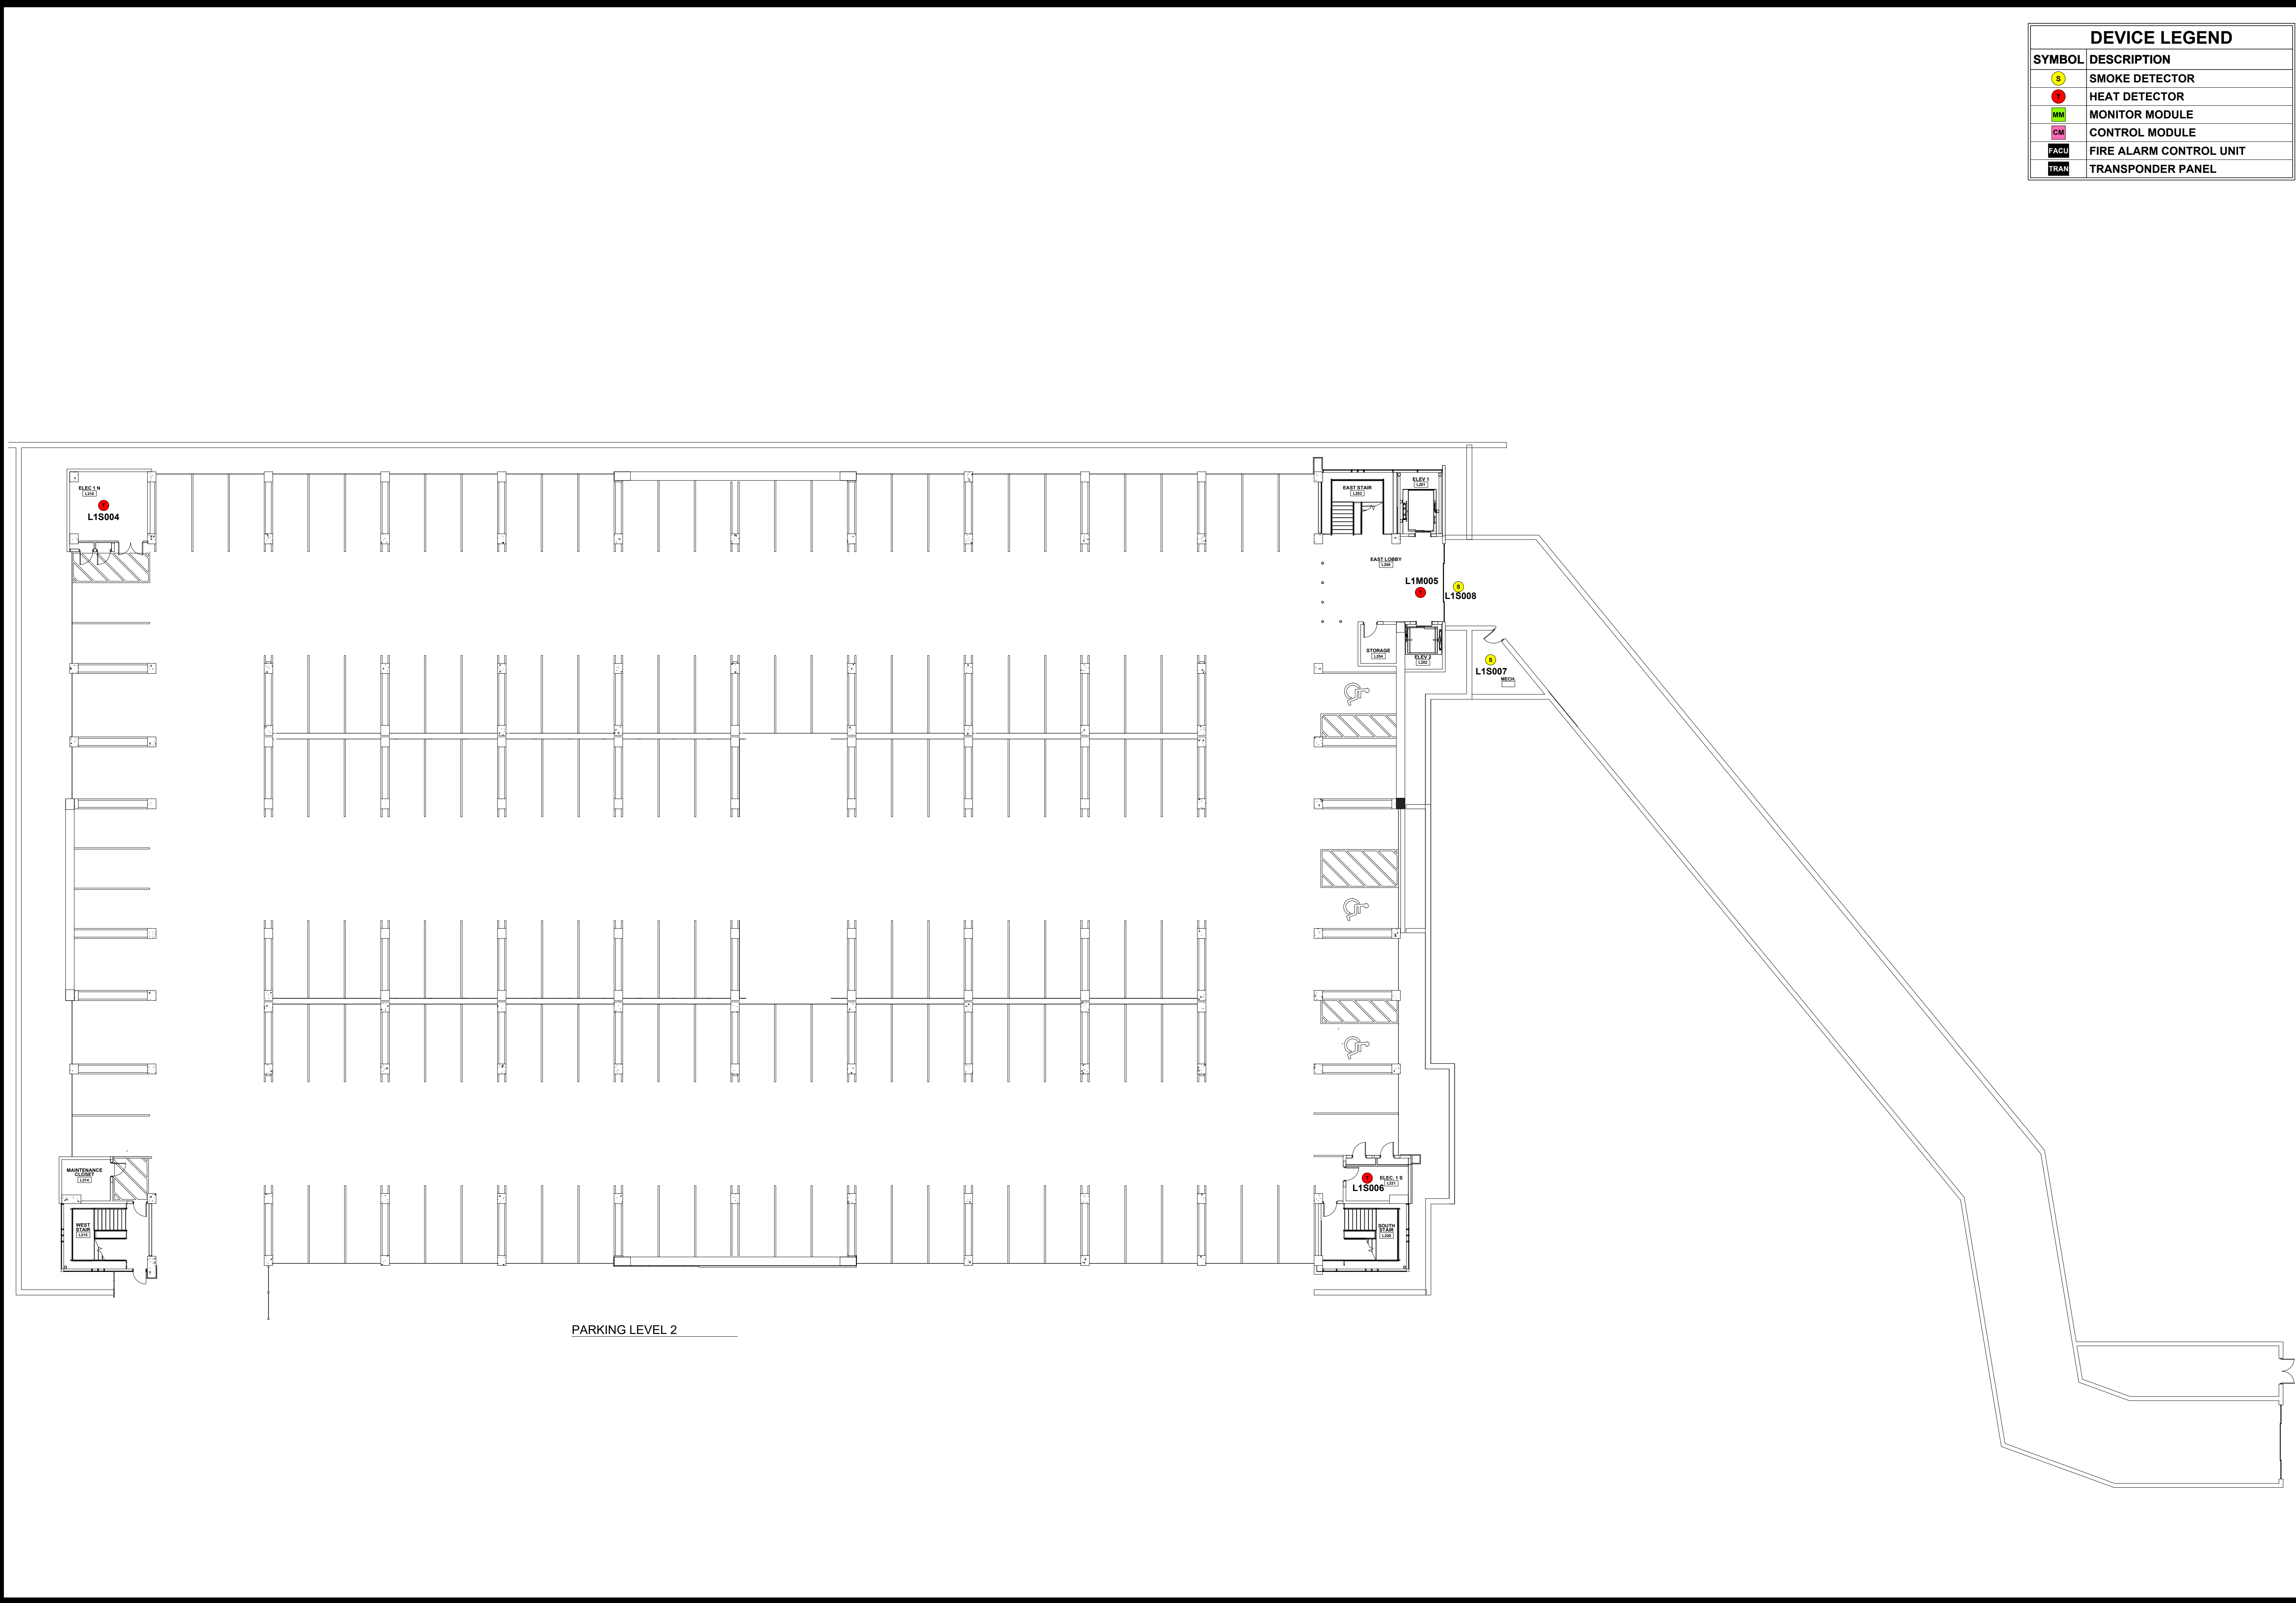

| DEVICE LEGEND |                         |
|---------------|-------------------------|
| SYMBOL        | DESCRIPTION             |
| S             | SMOKE DETECTOR          |
| H             | HEAT DETECTOR           |
| MM            | MONITOR MODULE          |
| CM            | CONTROL MODULE          |
| FACU          | FIRE ALARM CONTROL UNIT |
| TRAN          | TRANSPONDER PANEL       |

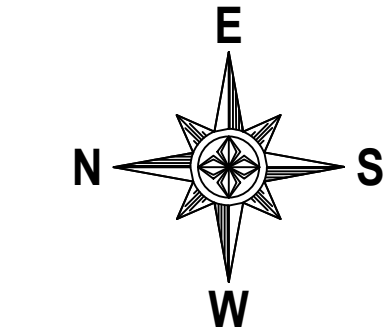

NOTE:  
NFS DRAWINGS ARE BASED ON THE PROJECT  
ARCHITECTURE/ENGINEER (A/E) PLANS AND  
SPECIFICATIONS FURNISHED TO NFS. A/E IS SOLELY  
RESPONSIBLE (NOT NFS) FOR THE TYPE, SIZE,  
LOCATION, AND SUITABILITY OF ALL FIRE ALARMS,  
CONTROL PANELS, AND OTHER DEVICES SHOWN ON  
THE A/E PLANS. NFS DRAWINGS ARE TO SHOW ONLY  
THE WIRING DIAGRAMS BETWEEN FIRE ALARM  
DEVICES AND CONTROL PANELS. NFS IS NOT  
RESPONSIBLE FOR THE INFORMATION SHOWN ON THE  
A/E PLANS.

NORTH PATIENT PARKING GARAGE  
1865 EAST MEDICAL DRIVE NORTH  
SALT LAKE CITY, UTAH 84132  
FIRE ALARM SYSTEM

**NFS**

NELSON FIRE SYSTEMS  
801-468-8300

DRAWN BY: XXXX  
DESIGNED BY: XXXX  
APPROVED BY: XXXX  
DATE: 11/30/2023 8:11:14 AM  
SCALE: N.T.S.  
PROJECT NO: XXXX  
REVISION NO: XXXX  
DRAWING NAME:  
UOFU PATIENT P2.DWG


NELSON FIRE SYSTEMS

PARKING 2


PAGE:

**FINAL MAP**



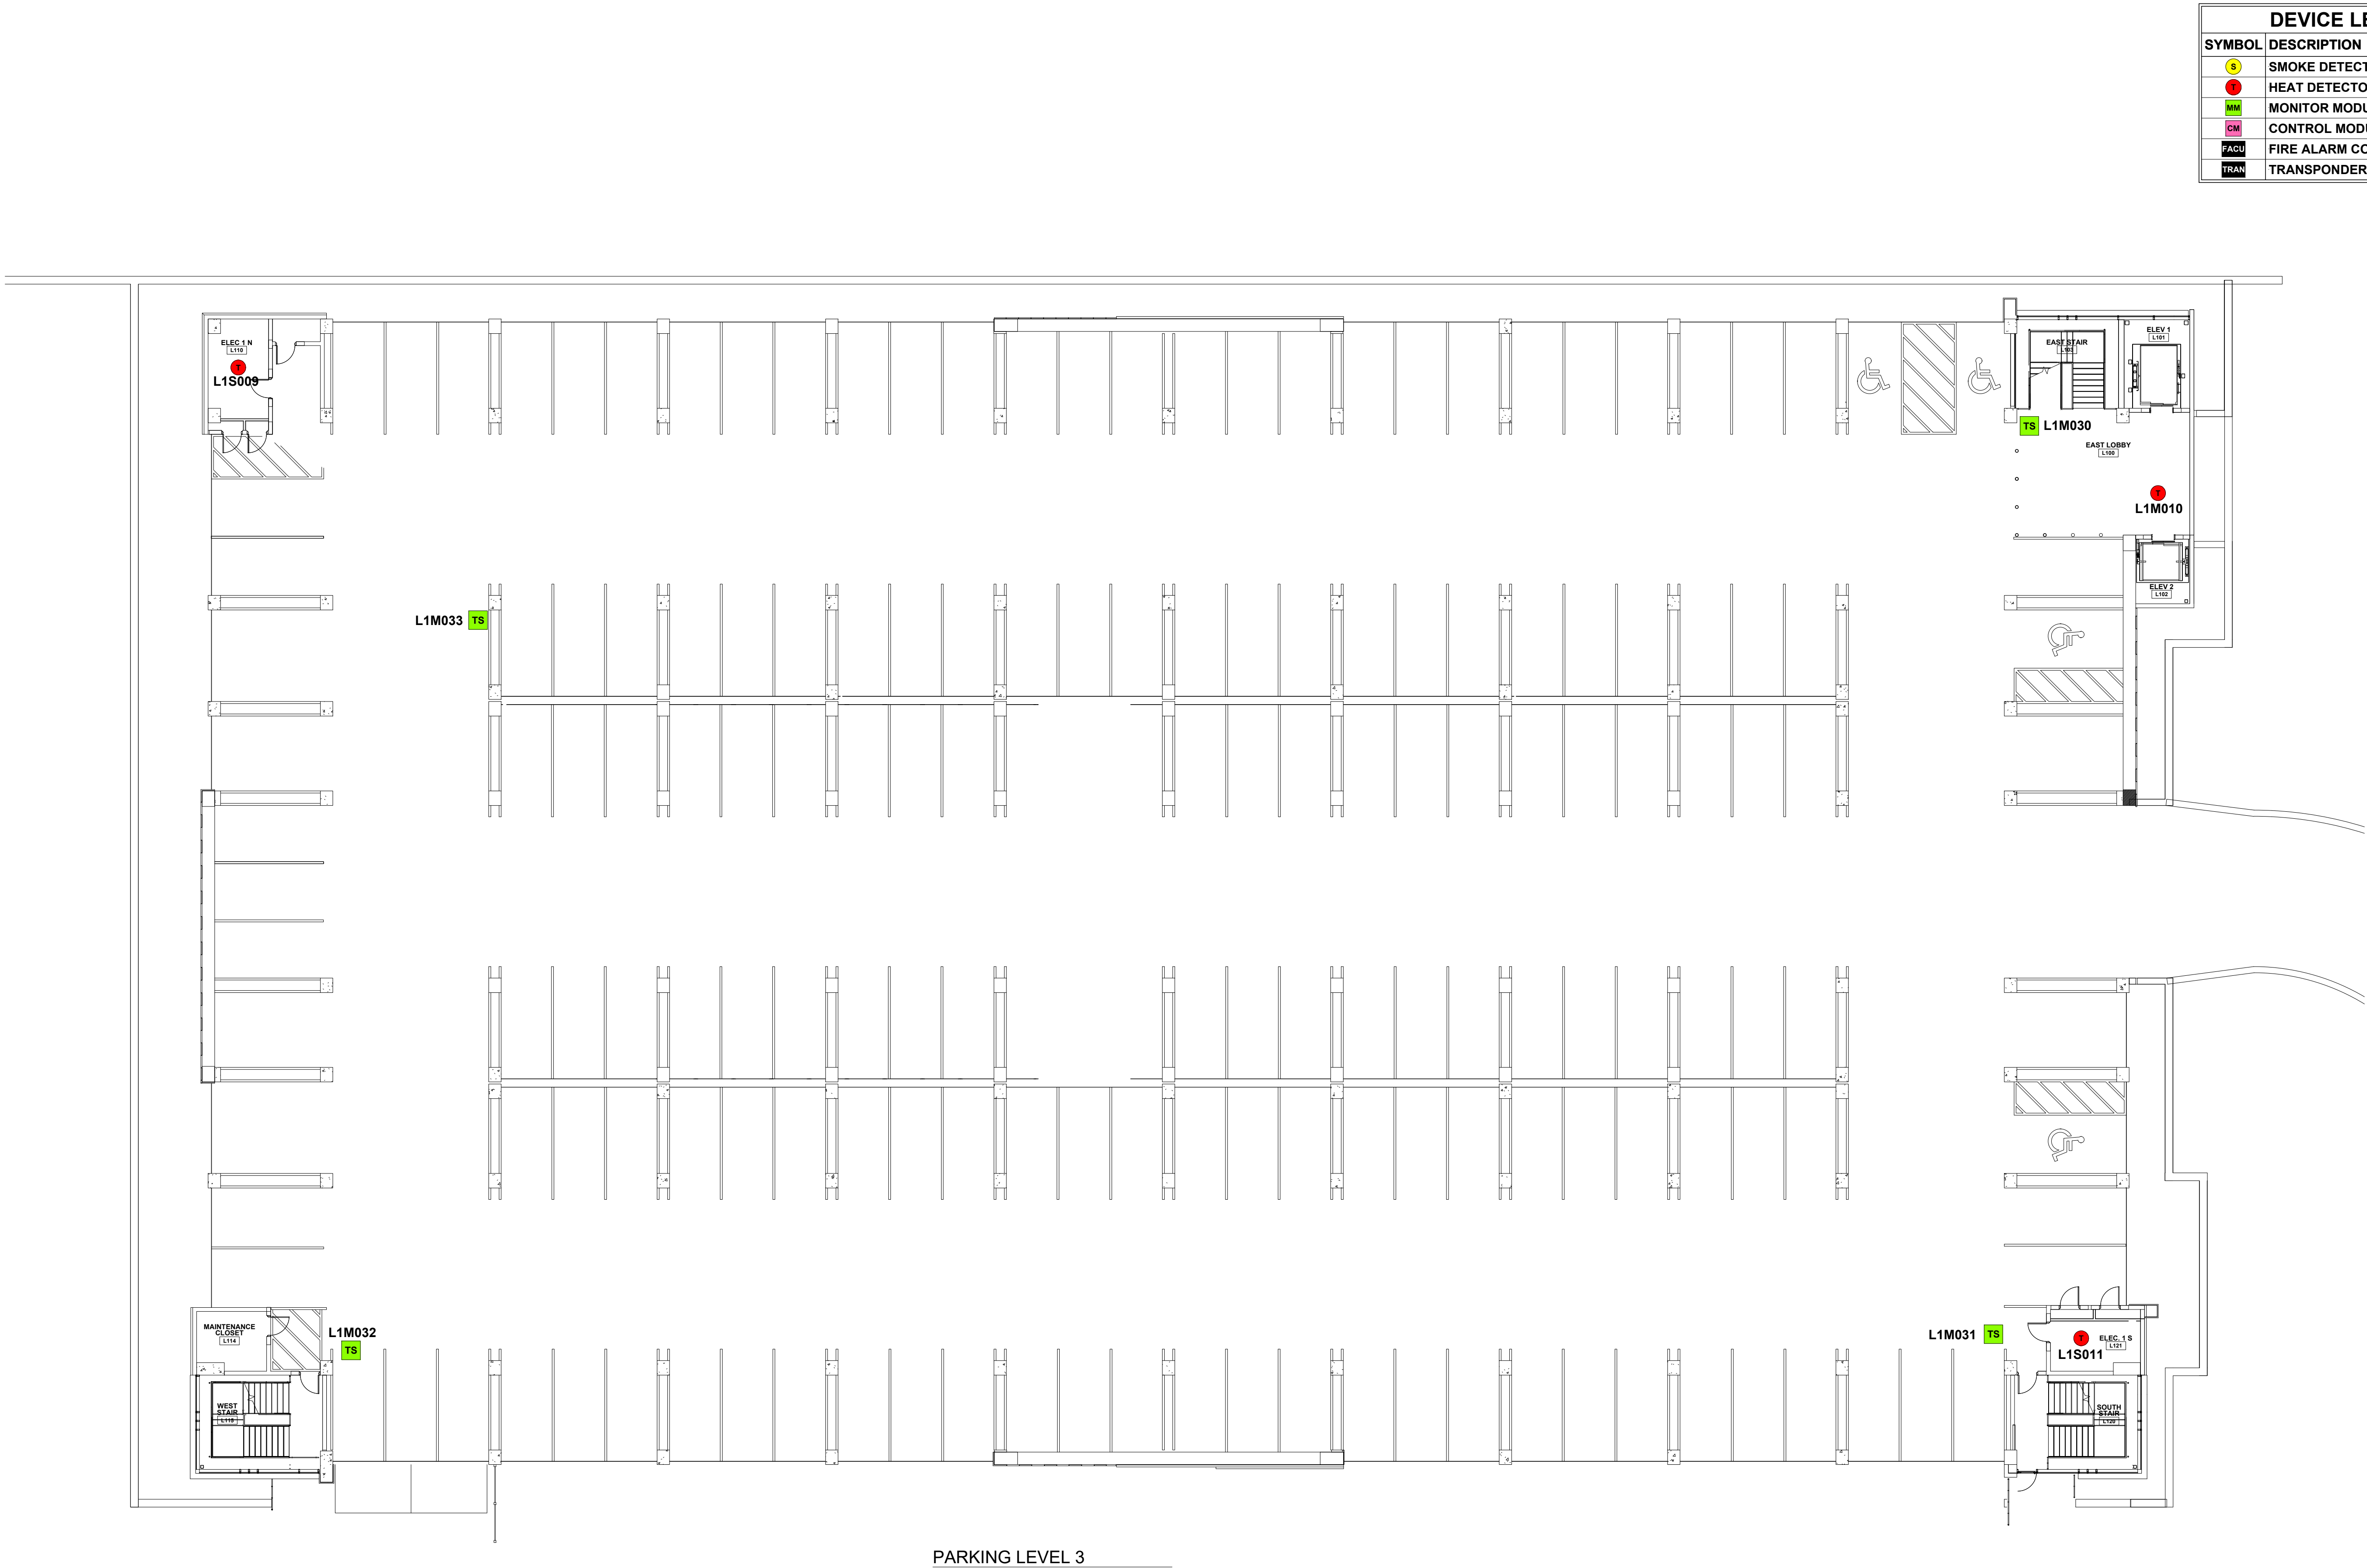

| DEVICE LEGEND |                         |
|---------------|-------------------------|
| SYMBOL        | DESCRIPTION             |
|               | SMOKE DETECTOR          |
|               | HEAT DETECTOR           |
|               | MONITOR MODULE          |
|               | CONTROL MODULE          |
|               | FIRE ALARM CONTROL UNIT |
|               | TRANSPONDER PANEL       |

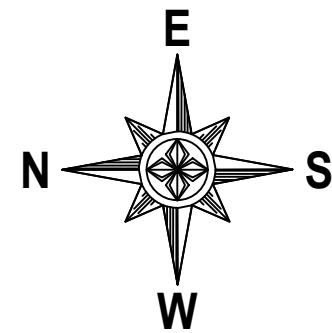

NOTE:  
NFS DRAWINGS ARE BASED ON THE PROJECT  
ARCHITECTURE/ENGINEER (A/E) PLANS AND  
SPECIFICATIONS FURNISHED TO NFS. A/E IS SOLELY  
RESPONSIBLE (NOT NFS) FOR THE TYPE, SIZE,  
LOCATION, AND SUITABILITY OF ALL FIRE ALARMS,  
CONTROL PANELS, AND OTHER DEVICES SHOWN ON  
THE A/E PLANS. NFS DRAWINGS ARE TO SHOW ONLY  
THE WIRING DIAGRAMS BETWEEN FIRE ALARM  
DEVICES AND CONTROL PANELS. NFS IS NOT  
RESPONSIBLE FOR THE INFORMATION SHOWN ON THE  
A/E PLANS.

NORTH PATIENT PARKING GARAGE  
1865 EAST MEDICAL DRIVE NORTH  
SALT LAKE CITY, UTAH 84132  
FIRE ALARM SYSTEM

**NFS**

NELSON FIRE SYSTEMS  
801-468-8300

DRAWN BY: XXXX  
DESIGNED BY: XXXX  
APPROVED BY: XXXX  
DATE: 2/26/2024 2:24:35 PM  
SCALE: N.T.S.  
PROJECT NO: XXXX  
REVISION NO: XXXX  
DRAWING NAME:  
UOFU PATIENT P3.DWG


NELSON FIRE SYSTEMS

PARKING 3


PAGE:

**FINAL MAP**



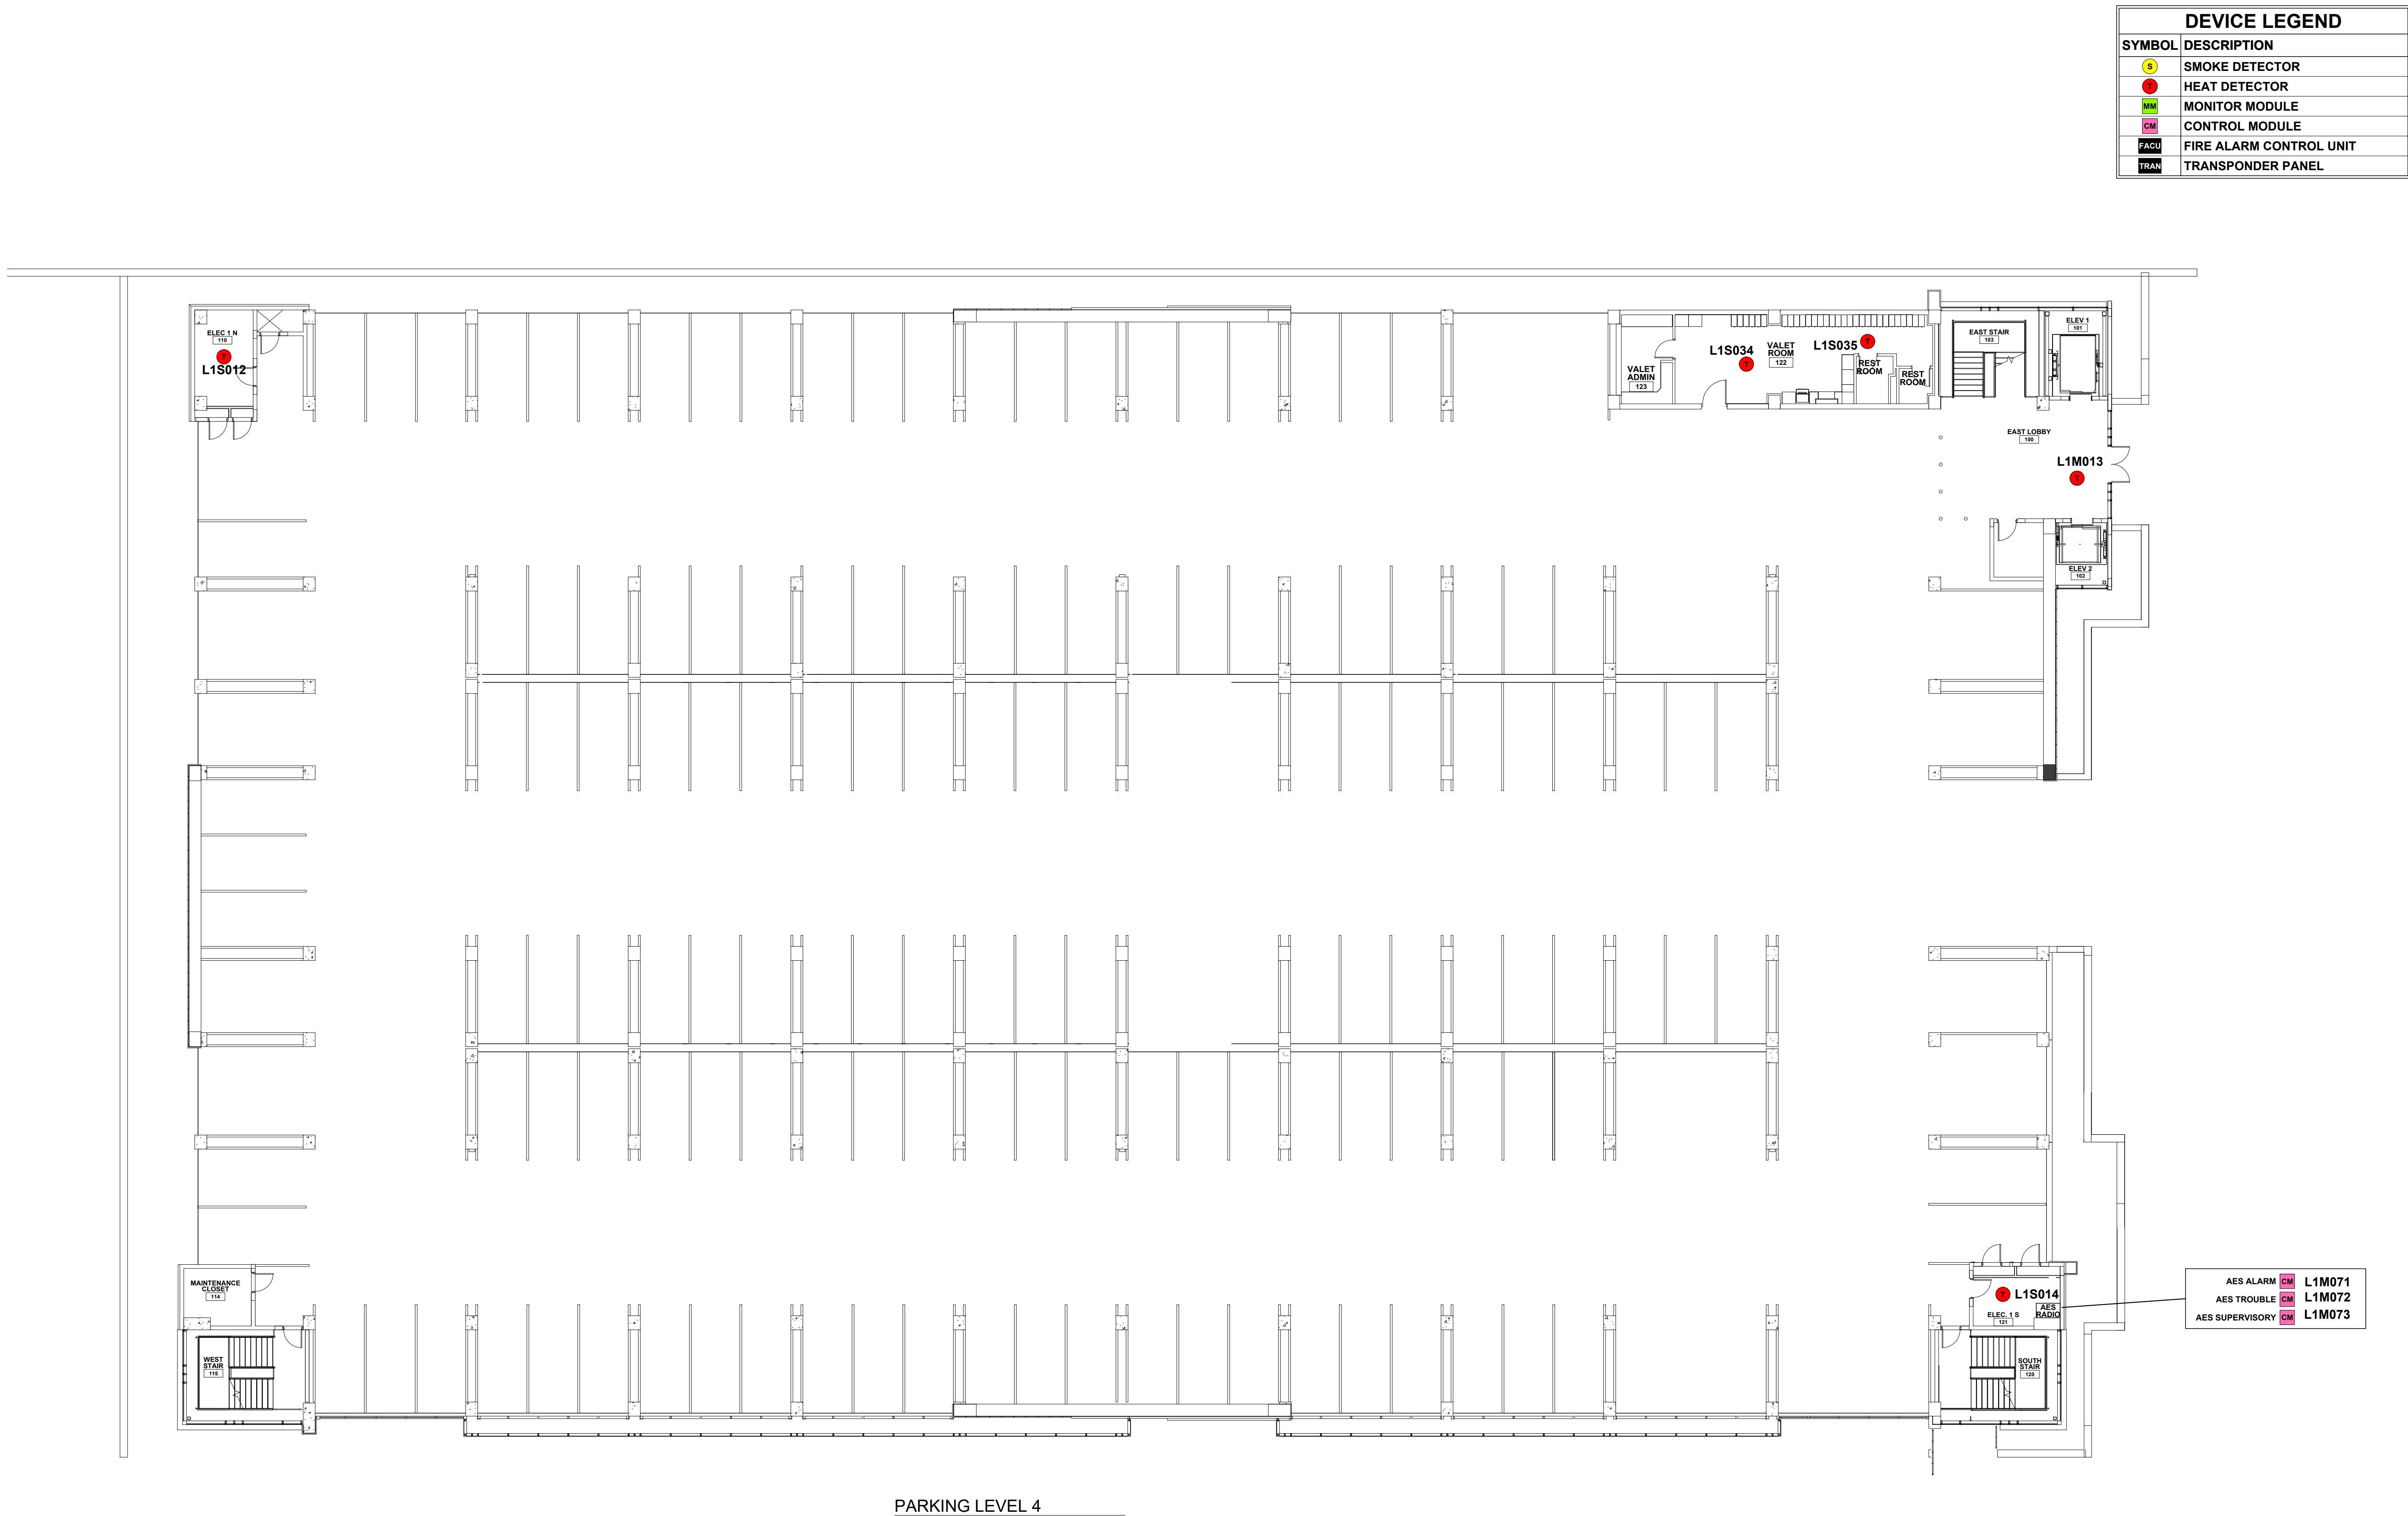

PARKING LEVEL 4

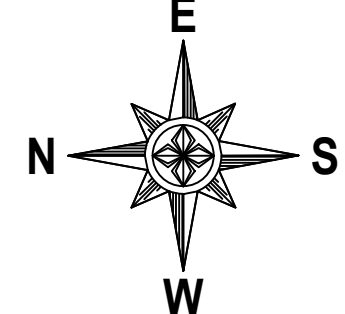

NOTE:  
NFS DRAWINGS ARE BASED ON THE PROJECT ARCHITECTURE/ENGINEER (A/E) PLANS AND SPECIFICATIONS FURNISHED TO NFS. A/E IS SOLELY RESPONSIBLE (NOT NFS) FOR THE TYPE, SIZE, LOCATION, AND SUITABILITY OF ALL FIRE ALARMS, CONTROL PANELS, AND OTHER DEVICES SHOWN ON THE A/E PLANS. NFS DRAWINGS ARE TO SHOW ONLY THE WIRING DIAGRAMS BETWEEN FIRE ALARM DEVICES AND CONTROL PANELS. NFS IS NOT RESPONSIBLE FOR THE INFORMATION SHOWN ON THE A/E PLANS.

NORTH PATIENT PARKING GARAGE  
1865 EAST MEDICAL DRIVE NORTH  
SALT LAKE CITY, UTAH 84132  
FIRE ALARM SYSTEM


**NFS**  
NELSON FIRE SYSTEMS  
801-468-8300

DRAWN BY: XXXX  
DESIGNED BY: XXXX  
APPROVED BY: XXXX  
DATE: 11/30/2023 8:11:10 AM  
SCALE: N.T.S.  
PROJECT NO: XXXX  
REVISION NO: XXXX  
DRAWING NAME:  
UOFU PATIENT P4.DWG

NELSON FIRE SYSTEMS  
PARKING 4

PAGE:  
**FINAL MAP**



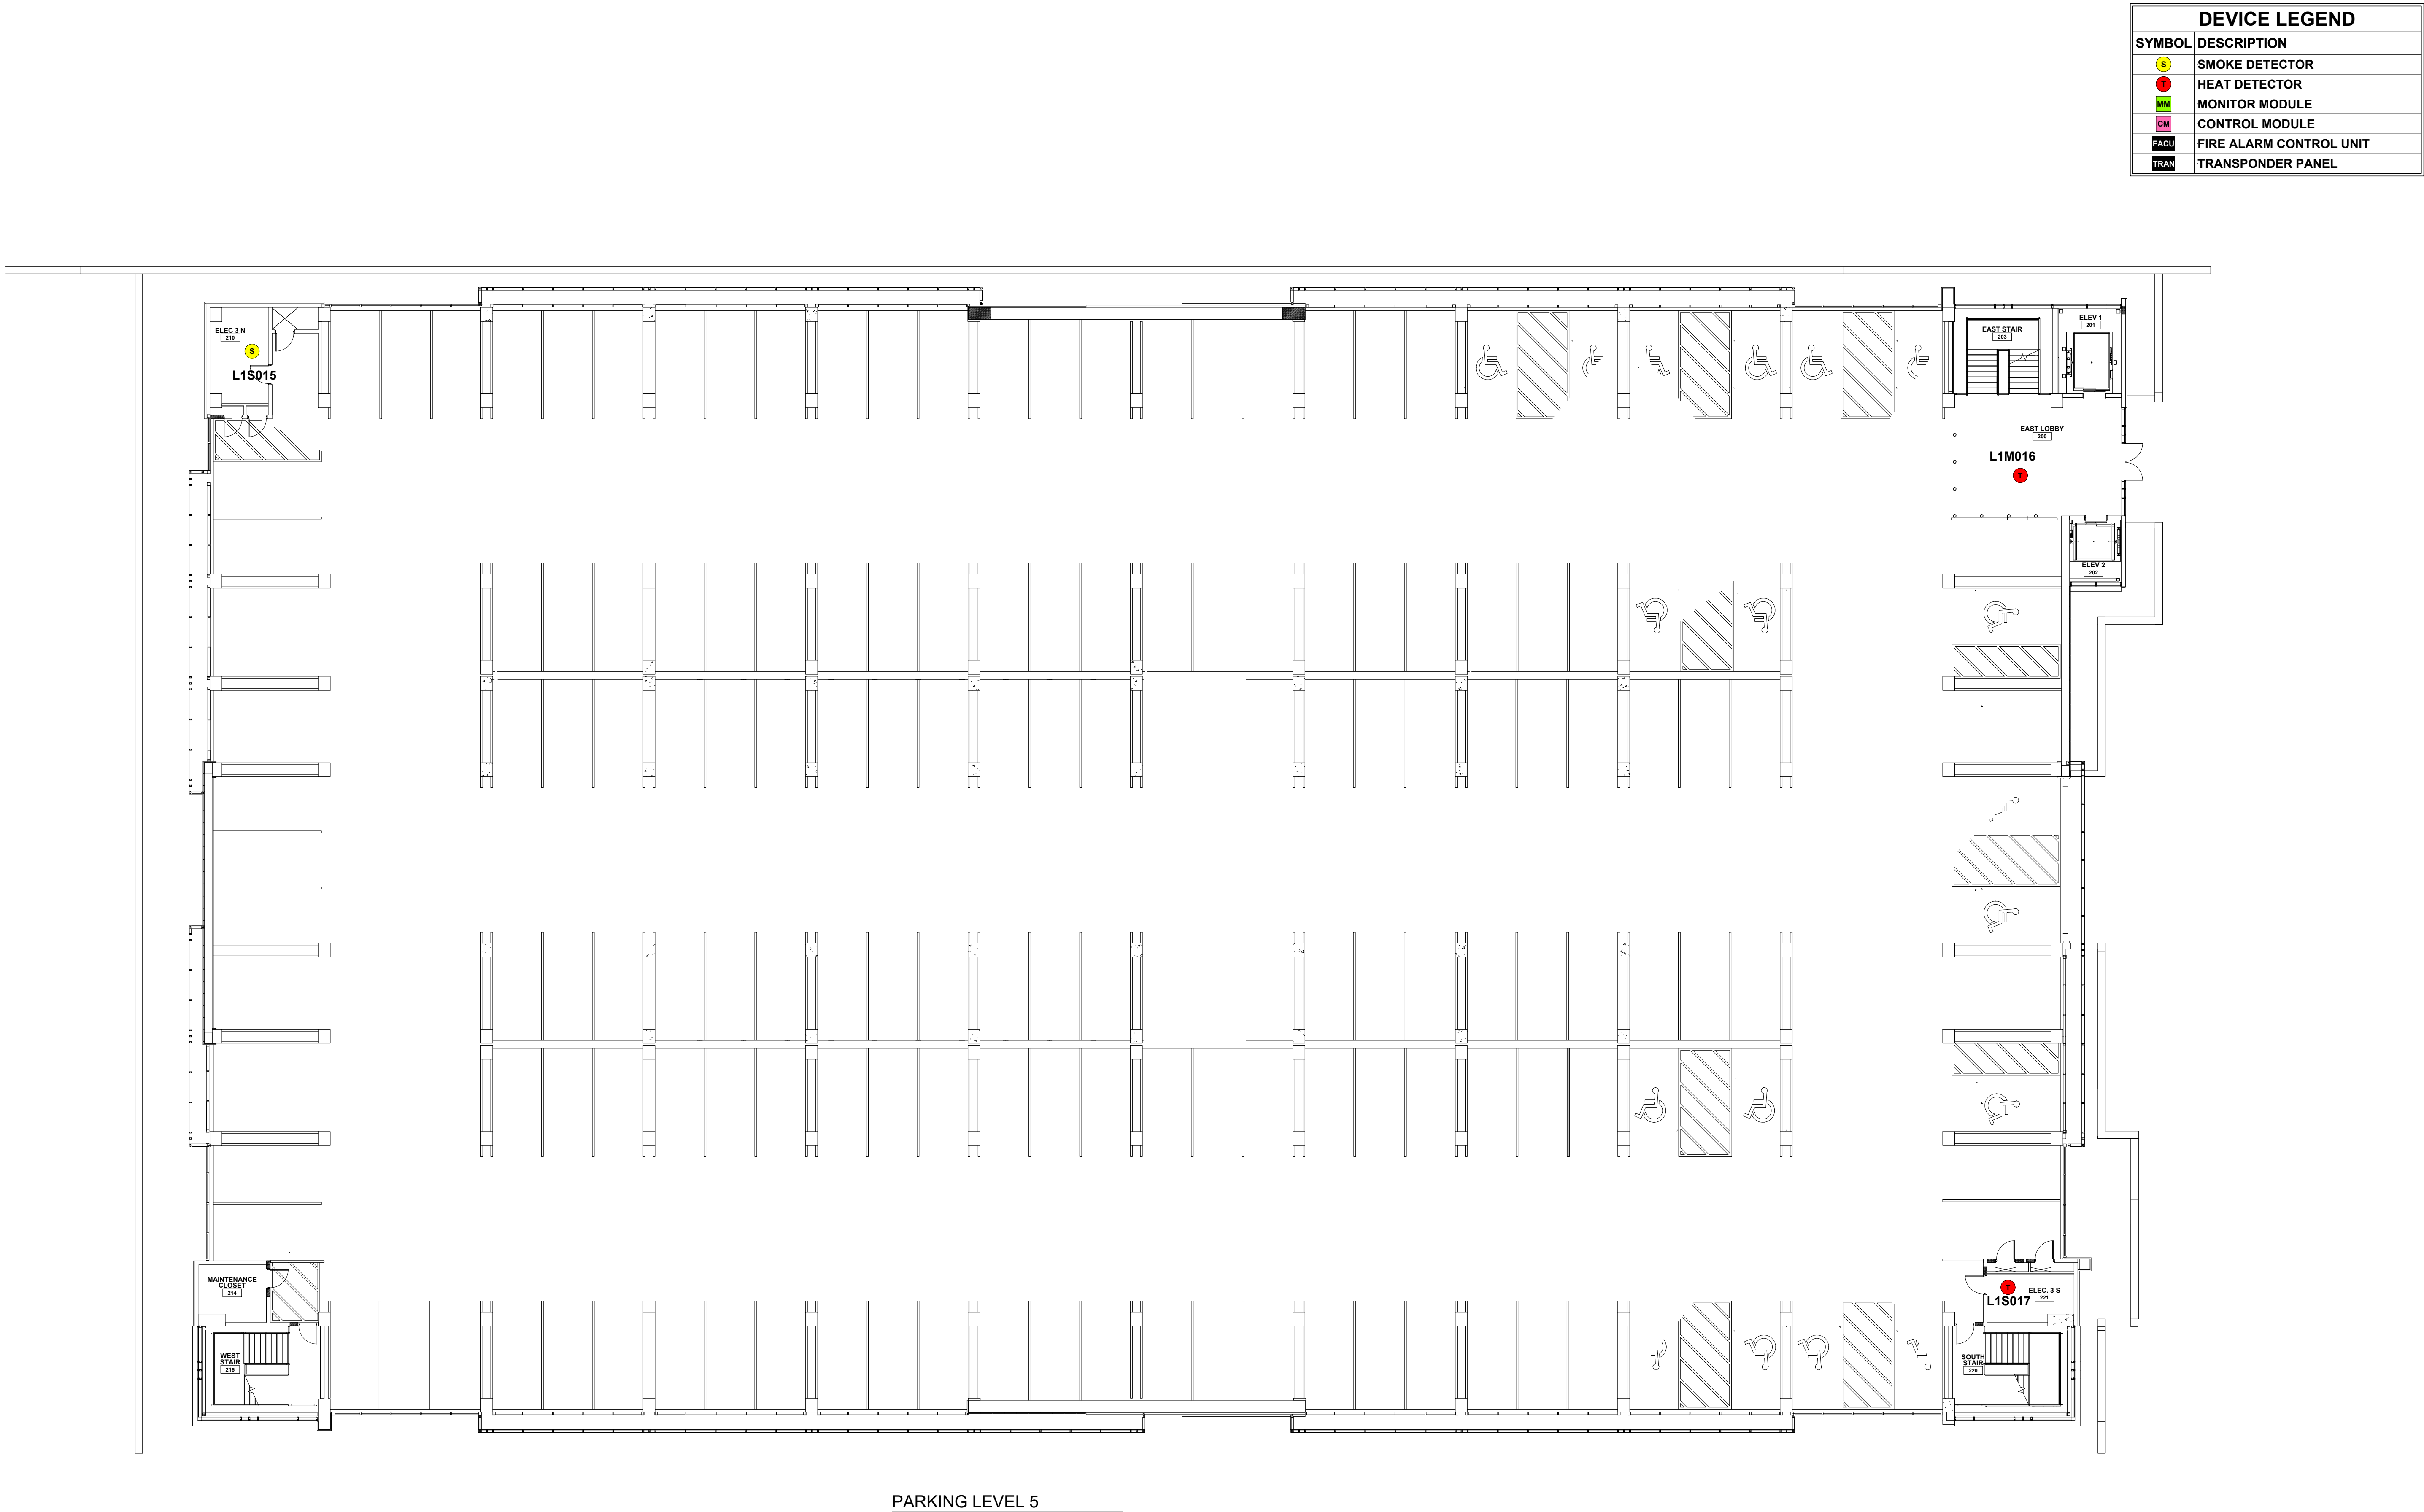

| DEVICE LEGEND |                         |
|---------------|-------------------------|
| SYMBOL        | DESCRIPTION             |
| S             | SMOKE DETECTOR          |
| ●             | HEAT DETECTOR           |
| MM            | MONITOR MODULE          |
| CM            | CONTROL MODULE          |
| FACU          | FIRE ALARM CONTROL UNIT |
| TRAN          | TRANSPONDER PANEL       |

NOTE:  
NFS DRAWINGS ARE BASED ON THE PROJECT ARCHITECTURE/ENGINEER (A/E) PLANS AND SPECIFICATIONS FURNISHED TO NFS. A/E IS SOLELY RESPONSIBLE (NOT NFS) FOR THE TYPE, SIZE, LOCATION, AND SUITABILITY OF ALL FIRE ALARMS, CONTROL PANELS, AND OTHER DEVICES SHOWN ON THE A/E PLANS. NFS DRAWINGS ARE TO SHOW ONLY THE WIRING DIAGRAMS BETWEEN FIRE ALARM DEVICES AND CONTROL PANELS. NFS IS NOT RESPONSIBLE FOR THE INFORMATION SHOWN ON THE A/E PLANS.

NORTH PATIENT PARKING GARAGE  
1865 EAST MEDICAL DRIVE NORTH  
SALT LAKE CITY, UTAH 84132  
FIRE ALARM SYSTEM

NFS


NELSON FIRE SYSTEMS  
801-468-8300

|               |                       |
|---------------|-----------------------|
| DRAWN BY:     | XXXX                  |
| DESIGNED BY:  | XXXX                  |
| APPROVED BY:  | XXXX                  |
| DATE:         | 11/30/2023 8:11:07 AM |
| SCALE:        | N.T.S.                |
| PROJECT NO:   | XXXX                  |
| REVISION NO:  | XXXX                  |
| DRAWING NAME: | UOFU PATIENT P5.DWG   |

NELSON FIRE SYSTEMS  
PARKING 5


PAGE:  
FINAL MAP



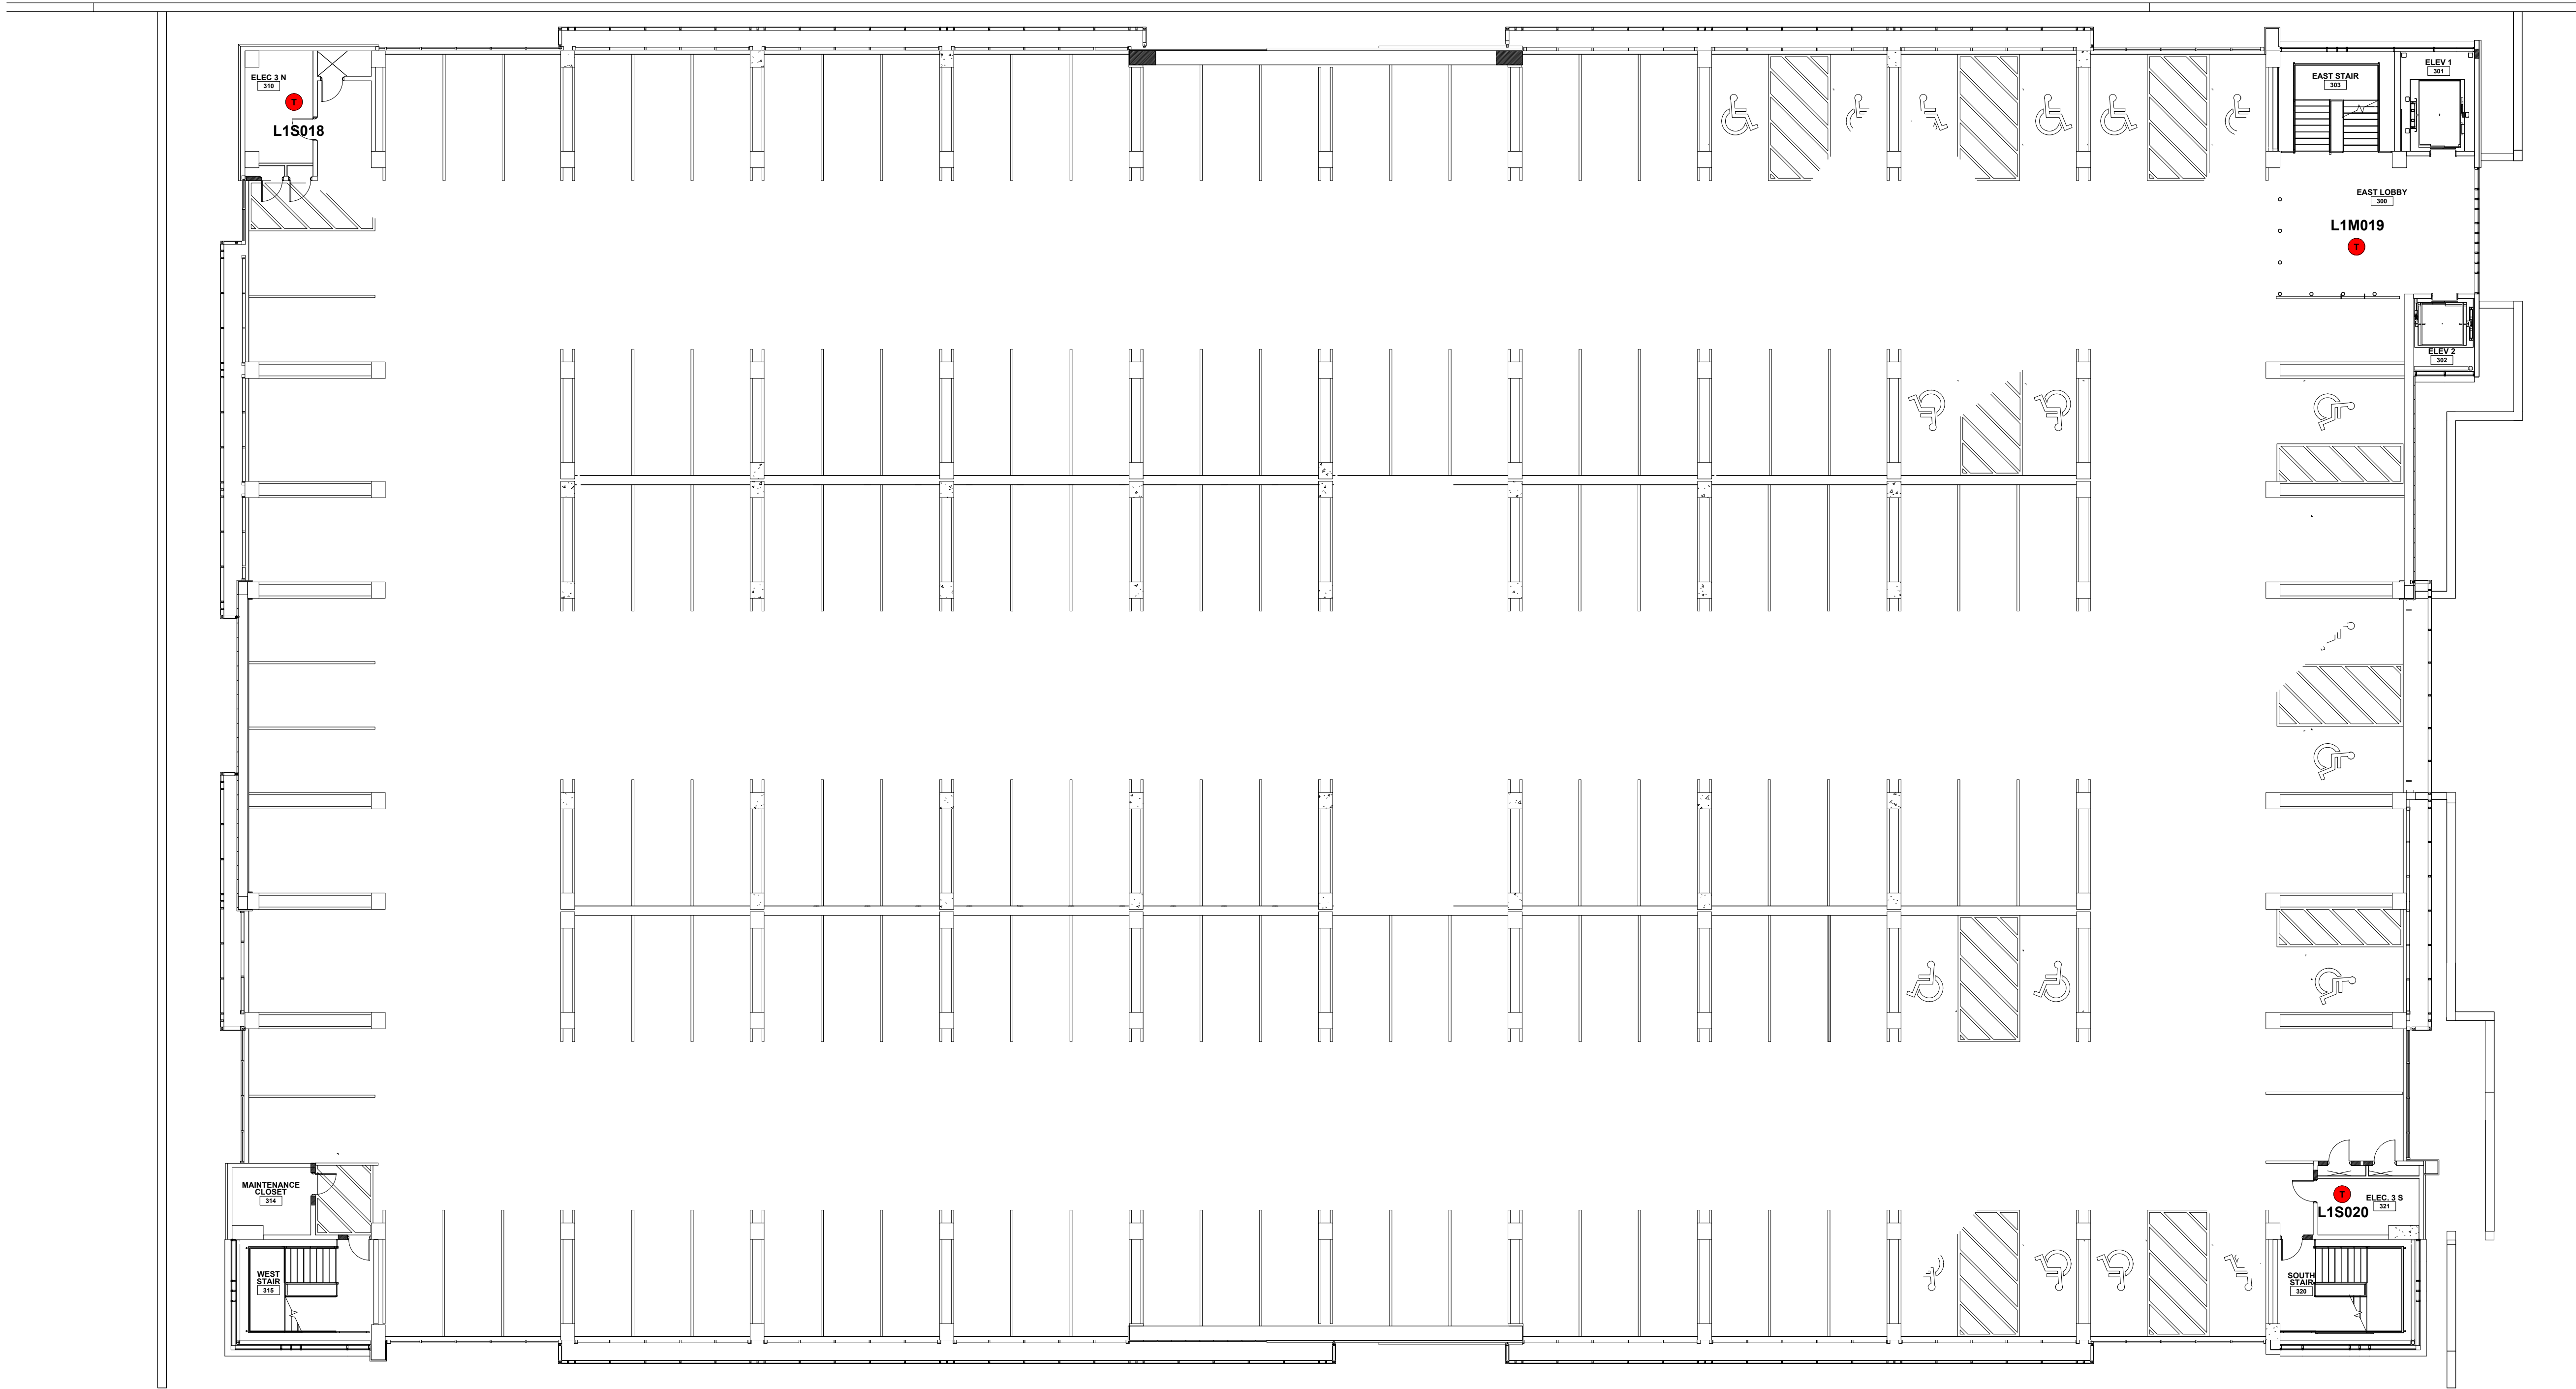

PARKING LEVEL 6

| DEVICE LEGEND |                         |
|---------------|-------------------------|
| SYMBOL        | DESCRIPTION             |
|               | SMOKE DETECTOR          |
|               | HEAT DETECTOR           |
|               | MONITOR MODULE          |
|               | CONTROL MODULE          |
|               | FIRE ALARM CONTROL UNIT |
|               | TRANSPONDER PANEL       |

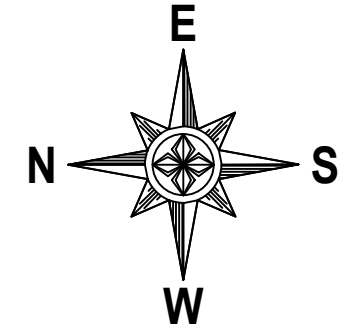

NOTE:  
NFS DRAWINGS ARE BASED ON THE PROJECT  
ARCHITECTURE/ENGINEER (A/E) PLANS AND  
SPECIFICATIONS FURNISHED TO NFS. A/E IS SOLELY  
RESPONSIBLE (NOT NFS) FOR THE TYPE, SIZE,  
LOCATION, AND SUITABILITY OF ALL FIRE ALARMS,  
CONTROL PANELS, AND OTHER DEVICES SHOWN ON  
THE A/E PLANS. NFS DRAWINGS ARE TO SHOW ONLY  
THE WIRING DIAGRAMS BETWEEN FIRE ALARM  
DEVICES AND CONTROL PANELS. NFS IS NOT  
RESPONSIBLE FOR THE INFORMATION SHOWN ON THE  
A/E PLANS.

NORTH PATIENT PARKING GARAGE  
1865 EAST MEDICAL DRIVE NORTH  
SALT LAKE CITY, UTAH 84132  
FIRE ALARM SYSTEM

**NFS**

NELSON FIRE SYSTEMS  
801-468-8300

DRAWN BY: XXXX  
DESIGNED BY: XXXX  
APPROVED BY: XXXX  
DATE: 11/30/2023 8:11:04 AM  
SCALE: N.T.S.  
PROJECT NO: XXXX  
REVISION NO: XXXX  
DRAWING NAME:  
UOFU PATIENT P6.DWG


NELSON FIRE SYSTEMS

PARKING 6

PAGE:

**FINAL MAP**



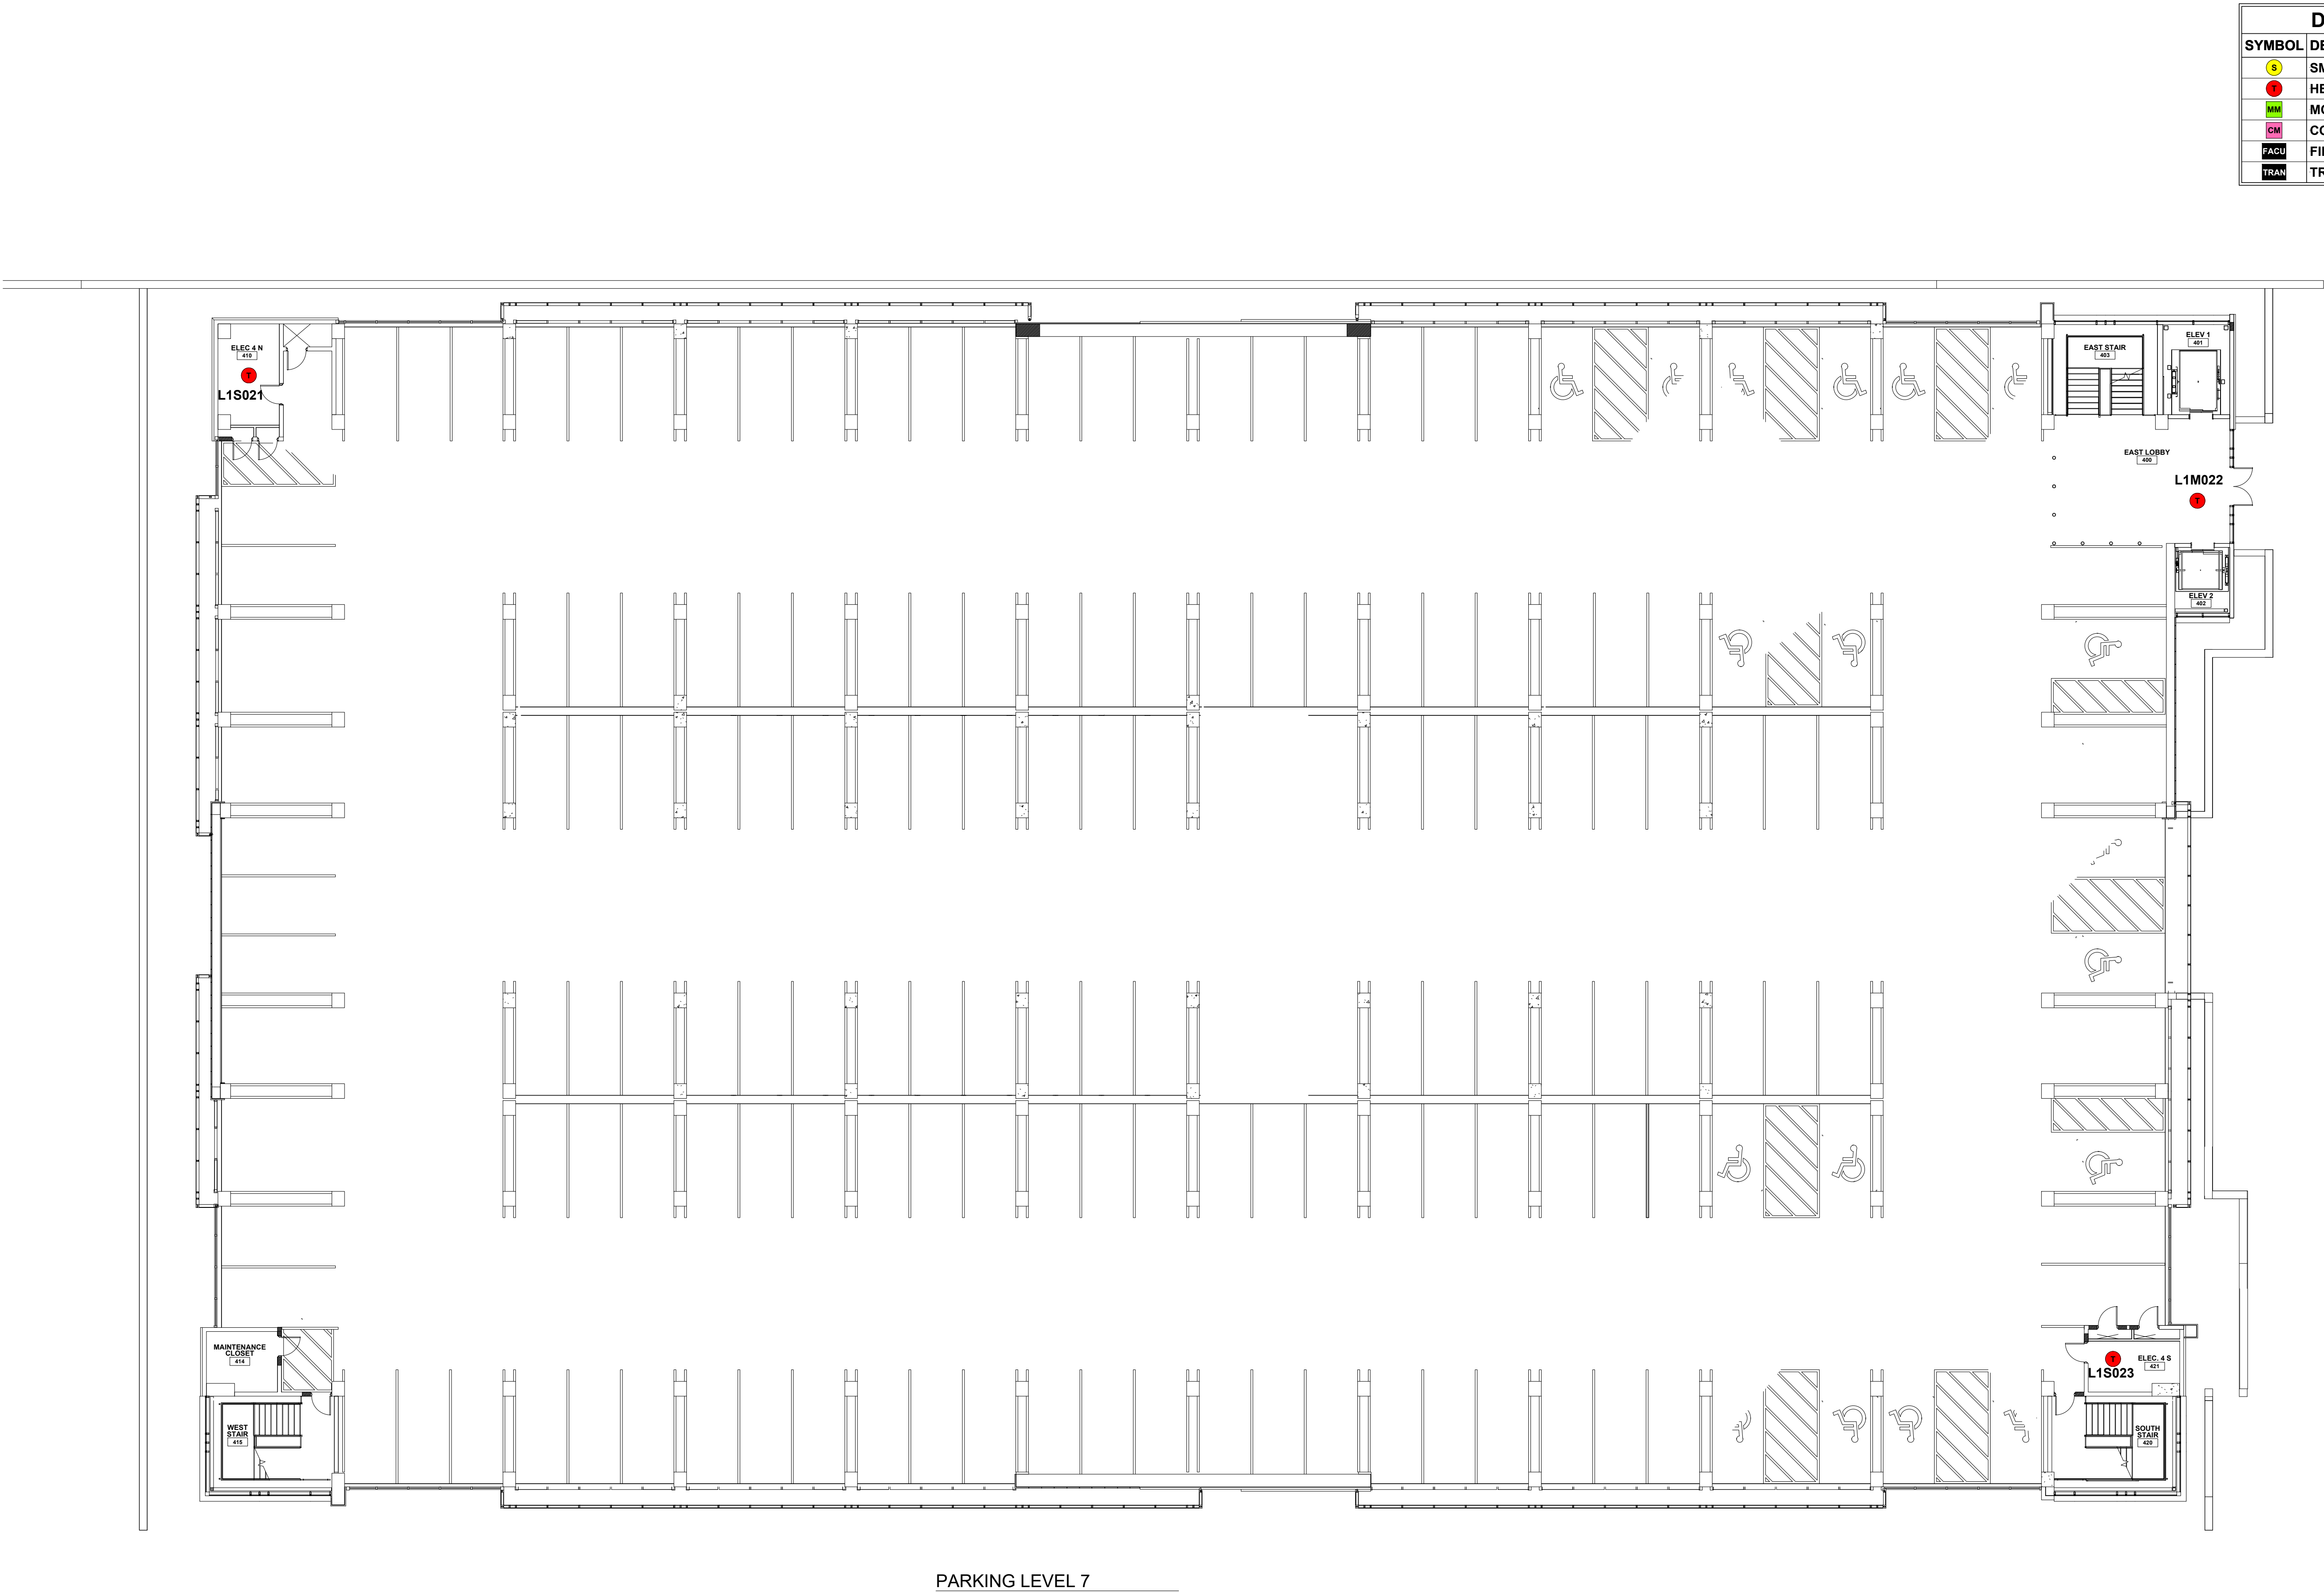

PARKING LEVEL 7

| DEVICE LEGEND |                         |
|---------------|-------------------------|
| SYMBOL        | DESCRIPTION             |
| S             | SMOKE DETECTOR          |
| H             | HEAT DETECTOR           |
| MM            | MONITOR MODULE          |
| CM            | CONTROL MODULE          |
| FACU          | FIRE ALARM CONTROL UNIT |
| TRAN          | TRANSPONDER PANEL       |

NOTE:  
NFS DRAWINGS ARE BASED ON THE PROJECT  
ARCHITECTURE/ENGINEER (A/E) PLANS AND  
SPECIFICATIONS FURNISHED TO NFS. A/E IS SOLELY  
RESPONSIBLE (NOT NFS) FOR THE TYPE, SIZE,  
LOCATION, AND SUITABILITY OF ALL FIRE ALARMS,  
CONTROL PANELS, AND OTHER DEVICES SHOWN ON  
THE A/E PLANS. NFS DRAWINGS ARE TO SHOW ONLY  
THE WIRING DIAGRAMS BETWEEN FIRE ALARM  
DEVICES AND CONTROL PANELS. NFS IS NOT  
RESPONSIBLE FOR THE INFORMATION SHOWN ON THE  
A/E PLANS.

NORTH PATIENT PARKING GARAGE  
1865 EAST MEDICAL DRIVE NORTH  
SALT LAKE CITY, UTAH 84132  
FIRE ALARM SYSTEM

|                     |                       |
|---------------------|-----------------------|
| NFS                 |                       |
| NELSON FIRE SYSTEMS |                       |
| 801-468-8300        |                       |
| DRAWN BY:           | XXXX                  |
| DESIGNED BY:        | XXXX                  |
| APPROVED BY:        | XXXX                  |
| DATE:               | 11/30/2023 8:11:02 AM |
| SCALE:              | N.T.S.                |
| PROJECT NO:         | XXXX                  |
| REVISION NO:        | XXXX                  |
| DRAWING NAME:       | UOFU PATIENT P7.DWG   |


NELSON FIRE SYSTEMS

PARKING 7

PAGE:


FINAL MAP



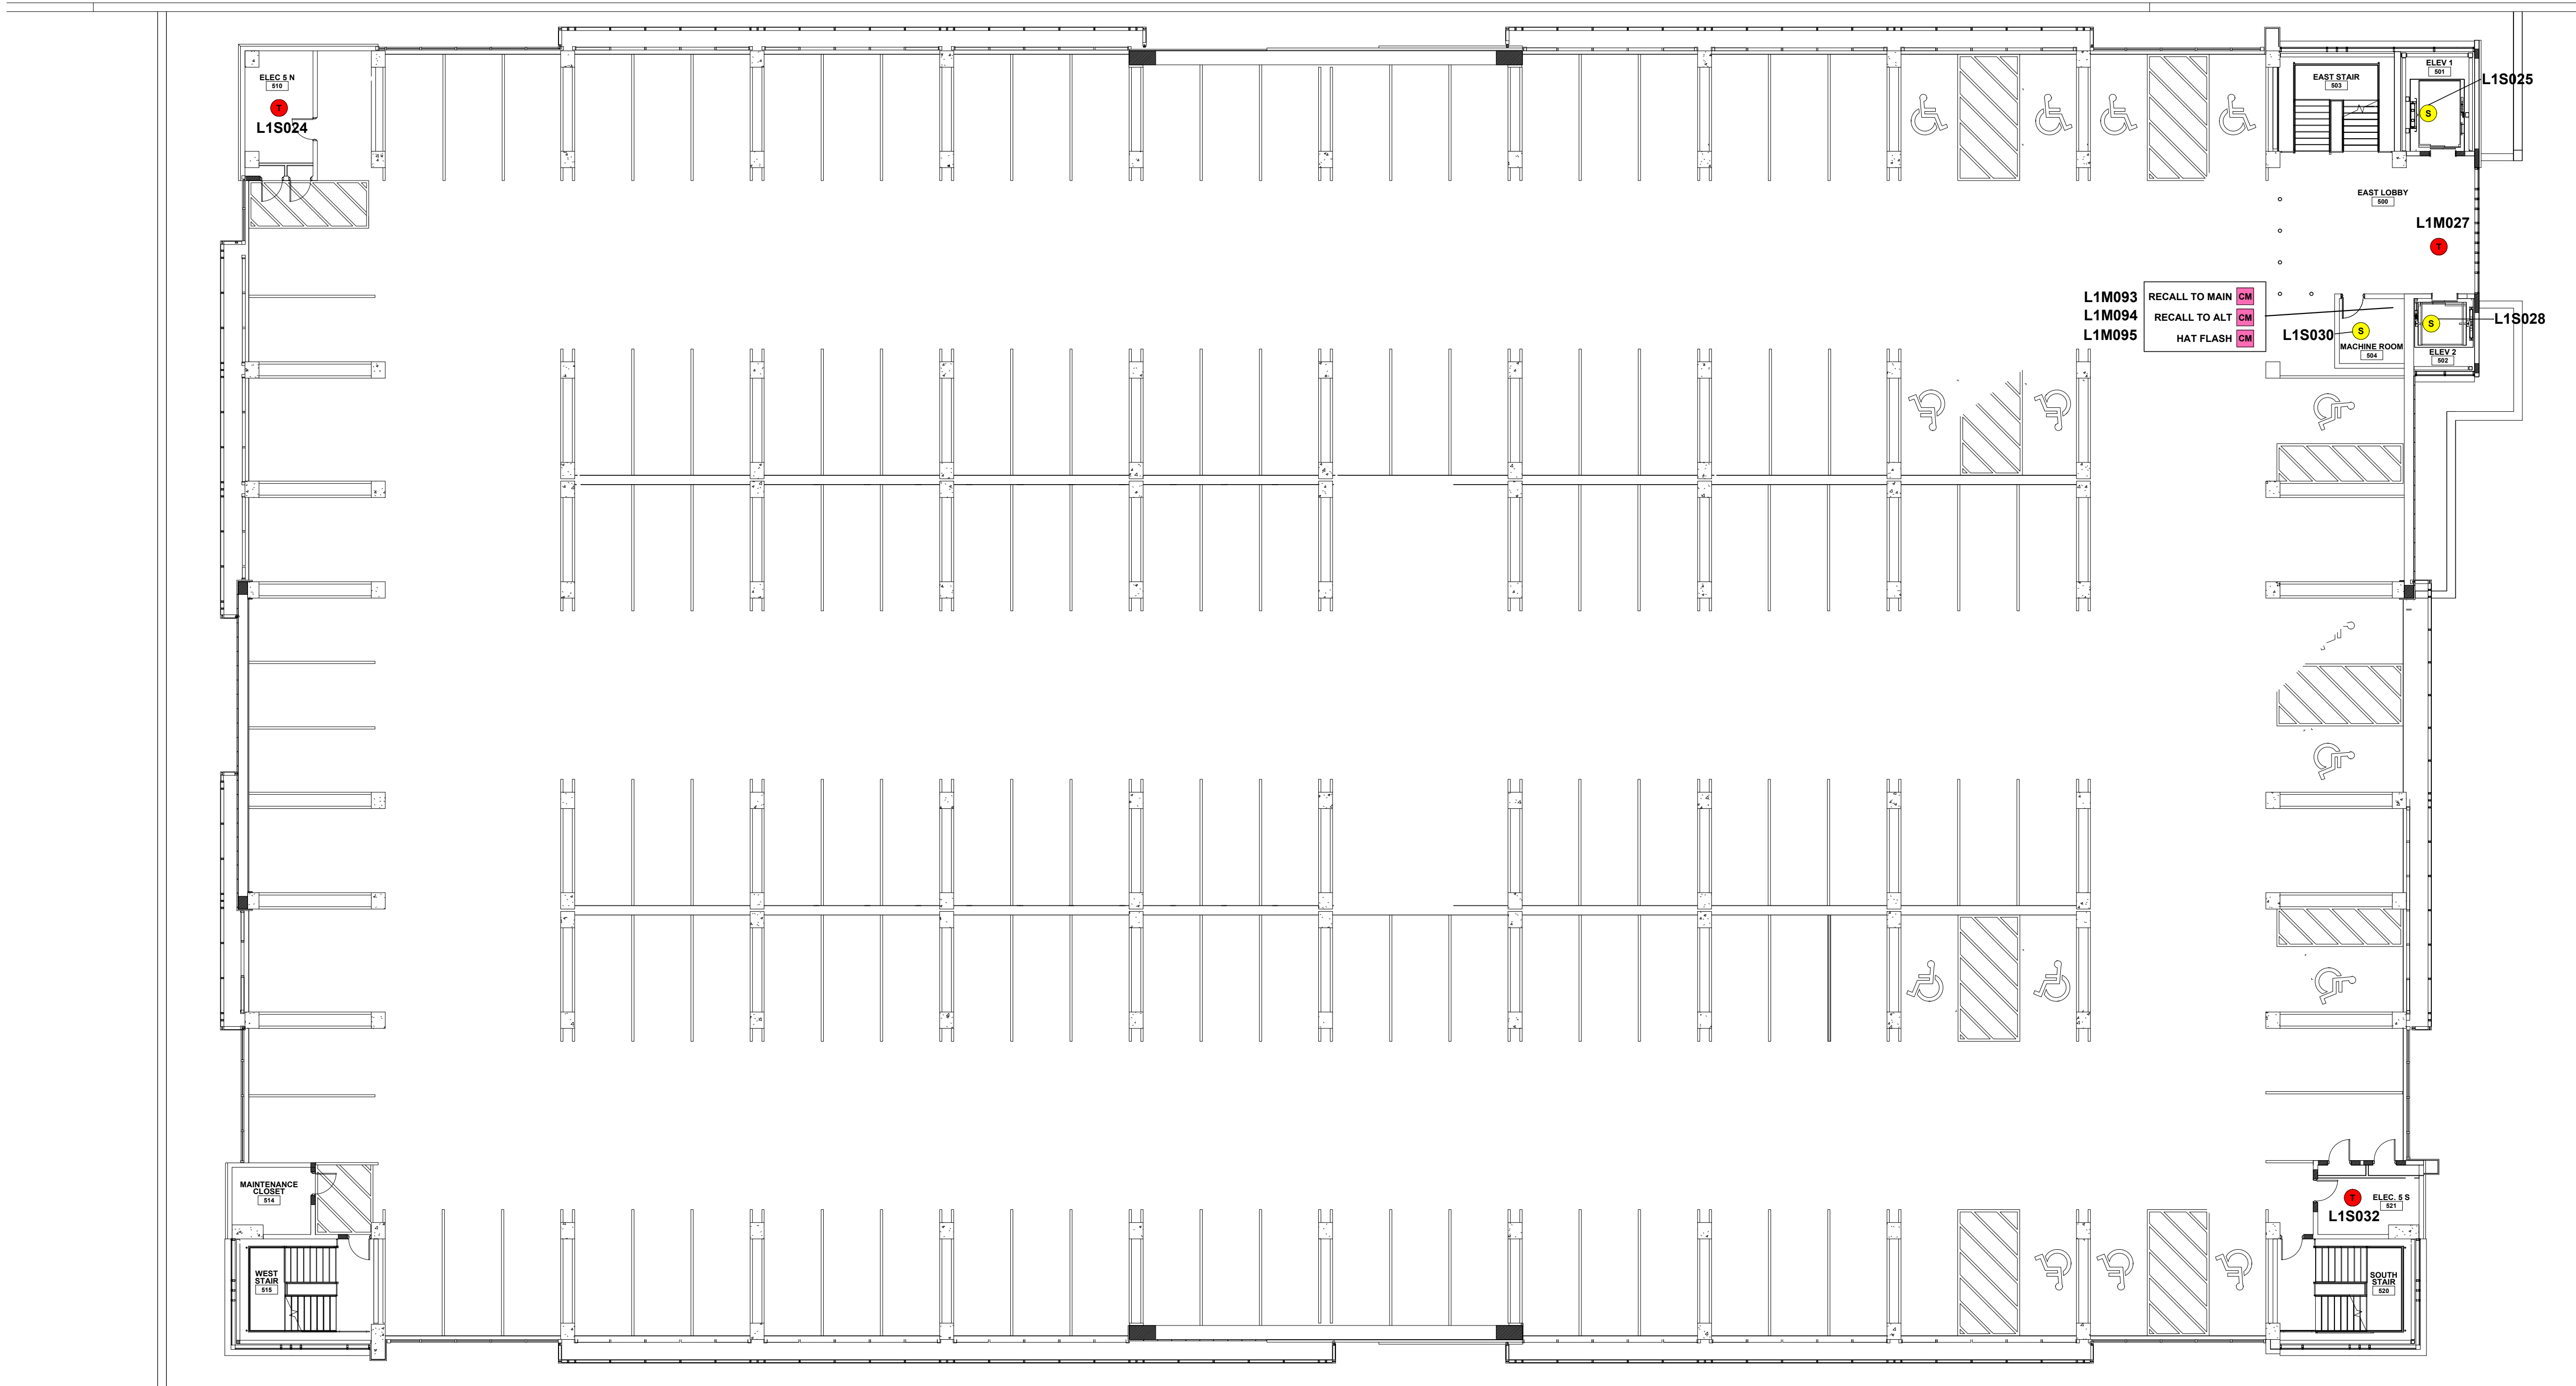

PARKING LEVEL 8

| DEVICE LEGEND |                         |
|---------------|-------------------------|
| SYMBOL        | DESCRIPTION             |
| S             | SMOKE DETECTOR          |
| H             | HEAT DETECTOR           |
| MM            | MONITOR MODULE          |
| CM            | CONTROL MODULE          |
| FACU          | FIRE ALARM CONTROL UNIT |
| TRAN          | TRANSPONDER PANEL       |

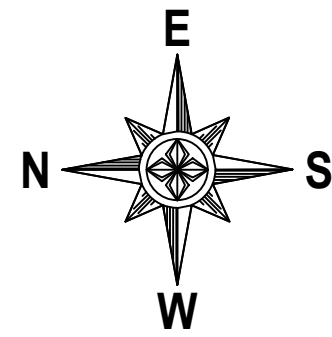

NOTE: NFS DRAWINGS ARE BASED ON THE PROJECT ARCHITECTURE/ENGINEER (A/E) PLANS AND SPECIFICATIONS FURNISHED TO NFS. A/E IS SOLELY RESPONSIBLE (NOT NFS) FOR THE TYPE, SIZE, LOCATION, AND SUITABILITY OF ALL FIRE ALARMS, CONTROL PANELS, AND OTHER DEVICES SHOWN ON THE A/E PLANS. NFS DRAWINGS ARE TO SHOW ONLY THE WIRING DIAGRAMS BETWEEN FIRE ALARM DEVICES AND CONTROL PANELS. NFS IS NOT RESPONSIBLE FOR THE INFORMATION SHOWN ON THE A/E PLANS.

NORTH PATIENT PARKING GARAGE  
1865 EAST MEDICAL DRIVE NORTH  
SALT LAKE CITY, UTAH 84132  
FIRE ALARM SYSTEM

**NFS**

NELSON FIRE SYSTEMS  
801-468-8300

DRAWN BY: XXXX  
DESIGNED BY: XXXX  
APPROVED BY: XXXX  
DATE: 11/30/2023 8:11:00 AM  
SCALE: N.T.S.  
PROJECT NO: XXXX  
REVISION NO: XXXX  
DRAWING NAME:  
UOFU PATIENT P8.DWG

NELSON FIRE SYSTEMS

PARKING 8

PAGE:

**FINAL MAP**

